



FIRST FLOOR - ABRIELLA BEDROOM LAYOUT  
SCALE 1:25

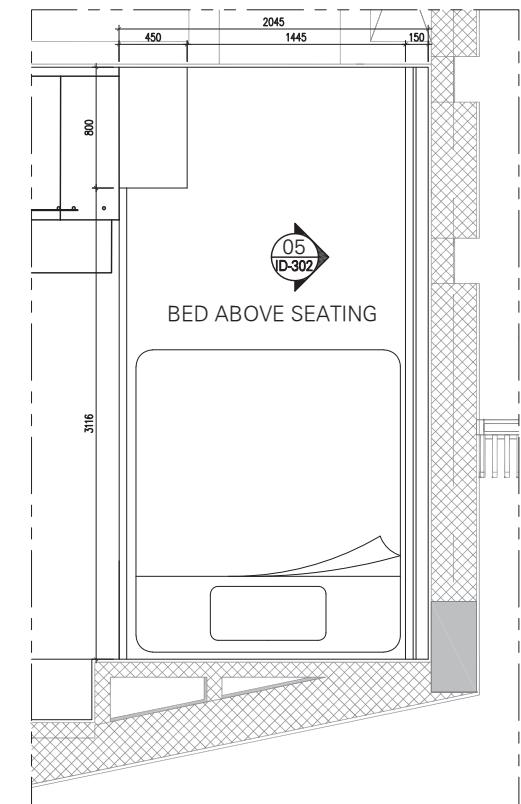

General Notes:											
1. All dimensions are in millimeters unless otherwise noted. 2. Any inconsistency or discrepancy is to be brought to the attention of and resolved by the architect/designer. 3. All dimensions are to be checked on site before commencing work. 4. This drawing is to be coordinated with the Lead Consultant.											
Notes											
* ALL DRAWINGS ARE FOR DESIGN INTENT ONLY AND ARE NOT FOR CONSTRUCTION. THE APPOINTED CONTRACTOR SHOULD PROVIDE SHOP DRAWING FOR APPROVAL.											
* CONTRACTOR TO DO A SITE SURVEY TO SPECIFY CORRECT QUANTITY & DIMENSIONS AS PER SITE MEASUREMENTS & DRAWINGS.											
* CONTRACTOR TO CHECK THE MECHANISM & FUNCTIONALITY OF THE DESIGN INTEND.											
* MATERIAL MUST BE PRESENTED TO PRIOR TO PURCHASE FOR TO APPROVE.											
<table border="1"> <tr> <td>0</td><td>2025.05.20</td><td>mp</td><td>Initial issue</td></tr> <tr> <td>Rev</td><td>Date</td><td>Drawn</td><td>Revisions</td></tr> </table>				0	2025.05.20	mp	Initial issue	Rev	Date	Drawn	Revisions
0	2025.05.20	mp	Initial issue								
Rev	Date	Drawn	Revisions								
Design Architect:											
<table border="1"> <tr> <td>Client:</td><td>Zach-Aimee</td></tr> <tr> <td>Project Title:</td><td>Private Villa - Dubai Hills</td></tr> <tr> <td>Location:</td><td>Dubai, U.A.E.</td></tr> </table>				Client:	Zach-Aimee	Project Title:	Private Villa - Dubai Hills	Location:	Dubai, U.A.E.		
Client:	Zach-Aimee										
Project Title:	Private Villa - Dubai Hills										
Location:	Dubai, U.A.E.										
<table border="1"> <tr> <td>Plot Area:</td><td>0000.00 Sqm</td></tr> <tr> <td></td><td>0000.00 SqFt</td></tr> <tr> <td>Old Gate Level:</td><td>0.00 = 0.000</td></tr> <tr> <td>NEW GATE LEVEL =</td><td>0.000</td></tr> </table>				Plot Area:	0000.00 Sqm		0000.00 SqFt	Old Gate Level:	0.00 = 0.000	NEW GATE LEVEL =	0.000
Plot Area:	0000.00 Sqm										
	0000.00 SqFt										
Old Gate Level:	0.00 = 0.000										
NEW GATE LEVEL =	0.000										
Sheet Contents:											
FIRST FLOOR ABRIELLA BEDROOM GENERAL LAYOUT											
<table border="1"> <tr> <td>Designed by:</td><td>Drawn By:</td><td>Checked By:</td><td>Issued By:</td></tr> <tr> <td>ab</td><td>mp</td><td>ab</td><td>ab</td></tr> </table>				Designed by:	Drawn By:	Checked By:	Issued By:	ab	mp	ab	ab
Designed by:	Drawn By:	Checked By:	Issued By:								
ab	mp	ab	ab								
<table border="1"> <tr> <td>Scale:</td><td>Sheet Size:</td><td>Stage:</td><td>Rev No:</td></tr> <tr> <td>1:25</td><td>A1</td><td>Conceptual Stage</td><td>0</td></tr> </table>				Scale:	Sheet Size:	Stage:	Rev No:	1:25	A1	Conceptual Stage	0
Scale:	Sheet Size:	Stage:	Rev No:								
1:25	A1	Conceptual Stage	0								
Drwg No. ID-102											

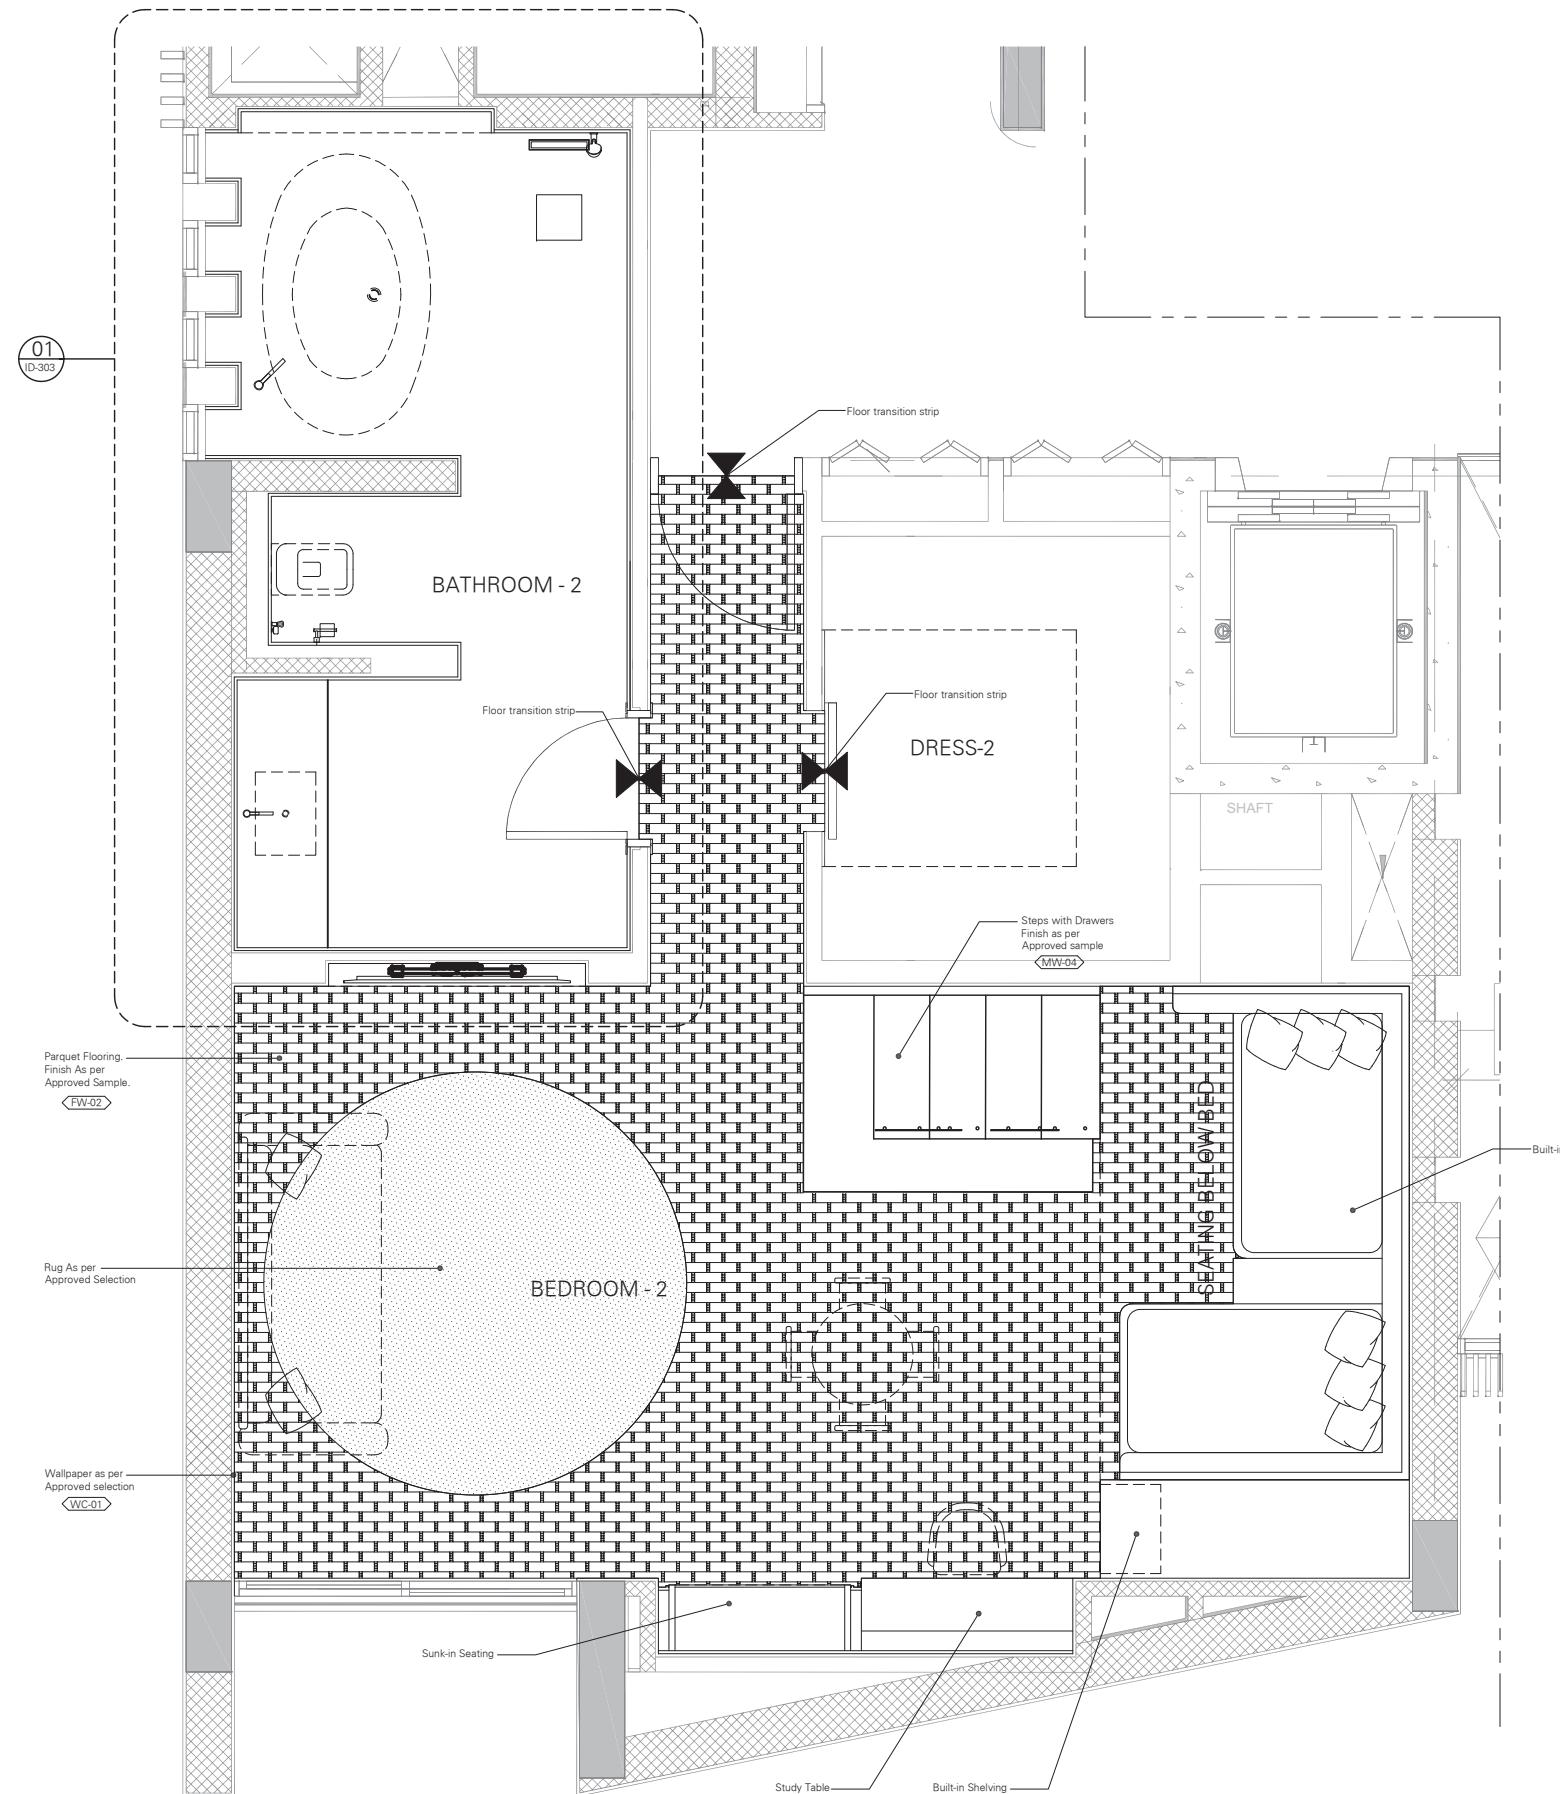

FIRST FLOOR - ANABELLA BEDROOM - FLOORING & FINISHING LAYOUT

SCALE 1:25

**General Notes:**

- All dimensions are in millimeters unless otherwise noted.
- Any inconsistency or discrepancy is to be brought to the attention of and resolved by the architect/designer.
- All dimensions are to be checked on site before commencing work.
- This drawing is to be coordinated with the Lead Consultant.

**Notes**

- \* ALL DRAWINGS ARE FOR DESIGN INTENT ONLY AND ARE NOT FOR CONSTRUCTION. THE APPOINTED CONTRACTOR SHOULD PROVIDE SHOP DRAWING FOR APPROVAL.
- \* CONTRACTOR TO DO A SITE SURVEY TO SPECIFY CORRECT QUANTITY & DIMENSIONS AS PER SITE MEASUREMENTS & DRAWINGS.
- \* CONTRACTOR TO CHECK THE MECHANISM & FUNCTIONALITY OF THE DESIGN INTEND.
- \* MATERIAL MUST BE PRESENTED TO PRIOR TO PURCHASE FOR TO APPROVE.

0	2025.05.20	mp	Initial issue
Rev	Date	Drawn	Revisions

**Design Architect:**

**Client:**  
Zach-Aimee


**Project Title:**  
Private Villa -Dubai Hills

**Location:**  
Dubai, U.A.E.

**Plot Area:** 0000.00 Sqm  
0000.00 SqFt  
**Old Gate Level:** 0.00 = 0.000  
**NEW GATE LEVEL:** = 0.000  
Proposed Gate Level is to be 000 mm above existing Asphalt Road Level

Sheet Contents:			
FIRST FLOOR ABRIELLA BEDROOM FLOORING + FINISHING LAYOUT			
Designed by: Drawn By: Checked By: Issued By: ab mp ab ab			
Scale: 1:25	Sheet Size: A1	Stage: Conceptual Stage	Rev No: 0

**Drwg No.** ID-105

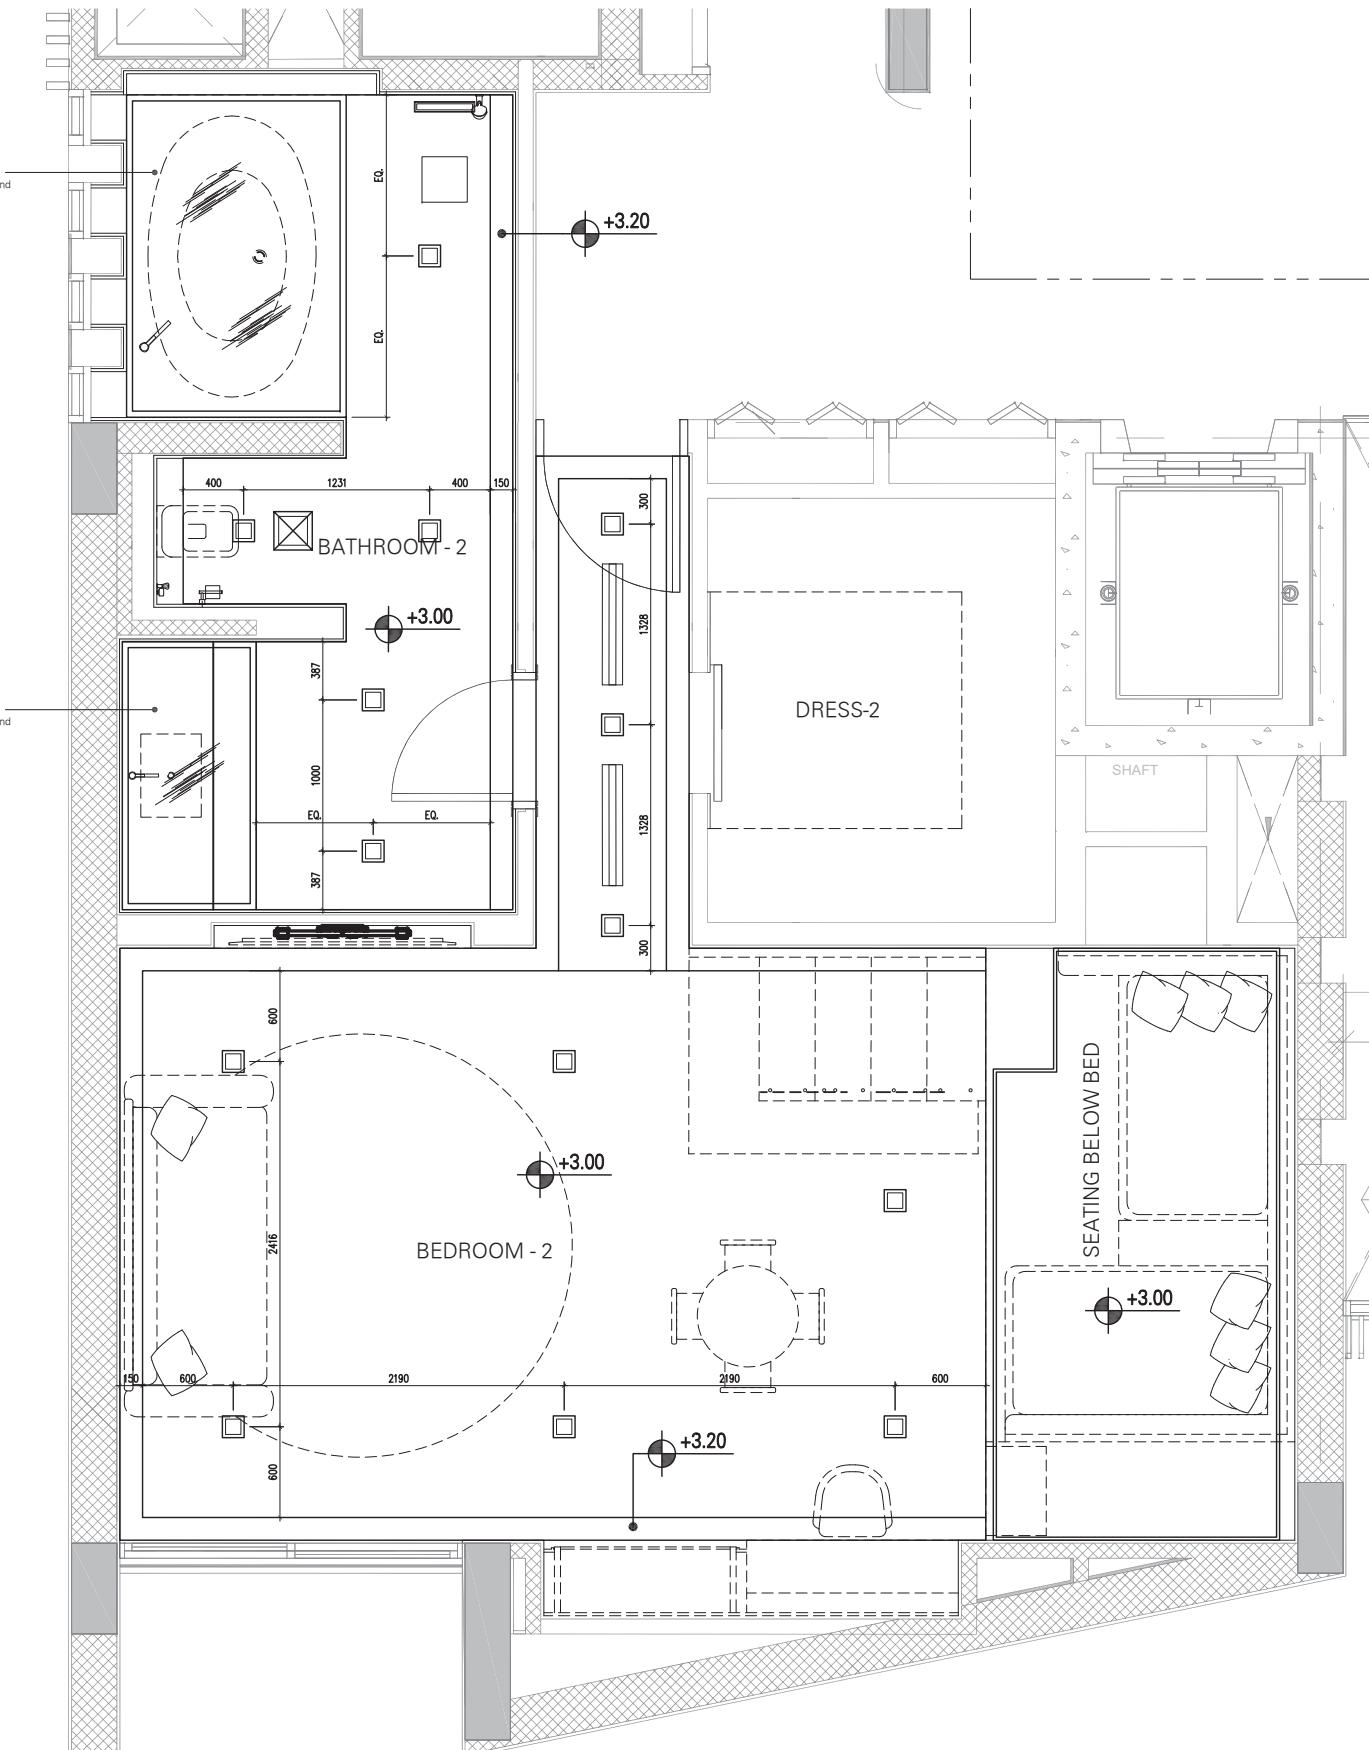

FIRST FLOOR - ABRIELLA BEDROOM - REFLECTED CEILING LAYOUT

SCALE 1:25

**General Notes:**

- All dimensions are in millimeters unless otherwise noted.
- Any inconsistency or discrepancy is to be brought to the attention of and resolved by the architect/designer.
- All dimensions are to be checked on site before commencing work.
- This drawing is to be coordinated with the Lead Consultant.

**Notes**

- \* ALL DRAWINGS ARE FOR DESIGN INTENT ONLY AND ARE NOT FOR CONSTRUCTION. THE APPOINTED CONTRACTOR SHOULD PROVIDE SHOP DRAWING FOR APPROVAL.
- \* CONTRACTOR TO DO A SITE SURVEY TO SPECIFY CORRECT QUANTITY & DIMENSIONS AS PER SITE MEASUREMENTS & DRAWINGS.
- \* CONTRACTOR TO CHECK THE MECHANISM & FUNCTIONALITY OF THE DESIGN INTEND.
- \* MATERIAL MUST BE PRESENTED TO PRIOR TO PURCHASE FOR TO APPROVE.

**LEGEND :**

- Recessed Downlight
- ☒ Exhaust Grill

0	2025.05.20	mp	Initial issue
Rev	Date	Drawn	Revisions

**Design Architect:**

**Client:**  
Zach-Aimee

**Project Title:**  
Private Villa -Dubai Hills

**Location:**  
Dubai, U.A.E.

**Plot Area:** 0000.00 Sqm  
0000.00 SqFt  
**Old Gate Level:** 0.00 = 0.000  
**NEW GATE LEVEL = 0.000**  
Proposed Gate Level is to be 000 mm above existing Asphalt Road Level

Sheet Contents:			
FIRST FLOOR ABRIELLA BEDROOM REFLECTED CEILING LAYOUT			
Designed by:	Drawn By:	Checked By:	Issued By:
ab	mp	ab	ab

Scale: 1:25 Sheet Size: A1 Stage: Conceptual Rev No: 0


Drwg No. ID-201

**General Notes:**

- All dimensions are in millimeters unless otherwise noted.
- Any inconsistency or discrepancy is to be brought to the attention of and resolved by the architect/designer.
- All dimensions are to be checked on site before commencing work.
- This drawing is to be coordinated with the Lead Consultant.


**Notes**

- \* ALL DRAWINGS ARE FOR DESIGN INTENT ONLY AND ARE NOT FOR CONSTRUCTION. THE APPOINTED CONTRACTOR SHOULD PROVIDE SHOP DRAWING FOR APPROVAL.
- \* CONTRACTOR TO DO A SITE SURVEY TO SPECIFY CORRECT QUANTITY & DIMENSIONS AS PER SITE MEASUREMENTS & DRAWINGS.
- \* CONTRACTOR TO CHECK THE MECHANISM & FUNCTIONALITY OF THE DESIGN INTEND.
- \* MATERIAL MUST BE PRESENTED TO PRIOR TO PURCHASE FOR TO APPROVE.

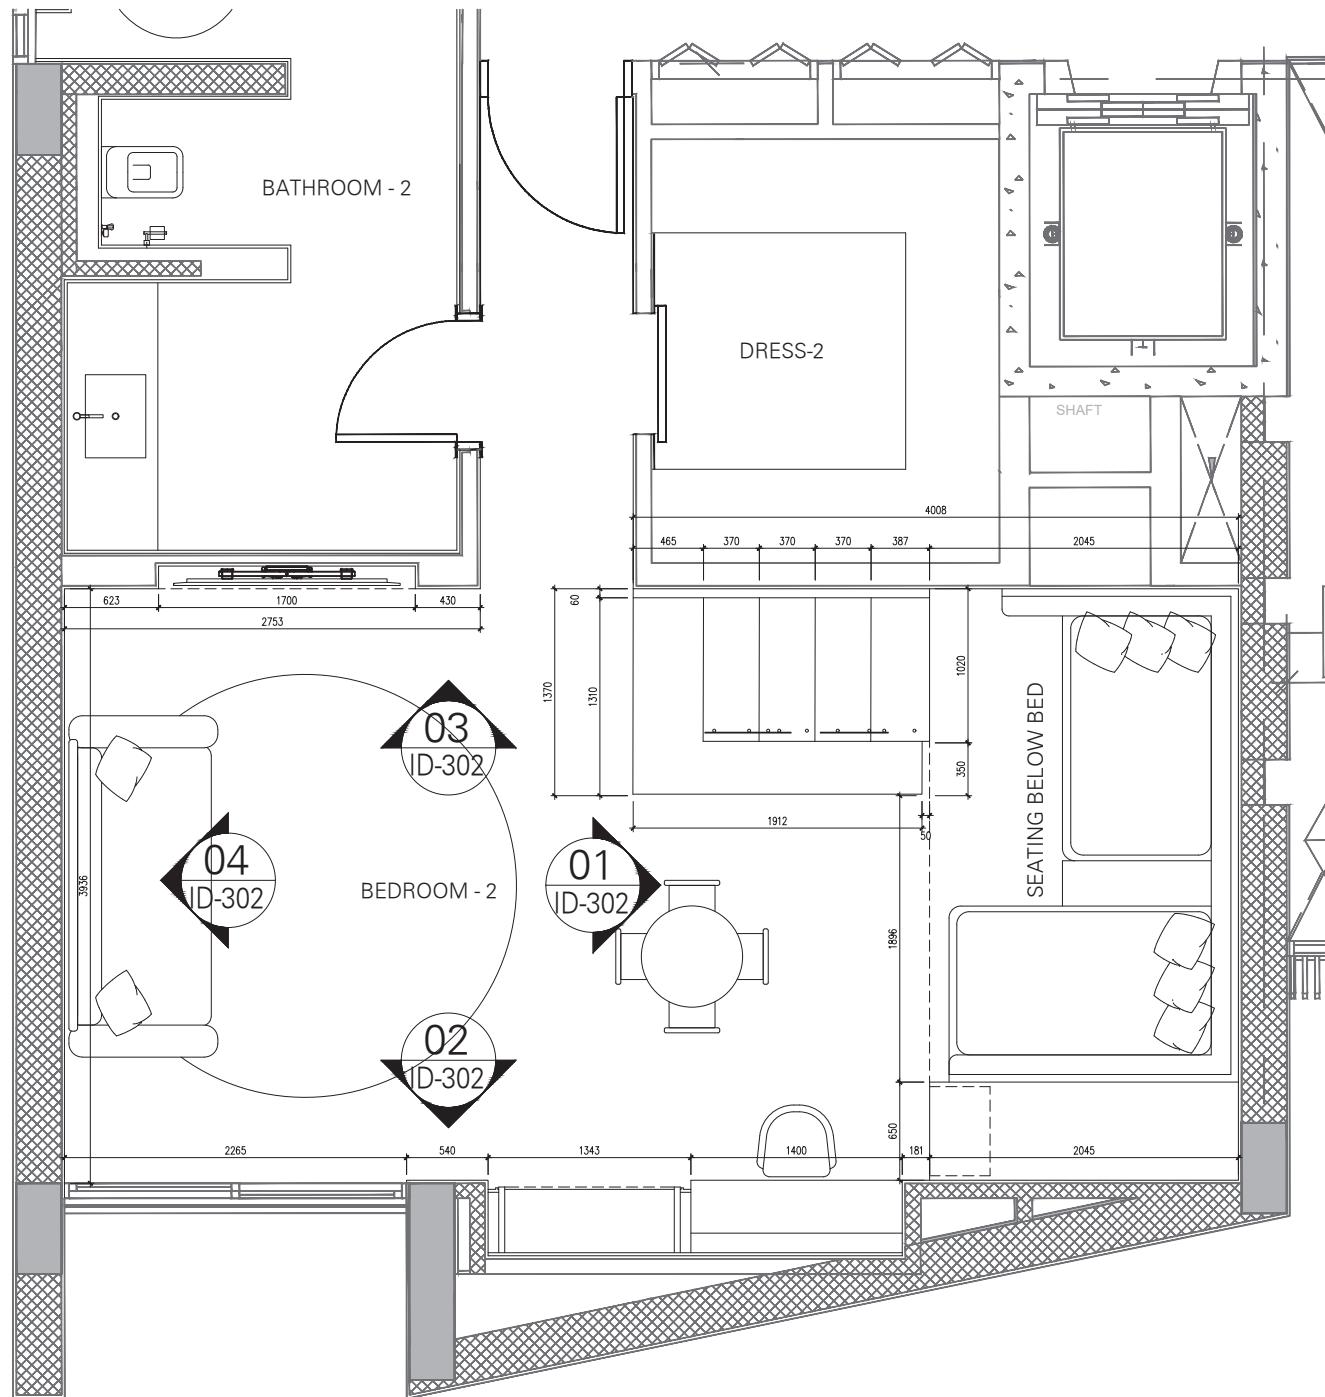

**FIRST FLOOR - ABRIELLA BEDROOM LAYOUT**

SCALE 1:50

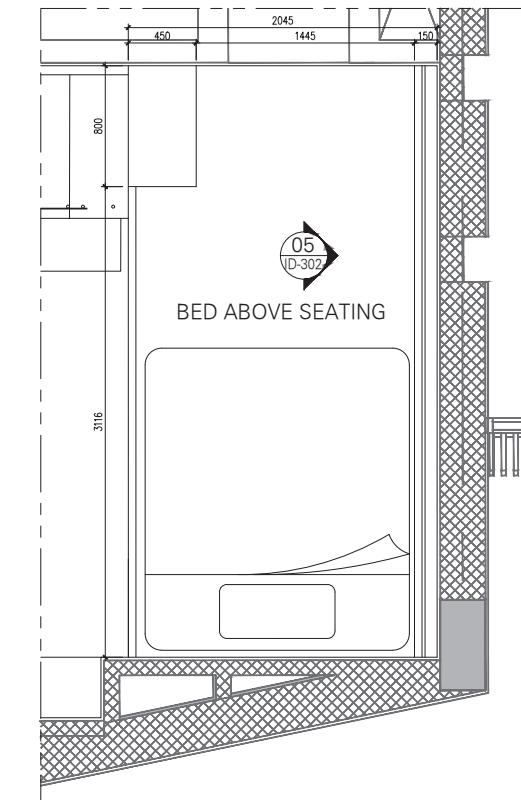

**Client:** Zach-Aimee  
**Project Title:** Private Villa -Dubai Hills

**Location:** Dubai, U.A.E.


**Plot Area:** 0000.00 Sqm  
0000.00 SqFt  
**Old Gate Level:** 0.00 = 0.000  
**NEW GATE LEVEL = 0.000**  
Proposed Gate Level is to be 000 mm above existing Asphalt Road Level

**Sheet Contents:**  
FIRST FLOOR  
ABRIELLA BEDROOM  
PLAN

Designed by:	Drawn By:	Checked By:	Issued By:
ab	mp	ab	ab

Scale: 1:25 Sheet Size: A1 Stage: Conceptual Rev No: 0

**Drwg No.** ID-302-1

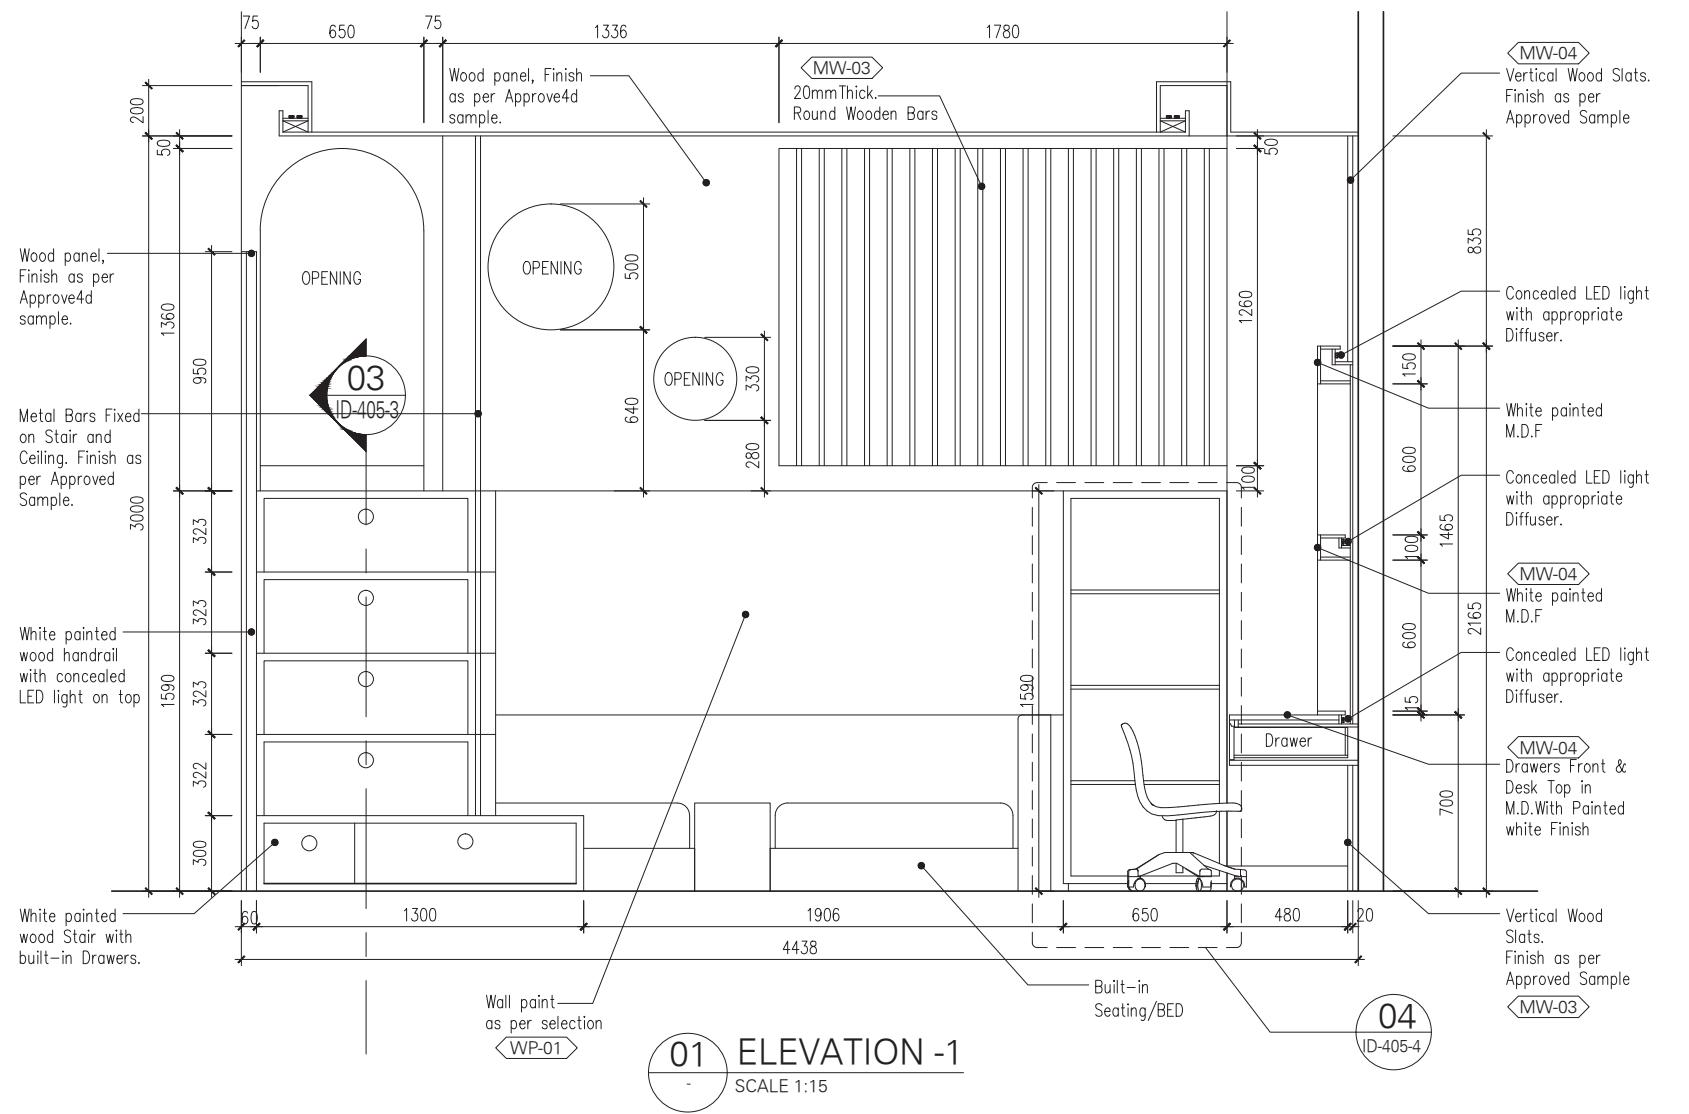



VISUAL - 1

**General Notes:**

- All dimensions are in millimeters unless otherwise noted.
- Any inconsistency or discrepancy is to be brought to the attention of and resolved by the architect/designer.
- All dimensions are to be checked on site before commencing work.
- This drawing is to be coordinated with the Lead Consultant.

**Notes**

- \* ALL DRAWINGS ARE FOR DESIGN INTENT ONLY AND ARE NOT FOR CONSTRUCTION. THE APPOINTED CONTRACTOR SHOULD PROVIDE SHOP DRAWING FOR APPROVAL.
- \* CONTRACTOR TO DO A SITE SURVEY TO SPECIFY CORRECT QUANTITY & DIMENSIONS AS PER SITE MEASUREMENTS & DRAWINGS.
- \* CONTRACTOR TO CHECK THE MECHANISM & FUNCTIONALITY OF THE DESIGN INTEND.
- \* MATERIAL MUST BE PRESENTED TO PRIOR TO PURCHASE FOR TO APPROVE.

0	2025.05.21	mp	Initial issue
Rev	Date	Drawn	Revisions

**Design Architect:**

**Client:** Zach-Aimee  
**Project Title:** Private Villa -Dubai Hills


**Location:** Dubai, U.A.E.

**Plot Area:** 0000.00 Sqm  
0000.00 SqFt  
**Old Gate Level:** 0.00 = 0.000  
**NEW GATE LEVEL = 0.000**  
Proposed Gate Level is to be 000 mm above existing Asphalt Road Level

<b>Sheet Contents:</b>			
FIRST FLOOR ABRIELLA BEDROOM VISUAL - 1			
Designed by:	Drawn By:	Checked By:	Issued By:
ab	mp	ab	ab

**Scale:** Sheet Size: Stage: Rev No:  
1:25 A1 Conceptual Stage 0

**Drwg No.** ID-302-2-R

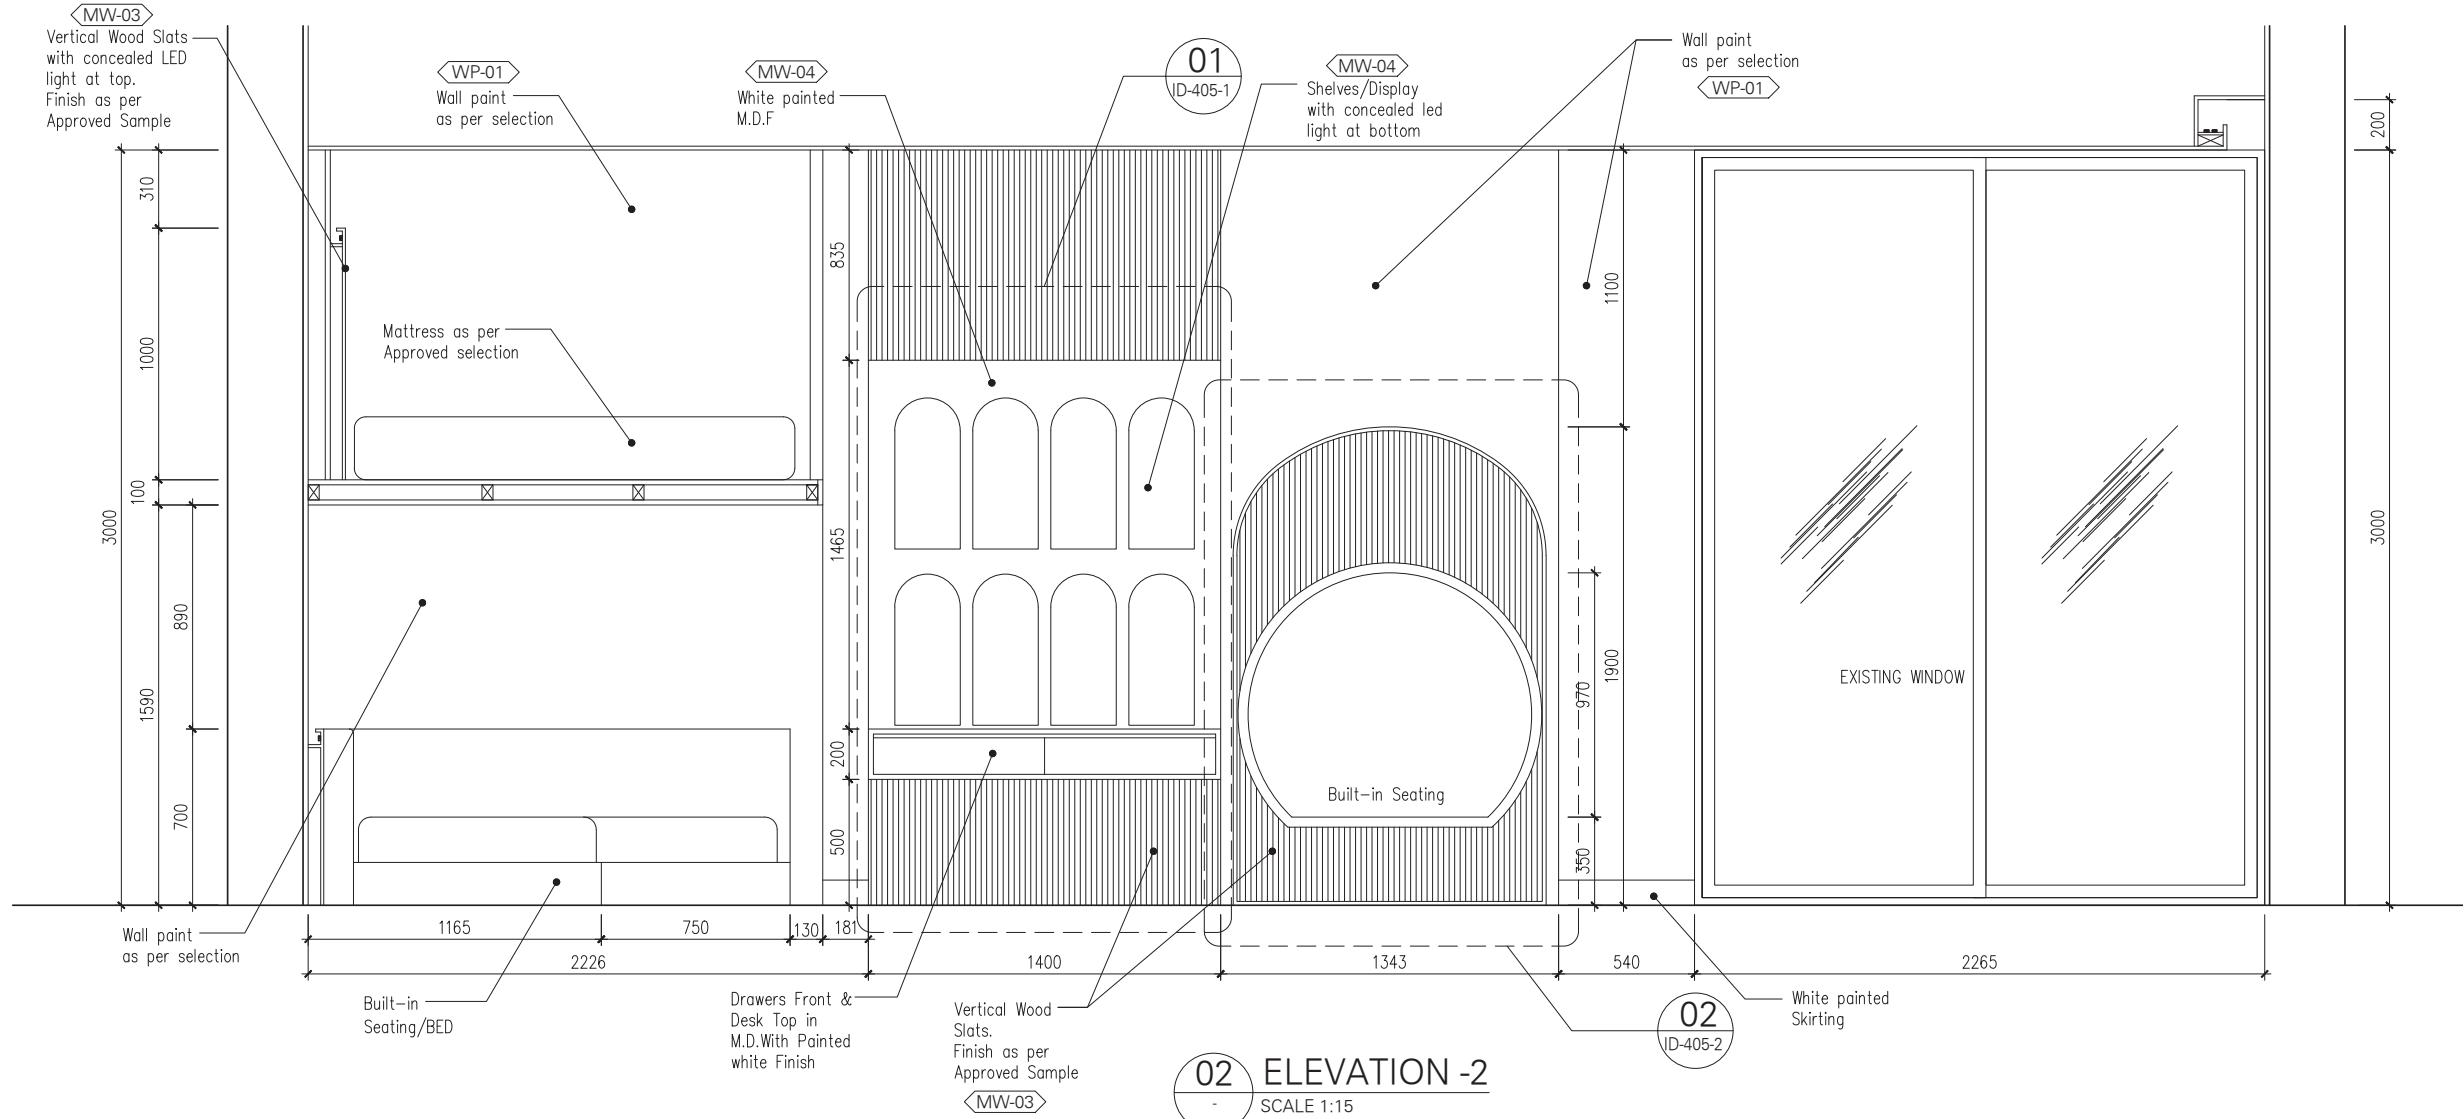

02 ELEVATION - 2

SCALE 1:15



**General Notes:**

- All dimensions are in millimeters unless otherwise noted.
- Any inconsistency or discrepancy is to be brought to the attention of and resolved by the architect/designer.
- All dimensions are to be checked on site before commencing work.
- This drawing is to be coordinated with the Lead Consultant.

**Notes**

\* ALL DRAWINGS ARE FOR DESIGN INTENT ONLY AND ARE NOT FOR CONSTRUCTION. THE APPOINTED CONTRACTOR SHOULD PROVIDE SHOP DRAWING FOR APPROVAL.

\* CONTRACTOR TO DO A SITE SURVEY TO SPECIFY CORRECT QUANTITY & DIMENSIONS AS PER SITE MEASUREMENTS & DRAWINGS.

\* CONTRACTOR TO CHECK THE MECHANISM & FUNCTIONALITY OF THE DESIGN INTEND.

\* MATERIAL MUST BE PRESENTED TO PRIOR TO PURCHASE FOR TO APPROVE.

0	2025.05.21	mp	Initial issue
Rev	Date	Drawn	Revisions

**Design Architect:**

**Client:** Zach-Aimee  
**Project Title:** Private Villa -Dubai Hills


**Location:** Dubai, U.A.E.

**Plot Area:** 0000.00 Sqm  
0000.00 SqFt  
**Old Gate Level:** 0.00 = 0.000  
**NEW GATE LEVEL = 0.000**  
Proposed Gate Level is to be 000 mm above existing Asphalt Road Level

Sheet Contents:			
FIRST FLOOR ABRIELLA BEDROOM ELEVATION-2			
Designed by:	Drawn By:	Checked By:	Issued By:
ab	mp	ab	ab


**Scale:** 1:15      **Sheet Size:** A1      **Stage:** Conceptual Stage      **Rev No:** 0

**Drwg No.** ID-302-3

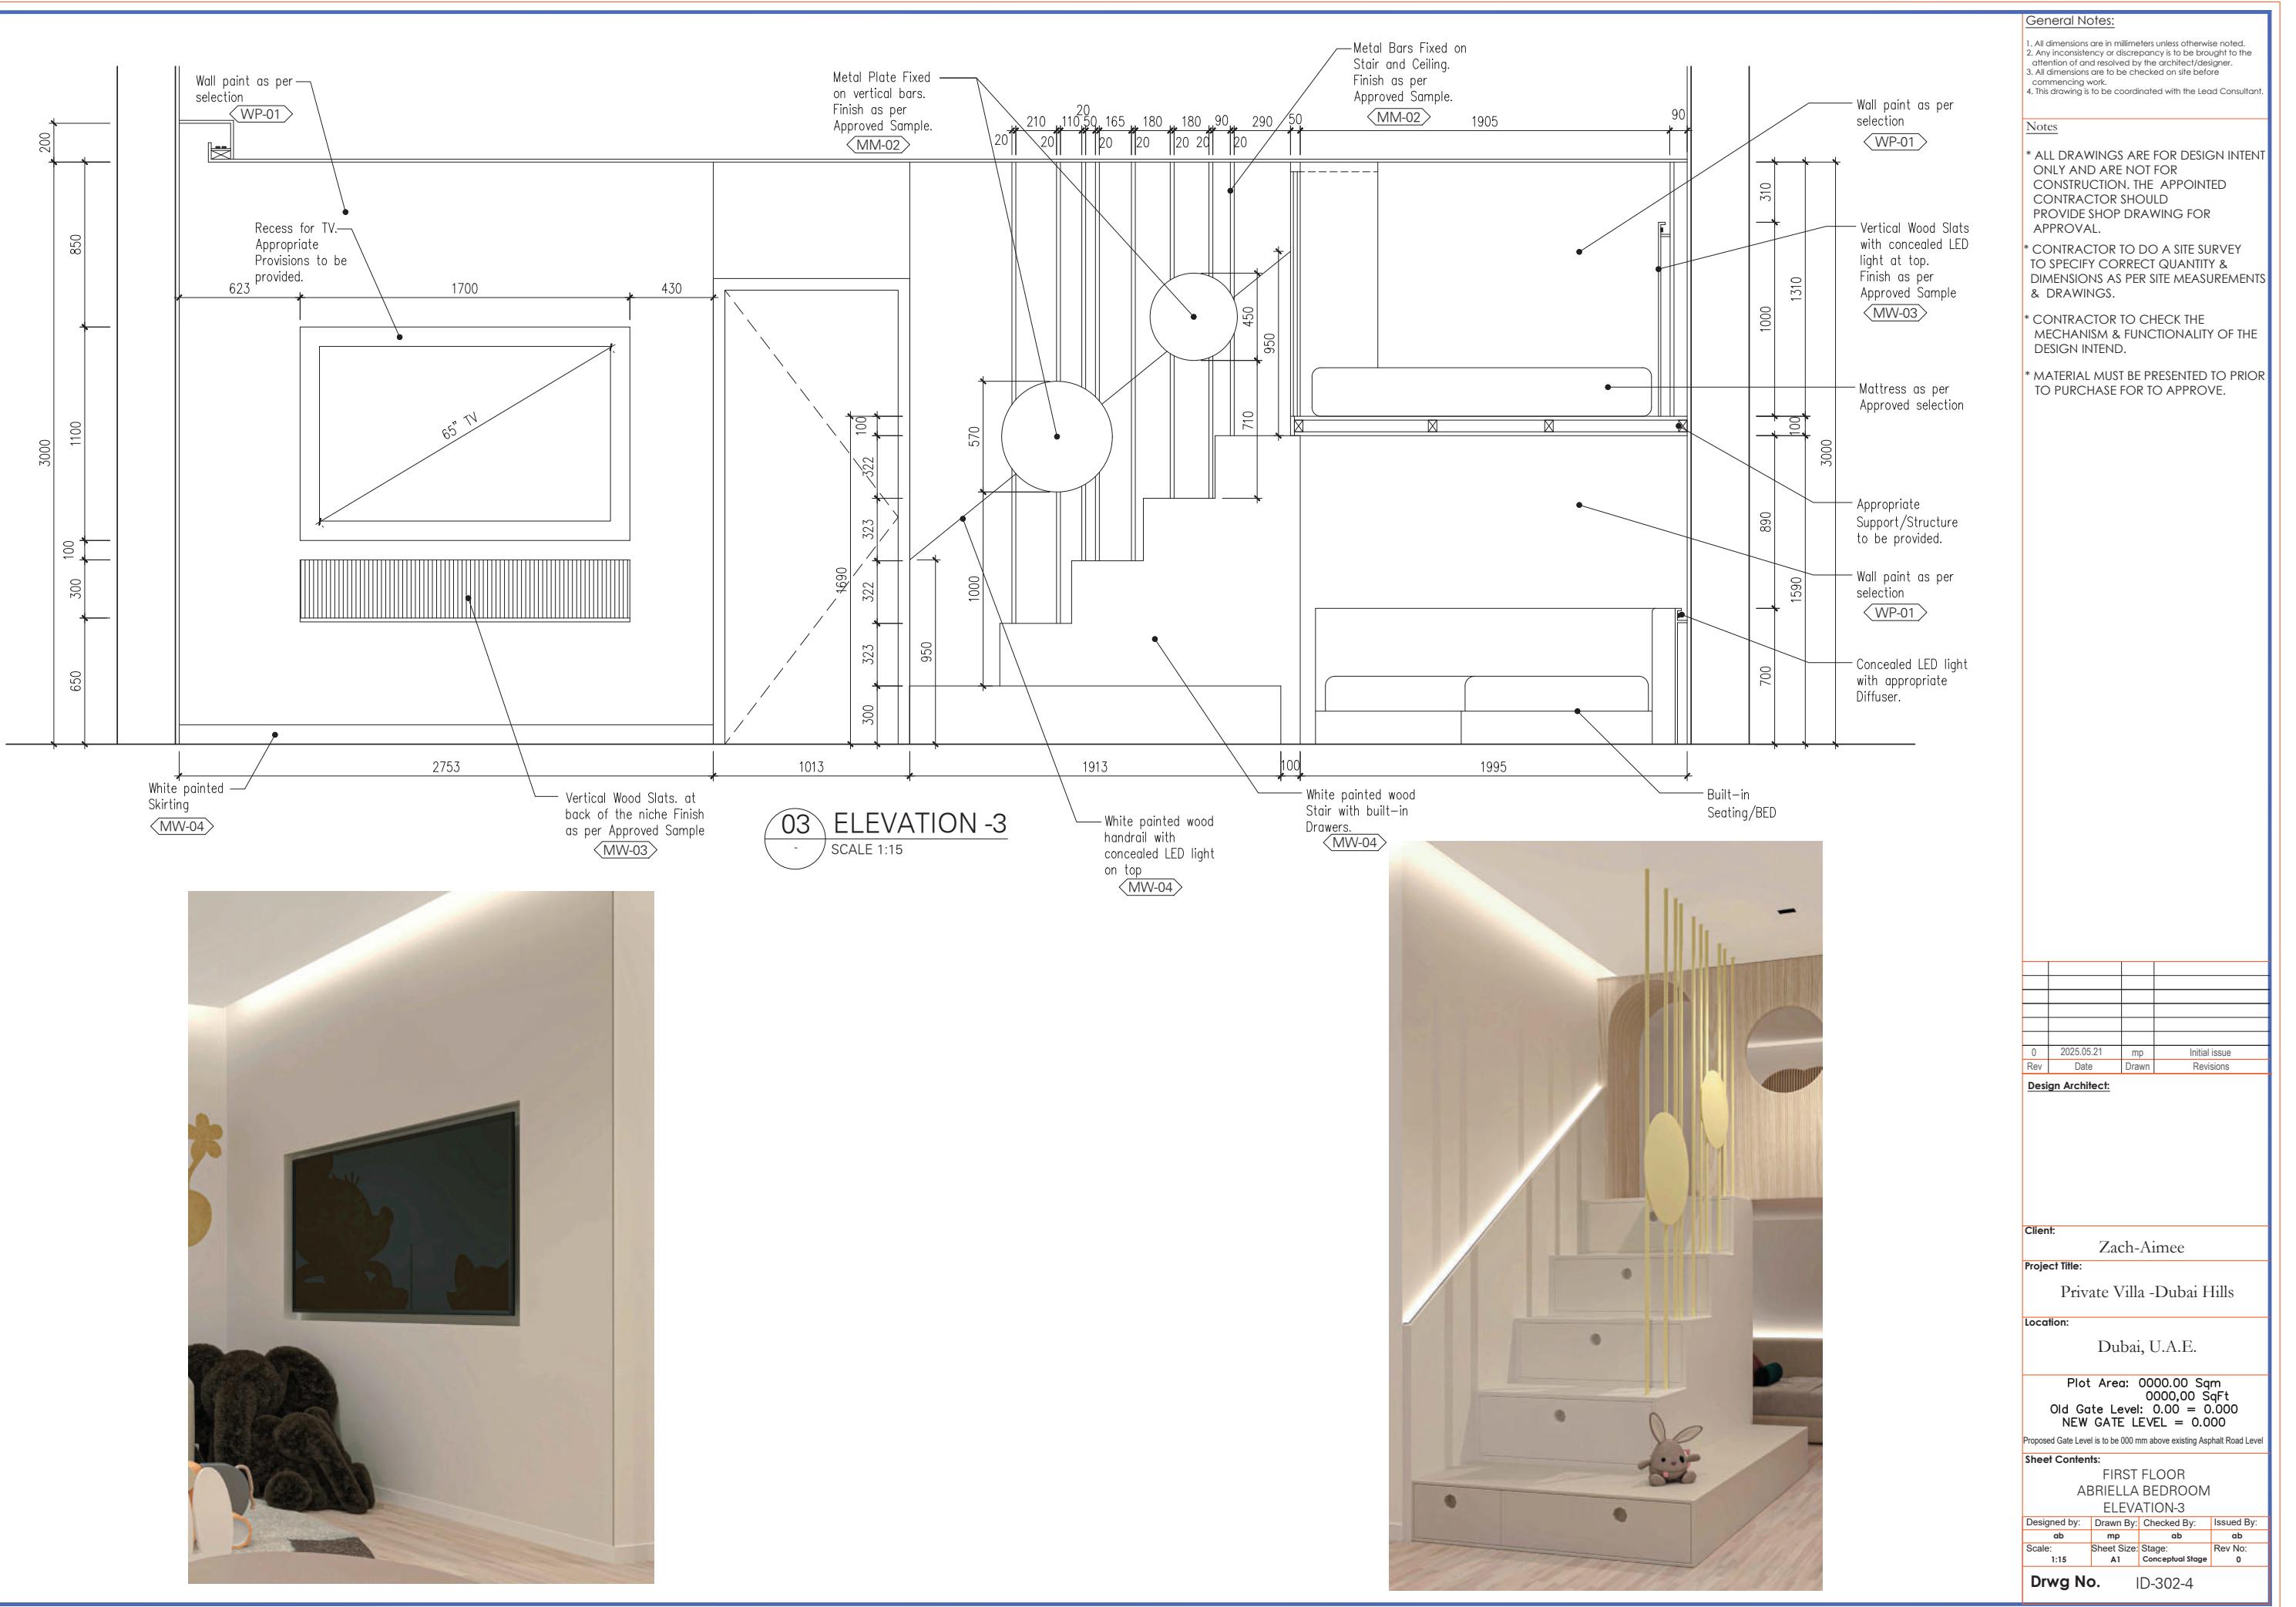



## VISUAL - 2

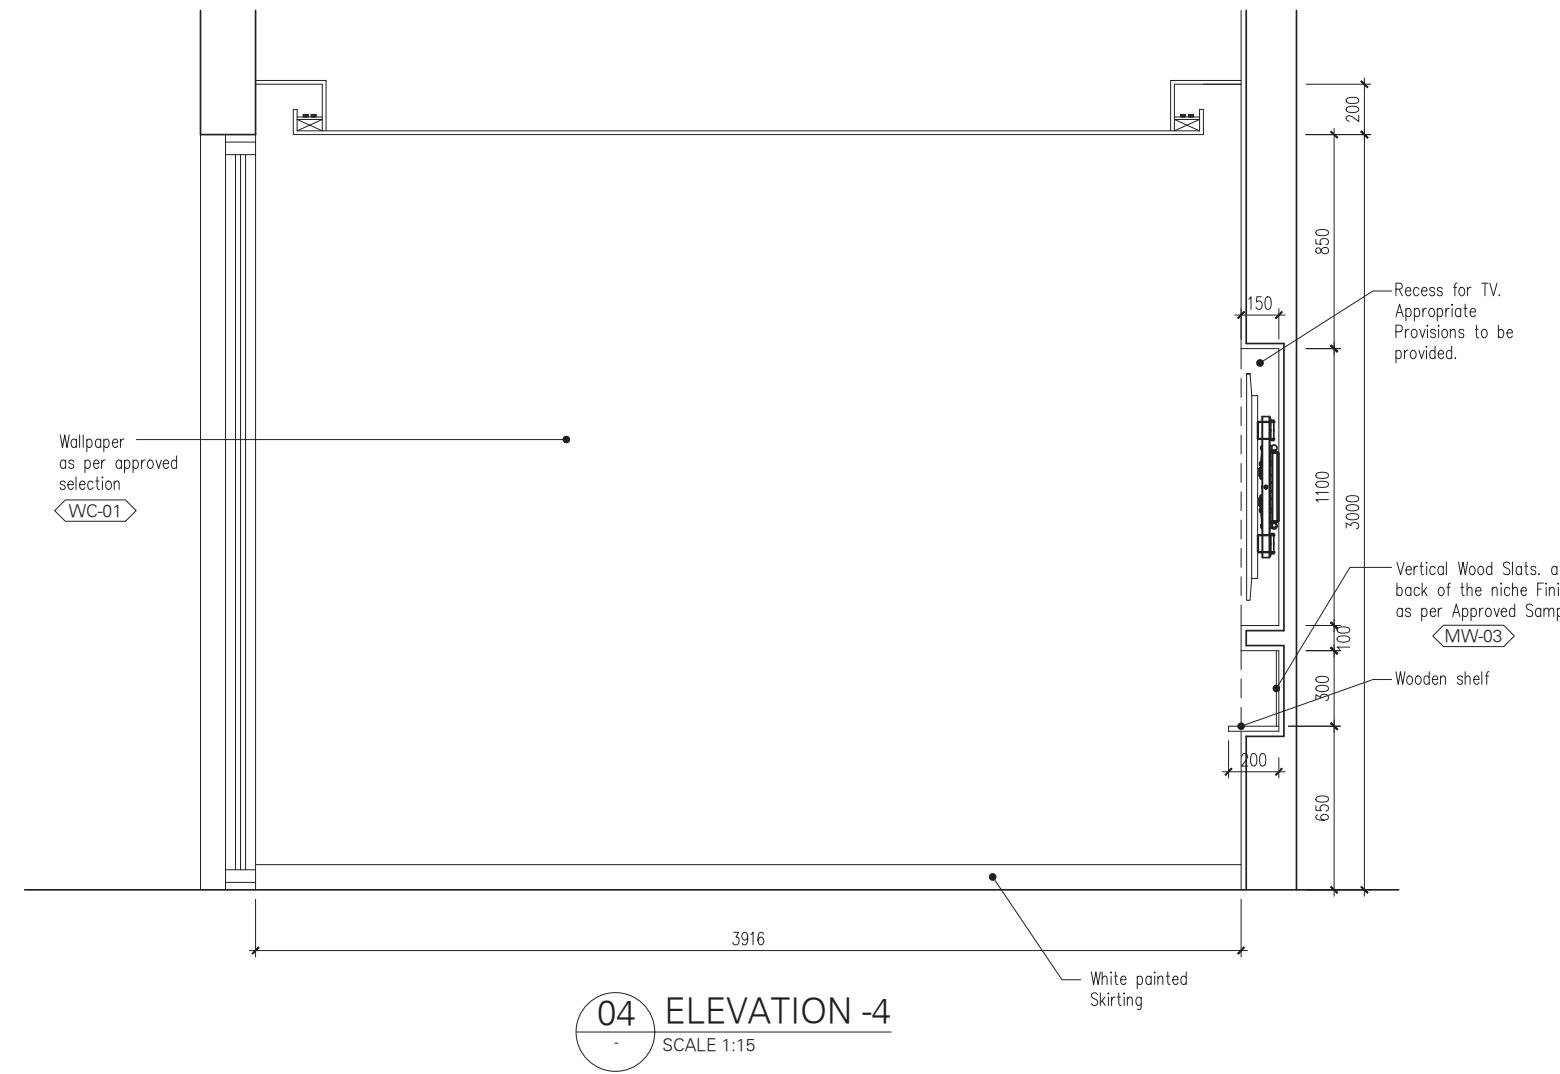

**General Notes:**

- All dimensions are in millimeters unless otherwise noted.
- Any inconsistency or discrepancy is to be brought to the attention of and resolved by the architect/designer.
- All dimensions are to be checked on site before commencing work.
- This drawing is to be coordinated with the Lead Consultant.

**Notes**

- \* ALL DRAWINGS ARE FOR DESIGN INTENT ONLY AND ARE NOT FOR CONSTRUCTION. THE APPOINTED CONTRACTOR SHOULD PROVIDE SHOP DRAWING FOR APPROVAL.
- \* CONTRACTOR TO DO A SITE SURVEY TO SPECIFY CORRECT QUANTITY & DIMENSIONS AS PER SITE MEASUREMENTS & DRAWINGS.
- \* CONTRACTOR TO CHECK THE MECHANISM & FUNCTIONALITY OF THE DESIGN INTEND.
- \* MATERIAL MUST BE PRESENTED TO PRIOR TO PURCHASE FOR TO APPROVE.

0	2025.05.21	mp	Initial issue
Rev	Date	Drawn	Revisions

**Design Architect:**

**Client:**  
Zach-Aimee

**Project Title:**  
Private Villa -Dubai Hills

**Location:**  
Dubai, U.A.E.

**Plot Area:** 0000.00 Sqm  
0000.00 SqFt  
**Old Gate Level:** 0.00 = 0.000  
**NEW GATE LEVEL = 0.000**  
Proposed Gate Level is to be 000 mm above existing Asphalt Road Level

**Sheet Contents:**  
FIRST FLOOR  
ABRIELLA BEDROOM  
ELEVATION-4

Designed by:	Drawn By:	Checked By:	Issued By:
ab	mp	ab	ab
Scale: 1:15	Sheet Size: A1	Stage: Conceptual	Rev No: 0

**Drwg No.** ID-302-5



VISUAL - 3

**General Notes:**

- All dimensions are in millimeters unless otherwise noted.
- Any inconsistency or discrepancy is to be brought to the attention of and resolved by the architect/designer.
- All dimensions are to be checked on site before commencing work.
- This drawing is to be coordinated with the Lead Consultant.

**Notes**

- \* ALL DRAWINGS ARE FOR DESIGN INTENT ONLY AND ARE NOT FOR CONSTRUCTION. THE APPOINTED CONTRACTOR SHOULD PROVIDE SHOP DRAWING FOR APPROVAL.
- \* CONTRACTOR TO DO A SITE SURVEY TO SPECIFY CORRECT QUANTITY & DIMENSIONS AS PER SITE MEASUREMENTS & DRAWINGS.
- \* CONTRACTOR TO CHECK THE MECHANISM & FUNCTIONALITY OF THE DESIGN INTEND.
- \* MATERIAL MUST BE PRESENTED TO PRIOR TO PURCHASE FOR TO APPROVE.

0	2025.05.21	mp	Initial issue
Rev	Date	Drawn	Revisions

**Design Architect:**

**Client:** Zach-Aimee  
**Project Title:** Private Villa -Dubai Hills

**Location:** Dubai, U.A.E.

**Plot Area:** 0000.00 Sqm  
0000.00 SqFt  
**Old Gate Level:** 0.00 = 0.000  
**NEW GATE LEVEL** = 0.000  
Proposed Gate Level is to be 000 mm above existing Asphalt Road Level

<b>Sheet Contents:</b>			
FIRST FLOOR ABRIELLA BEDROOM VISUAL - 3			
Designed by:	Drawn By:	Checked By:	Issued By:
ab	mp	ab	ab

**Scale:** 1:15      **Sheet Size:** A1      **Stage:** Conceptual Stage      **Rev No:** 0

**Drwg No.** ID-302-5-R

**General Notes:**

- All dimensions are in millimeters unless otherwise noted.
- Any inconsistency or discrepancy is to be brought to the attention of and resolved by the architect/designer.
- All dimensions are to be checked on site before commencing work.
- This drawing is to be coordinated with the Lead Consultant.


**Notes**

\* ALL DRAWINGS ARE FOR DESIGN INTENT ONLY AND ARE NOT FOR CONSTRUCTION. THE APPOINTED CONTRACTOR SHOULD PROVIDE SHOP DRAWING FOR APPROVAL.

\* CONTRACTOR TO DO A SITE SURVEY TO SPECIFY CORRECT QUANTITY & DIMENSIONS AS PER SITE MEASUREMENTS & DRAWINGS.

\* CONTRACTOR TO CHECK THE MECHANISM & FUNCTIONALITY OF THE DESIGN INTEND.

\* MATERIAL MUST BE PRESENTED TO PRIOR TO PURCHASE FOR TO APPROVE.

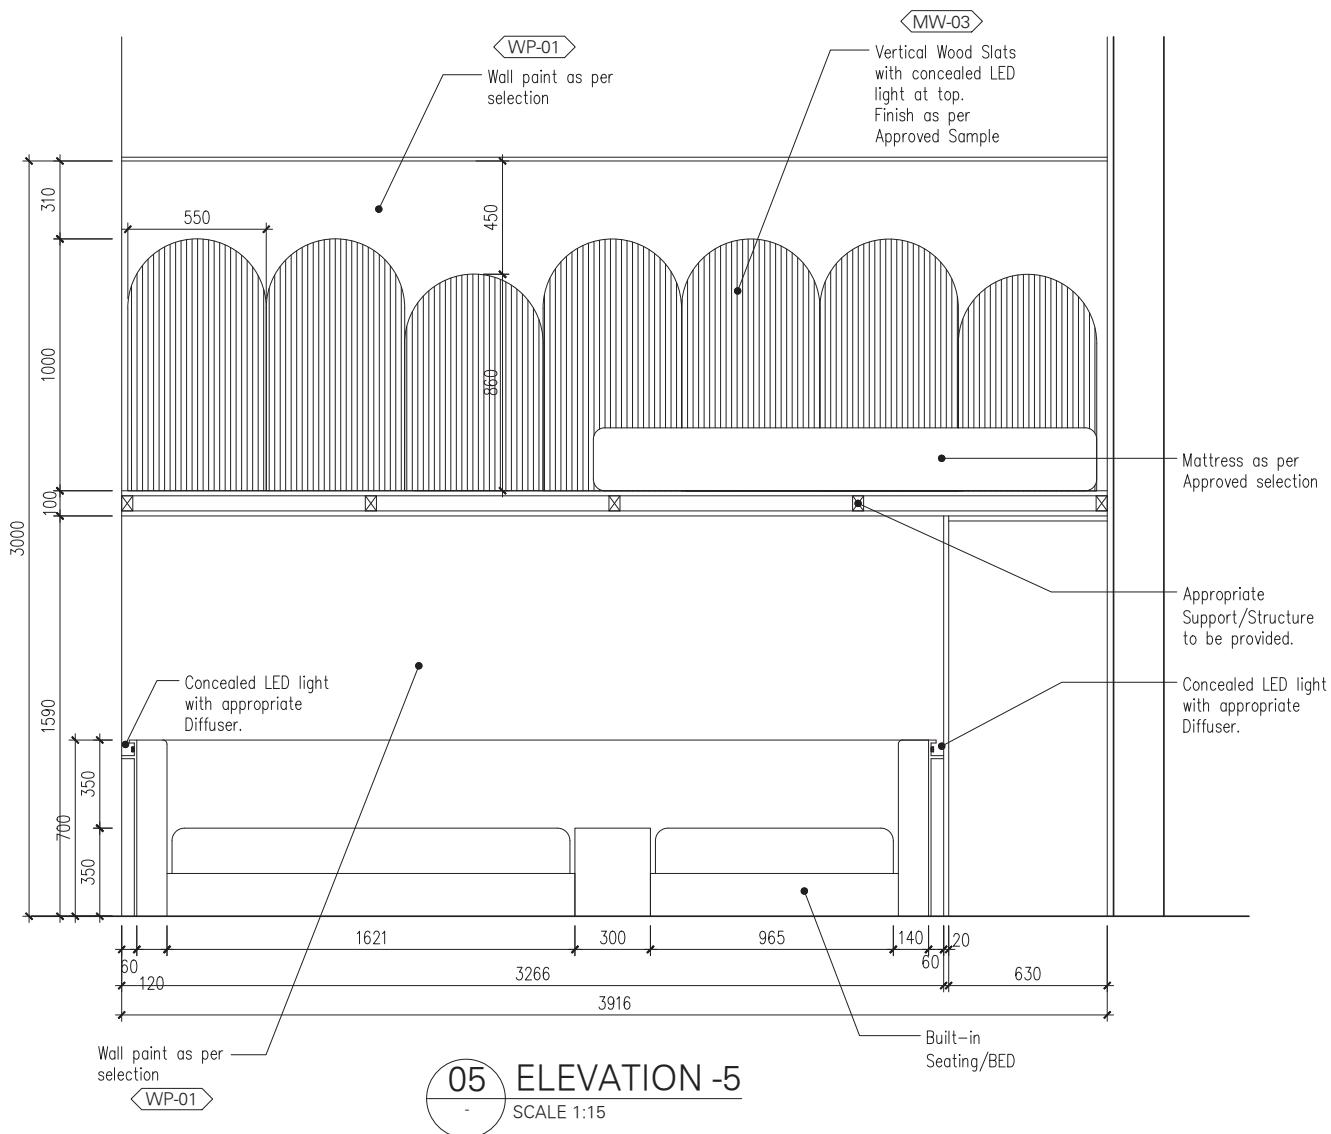

0	2025.05.21	mp	Initial issue
Rev	Date	Drawn	Revisions

**Design Architect:**

**Client:** Zach-Aimee  
**Project Title:** Private Villa -Dubai Hills


**Location:** Dubai, U.A.E.

**Plot Area:** 0000.00 Sqm  
0000.00 SqFt  
**Old Gate Level:** 0.00 = 0.000  
**NEW GATE LEVEL = 0.000**  
Proposed Gate Level is to be 000 mm above existing Asphalt Road Level

<b>Sheet Contents:</b>			
FIRST FLOOR ABRIELLA BEDROOM ELEVATION-5			
Designed by:	Drawn By:	Checked By:	Issued By:
ab	mp	ab	ab

**Scale:** 1:15      **Sheet Size:** A1      **Stage:** Conceptual Stage  
**Rev No:** 0


**Drwg No.** ID-302-6

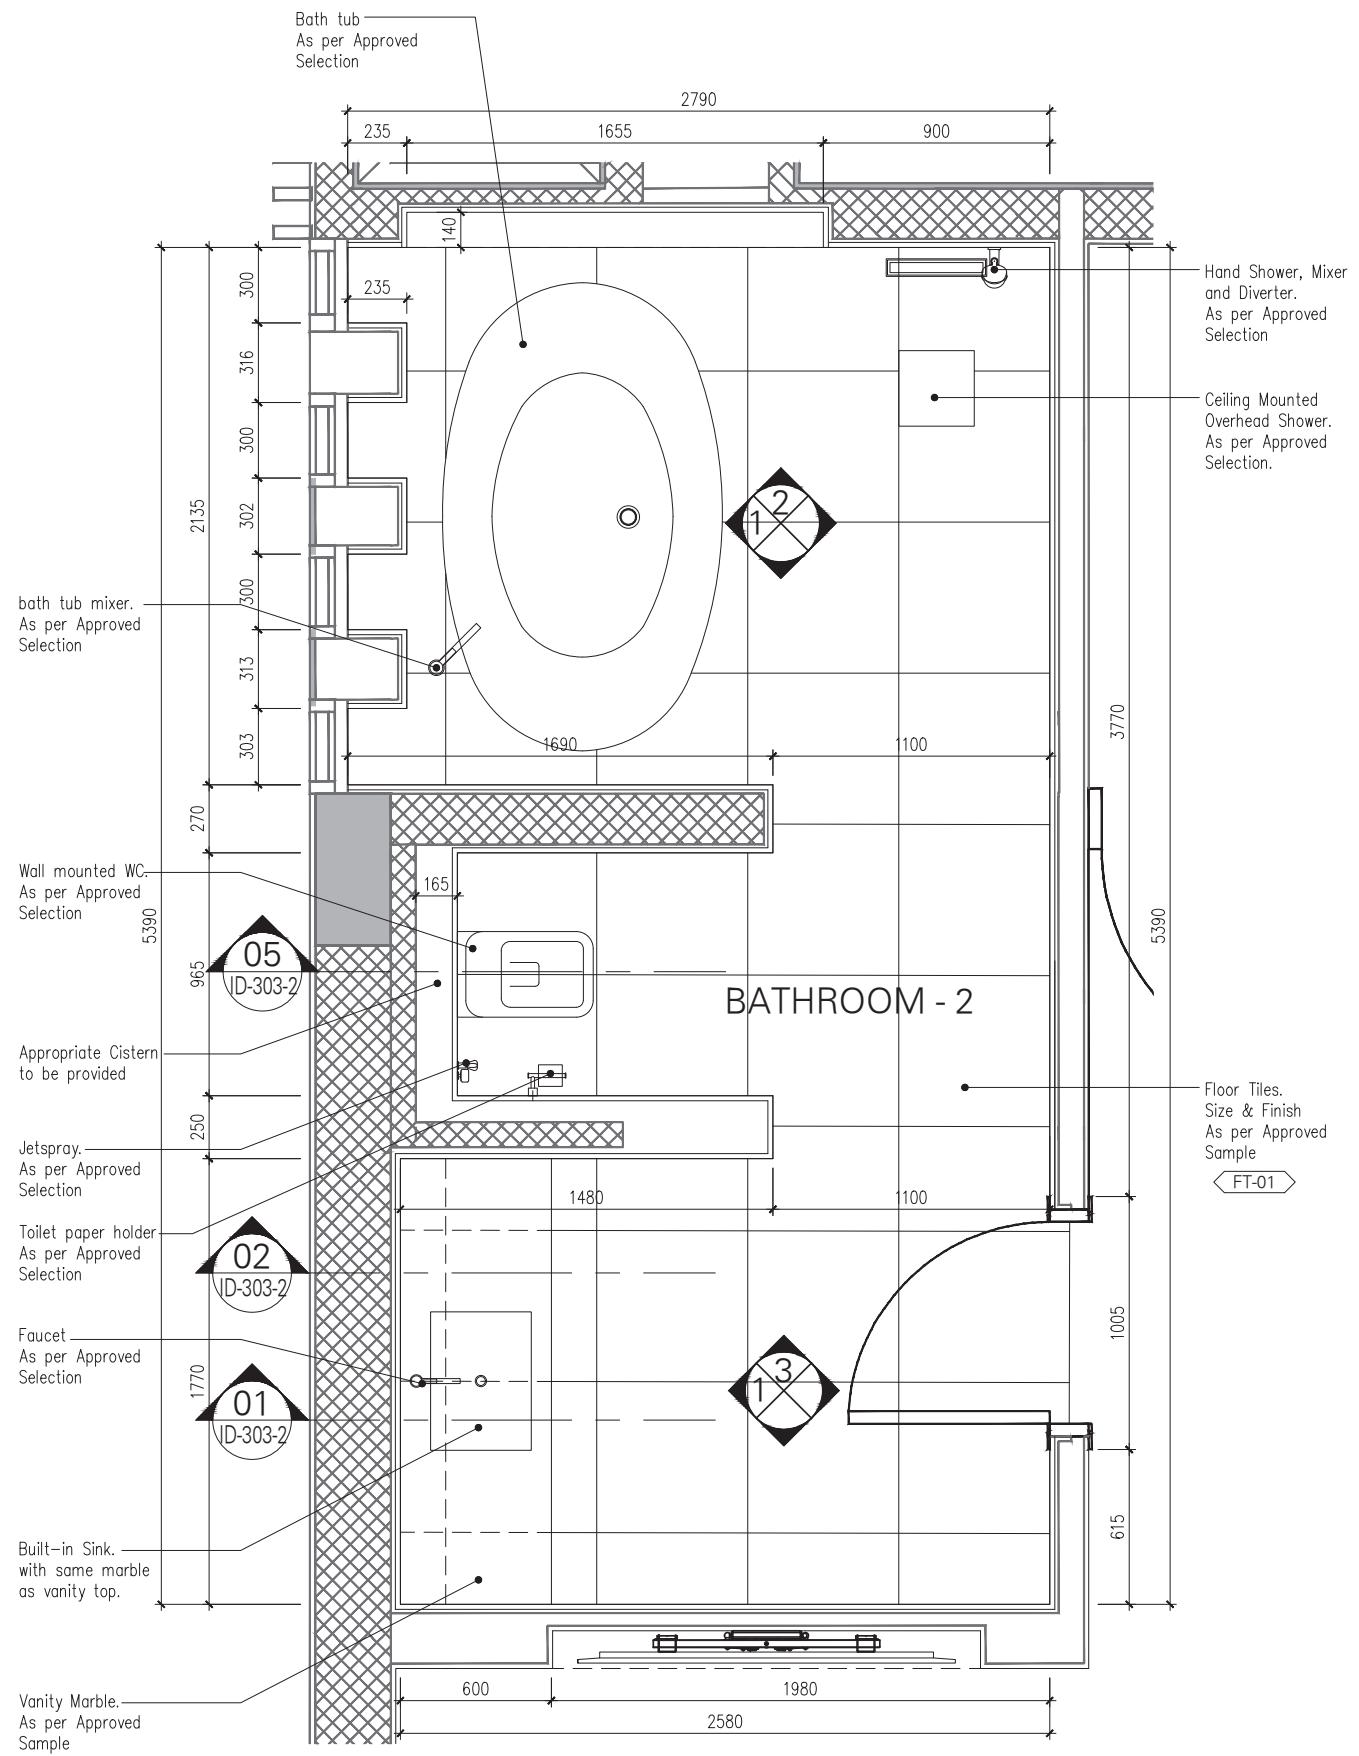

**01 FIRST FLOOR - ANABELLA BATHROOM - PLAN**

---

SCALE 1:25

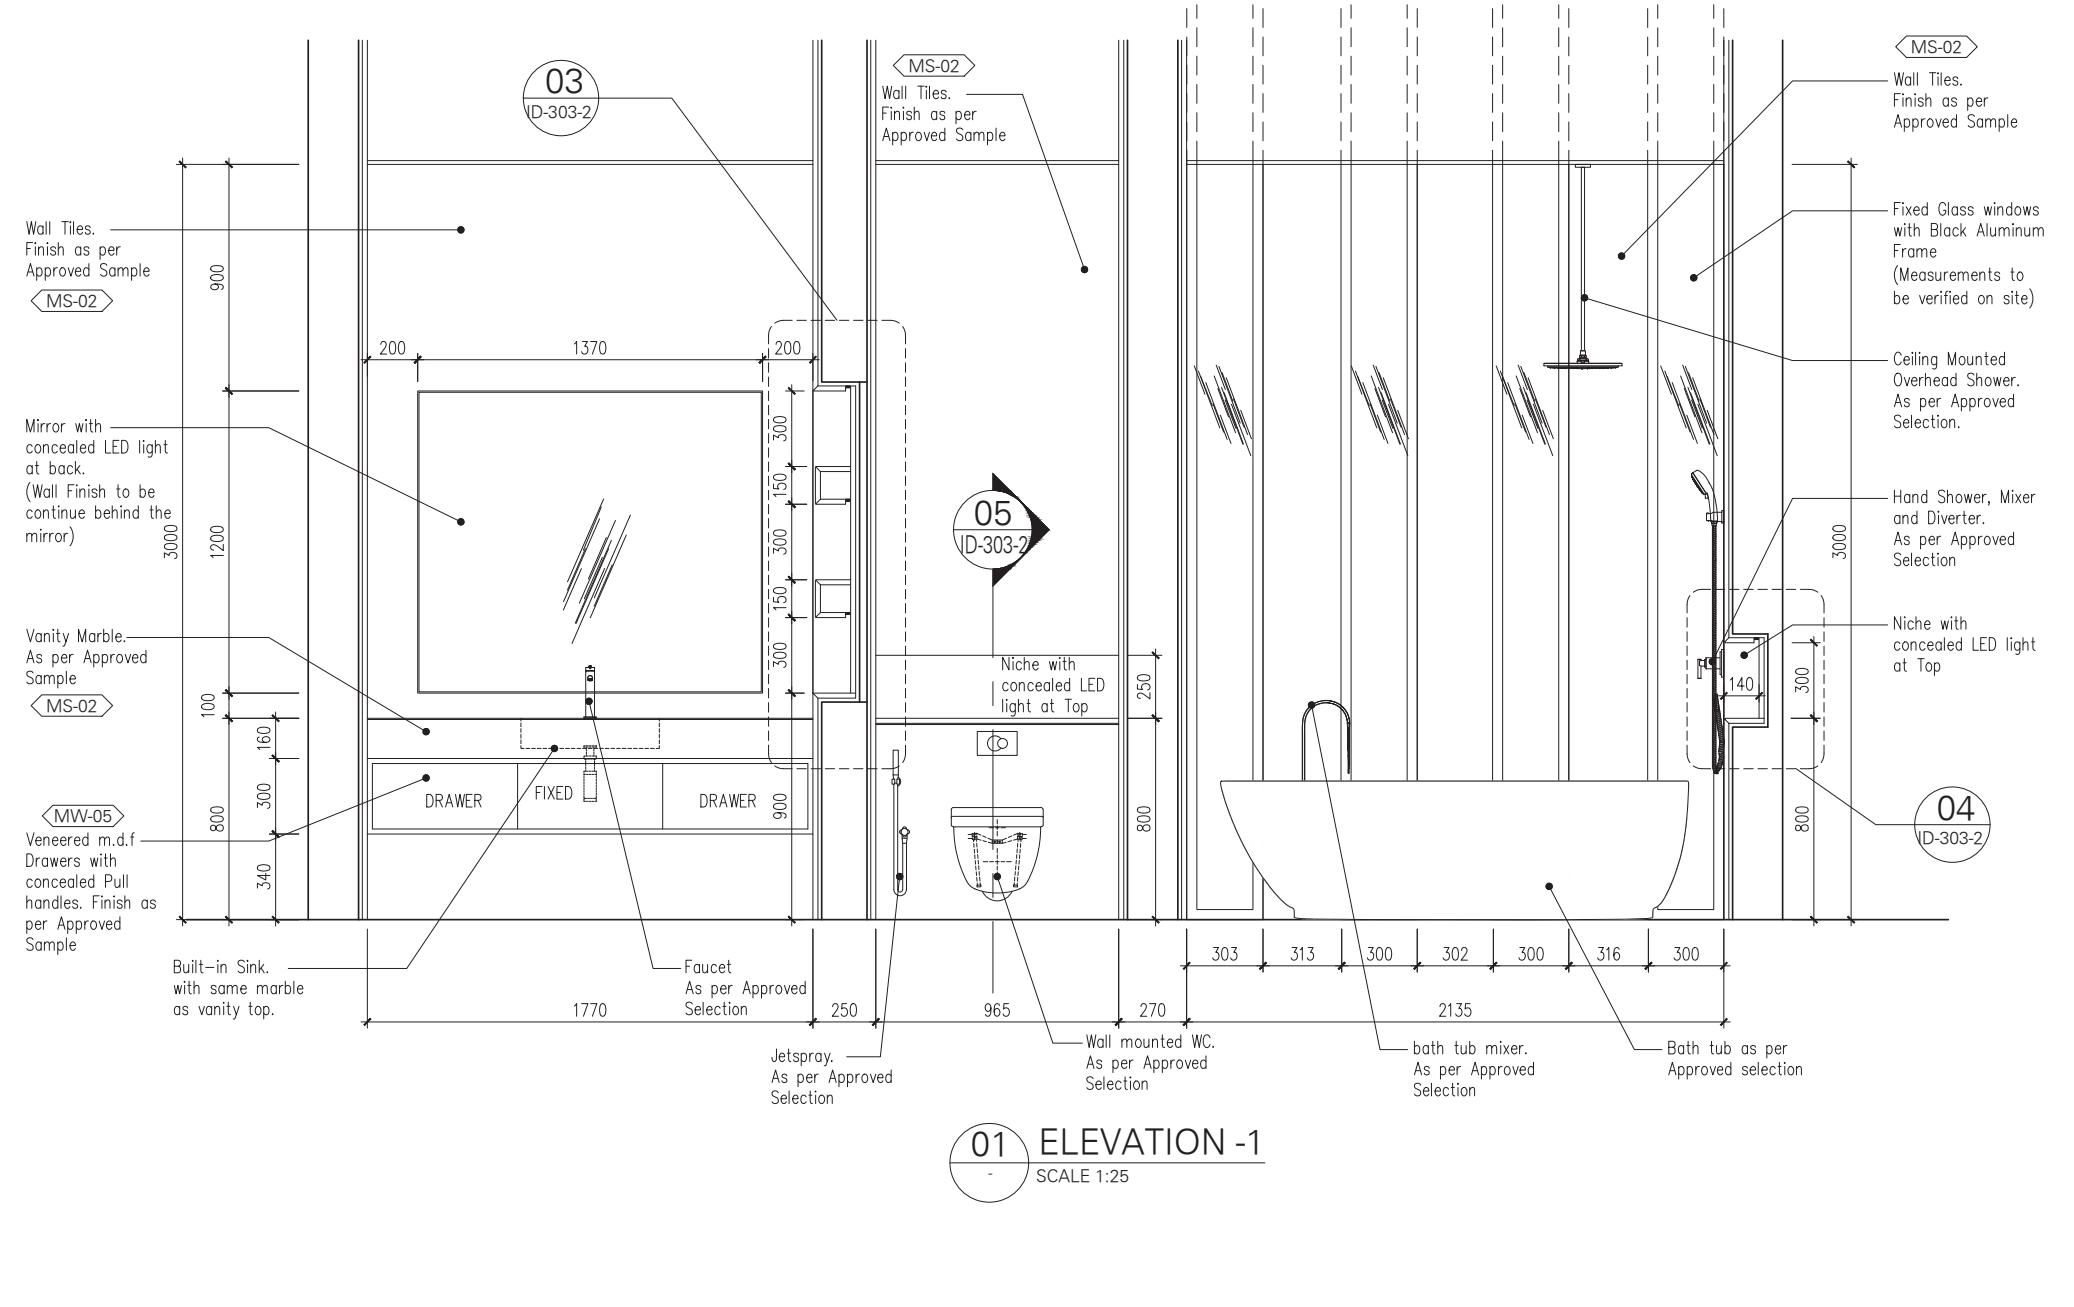

**General Notes:**

1. All dimensions are in millimeters unless otherwise noted.
2. Any inconsistency or discrepancy is to be brought to the attention of and resolved by the architect/designer.
3. All dimensions are to be checked on site before commencing work.
4. This drawing is to be coordinated with the Lead Consultant.

## Notes

\* ALL DRAWINGS ARE FOR DESIGN INTENT ONLY AND ARE NOT FOR CONSTRUCTION. THE APPOINTED CONTRACTOR SHOULD PROVIDE SHOP DRAWING FOR APPROVAL.

\* CONTRACTOR TO DO A SITE SURVEY  
TO SPECIFY CORRECT QUANTITY &  
DIMENSIONS AS PER SITE MEASUREMENTS  
& DRAWINGS.

\* CONTRACTOR TO CHECK THE MECHANISM & FUNCTIONALITY OF THE DESIGN INTEND.

\* MATERIAL MUST BE PRESENTED TO PRIOR  
TO PURCHASE FOR TO APPROVE.

Rev | Date

Zach-Aimee

**Project Title:**

## Private Villa -Dubai Hills

**Location:**

Dubai, U.A.E.

Plot Area: 0000.00 Sqm  
0000.00 SqFt  
Old Gate Level: 0.00 = 0.000  
NEW GATE LEVEL = 0.000  
Proposed Gate Level is to be 000 mm above existing Asphalt Road Level

**Sheet Contents:**

**FIRST FLOOR**  
**ABRIELLA BATHROOM**  
**ELEVATION-01**

Scale:	Sheet Size:	Stage:	Re
1:25	A1	Conceptual Stage	



VISUALI - 1

**General Notes:**

- All dimensions are in millimeters unless otherwise noted.
- Any inconsistency or discrepancy is to be brought to the attention of and resolved by the architect/designer.
- All dimensions are to be checked on site before commencing work.
- This drawing is to be coordinated with the Lead Consultant.

**Notes**

- \* ALL DRAWINGS ARE FOR DESIGN INTENT ONLY AND ARE NOT FOR CONSTRUCTION. THE APPOINTED CONTRACTOR SHOULD PROVIDE SHOP DRAWING FOR APPROVAL.
- \* CONTRACTOR TO DO A SITE SURVEY TO SPECIFY CORRECT QUANTITY & DIMENSIONS AS PER SITE MEASUREMENTS & DRAWINGS.
- \* CONTRACTOR TO CHECK THE MECHANISM & FUNCTIONALITY OF THE DESIGN INTEND.
- \* MATERIAL MUST BE PRESENTED TO PRIOR TO PURCHASE FOR TO APPROVE.

0	2025.05.21	mp	Initial issue
Rev	Date	Drawn	Revisions

**Design Architect:**

**Client:** Zach-Aimee  
**Project Title:** Private Villa -Dubai Hills

**Location:** Dubai, U.A.E.

**Plot Area:** 0000.00 Sqm  
0000.00 SqFt  
**Old Gate Level:** 0.00 = 0.000  
**NEW GATE LEVEL = 0.000**  
Proposed Gate Level is to be 000 mm above existing Asphalt Road Level

<b>Sheet Contents:</b>			
FIRST FLOOR ABRIELLA BATHROOM VISUAL - 1			
Designed by:	Drawn By:	Checked By:	Issued By:
ab	mp	ab	ab

**Scale:** 1:25      **Sheet Size:** A1      **Stage:** Conceptual Stage  
Rev No: 0

**Drwg No.** ID-303-2-R

**General Notes:**

- All dimensions are in millimeters unless otherwise noted.
- Any inconsistency or discrepancy is to be brought to the attention of and resolved by the architect/designer.
- All dimensions are to be checked on site before commencing work.
- This drawing is to be coordinated with the Lead Consultant.


**Notes**

\* ALL DRAWINGS ARE FOR DESIGN INTENT ONLY AND ARE NOT FOR CONSTRUCTION. THE APPOINTED CONTRACTOR SHOULD PROVIDE SHOP DRAWING FOR APPROVAL.

\* CONTRACTOR TO DO A SITE SURVEY TO SPECIFY CORRECT QUANTITY & DIMENSIONS AS PER SITE MEASUREMENTS & DRAWINGS.

\* CONTRACTOR TO CHECK THE MECHANISM & FUNCTIONALITY OF THE DESIGN INTEND.

\* MATERIAL MUST BE PRESENTED TO PRIOR TO PURCHASE FOR TO APPROVE.

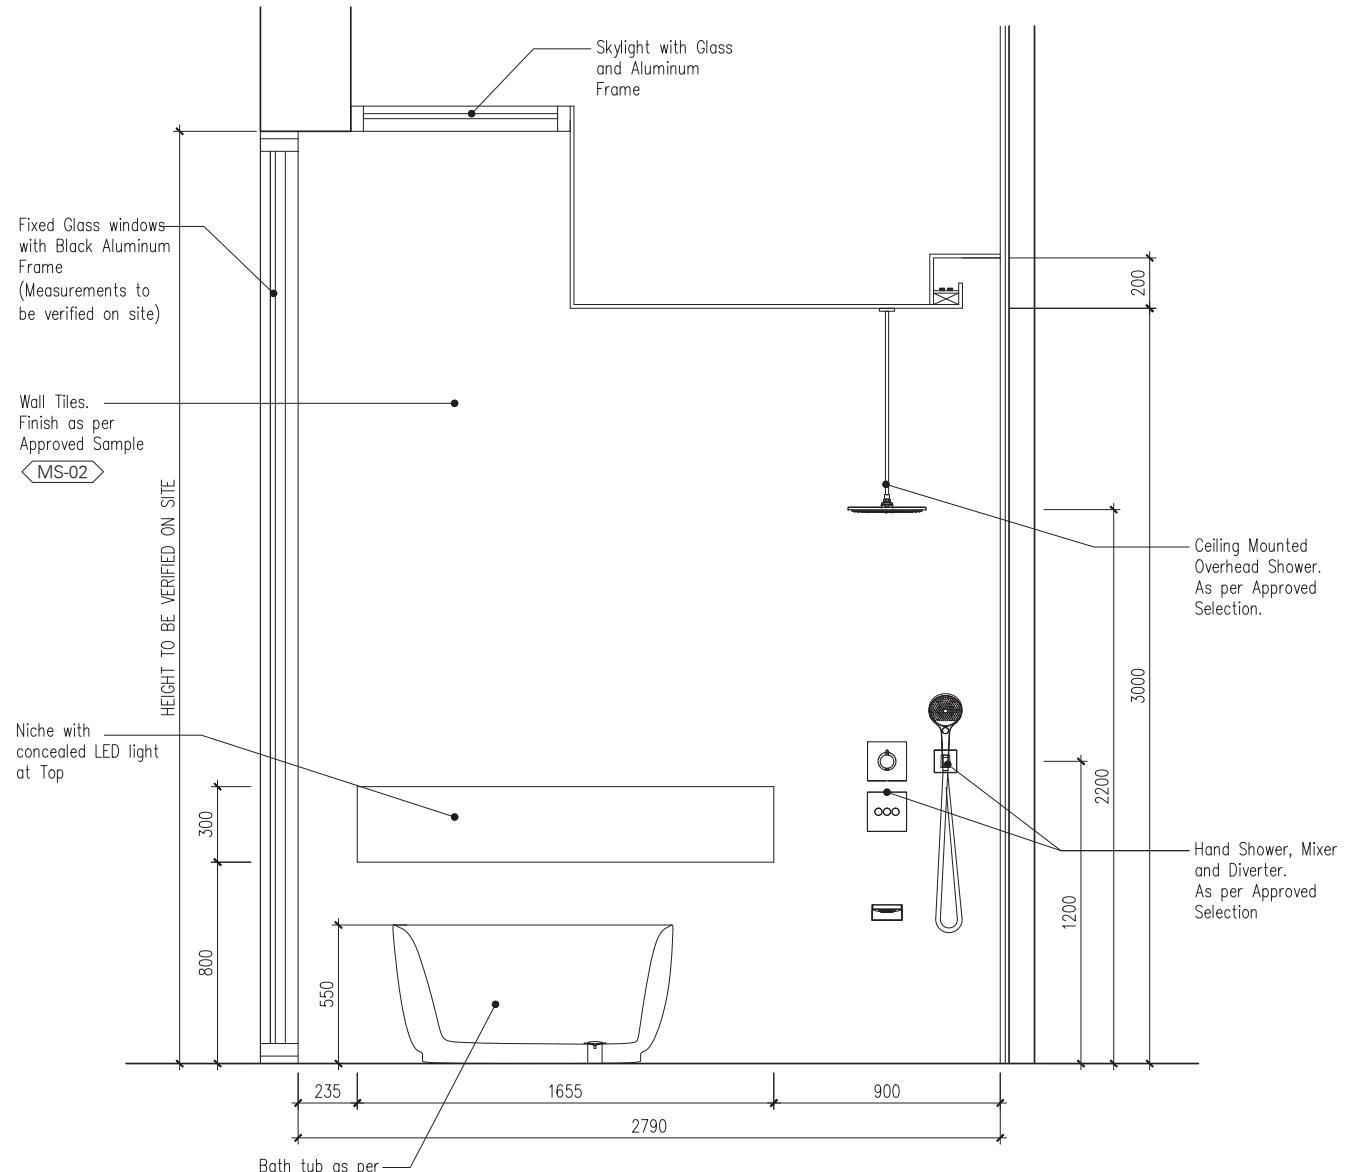

02 ELEVATION -2  
SCALE 1:25

0	2025.05.21	mp	Initial issue
Rev	Date	Drawn	Revisions

**Design Architect:**

**Client:**  
Zach-Aimee

**Project Title:**  
Private Villa -Dubai Hills


**Location:**  
Dubai, U.A.E.

**Plot Area:** 0000.00 Sqm  
0000.00 SqFt  
**Old Gate Level:** 0.00 = 0.000  
**NEW GATE LEVEL = 0.000**  
Proposed Gate Level is to be 000 mm above existing Asphalt Road Level

<b>Sheet Contents:</b>			
FIRST FLOOR ABRIELLA BATHROOM ELEVATION - 02			
Designed by:	Drawn By:	Checked By:	Issued By:
ab	mp	ab	ab

**Scale:** 1:25      **Sheet Size:** A1      **Stage:** Conceptual Stage  
Rev No: 0

**Drwg No.** ID-303-3

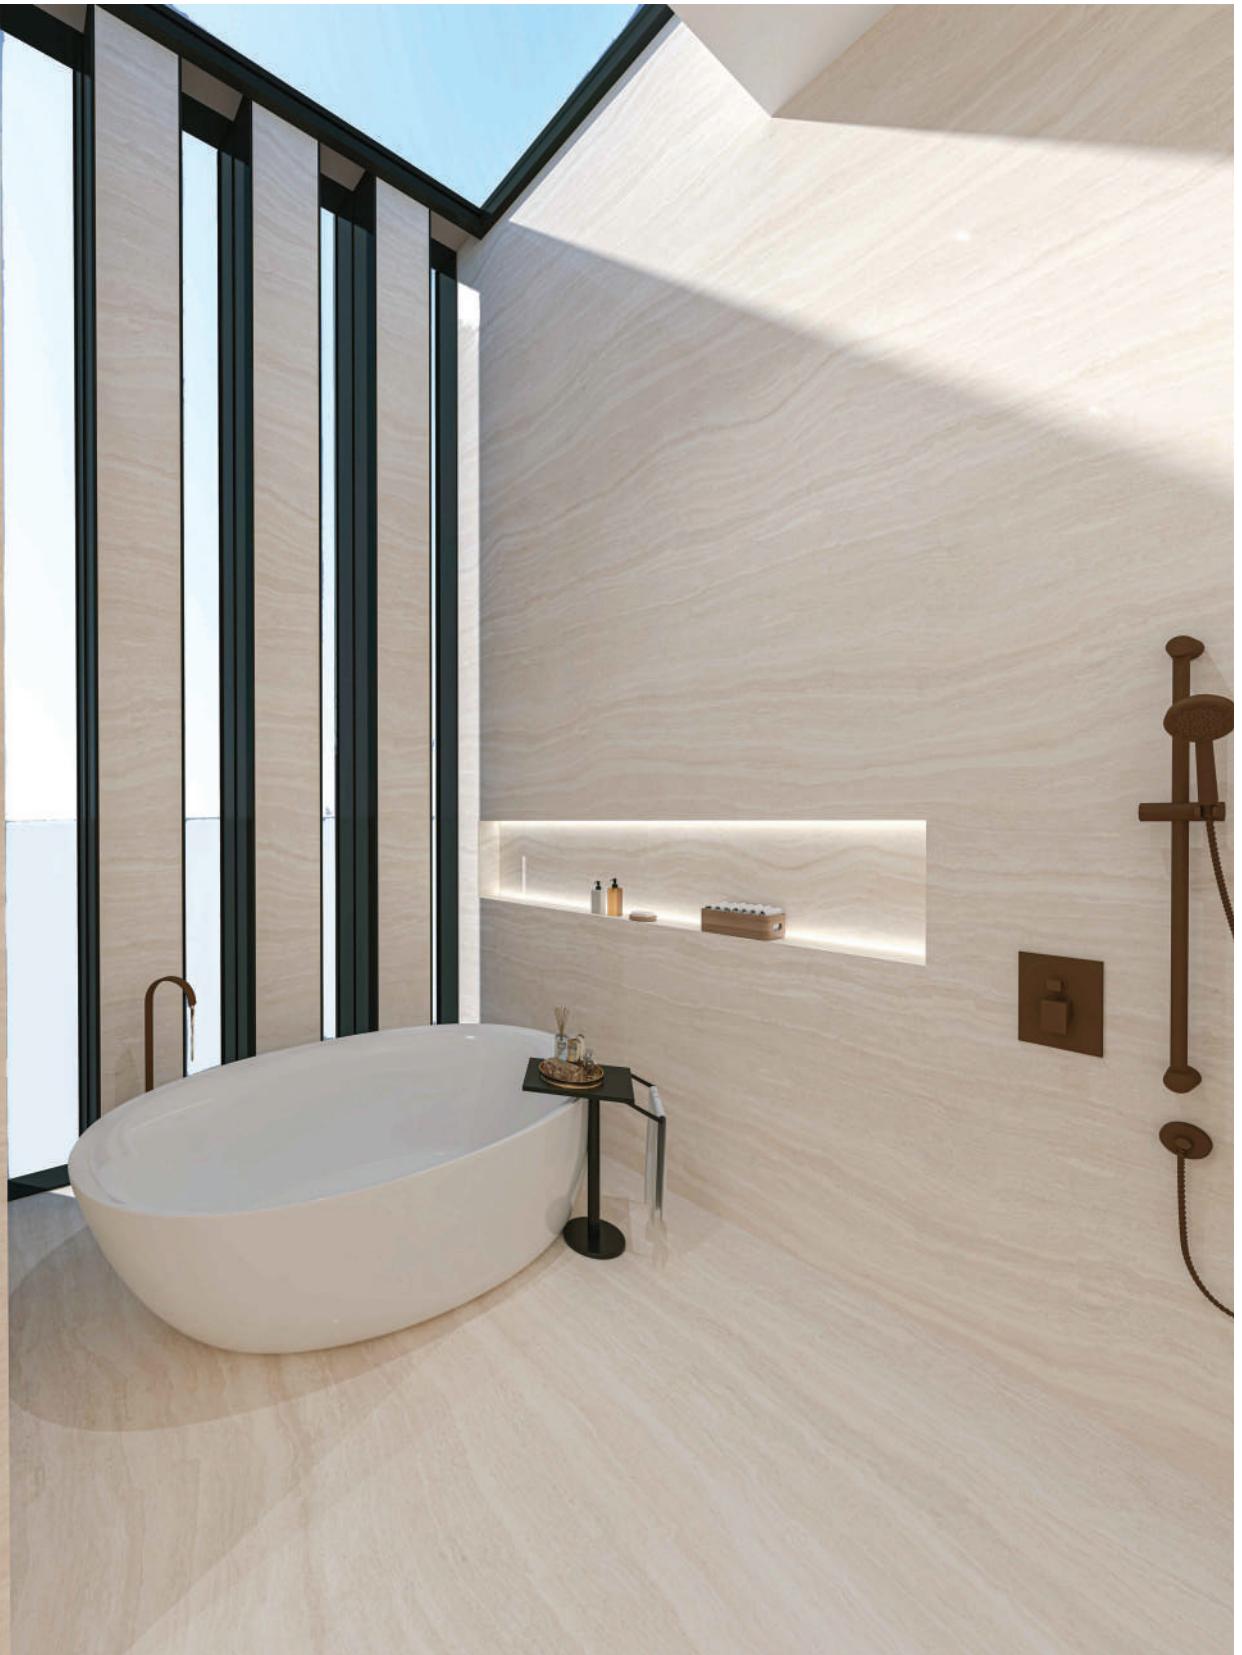

VISUALI - 3

**General Notes:**

- All dimensions are in millimeters unless otherwise noted.
- Any inconsistency or discrepancy is to be brought to the attention of and resolved by the architect/designer.
- All dimensions are to be checked on site before commencing work.
- This drawing is to be coordinated with the Lead Consultant.

**Notes**

- \* ALL DRAWINGS ARE FOR DESIGN INTENT ONLY AND ARE NOT FOR CONSTRUCTION. THE APPOINTED CONTRACTOR SHOULD PROVIDE SHOP DRAWING FOR APPROVAL.
- \* CONTRACTOR TO DO A SITE SURVEY TO SPECIFY CORRECT QUANTITY & DIMENSIONS AS PER SITE MEASUREMENTS & DRAWINGS.
- \* CONTRACTOR TO CHECK THE MECHANISM & FUNCTIONALITY OF THE DESIGN INTEND.
- \* MATERIAL MUST BE PRESENTED TO PRIOR TO PURCHASE FOR TO APPROVE.

0	2025.05.21	mp	Initial issue
Rev	Date	Drawn	Revisions

**Design Architect:**

**Client:** Zach-Aimee  
**Project Title:** Private Villa -Dubai Hills

**Location:** Dubai, U.A.E.

**Plot Area:** 0000.00 Sqm  
0000.00 SqFt  
**Old Gate Level:** 0.00 = 0.000  
**NEW GATE LEVEL = 0.000**  
Proposed Gate Level is to be 000 mm above existing Asphalt Road Level

<b>Sheet Contents:</b>			
FIRST FLOOR ABRIELLA BATHROOM VISUAL - 3			
Designed by:	Drawn By:	Checked By:	Issued By:
ab	mp	ab	ab

**Scale:** 1:25      **Sheet Size:** A1      **Stage:** Conceptual Stage  
**Rev No:** 0

**Drwg No.** ID-303-3-R



VISUALI - 2

**General Notes:**

- All dimensions are in millimeters unless otherwise noted.
- Any inconsistency or discrepancy is to be brought to the attention of and resolved by the architect/designer.
- All dimensions are to be checked on site before commencing work.
- This drawing is to be coordinated with the Lead Consultant.

**Notes**

- \* ALL DRAWINGS ARE FOR DESIGN INTENT ONLY AND ARE NOT FOR CONSTRUCTION. THE APPOINTED CONTRACTOR SHOULD PROVIDE SHOP DRAWING FOR APPROVAL.
- \* CONTRACTOR TO DO A SITE SURVEY TO SPECIFY CORRECT QUANTITY & DIMENSIONS AS PER SITE MEASUREMENTS & DRAWINGS.
- \* CONTRACTOR TO CHECK THE MECHANISM & FUNCTIONALITY OF THE DESIGN INTEND.
- \* MATERIAL MUST BE PRESENTED TO PRIOR TO PURCHASE FOR TO APPROVE.

0	2025.05.21	mp	Initial issue
Rev	Date	Drawn	Revisions

**Design Architect:**

**Client:**  
Zach-Aimee

**Project Title:**  
Private Villa -Dubai Hills


**Location:**  
Dubai, U.A.E.

**Plot Area:** 0000.00 Sqm  
0000.00 SqFt  
**Old Gate Level:** 0.00 = 0.000  
**NEW GATE LEVEL = 0.000**  
Proposed Gate Level is to be 000 mm above existing Asphalt Road Level

<b>Sheet Contents:</b>			
FIRST FLOOR ABRIELLA BATHROOM VISUAL - 2			
Designed by:	Drawn By:	Checked By:	Issued By:
ab	mp	ab	ab

**Scale:** Sheet Size: Stage:  
1:25 A1 Conceptual Stage: Rev No: 0

**Drwg No.** ID-303-2-R-2

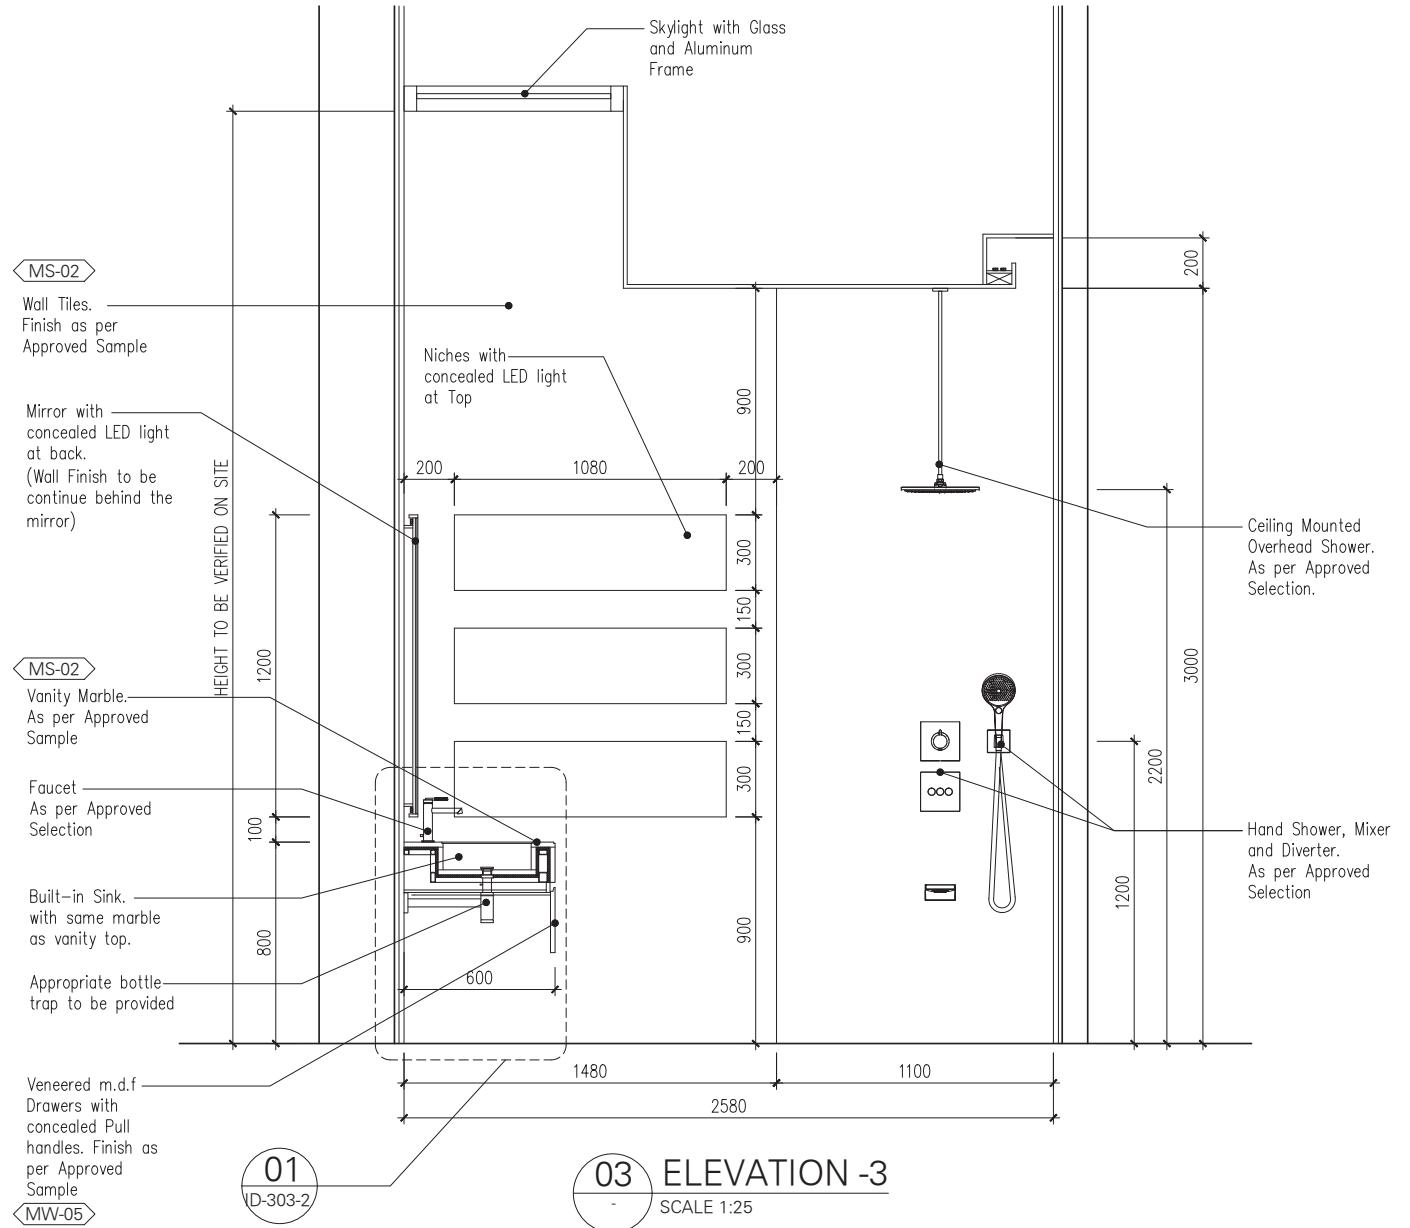

**General Notes:**

1. All dimensions are in millimeters unless otherwise noted.
2. Any inconsistency or discrepancy is to be brought to the attention of and resolved by the architect/designer.
3. All dimensions are to be checked on site before commencing work.
4. This drawing is to be coordinated with the Lead Consultant.

## Notes

\* ALL DRAWINGS ARE FOR DESIGN INTENT ONLY AND ARE NOT FOR CONSTRUCTION. THE APPOINTED CONTRACTOR SHOULD PROVIDE SHOP DRAWING FOR APPROVAL.

\* CONTRACTOR TO DO A SITE SURVEY  
TO SPECIFY CORRECT QUANTITY &  
DIMENSIONS AS PER SITE MEASUREMENTS  
& DRAWINGS.

\* CONTRACTOR TO CHECK THE MECHANISM & FUNCTIONALITY OF THE DESIGN INTEND.

\* MATERIAL MUST BE PRESENTED TO PRIOR  
TO PURCHASE FOR TO APPROVE.

## Design Architect:

Zach-Aimee

**Project Title:**

## Private Villa -Dubai Hills

**Location:**

Dubai, U.A.E.

Plot Area: 0000.00 Sqm  
0000.00 SqFt  
Old Gate Level: 0.00 = 0.000  
NEW GATE LEVEL = 0.000  
Proposed Gate Level is to be 000 mm above existing Asphalt Road Level

<b>FIRST FLOOR</b>			
<b>ABRIELLA BATHROOM</b>			
<b> ELEVATION - 03</b>			
<b>Designed by:</b>	<b>Drawn By:</b>	<b>Checked By:</b>	<b>Issued By:</b>
ob	mp	ab	ab
<b>Scale:</b>	<b>Sheet Size:</b>	<b>Stage:</b>	<b>Rev No:</b>

Drwg No. ID-303-4

**General Notes:**

- All dimensions are in millimeters unless otherwise noted.
- Any inconsistency or discrepancy is to be brought to the attention of and resolved by the architect/designer.
- All dimensions are to be checked on site before commencing work.
- This drawing is to be coordinated with the Lead Consultant.


**Notes**

\* ALL DRAWINGS ARE FOR DESIGN INTENT ONLY AND ARE NOT FOR CONSTRUCTION. THE APPOINTED CONTRACTOR SHOULD PROVIDE SHOP DRAWING FOR APPROVAL.

\* CONTRACTOR TO DO A SITE SURVEY TO SPECIFY CORRECT QUANTITY & DIMENSIONS AS PER SITE MEASUREMENTS & DRAWINGS.

\* CONTRACTOR TO CHECK THE MECHANISM & FUNCTIONALITY OF THE DESIGN INTEND.


\* MATERIAL MUST BE PRESENTED TO PRIOR TO PURCHASE FOR TO APPROVE.

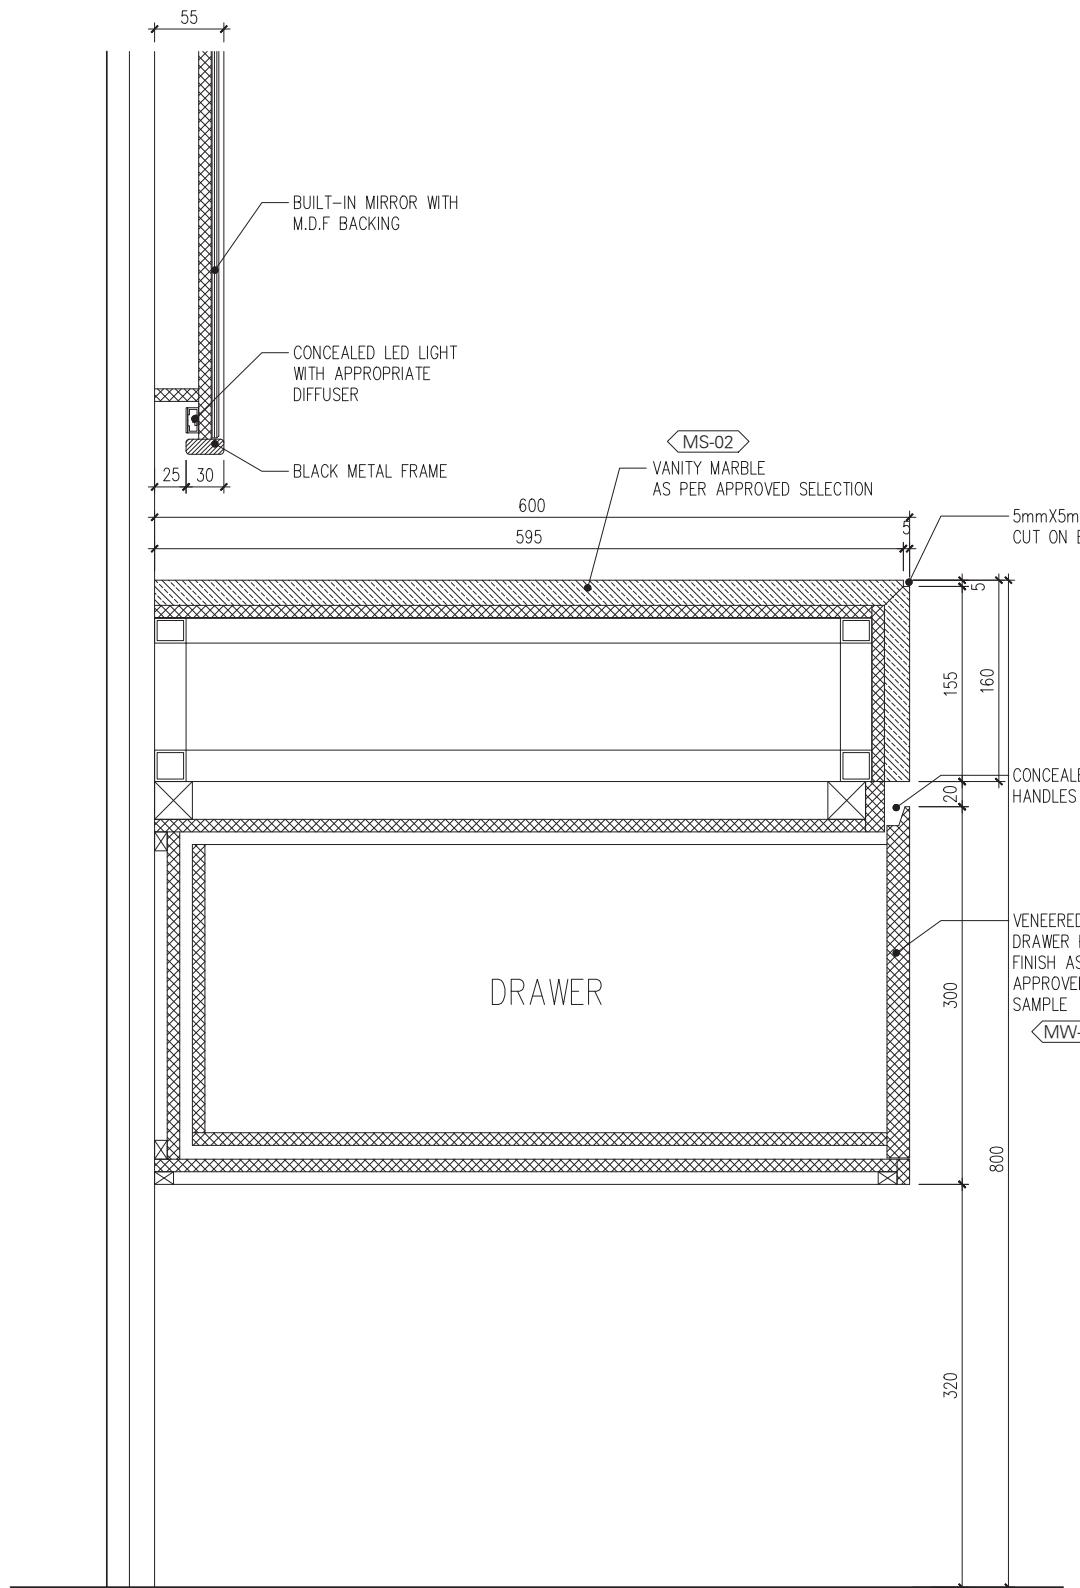

01

VANITY SECTION THROUGH DRAWERS

SCALE 1:3

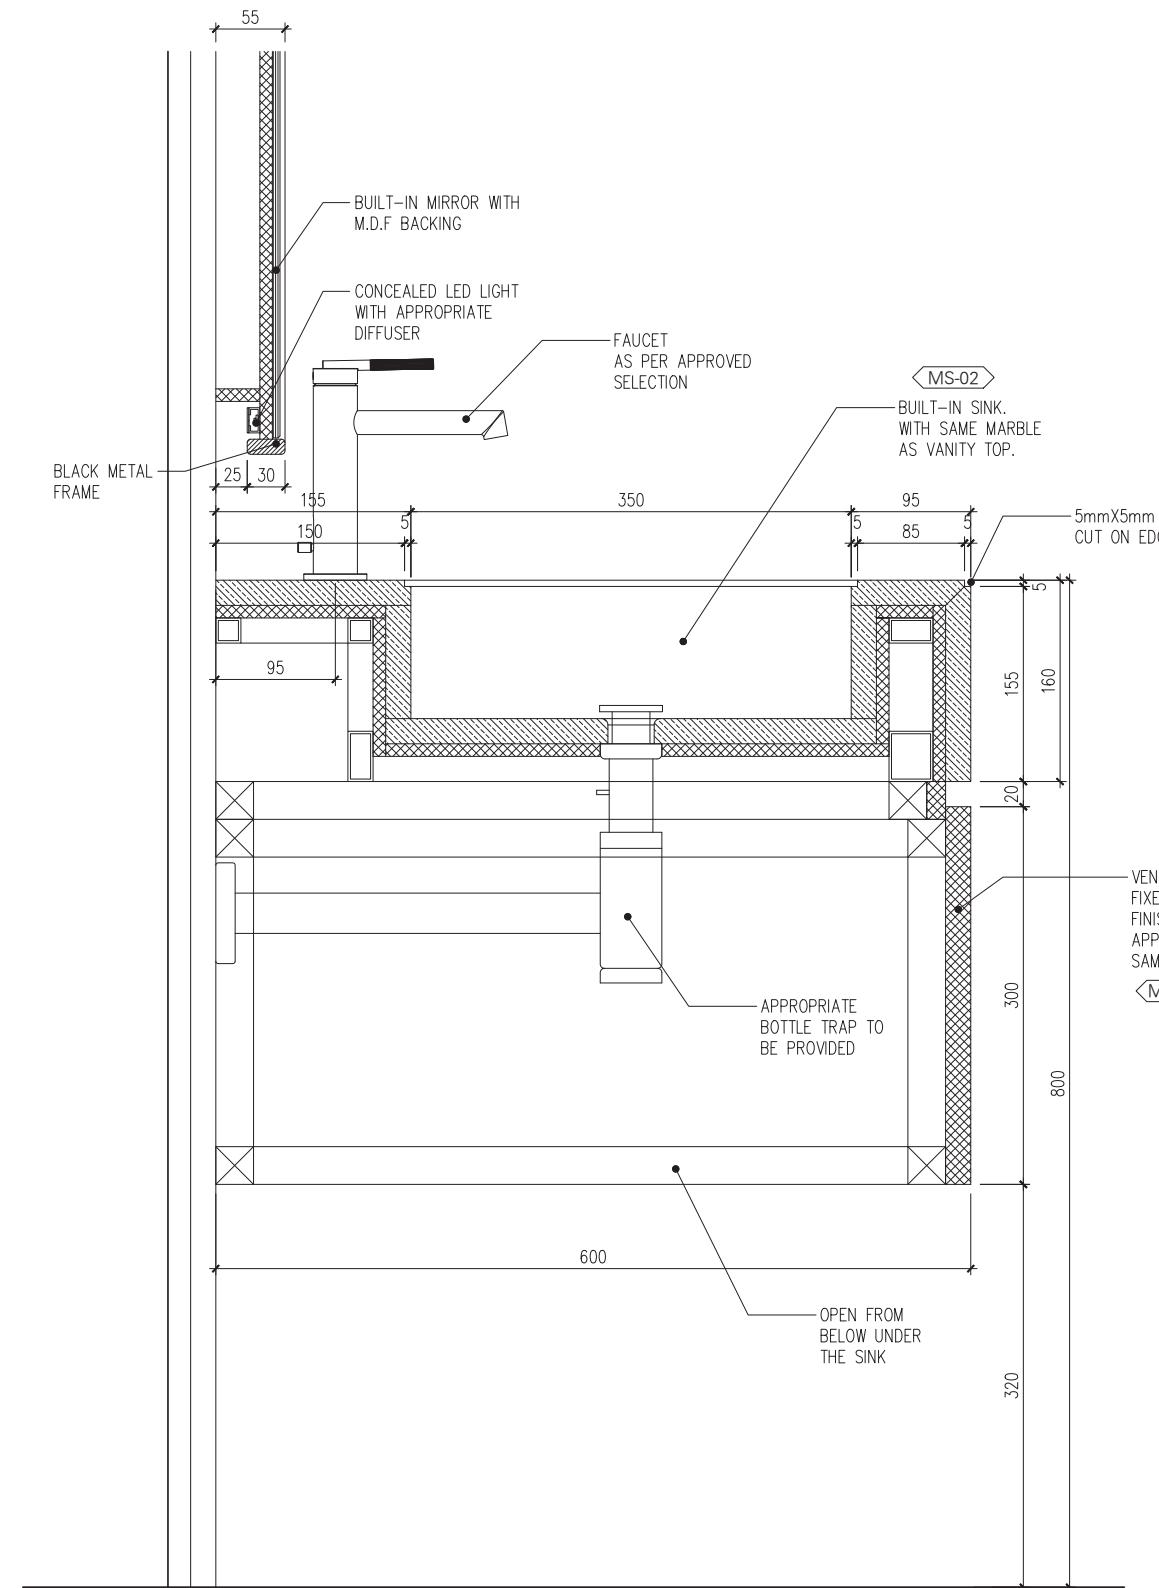

02

VANITY SECTION THROUGH SINK

SCALE 1:3

**Client:** Zach-Aimee  
**Project Title:** Private Villa -Dubai Hills  
**Location:** Dubai, U.A.E.

**Plot Area:** 0000.00 Sqm  
0000.00 SqFt  
**Old Gate Level:** 0.00 = 0.00  
**NEW GATE LEVEL = 0.000**  
Proposed Gate Level is to be 000 mm above existing Asphalt Road Level

**Sheet Contents:**  
FIRST FLOOR  
ABRIELLA BATHROOM  
VANITY DETAILS  
Designed by: Drawn By: Checked By: Issued By:  
ab mp ab ab  
Scale: Sheet Size: Stage: Rev No:  
1:25 A1 Conceptual Stage 0


**Drwg No.** ID-303-5

**General Notes:**

- All dimensions are in millimeters unless otherwise noted.
- Any inconsistency or discrepancy is to be brought to the attention of and resolved by the architect/designer.
- All dimensions are to be checked on site before commencing work.
- This drawing is to be coordinated with the Lead Consultant.

**Notes**

- \* ALL DRAWINGS ARE FOR DESIGN INTENT ONLY AND ARE NOT FOR CONSTRUCTION. THE APPOINTED CONTRACTOR SHOULD PROVIDE SHOP DRAWING FOR APPROVAL.
- \* CONTRACTOR TO DO A SITE SURVEY TO SPECIFY CORRECT QUANTITY & DIMENSIONS AS PER SITE MEASUREMENTS & DRAWINGS.
- \* CONTRACTOR TO CHECK THE MECHANISM & FUNCTIONALITY OF THE DESIGN INTEND.
- \* MATERIAL MUST BE PRESENTED TO PRIOR TO PURCHASE FOR TO APPROVE.

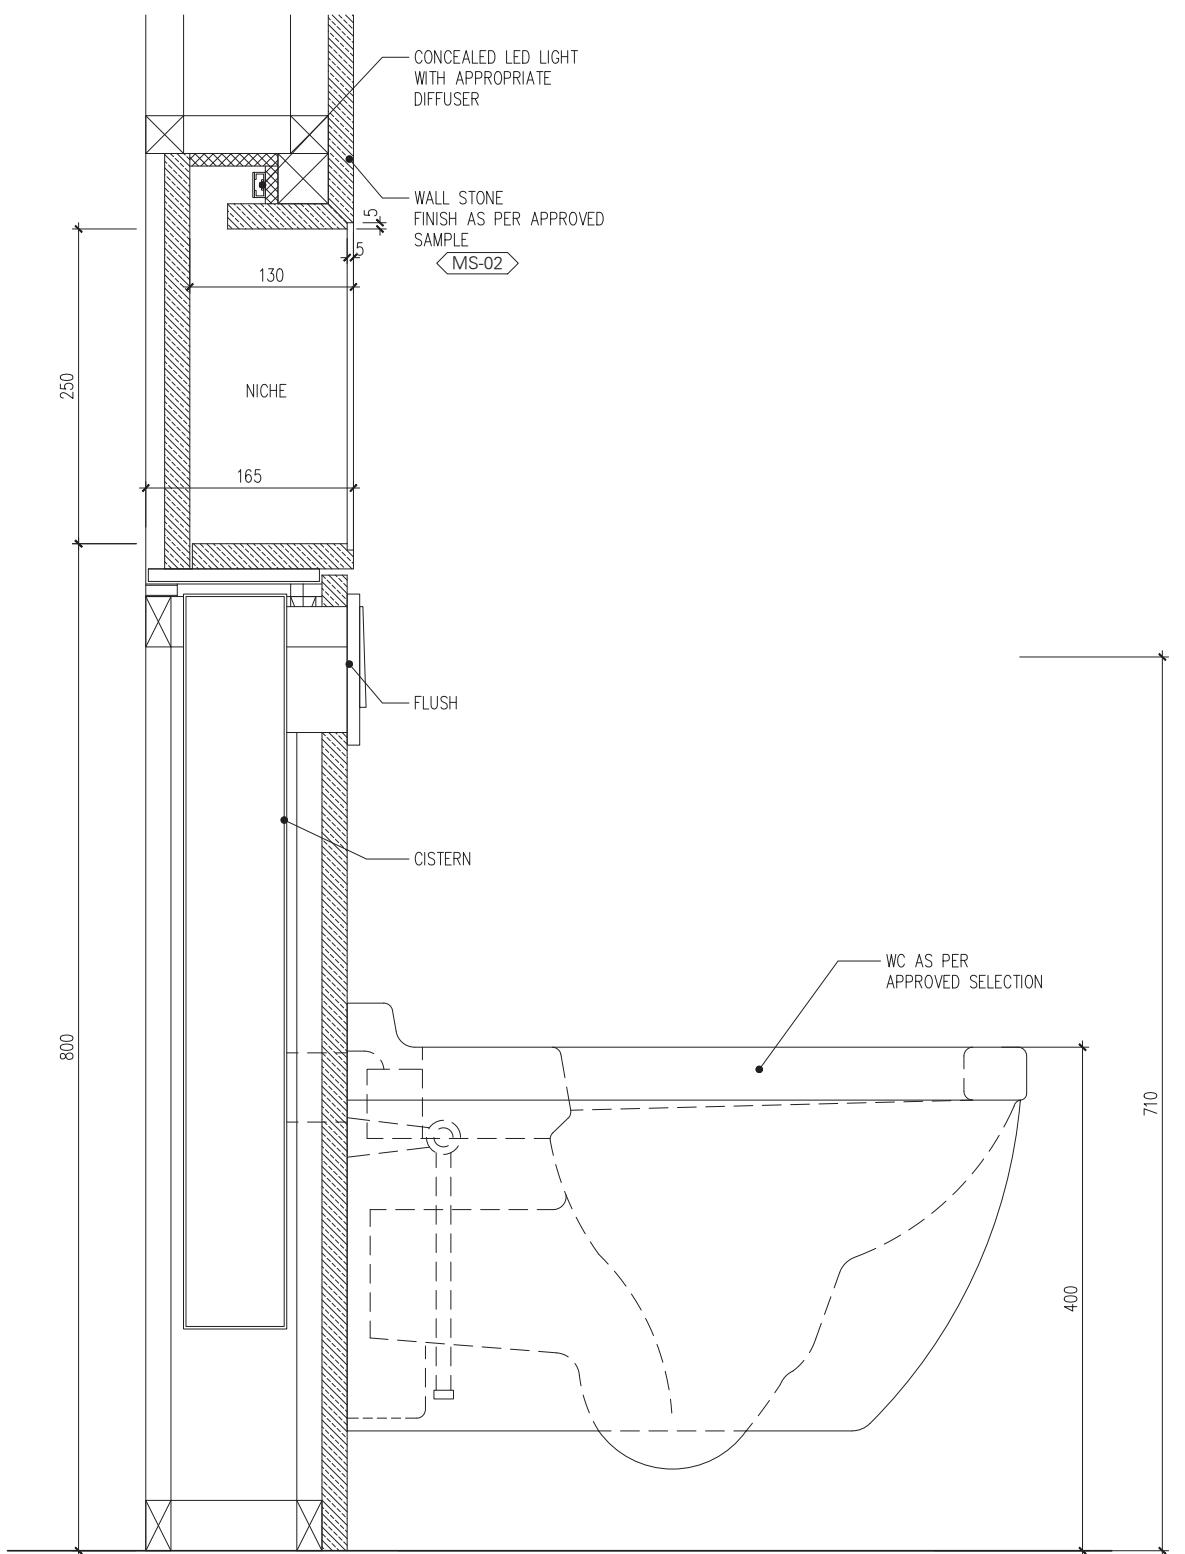

05

WC WITH CISTERN AND NICHE DETAIL

- SCALE 1:5

0	2025.05.21	mp	Initial issue
Rev	Date	Drawn	Revisions

**Design Architect:**

**Client:**  
Zach-Aimee

**Project Title:**  
Private Villa -Dubai Hills

**Location:**  
Dubai, U.A.E.

**Plot Area:** 0000.00 Sqm  
0000.00 SqFt  
**Old Gate Level:** 0.00 = 0.000  
**NEW GATE LEVEL = 0.000**  
Proposed Gate Level is to be 000 mm above existing Asphalt Road Level

<b>Sheet Contents:</b>			
FIRST FLOOR ABRIELLA BATHROOM WC DETAILS			
Designed by:	Drawn By:	Checked By:	Issued By:
ab	mp	ab	ab



**Drwg No.** ID-303-6

**General Notes:**


- All dimensions are in millimeters unless otherwise noted.
- Any inconsistency or discrepancy is to be brought to the attention of and resolved by the architect/designer.
- All dimensions are to be checked on site before commencing work.
- This drawing is to be coordinated with the Lead Consultant.

**Notes**

- \* ALL DRAWINGS ARE FOR DESIGN INTENT ONLY AND ARE NOT FOR CONSTRUCTION. THE APPOINTED CONTRACTOR SHOULD PROVIDE SHOP DRAWING FOR APPROVAL.
- \* CONTRACTOR TO DO A SITE SURVEY TO SPECIFY CORRECT QUANTITY & DIMENSIONS AS PER SITE MEASUREMENTS & DRAWINGS.
- \* CONTRACTOR TO CHECK THE MECHANISM & FUNCTIONALITY OF THE DESIGN INTEND.
- \* MATERIAL MUST BE PRESENTED TO PRIOR TO PURCHASE FOR TO APPROVE.

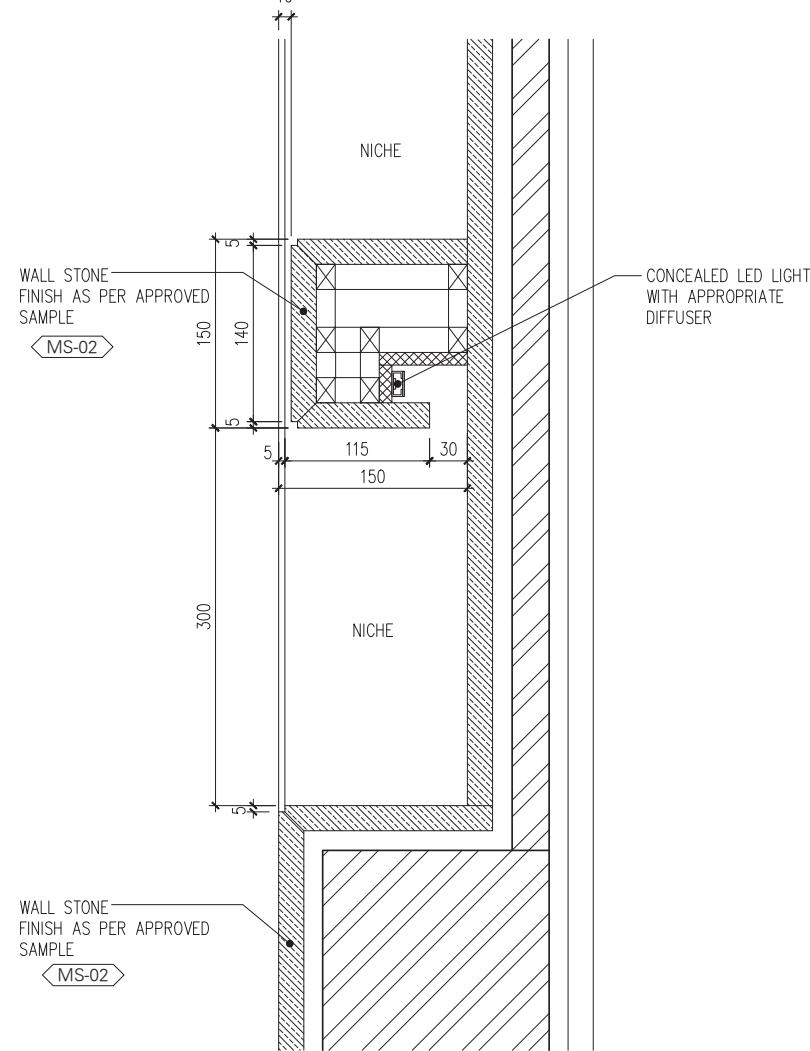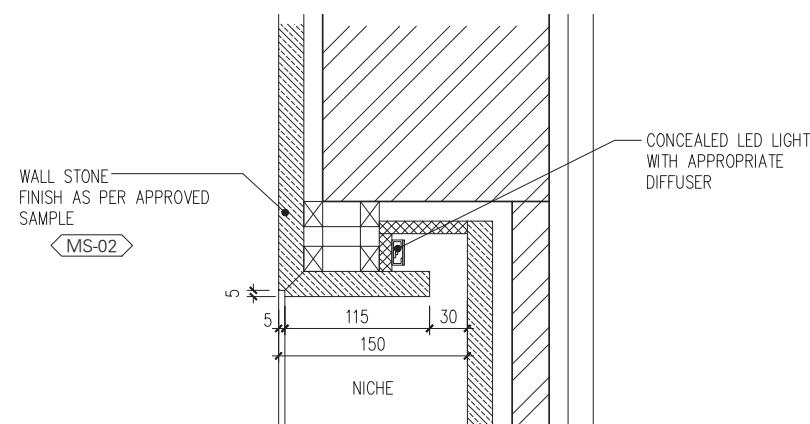

03 NICHE DETAIL  
SCALE 1:3

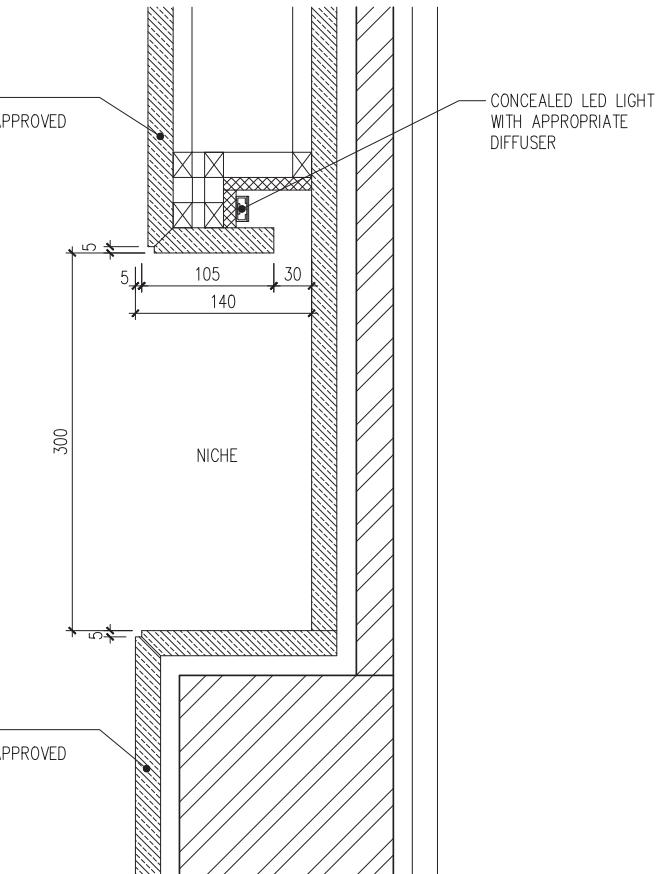

04 NICHE DETAIL  
SCALE 1:3

0	2025.05.21	mp	Initial issue
Rev	Date	Drawn	Revisions

**Design Architect:**

**Client:** Zach-Aimee  
**Project Title:** Private Villa -Dubai Hills

**Location:** Dubai, U.A.E.  
**Plot Area:** 0000.00 Sqm  
0000.00 SqFt  
**Old Gate Level:** 0.00 = 0.000  
**NEW GATE LEVEL = 0.000**

Proposed Gate Level is to be 000 mm above existing Asphalt Road Level  
**Sheet Contents:**  
FIRST FLOOR  
ABRIELLA BATHROOM  
NICHE DETAILS

Designed by:	Drawn By:	Checked By:	Issued By:
ab	mp	ab	ab
Scale:	Sheet Size:	Stage:	Rev No:

**Drwg No.** ID-303-7

**General Notes:**

- All dimensions are in millimeters unless otherwise noted.
- Any inconsistency or discrepancy is to be brought to the attention of and resolved by the architect/designer.
- All dimensions are to be checked on site before commencing work.
- This drawing is to be coordinated with the Lead Consultant.


**Notes**

\* ALL DRAWINGS ARE FOR DESIGN INTENT ONLY AND ARE NOT FOR CONSTRUCTION. THE APPOINTED CONTRACTOR SHOULD PROVIDE SHOP DRAWING FOR APPROVAL.


\* CONTRACTOR TO DO A SITE SURVEY TO SPECIFY CORRECT QUANTITY & DIMENSIONS AS PER SITE MEASUREMENTS & DRAWINGS.

\* CONTRACTOR TO CHECK THE MECHANISM & FUNCTIONALITY OF THE DESIGN INTEND.

\* MATERIAL MUST BE PRESENTED TO PRIOR TO PURCHASE FOR TO APPROVE.

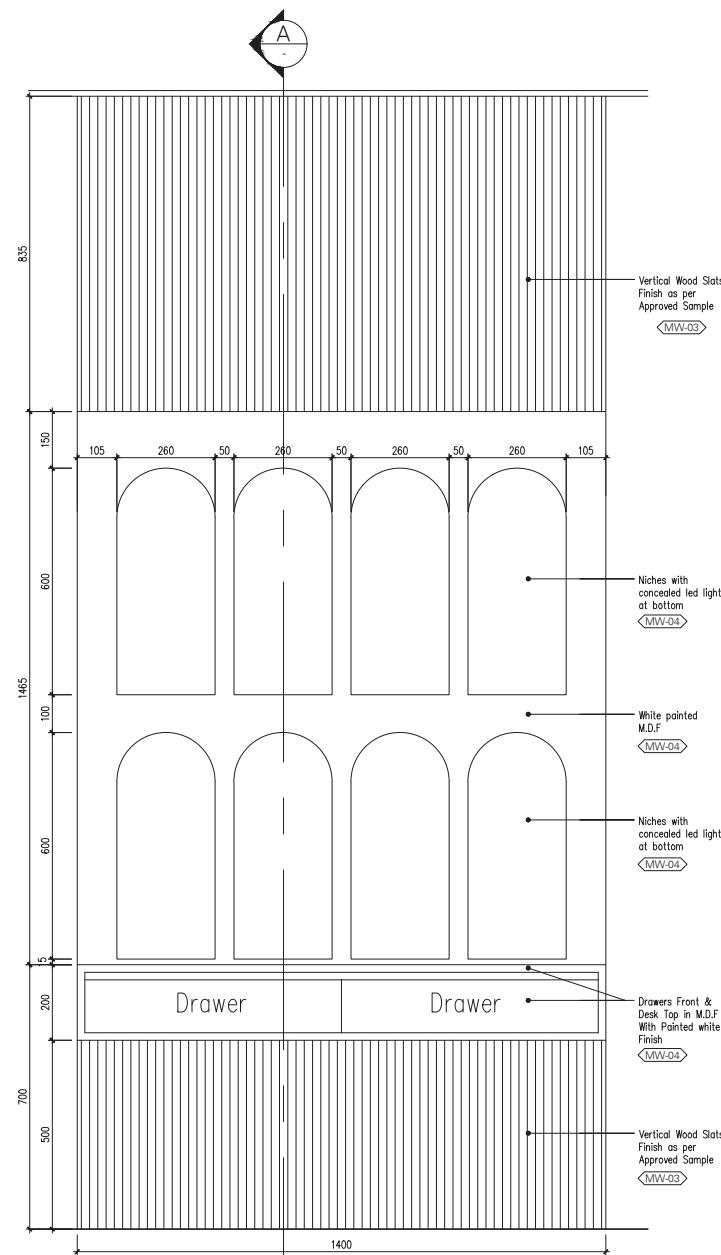

01 ELEVATION DETAIL -1  
SCALE 1:10

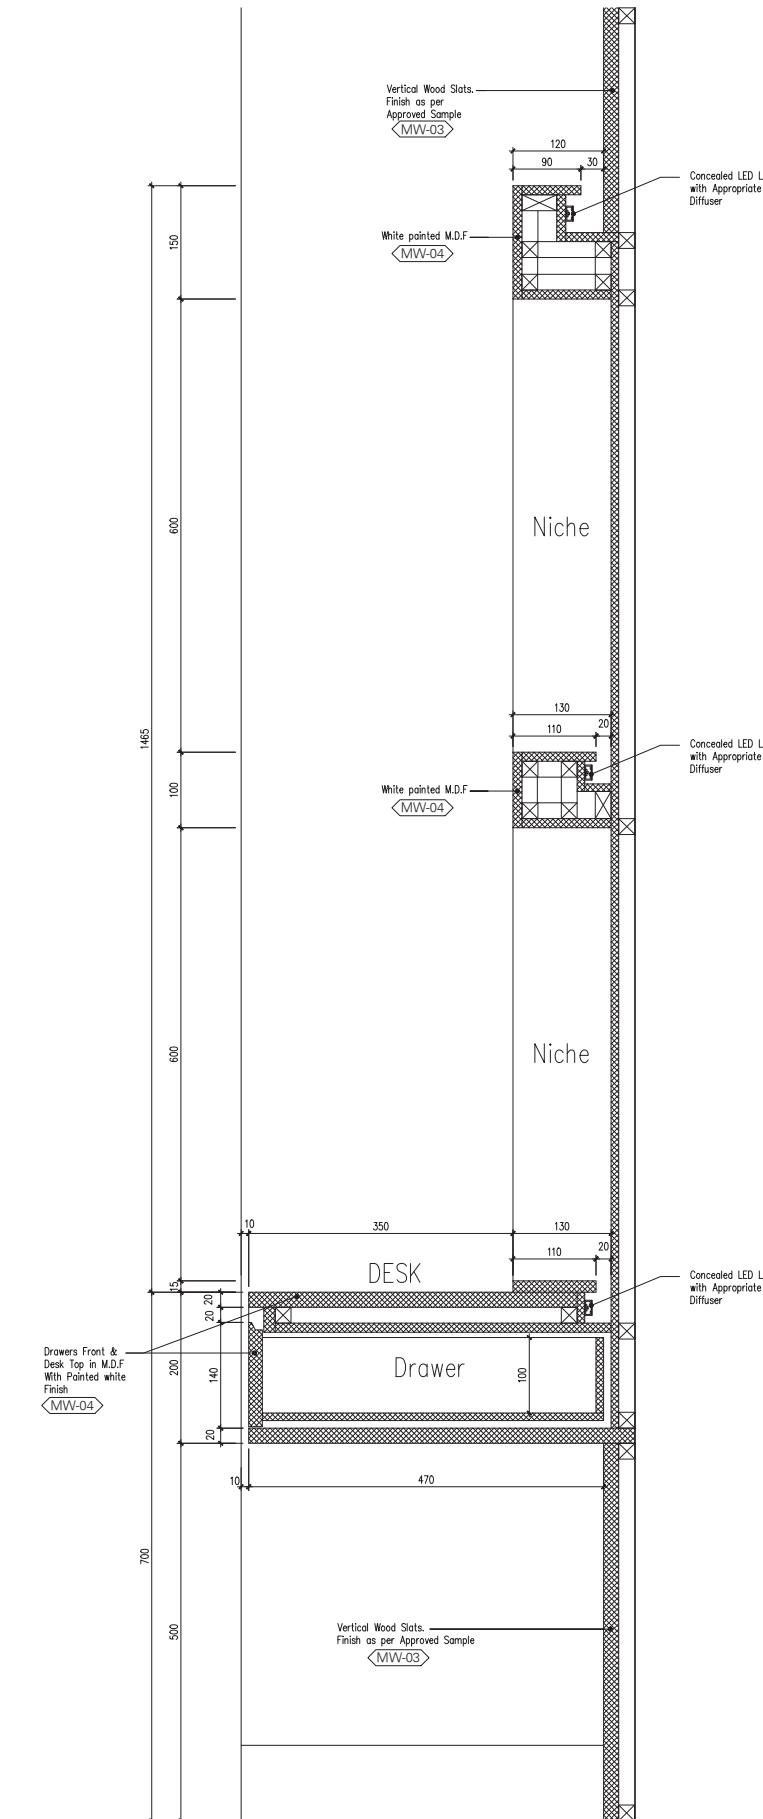

A SECTION DETAIL  
SCALE 1:5

0 2025.05.21 mp Initial issue  
Rev Date Drawn Revisions

**Design Architect:**

**Client:** Zach-Aimee  
**Project Title:** Private Villa -Dubai Hills


**Location:** Dubai, U.A.E.

**Plot Area:** 0000.00 Sqm  
0000.00 SqFt  
**Old Gate Level:** 0.00 = 0.000  
**NEW GATE LEVEL = 0.000**  
Proposed Gate Level is to be 000 mm above existing Asphalt Road Level


**Sheet Contents:**  
FIRST FLOOR  
ABRIELLA BEDROOM  
STUDY DESK + NICHES DETAIL  
Designed by: Drawn By: Checked By: Issued By:  
ab mp ab ab

Scale: Sheet Size: Stage: Rev No:  
1:25 A1 Conceptual Stage 0

**Drwg No.** ID- 405-1

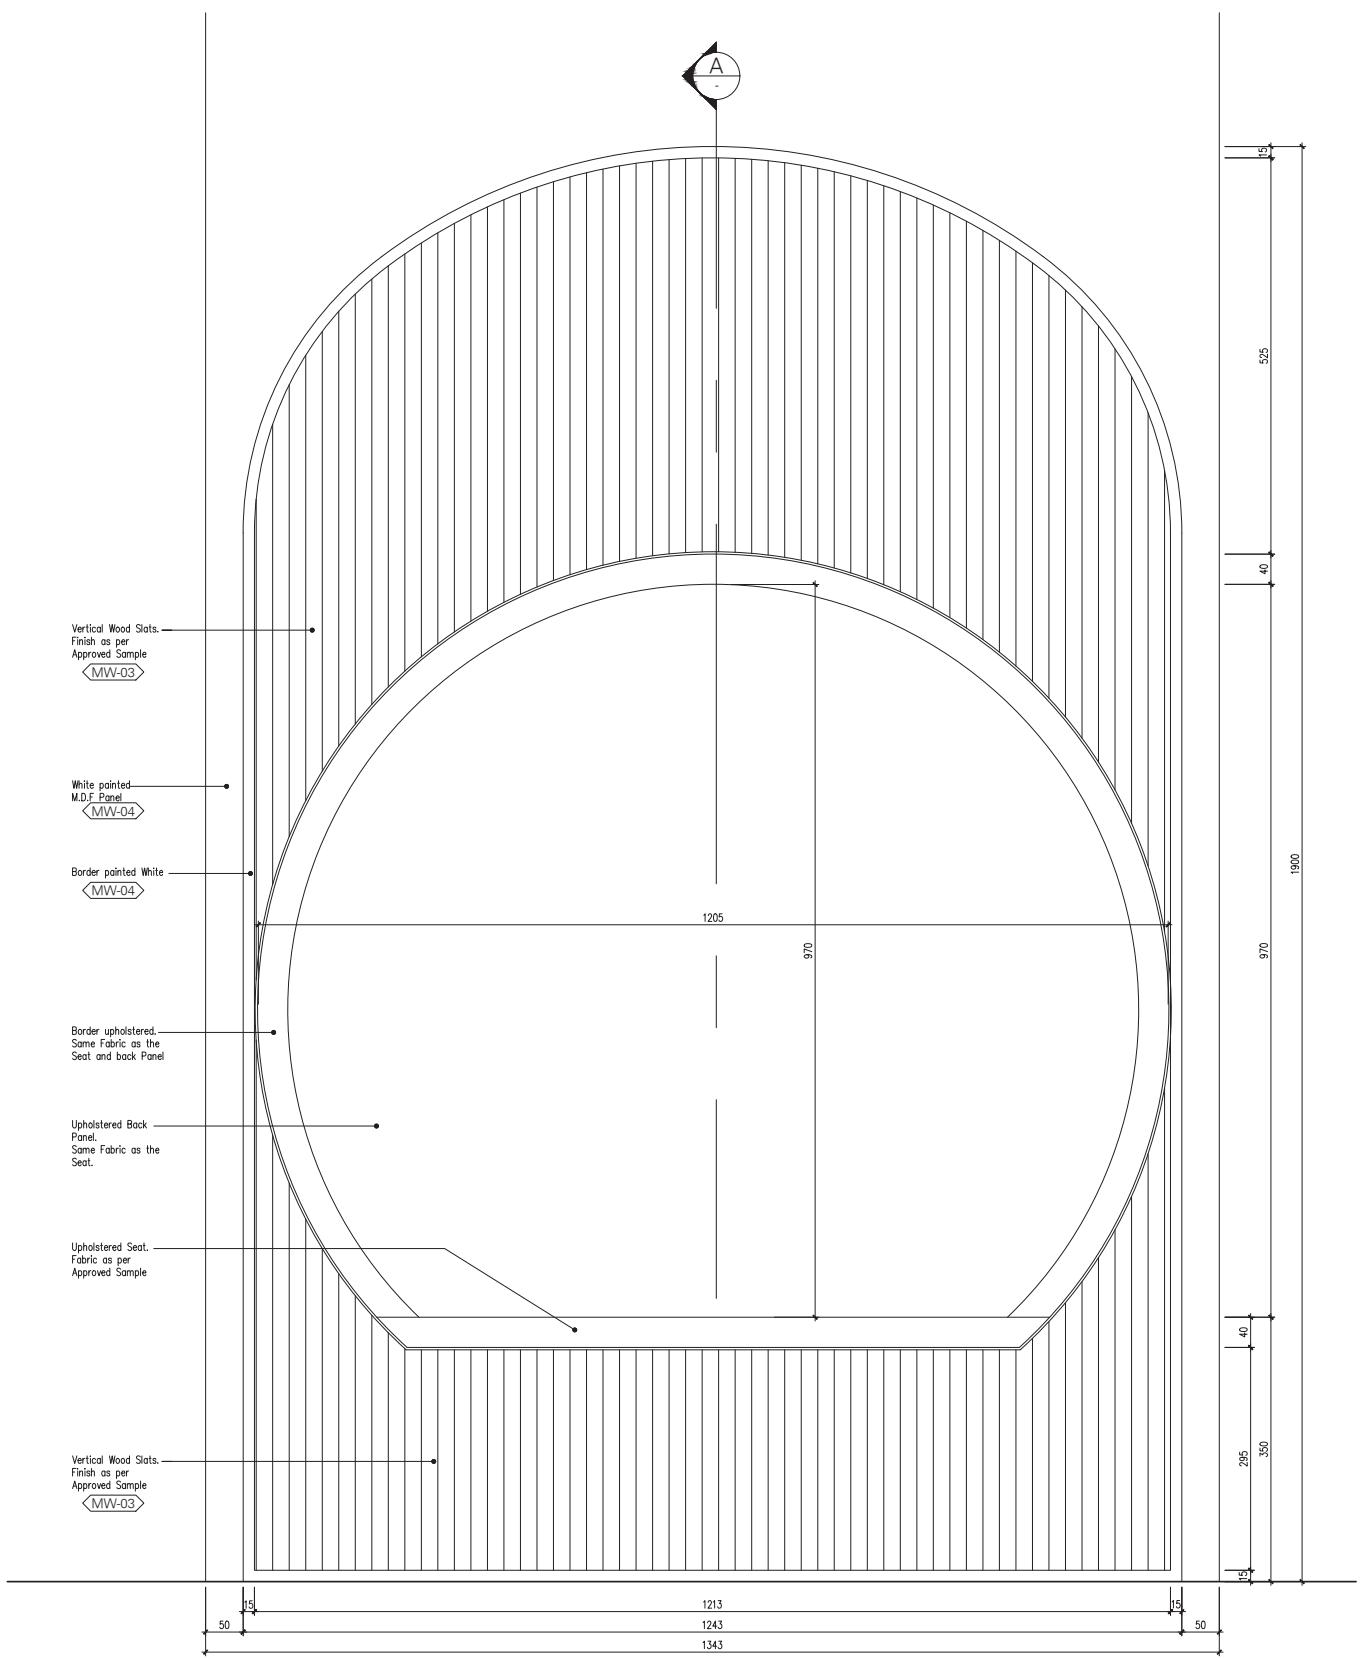

**02 ELEVATION DETAIL -2**

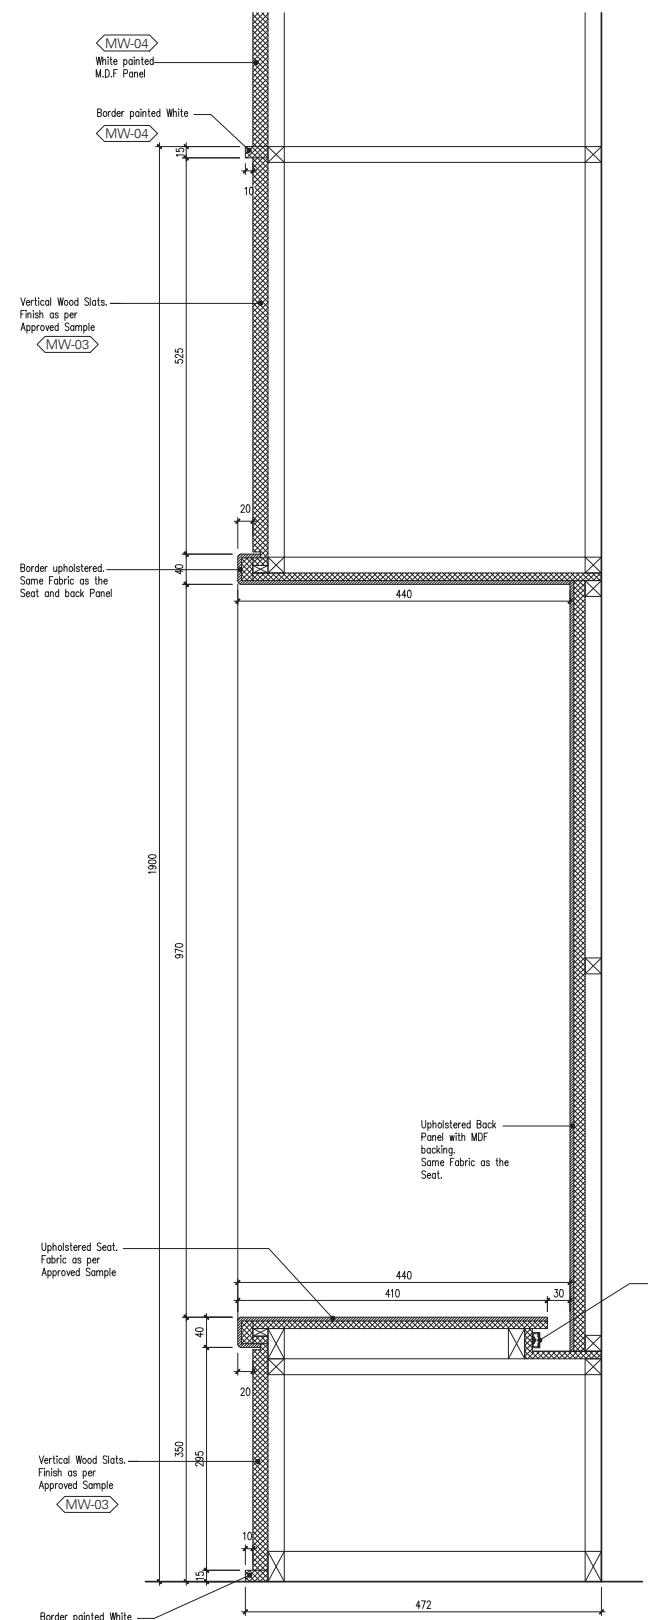

A SECTION DETAIL  
SCALE 1:5

**General Notes:**

- All dimensions are in millimeters unless otherwise noted.
- Any inconsistency or discrepancy is to be brought to the attention of and resolved by the architect/designer.
- All dimensions are to be checked on site before commencing work.
- This drawing is to be coordinated with the Lead Consultant.

## Notes

- ALL DRAWINGS ARE FOR DESIGN INTENT ONLY AND ARE NOT FOR CONSTRUCTION. THE APPOINTED CONTRACTOR SHOULD PROVIDE SHOP DRAWING FOR APPROVAL.

CONTRACTOR TO DO A SITE SURVEY TO SPECIFY CORRECT QUANTITY & DIMENSIONS AS PER SITE MEASUREMENTS & DRAWINGS.

CONTRACTOR TO CHECK THE MECHANISM & FUNCTIONALITY OF THE DESIGN INTEND.

MATERIAL MUST BE PRESENTED TO PRIOR TO PURCHASE FOR TO APPROVE.

#### **Design Architect:**

lient: Zach-Aimee

**Project Title:**

Private

Dakhi UAE


Plot Area: 0000.00 Sqm  
0000,00 SqFt  
Old Gate Level: 0.00 = 0.000  
NEW GATE LEVEL = 0.000

Proposed Gate Level is to be 0

**FIRST FLOOR**  
**ABRIELLA BEDROOM**  
**BUILT-IN SEATING DETAIL**

Designed by:	Drawn By:	Checked By:	Issued By:
ab	mp	ab	ab
cale: 1:25	Sheet Size: A1	Stage: Conceptual Stage	Rev No: 0

Drwg No. ID- 405-2

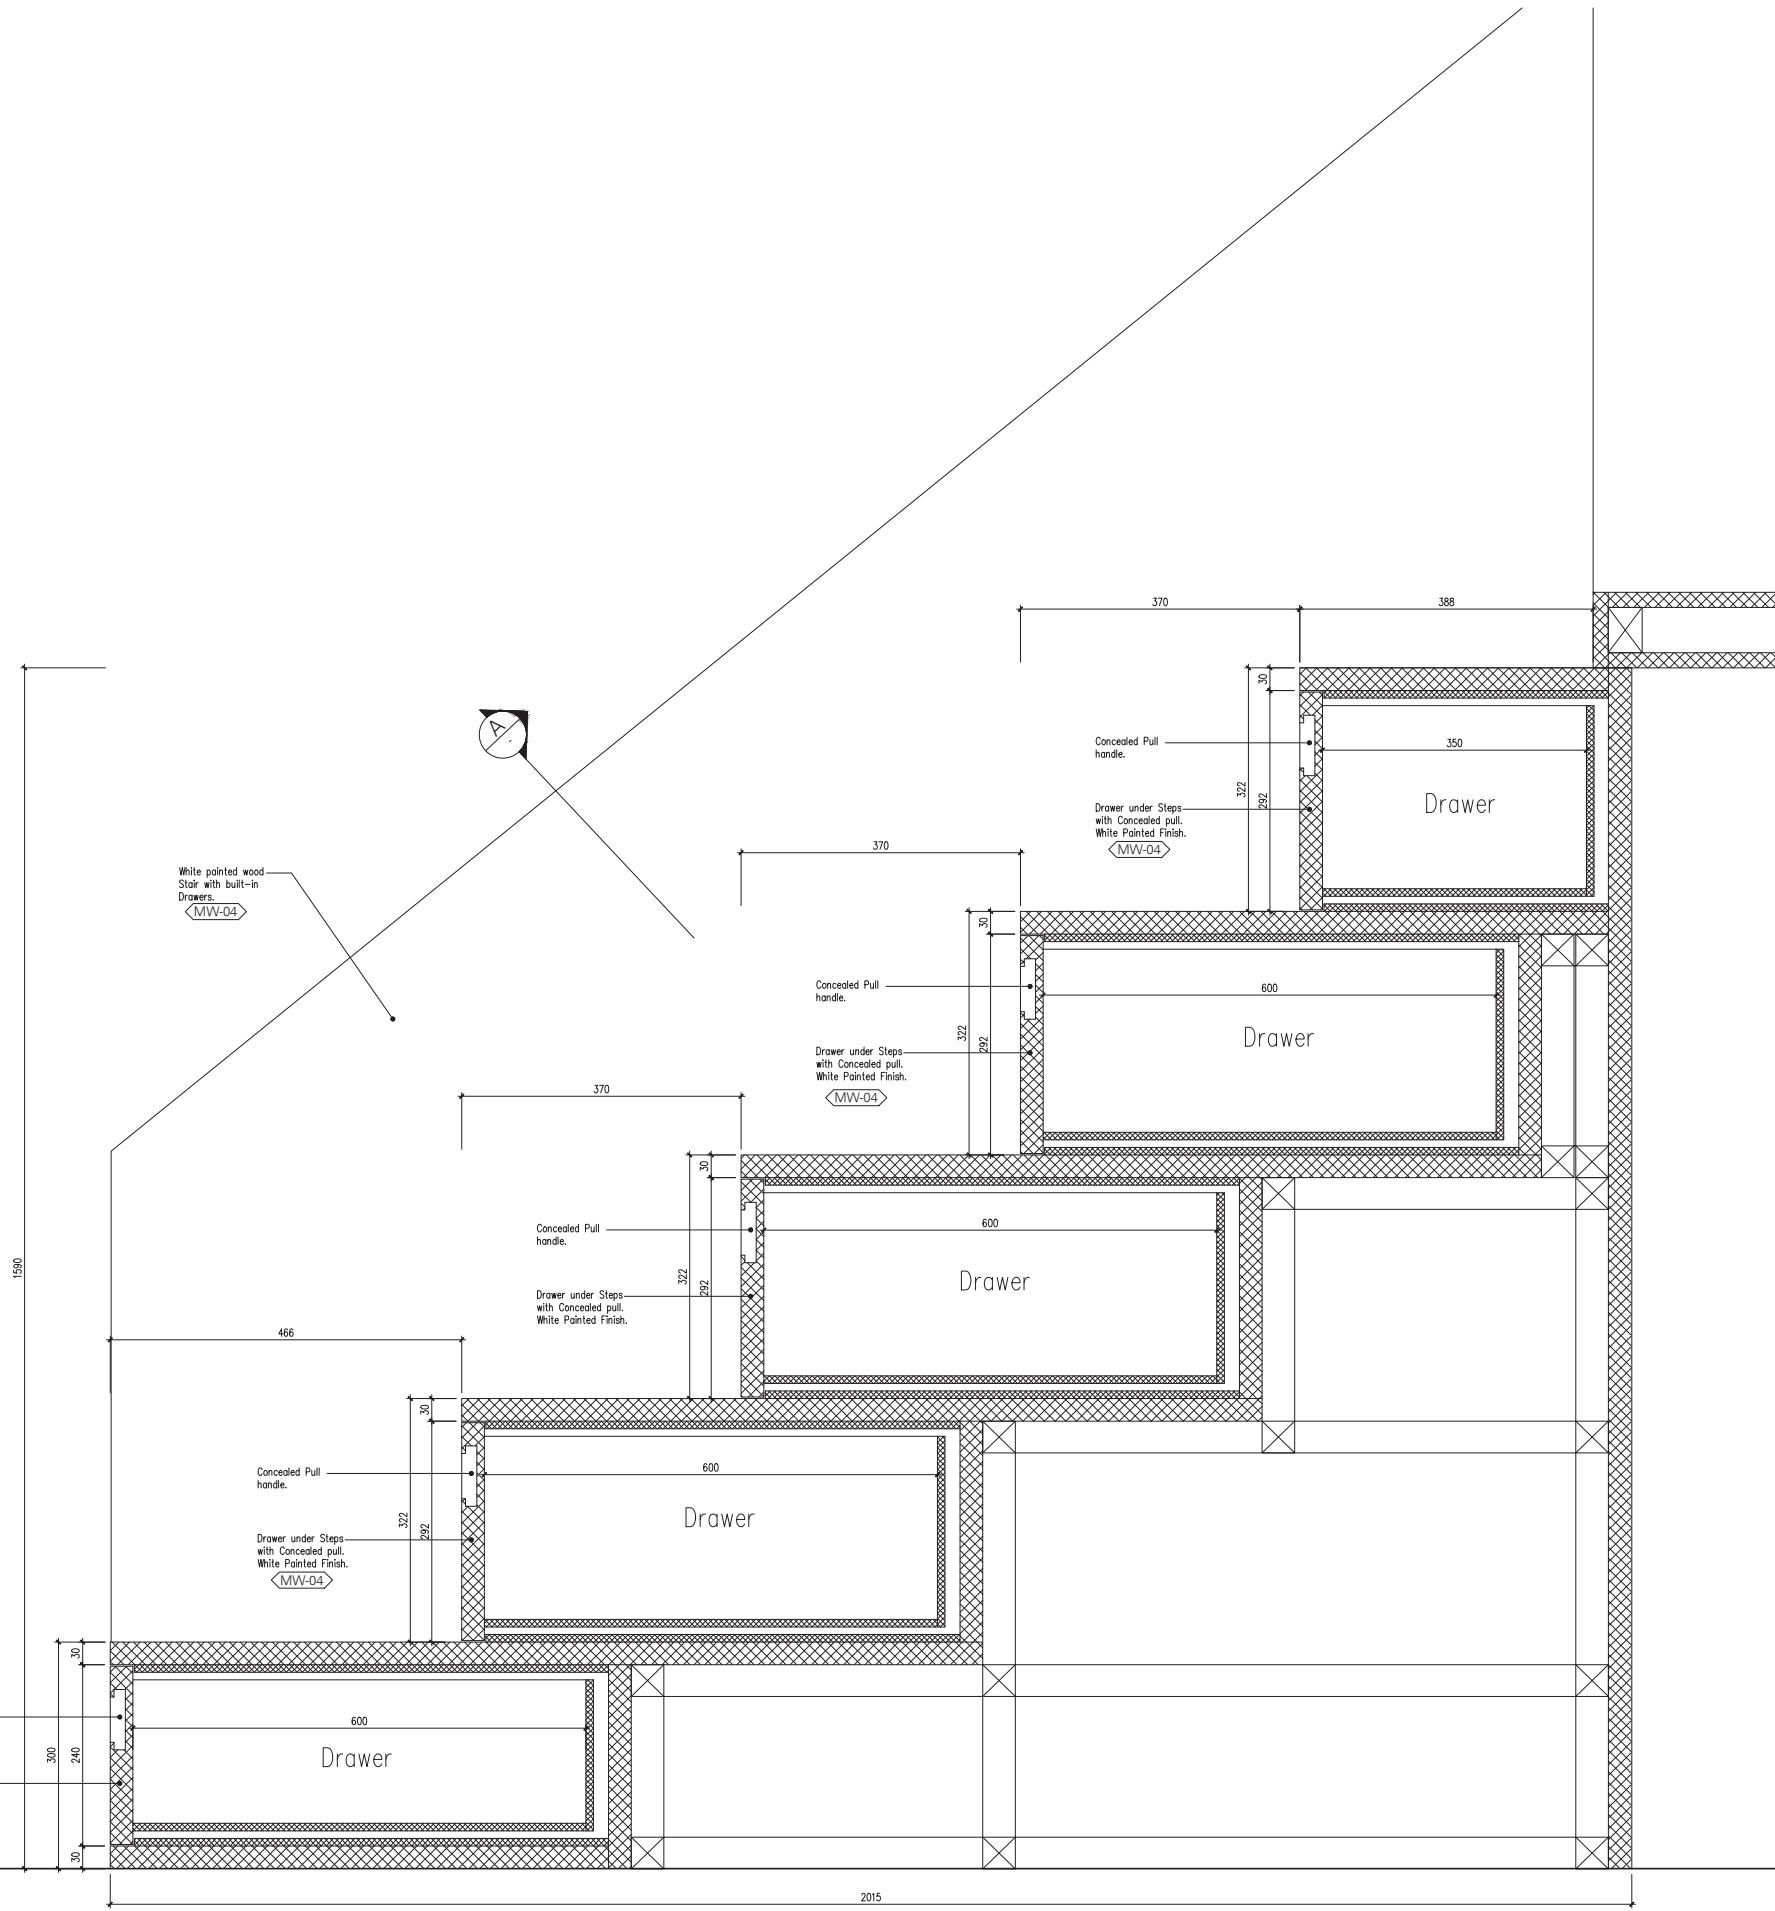

**03 STAIR SECTION DETAIL**  
SCALE 1:5

**A** HANDBRAIL SECTION DETAIL  
SCALE 1:2

**General Notes:**

1. All dimensions are in millimeters unless otherwise noted.
2. Any inconsistency or discrepancy is to be brought to the attention of and resolved by the architect/designer.
3. All dimensions are to be checked on site before commencing work.
4. This drawing is to be coordinated with the Lead Consultant.

## Notes

\* ALL DRAWINGS ARE FOR DESIGN INTENT ONLY AND ARE NOT FOR CONSTRUCTION. THE APPOINTED CONTRACTOR SHOULD PROVIDE SHOP DRAWING FOR APPROVAL.

\* CONTRACTOR TO DO A SITE SURVEY  
TO SPECIFY CORRECT QUANTITY &  
DIMENSIONS AS PER SITE MEASUREMENTS  
& DRAWINGS.

\* CONTRACTOR TO CHECK THE MECHANISM & FUNCTIONALITY OF THE DESIGN INTEND.

\* MATERIAL MUST BE PRESENTED TO PRIOR  
TO PURCHASE FOR TO APPROVE.

Rev	Date	Drawn	Revisions
<b>Design Architect:</b>			

Zach-Aimee

**Title:**

Private Villa -Dubai Hills

[View Details](#)

Plot Area: 0000.00 Sqm  
0000.00 SqFt  
Old Gate Level: 0.00 = 0.000  
**NEW GATE LEVEL = 0.000**  
Proposed Gate Level is to be 000 mm above existing Asphalt Road Level

Sheet Contents:				
FIRST FLOOR ABRIELLA BEDROOM STAIR DETAIL				
Designed by:	Drawn By:	Checked By:	Issued By:	
ab	mp	ab	ab	
Scale: 1-25	Sheet Size: A1	Stage: Conceptual	Rev No: 0	

Drwg No. ID- 405-3

**General Notes:**

- All dimensions are in millimeters unless otherwise noted.
- Any inconsistency or discrepancy is to be brought to the attention of and resolved by the architect/designer.
- All dimensions are to be checked on site before commencing work.
- This drawing is to be coordinated with the Lead Consultant.


**Notes**

\* ALL DRAWINGS ARE FOR DESIGN INTENT ONLY AND ARE NOT FOR CONSTRUCTION. THE APPOINTED CONTRACTOR SHOULD PROVIDE SHOP DRAWING FOR APPROVAL.


\* CONTRACTOR TO DO A SITE SURVEY TO SPECIFY CORRECT QUANTITY & DIMENSIONS AS PER SITE MEASUREMENTS & DRAWINGS.

\* CONTRACTOR TO CHECK THE MECHANISM & FUNCTIONALITY OF THE DESIGN INTEND.


\* MATERIAL MUST BE PRESENTED TO PRIOR TO PURCHASE FOR TO APPROVE.

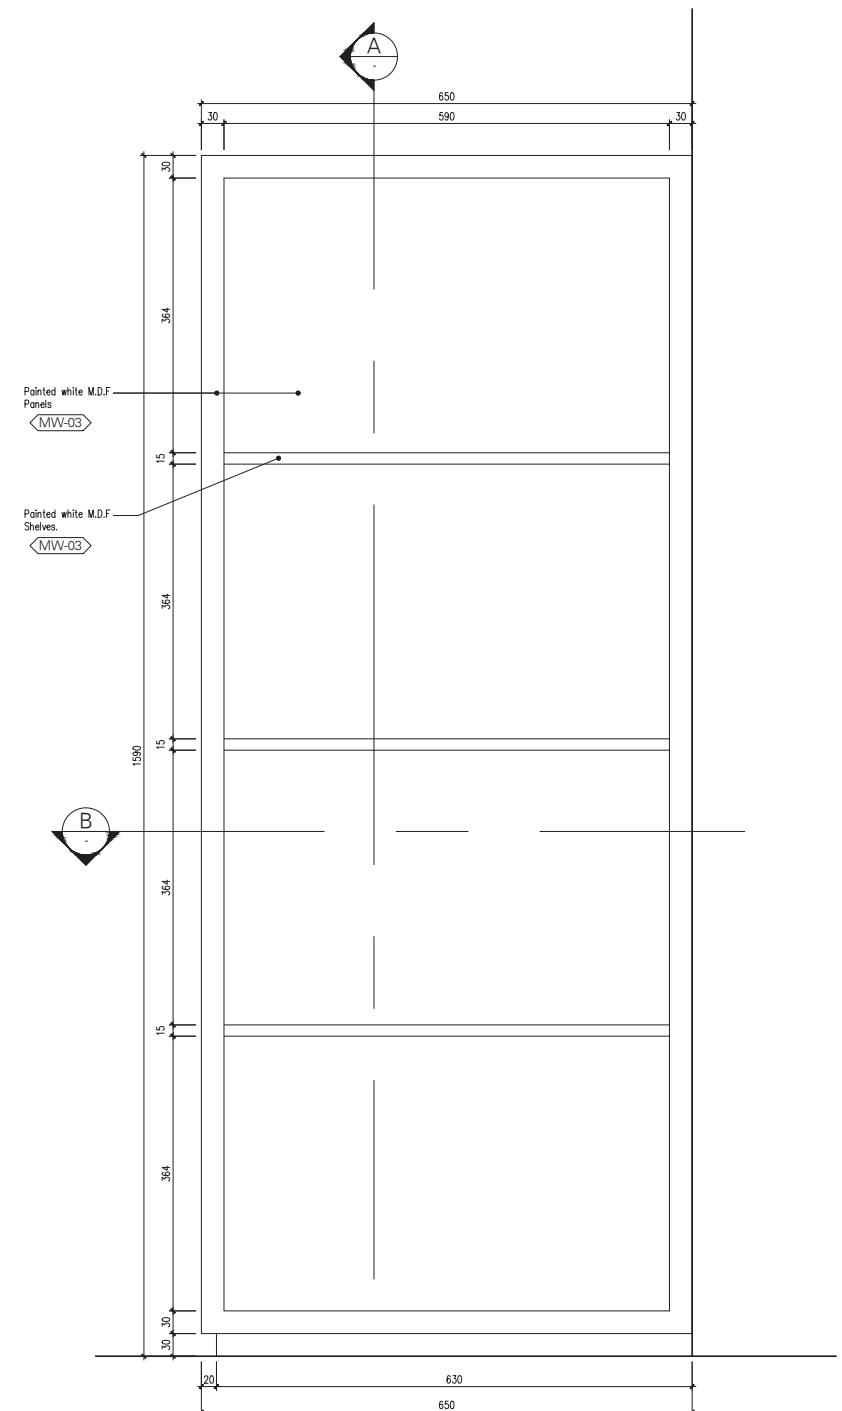

04 SHELVING UNIT ELEVATION  
SCALE 1:5

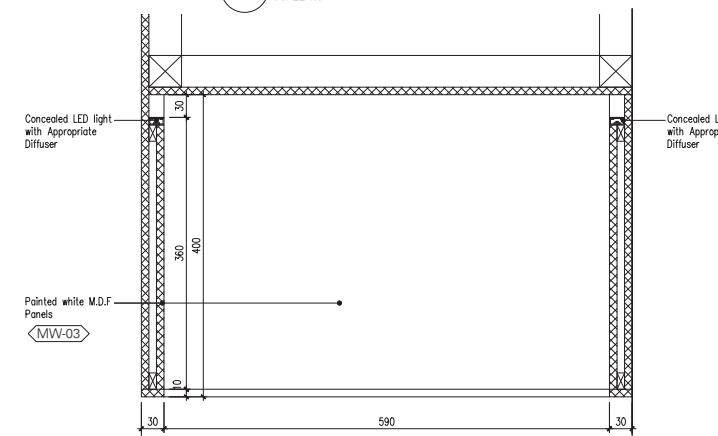

B SHELVING PLAN SECTION  
SCALE 1:5

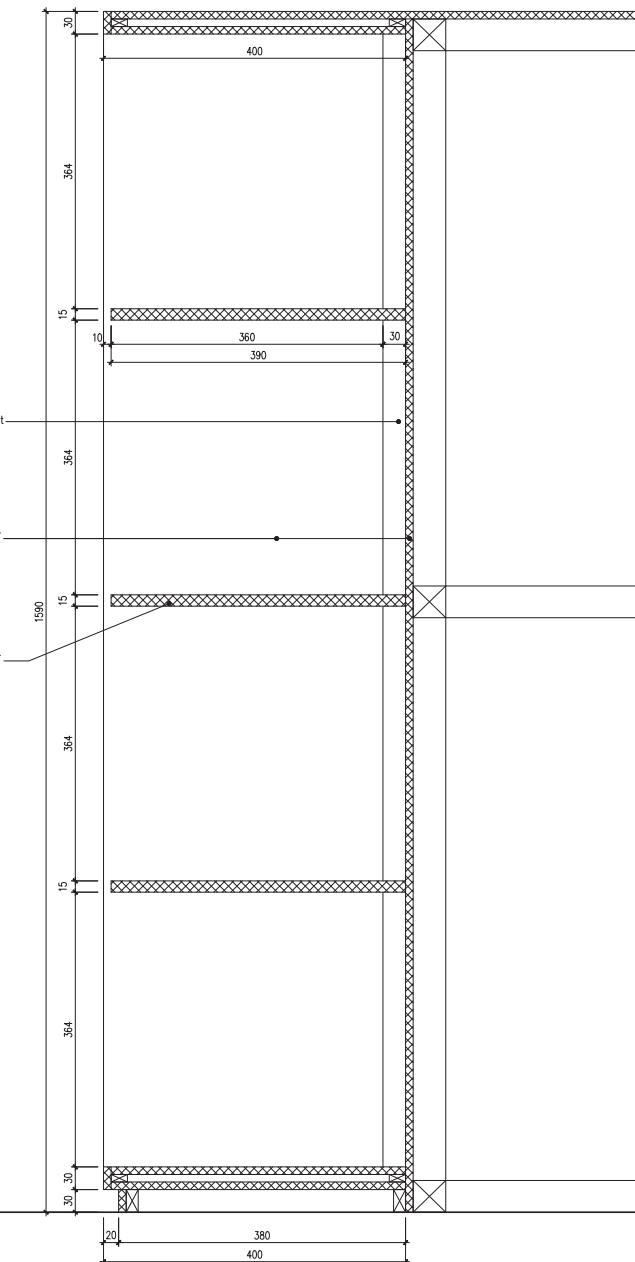

A SHELVING SECTION  
SCALE 1:5

0 2025.05.21 mp Initial issue  
Rev Date Drawn Revisions

**Design Architect:**

**Client:** Zach-Aimee  
**Project Title:** Private Villa -Dubai Hills

**Location:** Dubai, U.A.E.  
**Plot Area:** 0000.00 Sqm  
0000.00 SqFt  
**Old Gate Level:** 0.00 = 0.000  
**NEW GATE LEVEL = 0.000**  
Proposed Gate Level is to be 000 mm above existing Asphalt Road Level

**Sheet Contents:**  
FIRST FLOOR  
ABRIELLA BEDROOM  
SHELVING UNIT DETAIL

Designed by: Drawn By: Checked By: Issued By:  
ab mp ab ab

Scale: Sheet Size: Stage: Rev No:  
1:25 A1 Conceptual Stage 0

**Drwg No.** ID- 405-4

**General Notes:**

- All dimensions are in millimeters unless otherwise noted.
- Any inconsistency or discrepancy is to be brought to the attention of and resolved by the architect/designer.
- All dimensions are to be checked on site before commencing work.
- This drawing is to be coordinated with the Lead Consultant.


**Notes**

\* ALL DRAWINGS ARE FOR DESIGN INTENT ONLY AND ARE NOT FOR CONSTRUCTION. THE APPOINTED CONTRACTOR SHOULD PROVIDE SHOP DRAWING FOR APPROVAL.

\* CONTRACTOR TO DO A SITE SURVEY TO SPECIFY CORRECT QUANTITY & DIMENSIONS AS PER SITE MEASUREMENTS & DRAWINGS.

\* CONTRACTOR TO CHECK THE MECHANISM & FUNCTIONALITY OF THE DESIGN INTEND.

\* MATERIAL MUST BE PRESENTED TO PRIOR TO PURCHASE FOR TO APPROVE.

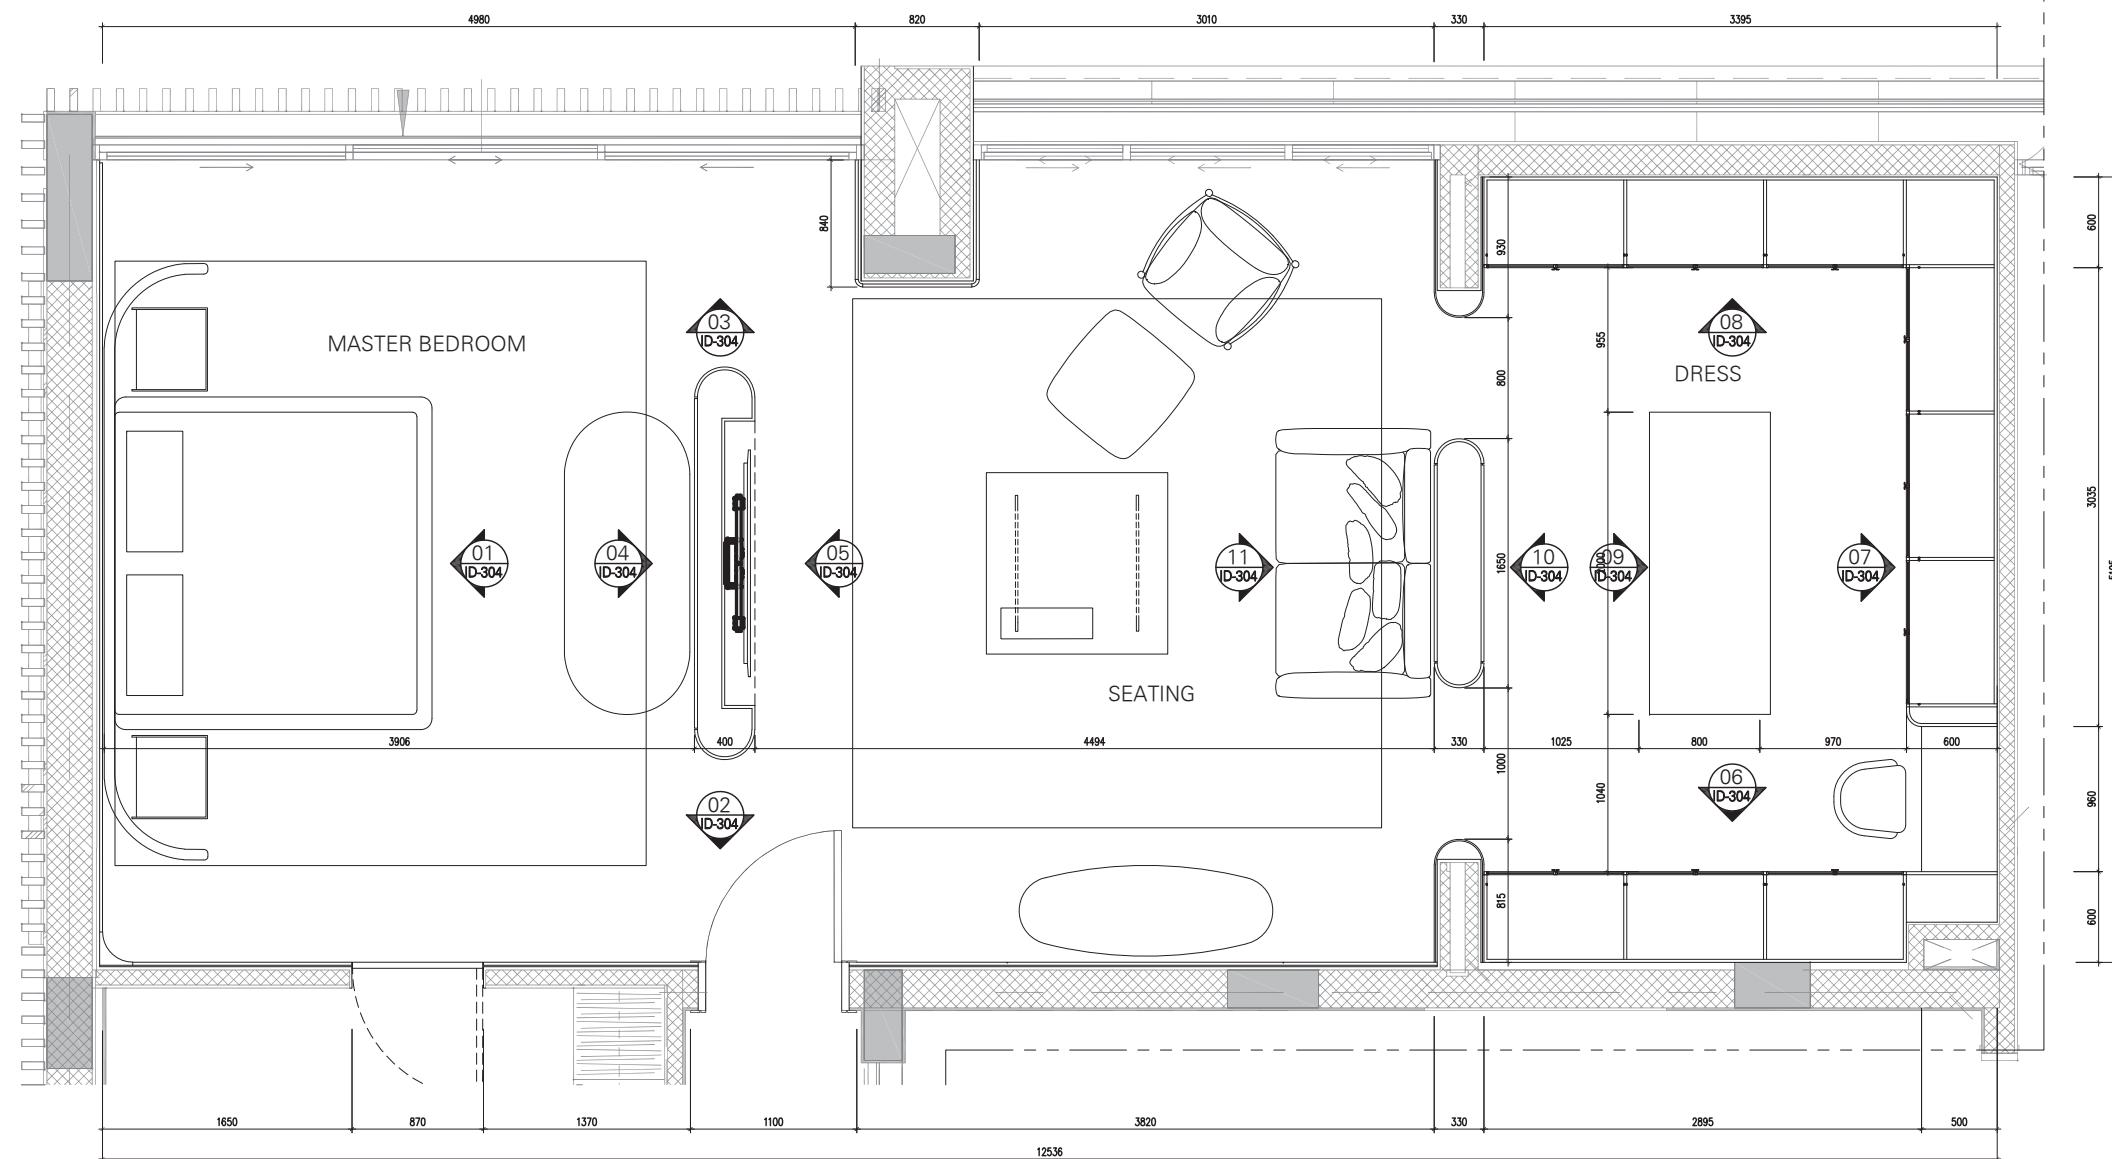

FIRST FLOOR - MASTERR BEDROOM LAYOUT  
SCALE 1:25

**Design Architect:**

0	2025.05.20	mp	Initial issue
Rev	Date	Drawn	Revisions

**Client:**  
Zach-Aimee

**Project Title:**  
Private Villa -Dubai Hills

**Location:**  
Dubai, U.A.E.

**Plot Area:** 0000.00 Sqm  
0000.00 SqFt  
**Old Gate Level:** 0.00 = 0.000  
**NEW GATE LEVEL = 0.000**  
Proposed Gate Level is to be 000 mm above existing Asphalt Road Level

**Sheet Contents:**  
FIRST FLOOR  
MASTER BEDROOM  
GENERAL LAYOUT  
Designed by: Drawn By: Checked By: Issued By:  
ab mp ab ab  
Scale: Sheet Size: Stage: Rev No:  
1:25 A1 Conceptual Stage 0

**Drwg No.** ID-102

**General Notes:**

- All dimensions are in millimeters unless otherwise noted.
- Any inconsistency or discrepancy is to be brought to the attention of and resolved by the architect/designer.
- All dimensions are to be checked on site before commencing work.
- This drawing is to be coordinated with the Lead Consultant.


**Notes**

\* ALL DRAWINGS ARE FOR DESIGN INTENT ONLY AND ARE NOT FOR CONSTRUCTION. THE APPOINTED CONTRACTOR SHOULD PROVIDE SHOP DRAWING FOR APPROVAL.

\* CONTRACTOR TO DO A SITE SURVEY TO SPECIFY CORRECT QUANTITY & DIMENSIONS AS PER SITE MEASUREMENTS & DRAWINGS.

\* CONTRACTOR TO CHECK THE MECHANISM & FUNCTIONALITY OF THE DESIGN INTEND.

\* MATERIAL MUST BE PRESENTED TO PRIOR TO PURCHASE FOR TO APPROVE.

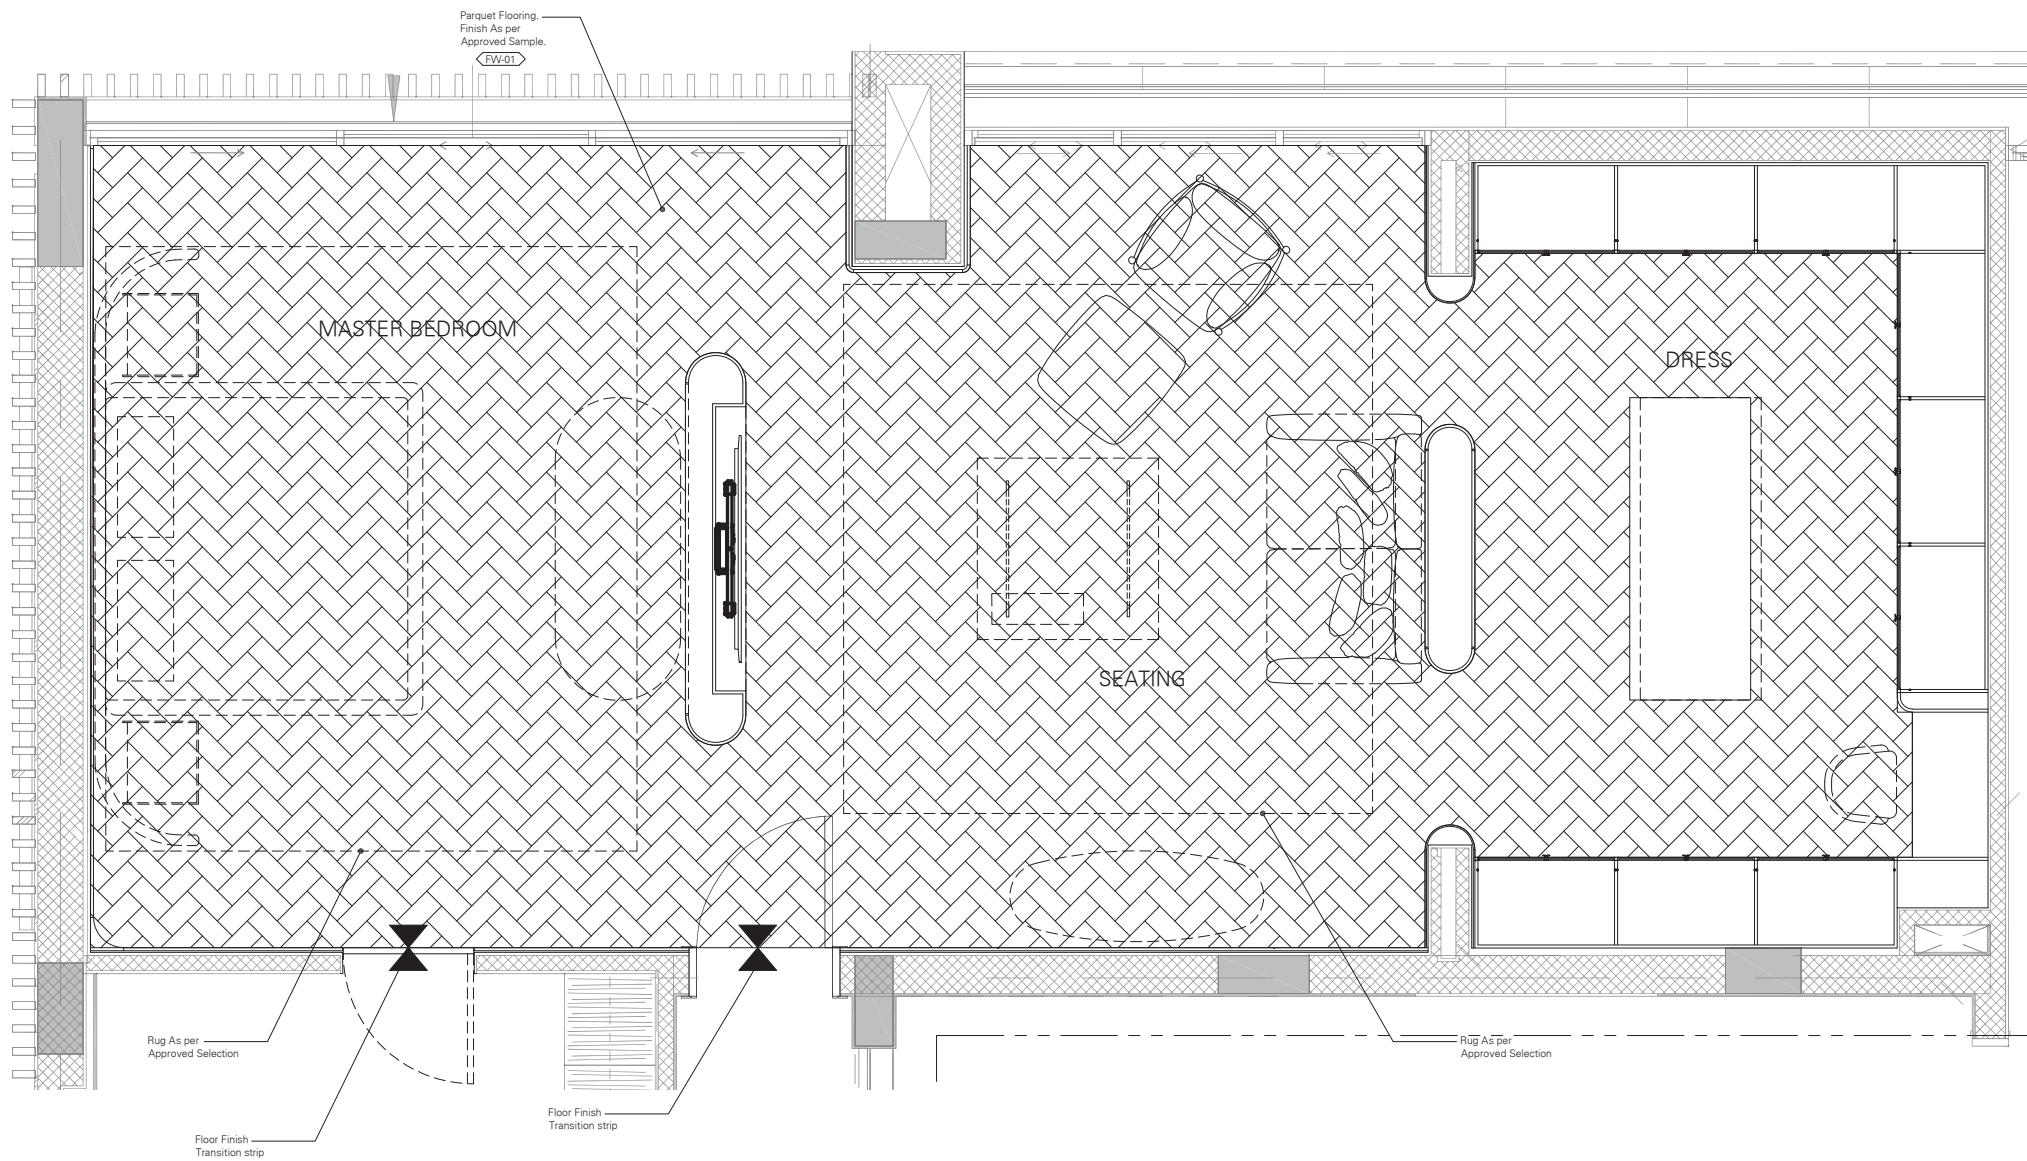

0	2025.06.02	mp	Initial issue
Rev	Date	Drawn	Revisions

**Design Architect:**

**Client:** Zach-Aimee

**Project Title:** Private Villa -Dubai Hills

**Location:** Dubai, U.A.E.

**Plot Area:** 0000.00 Sqm  
0000.00 SqFt  
**Old Gate Level:** 0.00 = 0.000  
**NEW GATE LEVEL = 0.000**

Proposed Gate Level is to be 000 mm above existing Asphalt Road Level

**Sheet Contents:**

FIRST FLOOR  
MASTER BEDROOM

FLOORING + FINISHING LAYOUT

Designed by:	Drawn By:	Checked By:	Issued By:
ab	mp	ab	ab

Scale: Sheet Size: Stage: Rev No:  
1:25 A1 Conceptual Stage 0

Drwg No. ID-106

**General Notes:**


- All dimensions are in millimeters unless otherwise noted.
- Any inconsistency or discrepancy is to be brought to the attention of and resolved by the architect/designer.
- All dimensions are to be checked on site before commencing work.
- This drawing is to be coordinated with the Lead Consultant.

**Notes**

- \* ALL DRAWINGS ARE FOR DESIGN INTENT ONLY AND ARE NOT FOR CONSTRUCTION. THE APPOINTED CONTRACTOR SHOULD PROVIDE SHOP DRAWING FOR APPROVAL.
- \* CONTRACTOR TO DO A SITE SURVEY TO SPECIFY CORRECT QUANTITY & DIMENSIONS AS PER SITE MEASUREMENTS & DRAWINGS.
- \* CONTRACTOR TO CHECK THE MECHANISM & FUNCTIONALITY OF THE DESIGN INTEND.
- \* MATERIAL MUST BE PRESENTED TO PRIOR TO PURCHASE FOR TO APPROVE.

**LEGEND :**

○ Recessed Downlight

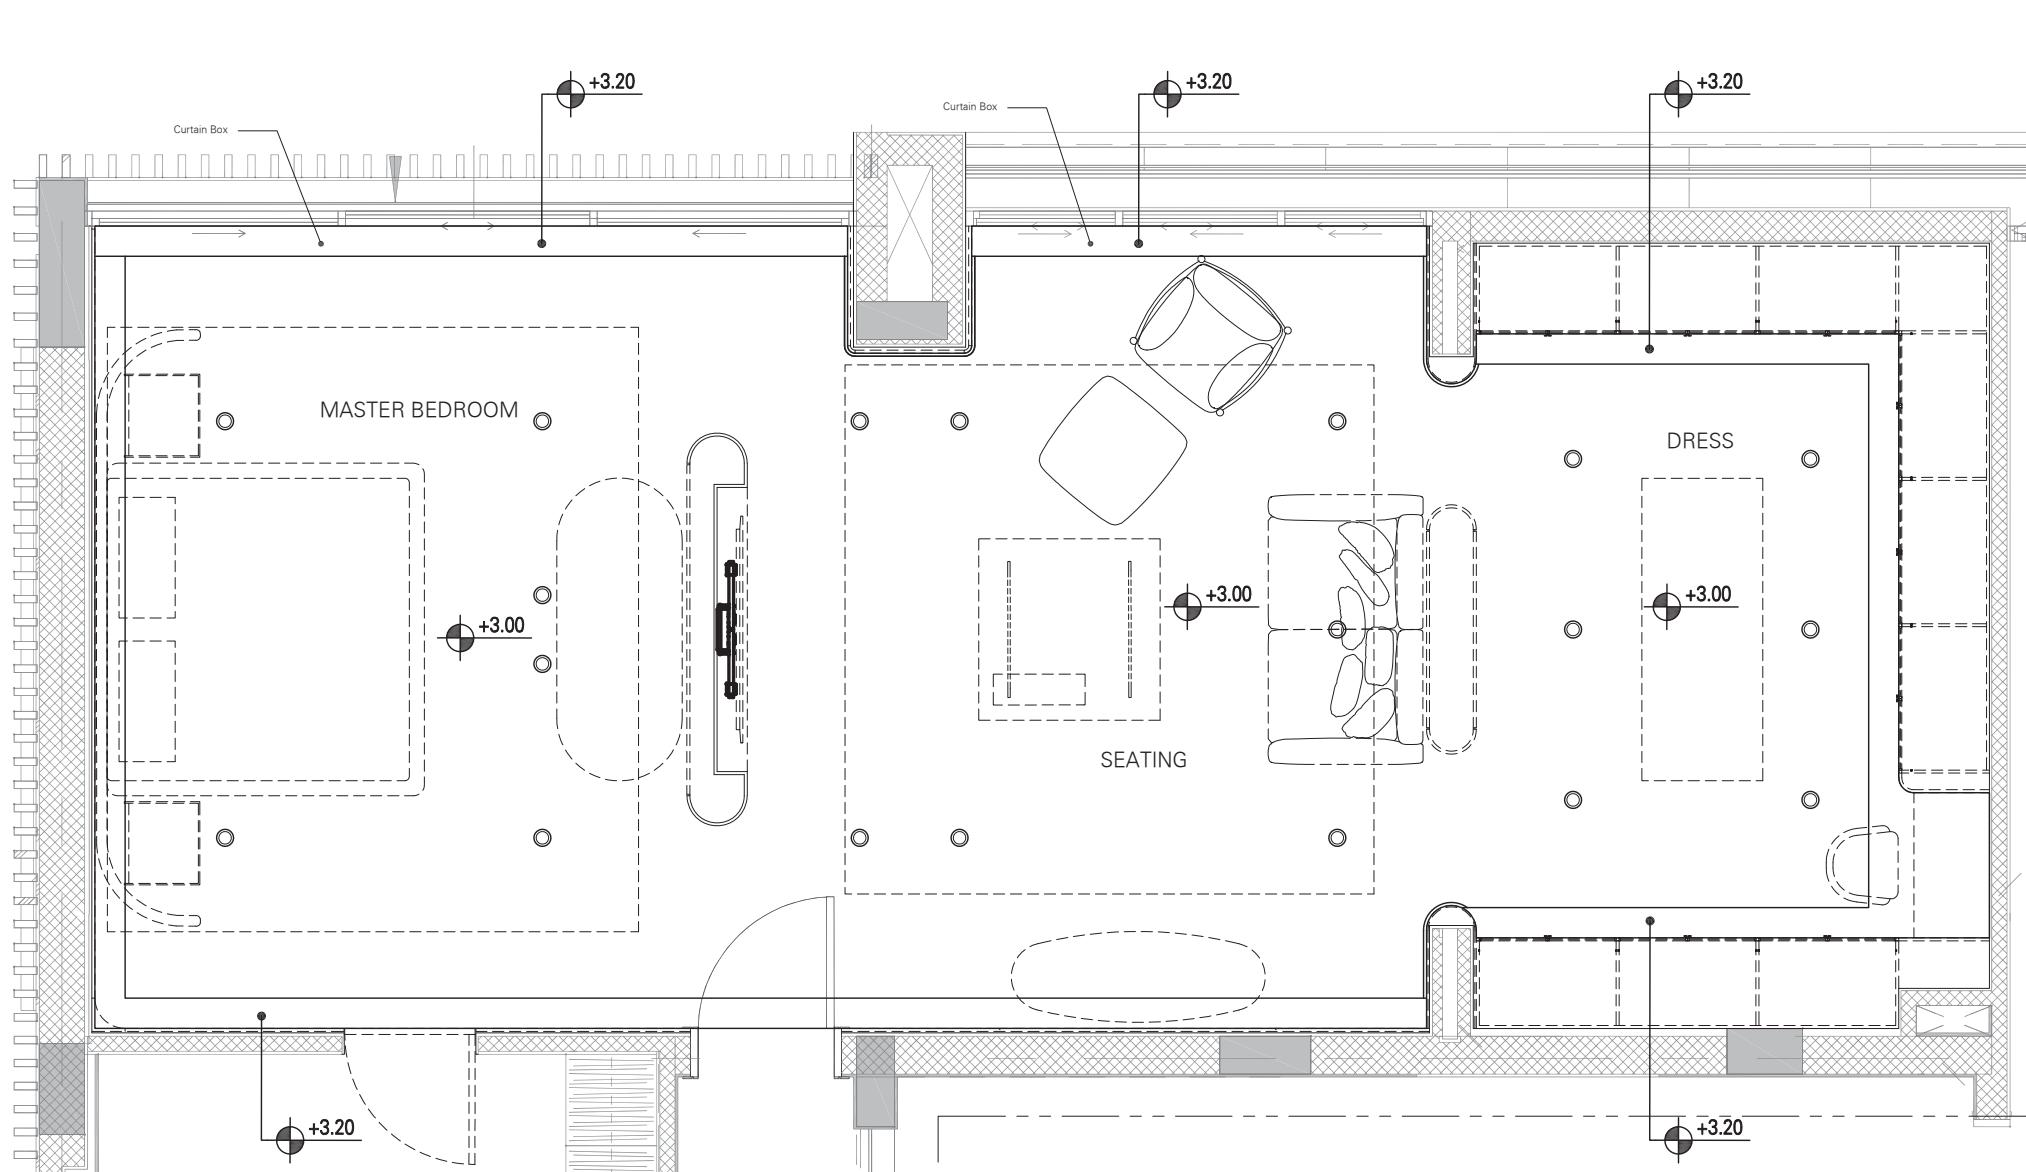

FIRST FLOOR - MASTER BEDROOM - REFLECTED CEILING LAYOUT  
SCALE 1:25

0	2025.05.20	mp	Initial issue
Rev	Date	Drawn	Revisions

**Design Architect:**

**Client:**  
Zach-Aimee

**Project Title:**  
Private Villa -Dubai Hills

**Location:**  
Dubai, U.A.E.

**Plot Area:** 0000.00 Sqm  
0000.00 SqFt  
**Old Gate Level:** 0.00 = 0.000  
**NEW GATE LEVEL:** = 0.000  
Proposed Gate Level is to be 000 mm above existing Asphalt Road Level

Sheet Contents:			
FIRST FLOOR MASTER BEDROOM REFLECTED CEILING LAYOUT			
Designed by:	Drawn By:	Checked By:	Issued By:
ab	mp	ab	ab

Scale: Sheet Size: Stage: Rev No:  
1:25 A1 Conceptual Stage 0

Drwg No. ID-202

**General Notes:**

- All dimensions are in millimeters unless otherwise noted.
- Any inconsistency or discrepancy is to be brought to the attention of and resolved by the architect/designer.
- All dimensions are to be checked on site before commencing work.
- This drawing is to be coordinated with the Lead Consultant.

**Notes**

\* ALL DRAWINGS ARE FOR DESIGN INTENT ONLY AND ARE NOT FOR CONSTRUCTION. THE APPOINTED CONTRACTOR SHOULD PROVIDE SHOP DRAWING FOR APPROVAL.

\* CONTRACTOR TO DO A SITE SURVEY TO SPECIFY CORRECT QUANTITY & DIMENSIONS AS PER SITE MEASUREMENTS & DRAWINGS.

\* CONTRACTOR TO CHECK THE MECHANISM & FUNCTIONALITY OF THE DESIGN INTEND.

\* MATERIAL MUST BE PRESENTED TO PRIOR TO PURCHASE FOR TO APPROVE.

0	2025.05.21	mp	Initial issue
Rev	Date	Drawn	Revisions

**Design Architect:**

**Client:** Zach-Aimee  
**Project Title:** Private Villa -Dubai Hills

**Location:** Dubai, U.A.E.


**Plot Area:** 0000.00 Sqm  
0000.00 SqFt  
**Old Gate Level:** 0.00 = 0.000  
**NEW GATE LEVEL = 0.000**  
Proposed Gate Level is to be 000 mm above existing Asphalt Road Level

**Sheet Contents:**  
FIRST FLOOR  
MASTER BEDROOM  
PLAN

Designed by:	Drawn By:	Checked By:	Issued By:
ab	mp	ab	ab

Scale: 1:25 Sheet Size: A1 Stage: Conceptual Rev No: 0

**Drwg No.** ID-304-1

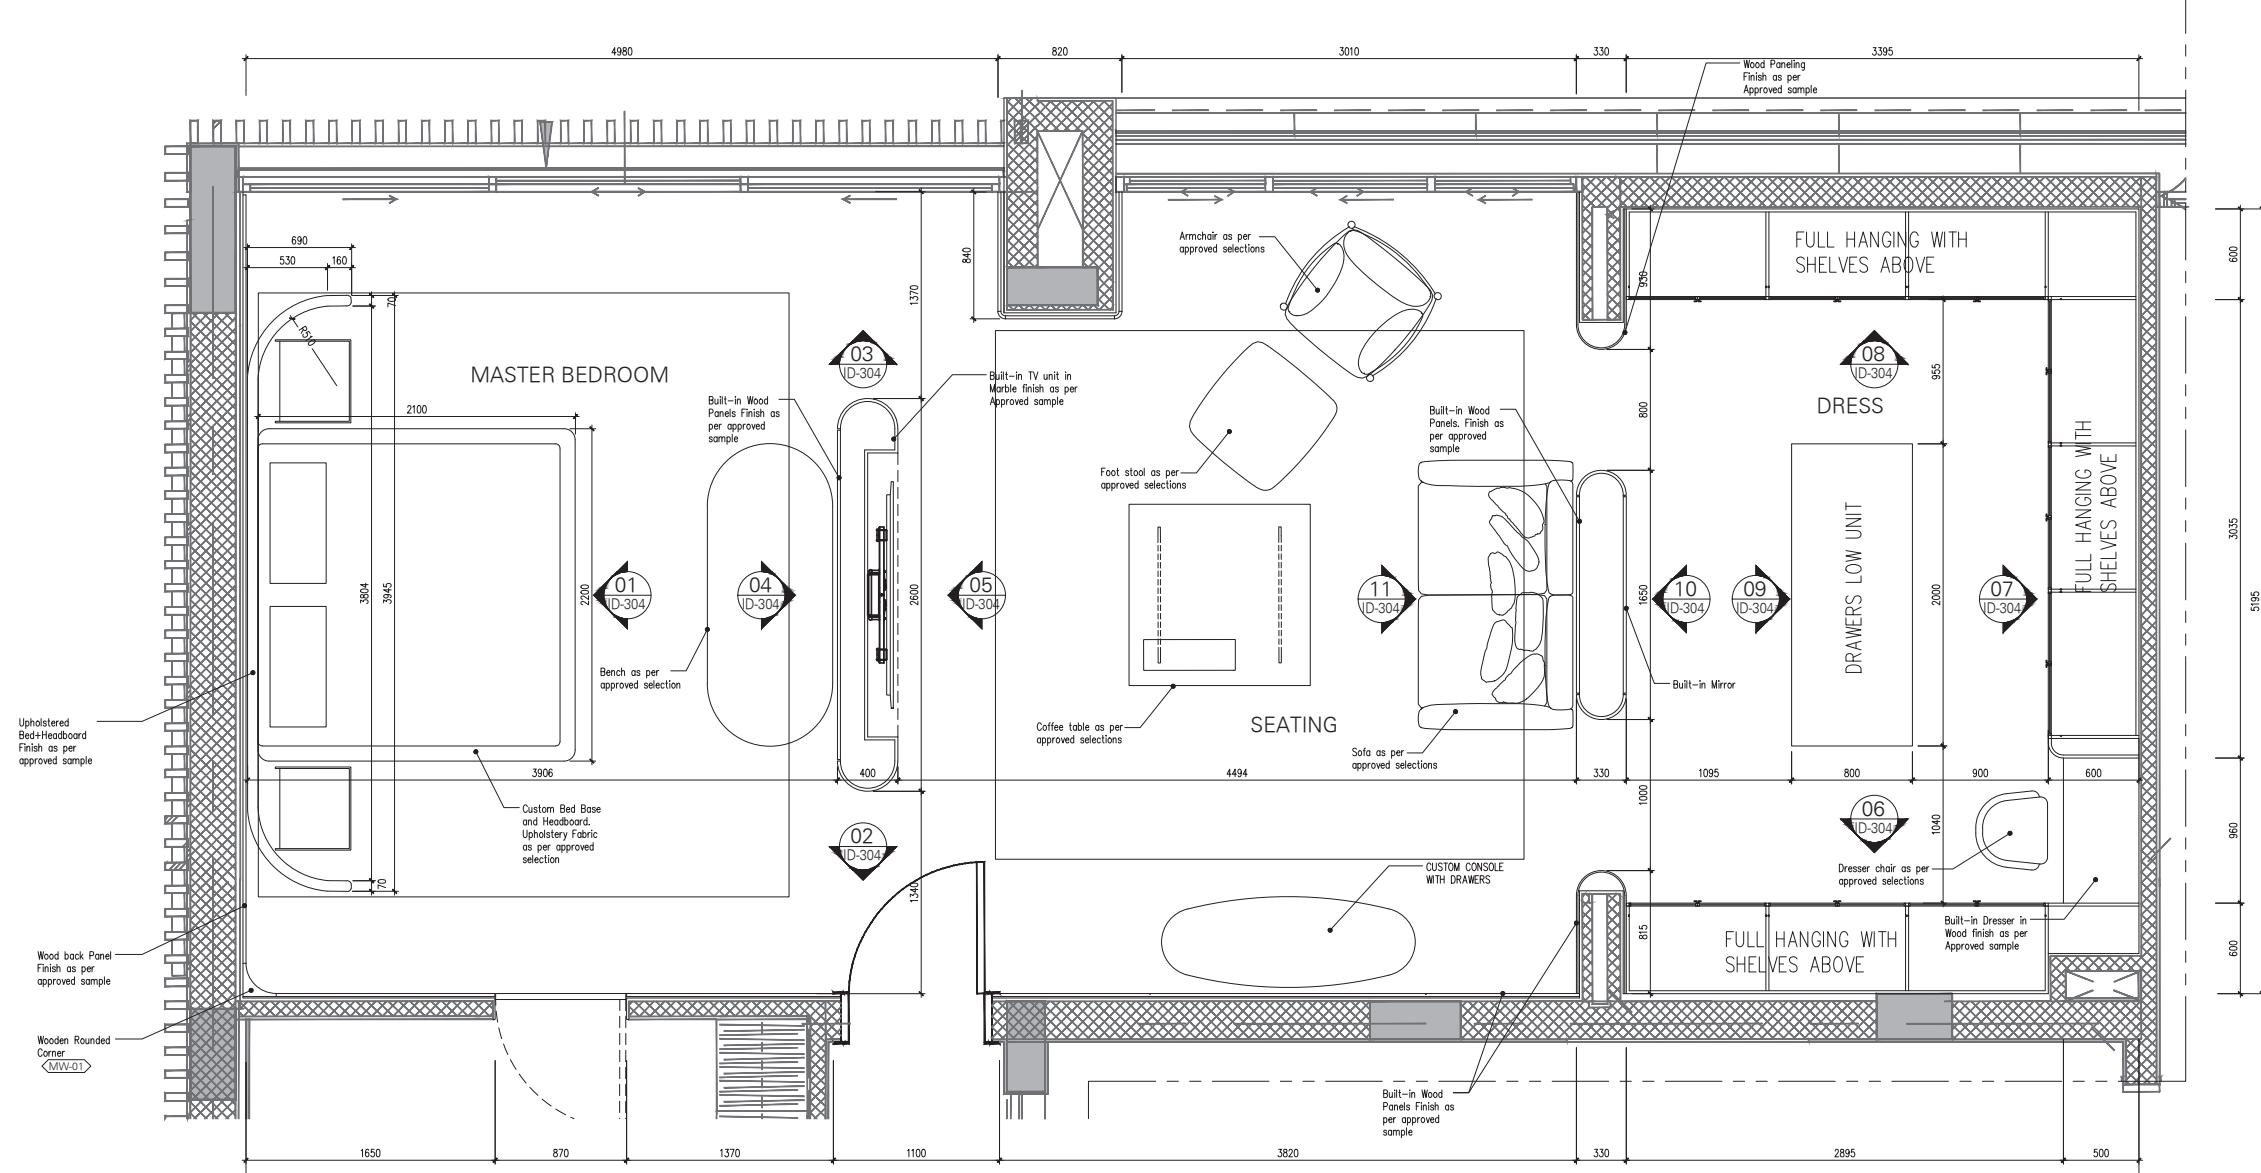

FIRST FLOOR - MASTER BEDROOM LAYOUT

SCALE 1:25


**Drwg No.** ID-304-1

**General Notes:**

- All dimensions are in millimeters unless otherwise noted.
- Any inconsistency or discrepancy is to be brought to the attention of and resolved by the architect/designer.
- All dimensions are to be checked on site before commencing work.
- This drawing is to be coordinated with the Lead Consultant.

**Notes**

- \* ALL DRAWINGS ARE FOR DESIGN INTENT ONLY AND ARE NOT FOR CONSTRUCTION. THE APPOINTED CONTRACTOR SHOULD PROVIDE SHOP DRAWING FOR APPROVAL.
- \* CONTRACTOR TO DO A SITE SURVEY TO SPECIFY CORRECT QUANTITY & DIMENSIONS AS PER SITE MEASUREMENTS & DRAWINGS.
- \* CONTRACTOR TO CHECK THE MECHANISM & FUNCTIONALITY OF THE DESIGN INTEND.
- \* MATERIAL MUST BE PRESENTED TO PRIOR TO PURCHASE FOR TO APPROVE.

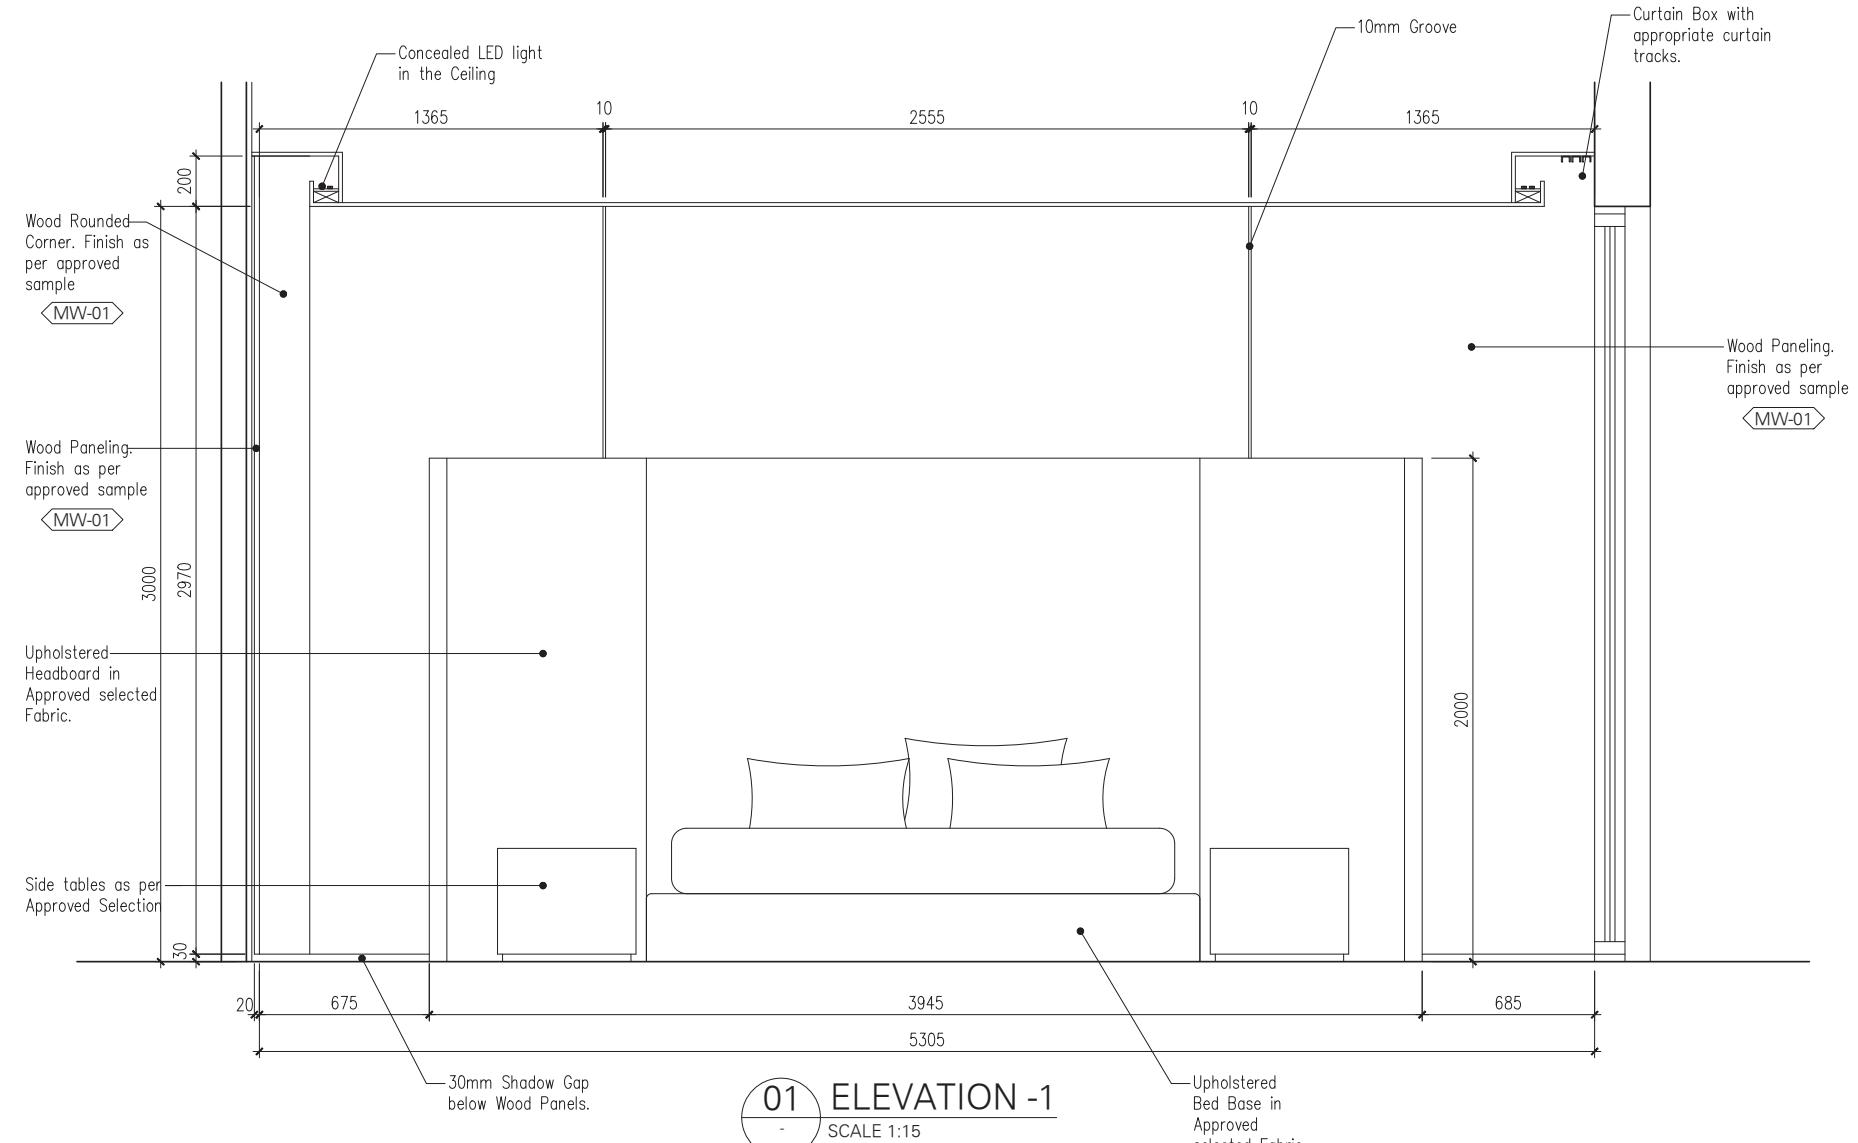

0	2025.05.02	mp	Initial issue
Rev	Date	Drawn	Revisions

**Design Architect:**

**Client:** Zach-Aimee

**Project Title:** Private Villa -Dubai Hills

**Location:** Dubai, U.A.E.

**Plot Area:** 0000.00 Sqm  
0000.00 SqFt  
**Old Gate Level:** 0.00 = 0.000  
**NEW GATE LEVEL = 0.000**  
Proposed Gate Level is to be 000 mm above existing Asphalt Road Level

<b>Sheet Contents:</b>			
FIRST FLOOR MASTER BEDROOM ELEVATION-1			
Designed by:	Drawn By:	Checked By:	Issued By:
ab	mp	ab	ab

**Scale:** 1:15      **Sheet Size:** A1      **Stage:** Conceptual Stage      **Rev No:** 0

**Drwg No.** ID-304-2



VISUAL - 1

**General Notes:**

- All dimensions are in millimeters unless otherwise noted.
- Any inconsistency or discrepancy is to be brought to the attention of and resolved by the architect/designer.
- All dimensions are to be checked on site before commencing work.
- This drawing is to be coordinated with the Lead Consultant.

**Notes**

- \* ALL DRAWINGS ARE FOR DESIGN INTENT ONLY AND ARE NOT FOR CONSTRUCTION. THE APPOINTED CONTRACTOR SHOULD PROVIDE SHOP DRAWING FOR APPROVAL.
- \* CONTRACTOR TO DO A SITE SURVEY TO SPECIFY CORRECT QUANTITY & DIMENSIONS AS PER SITE MEASUREMENTS & DRAWINGS.
- \* CONTRACTOR TO CHECK THE MECHANISM & FUNCTIONALITY OF THE DESIGN INTEND.
- \* MATERIAL MUST BE PRESENTED TO PRIOR TO PURCHASE FOR TO APPROVE.

0	2025.05.02	mp	Initial issue
Rev	Date	Drawn	Revisions

**Design Architect:**

**Client:**  
Zach-Aimee

**Project Title:**  
Private Villa -Dubai Hills

**Location:**  
Dubai, U.A.E.

**Plot Area:** 0000.00 Sqm  
0000.00 SqFt  
**Old Gate Level:** 0.00 = 0.000  
**NEW GATE LEVEL = 0.000**

Proposed Gate Level is to be 000 mm above existing Asphalt Road Level

**Sheet Contents:**  
FIRST FLOOR  
MASTER BEDROOM  
VISUAL - 1

Designed by:	Drawn By:	Checked By:	Issued By:
ab	mp	ab	ab

Scale:	Sheet Size:	Stage:	Rev No:
1:15	A1	Conceptual Stage	0

**Drwg No.** ID-304-2-R

**General Notes:**

- All dimensions are in millimeters unless otherwise noted.
- Any inconsistency or discrepancy is to be brought to the attention of and resolved by the architect/designer.
- All dimensions are to be checked on site before commencing work.
- This drawing is to be coordinated with the Lead Consultant.


**Notes**

\* ALL DRAWINGS ARE FOR DESIGN INTENT ONLY AND ARE NOT FOR CONSTRUCTION. THE APPOINTED CONTRACTOR SHOULD PROVIDE SHOP DRAWING FOR APPROVAL.

\* CONTRACTOR TO DO A SITE SURVEY TO SPECIFY CORRECT QUANTITY & DIMENSIONS AS PER SITE MEASUREMENTS & DRAWINGS.

\* CONTRACTOR TO CHECK THE MECHANISM & FUNCTIONALITY OF THE DESIGN INTEND.

\* MATERIAL MUST BE PRESENTED TO PRIOR TO PURCHASE FOR TO APPROVE.

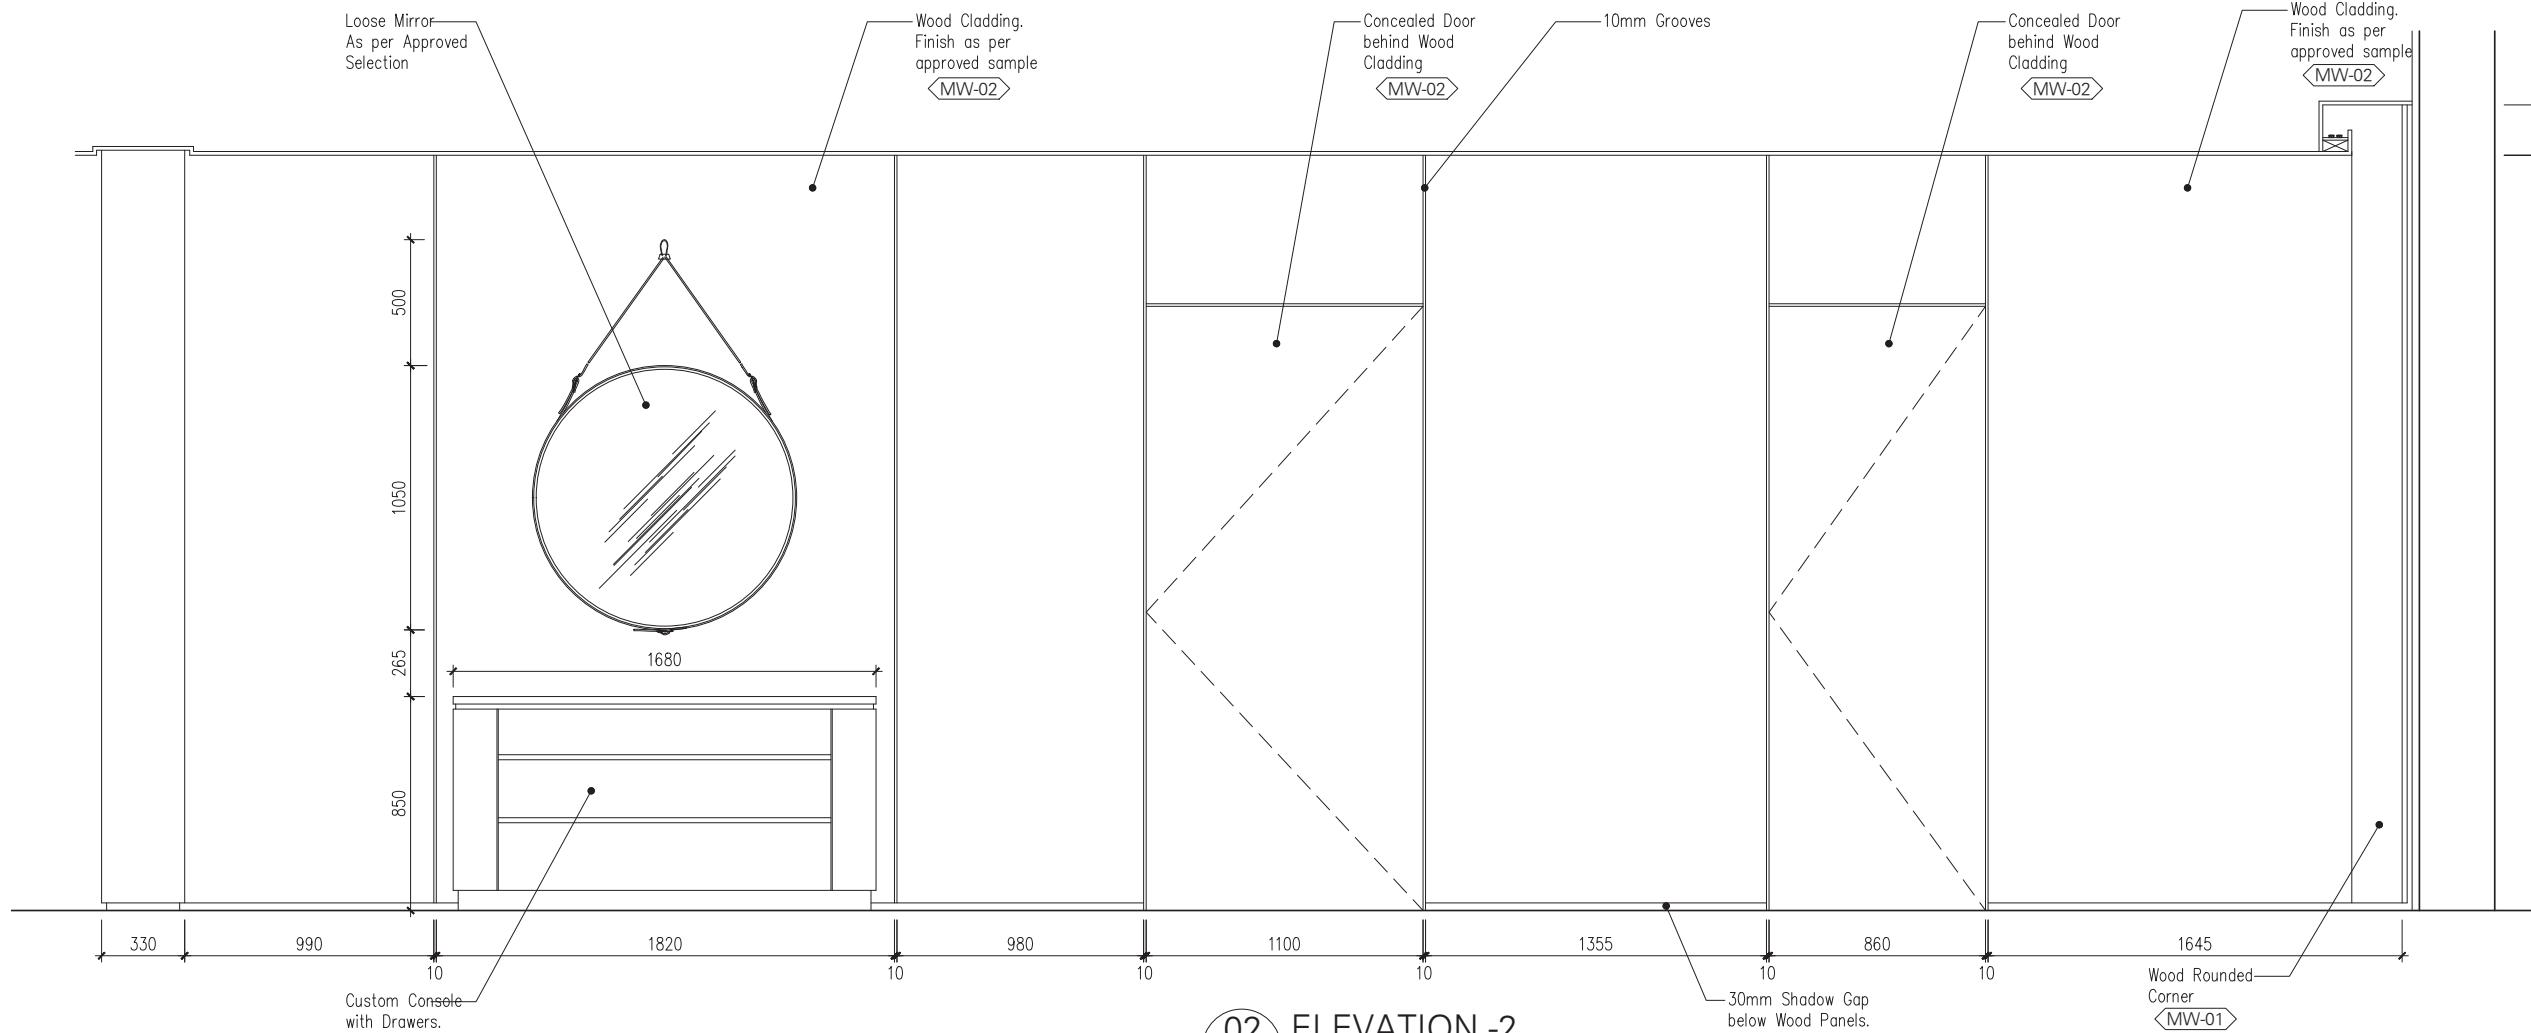

0	2025.06.02	mp	Initial issue
Rev	Date	Drawn	Revisions

**Design Architect:**

**Client:** Zach-Aimee  
**Project Title:** Private Villa -Dubai Hills

**Location:** Dubai, U.A.E.

**Plot Area:** 0000.00 Sqm  
0000.00 SqFt  
**Old Gate Level:** 0.00 = 0.000  
**NEW GATE LEVEL = 0.000**  
Proposed Gate Level is to be 000 mm above existing Asphalt Road Level

**Sheet Contents:**  
FIRST FLOOR  
MASTER BEDROOM  
ELEVATION-2

Designed by:	Drawn By:	Checked By:	Issued By:
ab	mp	ab	ab
Scale: 1:15	Sheet Size: A1	Stage: Conceptual	Rev No: 0

**Drwg No.** ID-304-3



VISUAL - 2

**General Notes:**

- All dimensions are in millimeters unless otherwise noted.
- Any inconsistency or discrepancy is to be brought to the attention of and resolved by the architect/designer.
- All dimensions are to be checked on site before commencing work.
- This drawing is to be coordinated with the Lead Consultant.

**Notes**

- \* ALL DRAWINGS ARE FOR DESIGN INTENT ONLY AND ARE NOT FOR CONSTRUCTION. THE APPOINTED CONTRACTOR SHOULD PROVIDE SHOP DRAWING FOR APPROVAL.
- \* CONTRACTOR TO DO A SITE SURVEY TO SPECIFY CORRECT QUANTITY & DIMENSIONS AS PER SITE MEASUREMENTS & DRAWINGS.
- \* CONTRACTOR TO CHECK THE MECHANISM & FUNCTIONALITY OF THE DESIGN INTEND.
- \* MATERIAL MUST BE PRESENTED TO PRIOR TO PURCHASE FOR TO APPROVE.

0	2025.05.02	mp	Initial issue
Rev	Date	Drawn	Revisions

**Design Architect:**

**Client:** Zach-Aimee  
**Project Title:** Private Villa -Dubai Hills

**Location:** Dubai, U.A.E.

**Plot Area:** 0000.00 Sqm  
0000.00 SqFt  
**Old Gate Level:** 0.00 = 0.000  
**NEW GATE LEVEL = 0.000**  
Proposed Gate Level is to be 000 mm above existing Asphalt Road Level

<b>Sheet Contents:</b>			
FIRST FLOOR MASTER BEDROOM VISUAL - 2			
Designed by: ab Drawn By: mp Checked By: ab Issued By: ab			
Scale:	Sheet Size:	Stage:	Rev No:
1:15	A1	Conceptual Stage	0


**Drwg No.** ID-304-3-R

**General Notes:**

- All dimensions are in millimeters unless otherwise noted.
- Any inconsistency or discrepancy is to be brought to the attention of and resolved by the architect/designer.
- All dimensions are to be checked on site before commencing work.
- This drawing is to be coordinated with the Lead Consultant.

**Notes**

- \* ALL DRAWINGS ARE FOR DESIGN INTENT ONLY AND ARE NOT FOR CONSTRUCTION. THE APPOINTED CONTRACTOR SHOULD PROVIDE SHOP DRAWING FOR APPROVAL.
- \* CONTRACTOR TO DO A SITE SURVEY TO SPECIFY CORRECT QUANTITY & DIMENSIONS AS PER SITE MEASUREMENTS & DRAWINGS.
- \* CONTRACTOR TO CHECK THE MECHANISM & FUNCTIONALITY OF THE DESIGN INTEND.
- \* MATERIAL MUST BE PRESENTED TO PRIOR TO PURCHASE FOR TO APPROVE.

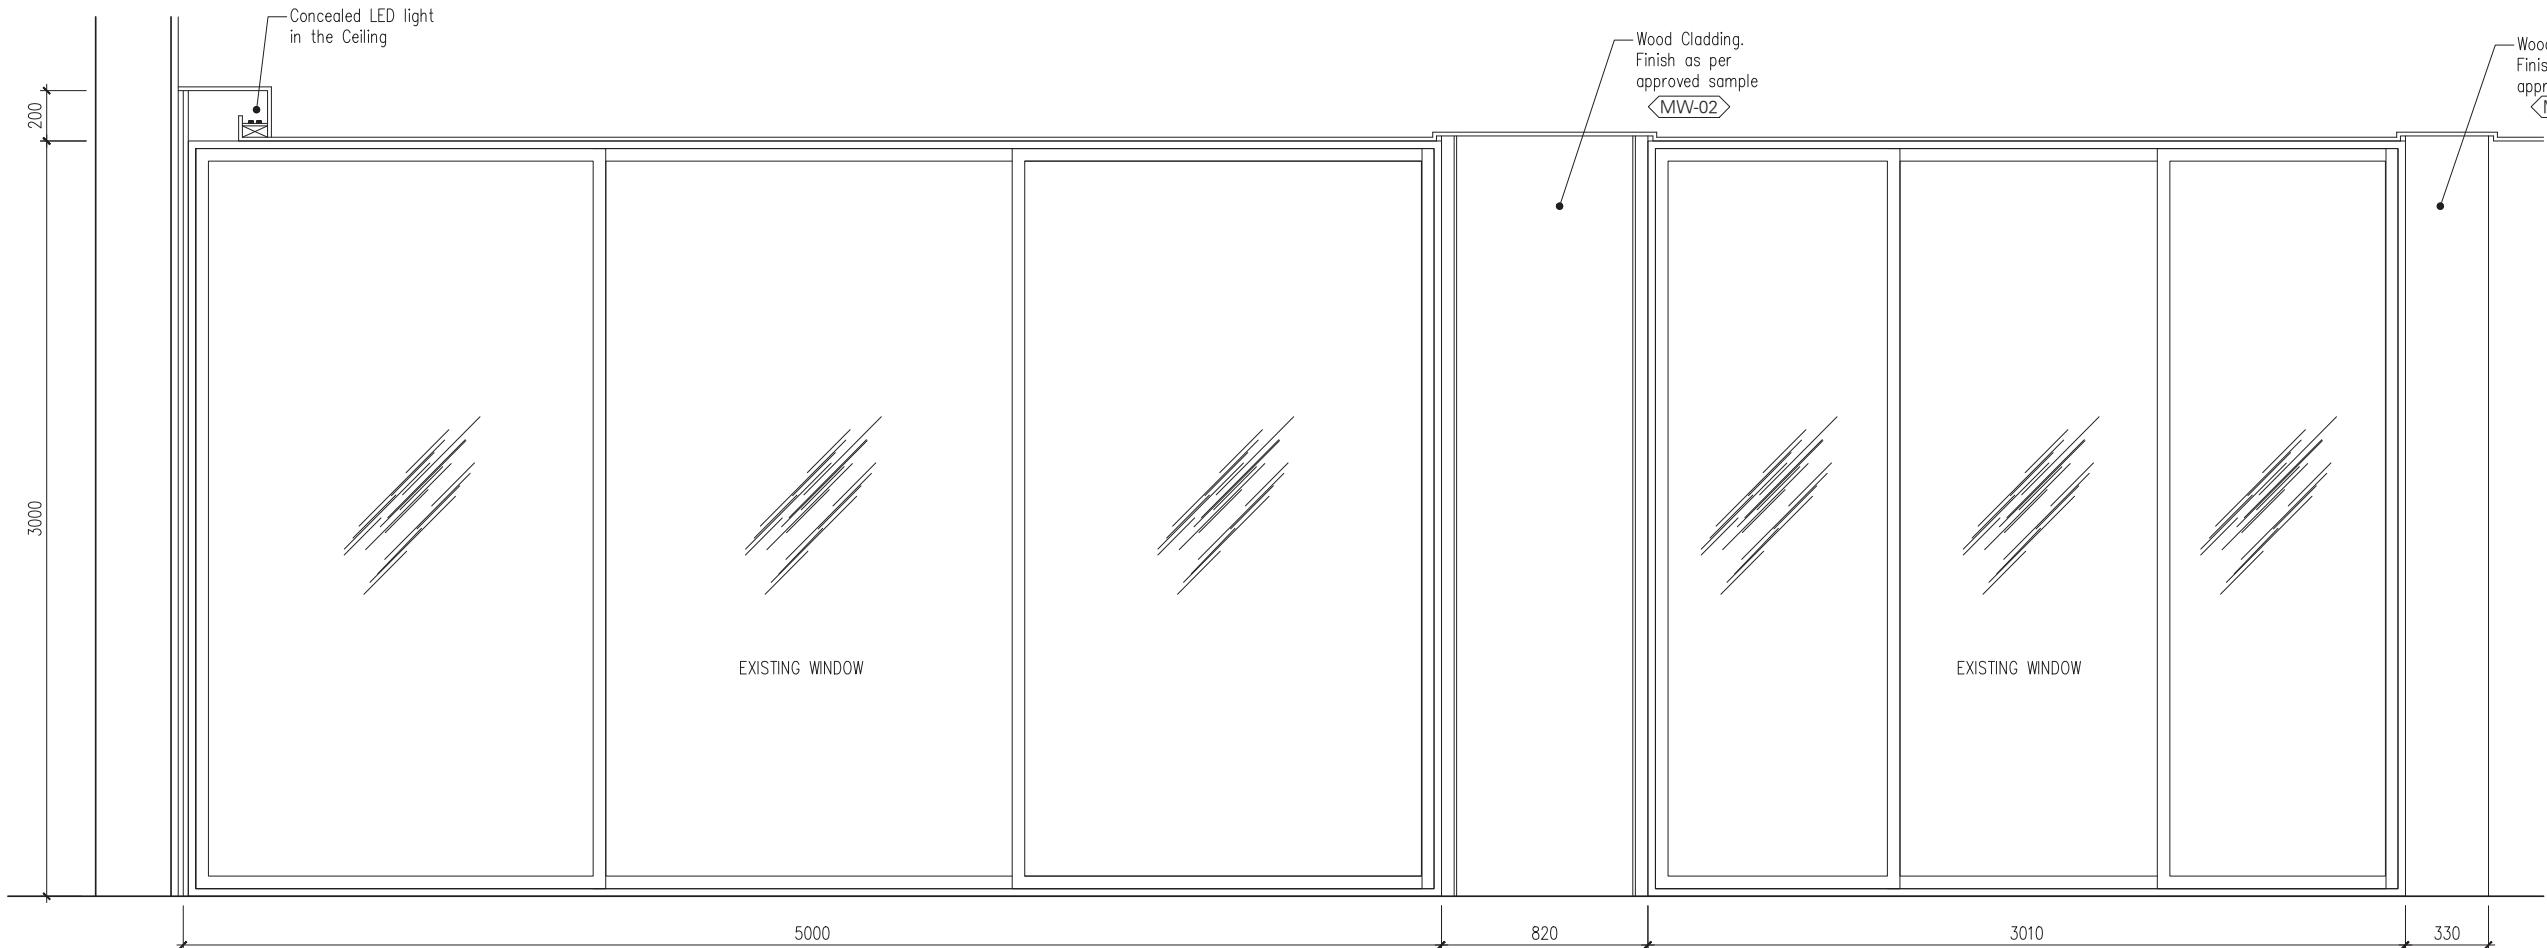

03 ELEVATION -3  
SCALE 1:15

0	2025.05.21	mp	Initial issue
Rev	Date	Drawn	Revisions

**Design Architect:**

**Client:** Zach-Aimee

**Project Title:** Private Villa -Dubai Hills

**Location:** Dubai, U.A.E.

**Plot Area:** 0000.00 Sqm  
0000.00 SqFt  
**Old Gate Level:** 0.00 = 0.000  
**NEW GATE LEVEL** = 0.000  
Proposed Gate Level is to be 000 mm above existing Asphalt Road Level

**Sheet Contents:**  
FIRST FLOOR  
MASTER BEDROOM  
ELEVATION-3  
Designed by: Drawn By: Checked By: Issued By:  
ab mp ab ab

Scale: Sheet Size: Stage: Rev No:  
1:15 A1 Conceptual Stage 0

**Drwg No.** ID-304-4

Page 1 of 1

**General Notes:**

- All dimensions are in millimeters unless otherwise noted.
- Any inconsistency or discrepancy is to be brought to the attention of and resolved by the architect/designer.
- All dimensions are to be checked on site before commencing work.
- This drawing is to be coordinated with the Lead Consultant.


**Notes**

\* ALL DRAWINGS ARE FOR DESIGN INTENT ONLY AND ARE NOT FOR CONSTRUCTION. THE APPOINTED CONTRACTOR SHOULD PROVIDE SHOP DRAWING FOR APPROVAL.

\* CONTRACTOR TO DO A SITE SURVEY TO SPECIFY CORRECT QUANTITY & DIMENSIONS AS PER SITE MEASUREMENTS & DRAWINGS.

\* CONTRACTOR TO CHECK THE MECHANISM & FUNCTIONALITY OF THE DESIGN INTEND.

\* MATERIAL MUST BE PRESENTED TO PRIOR TO PURCHASE FOR TO APPROVE.

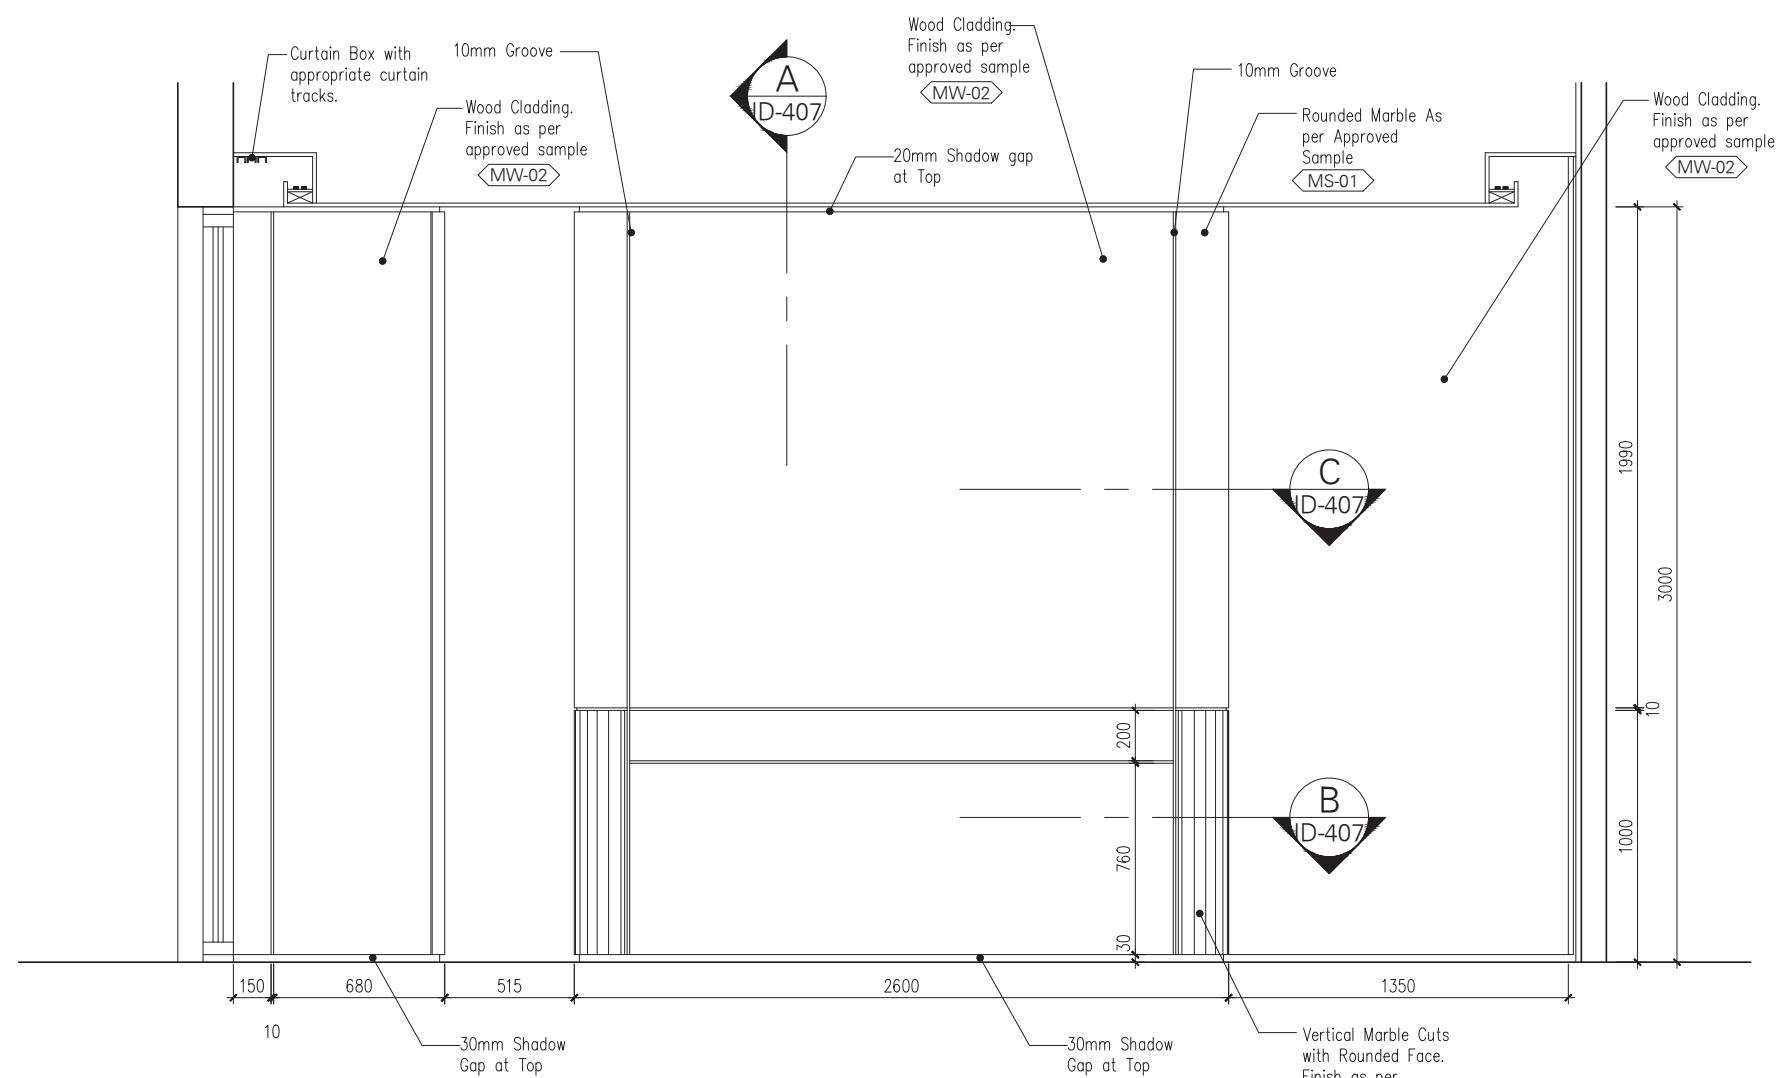

0	2025.05.21	mp	Initial issue
Rev	Date	Drawn	Revisions

**Design Architect:**

**Client:** Zach-Aimee  
**Project Title:** Private Villa -Dubai Hills

**Location:** Dubai, U.A.E.

**Plot Area:** 0000.00 Sqm  
0000.00 SqFt  
**Old Gate Level:** 0.00 = 0.000  
**NEW GATE LEVEL = 0.000**  
Proposed Gate Level is to be 000 mm above existing Asphalt Road Level

<b>Sheet Contents:</b>			
FIRST FLOOR MASTER BEDROOM ELEVATION-4			
Designed by:	Drawn By:	Checked By:	Issued By:
ab	mp	ab	ab

**Scale:** 1:25      **Sheet Size:** A1      **Stage:** Conceptual Stage  
**Rev No:** 0

**Drwg No.** ID-304-5

**General Notes:**

- All dimensions are in millimeters unless otherwise noted.
- Any inconsistency or discrepancy is to be brought to the attention of and resolved by the architect/designer.
- All dimensions are to be checked on site before commencing work.
- This drawing is to be coordinated with the Lead Consultant.


**Notes**

\* ALL DRAWINGS ARE FOR DESIGN INTENT ONLY AND ARE NOT FOR CONSTRUCTION. THE APPOINTED CONTRACTOR SHOULD PROVIDE SHOP DRAWING FOR APPROVAL.

\* CONTRACTOR TO DO A SITE SURVEY TO SPECIFY CORRECT QUANTITY & DIMENSIONS AS PER SITE MEASUREMENTS & DRAWINGS.

\* CONTRACTOR TO CHECK THE MECHANISM & FUNCTIONALITY OF THE DESIGN INTEND.

\* MATERIAL MUST BE PRESENTED TO PRIOR TO PURCHASE FOR TO APPROVE.

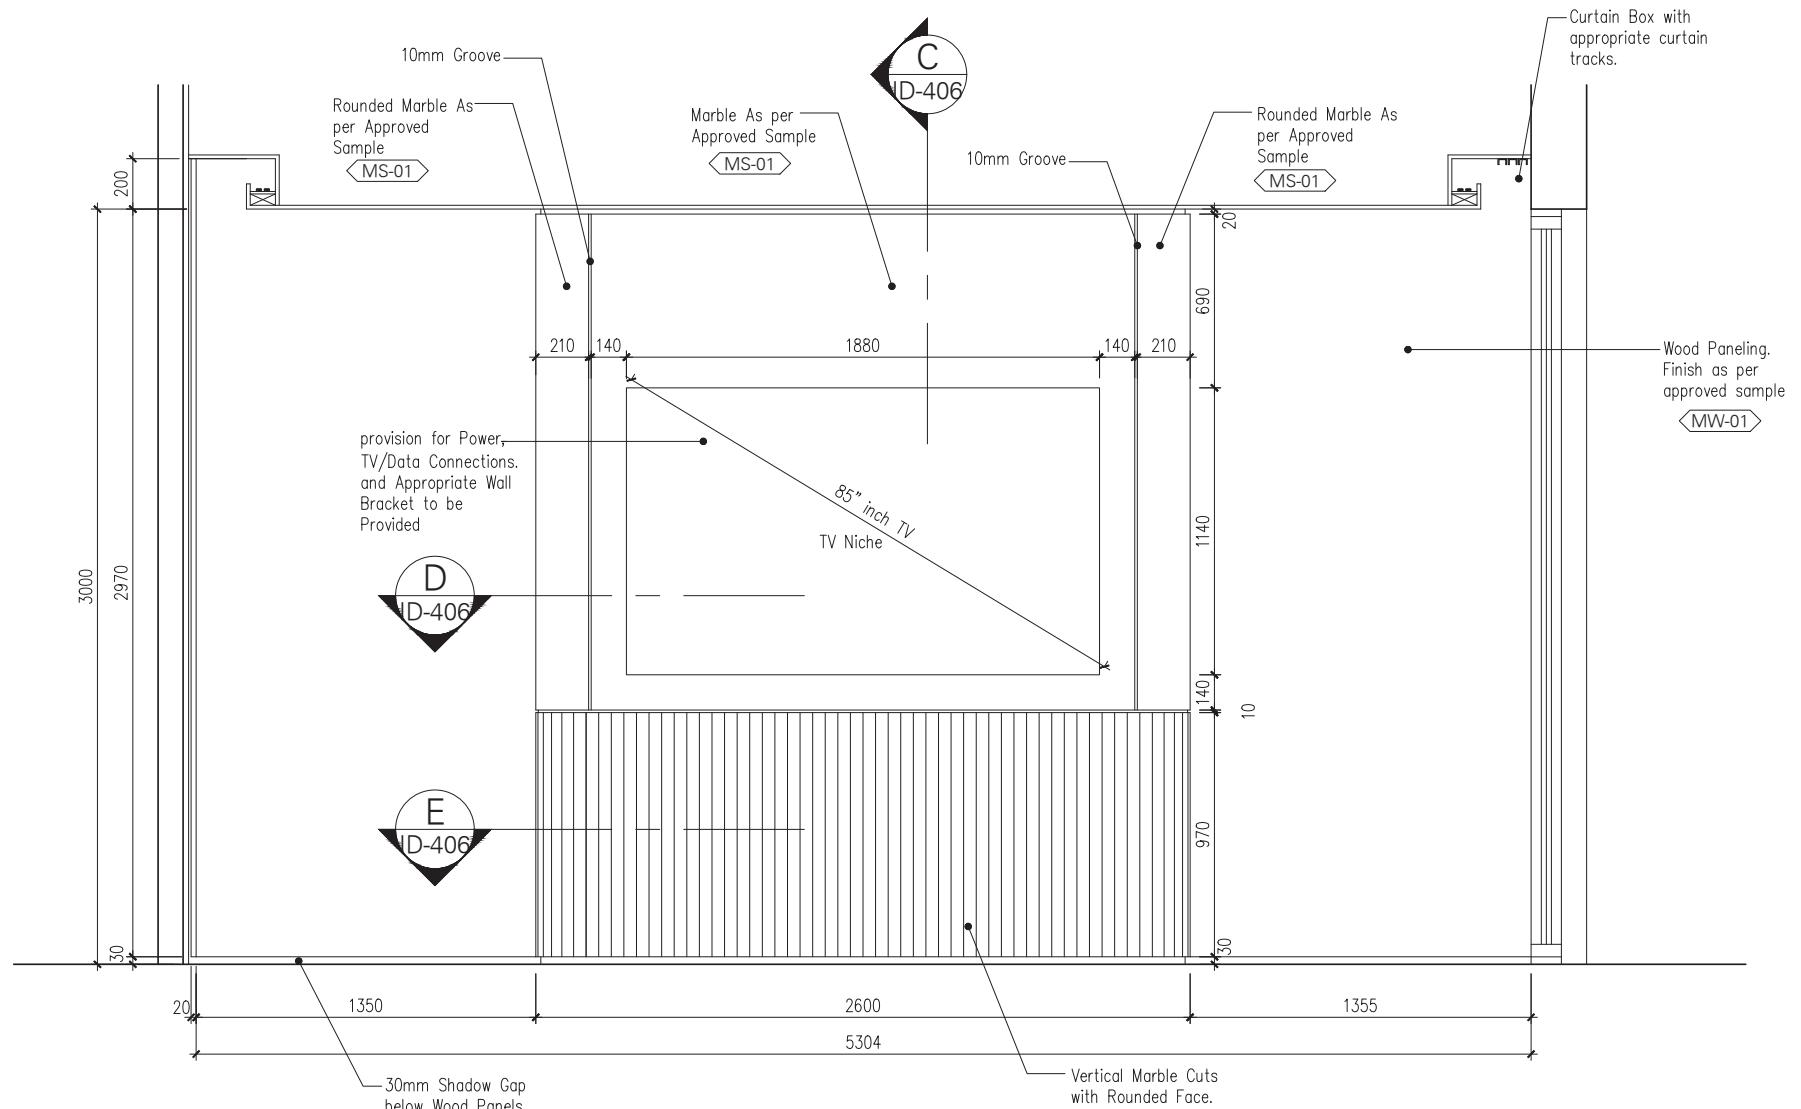

0	2025.05.21	mp	Initial issue
Rev	Date	Drawn	Revisions

**Design Architect:**

**Client:** Zach-Aimee  
**Project Title:** Private Villa -Dubai Hills

**Location:** Dubai, U.A.E.

**Plot Area:** 0000.00 Sqm  
0000.00 SqFt  
**Old Gate Level:** 0.00 = 0.000  
**NEW GATE LEVEL = 0.000**  
Proposed Gate Level is to be 000 mm above existing Asphalt Road Level

<b>Sheet Contents:</b>			
FIRST FLOOR MASTER BEDROOM ELEVATION-5			
Designed by:	Drawn By:	Checked By:	Issued By:
ab	mp	ab	ab

**Scale:** 1:15      **Sheet Size:** A1      **Stage:** Conceptual Stage  
**Rev No:** 0

**Drwg No.** ID-304-6



VISUAL - 3

**General Notes:**

- All dimensions are in millimeters unless otherwise noted.
- Any inconsistency or discrepancy is to be brought to the attention of and resolved by the architect/designer.
- All dimensions are to be checked on site before commencing work.
- This drawing is to be coordinated with the Lead Consultant.

**Notes**

- \* ALL DRAWINGS ARE FOR DESIGN INTENT ONLY AND ARE NOT FOR CONSTRUCTION. THE APPOINTED CONTRACTOR SHOULD PROVIDE SHOP DRAWING FOR APPROVAL.
- \* CONTRACTOR TO DO A SITE SURVEY TO SPECIFY CORRECT QUANTITY & DIMENSIONS AS PER SITE MEASUREMENTS & DRAWINGS.
- \* CONTRACTOR TO CHECK THE MECHANISM & FUNCTIONALITY OF THE DESIGN INTEND.
- \* MATERIAL MUST BE PRESENTED TO PRIOR TO PURCHASE FOR TO APPROVE.

0	2025.05.02	mp	Initial issue
Rev	Date	Drawn	Revisions

**Design Architect:**

**Client:** Zach-Aimee  
**Project Title:** Private Villa -Dubai Hills

**Location:** Dubai, U.A.E.

**Plot Area:** 0000.00 Sqm  
0000.00 SqFt  
**Old Gate Level:** 0.00 = 0.000  
**NEW GATE LEVEL = 0.000**

Proposed Gate Level is to be 000 mm above existing Asphalt Road Level

<b>Sheet Contents:</b>			
FIRST FLOOR			
MASTER BEDROOM			
Designed by:	Drawn By:	Checked By:	Issued By:
ab	mp	ab	ab
Scale:	Sheet Size:	Stage:	Rev No:
1:15	A1	Conceptual Stage	0

**Drwg No.** ID-304-6-R

**General Notes:**

- All dimensions are in millimeters unless otherwise noted.
- Any inconsistency or discrepancy is to be brought to the attention of and resolved by the architect/designer.
- All dimensions are to be checked on site before commencing work.
- This drawing is to be coordinated with the Lead Consultant.



**Notes**

\* ALL DRAWINGS ARE FOR DESIGN INTENT ONLY AND ARE NOT FOR CONSTRUCTION. THE APPOINTED CONTRACTOR SHOULD PROVIDE SHOP DRAWING FOR APPROVAL.

\* CONTRACTOR TO DO A SITE SURVEY TO SPECIFY CORRECT QUANTITY & DIMENSIONS AS PER SITE MEASUREMENTS & DRAWINGS.

\* CONTRACTOR TO CHECK THE MECHANISM & FUNCTIONALITY OF THE DESIGN INTEND.

\* MATERIAL MUST BE PRESENTED TO PRIOR TO PURCHASE FOR TO APPROVE.

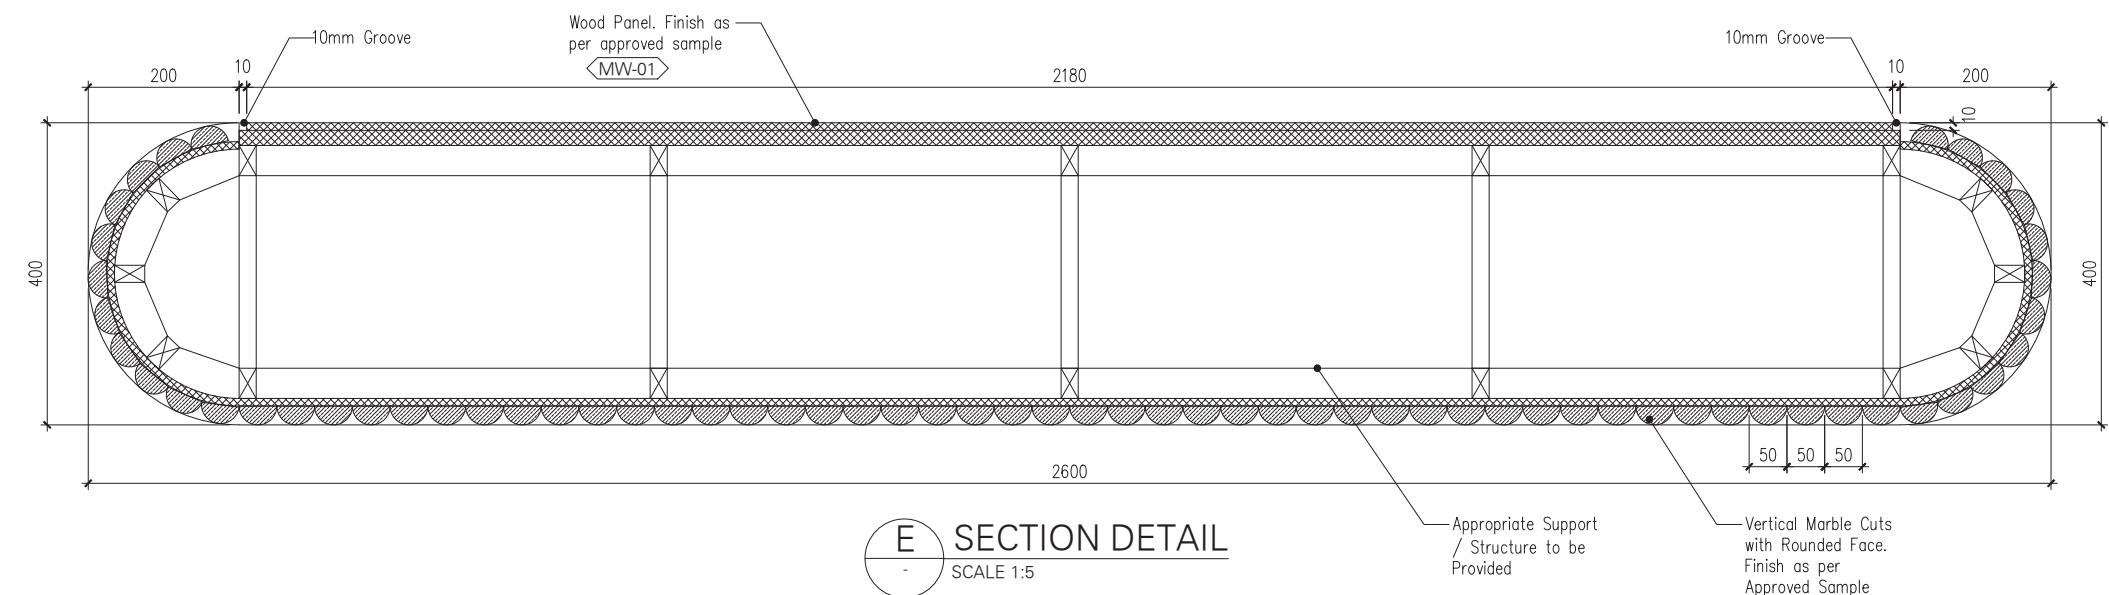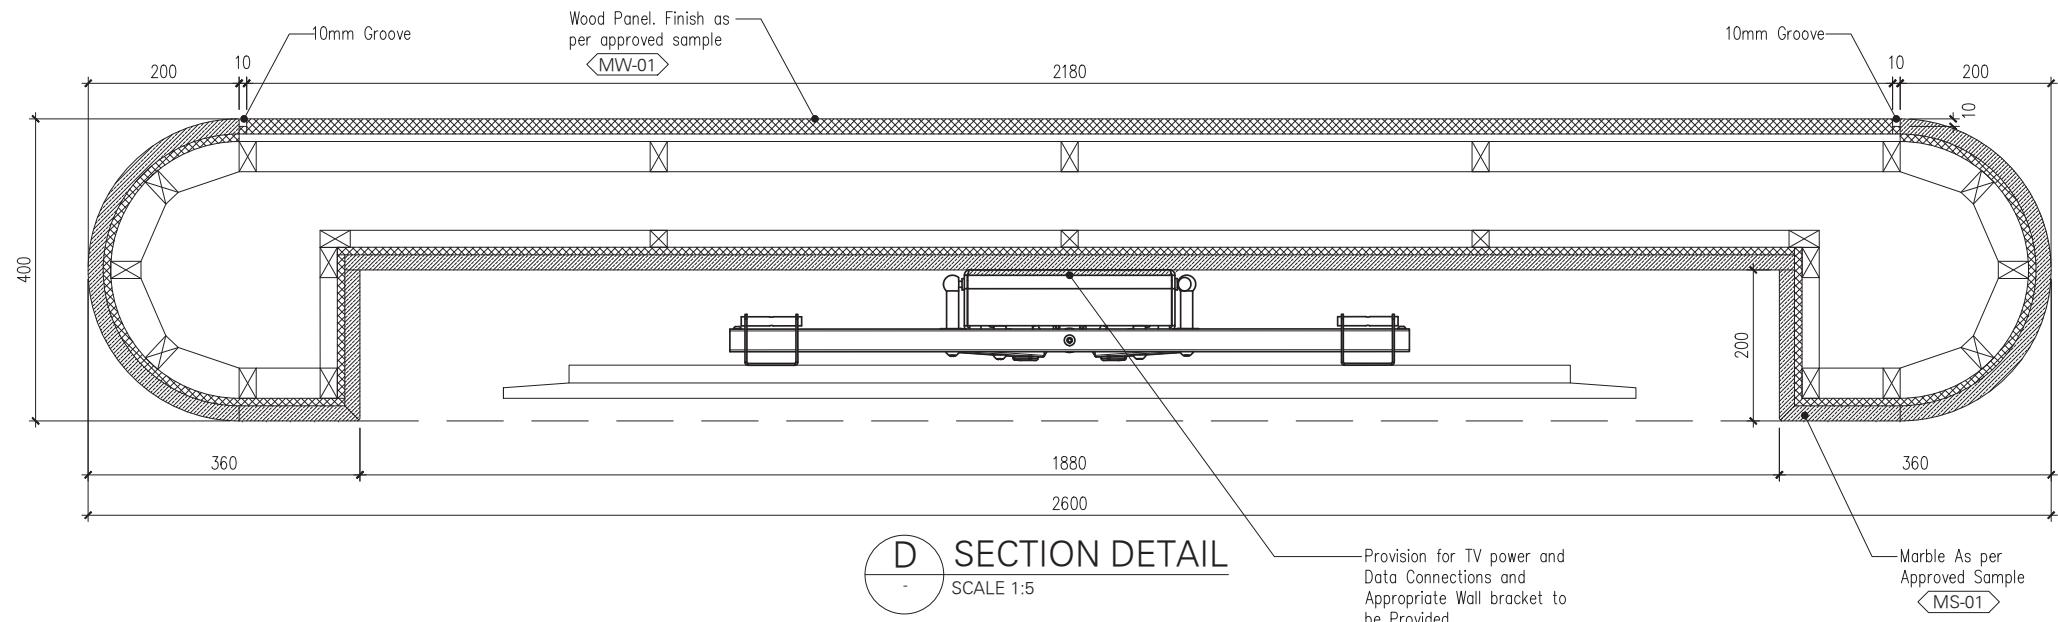

0	2025.06.02	mp	Initial issue
Rev	Date	Drawn	Revisions

**Design Architect:**

**Client:** Zach-Aimee  
**Project Title:** Private Villa -Dubai Hills

**Location:** Dubai, U.A.E.

**Plot Area:** 0000.00 Sqm  
0000.00 SqFt  
**Old Gate Level:** 0.00 = 0.000  
**NEW GATE LEVEL = 0.000**  
Proposed Gate Level is to be 000 mm above existing Asphalt Road Level

<b>Sheet Contents:</b>			
FIRST FLOOR MASTER BEDROOM SECTION DETAILS D & E			
Designed by:	Drawn By:	Checked By:	Issued By:
ab	mp	ab	ab

Scale: 1:5 Sheet Size: A1 Stage: Conceptual Rev No: 0



Drwg No. ID-304-7

**General Notes:**

- All dimensions are in millimeters unless otherwise noted.
- Any inconsistency or discrepancy is to be brought to the attention of and resolved by the architect/designer.
- All dimensions are to be checked on site before commencing work.
- This drawing is to be coordinated with the Lead Consultant.

**Notes**

- \* ALL DRAWINGS ARE FOR DESIGN INTENT ONLY AND ARE NOT FOR CONSTRUCTION. THE APPOINTED CONTRACTOR SHOULD PROVIDE SHOP DRAWING FOR APPROVAL.
- \* CONTRACTOR TO DO A SITE SURVEY TO SPECIFY CORRECT QUANTITY & DIMENSIONS AS PER SITE MEASUREMENTS & DRAWINGS.
- \* CONTRACTOR TO CHECK THE MECHANISM & FUNCTIONALITY OF THE DESIGN INTEND.
- \* MATERIAL MUST BE PRESENTED TO PRIOR TO PURCHASE FOR TO APPROVE.

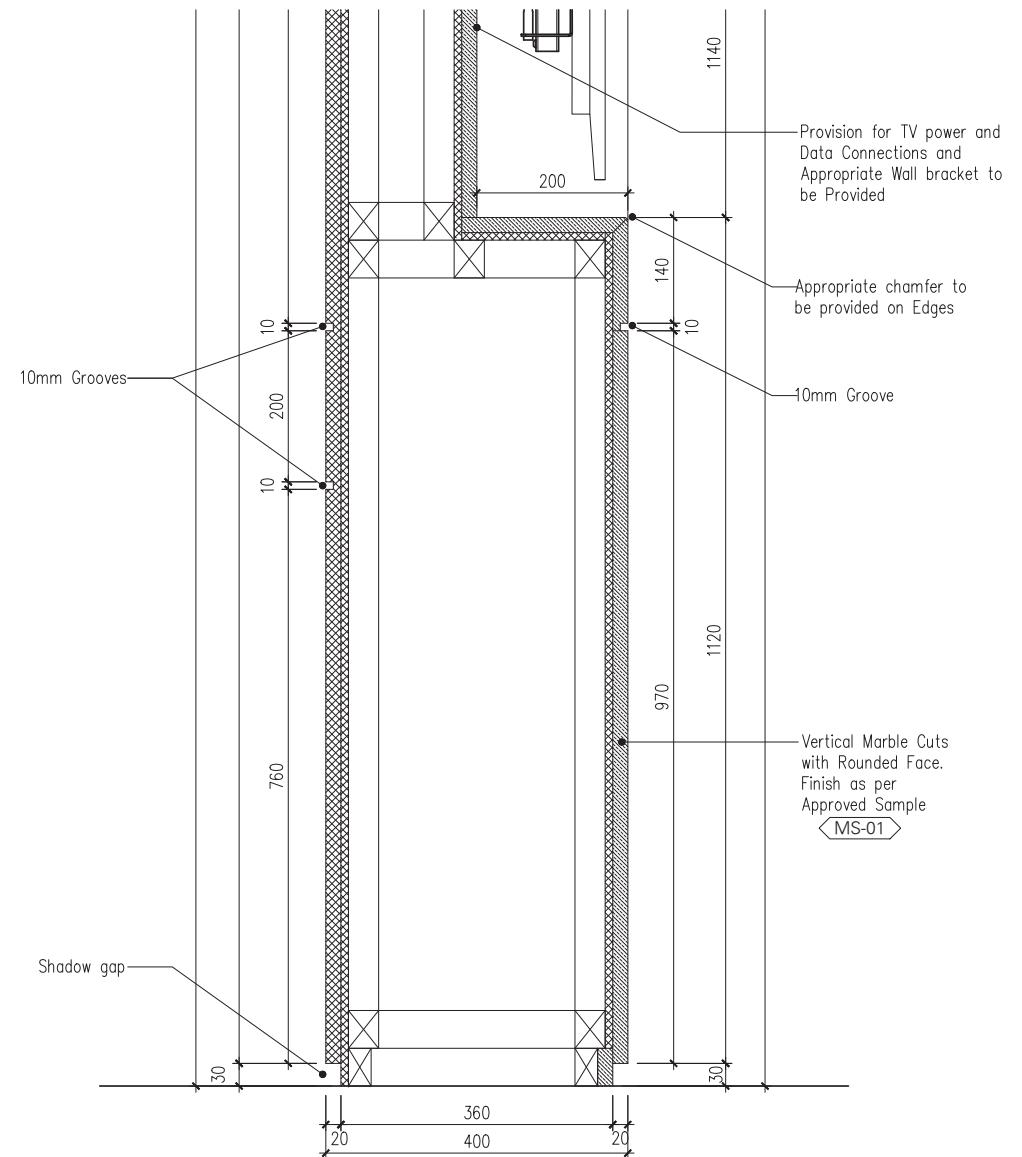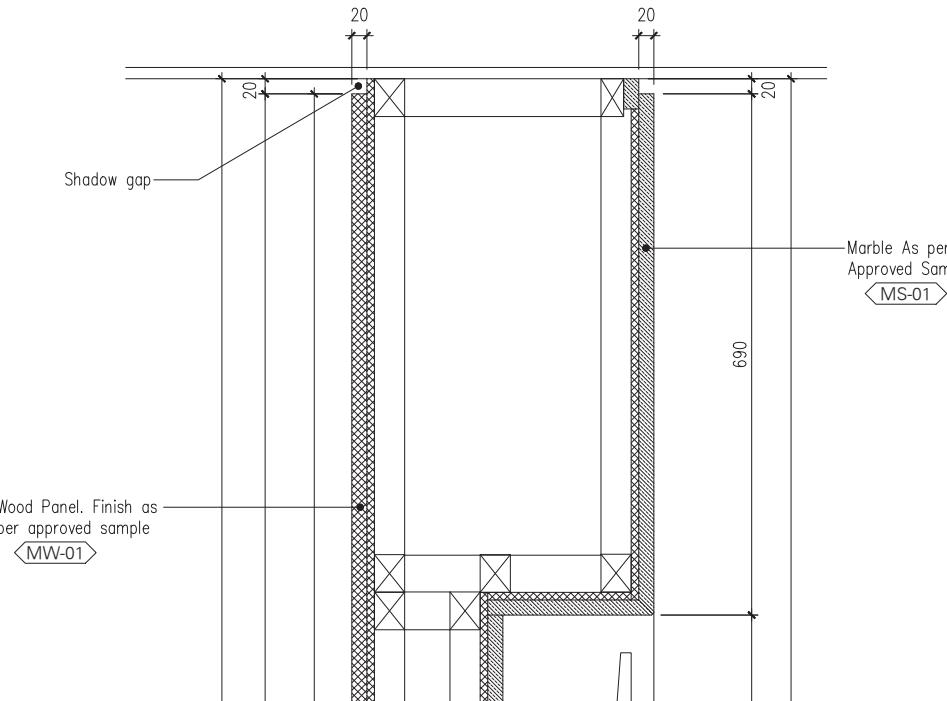

**C SECTION DETAIL**  
SCALE 1:5

0	2025.06.02	mp	Initial issue
Rev	Date	Drawn	Revisions

**Design Architect:**

**Client:**  
Zach-Aimee

**Project Title:**  
Private Villa -Dubai Hills

**Location:**  
Dubai, U.A.E.


**Plot Area:** 0000.00 Sqm  
0000.00 SqFt  
**Old Gate Level:** 0.00 = 0.000  
**NEW GATE LEVEL = 0.000**  
Proposed Gate Level is to be 000 mm above existing Asphalt Road Level

**Sheet Contents:**  
FIRST FLOOR  
MASTER BEDROOM  
SECTION DETAIL - C

Designed by:	Drawn By:	Checked By:	Issued By:
ab	mp	ab	ab

**Scale:** 1:5      **Sheet Size:** A1      **Stage:** Conceptual Stage      **Rev No:** 0

**Drwg No.** ID-304-8

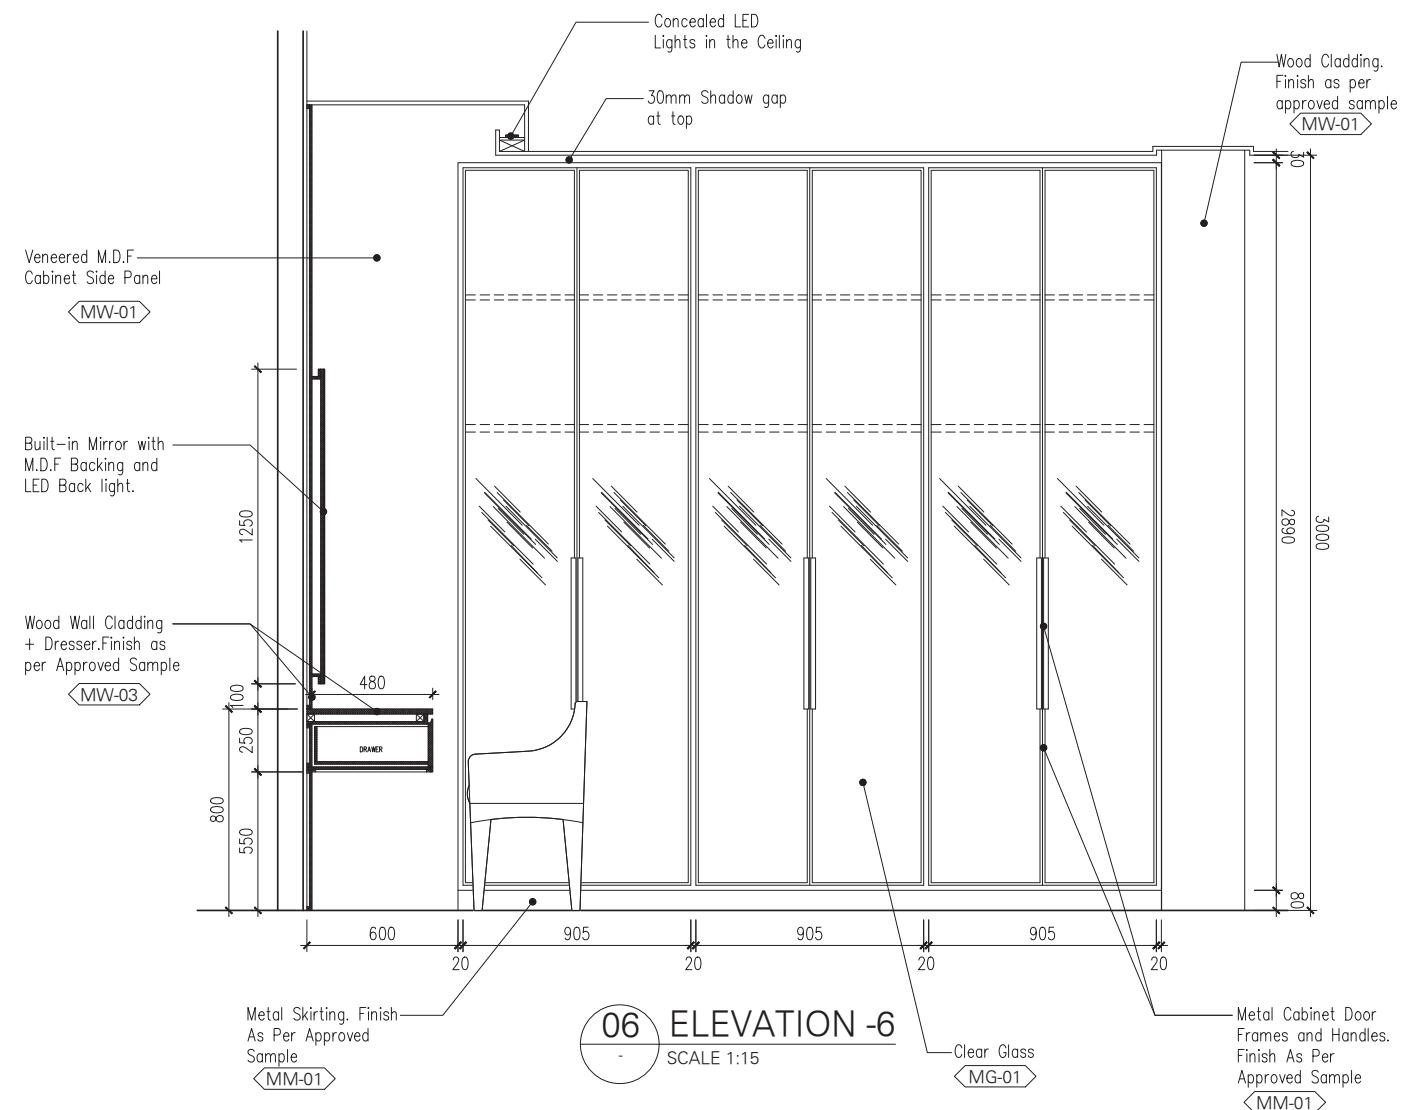

**06 ELEVATION -6**  
- SCALE 1:15

- ) SCALE 1:15

**General Notes:**

- All dimensions are in millimeters unless otherwise noted.
- Any inconsistency or discrepancy is to be brought to the attention of and resolved by the architect/designer.
- All dimensions are to be checked on site before commencing work.
- This drawing is to be coordinated with the Lead Consultant.


**Notes**

\* ALL DRAWINGS ARE FOR DESIGN INTENT ONLY AND ARE NOT FOR CONSTRUCTION. THE APPOINTED CONTRACTOR SHOULD PROVIDE SHOP DRAWING FOR APPROVAL.

\* CONTRACTOR TO DO A SITE SURVEY TO SPECIFY CORRECT QUANTITY & DIMENSIONS AS PER SITE MEASUREMENTS & DRAWINGS.

\* CONTRACTOR TO CHECK THE MECHANISM & FUNCTIONALITY OF THE DESIGN INTEND.

\* MATERIAL MUST BE PRESENTED TO PRIOR TO PURCHASE FOR TO APPROVE.

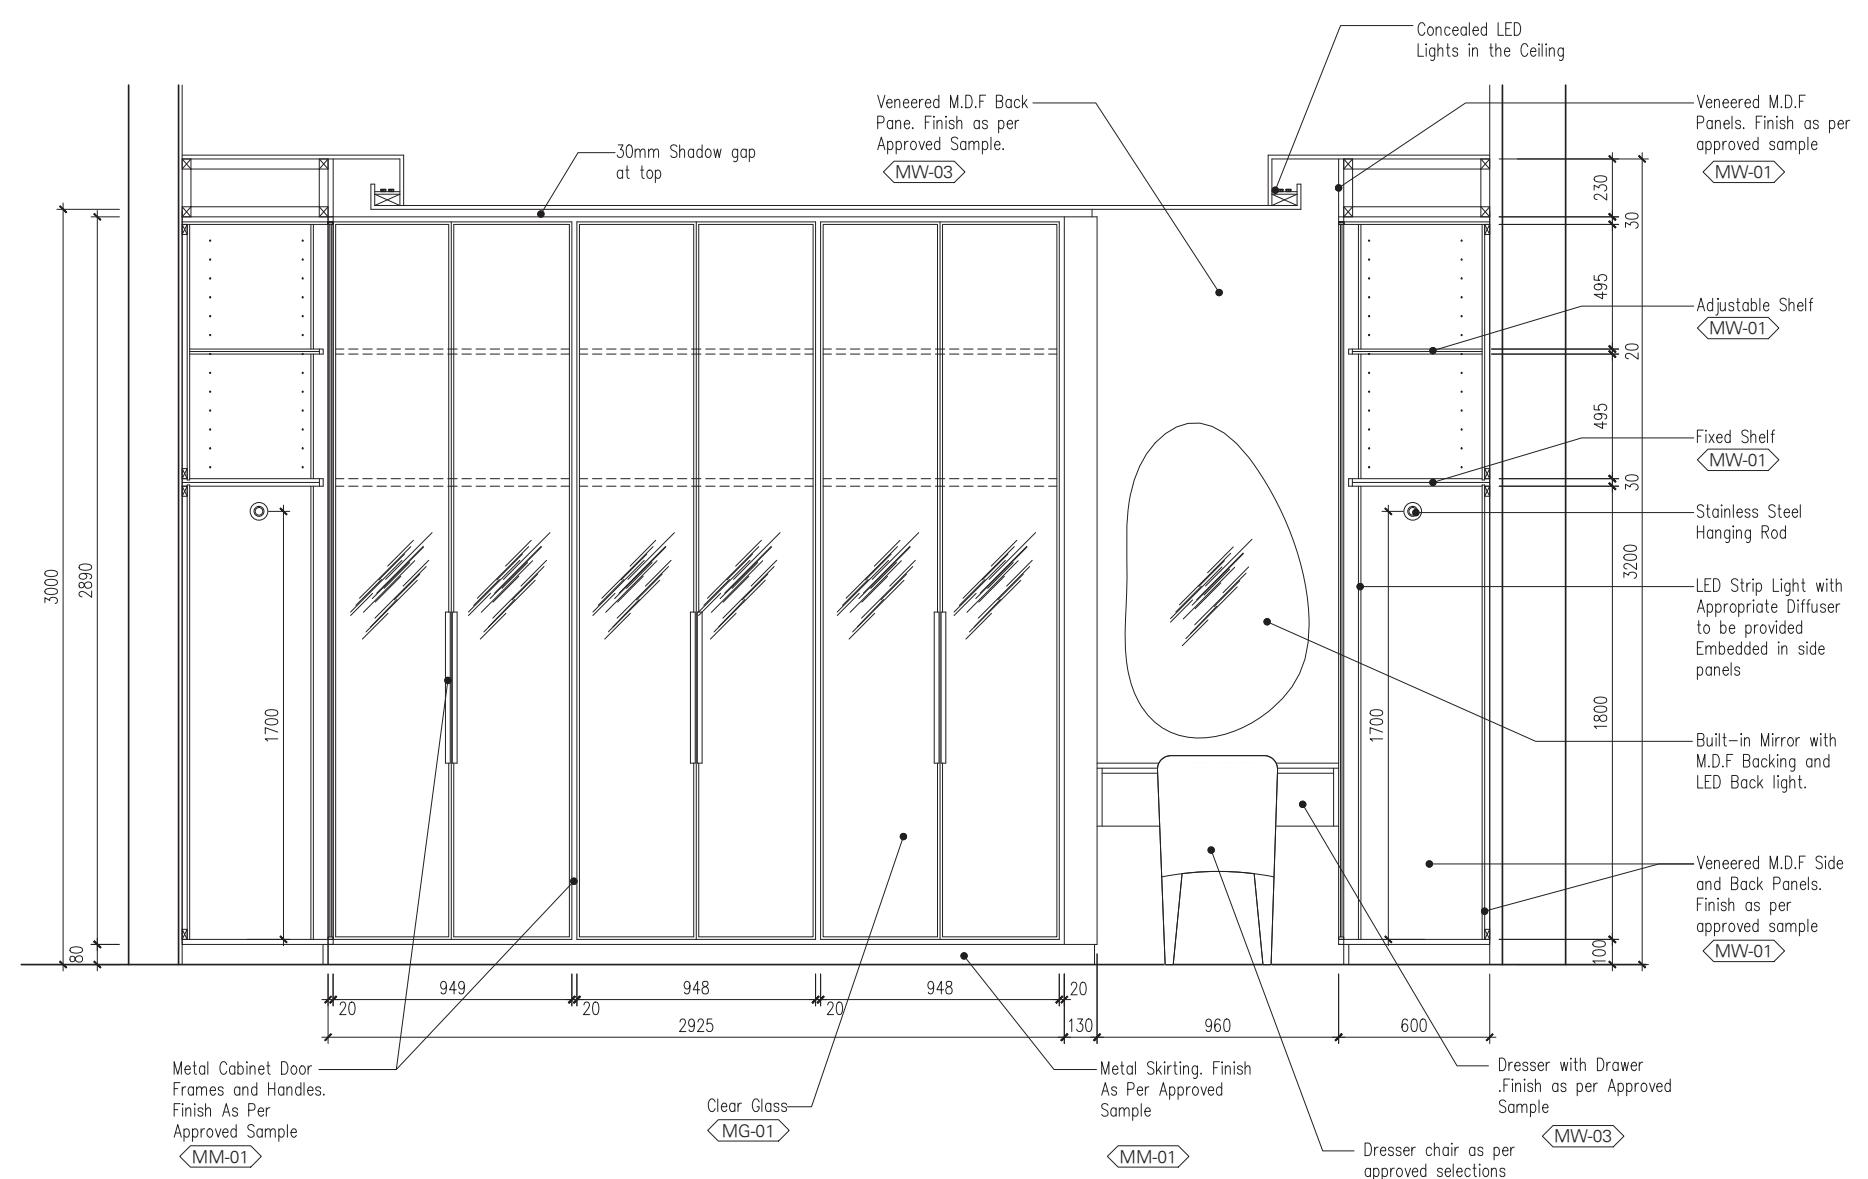

0	2025.06.02	mp	Initial issue
Rev	Date	Drawn	Revisions

**Design Architect:**

**Client:** Zach-Aimee

**Project Title:** Private Villa -Dubai Hills

**Location:** Dubai, U.A.E.

**Plot Area:** 0000.00 Sqm  
0000.00 SqFt  
**Old Gate Level:** 0.00 = 0.000  
**NEW GATE LEVEL = 0.000**  
Proposed Gate Level is to be 000 mm above existing Asphalt Road Level

<b>Sheet Contents:</b>			
FIRST FLOOR MASTER BEDROOM ELEVATION-7			
Designed by:	Drawn By:	Checked By:	Issued By:
ab	mp	ab	ab


**Scale:** 1:15 **Sheet Size:** A1 **Stage:** Conceptual Stage **Rev No:** 0

**Drwg No.** ID-304-8



VISUAL - 4

General Notes:															
1. All dimensions are in millimeters unless otherwise noted.															
2. Any inconsistency or discrepancy is to be brought to the attention of and resolved by the architect/designer.															
3. All dimensions are to be checked on site before commencing work.															
4. This drawing is to be coordinated with the Lead Consultant.															
Notes															
* ALL DRAWINGS ARE FOR DESIGN INTENT ONLY AND ARE NOT FOR CONSTRUCTION. THE APPOINTED CONTRACTOR SHOULD PROVIDE SHOP DRAWING FOR APPROVAL.															
* CONTRACTOR TO DO A SITE SURVEY TO SPECIFY CORRECT QUANTITY & DIMENSIONS AS PER SITE MEASUREMENTS & DRAWINGS.															
* CONTRACTOR TO CHECK THE MECHANISM & FUNCTIONALITY OF THE DESIGN INTEND.															
* MATERIAL MUST BE PRESENTED TO PRIOR TO PURCHASE FOR TO APPROVE.															
<table border="1"> <tr><td>0</td><td>2025.05.02</td><td>mp</td><td>Initial issue</td></tr> <tr><td>Rev</td><td>Date</td><td>Drawn</td><td>Revisions</td></tr> </table>				0	2025.05.02	mp	Initial issue	Rev	Date	Drawn	Revisions				
0	2025.05.02	mp	Initial issue												
Rev	Date	Drawn	Revisions												
Design Architect:															
<table border="1"> <tr><td>Client:</td><td>Zach-Aimee</td></tr> <tr><td>Project Title:</td><td>Private Villa -Dubai Hills</td></tr> <tr><td>Location:</td><td>Dubai, U.A.E.</td></tr> <tr><td>Plot Area:</td><td>0000.00 Sqm 0000.00 SqFt</td></tr> <tr><td>Old Gate Level:</td><td>0.00 = 0.000</td></tr> <tr><td>NEW GATE LEVEL =</td><td>0.000</td></tr> </table>				Client:	Zach-Aimee	Project Title:	Private Villa -Dubai Hills	Location:	Dubai, U.A.E.	Plot Area:	0000.00 Sqm 0000.00 SqFt	Old Gate Level:	0.00 = 0.000	NEW GATE LEVEL =	0.000
Client:	Zach-Aimee														
Project Title:	Private Villa -Dubai Hills														
Location:	Dubai, U.A.E.														
Plot Area:	0000.00 Sqm 0000.00 SqFt														
Old Gate Level:	0.00 = 0.000														
NEW GATE LEVEL =	0.000														
Proposed Gate Level is to be 000 mm above existing Asphalt Road Level															
Sheet Contents:															
FIRST FLOOR MASTER BEDROOM VISUAL - 4															
Designed by:	Drawn By:	Checked By:	Issued By:												
ab	mp	ab	ab												
Scale:	Sheet Size:	Stage:	Rev No:												
1:15	A1	Conceptual Stage	0												
Drwg No. ID-304-10-R															

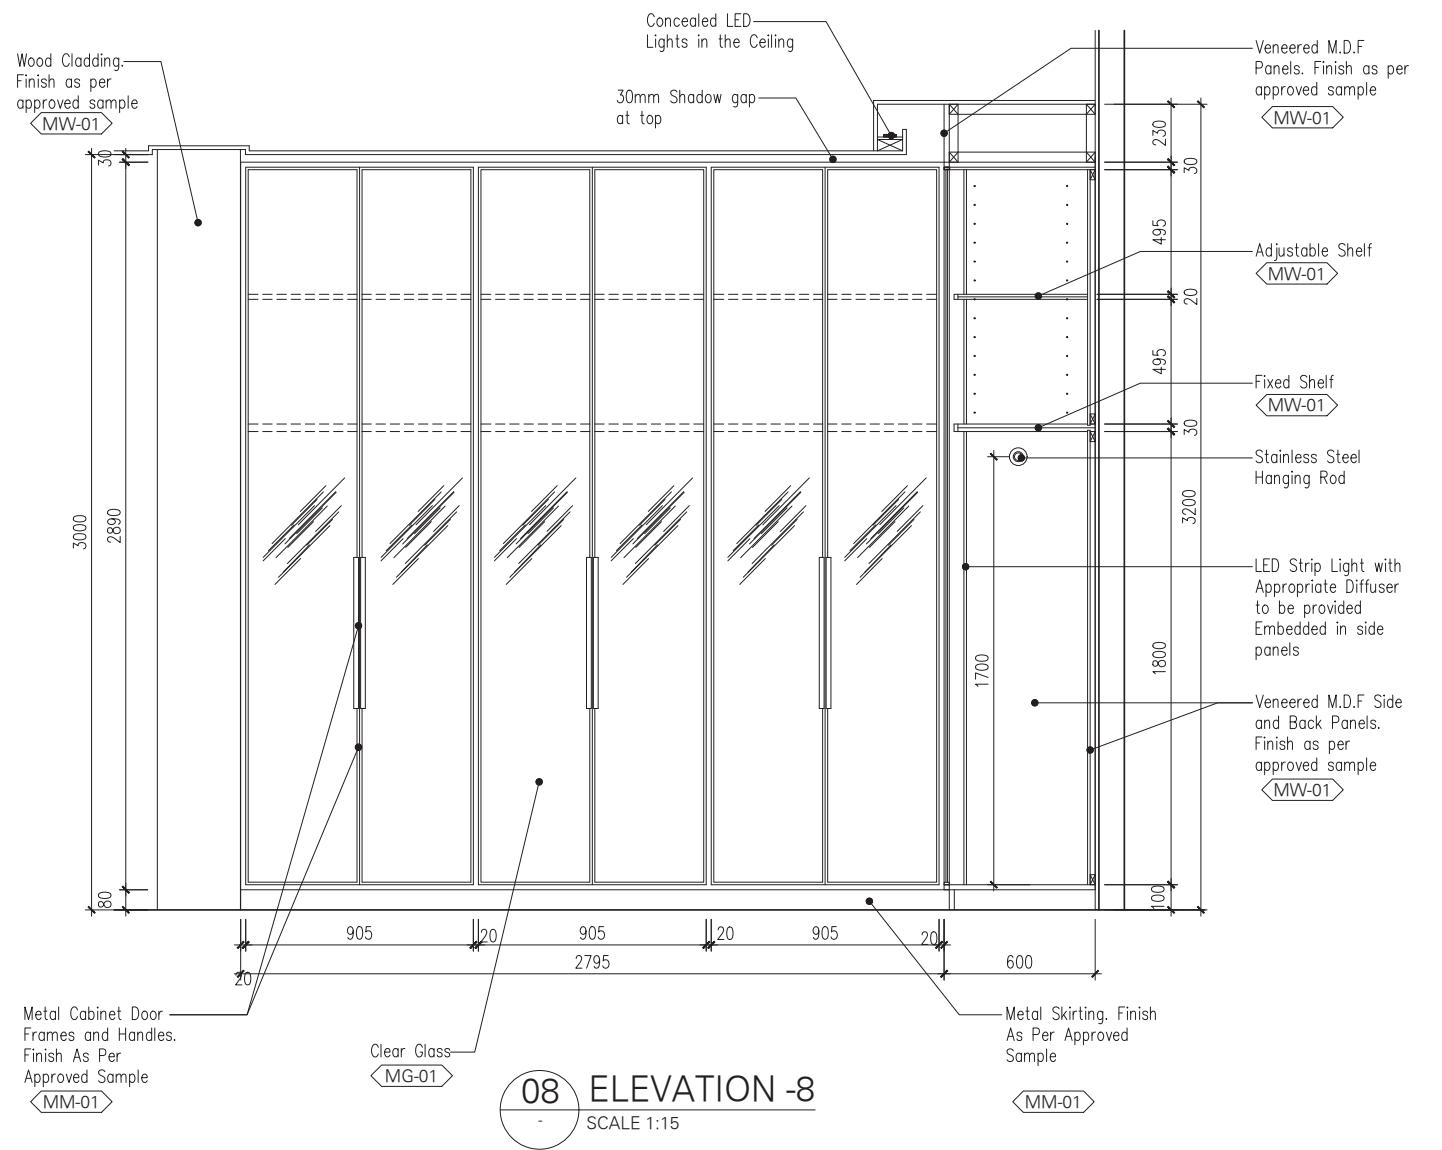

08 ELEVATION -8  
SCALE 1:15

**General Notes:**

- All dimensions are in millimeters unless otherwise noted.
- Any inconsistency or discrepancy is to be brought to the attention of and resolved by the architect/designer.
- All dimensions are to be checked on site before commencing work.
- This drawing is to be coordinated with the Lead Consultant.

**Notes**

- \* ALL DRAWINGS ARE FOR DESIGN INTENT ONLY AND ARE NOT FOR CONSTRUCTION. THE APPOINTED CONTRACTOR SHOULD PROVIDE SHOP DRAWING FOR APPROVAL.
- \* CONTRACTOR TO DO A SITE SURVEY TO SPECIFY CORRECT QUANTITY & DIMENSIONS AS PER SITE MEASUREMENTS & DRAWINGS.
- \* CONTRACTOR TO CHECK THE MECHANISM & FUNCTIONALITY OF THE DESIGN INTEND.
- \* MATERIAL MUST BE PRESENTED TO PRIOR TO PURCHASE FOR TO APPROVE.

0	2025.06.02	mp	Initial issue
Rev	Date	Drawn	Revisions

**Design Architect:**

**Client:**  
Zach-Aimee

**Project Title:**  
Private Villa -Dubai Hills

**Location:**  
Dubai, U.A.E.

**Plot Area:** 0000.00 Sqm  
0000.00 SqFt  
**Old Gate Level:** 0.00 = 0.000  
**NEW GATE LEVEL = 0.000**  
Proposed Gate Level is to be 000 mm above existing Asphalt Road Level

**Sheet Contents:**  
FIRST FLOOR  
MASTER BEDROOM  
ELEVATION-8

Designed by:	Drawn By:	Checked By:	Issued By:
ab	mp	ab	ab

**Scale:** 1:15      **Sheet Size:** A1      **Stage:** Conceptual Stage      **Rev No:** 0

**Drwg No.** ID-304-9

**General Notes:**

- All dimensions are in millimeters unless otherwise noted.
- Any inconsistency or discrepancy is to be brought to the attention of and resolved by the architect/designer.
- All dimensions are to be checked on site before commencing work.
- This drawing is to be coordinated with the Lead Consultant.


**Notes**

\* ALL DRAWINGS ARE FOR DESIGN INTENT ONLY AND ARE NOT FOR CONSTRUCTION. THE APPOINTED CONTRACTOR SHOULD PROVIDE SHOP DRAWING FOR APPROVAL.

\* CONTRACTOR TO DO A SITE SURVEY TO SPECIFY CORRECT QUANTITY & DIMENSIONS AS PER SITE MEASUREMENTS & DRAWINGS.

\* CONTRACTOR TO CHECK THE MECHANISM & FUNCTIONALITY OF THE DESIGN INTEND.

\* MATERIAL MUST BE PRESENTED TO PRIOR TO PURCHASE FOR TO APPROVE.

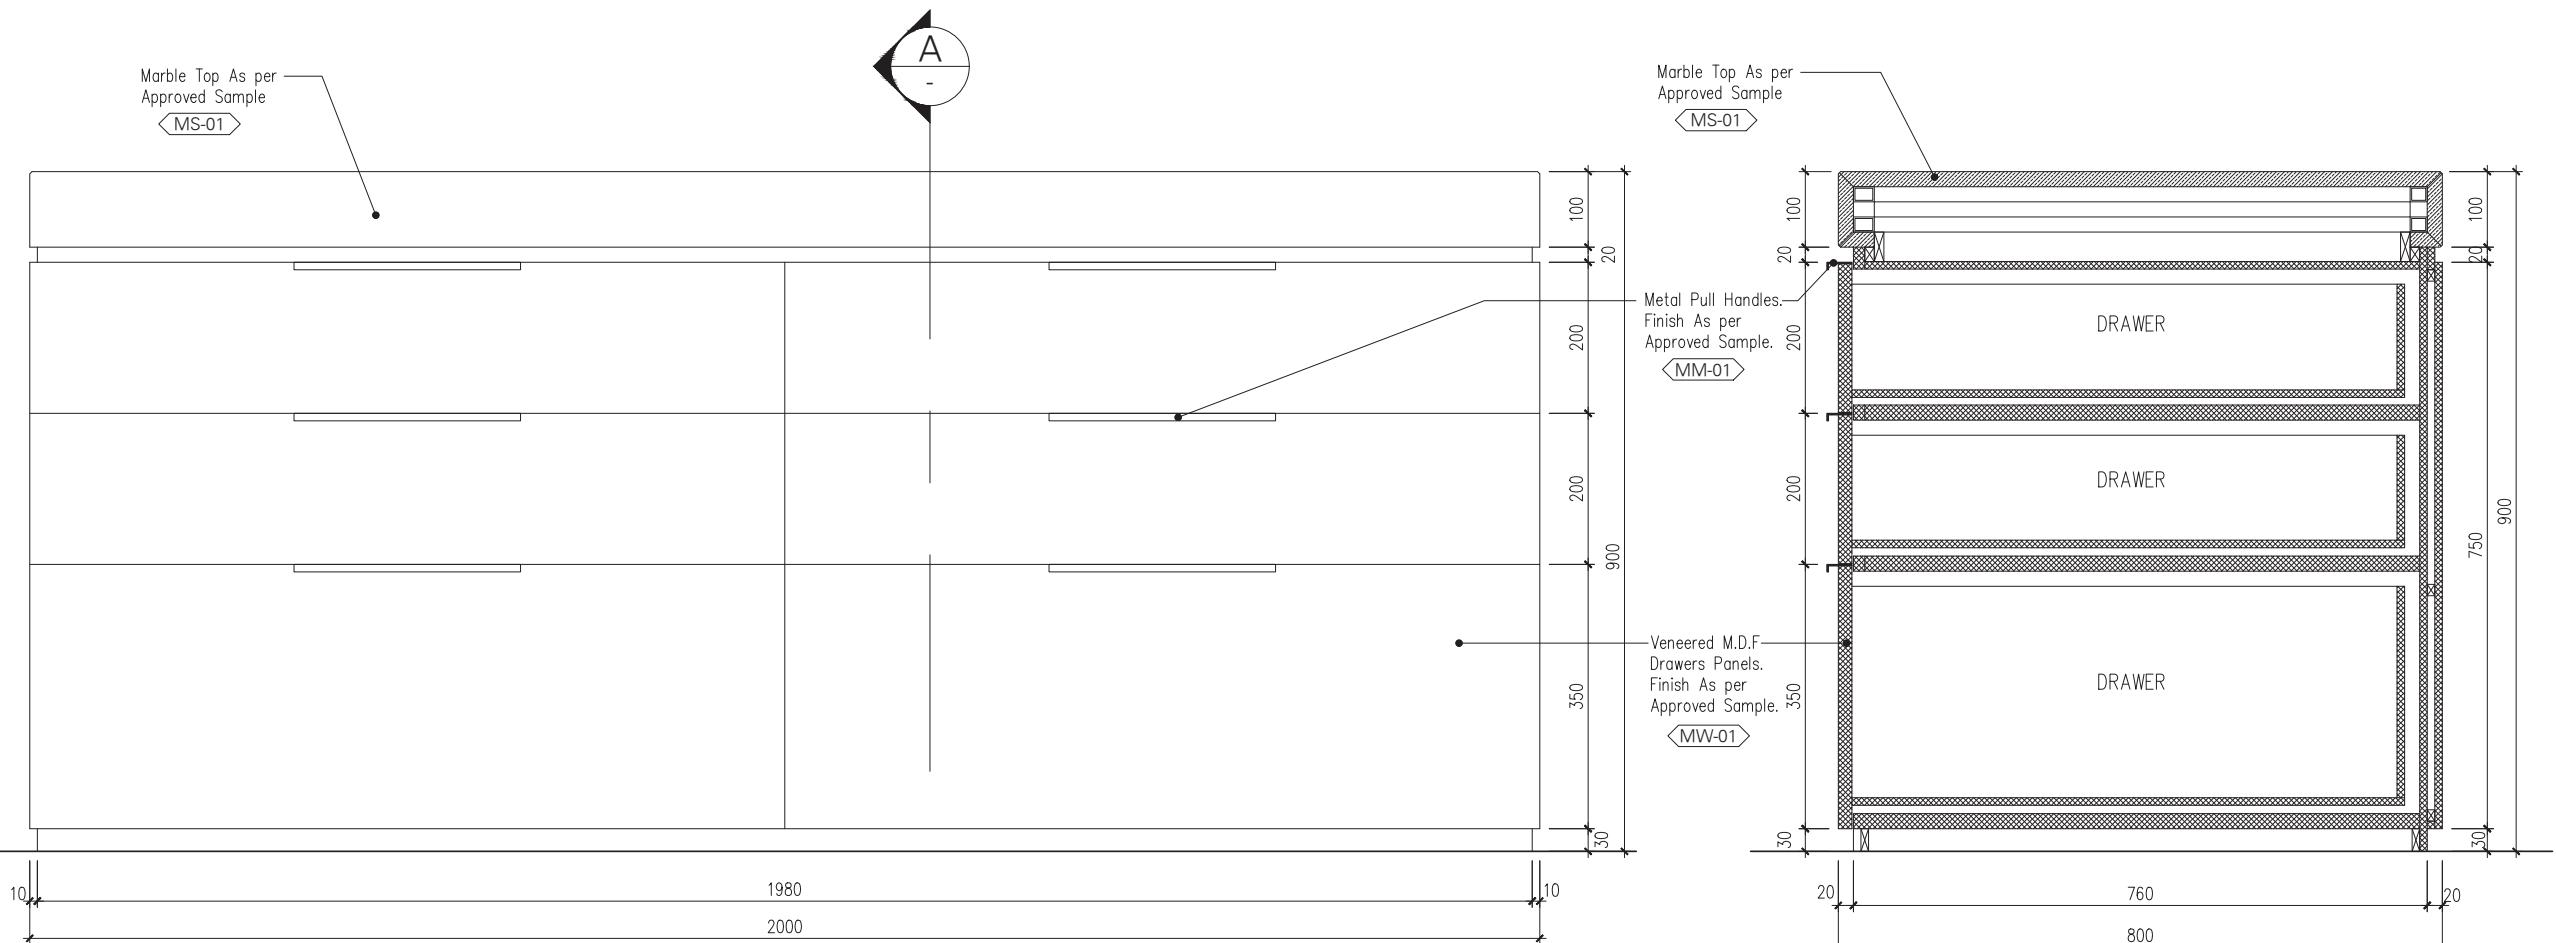

09 ELEVATION -9  
SCALE 1:5

A SECTION-A  
SCALE 1:5

**Client:** Zach-Aimee  
**Project Title:** Private Villa -Dubai Hills  
**Location:** Dubai, U.A.E.

**Plot Area:** 0000.00 Sqm  
0000.00 SqFt  
**Old Gate Level:** 0.00 = 0.000  
**NEW GATE LEVEL = 0.000**  
Proposed Gate Level is to be 000 mm above existing Asphalt Road Level

**Sheet Contents:**  
FIRST FLOOR  
MASTER BEDROOM  
DRAWERS ELEVATION & SECTION  
Designed by: Drawn By: Checked By: Issued By:  
ab mp ab ab  
Scale: Sheet Size: Stage: Rev No:  
1:5 A1 Conceptual Stage 0



**Drwg No.** ID-304-10

**General Notes:**


- All dimensions are in millimeters unless otherwise noted.
- Any inconsistency or discrepancy is to be brought to the attention of and resolved by the architect/designer.
- All dimensions are to be checked on site before commencing work.
- This drawing is to be coordinated with the Lead Consultant.

**Notes**

- \* ALL DRAWINGS ARE FOR DESIGN INTENT ONLY AND ARE NOT FOR CONSTRUCTION. THE APPOINTED CONTRACTOR SHOULD PROVIDE SHOP DRAWING FOR APPROVAL.
- \* CONTRACTOR TO DO A SITE SURVEY TO SPECIFY CORRECT QUANTITY & DIMENSIONS AS PER SITE MEASUREMENTS & DRAWINGS.
- \* CONTRACTOR TO CHECK THE MECHANISM & FUNCTIONALITY OF THE DESIGN INTEND.
- \* MATERIAL MUST BE PRESENTED TO PRIOR TO PURCHASE FOR TO APPROVE.

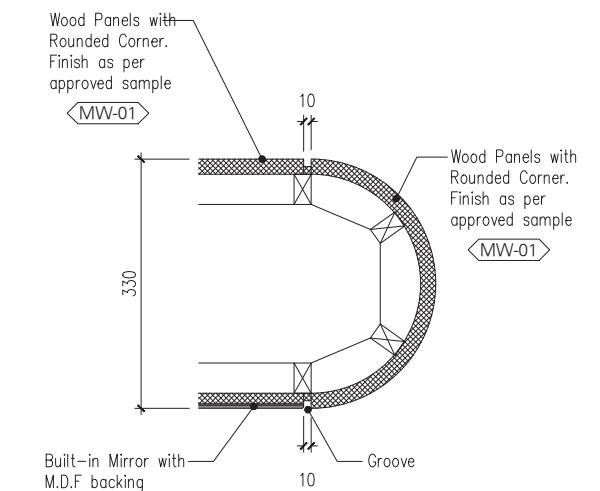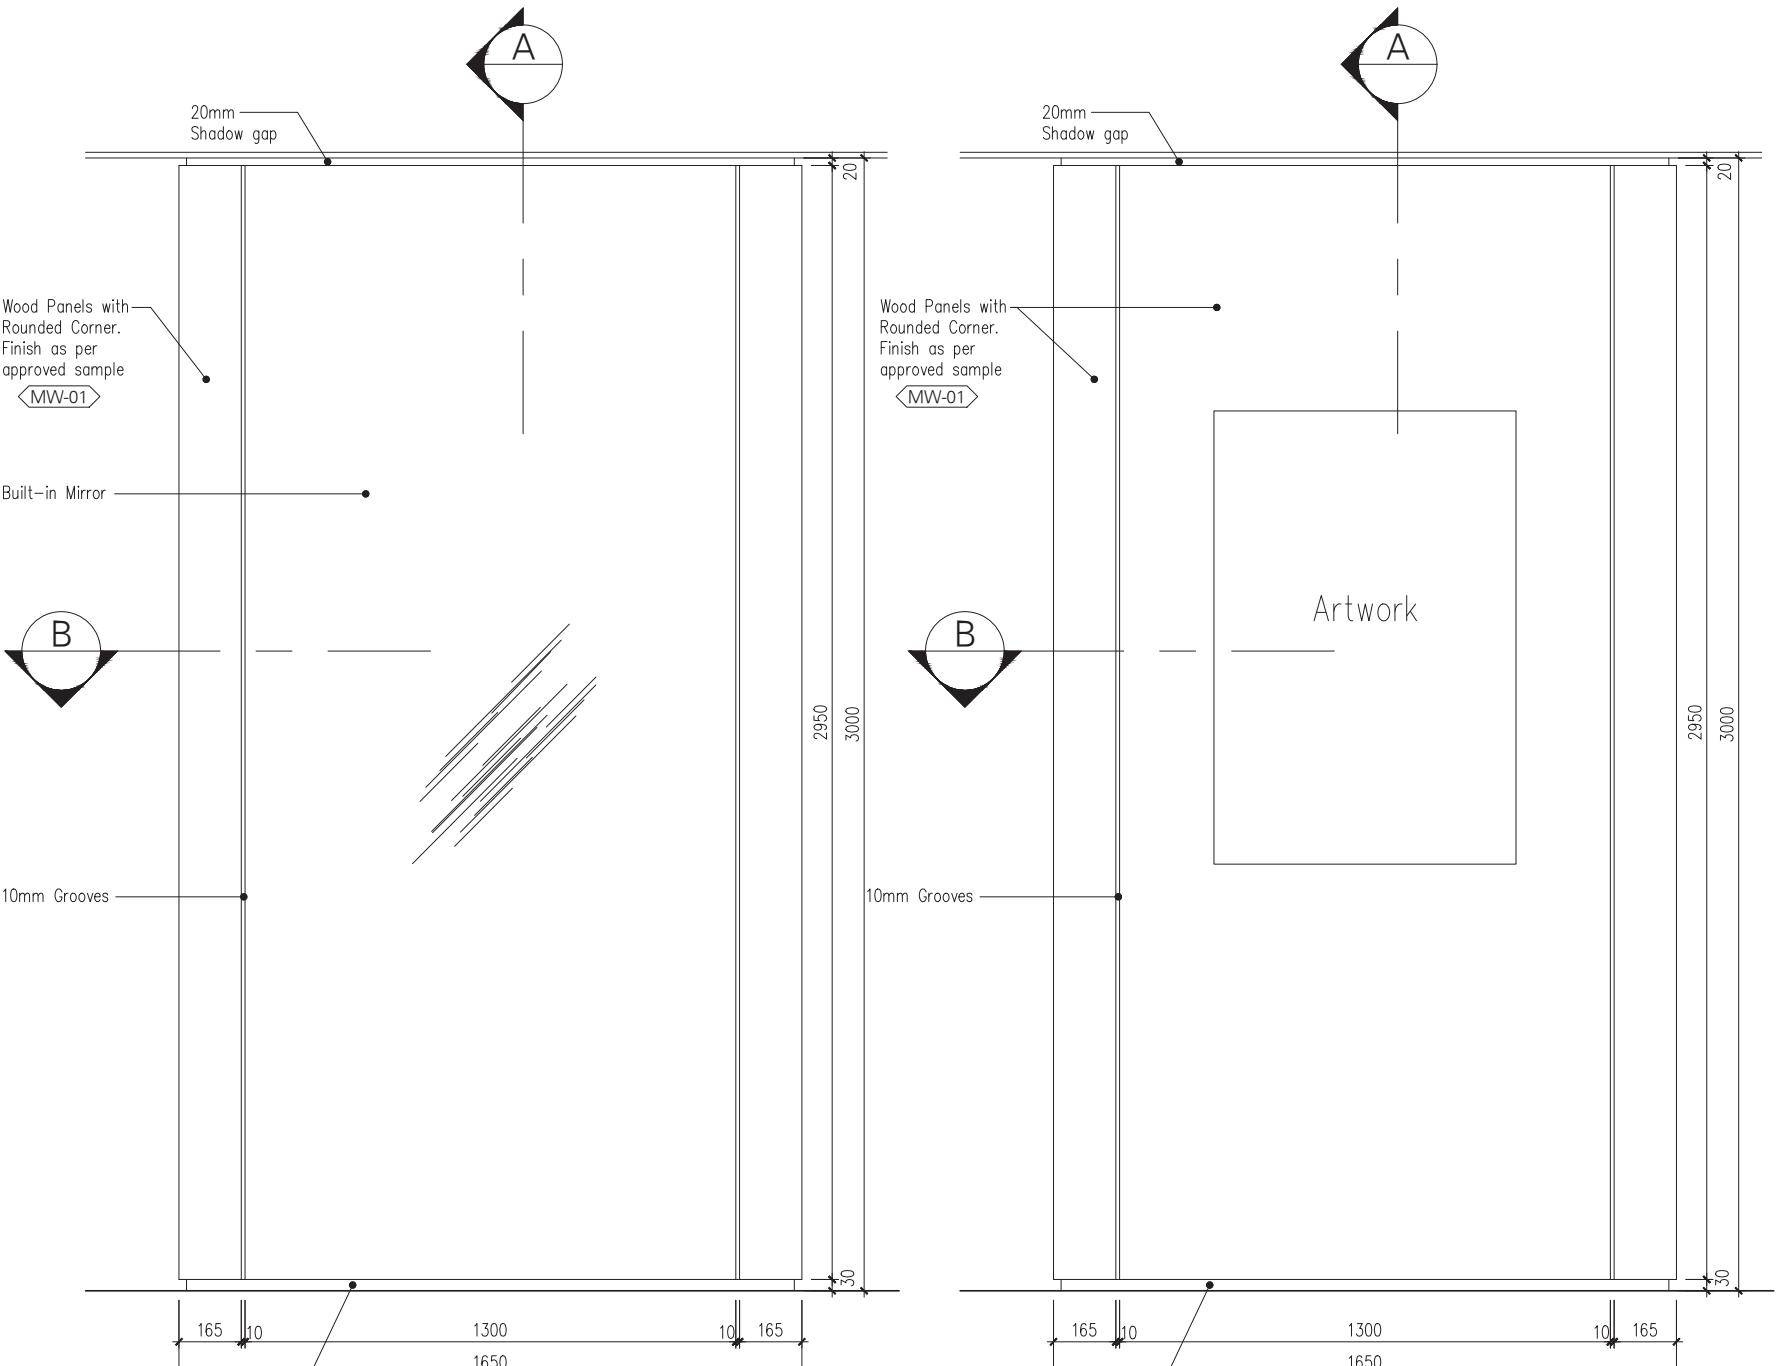

**B SECTION DETAIL**  
SCALE 1:5

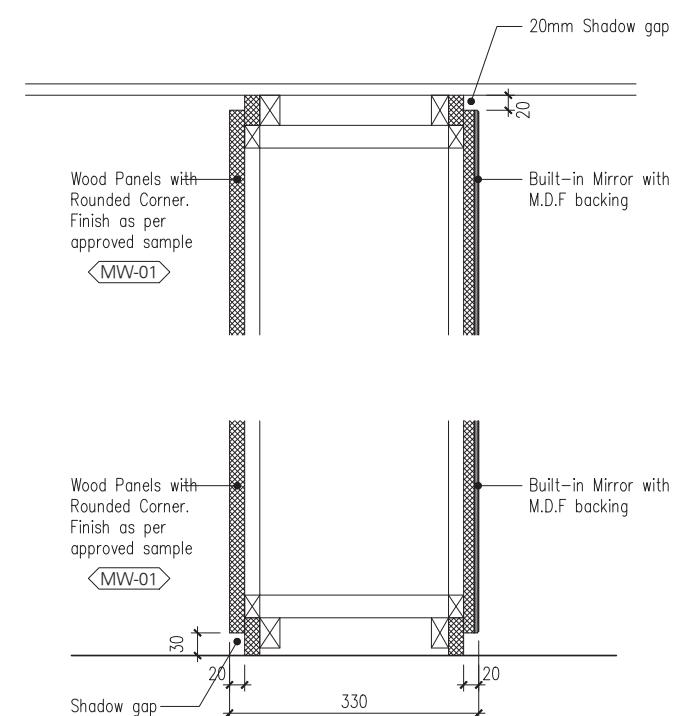

**A SECTION DETAIL**  
SCALE 1:5

0	2025.06.02	mp	Initial issue
Rev	Date	Drawn	Revisions

**Design Architect:**

**Client:**  
Zach-Aimee


**Project Title:**  
Private Villa -Dubai Hills

**Location:**  
Dubai, U.A.E.

**Plot Area:** 0000.00 Sqm  
0000.00 SqFt  
**Old Gate Level:** 0.00 = 0.000  
**NEW GATE LEVEL = 0.000**  
Proposed Gate Level is to be 000 mm above existing Asphalt Road Level

<b>Sheet Contents:</b>			
FIRST FLOOR MASTER BEDROOM ELEVATION 10 & 11 + DETAILS			
Designed by:	Drawn By:	Checked By:	Issued By:
ab	mp	ab	ab

**Drwg No.** ID-304-11

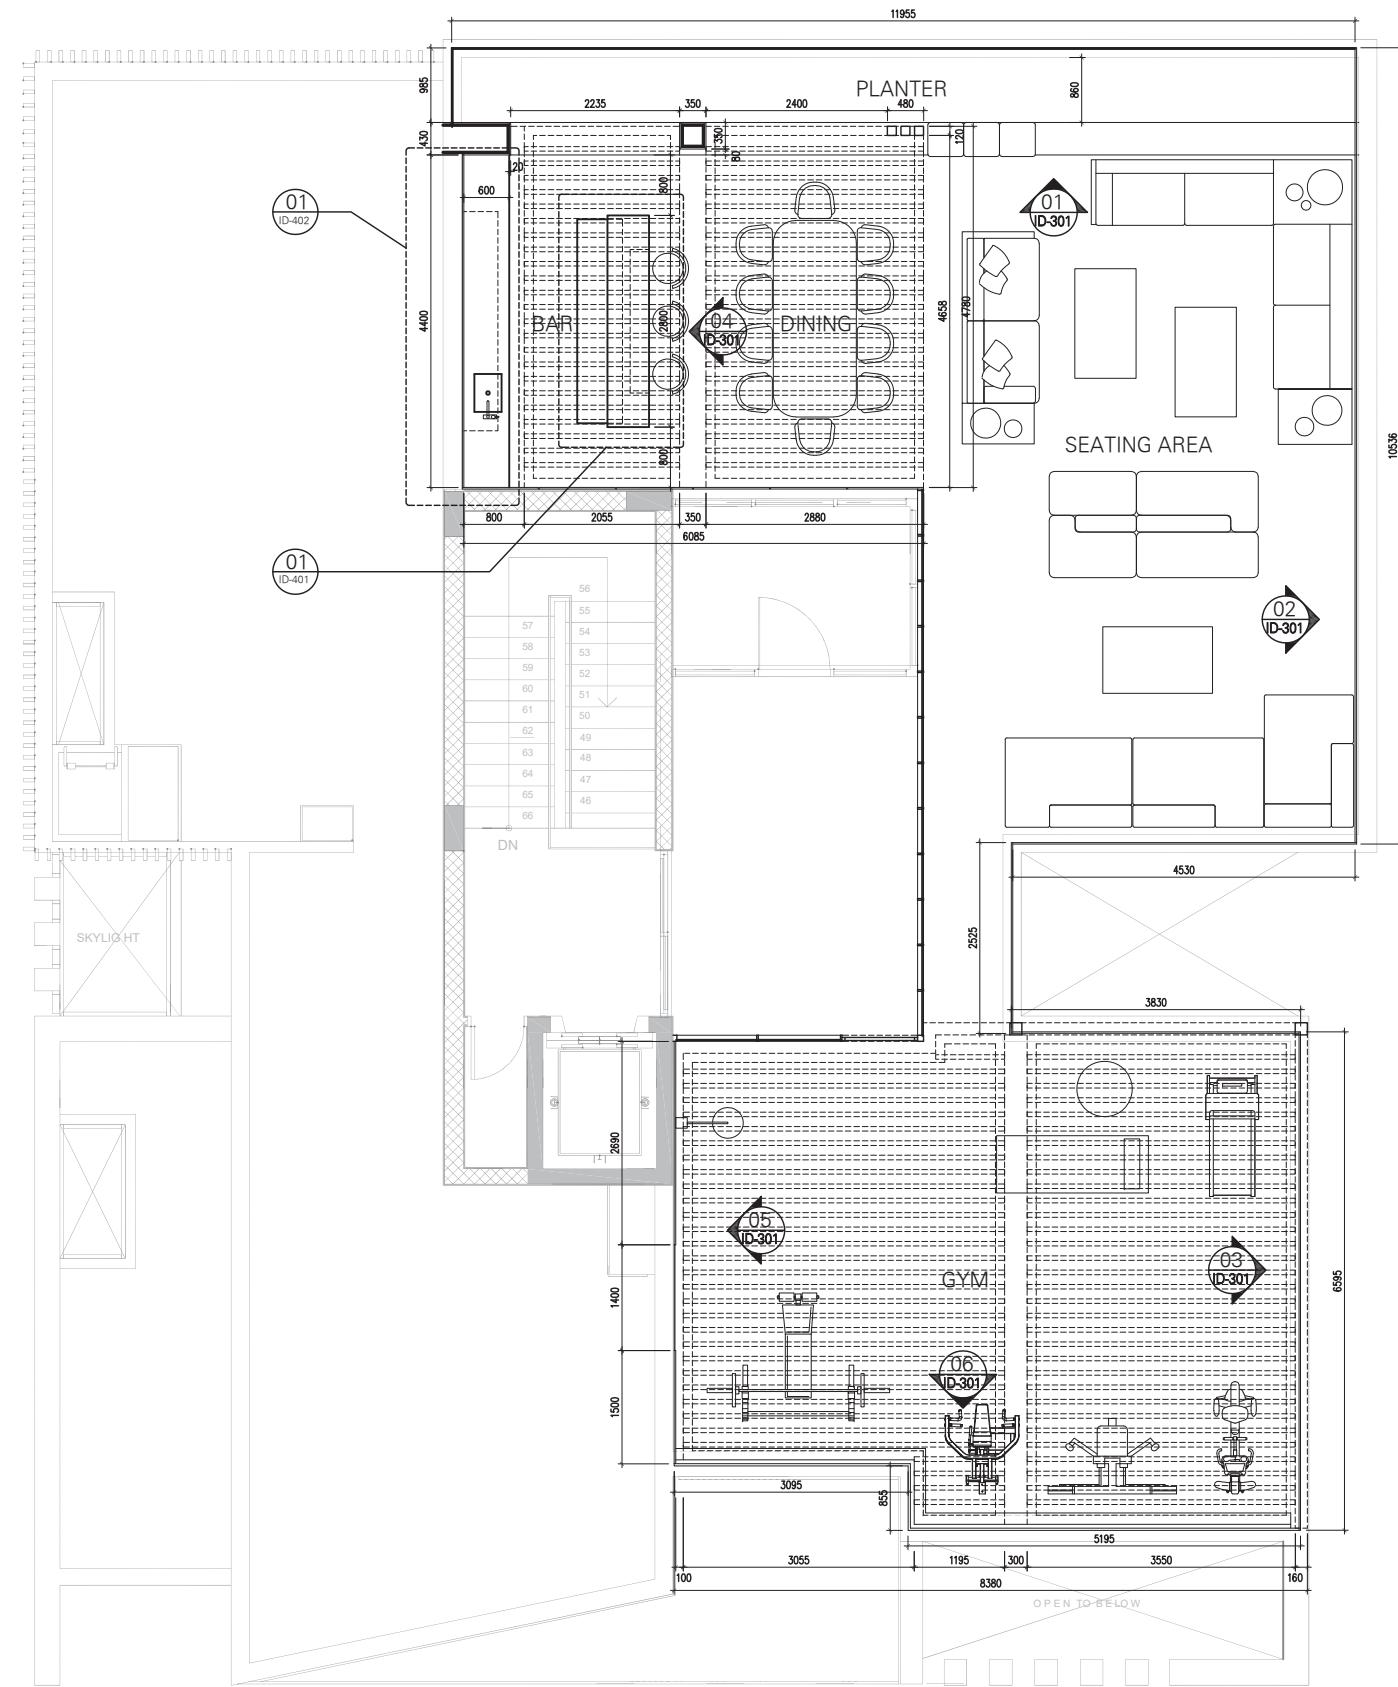

TERRACE - GENERAL LAYOUT

SCALE 1:50

**General Notes:**

- All dimensions are in millimeters unless otherwise noted.
- Any inconsistency or discrepancy is to be brought to the attention of and resolved by the architect/designer.
- All dimensions are to be checked on site before commencing work.
- This drawing is to be coordinated with the Lead Consultant.

**Notes**

- \* ALL DRAWINGS ARE FOR DESIGN INTENT ONLY AND ARE NOT FOR CONSTRUCTION. THE APPOINTED CONTRACTOR SHOULD PROVIDE SHOP DRAWING FOR APPROVAL.
- \* CONTRACTOR TO DO A SITE SURVEY TO SPECIFY CORRECT QUANTITY & DIMENSIONS AS PER SITE MEASUREMENTS & DRAWINGS.
- \* CONTRACTOR TO CHECK THE MECHANISM & FUNCTIONALITY OF THE DESIGN INTEND.
- \* MATERIAL MUST BE PRESENTED TO PRIOR TO PURCHASE FOR TO APPROVE.

0	2025.05.12	mp	Initial issue
Rev	Date	Drawn	Revisions

**Design Architect:**


**Client:**  
Zach-Aimee  
**Project Title:**  
Private Villa -Dubai Hills  
**Location:**  
Dubai, U.A.E.

**Plot Area:** 0000.00 Sqm  
0000.00 SqFt  
**Old Gate Level:** 0.00 = 0.000  
**NEW GATE LEVEL = 0.000**  
Proposed Gate Level is to be 000 mm above existing Asphalt Road Level

**Sheet Contents:**  
TERRACE FLOOR  
GENERAL LAYOUT

Designed by:	Drawn By:	Checked By:	Issued By:
ab	mp	ab	ab
Scale: 1:100	Sheet Size: A1	Stage: Conceptual Stage	Rev No: 0

**Drwg No.** ID-101

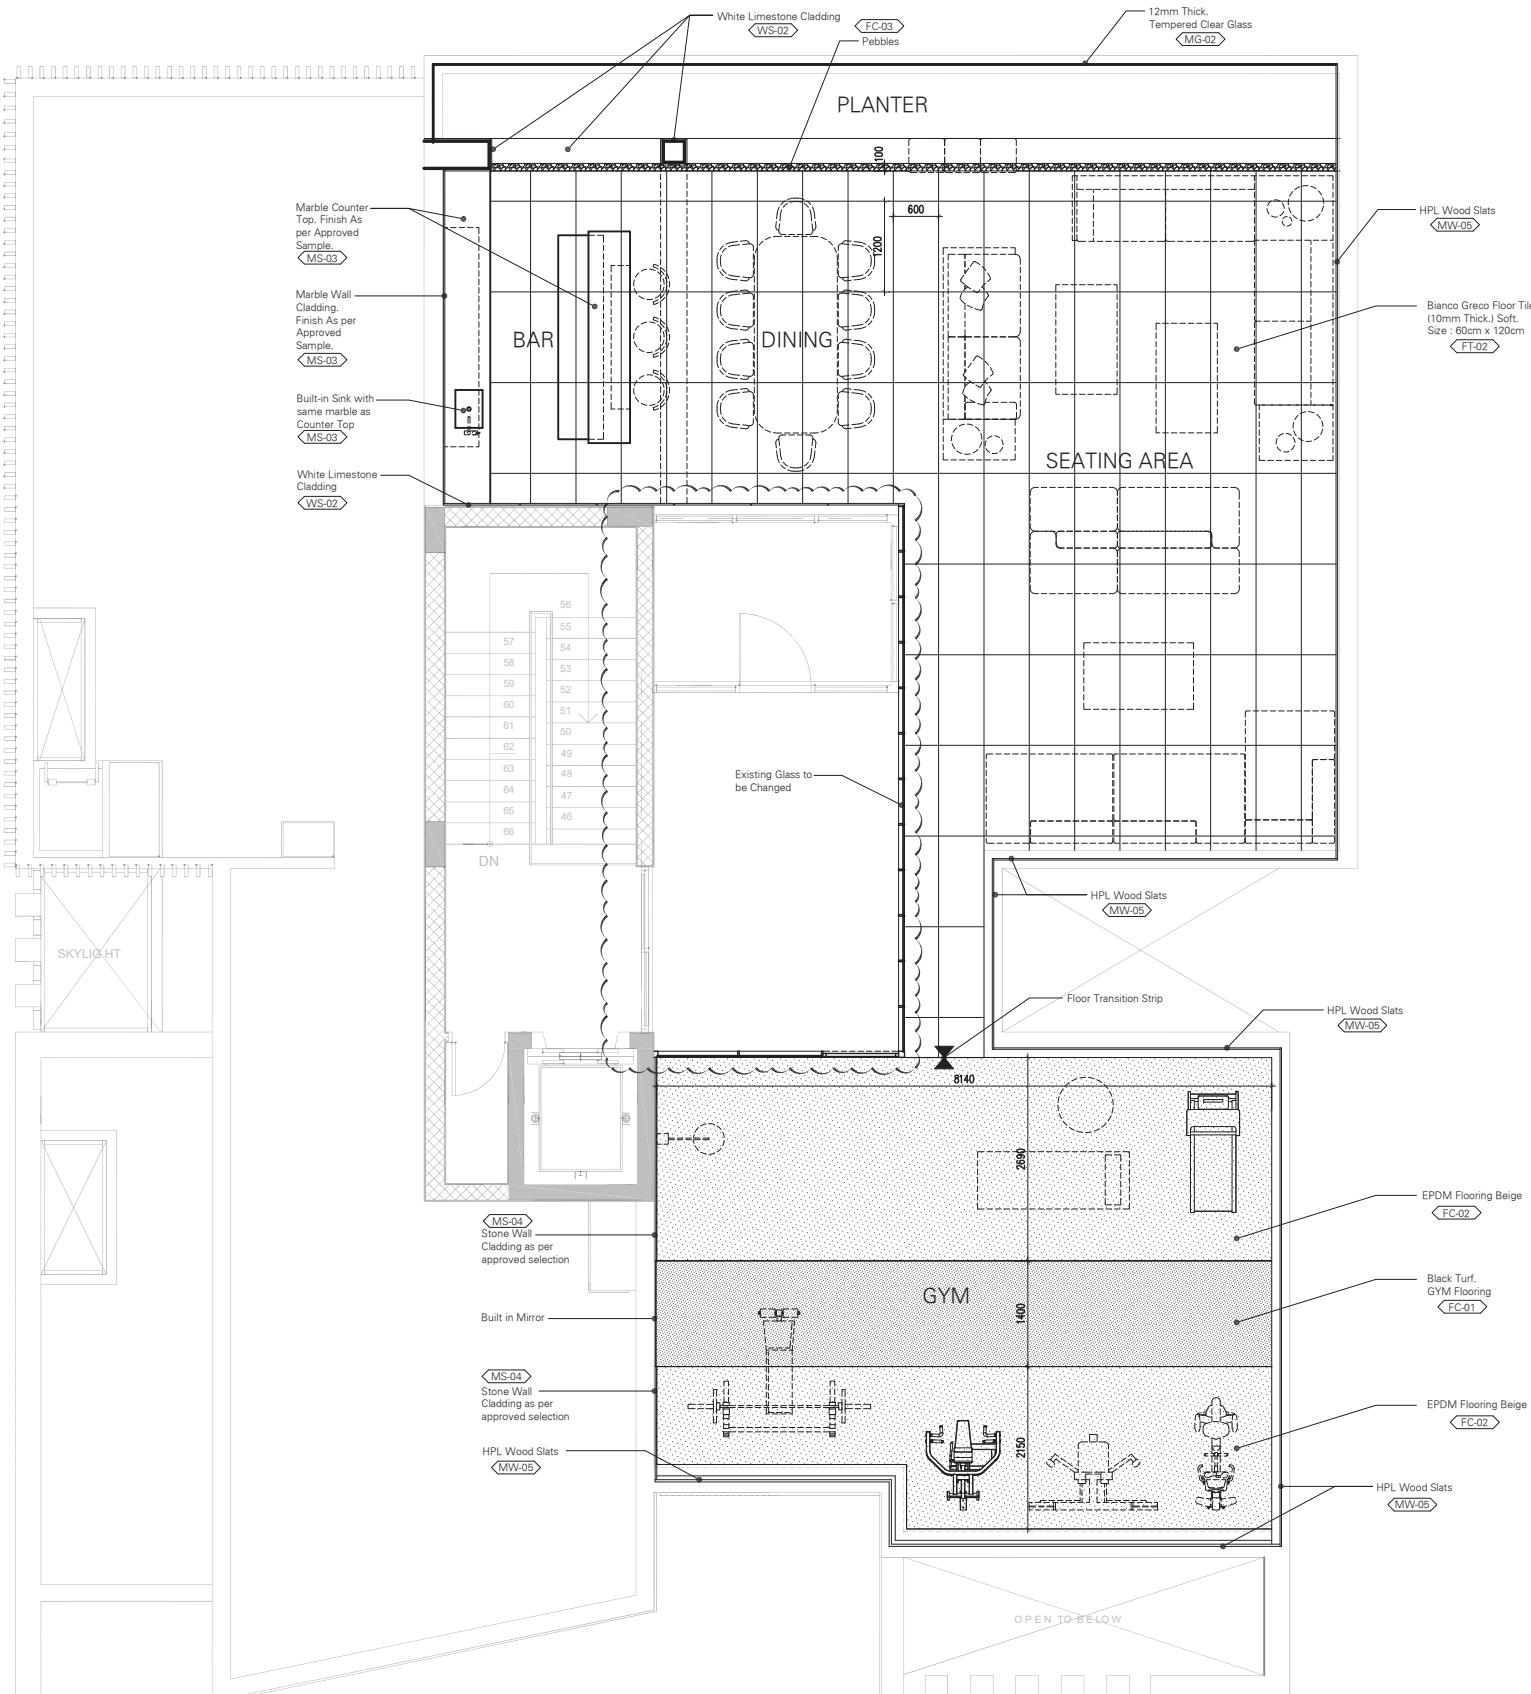

General Notes:

- All dimensions are in millimeters unless otherwise noted.
- Any inconsistency or discrepancy is to be brought to the attention of and resolved by the architect/designer.
- All dimensions are to be checked on site before commencing work.
- This drawing is to be coordinated with the Lead Consultant.

Notes

- \* ALL DRAWINGS ARE FOR DESIGN INTENT ONLY AND ARE NOT FOR CONSTRUCTION. THE APPOINTED CONTRACTOR SHOULD PROVIDE SHOP DRAWING FOR APPROVAL.
- \* CONTRACTOR TO DO A SITE SURVEY TO SPECIFY CORRECT QUANTITY & DIMENSIONS AS PER SITE MEASUREMENTS & DRAWINGS.
- \* CONTRACTOR TO CHECK THE MECHANISM & FUNCTIONALITY OF THE DESIGN INTEND.
- \* MATERIAL MUST BE PRESENTED TO PRIOR TO PURCHASE FOR TO APPROVE.

0	2025.05.12	mp	Initial issue
Rev	Date	Drawn	Revisions

Design Architect:

Client: Zach-Aimee  
Project Title: Private Villa -Dubai Hills

Location: Dubai, U.A.E.

Plot Area: 0000.00 Sqm  
0000.00 SqFt  
Old Gate Level: 0.00 = 0.000  
NEW GATE LEVEL = 0.000  
Proposed Gate Level is to be 000 mm above existing Asphalt Road Level

Sheet Contents: TERRACE FLOOR  
FLOORING & FINISHING LAYOUT

Designed by:	Drawn By:	Checked By:	Issued By:
ab	mp	ab	ab
Scale: 1:100	Sheet Size: A1	Stage: Conceptual Stage	Rev No: 0

Drwg No. ID-104

**General Notes:**

- All dimensions are in millimeters unless otherwise noted.
- Any inconsistency or discrepancy is to be brought to the attention of and resolved by the architect/designer.
- All dimensions are to be checked on site before commencing work.
- This drawing is to be coordinated with the Lead Consultant.


**Notes**

\* ALL DRAWINGS ARE FOR DESIGN INTENT ONLY AND ARE NOT FOR CONSTRUCTION. THE APPOINTED CONTRACTOR SHOULD PROVIDE SHOP DRAWING FOR APPROVAL.

\* CONTRACTOR TO DO A SITE SURVEY TO SPECIFY CORRECT QUANTITY & DIMENSIONS AS PER SITE MEASUREMENTS & DRAWINGS.

\* CONTRACTOR TO CHECK THE MECHANISM & FUNCTIONALITY OF THE DESIGN INTEND.

\* MATERIAL MUST BE PRESENTED TO PRIOR TO PURCHASE FOR TO APPROVE.

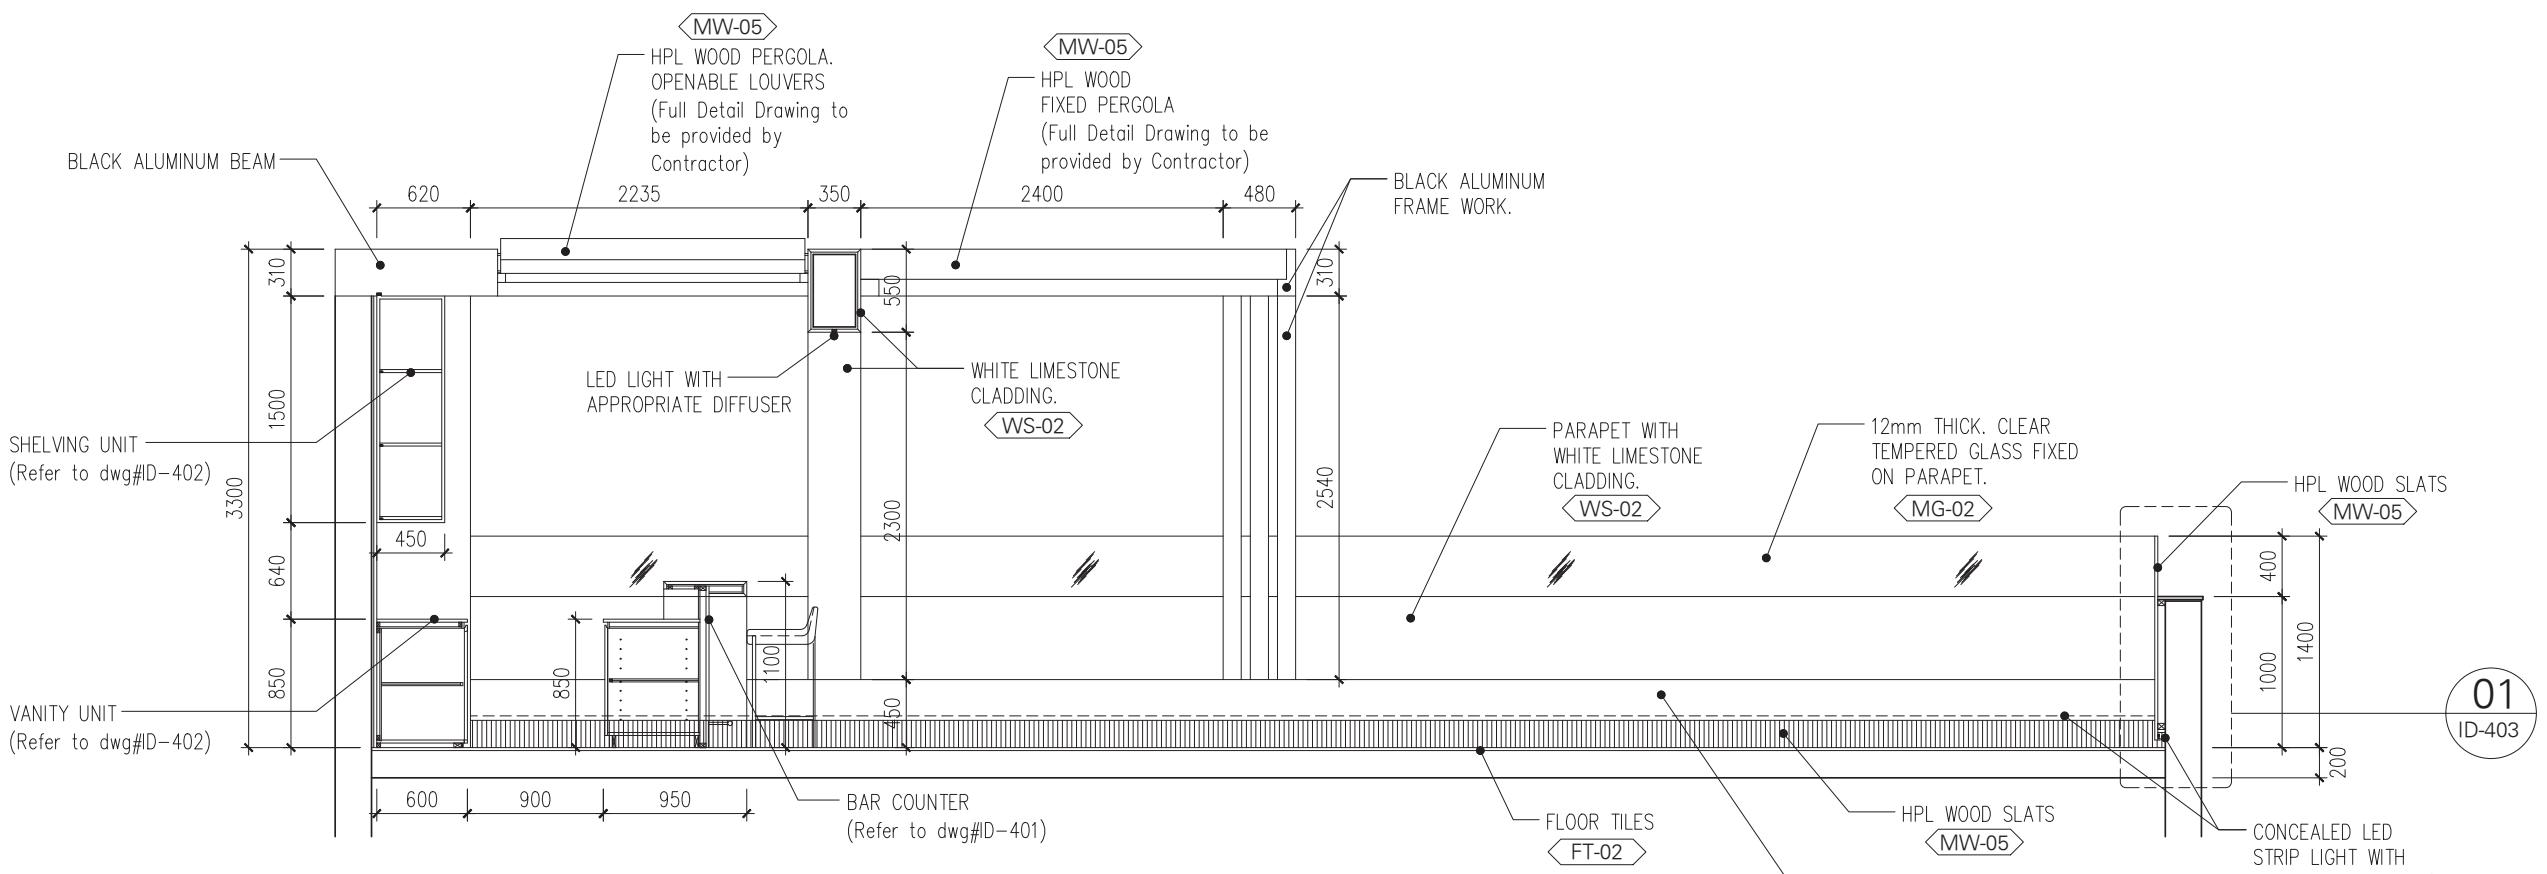

01 ELEVATION -1  
SCALE 1:25

0	2025.05.12	mp	Initial issue
Rev	Date	Drawn	Revisions

**Design Architect:**

**Client:** Zach-Aimee

**Project Title:** Private Villa -Dubai Hills

**Location:** Dubai, U.A.E.

**Plot Area:** 0000.00 Sqm  
0000.00 SqFt  
**Old Gate Level:** 0.00 = 0.000  
**NEW GATE LEVEL = 0.000**  
Proposed Gate Level is to be 000 mm above existing Asphalt Road Level

**Sheet Contents:** TERRACE ELEVATION - 1

Designed by:	Drawn By:	Checked By:	Issued By:
ab	mp	ab	ab
Scale: 1:100	Sheet Size: A1	Stage: Conceptual	Rev No: 0

**Drwg No.** ID-301-1



VISUAL - 1

**General Notes:**

- All dimensions are in millimeters unless otherwise noted.
- Any inconsistency or discrepancy is to be brought to the attention of and resolved by the architect/designer.
- All dimensions are to be checked on site before commencing work.
- This drawing is to be coordinated with the Lead Consultant.

**Notes**

- \* ALL DRAWINGS ARE FOR DESIGN INTENT ONLY AND ARE NOT FOR CONSTRUCTION. THE APPOINTED CONTRACTOR SHOULD PROVIDE SHOP DRAWING FOR APPROVAL.
- \* CONTRACTOR TO DO A SITE SURVEY TO SPECIFY CORRECT QUANTITY & DIMENSIONS AS PER SITE MEASUREMENTS & DRAWINGS.
- \* CONTRACTOR TO CHECK THE MECHANISM & FUNCTIONALITY OF THE DESIGN INTEND.
- \* MATERIAL MUST BE PRESENTED TO PRIOR TO PURCHASE FOR TO APPROVE.

0	2025.05.12	mp	Initial issue
Rev	Date	Drawn	Revisions

**Design Architect:**

**Client:**  
Zach-Aimee

**Project Title:**  
Private Villa -Dubai Hills

**Location:**  
Dubai, U.A.E.

**Plot Area:** 0000.00 Sqm  
0000.00 SqFt  
**Old Gate Level:** 0.00 = 0.000  
**NEW GATE LEVEL = 0.000**  
Proposed Gate Level is to be 000 mm above existing Asphalt Road Level

**Sheet Contents:**  
TERRACE  
VISUAL - 1

Designed by:	Drawn By:	Checked By:	Issued By:
ab	mp	ab	ab

Scale: 1:100 Sheet Size: A1 Stage: Conceptual Rev No: 0

**Drwg No.** ID-301-1-R



VISUAL - 2

**General Notes:**

- All dimensions are in millimeters unless otherwise noted.
- Any inconsistency or discrepancy is to be brought to the attention of and resolved by the architect/designer.
- All dimensions are to be checked on site before commencing work.
- This drawing is to be coordinated with the Lead Consultant.

**Notes**

\* ALL DRAWINGS ARE FOR DESIGN INTENT ONLY AND ARE NOT FOR CONSTRUCTION. THE APPOINTED CONTRACTOR SHOULD PROVIDE SHOP DRAWING FOR APPROVAL.

\* CONTRACTOR TO DO A SITE SURVEY TO SPECIFY CORRECT QUANTITY & DIMENSIONS AS PER SITE MEASUREMENTS & DRAWINGS.

\* CONTRACTOR TO CHECK THE MECHANISM & FUNCTIONALITY OF THE DESIGN INTEND.

\* MATERIAL MUST BE PRESENTED TO PRIOR TO PURCHASE FOR TO APPROVE.

0	2025.05.12	mp	Initial issue
Rev	Date	Drawn	Revisions

**Design Architect:**

**Client:** Zach-Aimee  
**Project Title:** Private Villa -Dubai Hills

**Location:** Dubai, U.A.E.

**Plot Area:** 0000.00 Sqm  
0000.00 SqFt  
**Old Gate Level:** 0.00 = 0.000  
**NEW GATE LEVEL = 0.000**  
Proposed Gate Level is to be 000 mm above existing Asphalt Road Level

**Sheet Contents:**  
TERRACE  
VISUAL - 2

Designed by:	Drawn By:	Checked By:	Issued By:
ab	mp	ab	ab

Scale: 1:100 Sheet Size: A1 Stage: Conceptual Rev No: 0


**Drwg No.** ID-301-1-R2

**General Notes:**

- All dimensions are in millimeters unless otherwise noted.
- Any inconsistency or discrepancy is to be brought to the attention of and resolved by the architect/designer.
- All dimensions are to be checked on site before commencing work.
- This drawing is to be coordinated with the Lead Consultant.

**Notes**

- \* ALL DRAWINGS ARE FOR DESIGN INTENT ONLY AND ARE NOT FOR CONSTRUCTION. THE APPOINTED CONTRACTOR SHOULD PROVIDE SHOP DRAWING FOR APPROVAL.
- \* CONTRACTOR TO DO A SITE SURVEY TO SPECIFY CORRECT QUANTITY & DIMENSIONS AS PER SITE MEASUREMENTS & DRAWINGS.
- \* CONTRACTOR TO CHECK THE MECHANISM & FUNCTIONALITY OF THE DESIGN INTEND.
- \* MATERIAL MUST BE PRESENTED TO PRIOR TO PURCHASE FOR TO APPROVE.

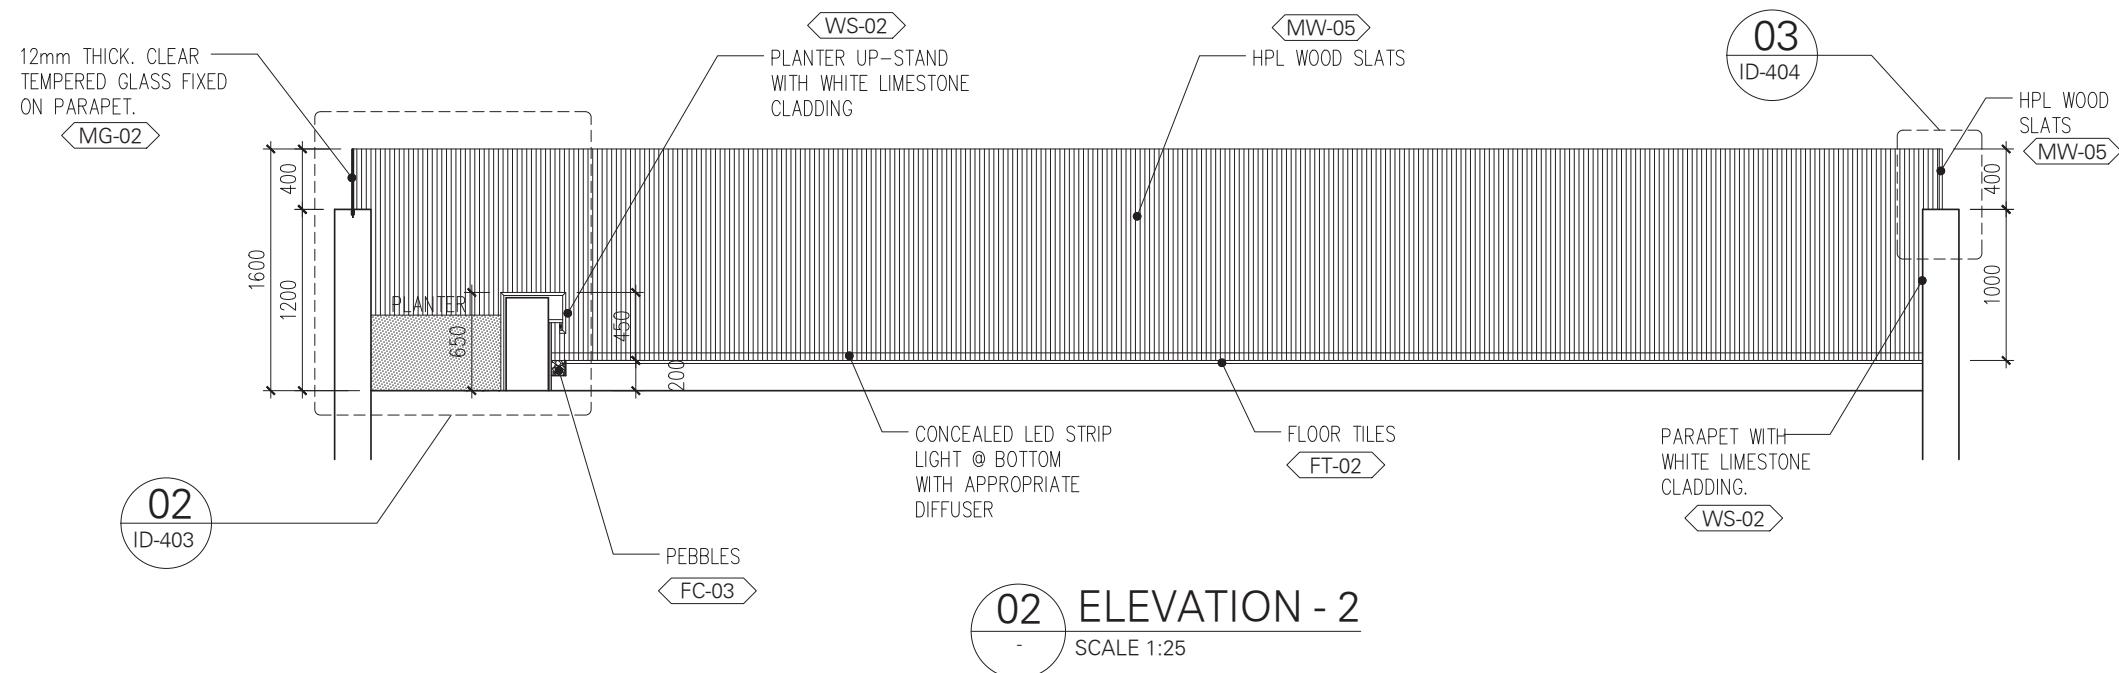

0	2025.05.12	mp	Initial issue
Rev	Date	Drawn	Revisions

**Design Architect:**

**Client:**  
Zach-Aimee

**Project Title:**  
Private Villa -Dubai Hills

**Location:**  
Dubai, U.A.E.

**Plot Area:** 0000.00 Sqm  
0000.00 SqFt  
**Old Gate Level:** 0.00 = 0.000  
**NEW GATE LEVEL = 0.000**  
Proposed Gate Level is to be 000 mm above existing Asphalt Road Level

**Sheet Contents:**  
TERRACE  
ELEVATION-2

Designed by:	Drawn By:	Checked By:	Issued By:
ab	mp	ab	ab
Scale: 1:100	Sheet Size: A1	Stage: Conceptual	Rev No: 0

**Drwg No.** ID-301-2



VISUAL - 3

**General Notes:**

- All dimensions are in millimeters unless otherwise noted.
- Any inconsistency or discrepancy is to be brought to the attention of and resolved by the architect/designer.
- All dimensions are to be checked on site before commencing work.
- This drawing is to be coordinated with the Lead Consultant.

**Notes**

- \* ALL DRAWINGS ARE FOR DESIGN INTENT ONLY AND ARE NOT FOR CONSTRUCTION. THE APPOINTED CONTRACTOR SHOULD PROVIDE SHOP DRAWING FOR APPROVAL.
- \* CONTRACTOR TO DO A SITE SURVEY TO SPECIFY CORRECT QUANTITY & DIMENSIONS AS PER SITE MEASUREMENTS & DRAWINGS.
- \* CONTRACTOR TO CHECK THE MECHANISM & FUNCTIONALITY OF THE DESIGN INTEND.
- \* MATERIAL MUST BE PRESENTED TO PRIOR TO PURCHASE FOR TO APPROVE.

0	2025.05.12	mp	Initial issue
Rev	Date	Drawn	Revisions

**Design Architect:**

**Client:** Zach-Aimee  
**Project Title:** Private Villa -Dubai Hills

**Location:** Dubai, U.A.E.

**Plot Area:** 0000.00 Sqm  
0000.00 SqFt  
**Old Gate Level:** 0.00 = 0.000  
**NEW GATE LEVEL = 0.000**  
Proposed Gate Level is to be 000 mm above existing Asphalt Road Level

**Sheet Contents:**  
TERRACE  
VISUAL - 3

Designed by:	Drawn By:	Checked By:	Issued By:
ab	mp	ab	ab

Scale: 1:100 Sheet Size: A1 Stage: Conceptual Rev No: 0

**Drwg No.** ID-301-2-R

**General Notes:**

- All dimensions are in millimeters unless otherwise noted.
- Any inconsistency or discrepancy is to be brought to the attention of and resolved by the architect/designer.
- All dimensions are to be checked on site before commencing work.
- This drawing is to be coordinated with the Lead Consultant.


**Notes**

\* ALL DRAWINGS ARE FOR DESIGN INTENT ONLY AND ARE NOT FOR CONSTRUCTION. THE APPOINTED CONTRACTOR SHOULD PROVIDE SHOP DRAWING FOR APPROVAL.

\* CONTRACTOR TO DO A SITE SURVEY TO SPECIFY CORRECT QUANTITY & DIMENSIONS AS PER SITE MEASUREMENTS & DRAWINGS.

\* CONTRACTOR TO CHECK THE MECHANISM & FUNCTIONALITY OF THE DESIGN INTEND.

\* MATERIAL MUST BE PRESENTED TO PRIOR TO PURCHASE FOR TO APPROVE.

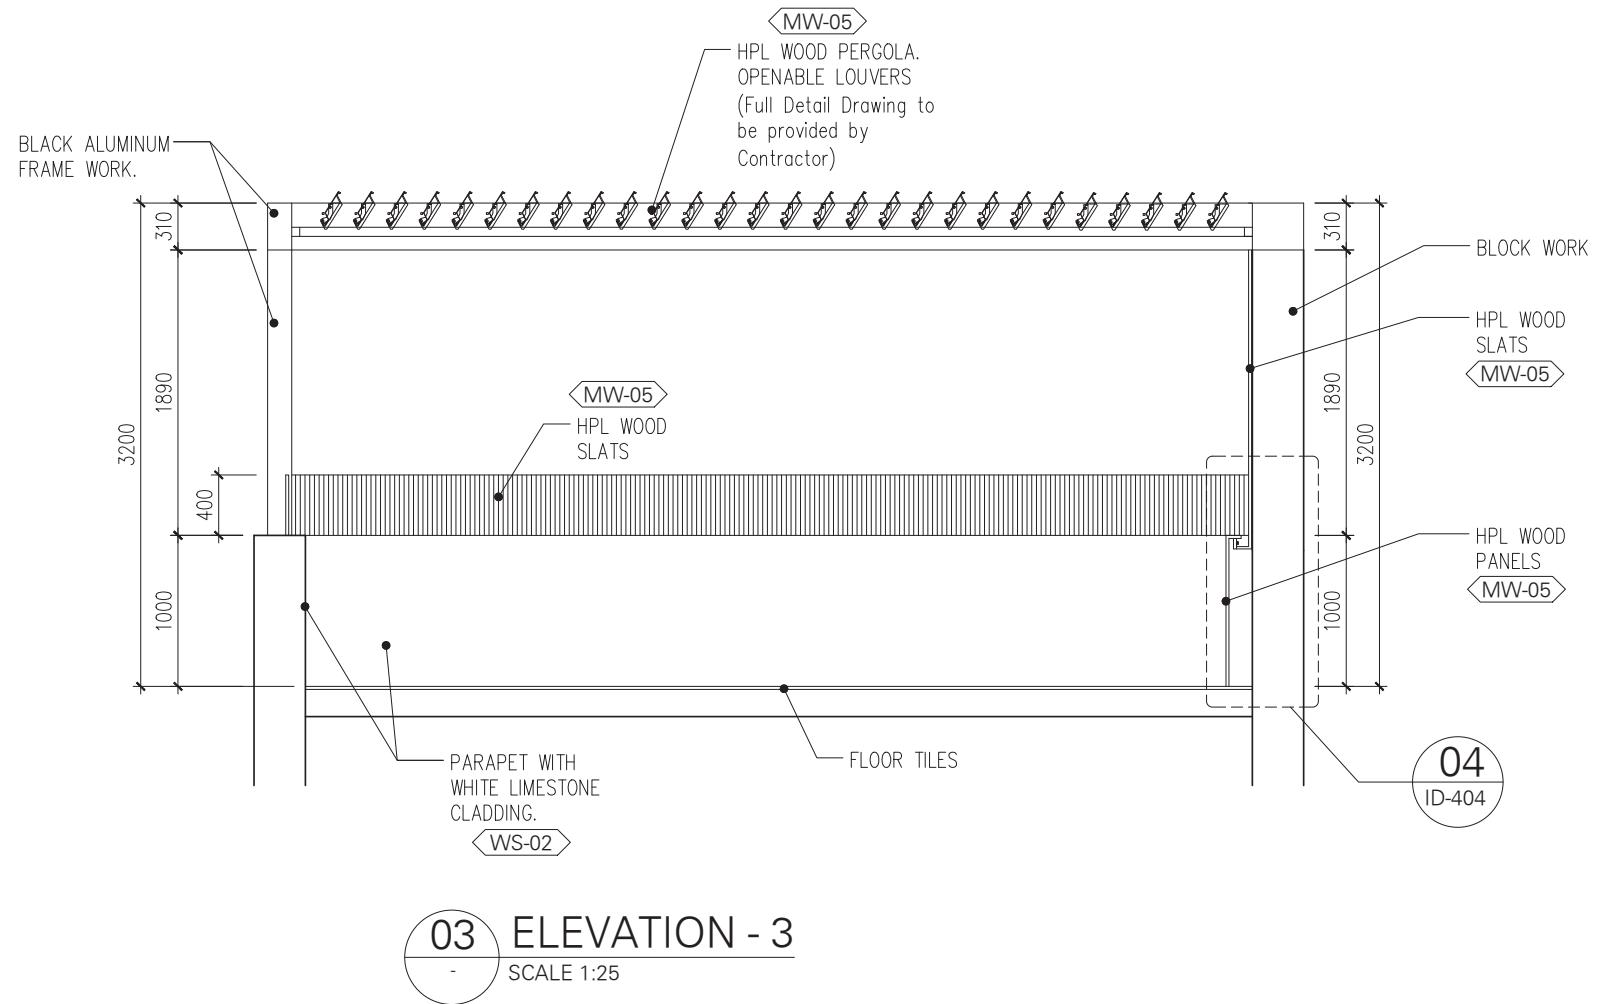

0	2025.05.12	mp	Initial issue
Rev	Date	Drawn	Revisions

**Design Architect:**

**Client:**  
Zach-Aimee

**Project Title:**  
Private Villa -Dubai Hills

**Location:**  
Dubai, U.A.E.

**Plot Area:** 0000.00 Sqm  
0000.00 SqFt  
**Old Gate Level:** 0.00 = 0.000  
**NEW GATE LEVEL = 0.000**  
Proposed Gate Level is to be 000 mm above existing Asphalt Road Level

**Sheet Contents:**  
TERRACE  
ELEVATION - 3

Designed by:	Drawn By:	Checked By:	Issued By:
ab	mp	ab	ab

**Scale:** 1:100      **Sheet Size:** A1      **Stage:** Conceptual Stage      **Rev No:** 0

**Drwg No.** ID-301-3

**General Notes:**

- All dimensions are in millimeters unless otherwise noted.
- Any inconsistency or discrepancy is to be brought to the attention of and resolved by the architect/designer.
- All dimensions are to be checked on site before commencing work.
- This drawing is to be coordinated with the Lead Consultant.


**Notes**

\* ALL DRAWINGS ARE FOR DESIGN INTENT ONLY AND ARE NOT FOR CONSTRUCTION. THE APPOINTED CONTRACTOR SHOULD PROVIDE SHOP DRAWING FOR APPROVAL.

\* CONTRACTOR TO DO A SITE SURVEY TO SPECIFY CORRECT QUANTITY & DIMENSIONS AS PER SITE MEASUREMENTS & DRAWINGS.

\* CONTRACTOR TO CHECK THE MECHANISM & FUNCTIONALITY OF THE DESIGN INTEND.

\* MATERIAL MUST BE PRESENTED TO PRIOR TO PURCHASE FOR TO APPROVE.

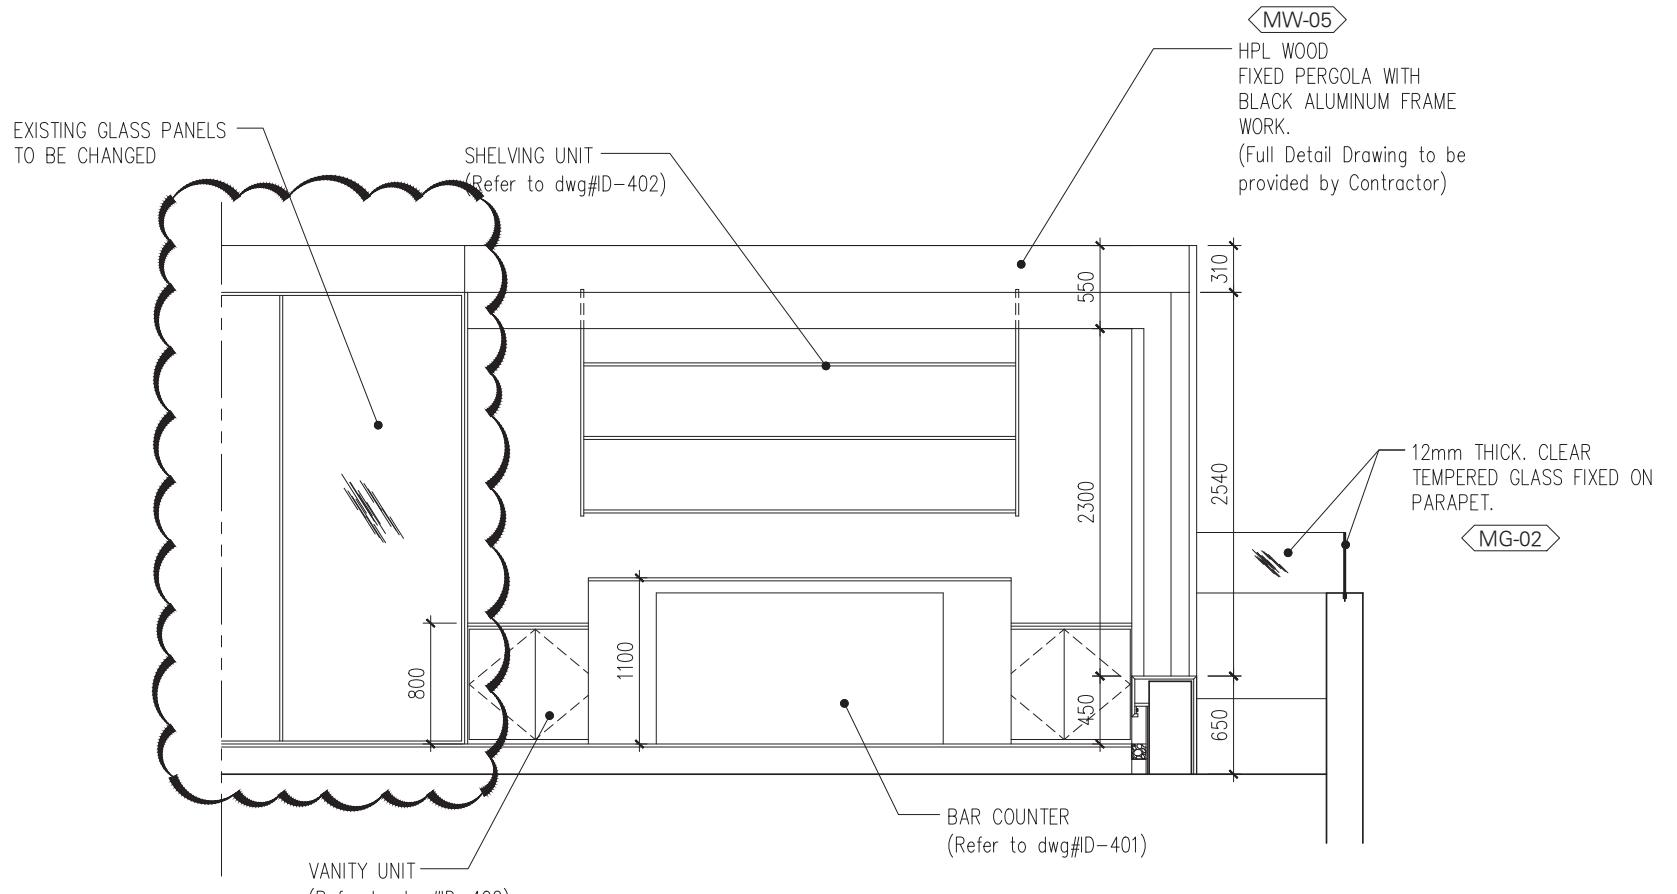

05 ELEVATION - 5  
SCALE 1:25

0	2025.05.12	mp	Initial issue
Rev	Date	Drawn	Revisions

**Design Architect:**

**Client:** Zach-Aimee

**Project Title:** Private Villa -Dubai Hills

**Location:** Dubai, U.A.E.

**Plot Area:** 0000.00 Sqm  
0000.00 SqFt  
**Old Gate Level:** 0.00 = 0.000  
**NEW GATE LEVEL = 0.000**  
Proposed Gate Level is to be 000 mm above existing Asphalt Road Level

**Sheet Contents:** TERRACE ELEVATION - 5

Designed by:	Drawn By:	Checked By:	Issued By:
ab	mp	ab	ab

Scale:	Sheet Size:	Stage:	Rev No:
1:100	A1	Conceptual Stage	0

**Drwg No.** ID-301-4

**General Notes:**

- All dimensions are in millimeters unless otherwise noted.
- Any inconsistency or discrepancy is to be brought to the attention of and resolved by the architect/designer.
- All dimensions are to be checked on site before commencing work.
- This drawing is to be coordinated with the Lead Consultant.

**Notes**

\* ALL DRAWINGS ARE FOR DESIGN INTENT ONLY AND ARE NOT FOR CONSTRUCTION. THE APPOINTED CONTRACTOR SHOULD PROVIDE SHOP DRAWING FOR APPROVAL.

\* CONTRACTOR TO DO A SITE SURVEY TO SPECIFY CORRECT QUANTITY & DIMENSIONS AS PER SITE MEASUREMENTS & DRAWINGS.

\* CONTRACTOR TO CHECK THE MECHANISM & FUNCTIONALITY OF THE DESIGN INTEND.

\* MATERIAL MUST BE PRESENTED TO PRIOR TO PURCHASE FOR TO APPROVE.

0	2025.05.12	mp	Initial issue
Rev	Date	Drawn	Revisions

**Design Architect:**

**Client:** Zach-Aimee  
**Project Title:** Private Villa -Dubai Hills

**Location:** Dubai, U.A.E.

**Plot Area:** 0000.00 Sqm  
0000.00 SqFt  
**Old Gate Level:** 0.00 = 0.000  
**NEW GATE LEVEL = 0.000**  
Proposed Gate Level is to be 000 mm above existing Asphalt Road Level

**Sheet Contents:**  
TERRACE  
VISUAL - 4

Designed by:	Drawn By:	Checked By:	Issued By:
ab	mp	ab	ab
Scale: 1:100	Sheet Size: A1	Stage: Conceptual Stage	Rev No: 0

**Drwg No.** ID-301-4-R




VISUAL - 4

**General Notes:**

- All dimensions are in millimeters unless otherwise noted.
- Any inconsistency or discrepancy is to be brought to the attention of and resolved by the architect/designer.
- All dimensions are to be checked on site before commencing work.
- This drawing is to be coordinated with the Lead Consultant.

**Notes**

- \* ALL DRAWINGS ARE FOR DESIGN INTENT ONLY AND ARE NOT FOR CONSTRUCTION. THE APPOINTED CONTRACTOR SHOULD PROVIDE SHOP DRAWING FOR APPROVAL.
- \* CONTRACTOR TO DO A SITE SURVEY TO SPECIFY CORRECT QUANTITY & DIMENSIONS AS PER SITE MEASUREMENTS & DRAWINGS.
- \* CONTRACTOR TO CHECK THE MECHANISM & FUNCTIONALITY OF THE DESIGN INTEND.
- \* MATERIAL MUST BE PRESENTED TO PRIOR TO PURCHASE FOR TO APPROVE.

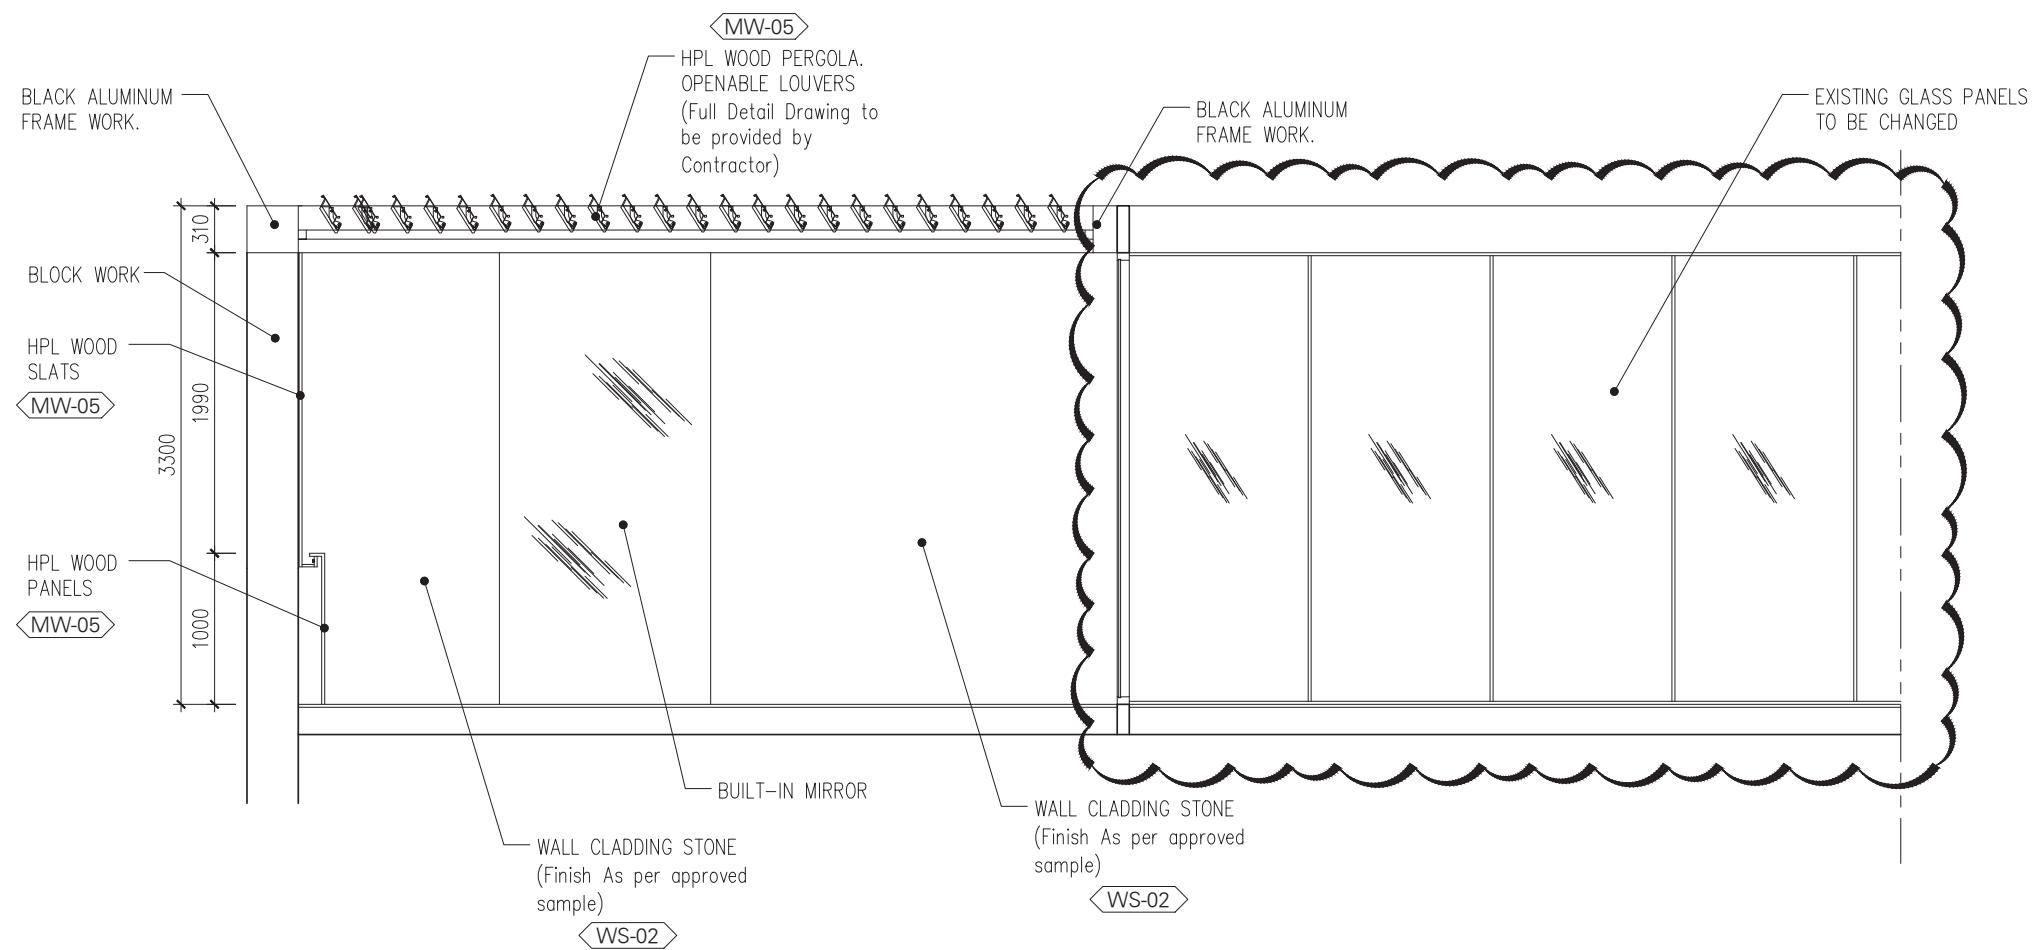

05 ELEVATION - 5  
SCALE 1:25

0	2025.05.12	mp	Initial issue
Rev	Date	Drawn	Revisions

**Design Architect:**

**Client:** Zach-Aimee

**Project Title:** Private Villa -Dubai Hills

**Location:** Dubai, U.A.E.

**Plot Area:** 0000.00 Sqm  
0000.00 SqFt  
**Old Gate Level:** 0.00 = 0.000  
**NEW GATE LEVEL = 0.000**

Proposed Gate Level is to be 000 mm above existing Asphalt Road Level

**Sheet Contents:** TERRACE  
ELEVATION - 5

Designed by:	Drawn By:	Checked By:	Issued By:
ab	mp	ab	ab
Scale: 1:100	Sheet Size: A1	Stage: Conceptual	Rev No: 0

**Drwg No.** ID-301-5



VISUAL - 5

**General Notes:**

- All dimensions are in millimeters unless otherwise noted.
- Any inconsistency or discrepancy is to be brought to the attention of and resolved by the architect/designer.
- All dimensions are to be checked on site before commencing work.
- This drawing is to be coordinated with the Lead Consultant.

**Notes**

\* ALL DRAWINGS ARE FOR DESIGN INTENT ONLY AND ARE NOT FOR CONSTRUCTION. THE APPOINTED CONTRACTOR SHOULD PROVIDE SHOP DRAWING FOR APPROVAL.

\* CONTRACTOR TO DO A SITE SURVEY TO SPECIFY CORRECT QUANTITY & DIMENSIONS AS PER SITE MEASUREMENTS & DRAWINGS.

\* CONTRACTOR TO CHECK THE MECHANISM & FUNCTIONALITY OF THE DESIGN INTEND.

\* MATERIAL MUST BE PRESENTED TO PRIOR TO PURCHASE FOR TO APPROVE.

0	2025.05.12	mp	Initial issue
Rev	Date	Drawn	Revisions

**Design Architect:**

**Client:** Zach-Aimee  
**Project Title:** Private Villa -Dubai Hills

**Location:** Dubai, U.A.E.

**Plot Area:** 0000.00 Sqm  
0000.00 SqFt  
**Old Gate Level:** 0.00 = 0.000  
**NEW GATE LEVEL = 0.000**  
Proposed Gate Level is to be 000 mm above existing Asphalt Road Level

**Sheet Contents:**  
TERRACE  
VISUAL - 5

Designed by:	Drawn By:	Checked By:	Issued By:
ab	mp	ab	ab
Scale: 1:100	Sheet Size: A1	Stage: Conceptual Stage	Rev No: 0

**Drwg No.** ID-301-5-R



VISUAL - 6

**General Notes:**

- All dimensions are in millimeters unless otherwise noted.
- Any inconsistency or discrepancy is to be brought to the attention of and resolved by the architect/designer.
- All dimensions are to be checked on site before commencing work.
- This drawing is to be coordinated with the Lead Consultant.

**Notes**

\* ALL DRAWINGS ARE FOR DESIGN INTENT ONLY AND ARE NOT FOR CONSTRUCTION. THE APPOINTED CONTRACTOR SHOULD PROVIDE SHOP DRAWING FOR APPROVAL.

\* CONTRACTOR TO DO A SITE SURVEY TO SPECIFY CORRECT QUANTITY & DIMENSIONS AS PER SITE MEASUREMENTS & DRAWINGS.

\* CONTRACTOR TO CHECK THE MECHANISM & FUNCTIONALITY OF THE DESIGN INTEND.

\* MATERIAL MUST BE PRESENTED TO PRIOR TO PURCHASE FOR TO APPROVE.

0	2025.05.12	mp	Initial issue
Rev	Date	Drawn	Revisions

**Design Architect:**

**Client:** Zach-Aimee  
**Project Title:** Private Villa -Dubai Hills


**Location:** Dubai, U.A.E.

**Plot Area:** 0000.00 Sqm  
0000.00 SqFt  
**Old Gate Level:** 0.00 = 0.000  
**NEW GATE LEVEL = 0.000**  
Proposed Gate Level is to be 000 mm above existing Asphalt Road Level

**Sheet Contents:**  
TERRACE  
VISUAL - 6

Designed by:	Drawn By:	Checked By:	Issued By:
ab	mp	ab	ab
Scale: 1:100	Sheet Size: A1	Stage: Conceptual Stage	Rev No: 0

**Drwg No.** ID-301-5-R2

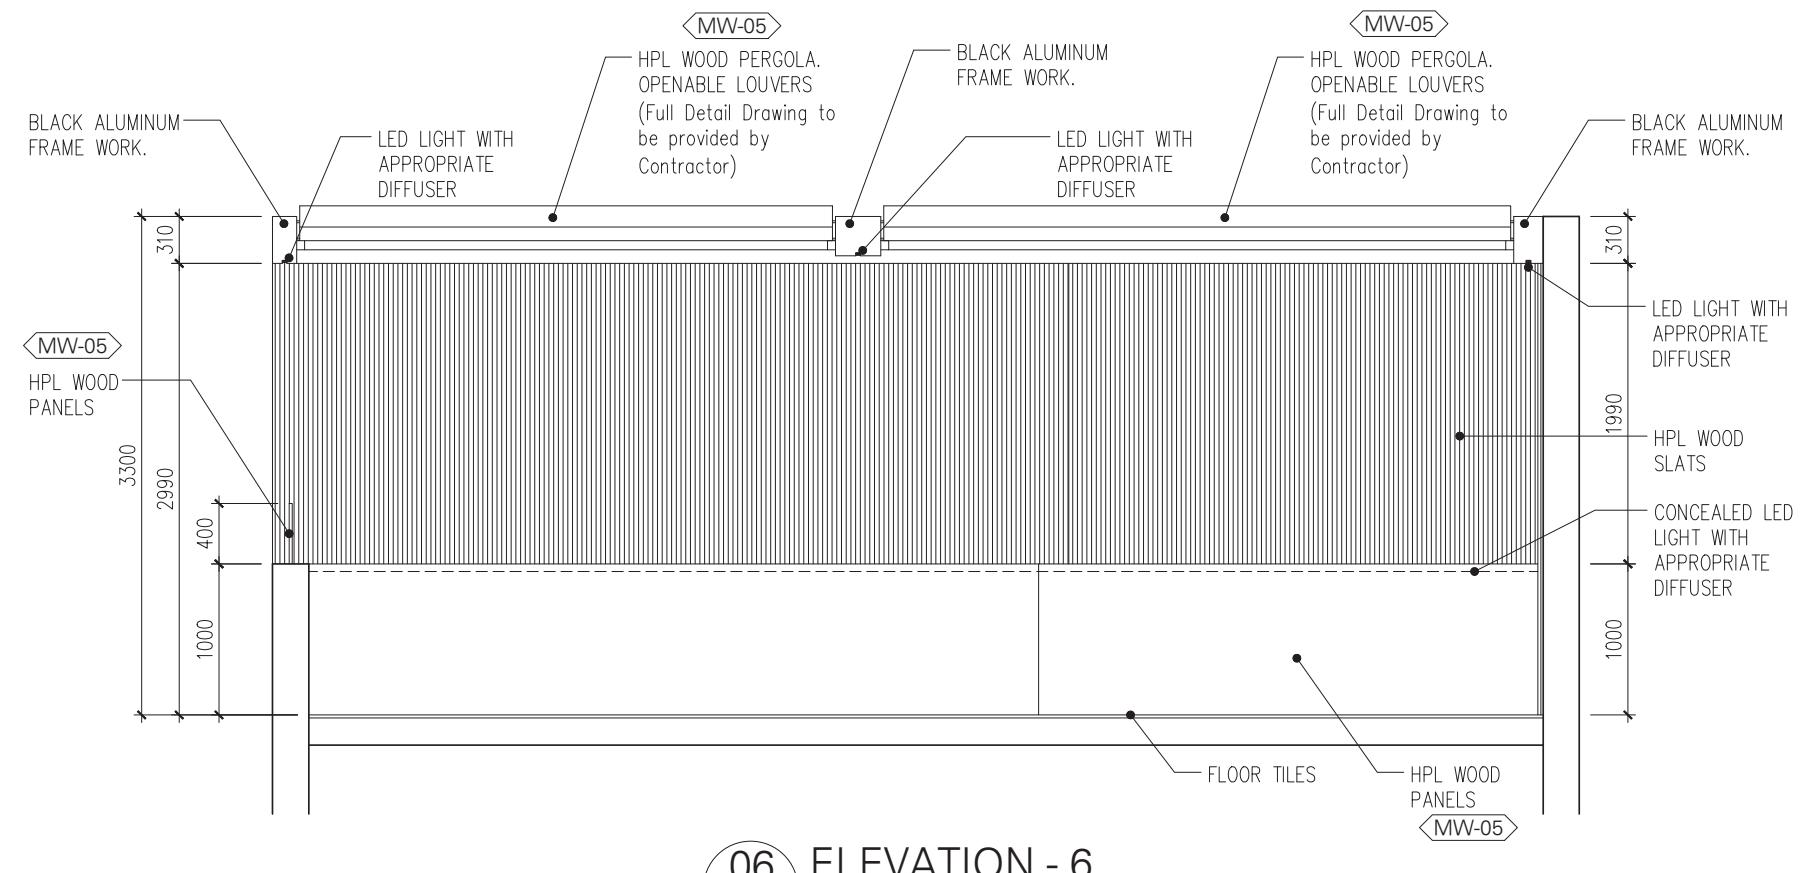

06 ELEVATION - 6  
SCALE 1:25

<b>General Notes:</b>											
1. All dimensions are in millimeters unless otherwise noted. 2. Any inconsistency or discrepancy is to be brought to the attention of and resolved by the architect/designer. 3. All dimensions are to be checked on site before commencing work. 4. This drawing is to be coordinated with the Lead Consultant.											
<b>Notes</b>											
<ul style="list-style-type: none"> <li>* ALL DRAWINGS ARE FOR DESIGN INTENT ONLY AND ARE NOT FOR CONSTRUCTION. THE APPOINTED CONTRACTOR SHOULD PROVIDE SHOP DRAWING FOR APPROVAL.</li> <li>* CONTRACTOR TO DO A SITE SURVEY TO SPECIFY CORRECT QUANTITY &amp; DIMENSIONS AS PER SITE MEASUREMENTS &amp; DRAWINGS.</li> <li>* CONTRACTOR TO CHECK THE MECHANISM &amp; FUNCTIONALITY OF THE DESIGN INTEND.</li> <li>* MATERIAL MUST BE PRESENTED TO PRIOR TO PURCHASE FOR TO APPROVE.</li> </ul>											
<table border="1" style="width: 100%; border-collapse: collapse;"> <tr><td>0</td><td>2025.05.12</td><td>mp</td><td>Initial issue</td></tr> <tr><td>Rev</td><td>Date</td><td>Drawn</td><td>Revisions</td></tr> </table>				0	2025.05.12	mp	Initial issue	Rev	Date	Drawn	Revisions
0	2025.05.12	mp	Initial issue								
Rev	Date	Drawn	Revisions								
<b>Design Architect:</b>											
<table border="1" style="width: 100%; border-collapse: collapse;"> <tr><td>Client:</td><td>Zach-Aimee</td></tr> <tr><td>Project Title:</td><td>Private Villa -Dubai Hills</td></tr> <tr><td>Location:</td><td>Dubai, U.A.E.</td></tr> </table>				Client:	Zach-Aimee	Project Title:	Private Villa -Dubai Hills	Location:	Dubai, U.A.E.		
Client:	Zach-Aimee										
Project Title:	Private Villa -Dubai Hills										
Location:	Dubai, U.A.E.										
<table border="1" style="width: 100%; border-collapse: collapse;"> <tr><td>Plot Area: 0000.00 Sqm 0000.00 SqFt</td></tr> <tr><td>Old Gate Level: 0.00 = 0.000 NEW GATE LEVEL = 0.000</td></tr> </table>				Plot Area: 0000.00 Sqm 0000.00 SqFt	Old Gate Level: 0.00 = 0.000 NEW GATE LEVEL = 0.000						
Plot Area: 0000.00 Sqm 0000.00 SqFt											
Old Gate Level: 0.00 = 0.000 NEW GATE LEVEL = 0.000											
Proposed Gate Level is to be 000 mm above existing Asphalt Road Level											
<b>Sheet Contents:</b>											
TERRACE ELEVATION - 6											
Designed by: ab	Drawn By: mp	Checked By: ab	Issued By: ab								
Scale: 1:100	Sheet Size: A1	Stage: Conceptual Stage	Rev No: 0								
<b>Drwg No.</b>		ID-301-6									



VISUAL - 7

**General Notes:**

- All dimensions are in millimeters unless otherwise noted.
- Any inconsistency or discrepancy is to be brought to the attention of and resolved by the architect/designer.
- All dimensions are to be checked on site before commencing work.
- This drawing is to be coordinated with the Lead Consultant.

**Notes**

\* ALL DRAWINGS ARE FOR DESIGN INTENT ONLY AND ARE NOT FOR CONSTRUCTION. THE APPOINTED CONTRACTOR SHOULD PROVIDE SHOP DRAWING FOR APPROVAL.

\* CONTRACTOR TO DO A SITE SURVEY TO SPECIFY CORRECT QUANTITY & DIMENSIONS AS PER SITE MEASUREMENTS & DRAWINGS.

\* CONTRACTOR TO CHECK THE MECHANISM & FUNCTIONALITY OF THE DESIGN INTEND.

\* MATERIAL MUST BE PRESENTED TO PRIOR TO PURCHASE FOR TO APPROVE.

0	2025.05.12	mp	Initial issue
Rev	Date	Drawn	Revisions

**Design Architect:**

**Client:** Zach-Aimee  
**Project Title:** Private Villa -Dubai Hills

**Location:** Dubai, U.A.E.

**Plot Area:** 0000.00 Sqm  
0000.00 SqFt  
**Old Gate Level:** 0.00 = 0.000  
**NEW GATE LEVEL = 0.000**  
Proposed Gate Level is to be 000 mm above existing Asphalt Road Level

**Sheet Contents:**  
TERRACE  
VISUAL - 7

Designed by:	Drawn By:	Checked By:	Issued By:
ab	mp	ab	ab
Scale: 1:100	Sheet Size: A1	Stage: Conceptual	Rev No: 0

**Drwg No.** ID-301-6-R

**General Notes:**

- All dimensions are in millimeters unless otherwise noted.
- Any inconsistency or discrepancy is to be brought to the attention of and resolved by the architect/designer.
- All dimensions are to be checked on site before commencing work.
- This drawing is to be coordinated with the Lead Consultant.

**Notes**

\* ALL DRAWINGS ARE FOR DESIGN INTENT ONLY AND ARE NOT FOR CONSTRUCTION. THE APPOINTED CONTRACTOR SHOULD PROVIDE SHOP DRAWING FOR APPROVAL.

\* CONTRACTOR TO DO A SITE SURVEY TO SPECIFY CORRECT QUANTITY & DIMENSIONS AS PER SITE MEASUREMENTS & DRAWINGS.

\* CONTRACTOR TO CHECK THE MECHANISM & FUNCTIONALITY OF THE DESIGN INTEND.

\* MATERIAL MUST BE PRESENTED TO PRIOR TO PURCHASE FOR TO APPROVE.



0	2025.05.12	mp	Initial issue
Rev	Date	Drawn	Revisions

**Design Architect:**

Zach-Aimee
Private Villa -Dubai Hills
Location:

Dubai, U.A.E.

Plot Area: 0000.00 Sqm  
0000.00 SqFt  
Old Gate Level: 0.00 = 0.000  
New Gate Level = 0.000  
Proposed Gate Level is to be 000 mm above existing Asphalt Road Level

**Sheet Contents:**  
TERRACE  
BAR COUNTER  
PLAN

Designed by:	Drawn By:	Checked By:	Issued By:
ab	mp	ab	ab
Scale: 1:100	Sheet Size: A1	Stage: Conceptual	Rev No: 0

**Drwg No.** ID-401-1

**General Notes:**

- All dimensions are in millimeters unless otherwise noted.
- Any inconsistency or discrepancy is to be brought to the attention of and resolved by the architect/designer.
- All dimensions are to be checked on site before commencing work.
- This drawing is to be coordinated with the Lead Consultant.


**Notes**

\* ALL DRAWINGS ARE FOR DESIGN INTENT ONLY AND ARE NOT FOR CONSTRUCTION. THE APPOINTED CONTRACTOR SHOULD PROVIDE SHOP DRAWING FOR APPROVAL.

\* CONTRACTOR TO DO A SITE SURVEY TO SPECIFY CORRECT QUANTITY & DIMENSIONS AS PER SITE MEASUREMENTS & DRAWINGS.

\* CONTRACTOR TO CHECK THE MECHANISM & FUNCTIONALITY OF THE DESIGN INTEND.

\* MATERIAL MUST BE PRESENTED TO PRIOR TO PURCHASE FOR TO APPROVE.

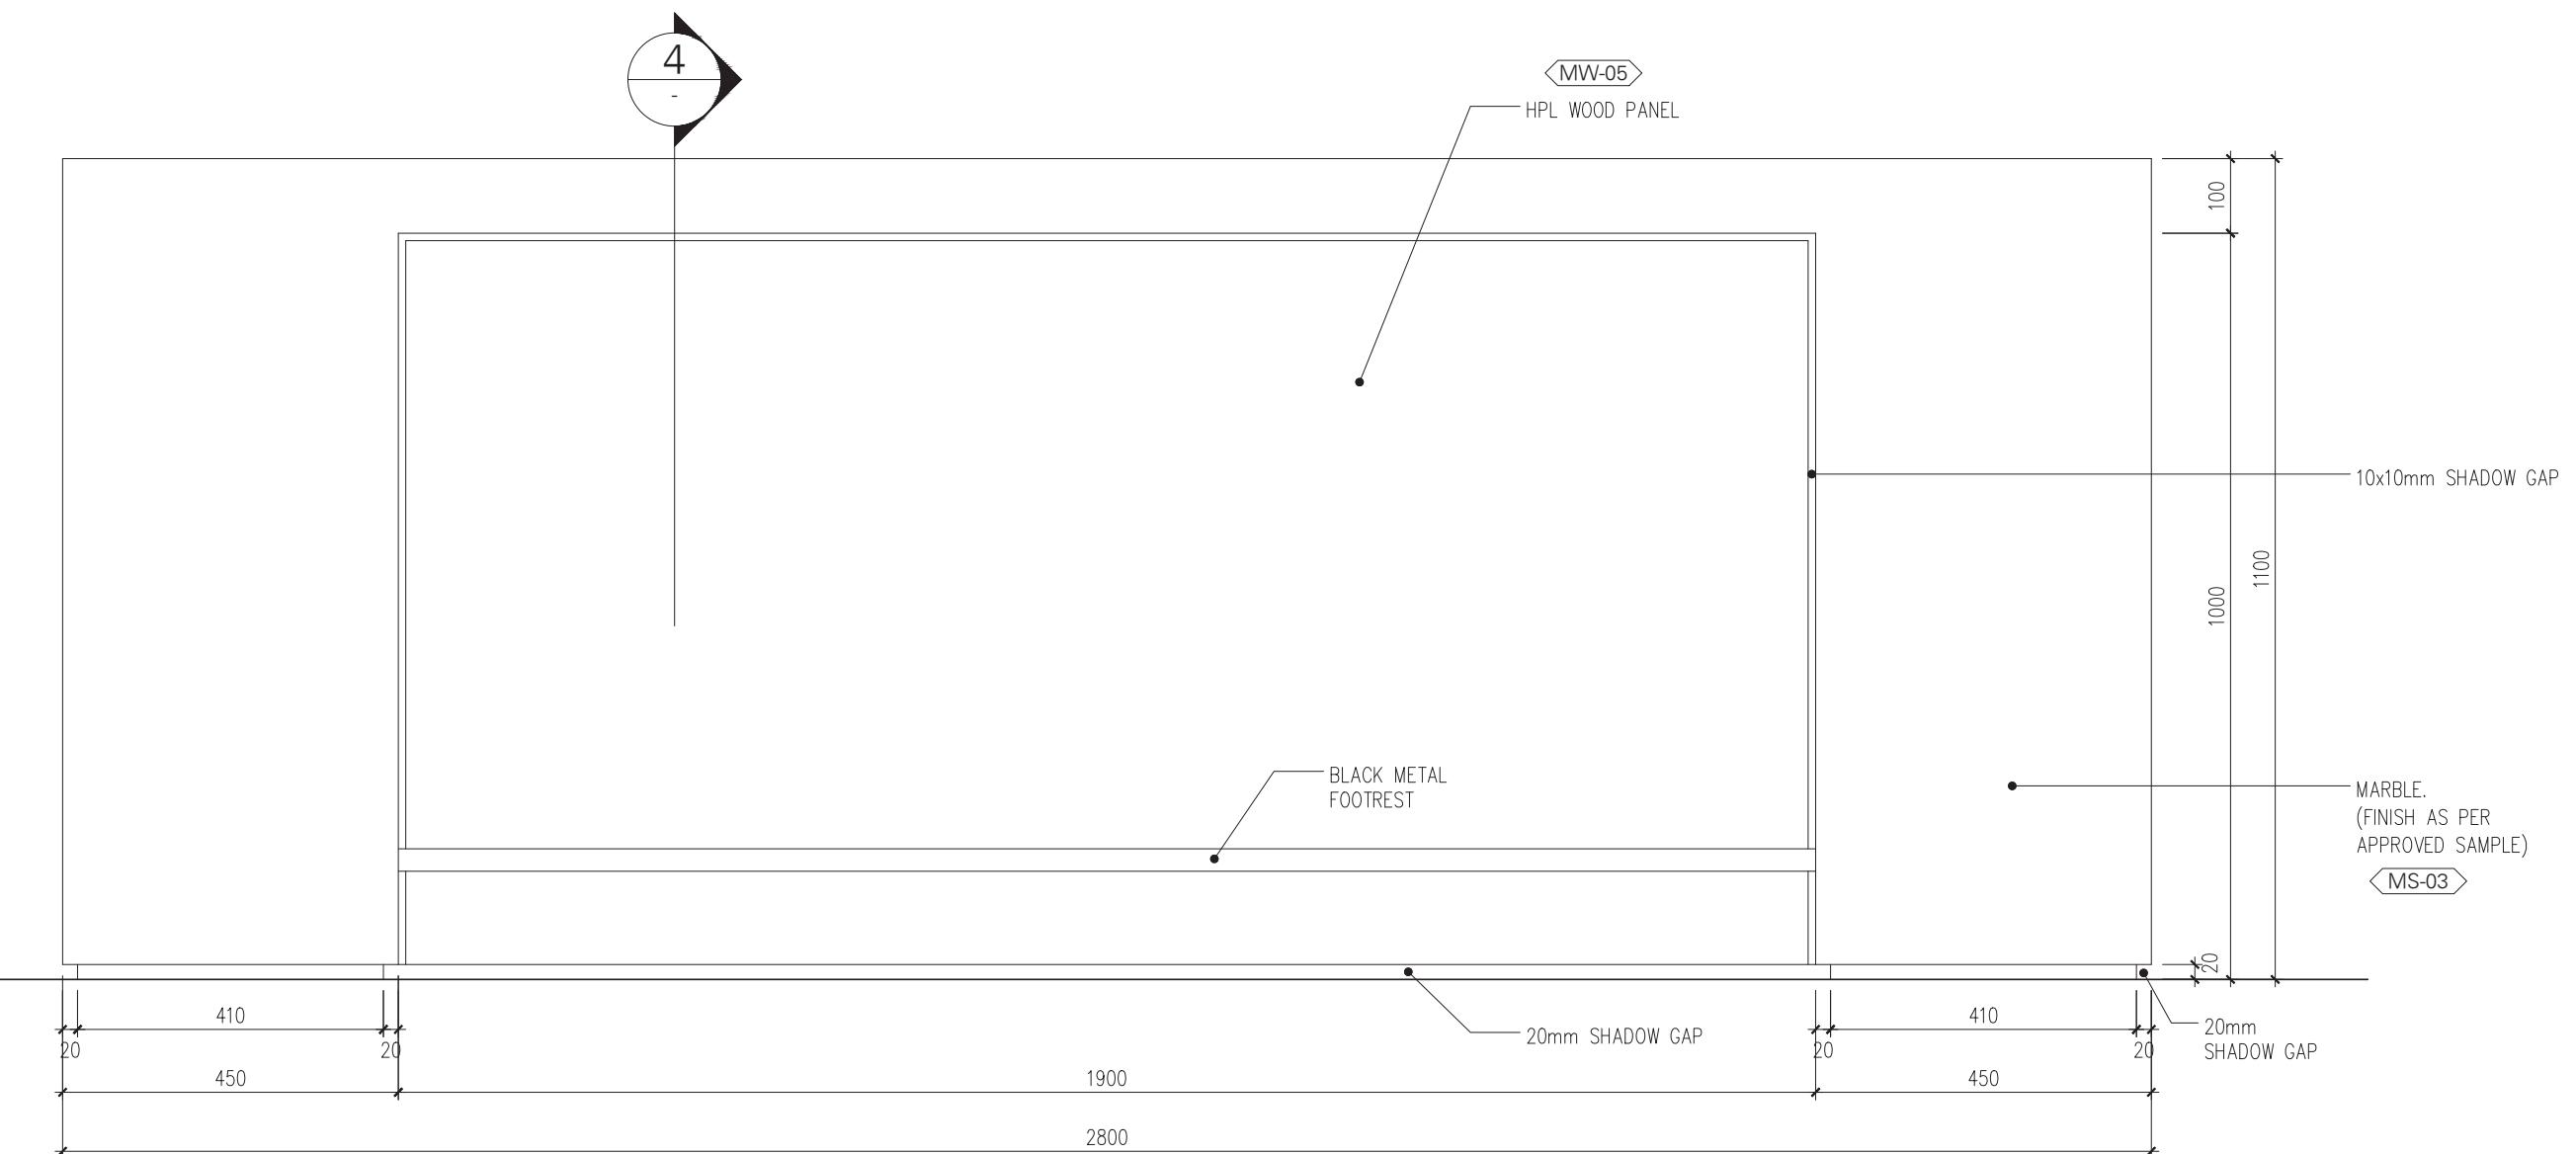

**2 BAR COUNTER FRONT ELEVATION**  
SCALE 1:5

**Client:** Zach-Aimee  
**Project Title:** Private Villa -Dubai Hills

**Location:** Dubai, U.A.E.  
**Plot Area:** 0000.00 Sqm  
0000.00 SqFt  
**Old Gate Level:** 0.00 = 0.000  
**NEW GATE LEVEL = 0.000**  
Proposed Gate Level is to be 000 mm above existing Asphalt Road Level

**Sheet Contents:** TERRACE  
BAR COUNTER  
FRONT ELEVATION

Designed by:	Drawn By:	Checked By:	Issued By:
ab	mp	ab	ab
Scale: 1:100	Sheet Size: A1	Stage: Conceptual	Rev No: 0

**Drwg No.** ID-401-2

**General Notes:**

- All dimensions are in millimeters unless otherwise noted.
- Any inconsistency or discrepancy is to be brought to the attention of and resolved by the architect/designer.
- All dimensions are to be checked on site before commencing work.
- This drawing is to be coordinated with the Lead Consultant.


**Notes**

\* ALL DRAWINGS ARE FOR DESIGN INTENT ONLY AND ARE NOT FOR CONSTRUCTION. THE APPOINTED CONTRACTOR SHOULD PROVIDE SHOP DRAWING FOR APPROVAL.

\* CONTRACTOR TO DO A SITE SURVEY TO SPECIFY CORRECT QUANTITY & DIMENSIONS AS PER SITE MEASUREMENTS & DRAWINGS.

\* CONTRACTOR TO CHECK THE MECHANISM & FUNCTIONALITY OF THE DESIGN INTEND.

\* MATERIAL MUST BE PRESENTED TO PRIOR TO PURCHASE FOR TO APPROVE.

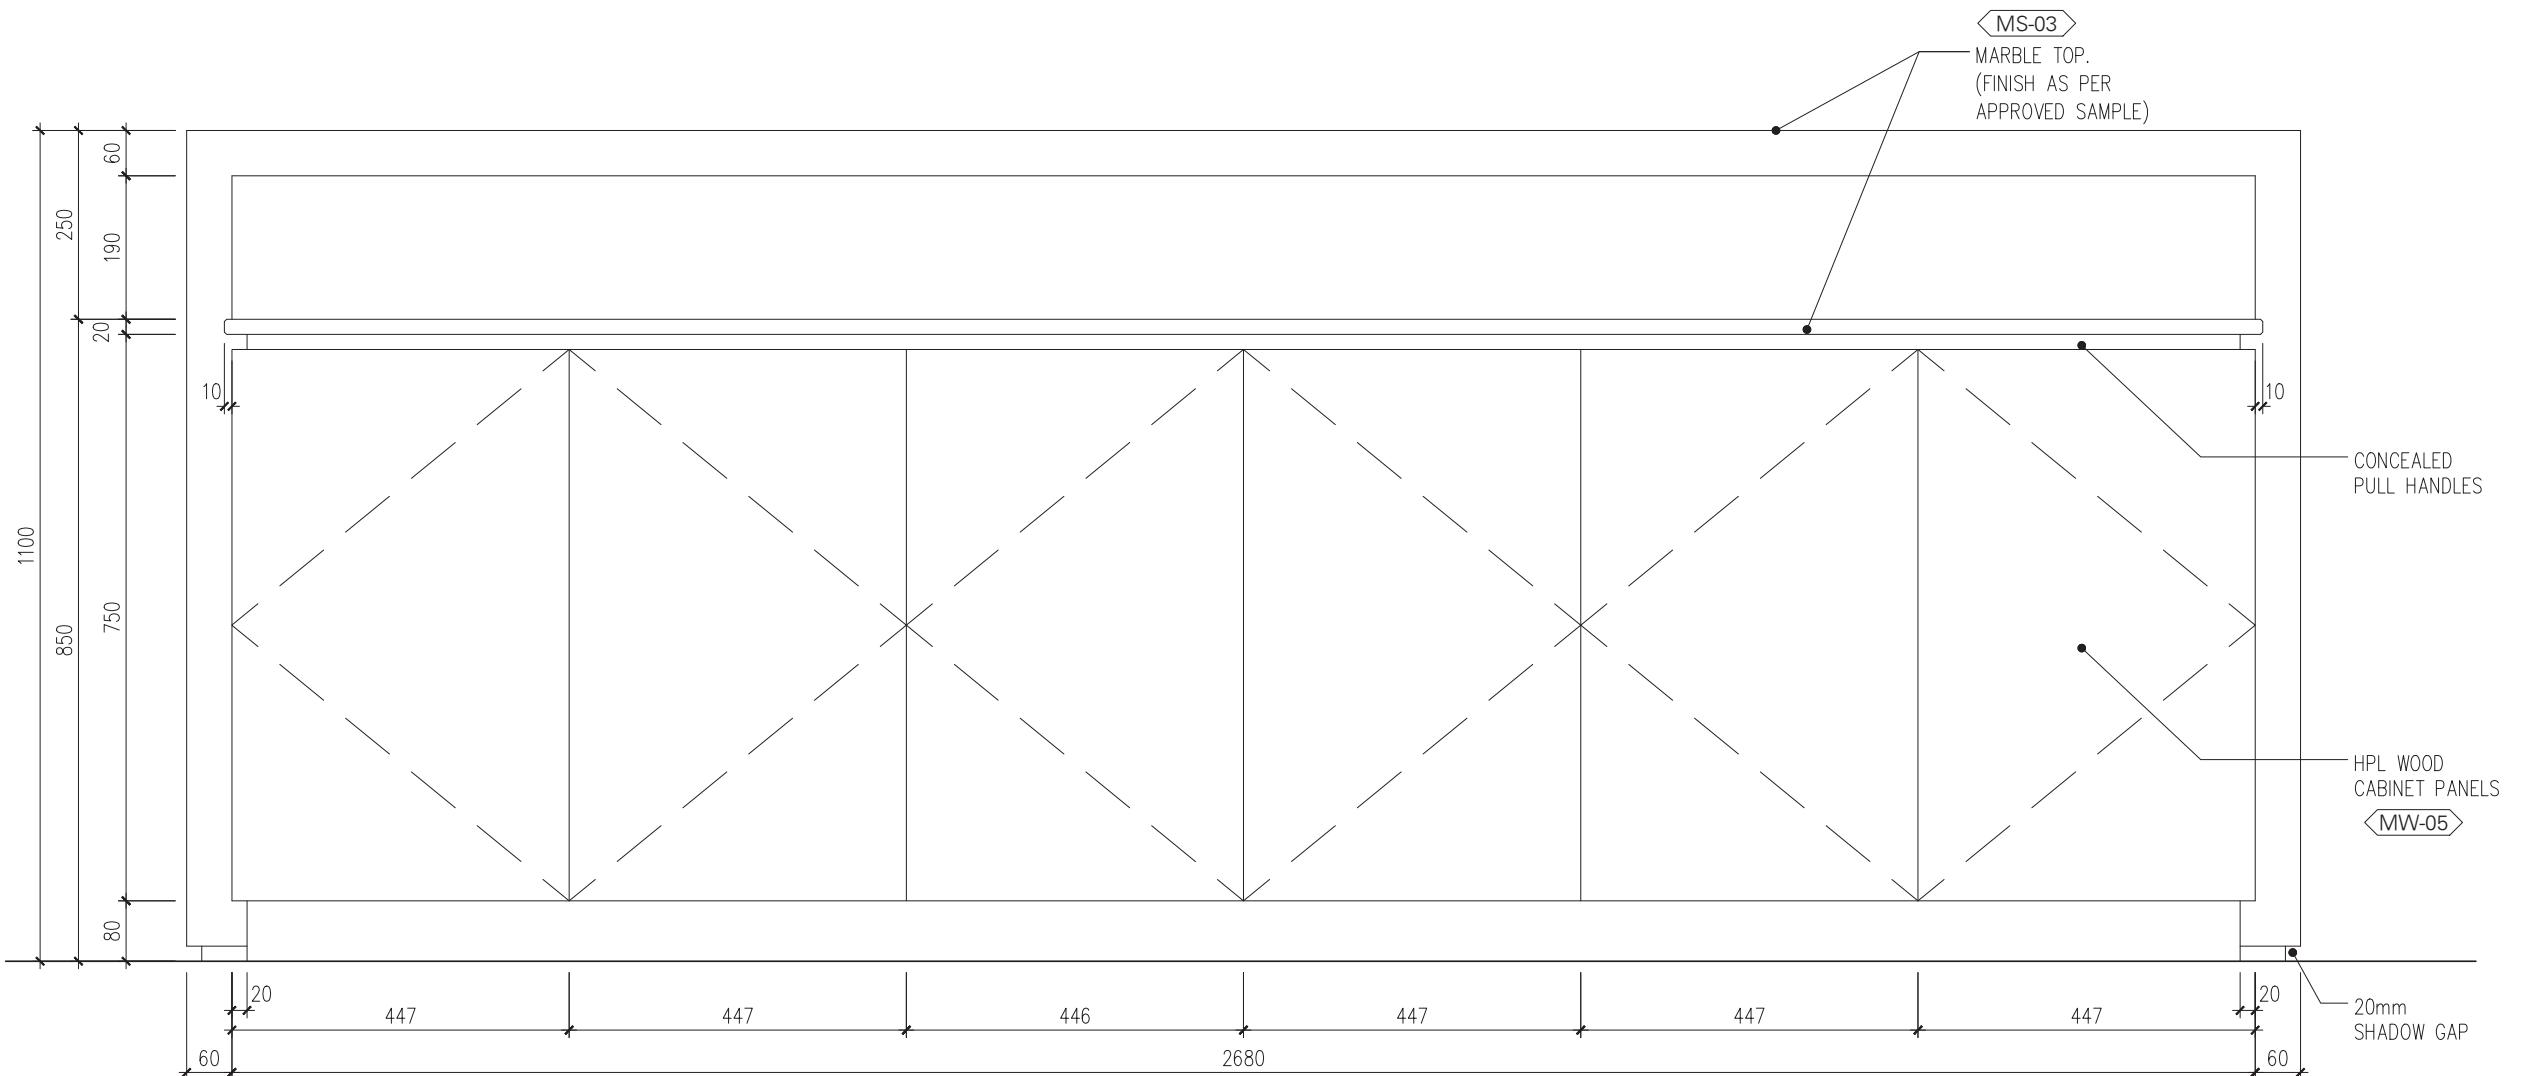

3 BAR COUNTER REAR ELEVATION  
SCALE 1:5

**Client:** Zach-Aimee  
**Project Title:** Private Villa -Dubai Hills  
**Location:** Dubai, U.A.E.  
**Plot Area:** 0000.00 Sqm 0000.00 SqFt  
**Old Gate Level:** 0.00 = 0.000  
**NEW GATE LEVEL = 0.000**  
Proposed Gate Level is to be 000 mm above existing Asphalt Road Level

Sheet Contents:			
TERRACE	BAR COUNTER	REAR ELEVATION	
Designed by:	Drawn By:	Checked By:	Issued By:
ab	mp	ab	ab

**Scale:** 1:100 **Sheet Size:** A1 **Stage:** Conceptual Stage **Rev No:** 0

**Drwg No.** ID-401-3

**General Notes:**

- All dimensions are in millimeters unless otherwise noted.
- Any inconsistency or discrepancy is to be brought to the attention of and resolved by the architect/designer.
- All dimensions are to be checked on site before commencing work.
- This drawing is to be coordinated with the Lead Consultant.


**Notes**

\* ALL DRAWINGS ARE FOR DESIGN INTENT ONLY AND ARE NOT FOR CONSTRUCTION. THE APPOINTED CONTRACTOR SHOULD PROVIDE SHOP DRAWING FOR APPROVAL.

\* CONTRACTOR TO DO A SITE SURVEY TO SPECIFY CORRECT QUANTITY & DIMENSIONS AS PER SITE MEASUREMENTS & DRAWINGS.

\* CONTRACTOR TO CHECK THE MECHANISM & FUNCTIONALITY OF THE DESIGN INTEND.

\* MATERIAL MUST BE PRESENTED TO PRIOR TO PURCHASE FOR TO APPROVE.

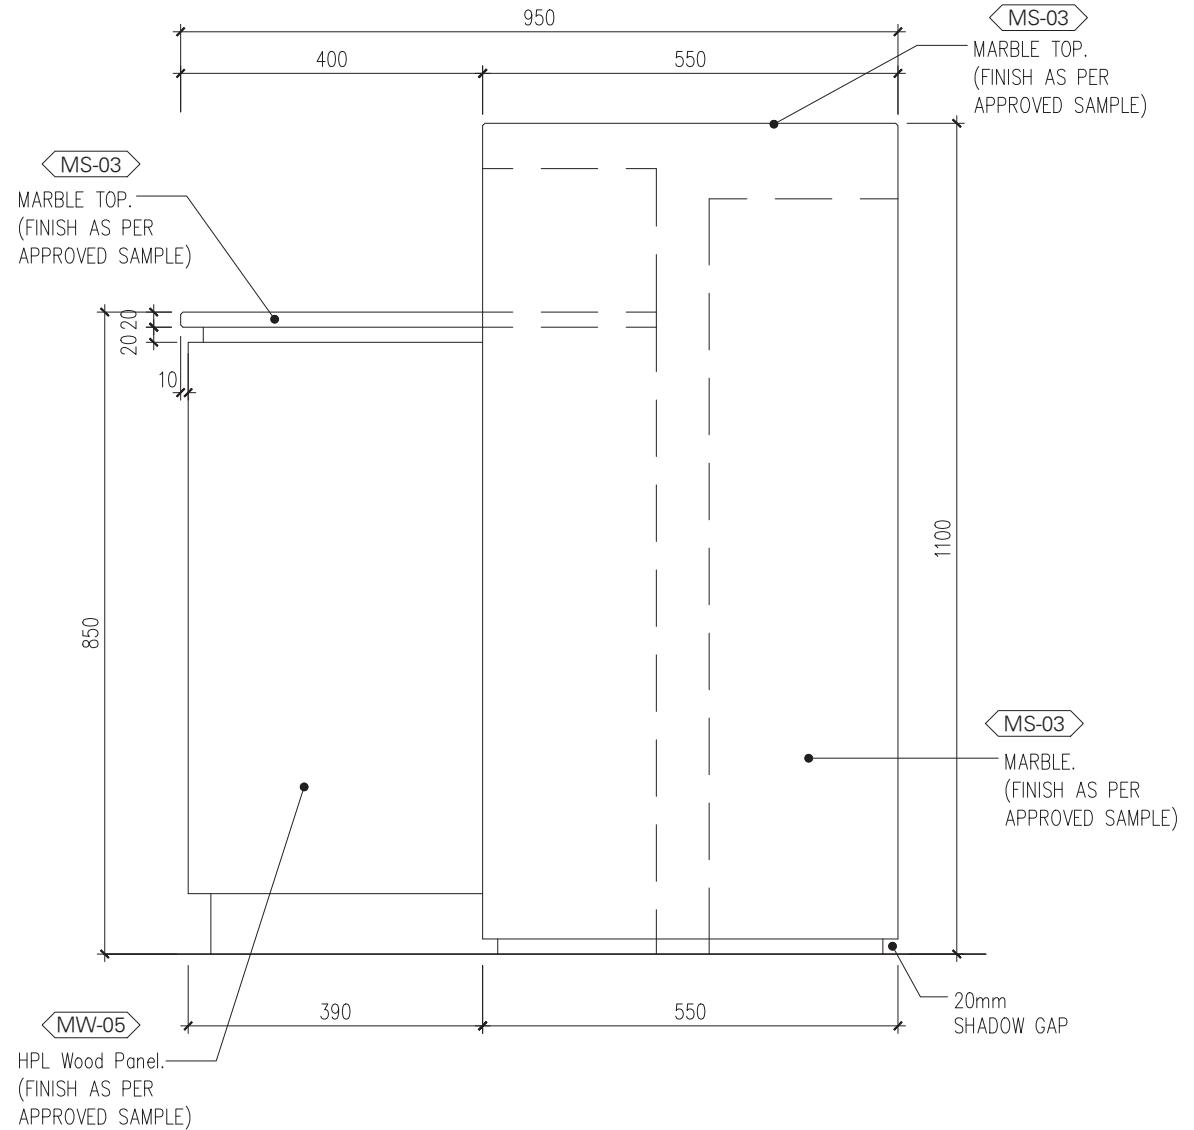

5

**BAR COUNTER SIDE ELEVATION**

SCALE 1:5

0	2025.05.12	mp	Initial issue
Rev	Date	Drawn	Revisions

**Design Architect:**

**Client:**  
Zach-Aimee


**Project Title:**  
Private Villa -Dubai Hills

**Location:**  
Dubai, U.A.E.

**Plot Area:** 0000.00 Sqm  
0000.00 SqFt  
**Old Gate Level:** 0.00 = 0.000  
**NEW GATE LEVEL = 0.000**  
Proposed Gate Level is to be 000 mm above existing Asphalt Road Level

<b>Sheet Contents:</b>			
TERRACE BAR COUNTER SIDE ELEVATION			
Designed by:	Drawn By:	Checked By:	Issued By:
ab	mp	ab	ab

**Drwg No.** ID-401-4

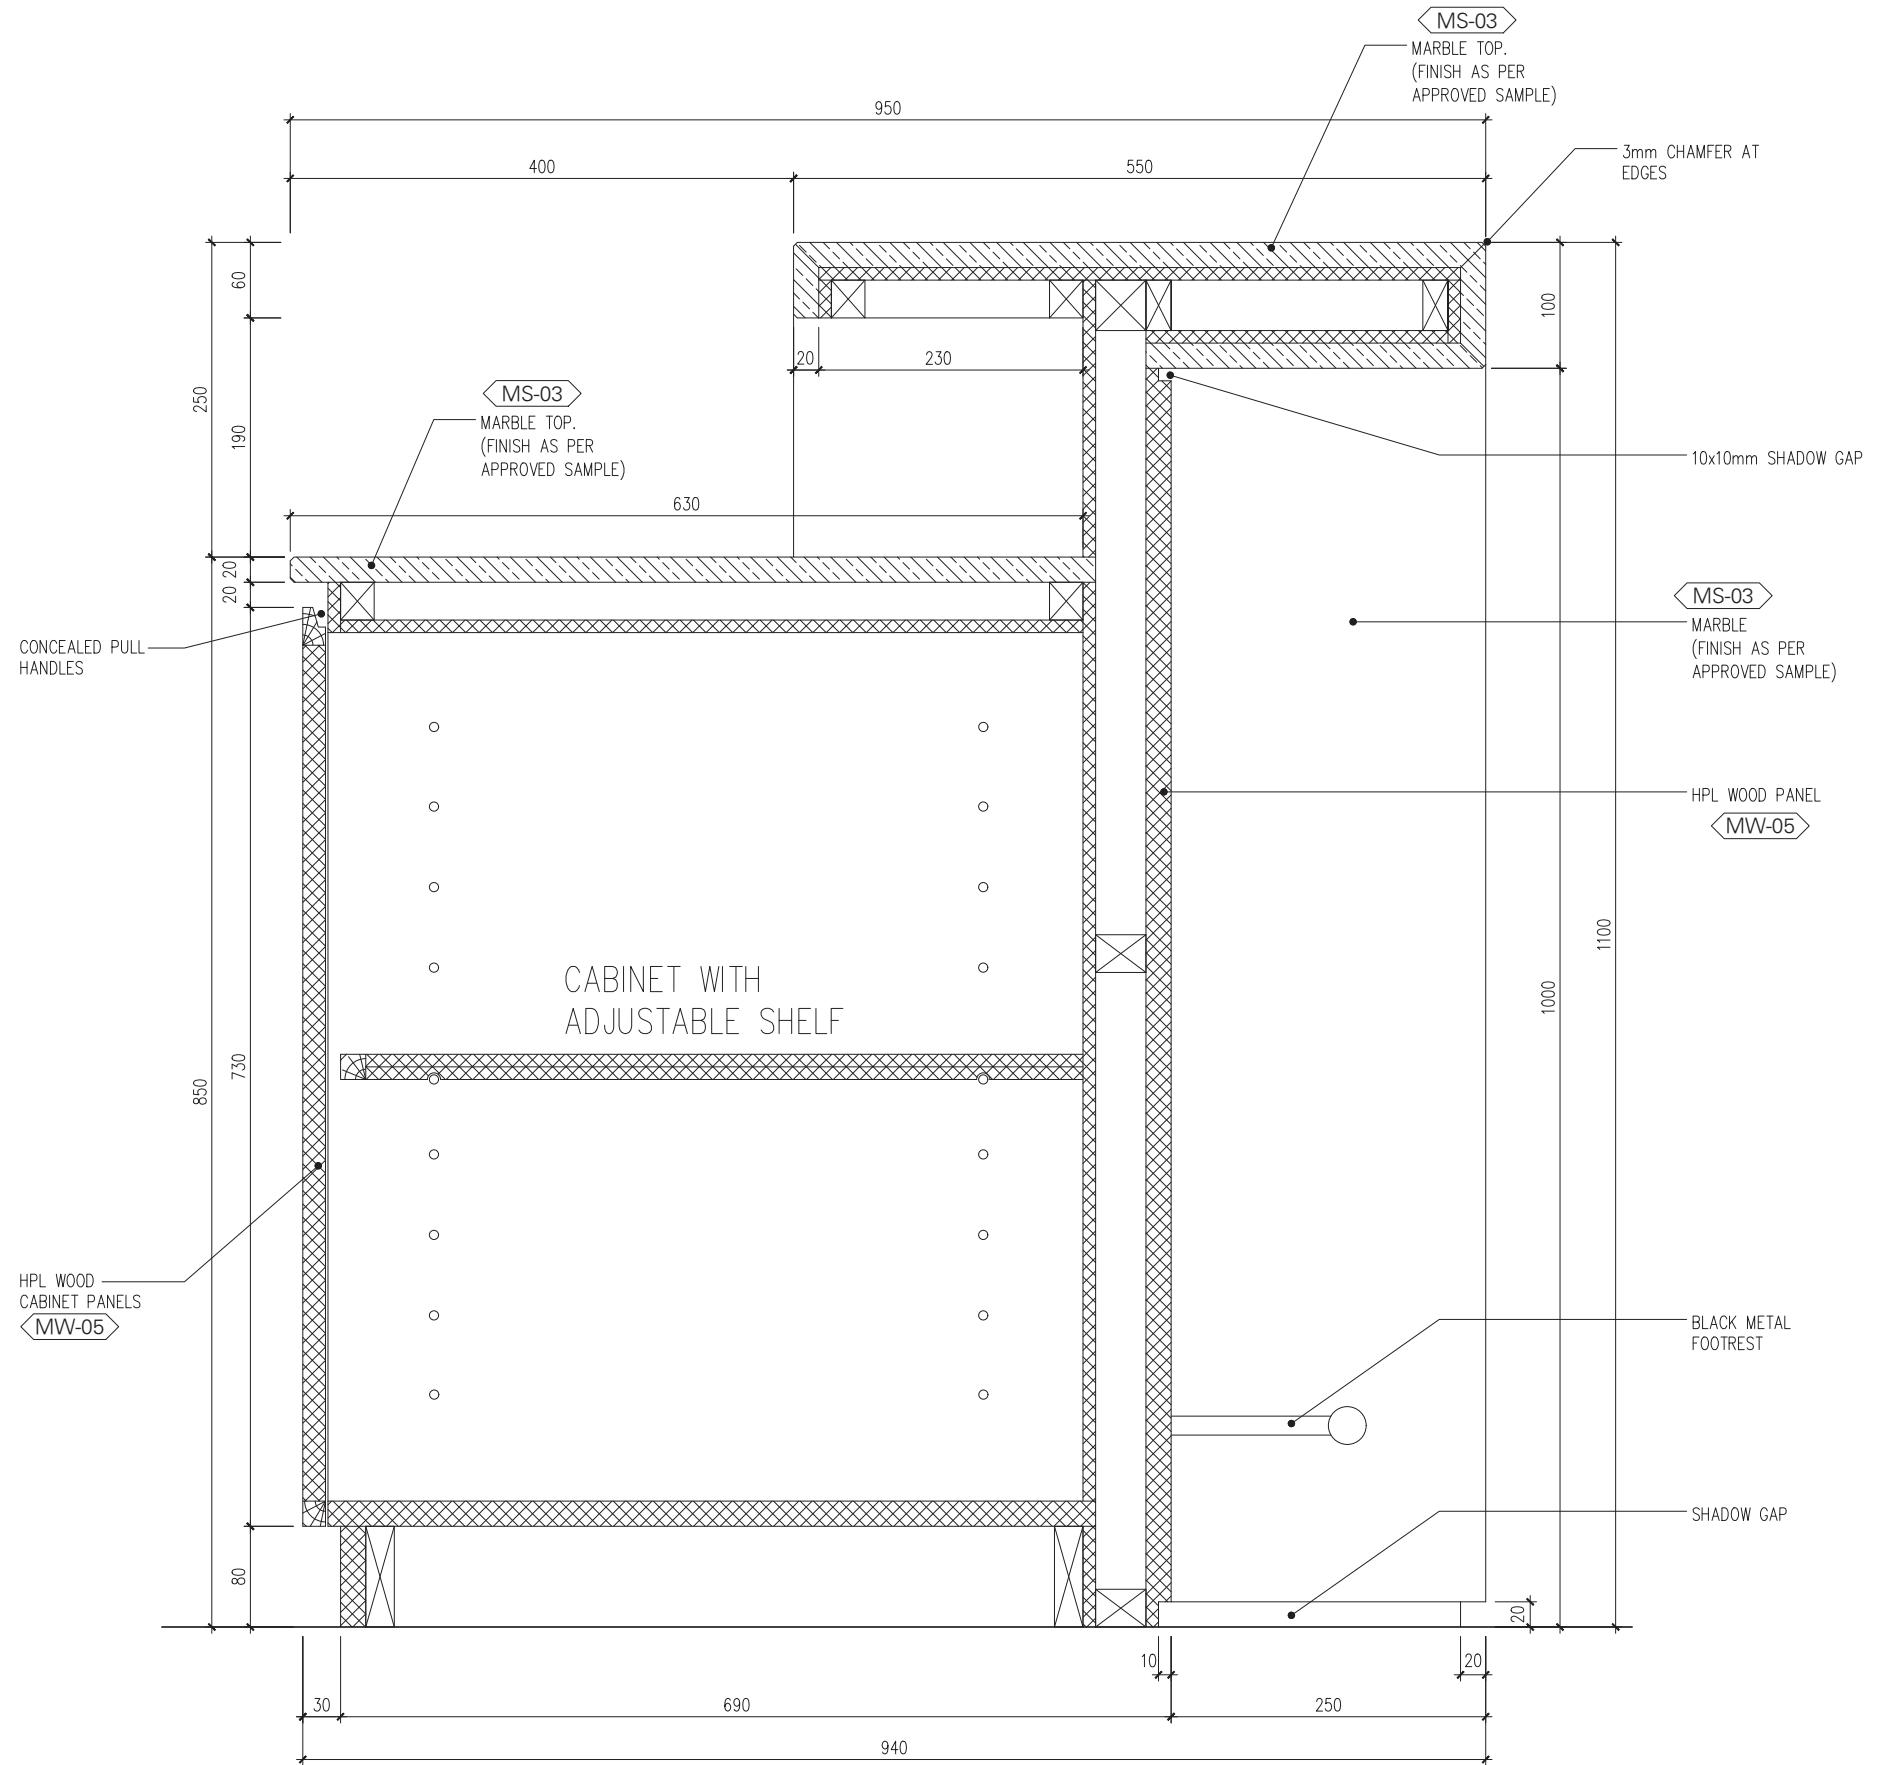

**4** BAR COUNTER SECTION  
- SCALE 1:5

**General Notes:**

- 1. All dimensions are in millimeters unless otherwise noted.
- 2. Any inconsistency or discrepancy is to be brought to the attention of and resolved by the architect/designer.
- 3. All dimensions are to be checked on site before commencing work.
- 4. This drawing is to be coordinated with the Lead Consultant.

### Notes

\* ALL DRAWINGS ARE FOR DESIGN INTENT ONLY AND ARE NOT FOR CONSTRUCTION. THE APPOINTED CONTRACTOR SHOULD PROVIDE SHOP DRAWING FOR APPROVAL.

**CONTRACTOR TO DO A SITE SURVEY  
TO SPECIFY CORRECT QUANTITY &  
DIMENSIONS AS PER SITE MEASUREMENTS  
& DRAWINGS.**

CONTRACTOR TO CHECK THE MECHANISM & FUNCTIONALITY OF THE DESIGN INTEND.

MATERIAL MUST BE PRESENTED TO PRIOR  
TO PURCHASE FOR TO APPROVE.

**Design Architect:**

Zach-Aimee

WILL DODD WILL

**Location:**

Dubai, U.A.E.

Blatt A - 0000.00-0

Old Gate Level: 0.00 = 0.000  
NEW GATE LEVEL = 0.000

The proposed Gate Level is to be 000 mm above existing Asphalt Road Level

<b>TERRACE BAR COUNTER VANITY DETAIL</b>			
Designed by:	Drawn By:	Checked By:	Issued By:
<b>ab</b>	<b>mp</b>	<b>ab</b>	<b>ab</b>
Specs:	Sheet Size:	Stage:	Rev. No.:


Drug No.: ID-101-E

**General Notes:**


- All dimensions are in millimeters unless otherwise noted.
- Any inconsistency or discrepancy is to be brought to the attention of and resolved by the architect/designer.
- All dimensions are to be checked on site before commencing work.
- This drawing is to be coordinated with the Lead Consultant.

**Notes**

- \* ALL DRAWINGS ARE FOR DESIGN INTENT ONLY AND ARE NOT FOR CONSTRUCTION. THE APPOINTED CONTRACTOR SHOULD PROVIDE SHOP DRAWING FOR APPROVAL.
- \* CONTRACTOR TO DO A SITE SURVEY TO SPECIFY CORRECT QUANTITY & DIMENSIONS AS PER SITE MEASUREMENTS & DRAWINGS.
- \* CONTRACTOR TO CHECK THE MECHANISM & FUNCTIONALITY OF THE DESIGN INTEND.
- \* MATERIAL MUST BE PRESENTED TO PRIOR TO PURCHASE FOR TO APPROVE.

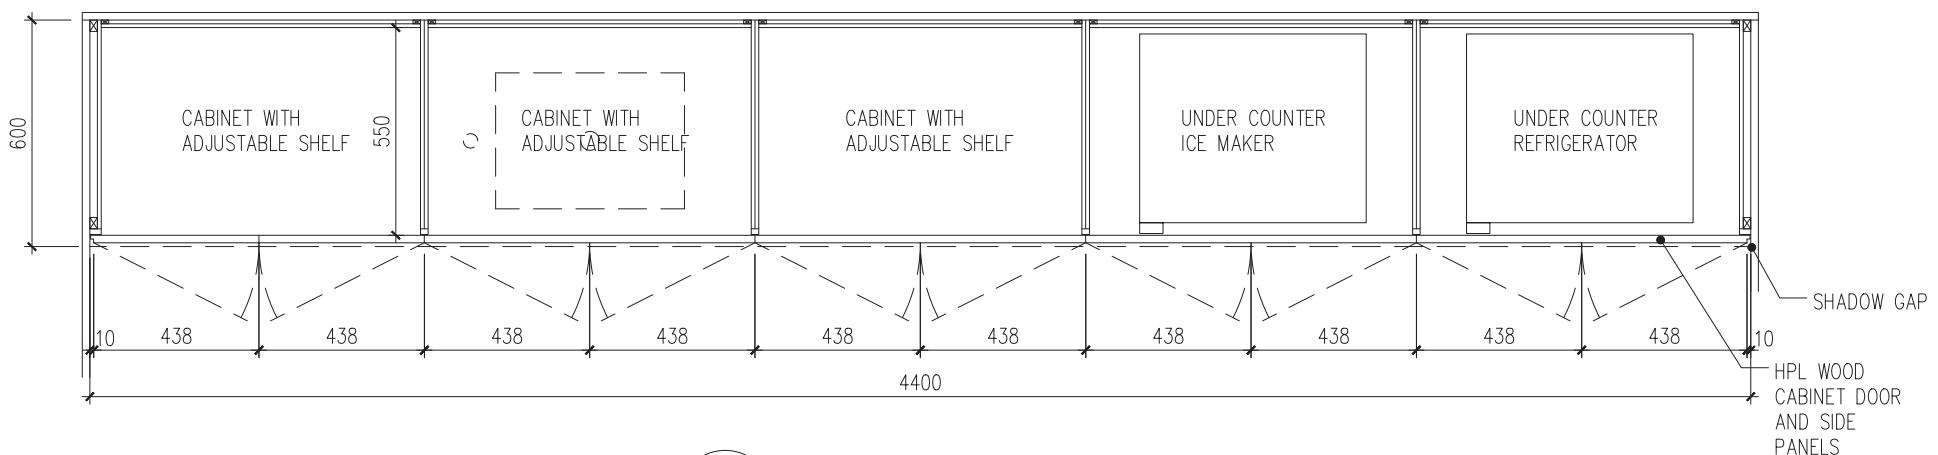

2 VANITY UNIT PLAN SECTION  
SCALE 1:10

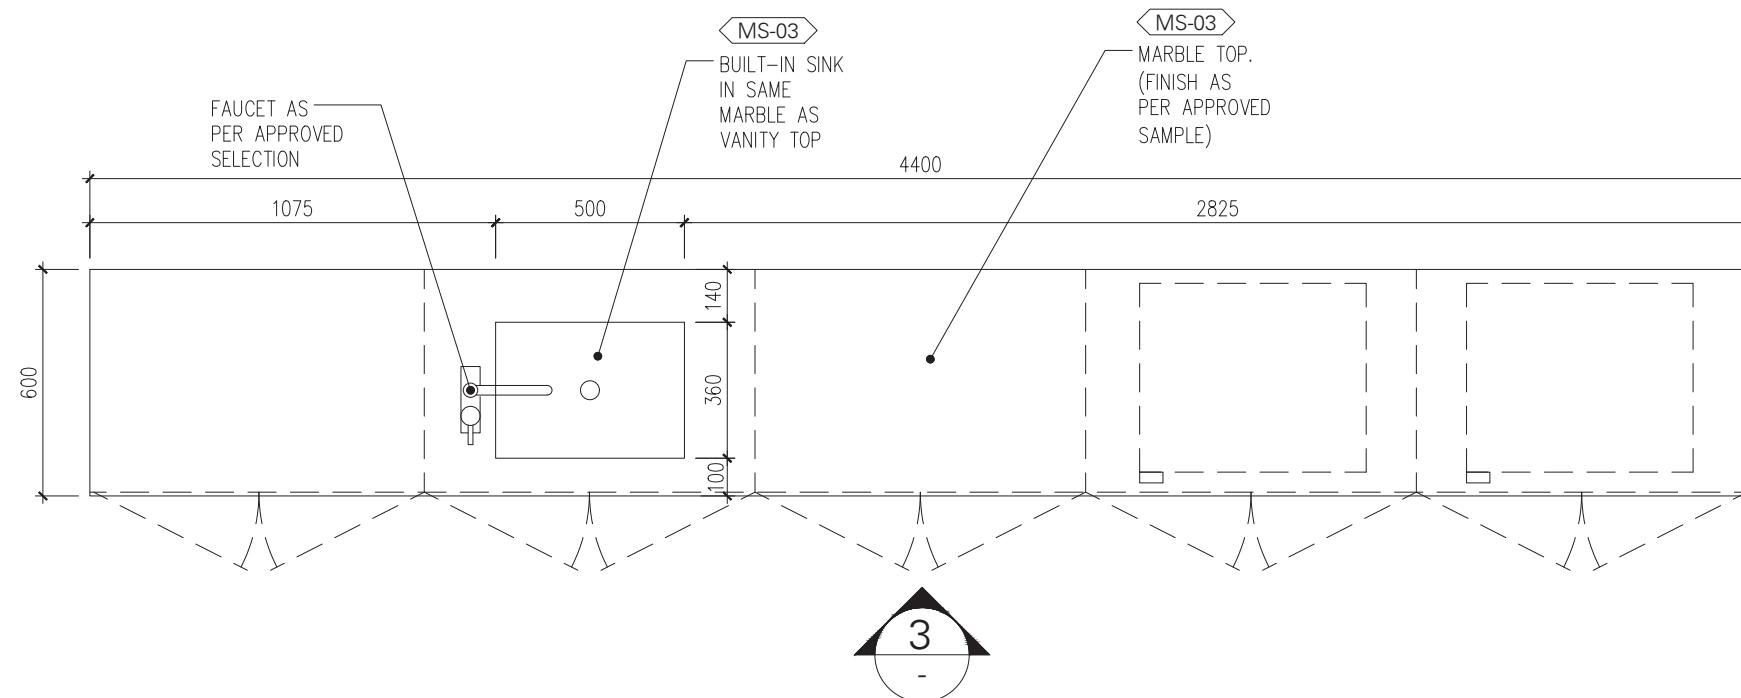

1 VANITY UNIT PLAN  
SCALE 1:10

0	2025.05.12	mp	Initial issue
Rev	Date	Drawn	Revisions

**Design Architect:**

**Client:**  
Zach-Aimee

**Project Title:**  
Private Villa -Dubai Hills

**Location:**  
Dubai, U.A.E.


**Plot Area:** 0000.00 Sqm  
0000.00 SqFt  
**Old Gate Level:** 0.00 = 0.000  
**NEW GATE LEVEL = 0.000**  
Proposed Gate Level is to be 000 mm above existing Asphalt Road Level

**Sheet Contents:**  
TERRACE  
VANITY UNIT  
PLAN AND SECTION


Designed by:	Drawn By:	Checked By:	Issued By:
ab	mp	ab	ab

**Scale:** 1:100    **Sheet Size:** A1    **Stage:** Conceptual Stage    **Rev No:** 0

**Drwg No.** ID-402-1

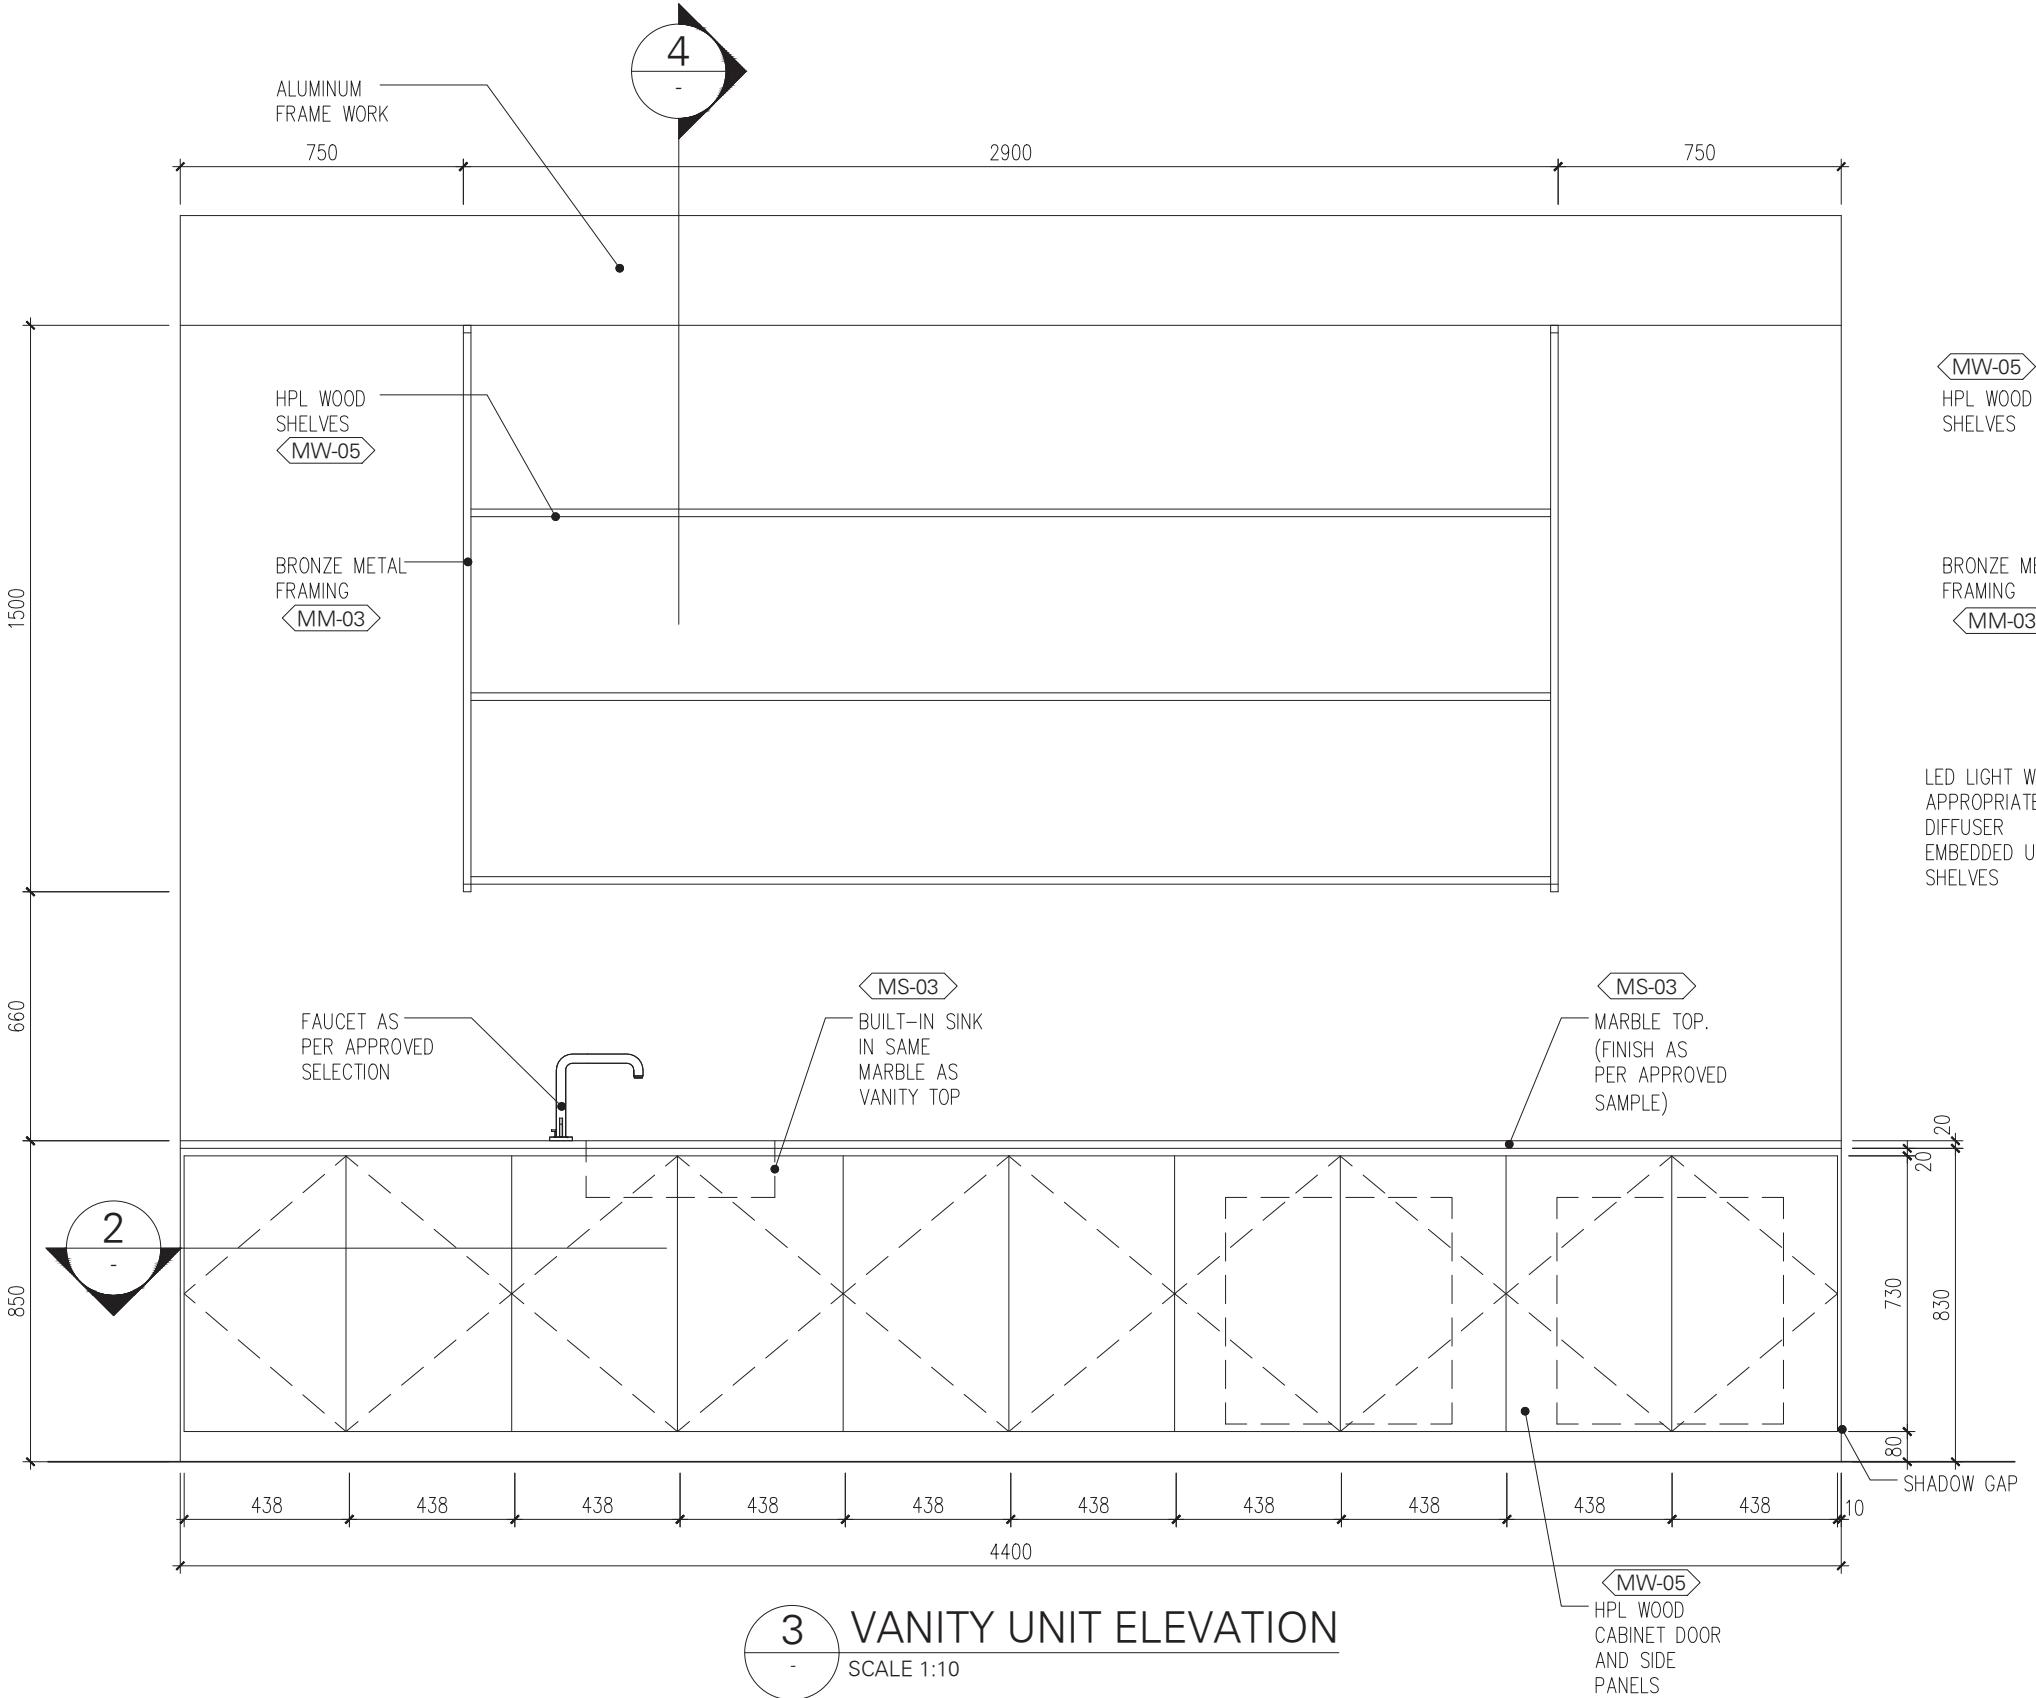

3 VANTY UNIT ELEVATION  
SCALE 1:10

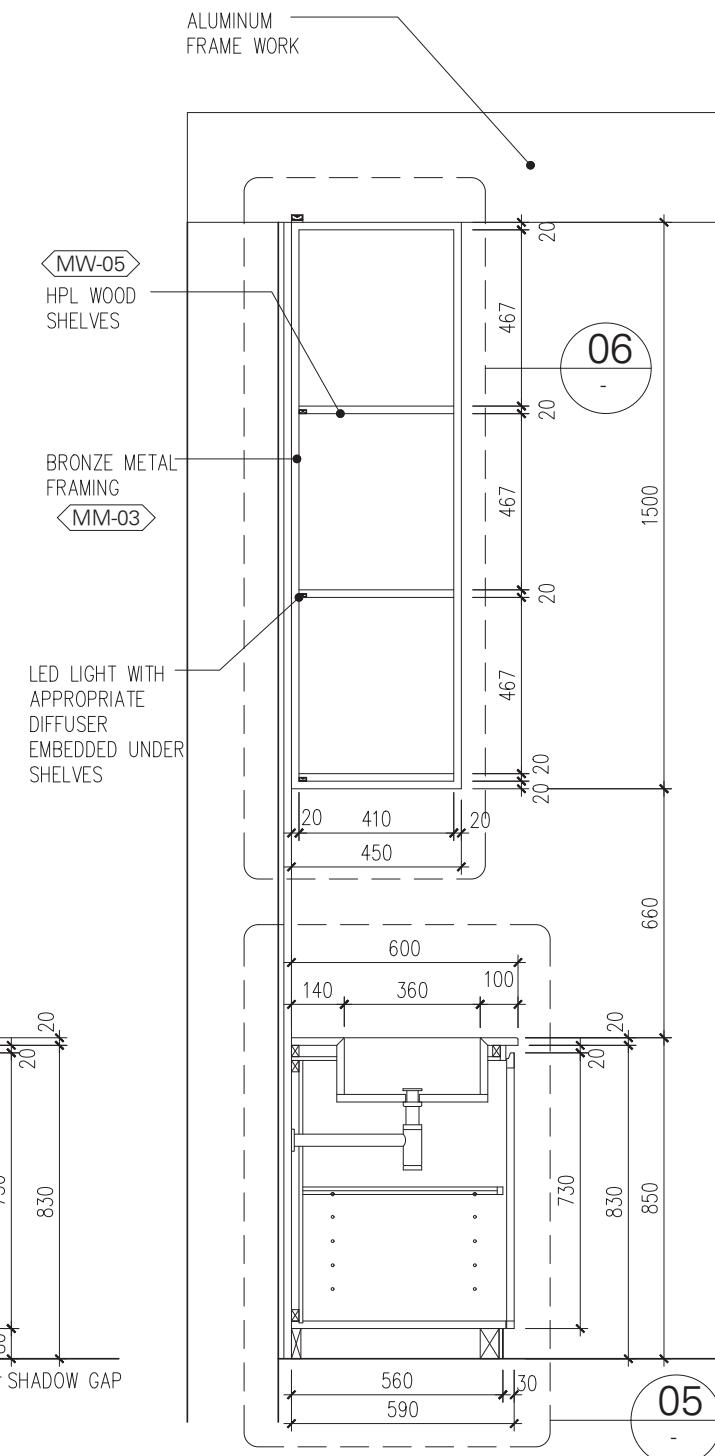

4 VANTY SECTION  
SCALE 1:10

**General Notes:**

- All dimensions are in millimeters unless otherwise noted.
- Any inconsistency or discrepancy is to be brought to the attention of and resolved by the architect/designer.
- All dimensions are to be checked on site before commencing work.
- This drawing is to be coordinated with the Lead Consultant.

**Notes**

\* ALL DRAWINGS ARE FOR DESIGN INTENT ONLY AND ARE NOT FOR CONSTRUCTION. THE APPOINTED CONTRACTOR SHOULD PROVIDE SHOP DRAWING FOR APPROVAL.

\* CONTRACTOR TO DO A SITE SURVEY TO SPECIFY CORRECT QUANTITY & DIMENSIONS AS PER SITE MEASUREMENTS & DRAWINGS.

\* CONTRACTOR TO CHECK THE MECHANISM & FUNCTIONALITY OF THE DESIGN INTEND.

\* MATERIAL MUST BE PRESENTED TO PRIOR TO PURCHASE FOR TO APPROVE.

0	2025.05.12	mp	Initial issue
Rev	Date	Drawn	Revisions

**Design Architect:**


**Client:** Zach-Aimee  
**Project Title:** Private Villa -Dubai Hills

**Location:** Dubai, U.A.E.


**Plot Area:** 0000.00 Sqm  
0000.00 SqFt  
**Old Gate Level:** 0.00 = 0.000  
**NEW GATE LEVEL = 0.000**  
Proposed Gate Level is to be 000 mm above existing Asphalt Road Level

**Sheet Contents:**  
TERRACE  
VANITY UNIT  
ELEVATION & SECTION  
Designed by: Drawn By: Checked By: Issued By:  
ab mp ab ab  
Scale: Sheet Size: Stage: Rev No:  
1:100 A1 Conceptual Stage 0

**Drwg No.** ID-402-2

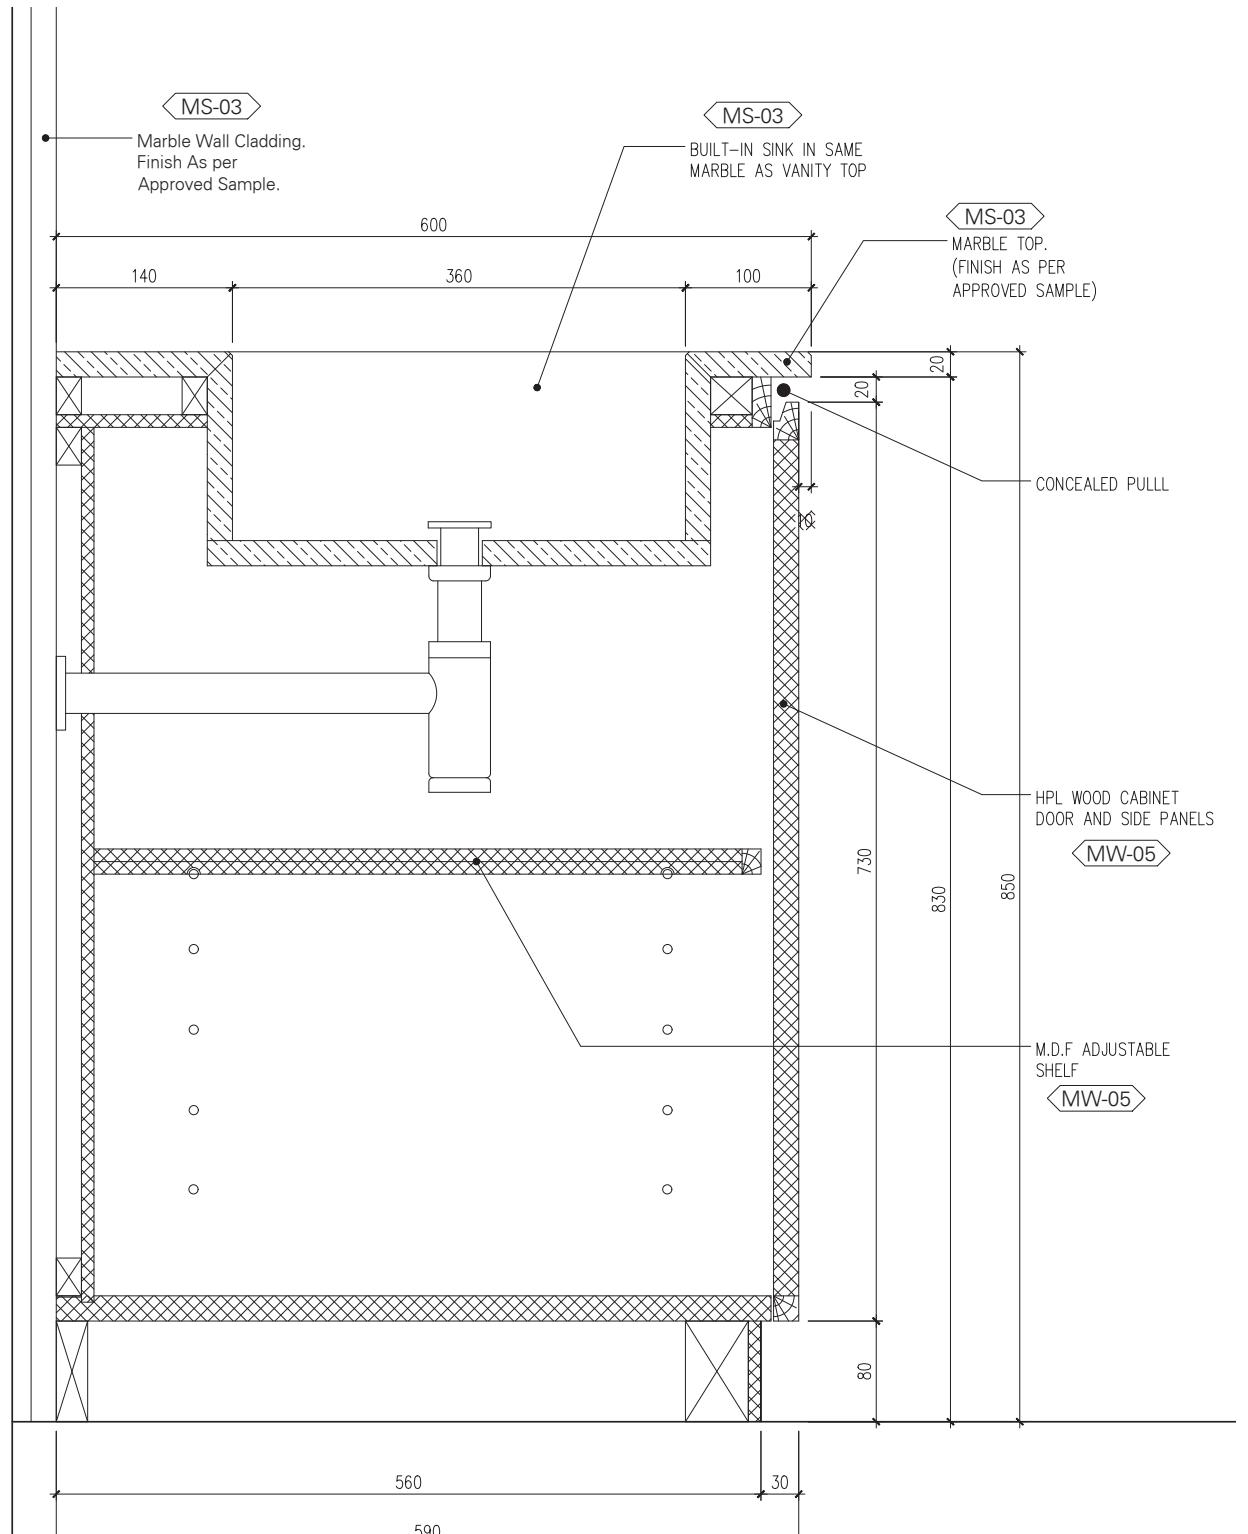

**5** VANITY SECTION DETAIL  
SCALE 1:5

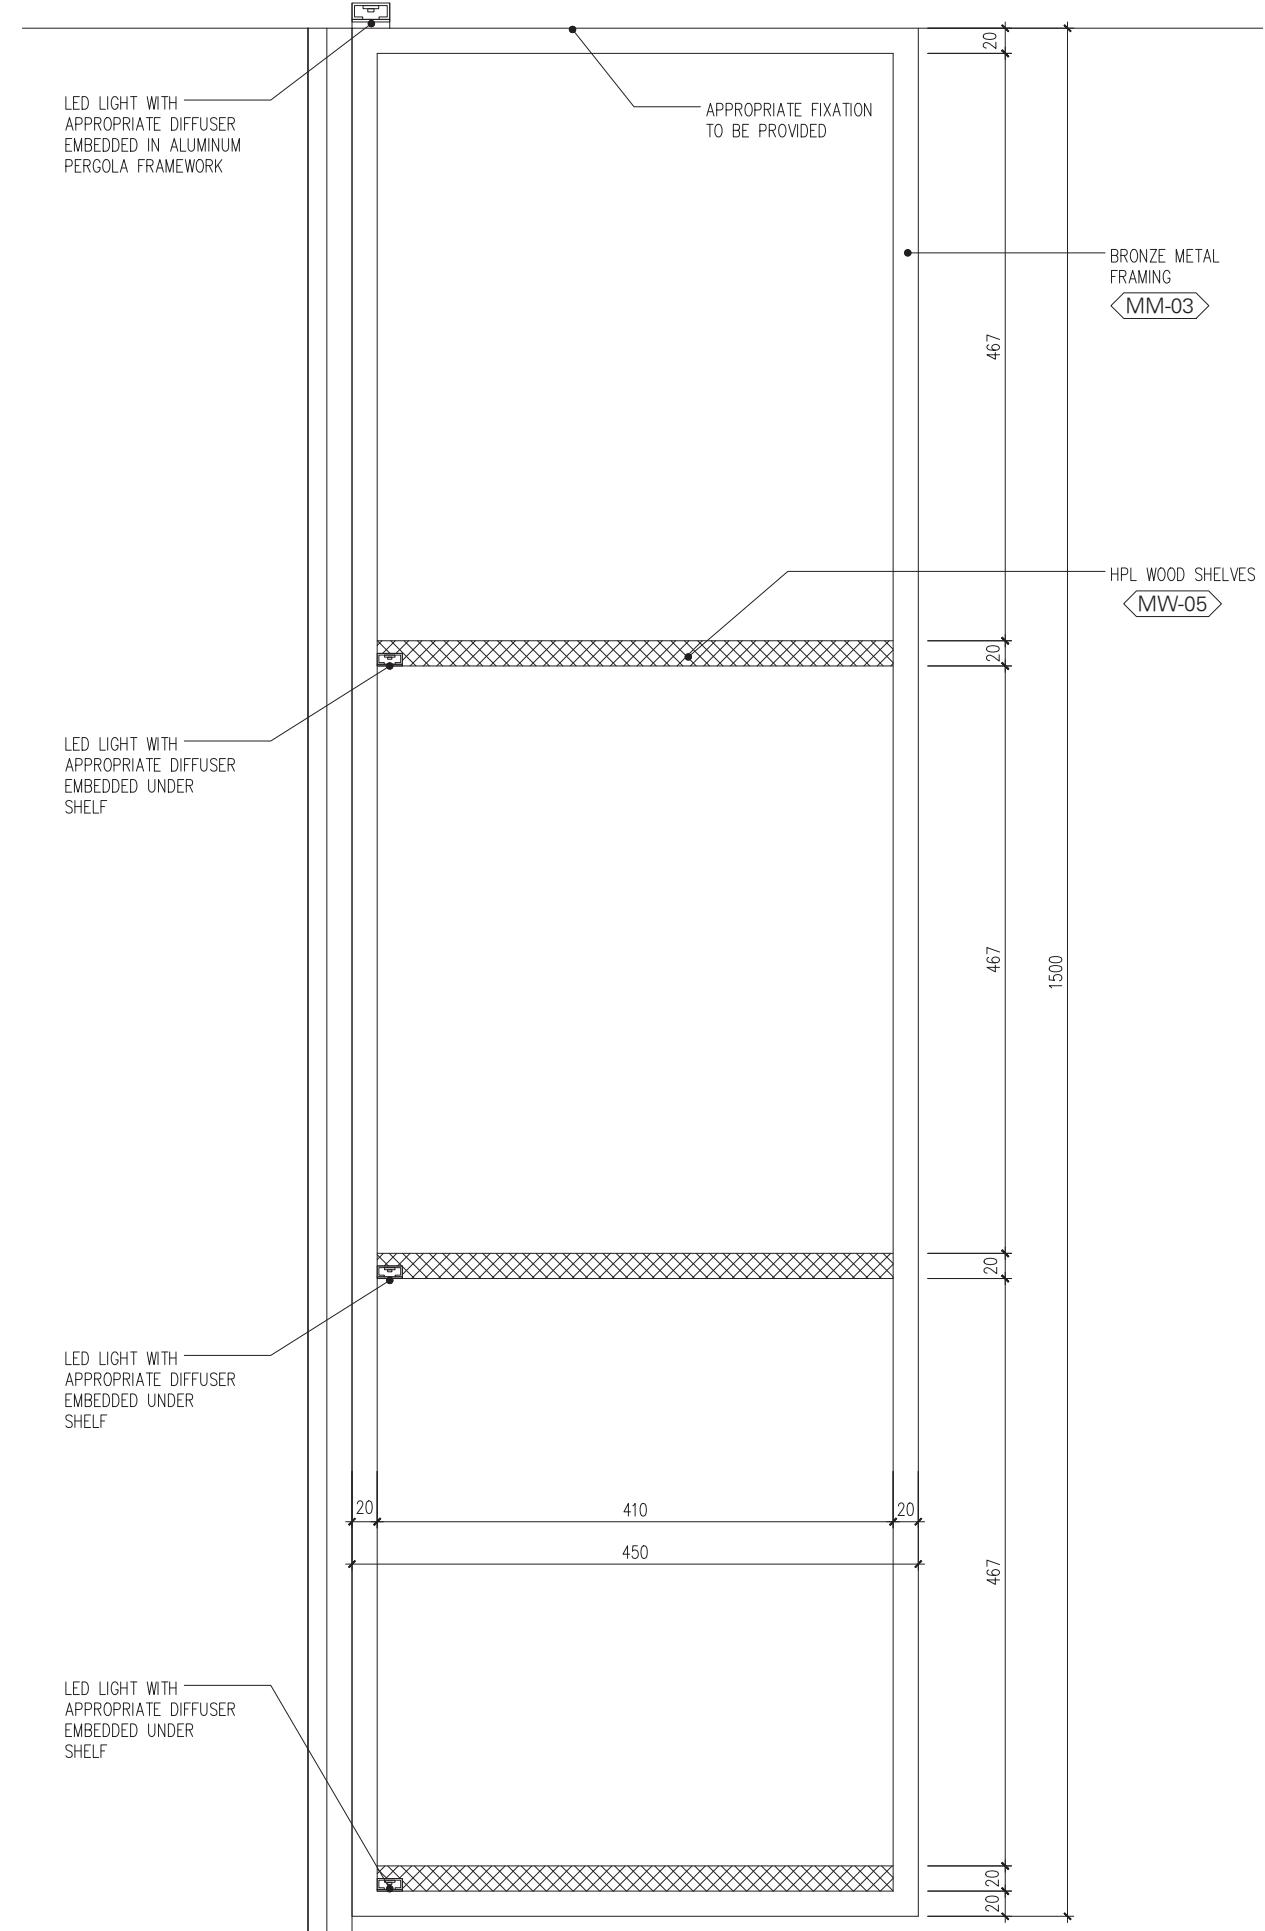

**6** SHELVING SECTION DETAIL  
SCALE 1:5

**General Notes:**

- All dimensions are in millimeters unless otherwise noted.
- Any inconsistency or discrepancy is to be brought to the attention of and resolved by the architect/designer.
- All dimensions are to be checked on site before commencing work.
- This drawing is to be coordinated with the Lead Consultant.

**Notes**

- \* ALL DRAWINGS ARE FOR DESIGN INTENT ONLY AND ARE NOT FOR CONSTRUCTION. THE APPOINTED CONTRACTOR SHOULD PROVIDE SHOP DRAWING FOR APPROVAL.
- \* CONTRACTOR TO DO A SITE SURVEY TO SPECIFY CORRECT QUANTITY & DIMENSIONS AS PER SITE MEASUREMENTS & DRAWINGS.
- \* CONTRACTOR TO CHECK THE MECHANISM & FUNCTIONALITY OF THE DESIGN INTEND.
- \* MATERIAL MUST BE PRESENTED TO PRIOR TO PURCHASE FOR TO APPROVE.

0	2025.05.12	mp	Initial issue
Rev	Date	Drawn	Revisions

**Design Architect:**

**Client:** Zach-Aimee  
**Project Title:** Private Villa -Dubai Hills  
**Location:** Dubai, U.A.E.

**Plot Area:** 0000.00 Sqm  
0000.00 SqFt  
**Old Gate Level:** 0.00 = 0.000  
**NEW GATE LEVEL = 0.000**  
Proposed Gate Level is to be 000 mm above existing Asphalt Road Level

**Sheet Contents:** TERRACE  
VANITY UNIT + SHELVING  
DETAILS

Designed by:	Drawn By:	Checked By:	Issued By:
ab	mp	ab	ab

Scale: Sheet Size: Stage: Rev No:  
1:100 A1 Conceptual Stage 0

**Drwg No.** ID-402-3

**General Notes:**

- All dimensions are in millimeters unless otherwise noted.
- Any inconsistency or discrepancy is to be brought to the attention of and resolved by the architect/designer.
- All dimensions are to be checked on site before commencing work.
- This drawing is to be coordinated with the Lead Consultant.



**Notes**

\* ALL DRAWINGS ARE FOR DESIGN INTENT ONLY AND ARE NOT FOR CONSTRUCTION. THE APPOINTED CONTRACTOR SHOULD PROVIDE SHOP DRAWING FOR APPROVAL.

\* CONTRACTOR TO DO A SITE SURVEY TO SPECIFY CORRECT QUANTITY & DIMENSIONS AS PER SITE MEASUREMENTS & DRAWINGS.

\* CONTRACTOR TO CHECK THE MECHANISM & FUNCTIONALITY OF THE DESIGN INTEND.

\* MATERIAL MUST BE PRESENTED TO PRIOR TO PURCHASE FOR TO APPROVE.

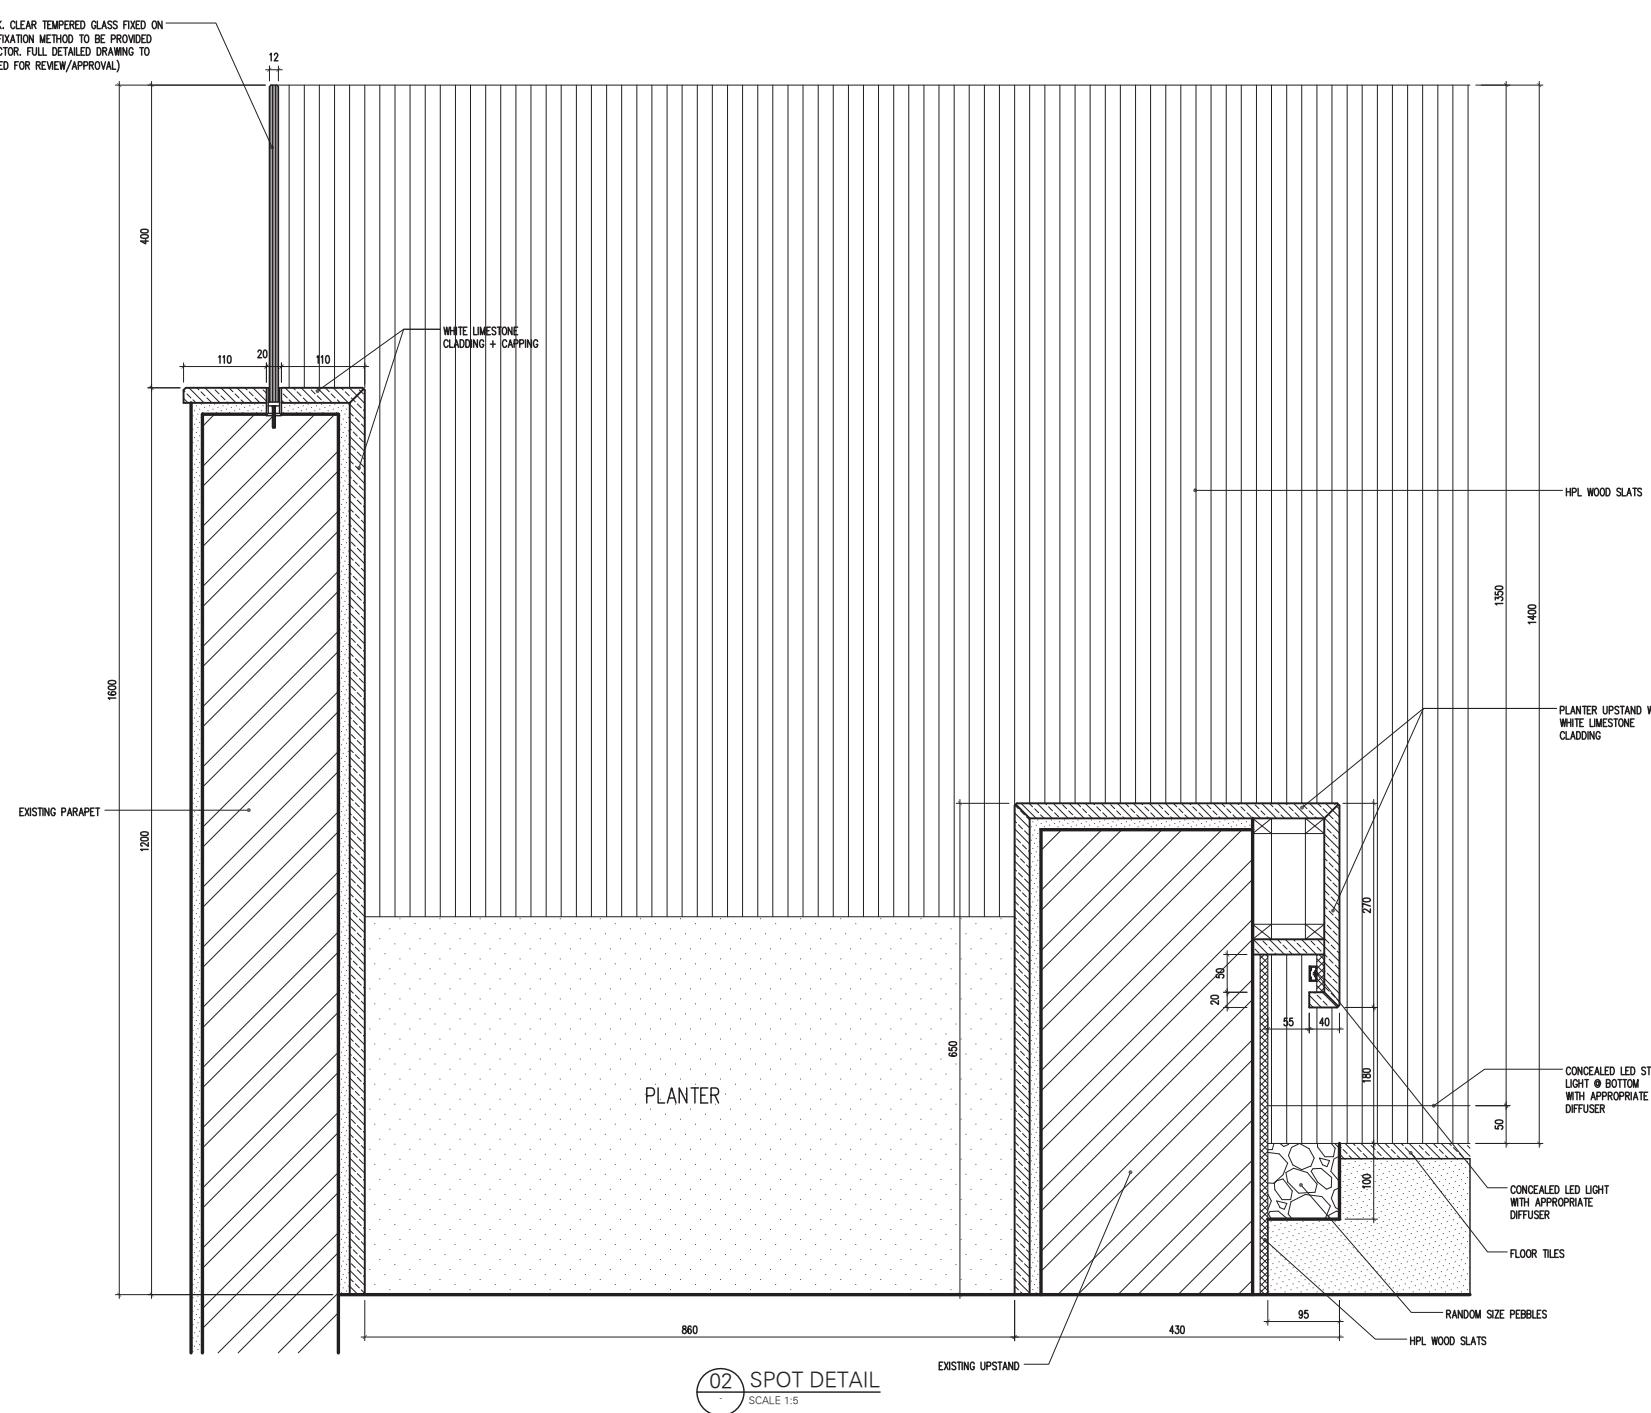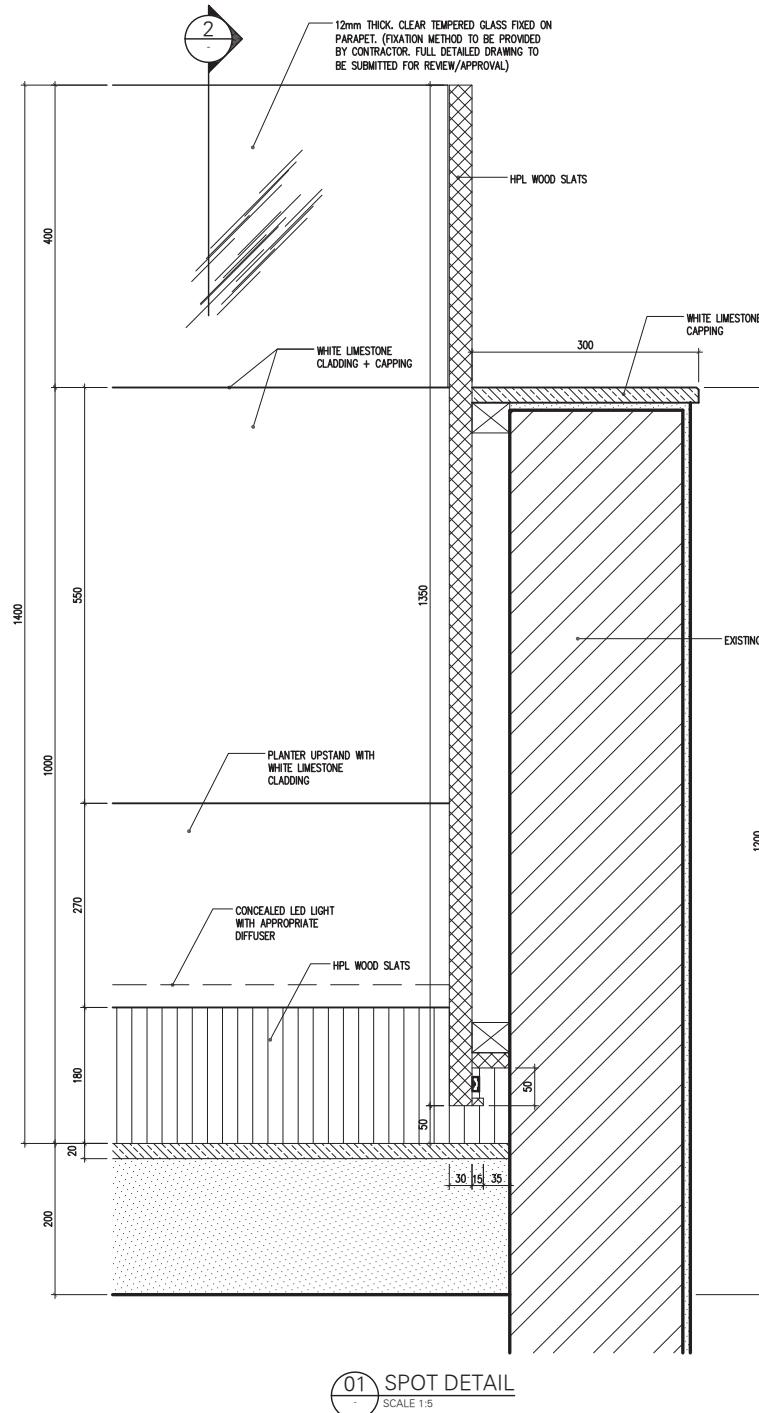

0	2025.05.12	mp	Initial issue
Rev	Date	Drawn	Revisions

**Design Architect:**

**Client:**  
Zach-Aimee

**Project Title:**  
Private Villa -Dubai Hills

**Location:**  
Dubai, U.A.E.

**Plot Area:** 0000.00 Sqm  
0000.00 SqFt  
**Old Gate Level:** 0.00 = 0.000  
**NEW GATE LEVEL:** = 0.000  
Proposed Gate Level is to be 000 mm above existing Asphalt Road Level

**Sheet Contents:**  
TERRACE  
SPOT DETAILS  
1 & 2

Designed by:	Drawn By:	Checked By:	Issued By:
ab	mp	ab	ab
Scale:	Sheet Size:	Stage:	Rev No:
1:100	A1	Conceptual Stage	0

**Drwg No.** ID-403

**General Notes:**

- All dimensions are in millimeters unless otherwise noted.
- Any inconsistency or discrepancy is to be brought to the attention of and resolved by the architect/designer.
- All dimensions are to be checked on site before commencing work.
- This drawing is to be coordinated with the Lead Consultant.


**Notes**

\* ALL DRAWINGS ARE FOR DESIGN INTENT ONLY AND ARE NOT FOR CONSTRUCTION. THE APPOINTED CONTRACTOR SHOULD PROVIDE SHOP DRAWING FOR APPROVAL.


\* CONTRACTOR TO DO A SITE SURVEY TO SPECIFY CORRECT QUANTITY & DIMENSIONS AS PER SITE MEASUREMENTS & DRAWINGS.

\* CONTRACTOR TO CHECK THE MECHANISM & FUNCTIONALITY OF THE DESIGN INTEND.

\* MATERIAL MUST BE PRESENTED TO PRIOR TO PURCHASE FOR TO APPROVE.

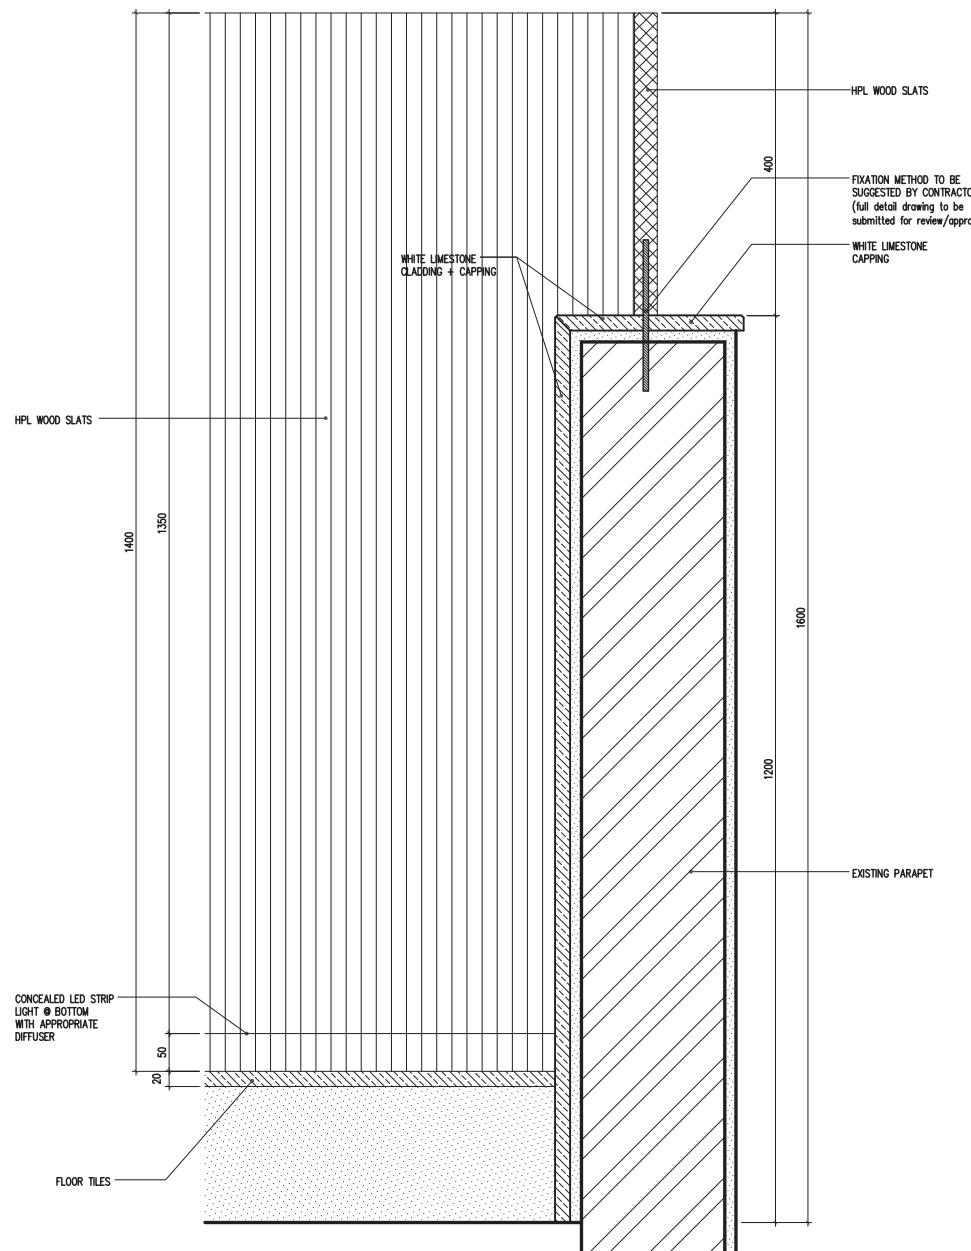

03 SPOT DETAIL  
SCALE 1:5

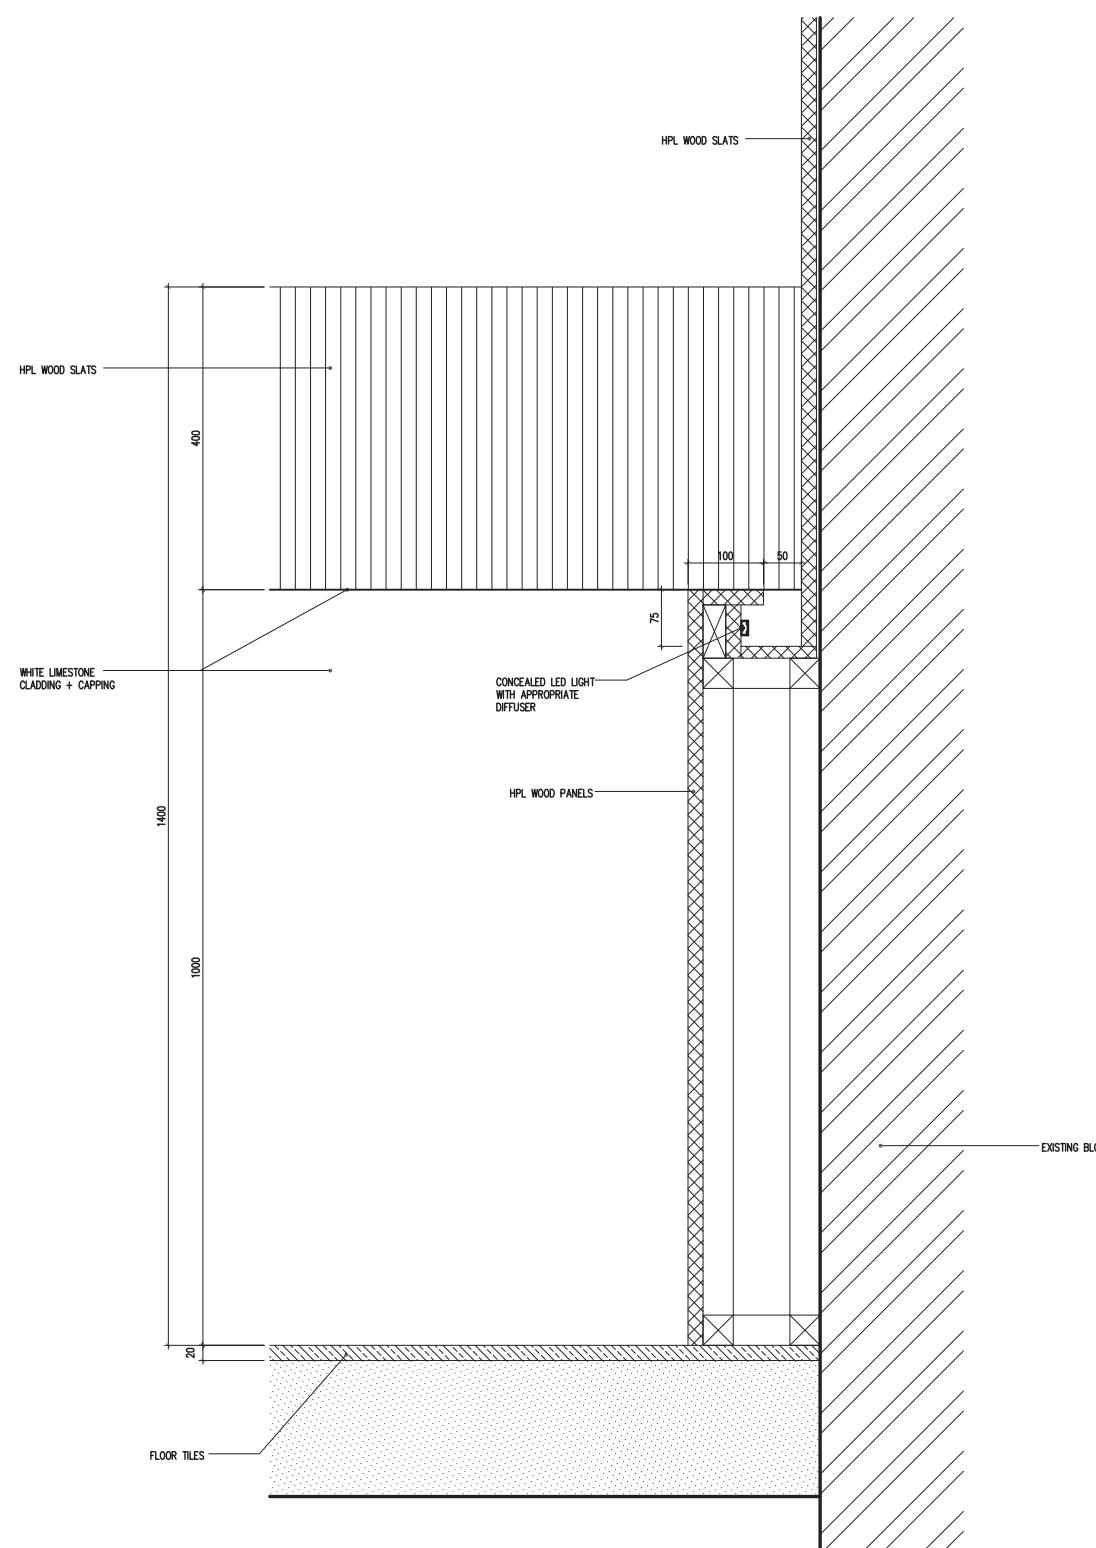

04 SPOT DETAIL  
SCALE 1:5

**Client:** Zach-Aimee  
**Project Title:** Private Villa -Dubai Hills  
**Location:** Dubai, U.A.E.

**Plot Area:** 0000.00 Sqm  
0000.00 SqFt  
**Old Gate Level:** 0.00 = 0.000  
**NEW GATE LEVEL = 0.000**  
Proposed Gate Level is to be 000 mm above existing Asphalt Road Level

**Sheet Contents:**  
TERRACE  
SPOT DETAILS  
3 & 4  
Designed by: Drawn By: Checked By: Issued By:  
ab mp ab ab  
Scale: Sheet Size: Stage: Rev No:  
1:100 A1 Conceptual Stage 0

**Drwg No.** ID-404

3 & 4