


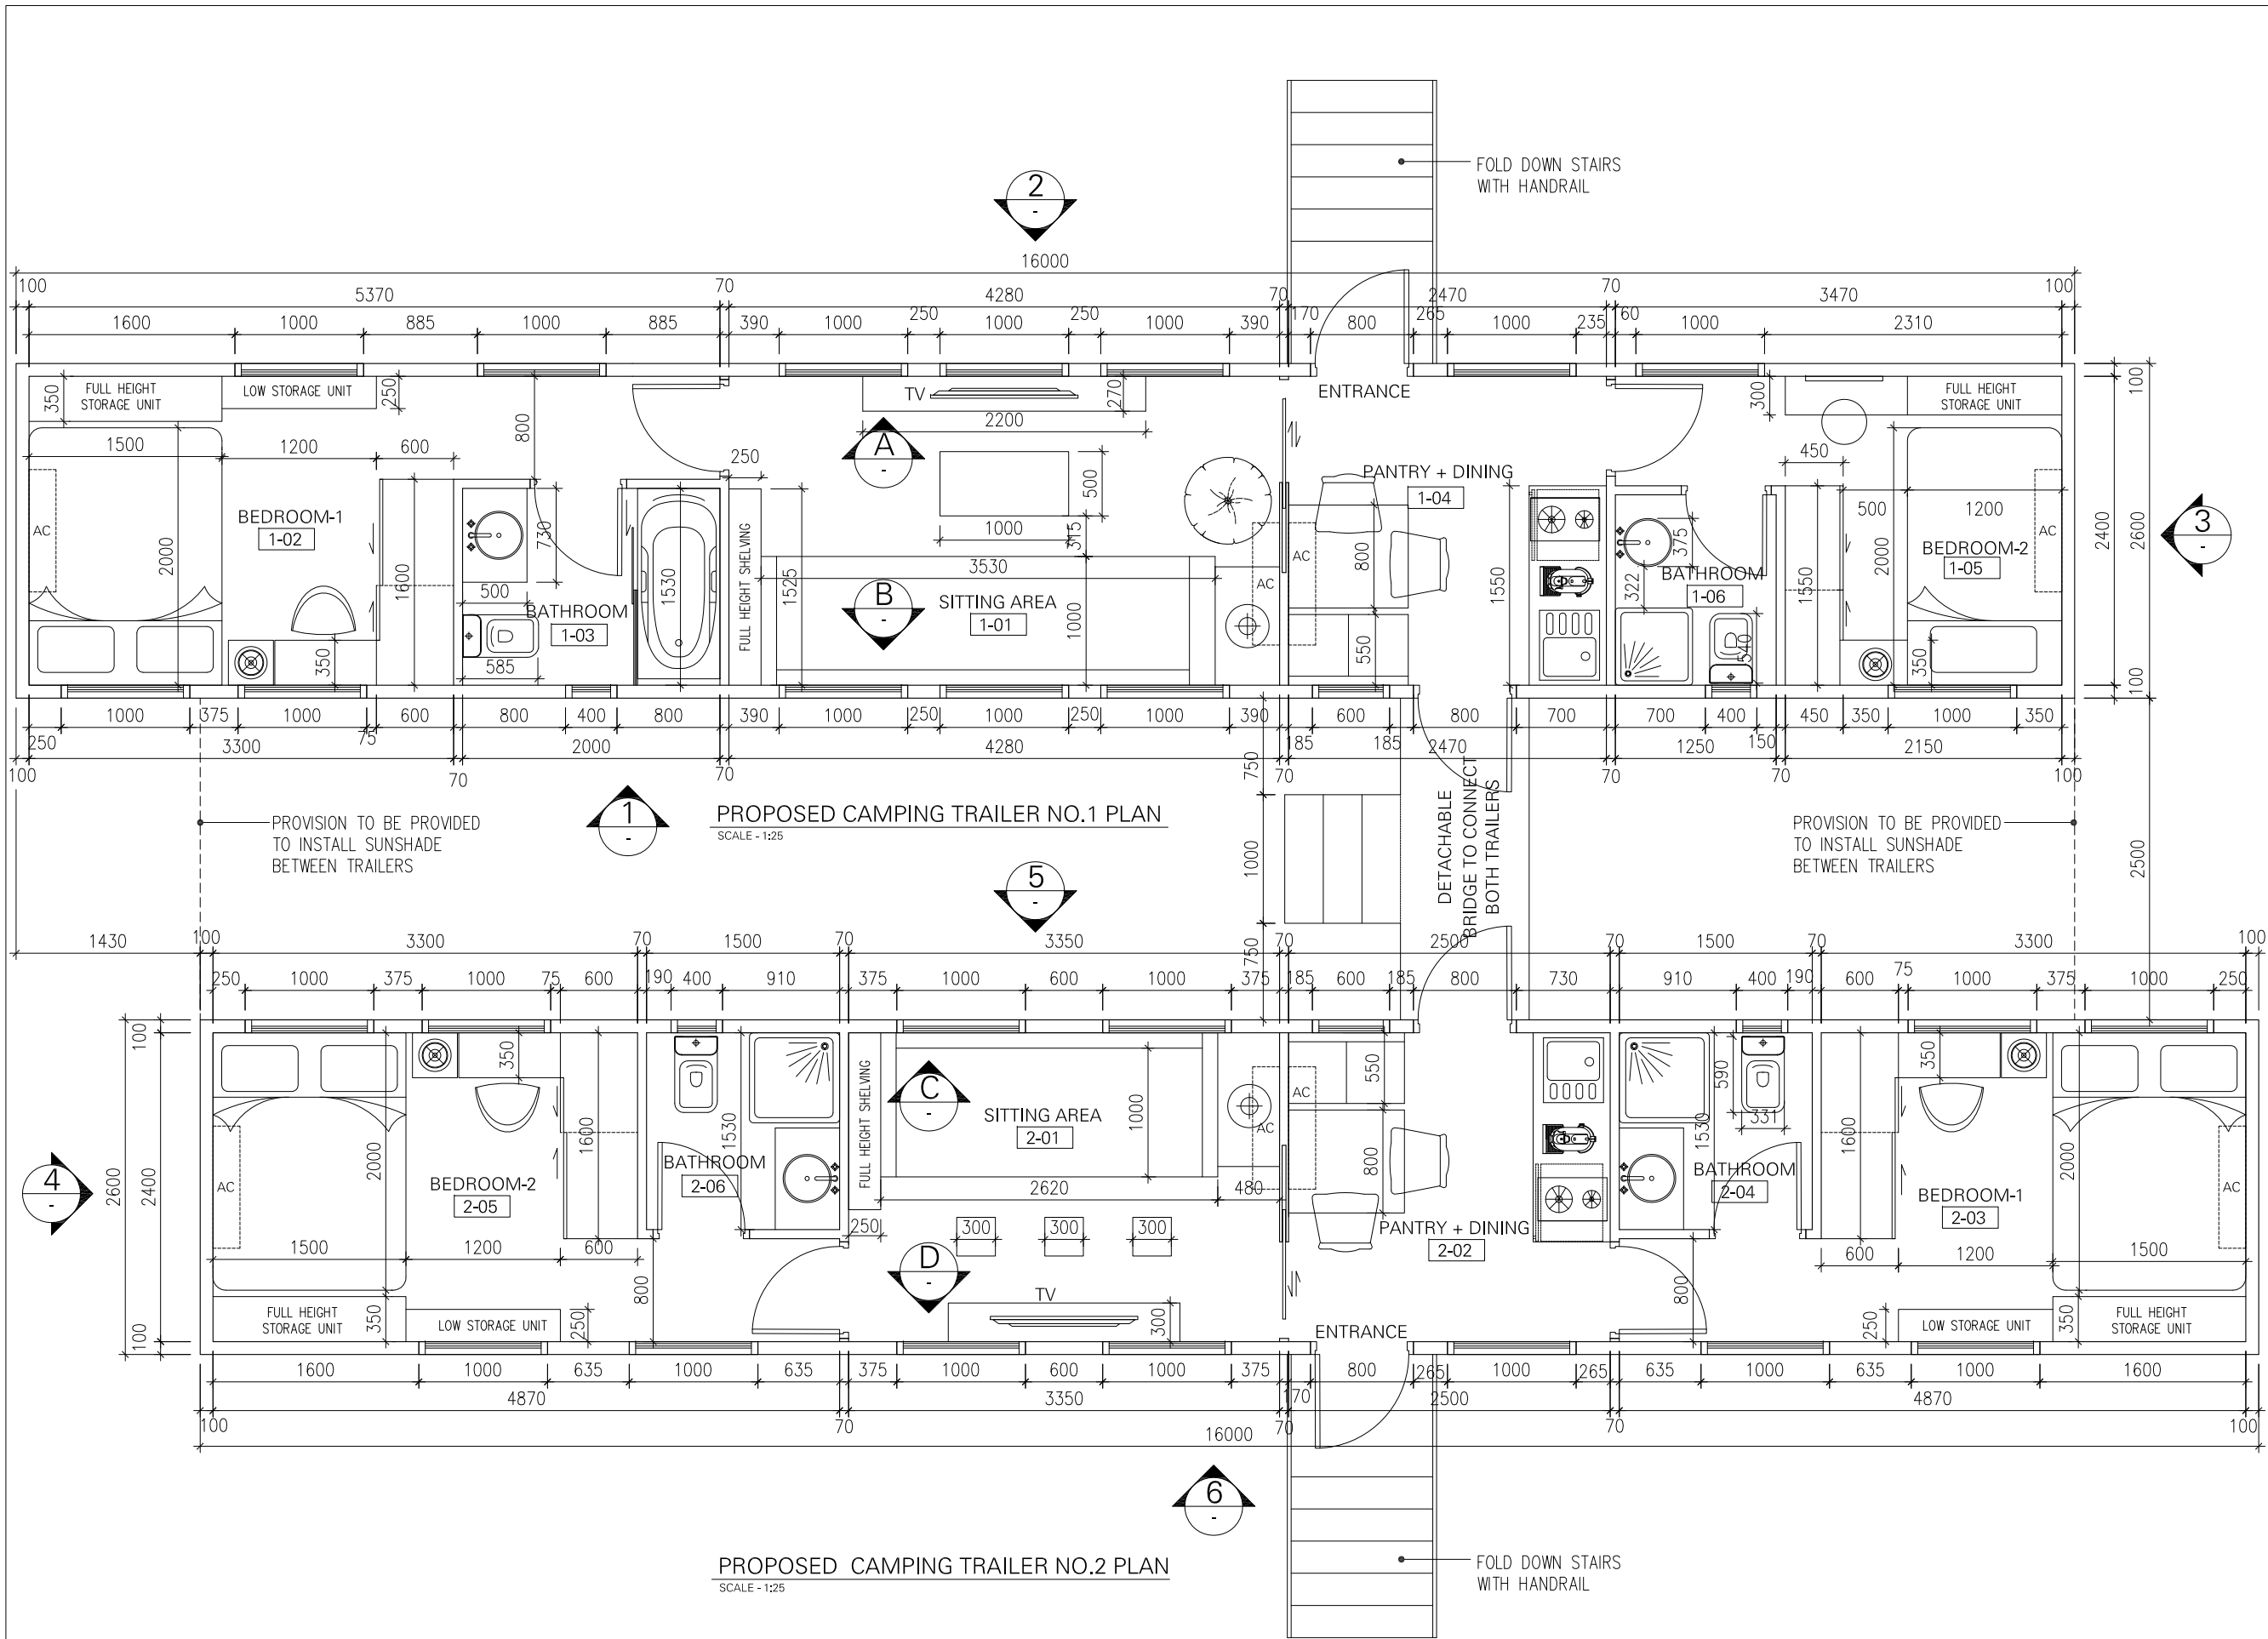

- GENERAL NOTES**
1. This drawing shall be read in conjunction with all other relevant architectural, structural & electrical drawings including those of other consultants.
 2. It is the responsibility of contractors & manufacturers to check all relevant site dimensions prior to the start of construction or manufacture.
 3. All materials and components must be installed on site in accordance with manufacturer's instructions, shop drawings and standard details.
 4. All dimensions are in millimeters unless noted otherwise.
 5. Full working drawings, specifications and samples are to be provided by Contractor/Supplier for approval prior to manufacture.

KEY PLAN

REV.	GENERAL REV.	MP	AM	SM	DATE
F	GENERAL REV.	MP	AM	SM	2023.06.20
E	GENERAL REV.	MP	AM	SM	2023.06.14
D	GENERAL REV.	MP	AM	SM	2023.06.08
C	GENERAL REV.	MP	AM	SM	2023.06.06
B	GENERAL REV.	MP	AM	SM	2023.06.05
A	GENERAL REV.	MP	AM	SM	2023.06.04
X	INITIAL ISSUE	MP	AM	SM	2023.06.29
REV.#	GENERAL NOTES	DRAWN BY	CHECKED BY	APPROVED BY	DATE

PROJECT TITLE: SAF - RIYADH
REFERENCE: SAF01 G


DRAWING TITLE: PROPOSED CAMPING TRAILER PLAN

DRAWING NUMBER: SK-98
REVISION: F


SCALE: 1:25
FORMAT: A1
ADDITIONAL NOTES: DESIGN DEVELOPMENT

SIMA MALAK + ALSSAMOURE DESIGN ASSOCIATES
P.O. Box 15707 - Riyadh 11454 KSA
Tel. 01 441 4963 - Fax. 01 441 3867
simals@simals.com


©SIMA MALAK + ALSSAMOURE DESIGN ASSOCIATES (شركة) 2003
This document including all drawing and text is the property and copyright of SIMA MALAK + ALSSAMOURE DESIGN ASSOCIATES for use solely with respect to this Project and shall not be copied or reproduced by any means except by agreement in writing from SIMA MALAK + ALSSAMOURE DESIGN ASSOCIATES.

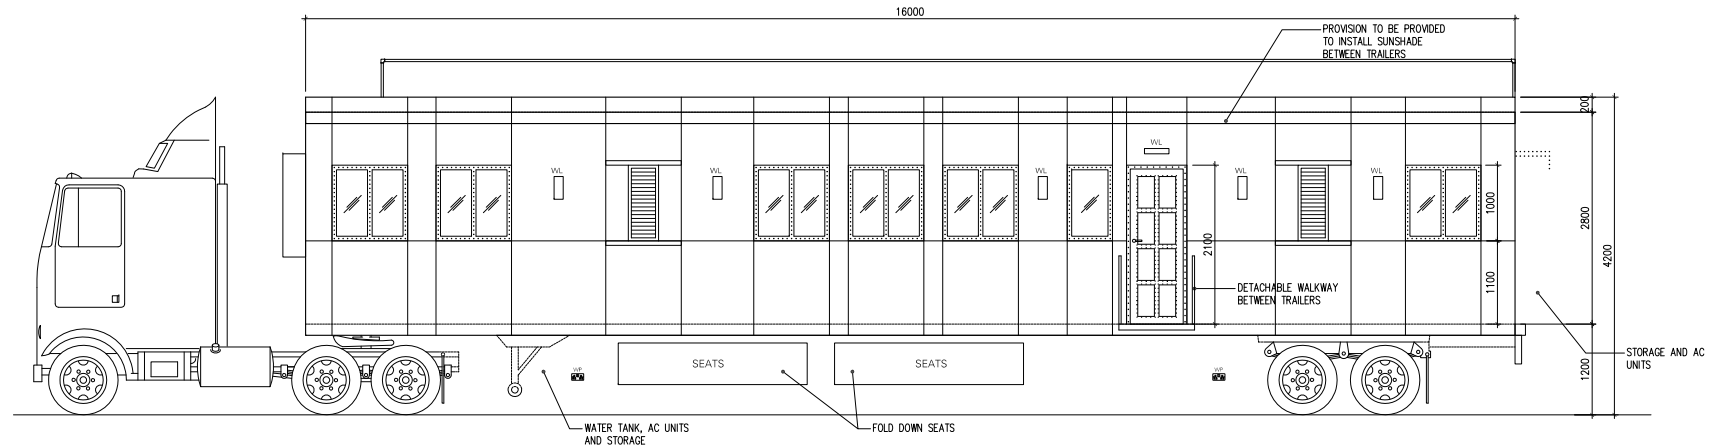


CAMPING TRAILER NO.1 ELEVATION - 01
SCALE - 1:50

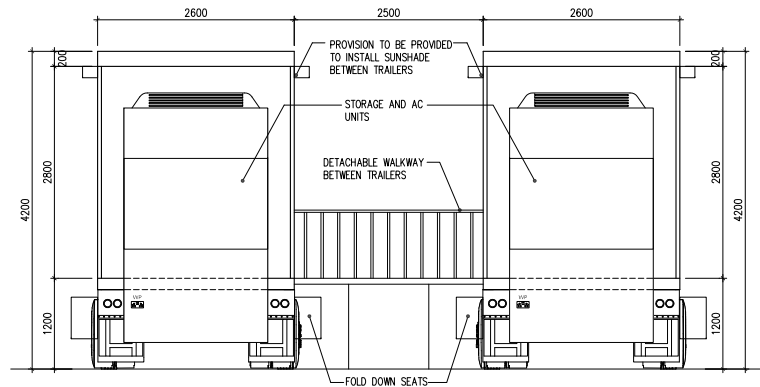


BACK ELEVATION - 03
SCALE - 1:50

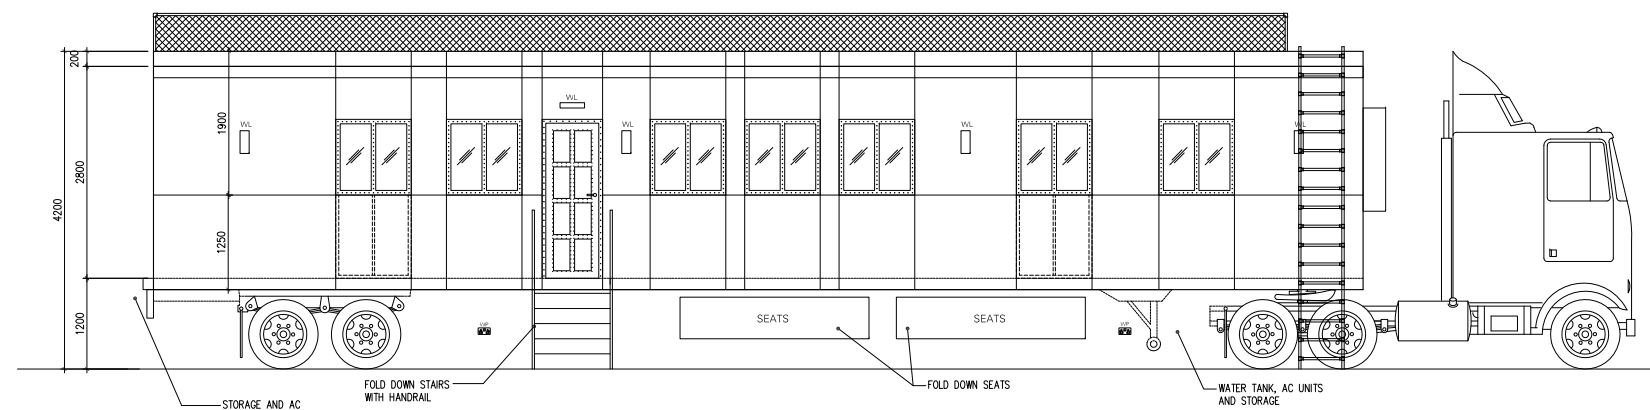


CAMPING TRAILER NO.1 ELEVATION - 02
SCALE - 1:50

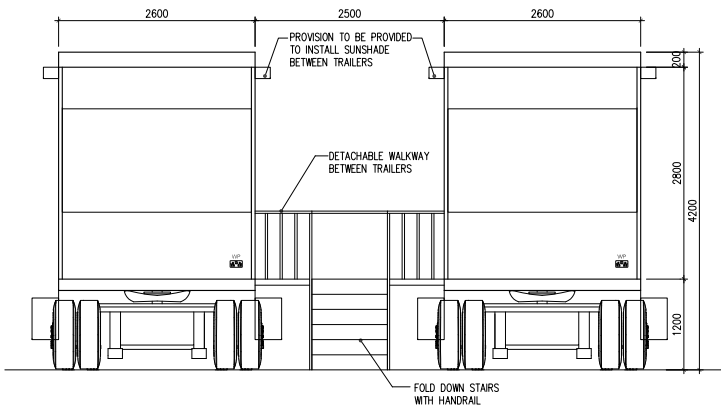

FRONT ELEVATION - 04
SCALE - 1:50

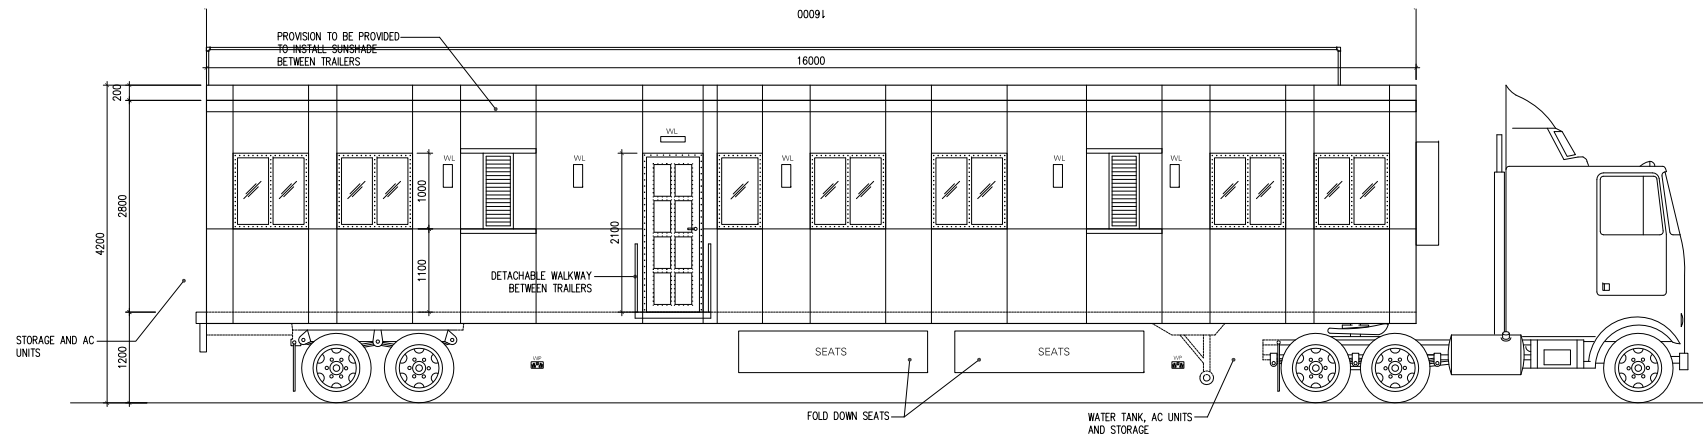

CAMPING TRAILER NO.2 ELEVATION - 05
SCALE - 1:50

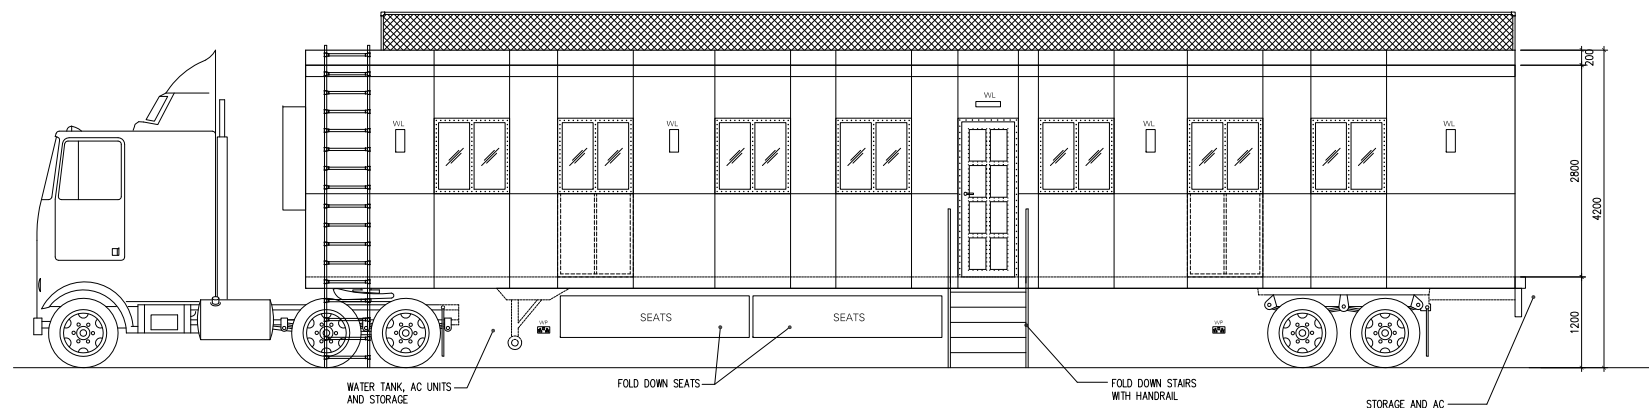

CAMPING TRAILER NO.2 ELEVATION - 06
SCALE - 1:50

GENERAL NOTES

1. This drawing shall be read in conjunction with all other relevant architectural, structural & electrical drawings including those of other consultants.
2. It is the responsibility of contractors & manufacturers to check all relevant site dimensions prior to the start of construction or manufacture.
3. All materials and components must be installed on site in accordance with manufacturer's instructions, shop drawings and standard details.
4. All dimensions are in millimeters unless noted otherwise.
5. Full working drawings, specifications and samples are to be provided by Contractor/Supplier for approval prior to manufacture.


KEY PLAN

B	GENERAL REV.	MP	AM	SM	2023.06.20
A	GENERAL REV.	MP	AM	SM	2023.06.15
X	INITIAL ISSUE	MP	AM	SM	2023.06.08
REV.#	GENERAL NOTES	DRAWN BY	CHECKED BY	APPROVED BY	DATE
PROJECT TITLE					REFERENCE
SAF - RIYADH					SAF01 G


DRAWING TITLE		PROPOSED CAMPING TRAILER ELEVATIONS	
DRAWING NUMBER		REVISION	
SK-102		B	
SCALE	FORMAT	ADDITIONAL NOTES	DESIGN DEVELOPMENT
1:50	A1		

**SIMA MALAK + ALSSAMOURE
DESIGN ASSOCIATES**
P.O. Box 15707 - Riyadh 11454 KSA
Tel. 01 441 4963 - Fax. 01 441 3867
simals@simals.com


©SIMA MALAK + ALSSAMOURE DESIGN ASSOCIATES (شركة) 2003
This document including all drawing and text is the property and
copyright of SIMA MALAK + ALSSAMOURE DESIGN ASSOCIATES for
use solely with respect to this Project and shall not be copied or
reproduced by any means except by agreement in writing from
SIMA MALAK + ALSSAMOURE DESIGN ASSOCIATES.

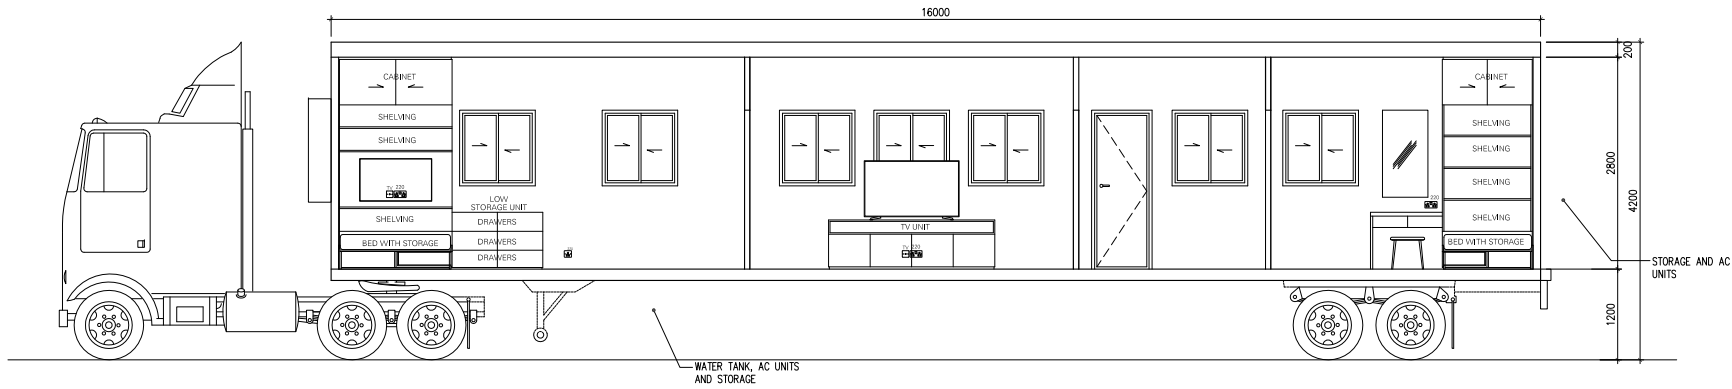


CAMPING TRAILER NO.1 - SECTION - A
SCALE - 1:50

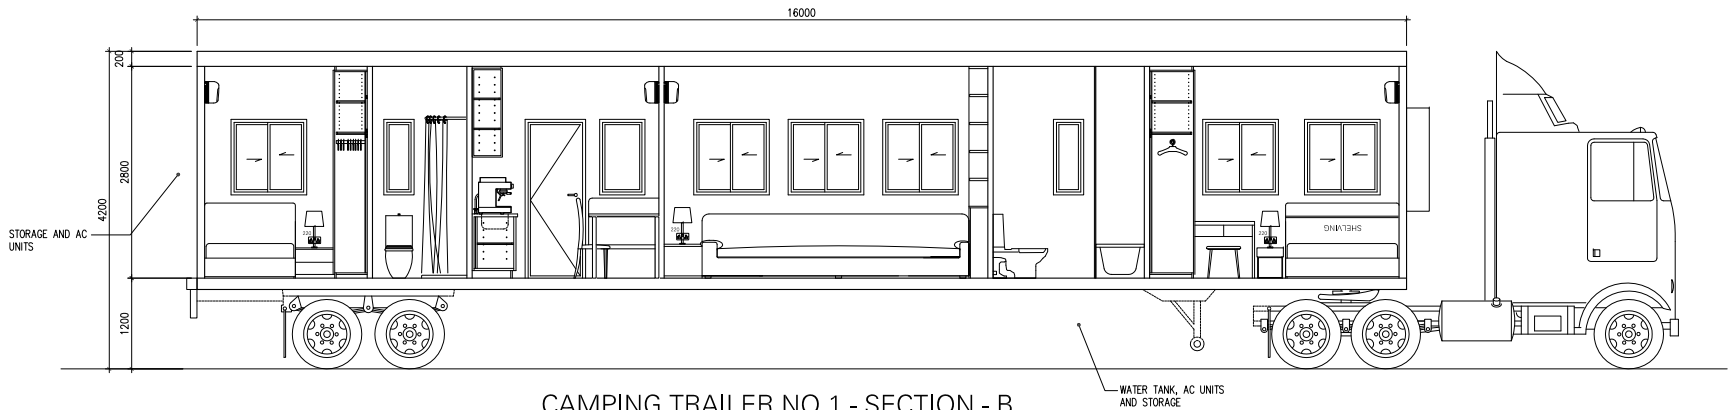

CAMPING TRAILER NO.1 - SECTION - B
SCALE - 1:50

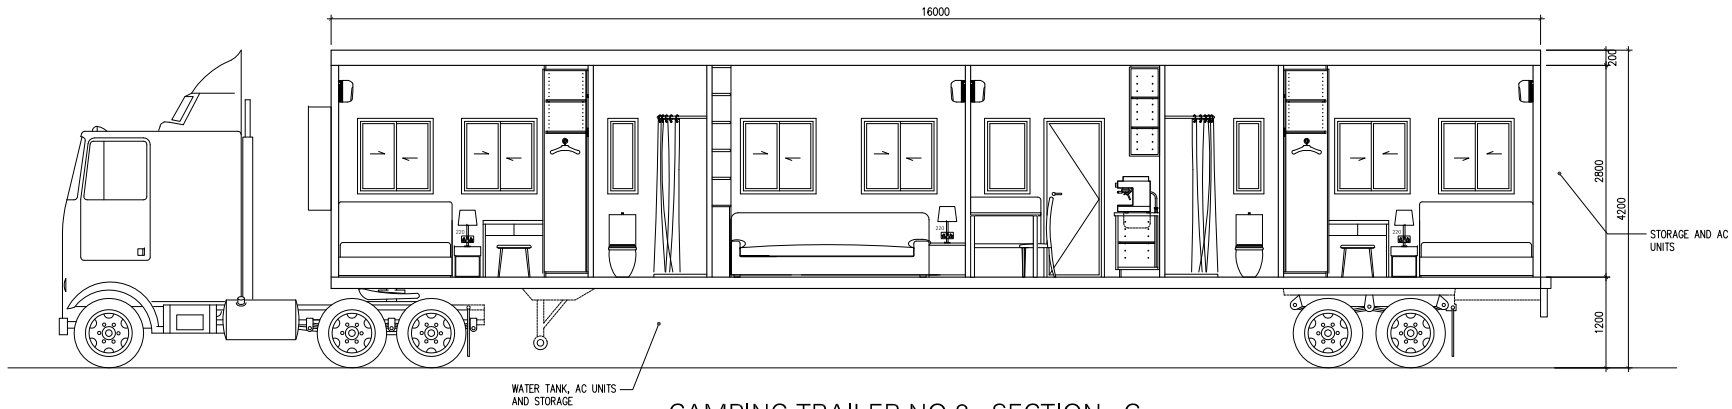

CAMPING TRAILER NO.2 - SECTION - C
SCALE - 1:50

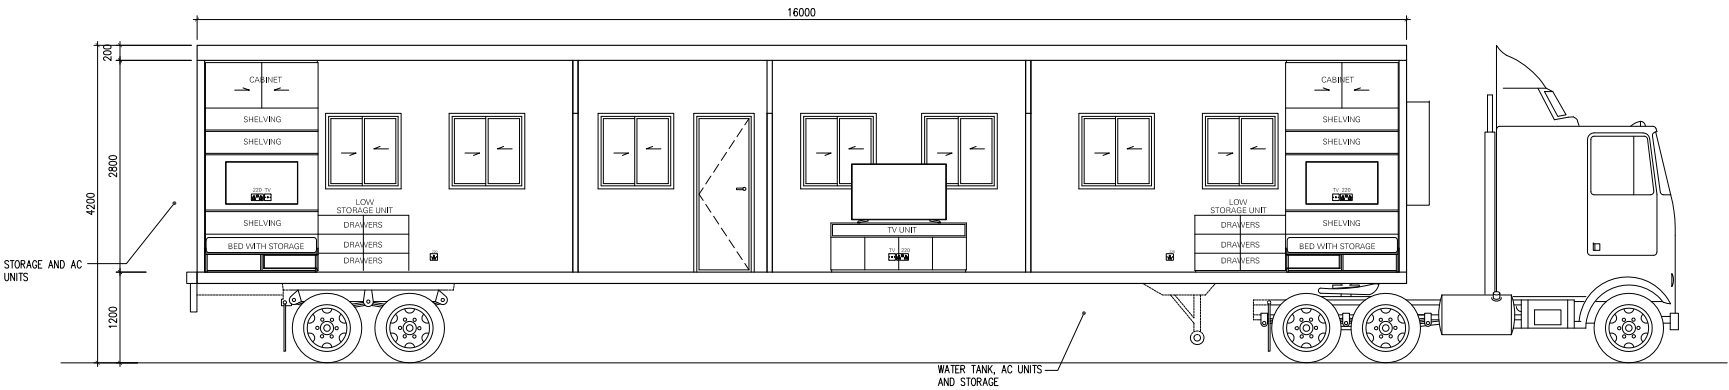

CAMPING TRAILER NO.2 - SECTION - D
SCALE - 1:50

GENERAL NOTES

1. This drawing shall be read in conjunction with all other relevant architectural, structural & electrical drawings including those of other consultants.
2. It is the responsibility of contractors & manufacturers to check all relevant site dimensions prior to the start of construction or manufacture.
3. All materials and components must be installed on site in accordance with manufacturer's instructions, shop drawings and standard details.
4. All dimensions are in millimeters unless noted otherwise.
5. Full working drawings, specifications and samples are to be provided by Contractor/Supplier for approval prior to manufacture.

KEY PLAN

INITIAL ISSUE	MP	AM	SM	2023.06.21
REV.# GENERAL NOTES	DRAWN BY	CHECKED BY	APPROVED BY	DATE
PROJECT TITLE				REFERENCE
SAF - RIYADH				SAF01
				G

DRAWING TITLE			
PROPOSED CAMPING TRAILER SECTIONS			
DRAWING NUMBER			REVISION
SK-103			-
SCALE	FORMAT	ADDITIONAL NOTES	DESIGN DEVELOPMENT
1:50	A1		

**SIMA MALAK + ALSSAMOURE
DESIGN ASSOCIATES**
P.O. Box 15707 - Riyadh 11454 KSA
Tel. 01 441 4963 - Fax. 01 441 3867
simals@simals.com

©SIMA MALAK + ALSSAMOURE DESIGN ASSOCIATES (شركة) 2003
This document including all drawing and text is the property and
copyright of SIMA MALAK + ALSSAMOURE DESIGN ASSOCIATES for
use solely with respect to this Project and shall not be copied or
reproduced by any means except by agreement in writing from
SIMA MALAK + ALSSAMOURE DESIGN ASSOCIATES.

TRAILER NO-01

ROOMS	FLOOR		WALLS		CEILING
SITTING AREA (1-01)	10.32 Sqm	PARQUET	28.15 Sqm	WOOD CLADDING	10.27 Sqm
BEDROOM-1 (1-02)	9.62 Sqm	PARQUET	36.36 Sqm	WOOD CLADDING	9.57 Sqm
PANTRY+DINING (1-04)	6.16 Sqm	PARQUET	19.06 Sqm	WOOD CLADDING	6.00 Sqm
BEDROOM-2 (1-05)	6.33 Sqm	PARQUET	27.83 Sqm	WOOD CLADDING	6.28 Sqm
BATHROOM (1-03)	3.07 Sqm	CERAMIC	17.80 Sqm	CERAMIC	3.06 Sqm
BATHROOM (1-06)	1.86 Sqm	CERAMIC	13.41 Sqm	CERAMIC	1.85 Sqm

TOTAL PARQUET FLOORING = 65.32 SQM

TOTAL WOOD CLADDED WALLS = 230.94 SQM


TOTAL CERAMIC FLOORING = 9.53 SQM

TOTAL WALL TILES = 60.85 SQM

TOTAL CEILING AREA = 73.95 SQM


TRAILER NO-02

ROOMS	FLOOR		WALLS		CEILING
SITTING AREA (2-01)	8.10 Sqm	PARQUET	25.05 Sqm	WOOD CLADDING	8.04 Sqm
BEDROOM-1 (2-03)	9.23 Sqm	PARQUET	33.60 Sqm	WOOD CLADDING	9.17 Sqm
PANTRY+DINING (2-02)	6.33 Sqm	PARQUET	27.83 Sqm	WOOD CLADDING	6.00 Sqm
BEDROOM-2 (2-05)	9.23 Sqm	PARQUET	33.60 Sqm	WOOD CLADDING	9.17 Sqm
BATHROOM (1-03)	2.30 Sqm	CERAMIC	14.82 Sqm	CERAMIC	2.29 Sqm
BATHROOM (1-06)	2.30 Sqm	CERAMIC	14.82 Sqm	CERAMIC	2.29 Sqm

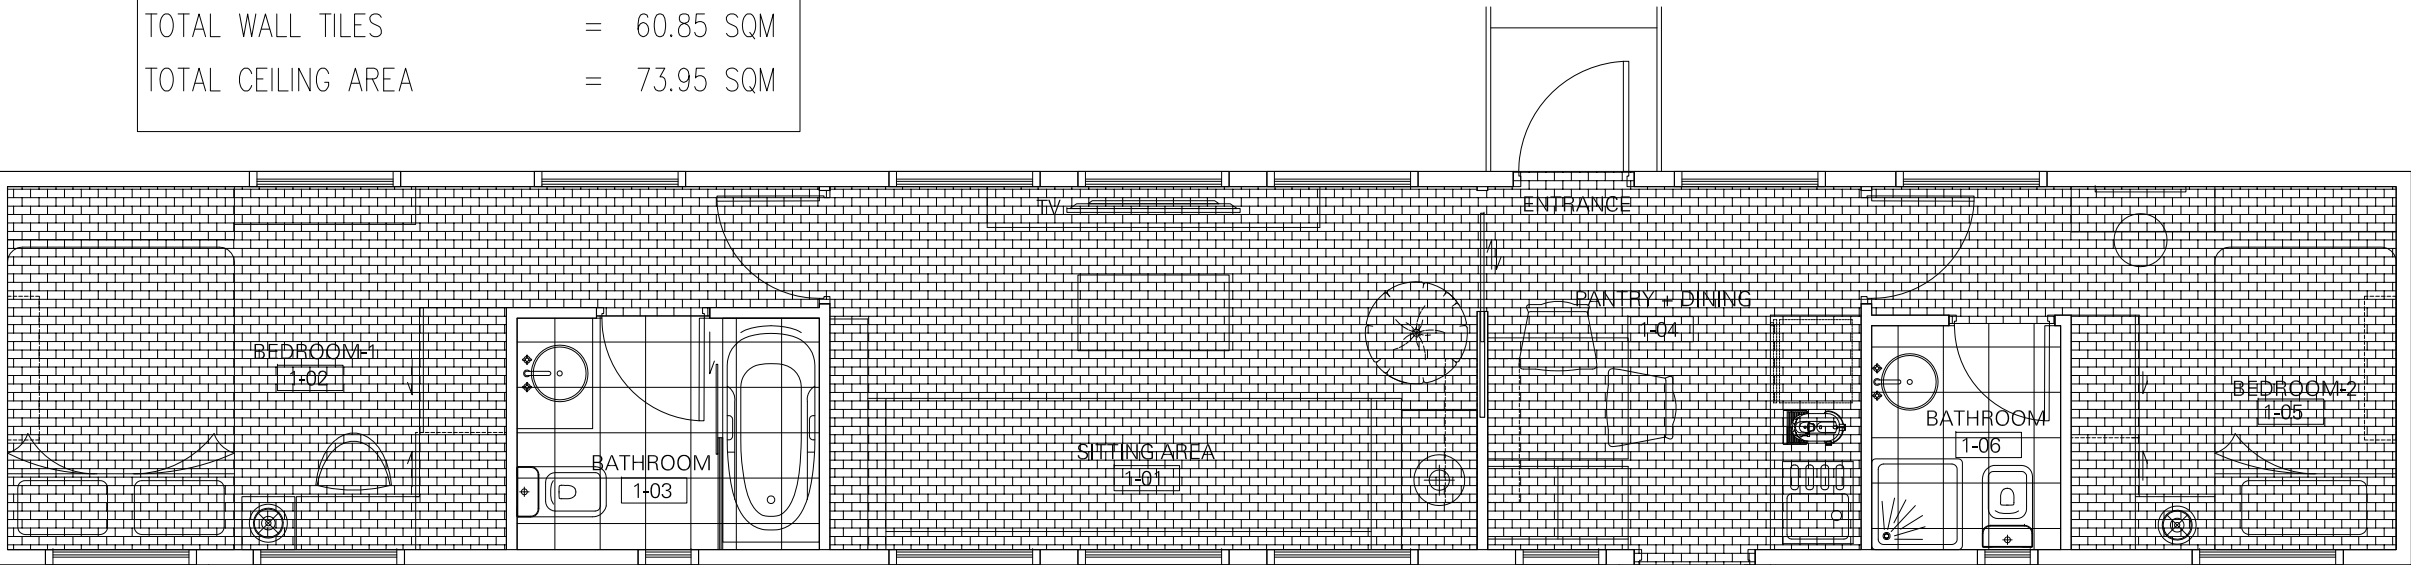

CAMPING TRAILER NO.1 FLOORING LAYOUT

SCALE - 1:25

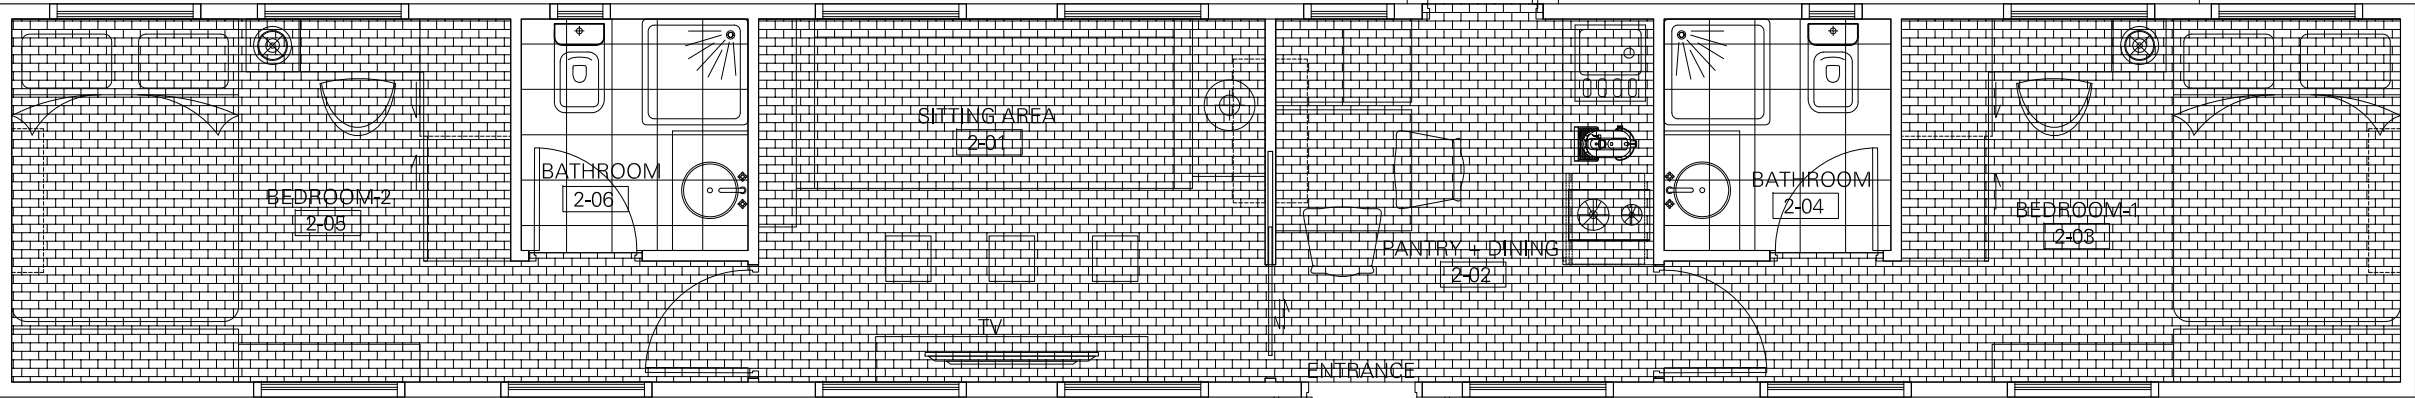

CAMPING TRAILER NO.2 FLOORING LAYOUT

SCALE - 1:25

GENERAL NOTES

1. This drawing shall be read in conjunction with all other relevant architectural, structural & electrical drawings including those of other consultants.
2. It is the responsibility of contractors & manufacturers to check all relevant site dimensions prior to the start of construction or manufacture.
3. All materials and components must be installed on site in accordance with manufacturer's instructions , shop drawings and standard details.
4. All dimensions are in millimeters unless noted otherwise.
5. Full working drawings, specifications and samples are to be provided by Contractor/Supplier for approval prior to manufacture.

KEY PLAN

✓	INITIAL ISSUE	MP	AM	SM	2023.12.10
REV.#	GENERAL NOTES	DRAWN BY	CHECKED BY	APPROVED BY	DATE
PROJECT TITLE					REFERENCE
SAF - RIYADH					SAF01 G

DRAWING TITLE		REVISION	
PROPOSED CAMPING TRAILER FLOORING LAYOUT + AREA CALC.			
DRAWING NUMBER			
SK-111			
SCALE	FORMAT	ADDITIONAL NOTES	DESIGN DEVELOPMENT
1:25	A1		

SIMA MALAK + ALSSAMOURE
DESIGN ASSOCIATES

P.O. Box 15707 - Riyadh 11454 KSA
Tel. 01 441 4963 - Fax. 01 441 3867
simals@simals.com

©SIMA MALAK + ALSSAMOURE DESIGN ASSOCIATES (شركة) 2003
This document including all drawing and text is the property and copyright of SIMA MALAK + ALSSAMOURE DESIGN ASSOCIATES for use solely with respect to this Project and shall not be copied or reproduced by any means except by agreement in writing from SIMA MALAK + ALSSAMOURE DESIGN ASSOCIATES.