



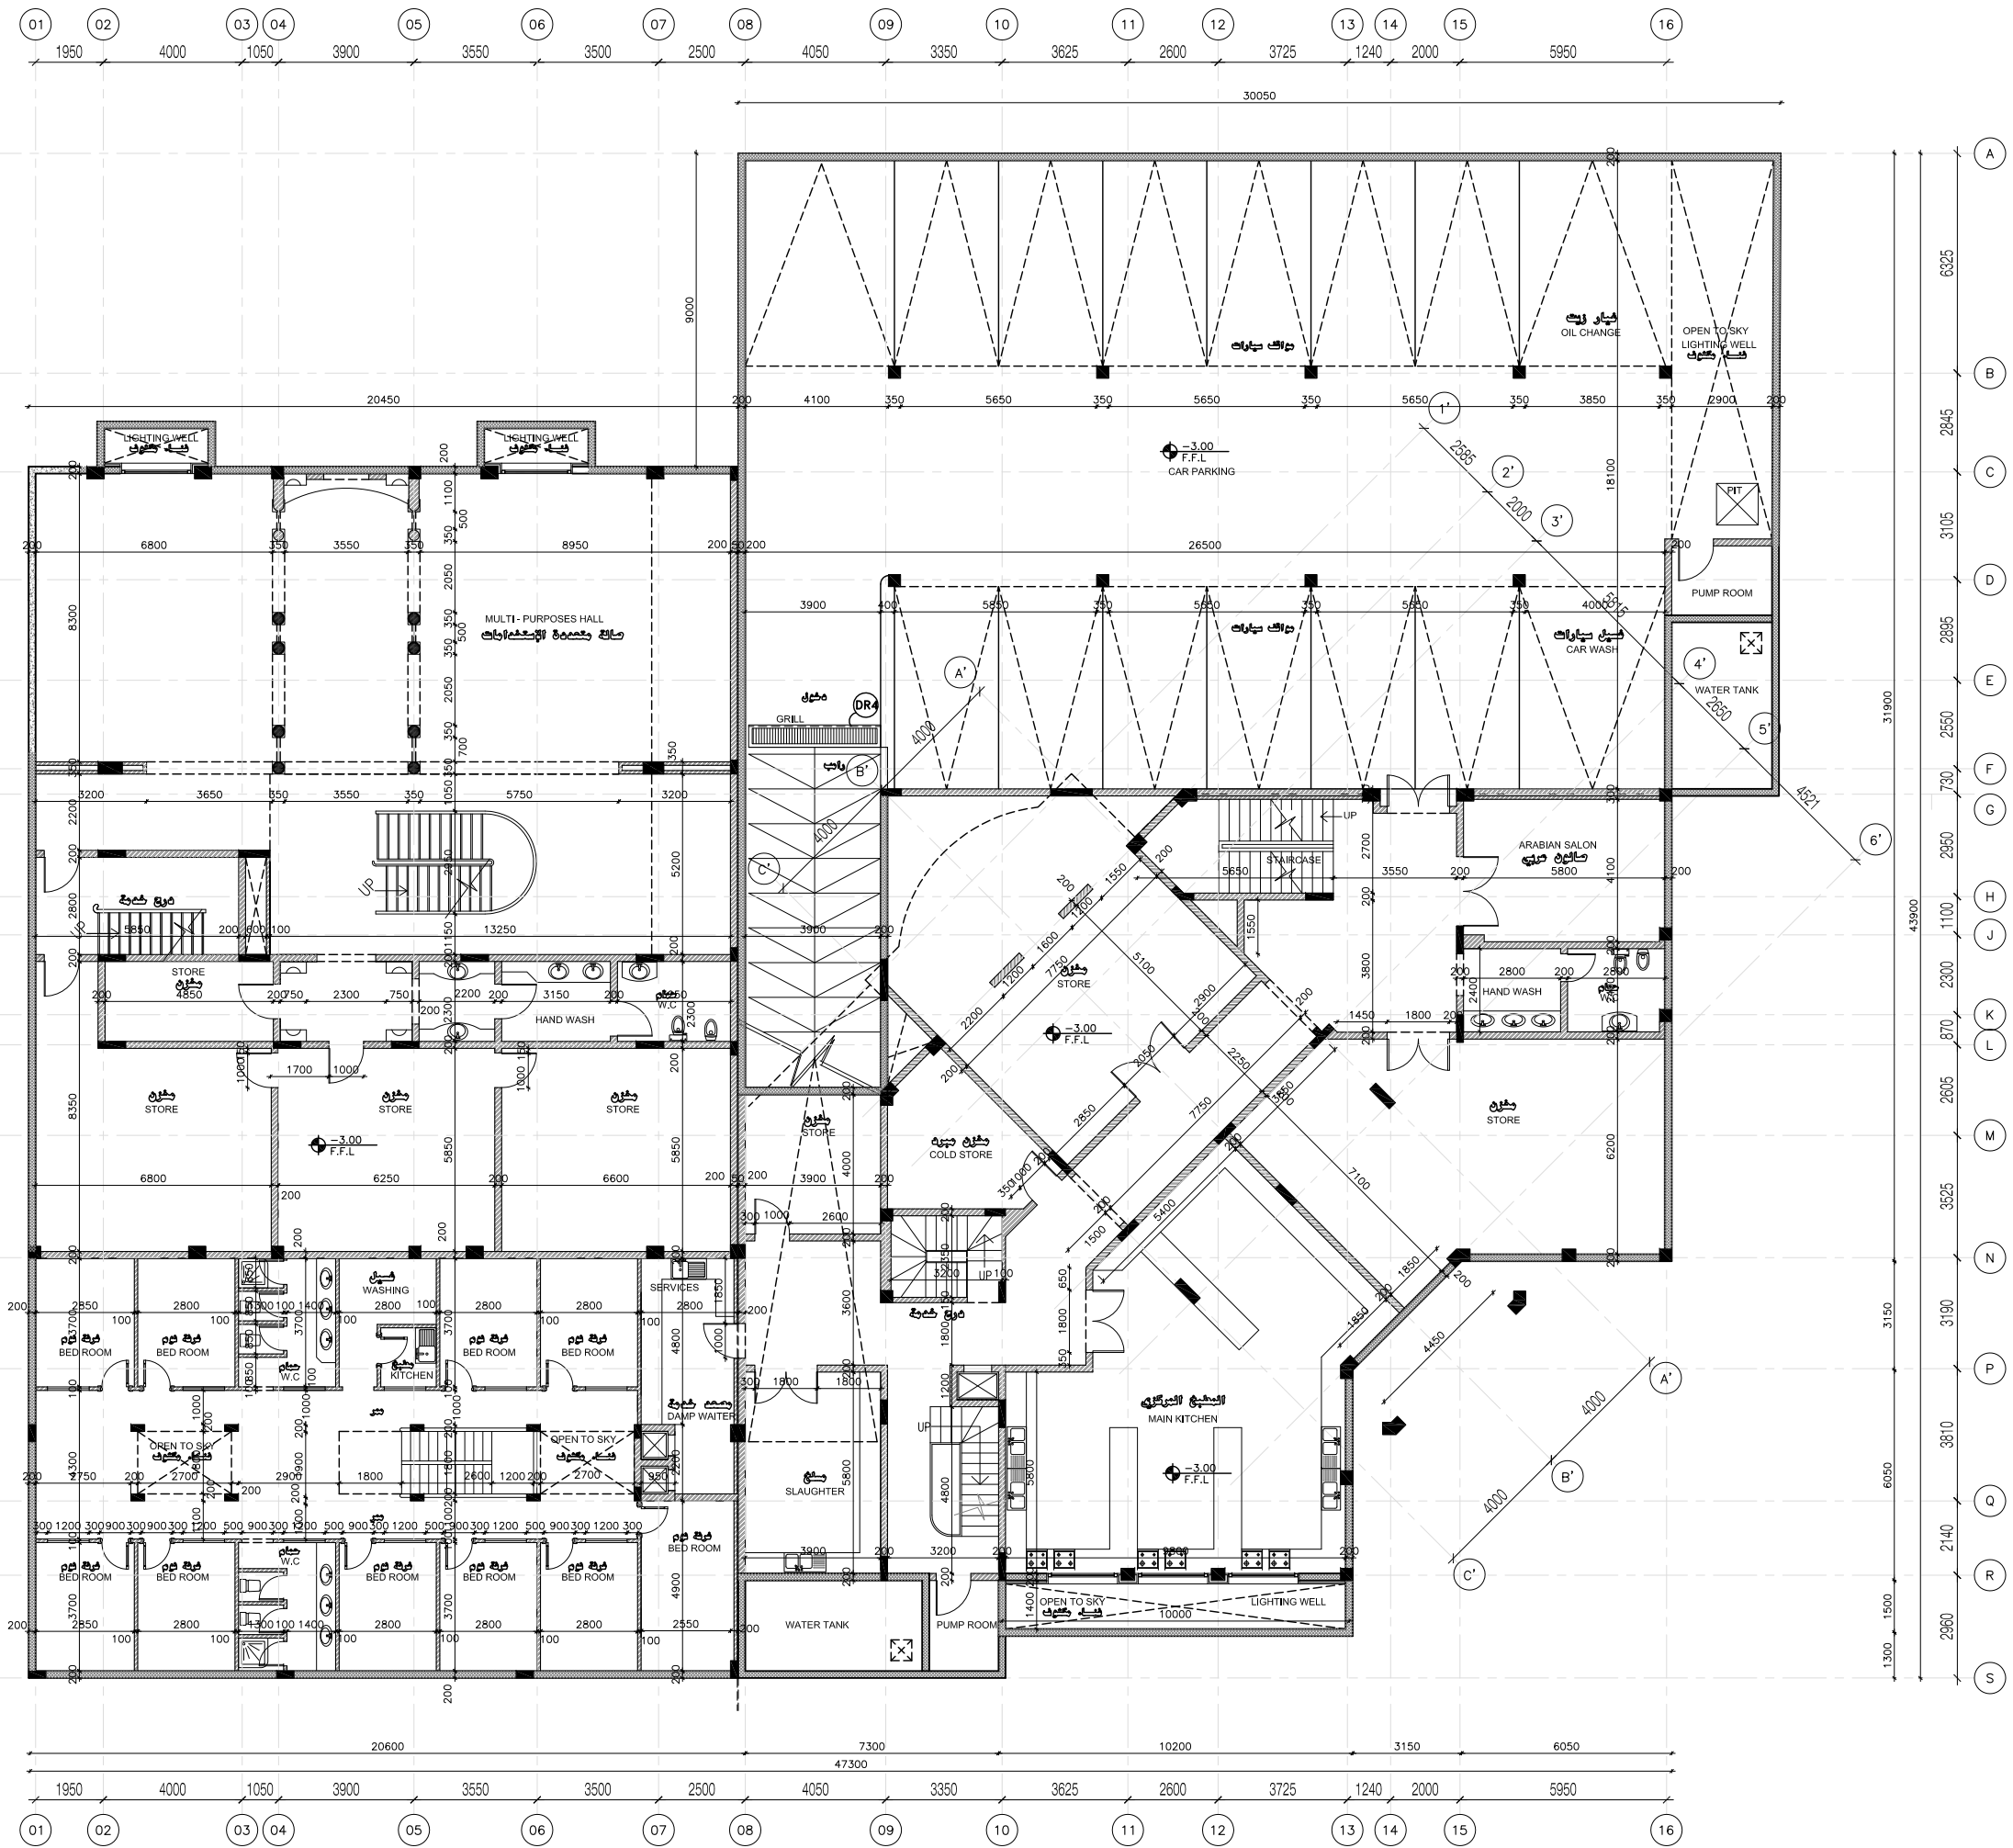


REV.	DATE	BY	DESCRIPTION
KEY PLAN			
CONSULTANT			
النسب للإستشارات الهندسية Proportions Consulting Engineering Tel: 2792277, Fax: 2797722 P.O.Box 75453, Riyadh-11578			
PROJECT			
PRIVATE HOUSING COMPLEX AL NAKHEEL / RIYADH - SAUDI ARABIA			
OWNER			
SHEET TITLE			
ARCHITECTURAL BASEMENT FLOOR PLAN			
TENDER DOCUMENTS			
PROJECT NO. :	P0521	STAGE :	WORKING DRAWINGS
DESIGNED BY :	Proportion Group	DRAWN BY :	CAD
DATE :	JAN. 2008	SCALE :	1:100M
A020001 ARCHITECTURAL			REVISION 0

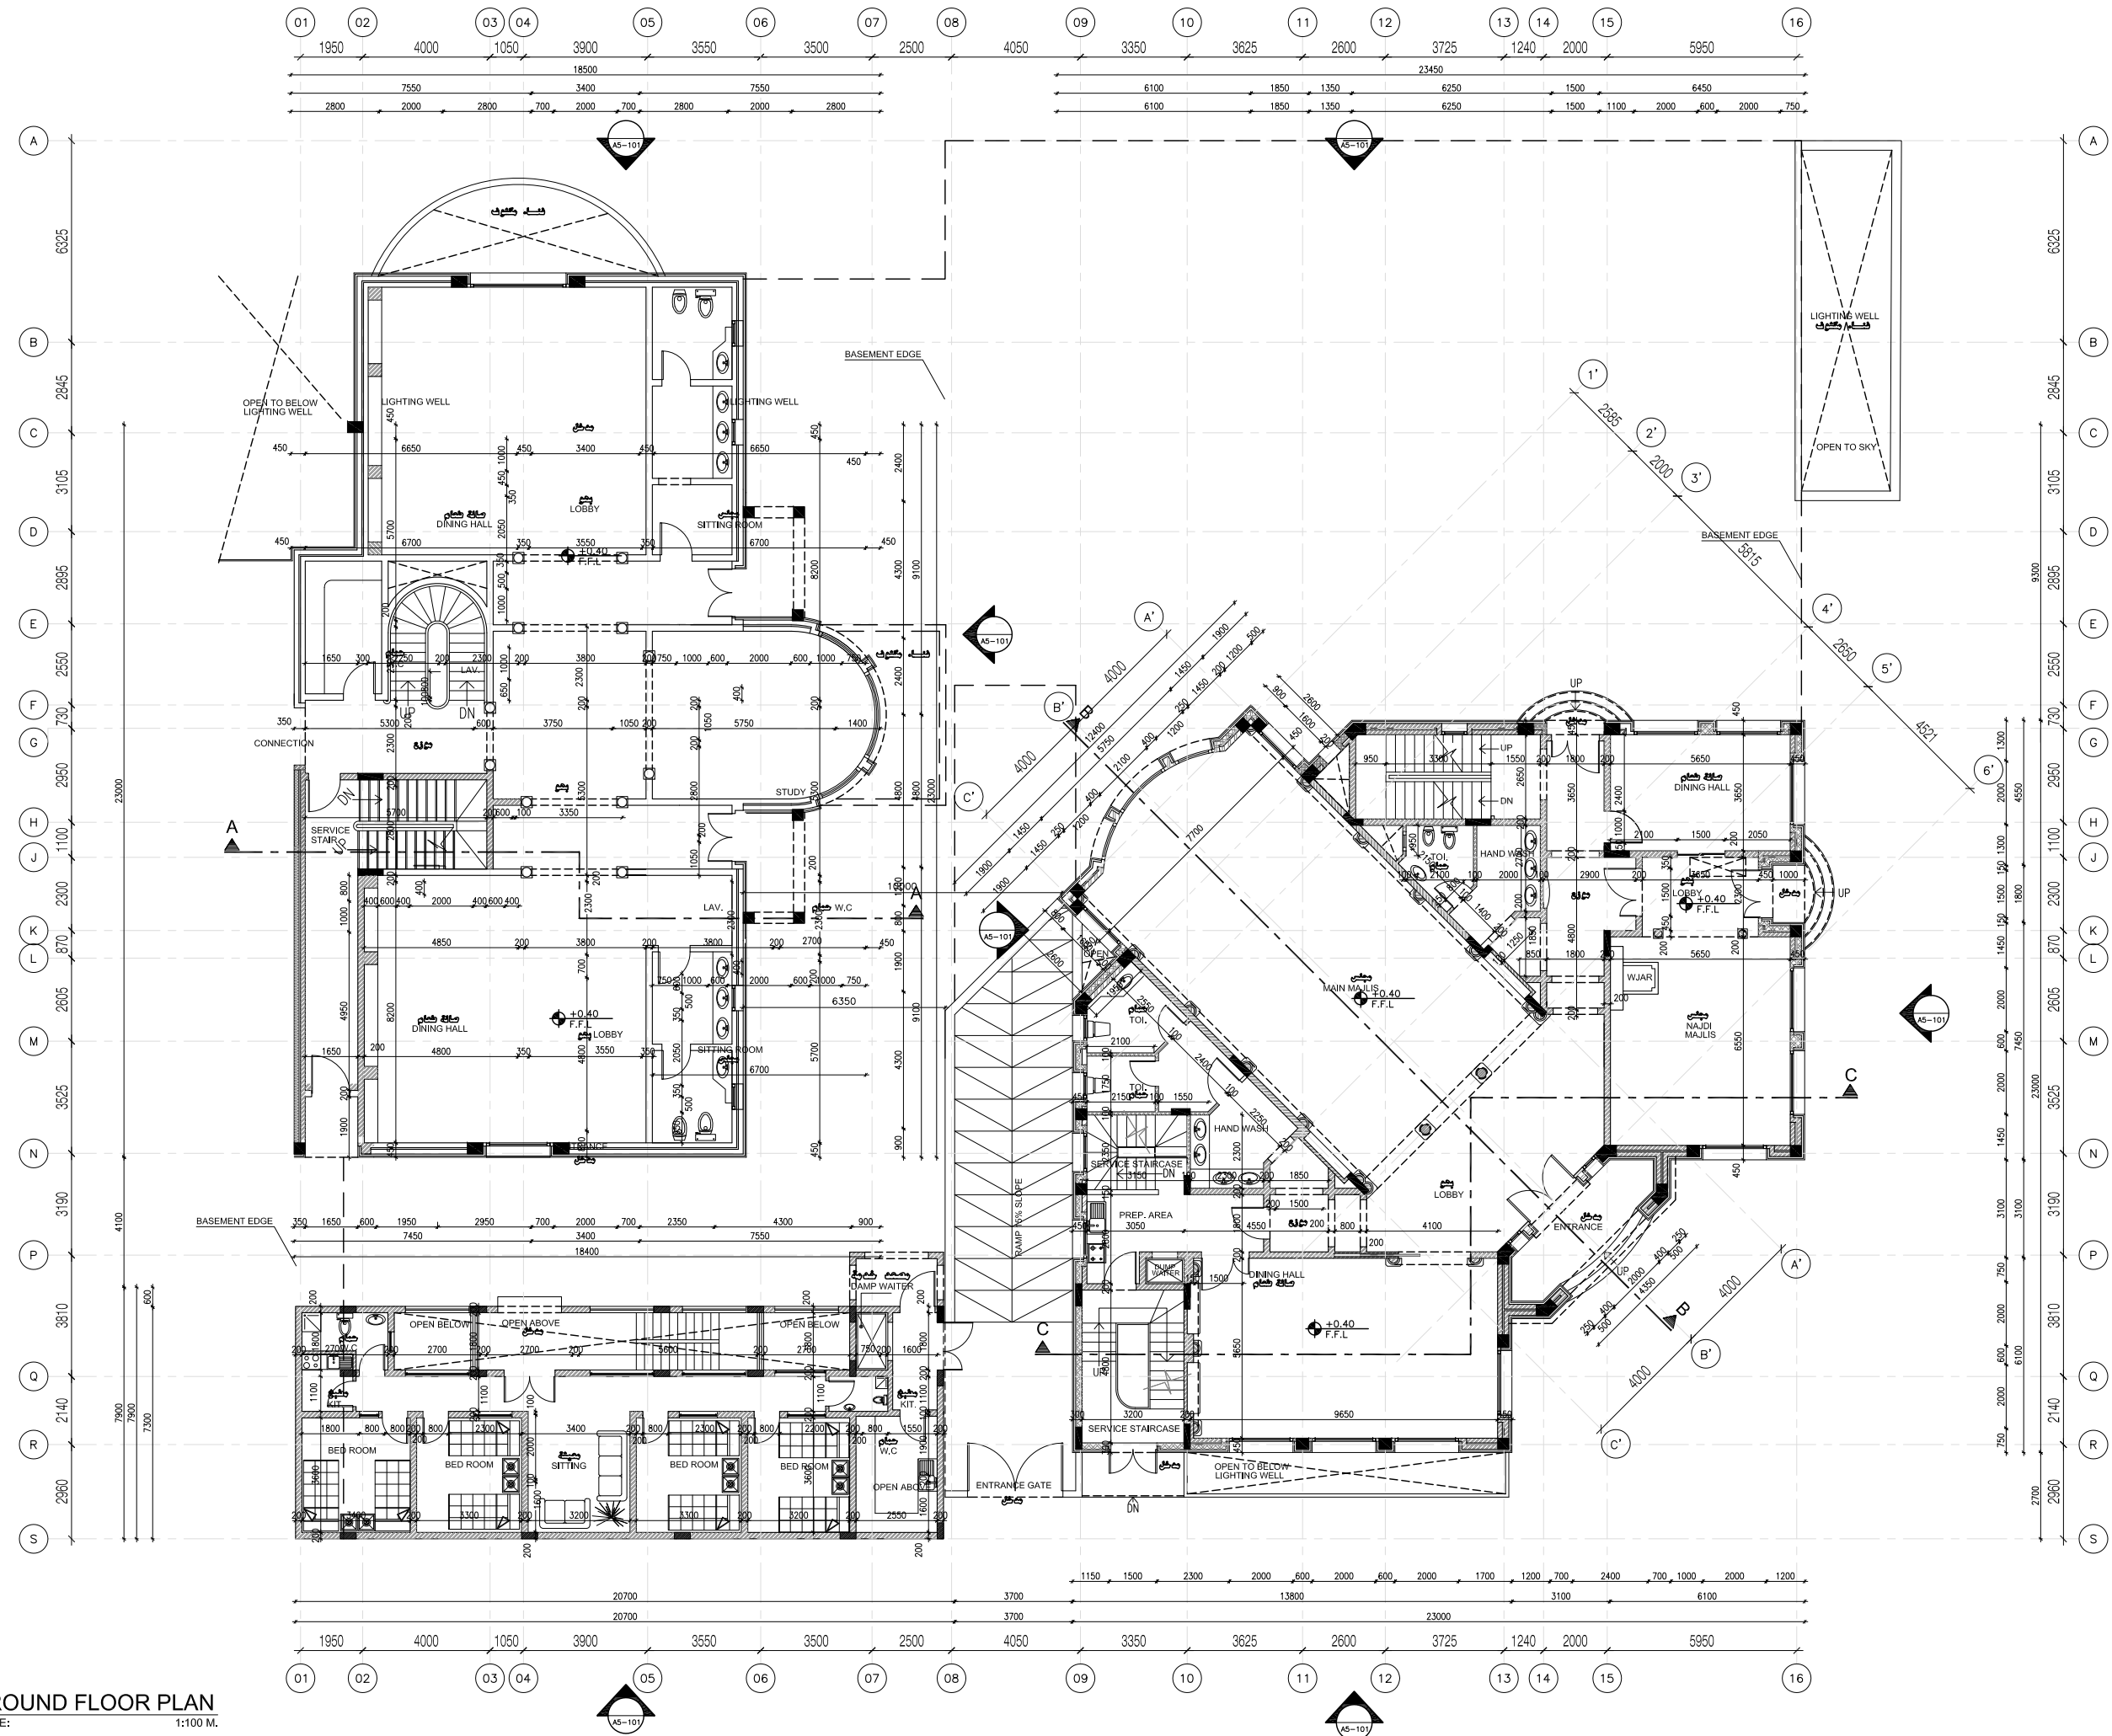


REV.	DATE	BY	DESCRIPTION
KEY PLAN			
CONSULTANT			
 النسب الاستشارات الهندسية Proportions Consulting Engineering Tel: 2792277, Fax: 2797722 P.O.Box 75453, Riyadh-11578			
PROJECT			
PRIVATE HOUSING COMPLEX AL NAKHEEL / RIYADH - SAUDI ARABIA			
OWNER			
SHEET TITLE			
ARCHITECTURAL GROUND FLOOR PLAN			
TENDER DOCUMENTS			
PROJECT NO. :	P0521	STAGE :	WORKING DRAWINGS
DESIGNED BY :	Proportion Group	DRAWN BY :	CAD
DATE :	JAN. 2006	SCALE :	1:100M
A020101 ARCHITECTURAL			REVISION 0



REV.	DATE	BY	DESCRIPTION
KEY PLAN			
CONSULTANT			
 النسب الاستشارات الهندسية Proportions Consulting Engineering Tel: 2792277, Fax: 2797722 P.O.Box 75453, Riyadh-11578			
PROJECT			
PRIVATE HOUSING COMPLEX AL NAKHEEL / RIYADH - SAUDI ARABIA			
OWNER			
SHEET TITLE			
ARCHITECTURAL FIRST FLOOR PLAN			
TENDER DOCUMENTS			
PROJECT NO. :	P0521	STAGE :	WORKING DRAWINGS
DESIGNED BY :	Proportion Group	DRAWN BY :	CAD
DATE :	JAN. 2008	SCALE :	1:100M
A020201 ARCHITECTURAL			REVISION 0

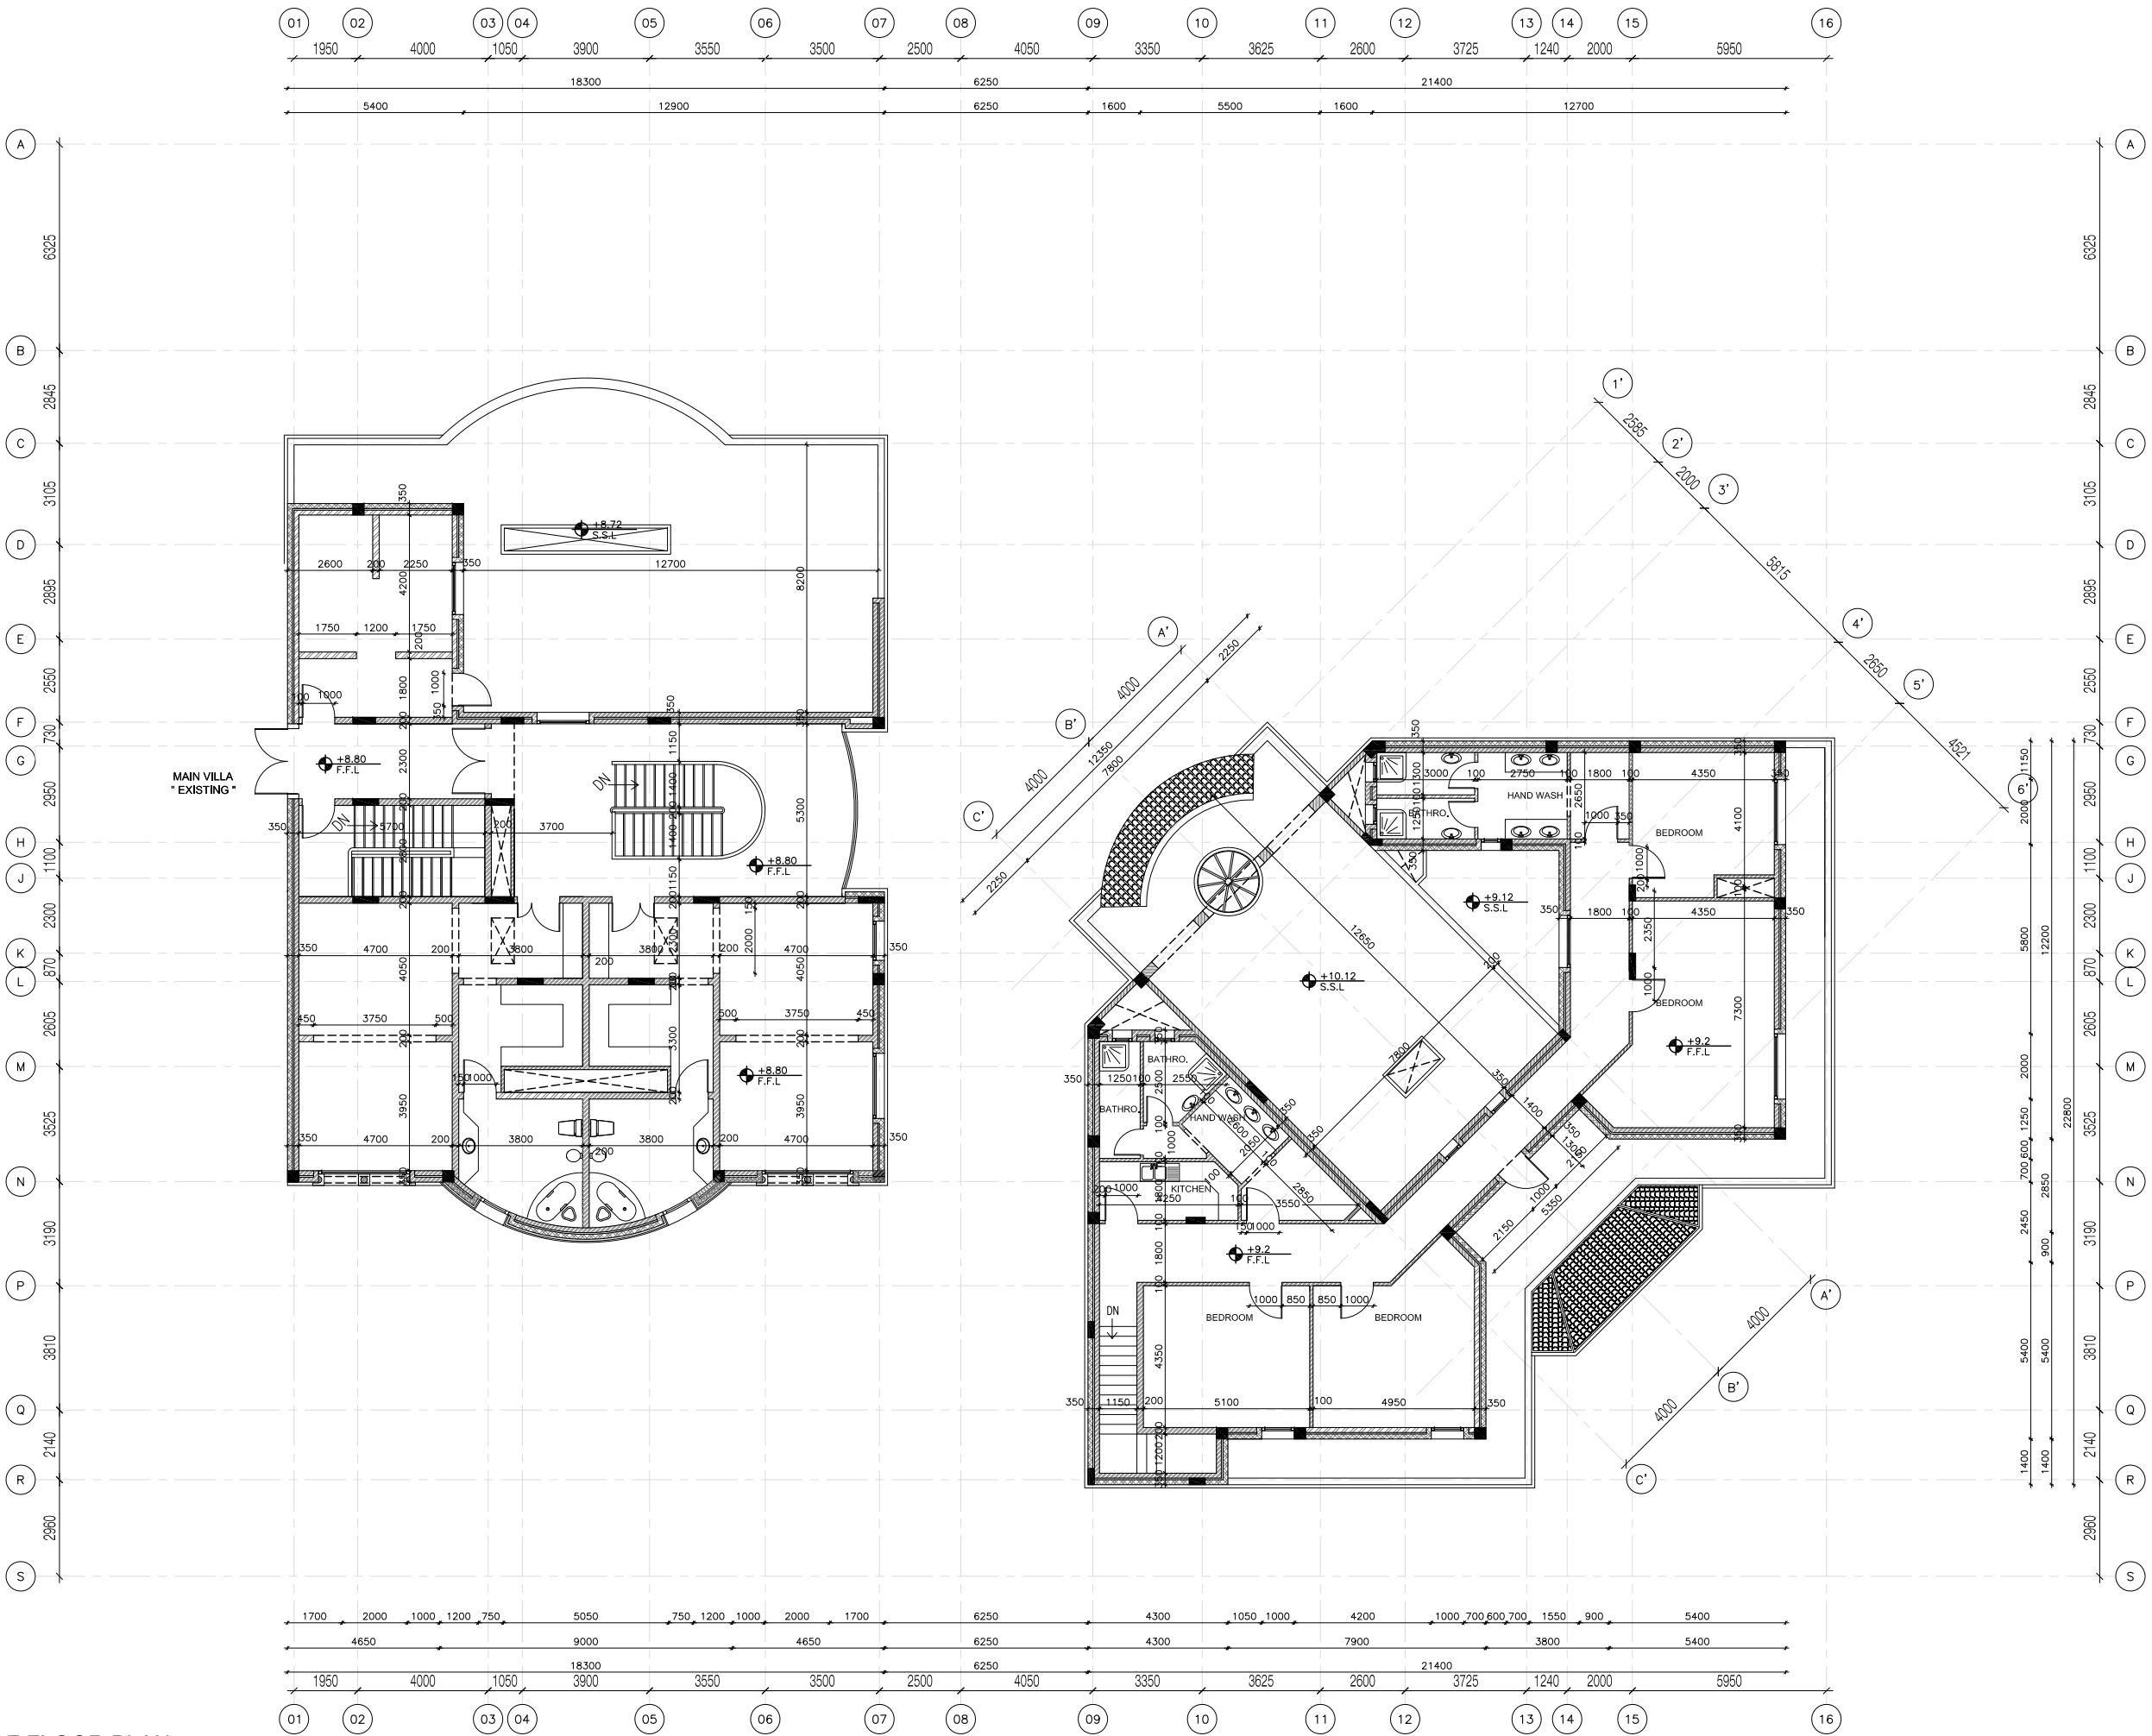

REV.	DATE	BY	DESCRIPTION		
KEY PLAN					
CONSULTANT					
 النسب للإستشارات الهندسية Proportions Consulting Engineering Tel: 2792277, Fax: 2797722 P.O.Box 75453, Riyadh-11578					
PROJECT					
PRIVATE HOUSING COMPLEX AL NAKHEEL / RIYADH - SAUDI ARABIA					
OWNER					
SHEET TITLE					
ARCHITECTURAL ROOF FLOOR PLAN					
TENDER DOCUMENTS					
PROJECT NO. :	P0521		STAGE :	WORKING DRAWING	
DESIGNED BY :	Proportion Group		DRAWN BY :	CAD	
DATE :	JAN. 2008		SCALE :	1:100M	
A020301 ARCHITECTURAL					REVISION 0

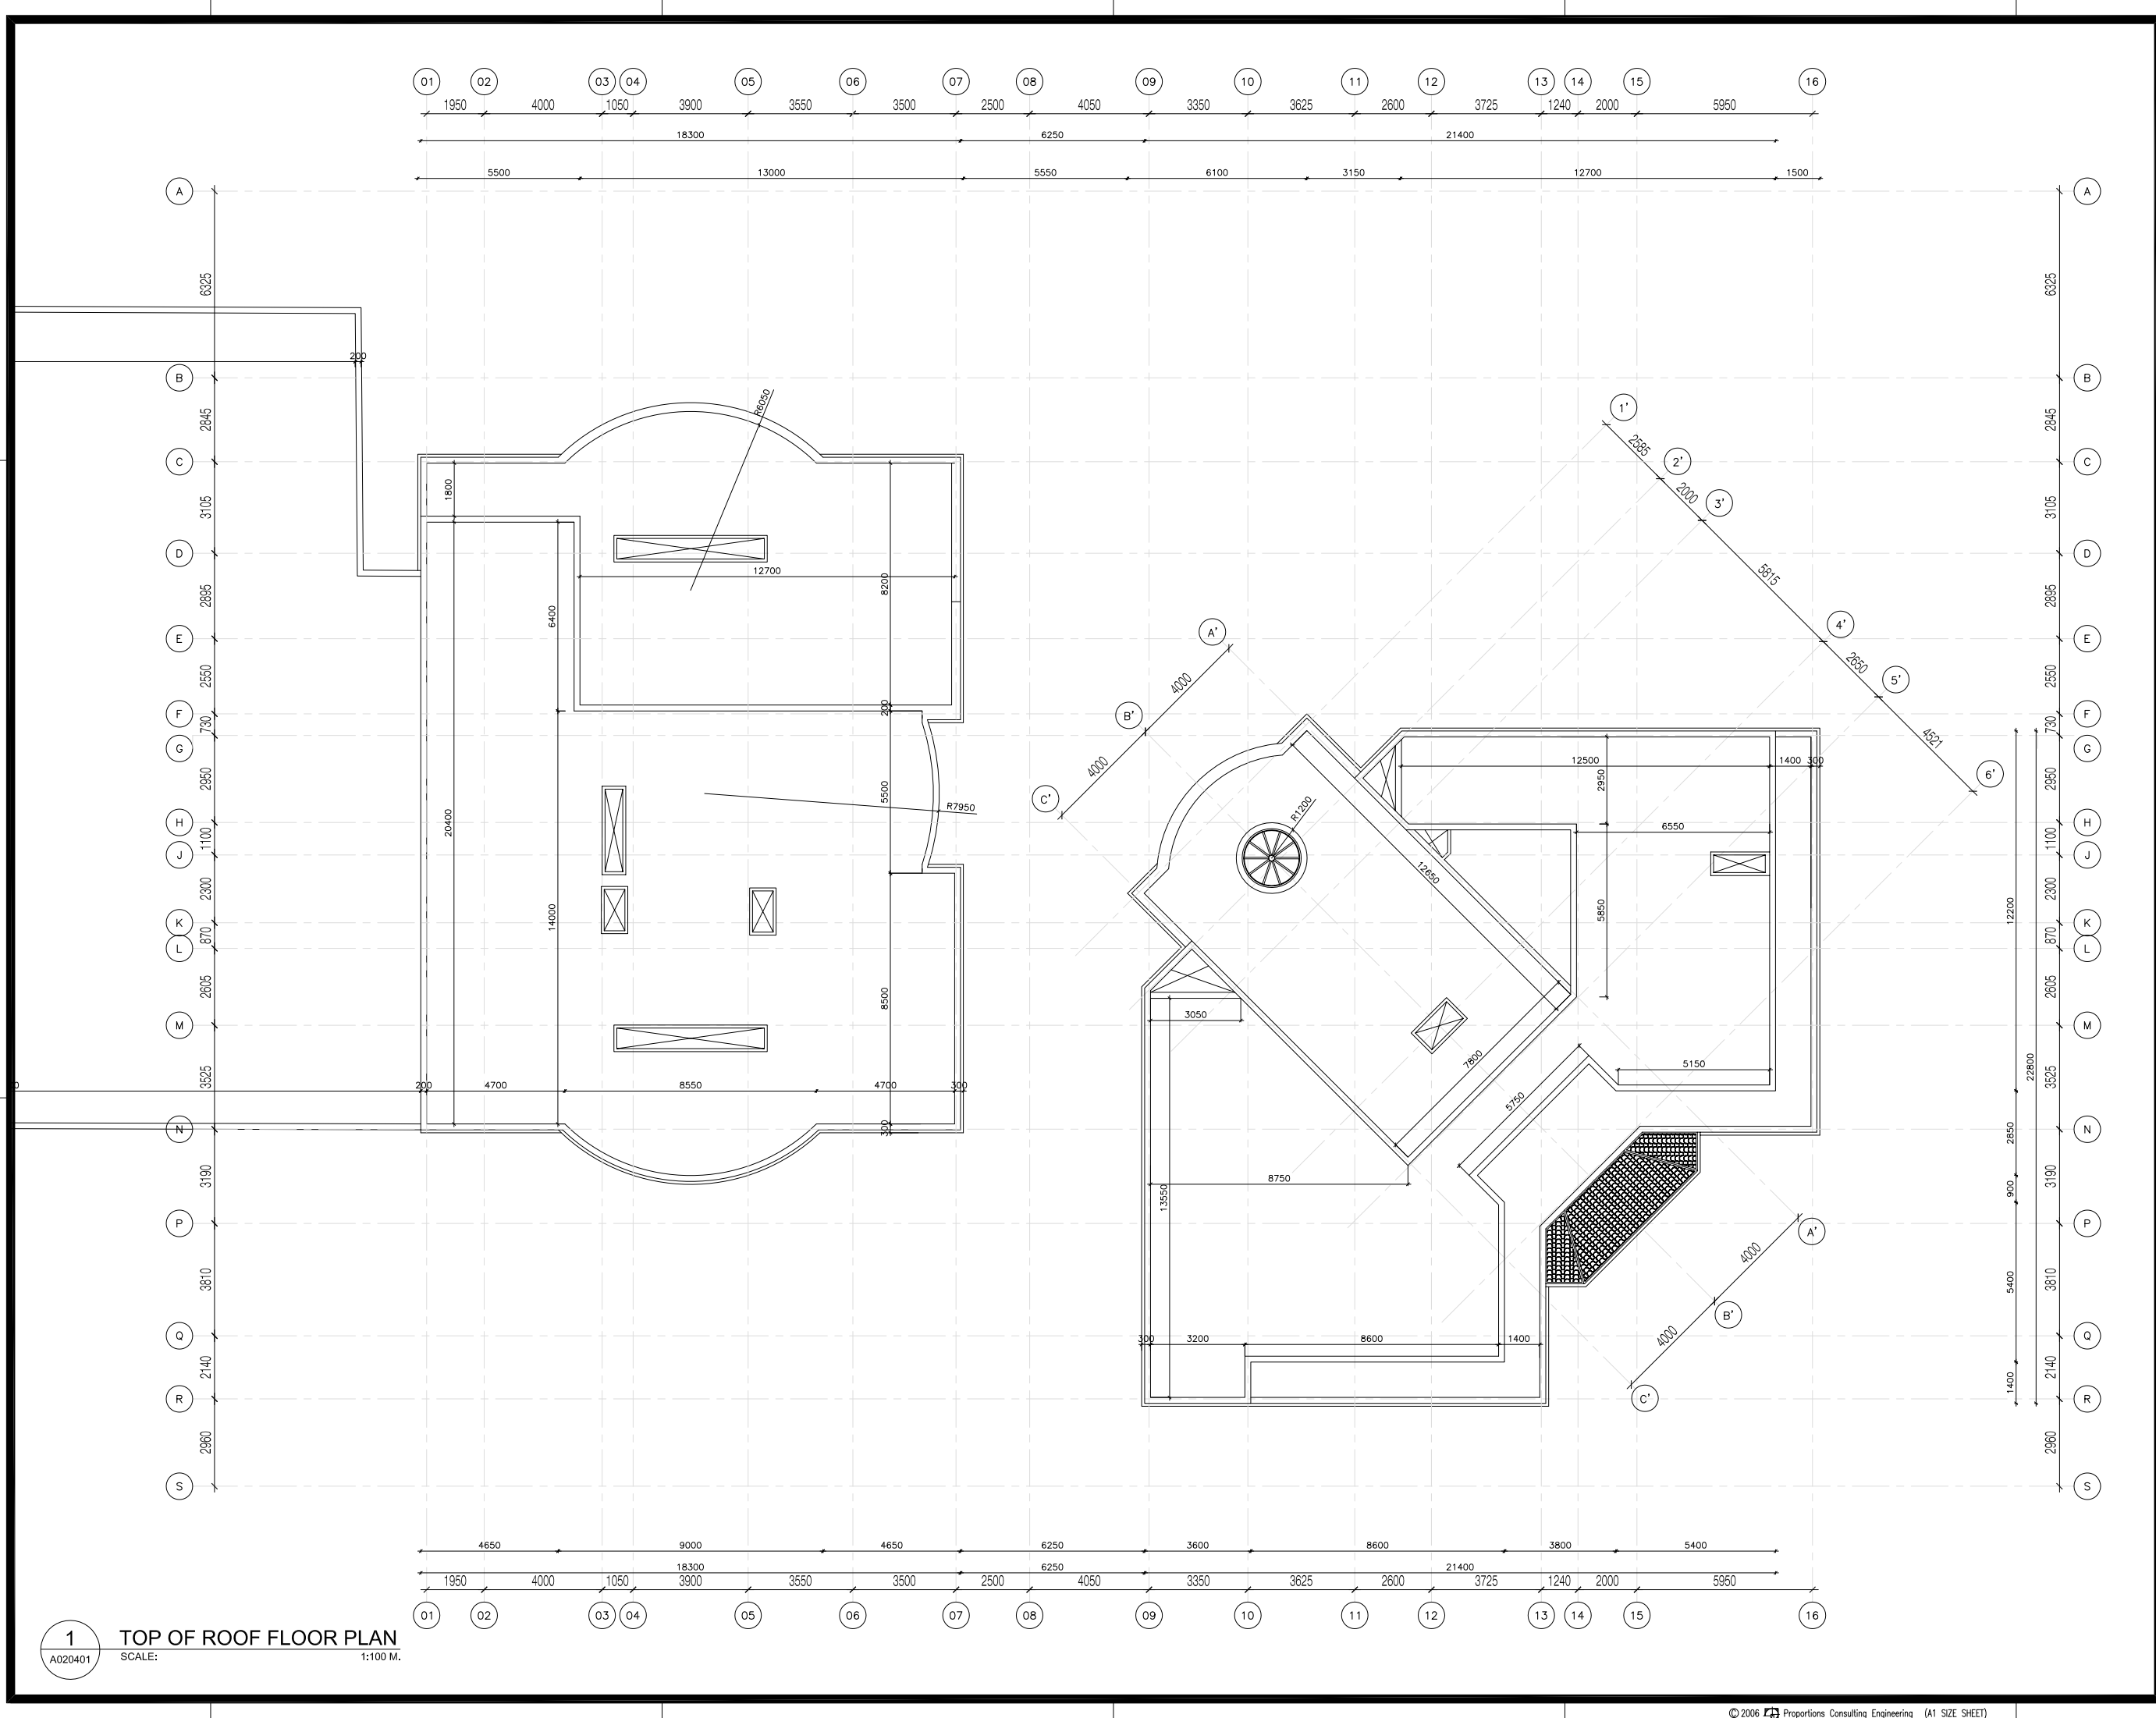


REV.	DATE	BY	DESCRIPTION
KEY PLAN			
CONSULTANT			
 النسب للإستشارات الهندسية Proportions Consulting Engineering Tel: 2792277, Fax: 2797722 P.O.Box 75453, Riyadh-11578			
PROJECT			
PRIVATE HOUSING COMPLEX AL NAKHEEL / RIYADH - SAUDI ARABIA			
OWNER			
SHEET TITLE			
ARCHITECTURAL TOP OF ROOF FLOOR PLAN			
TENDER DOCUMENTS			
PROJECT NO. :	P0521	STAGE :	WORKING DRAWINGS
DESIGNED BY :	Proportion Group	DRAWN BY :	CAD
DATE :	JAN. 2008	SCALE :	1:100M
A020401 ARCHITECTURAL			REVISION 0


1 TOP OF ROOF FLOOR PLAN
A020401 SCALE: 1:100 M.




1 WEST ELEVATION
A120201 SCALE: 1:100 M.

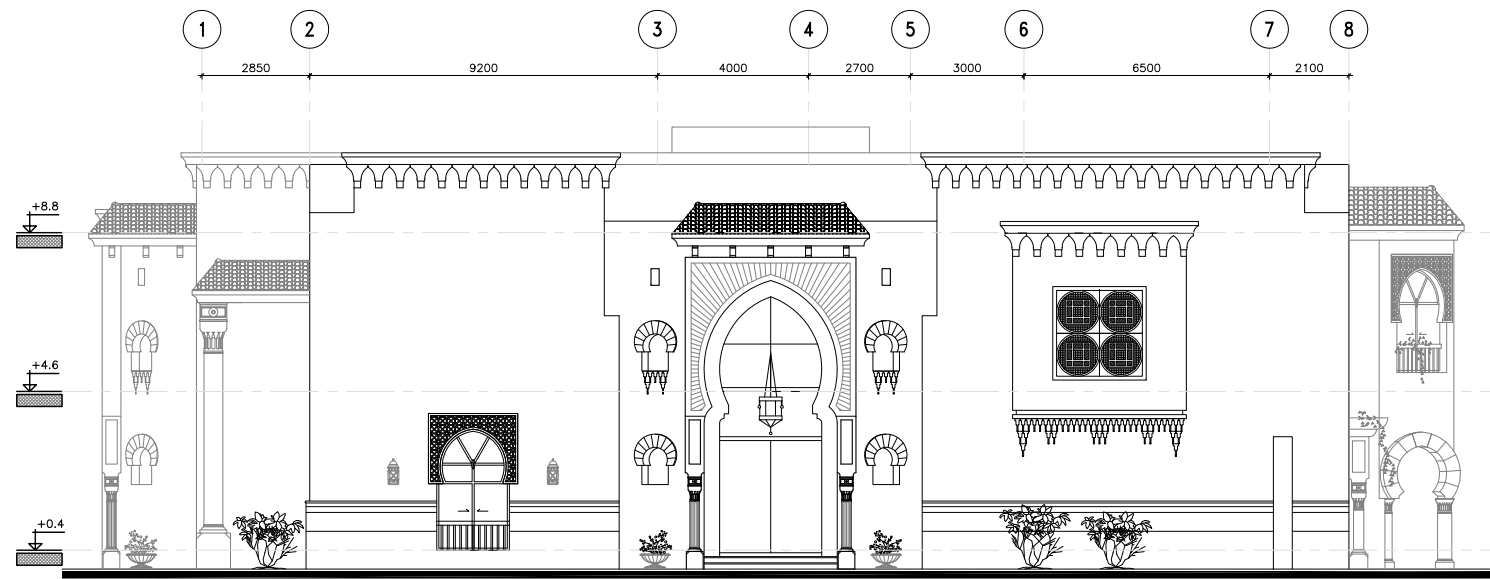

2 SOUTH ELEVATION
A120201 SCALE: 1:100 M.

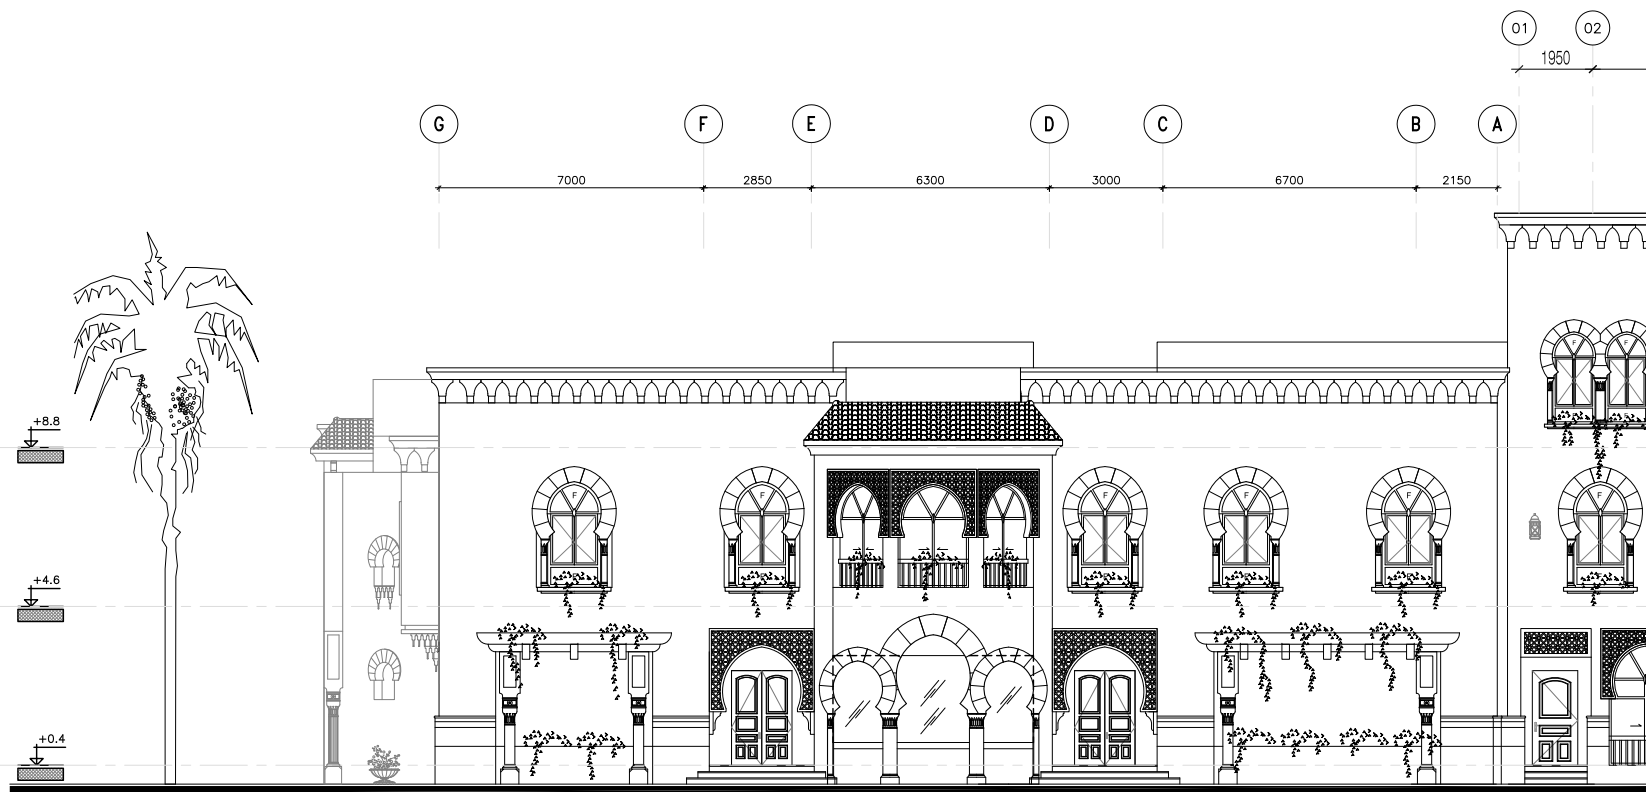

3 EAST ELEVATION
A120201 SCALE: 1:100 M.

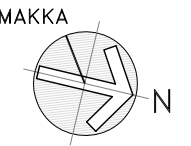

REV.	DATE	BY	DESCRIPTION

KEY PLAN

CONSULTANT



PROJECT

PRIVATE HOUSING COMPLEX
AL NAKHEEL / RIYADH - SAUDI ARABIA

OWNER

SHEET TITLE


EXISTING BUILDING
ELEVATIONS

TENDER DOCUMENTS


PROJECT NO. :	P0521	STAGE :	WORKING DRAWINGS
DESIGNED BY :	Proportion Group	DRAWN BY :	CAD
DATE :	JAN. 2006	SCALE :	1:100M

A120201
ARCHITECTURAL


REVISION
0

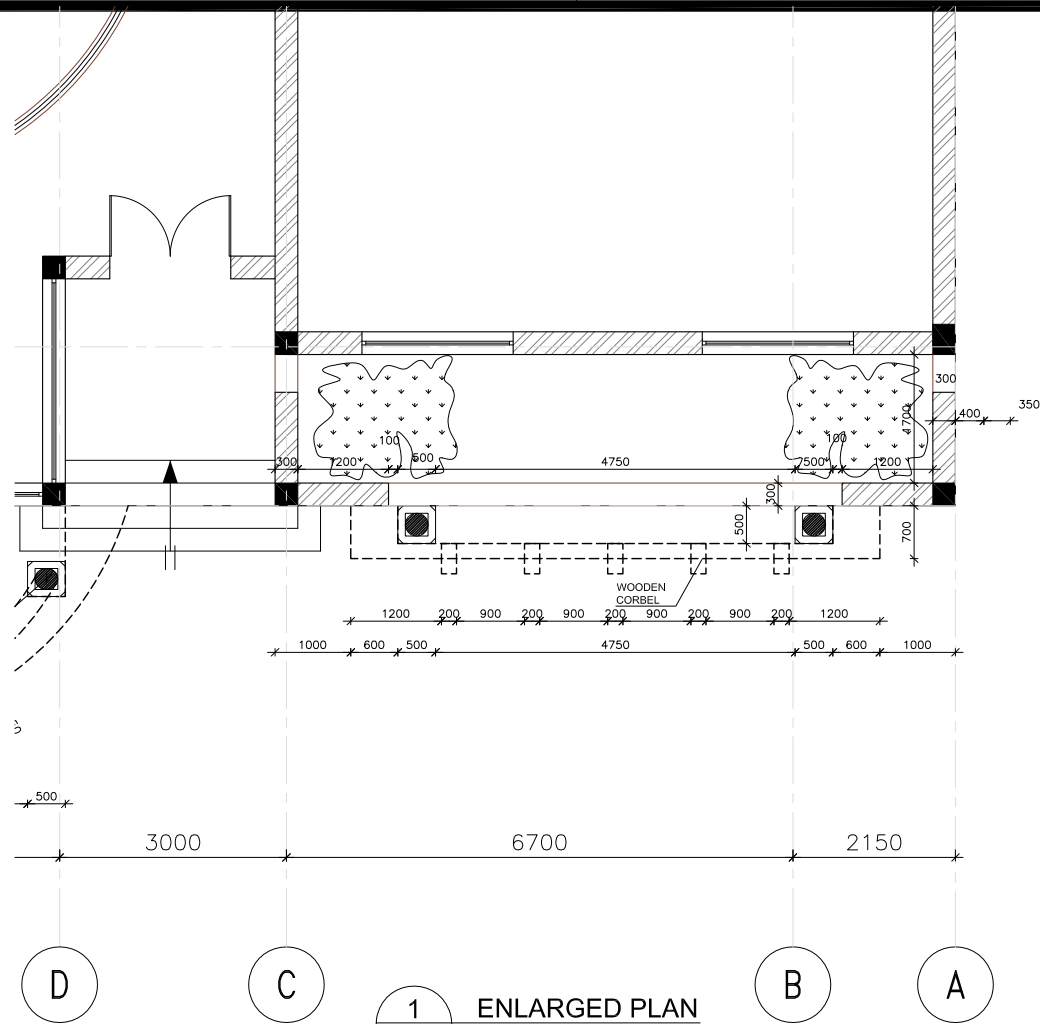


1 ENLARGED PLAN
SCALE: 1:50 M.
A120301

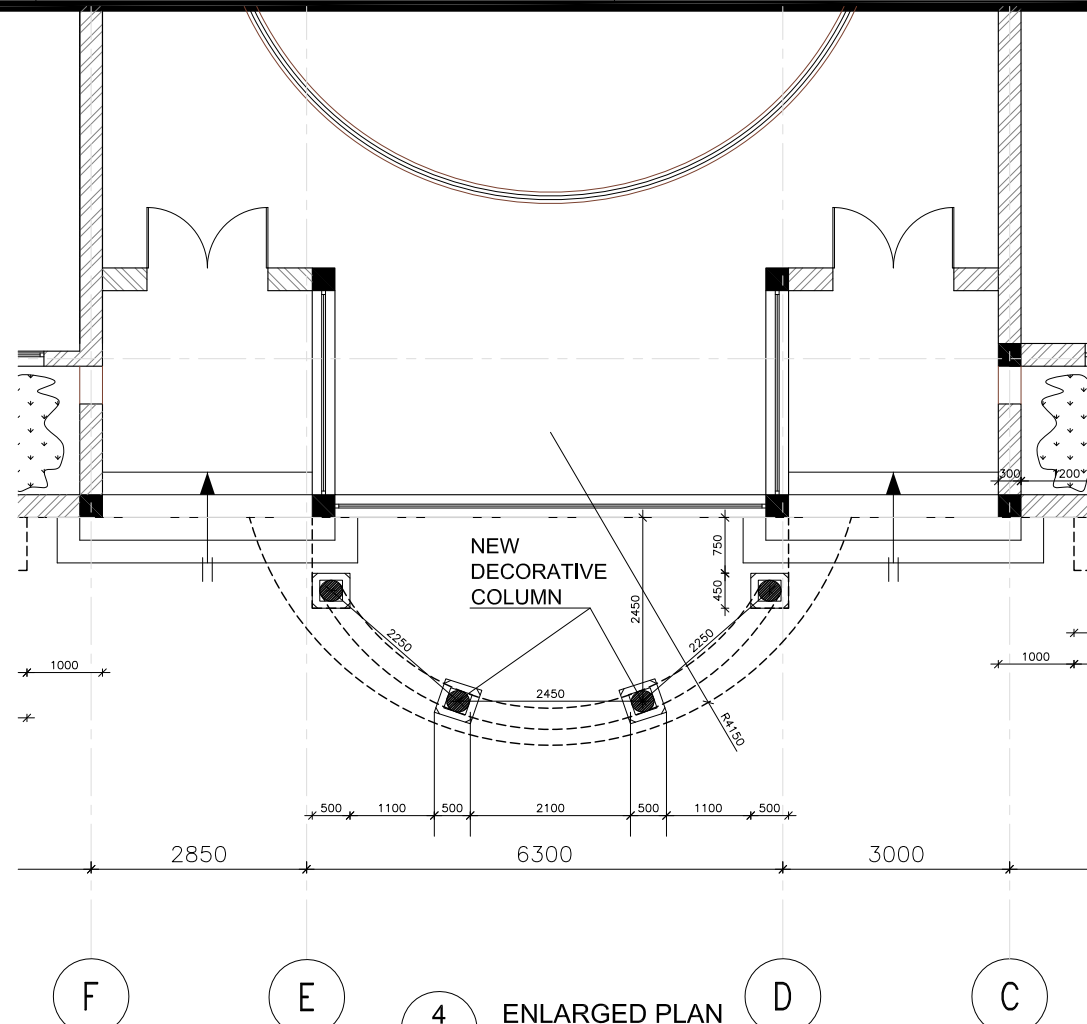


4 ENLARGED PLAN
SCALE: 1:50 M.
A120301

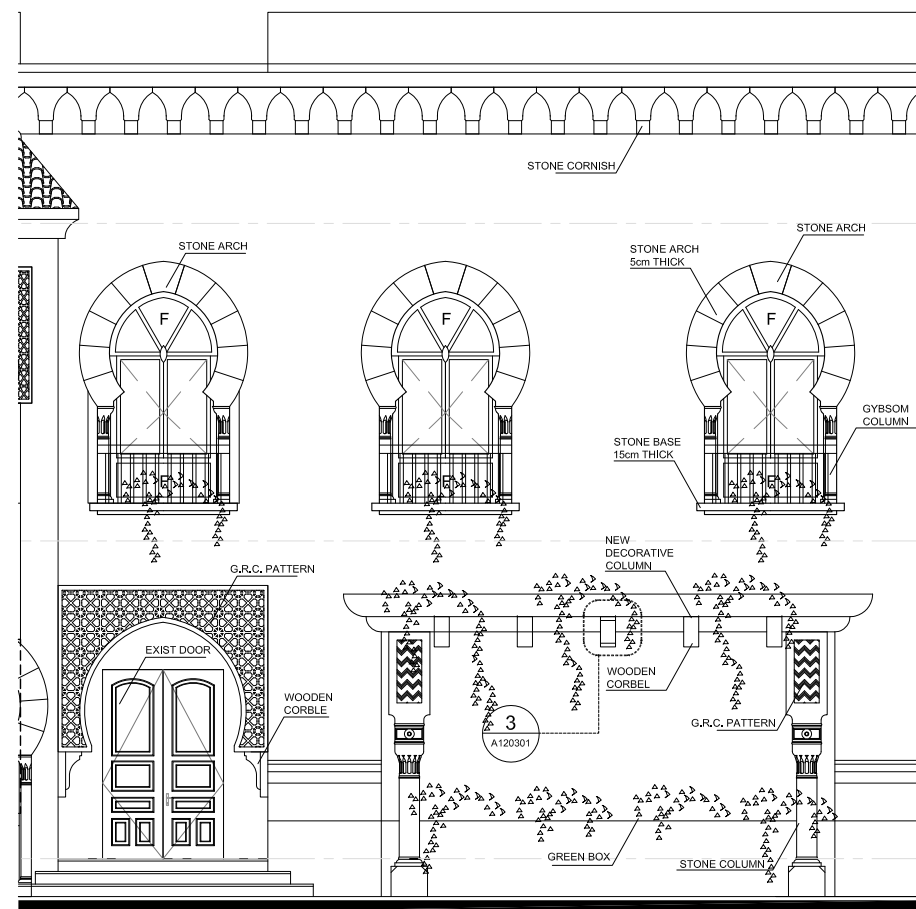

2 ENLARGED ELEVATION
SCALE: 1:50 M.
A120301

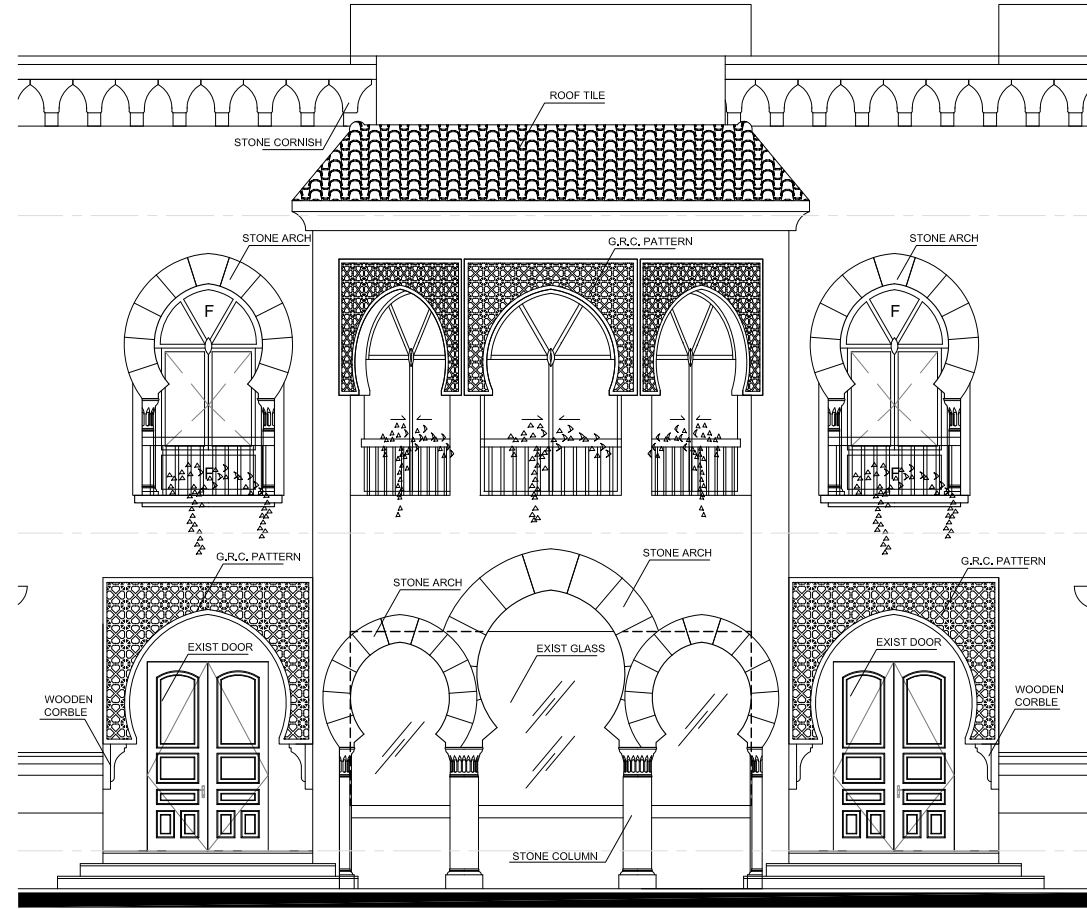

5 ENLARGED ELEVATION
SCALE: 1:50 M.
A120301

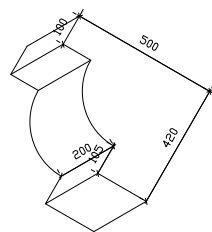

3 CORBLE DETAILS
SCALE: 1:10 M.
A120301

REV.	DATE	BY	DESCRIPTION

KEY PLAN

CONSULTANT



PROJECT

PRIVATE HOUSING COMPLEX
AL NAKHEEL / RIYADH - SAUDI ARABIA

OWNER

SHEET TITLE

EXISTING BUILDING
DETAILS

TENDER DOCUMENTS

PROJECT NO. :	P0521	STAGE :	WORKING DRAWINGS
DESIGNED BY :	Proportion Group	DRAWN BY :	CAD
DATE :	JAN. 2008	SCALE :	1:50M


A120301
ARCHITECTURAL

REVISION
0


3

4

5

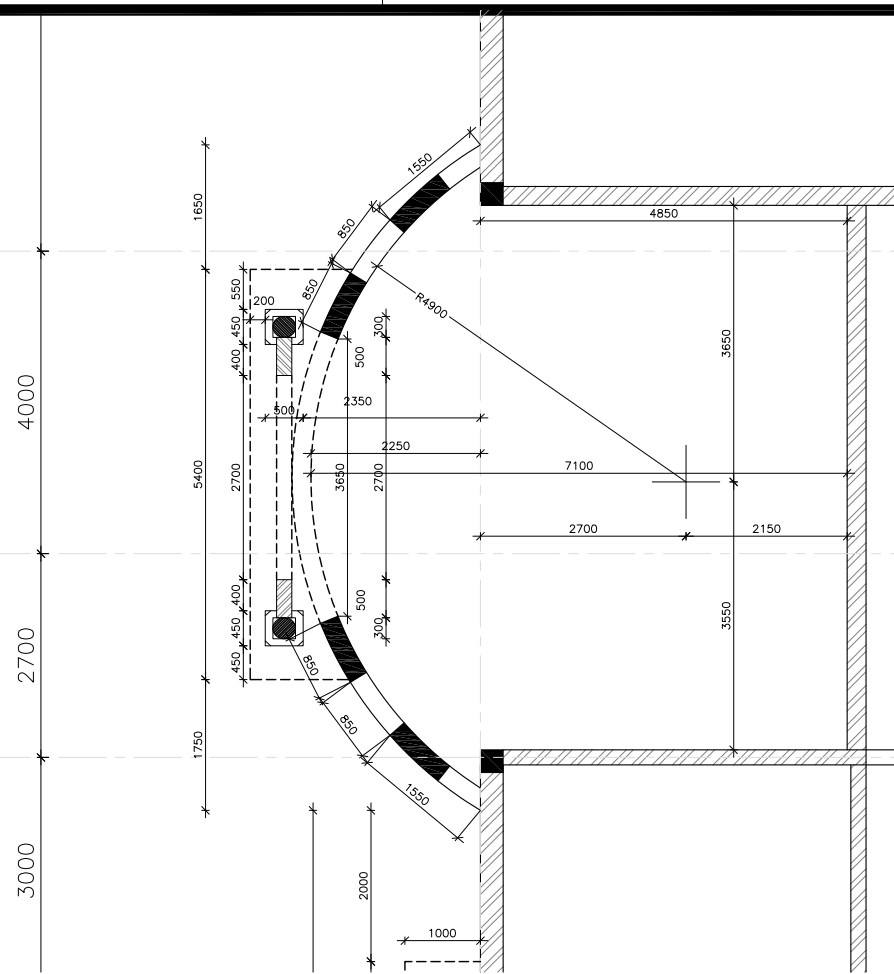

1 ENLARGED PLAN
A120302 SCALE: 1:50 M.

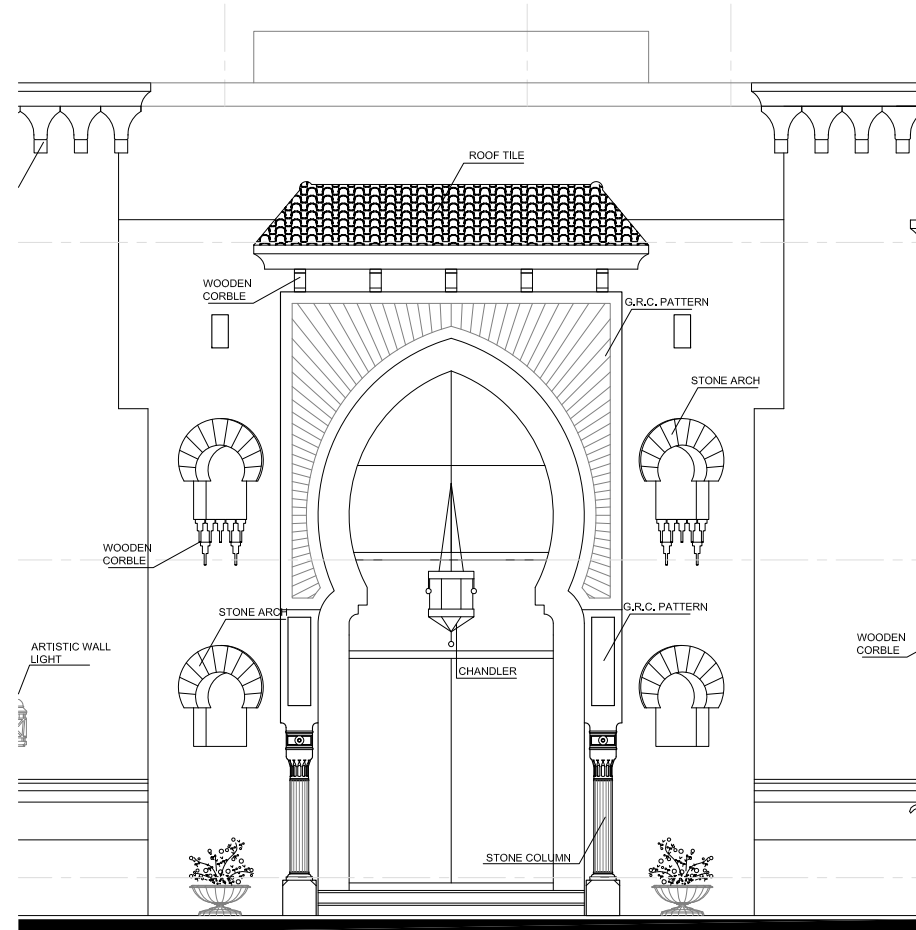


2 ENLARGED ELEVATION
A120302 SCALE: 1:50 M.

F


E

D


C

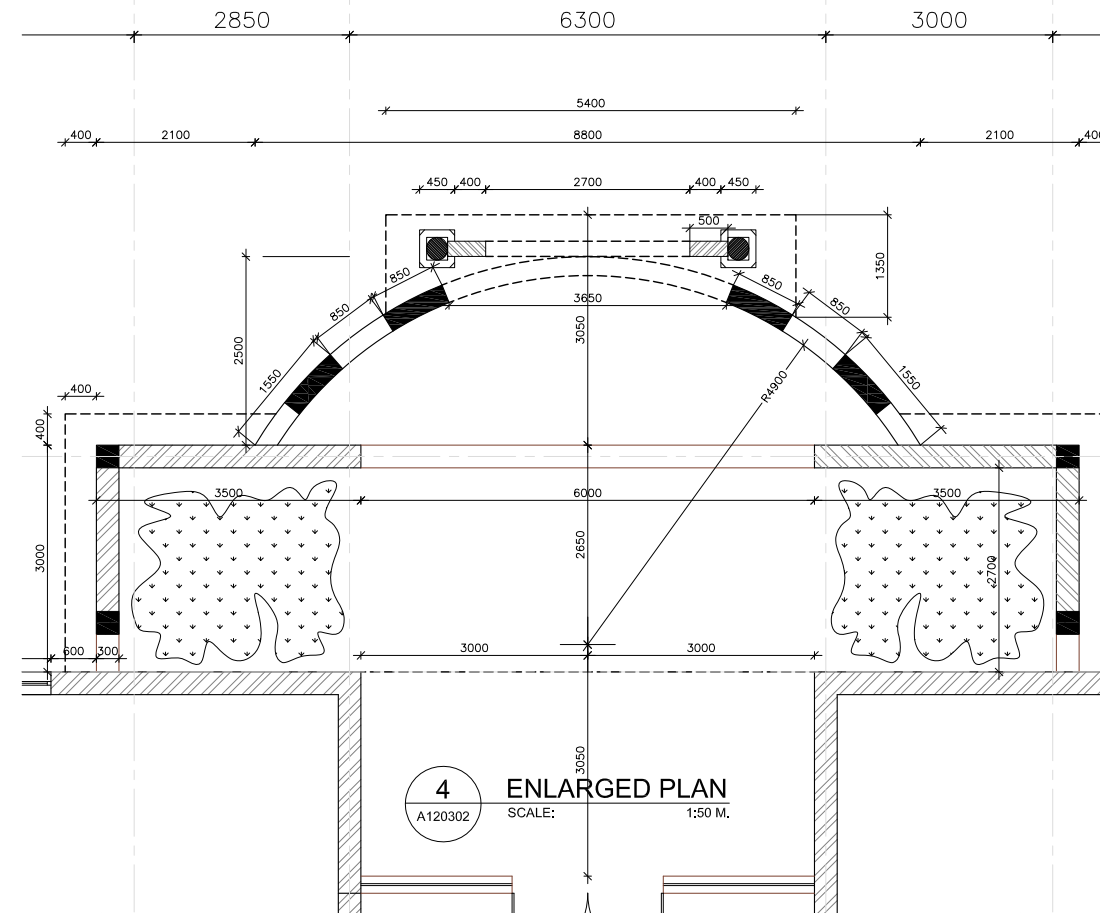

4 ENLARGED PLAN
A120302 SCALE: 1:50 M.

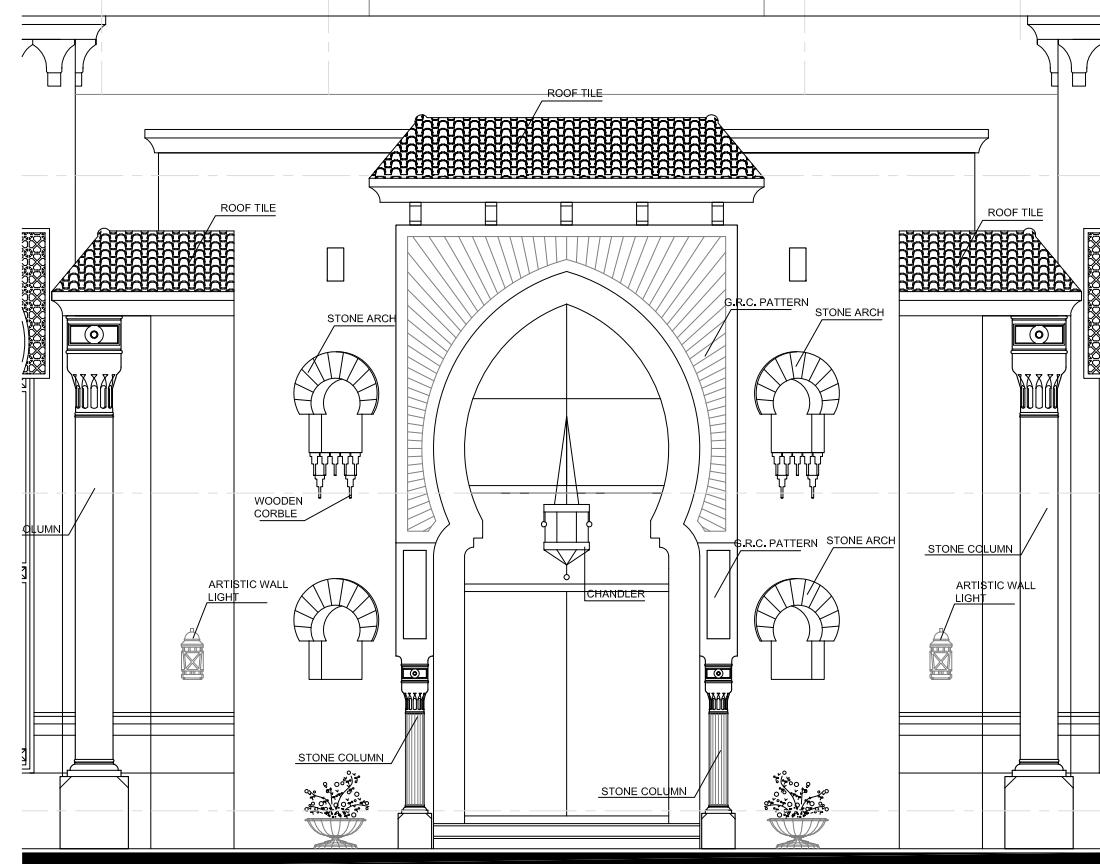

5 ENLARGED ELEVATION
A120302 SCALE: 1:50 M.

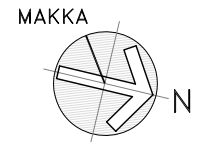

REV.	DATE	BY	DESCRIPTION

KEY PLAN

CONSULTANT



PROJECT

PRIVATE HOUSING COMPLEX
AL NAKHEEL / RIYADH - SAUDI ARABIA

OWNER

SHEET TITLE





EXISTING BUILDING
DETAILS

TENDER DOCUMENTS

PROJECT NO. :	P0521	STAGE :	WORKING DRAWINGS
DESIGNED BY :	Proportion Group	DRAWN BY :	CAD
DATE :	JAN. 2008	SCALE :	1:100M

A120302
ARCHITECTURAL

REVISION
0

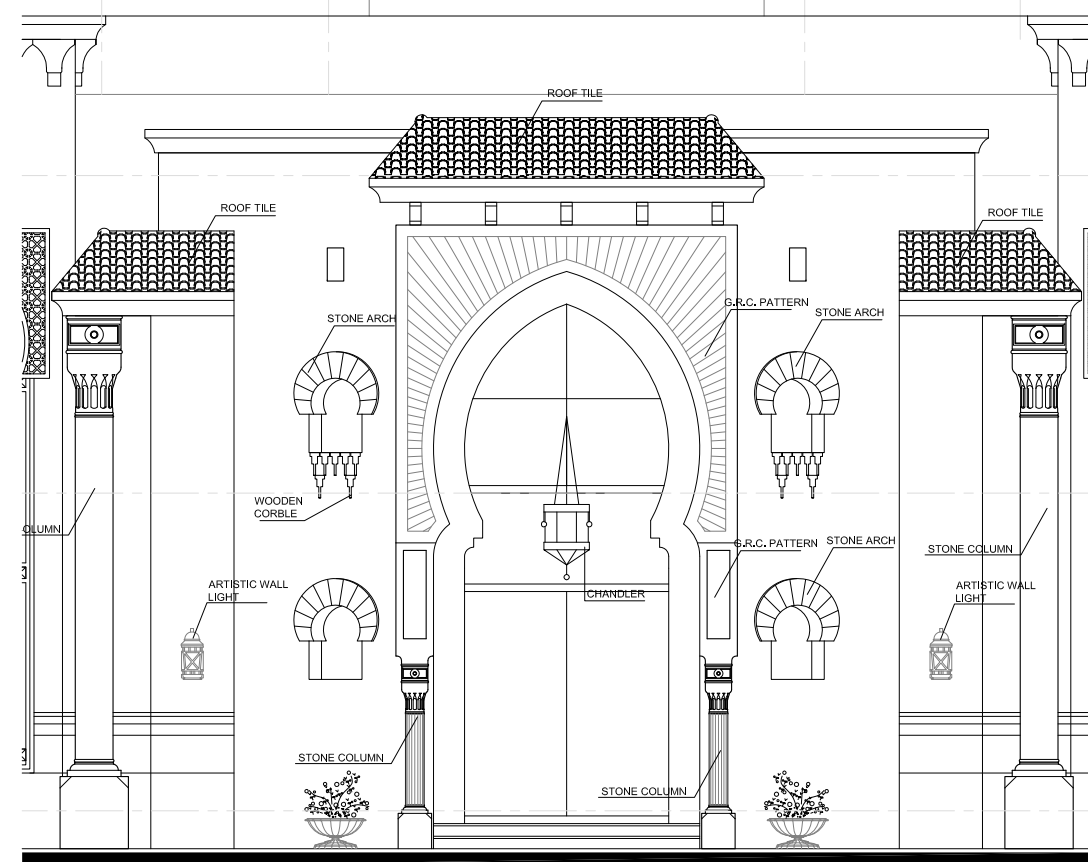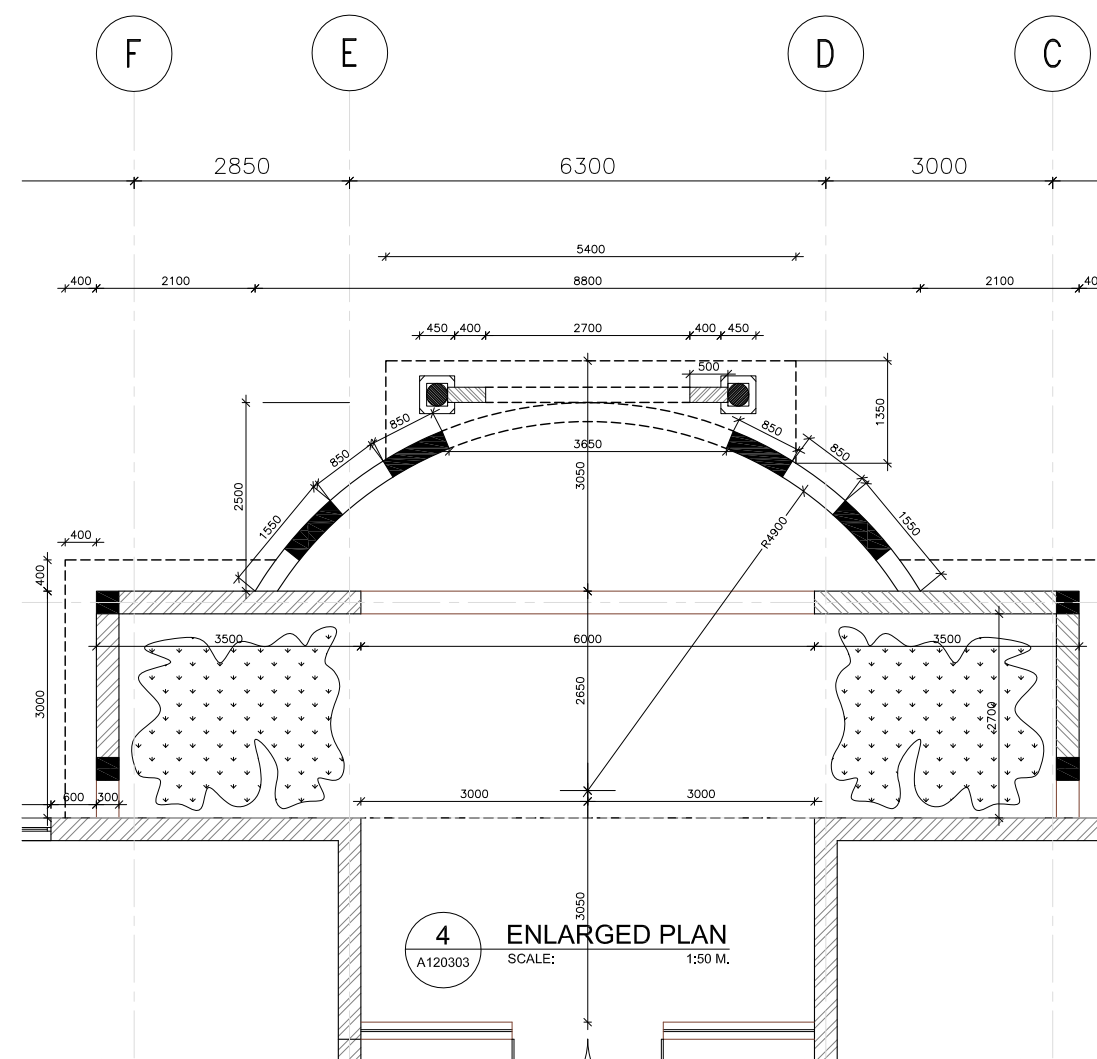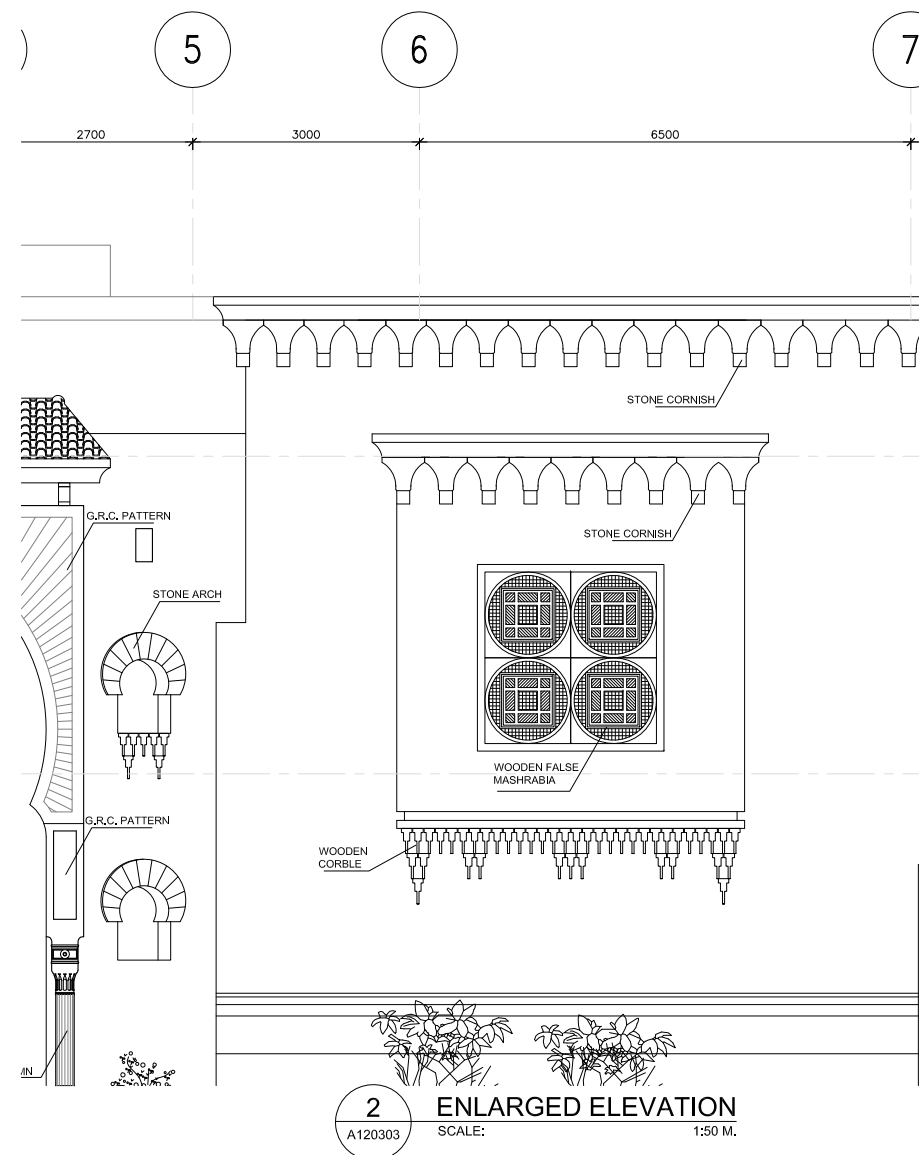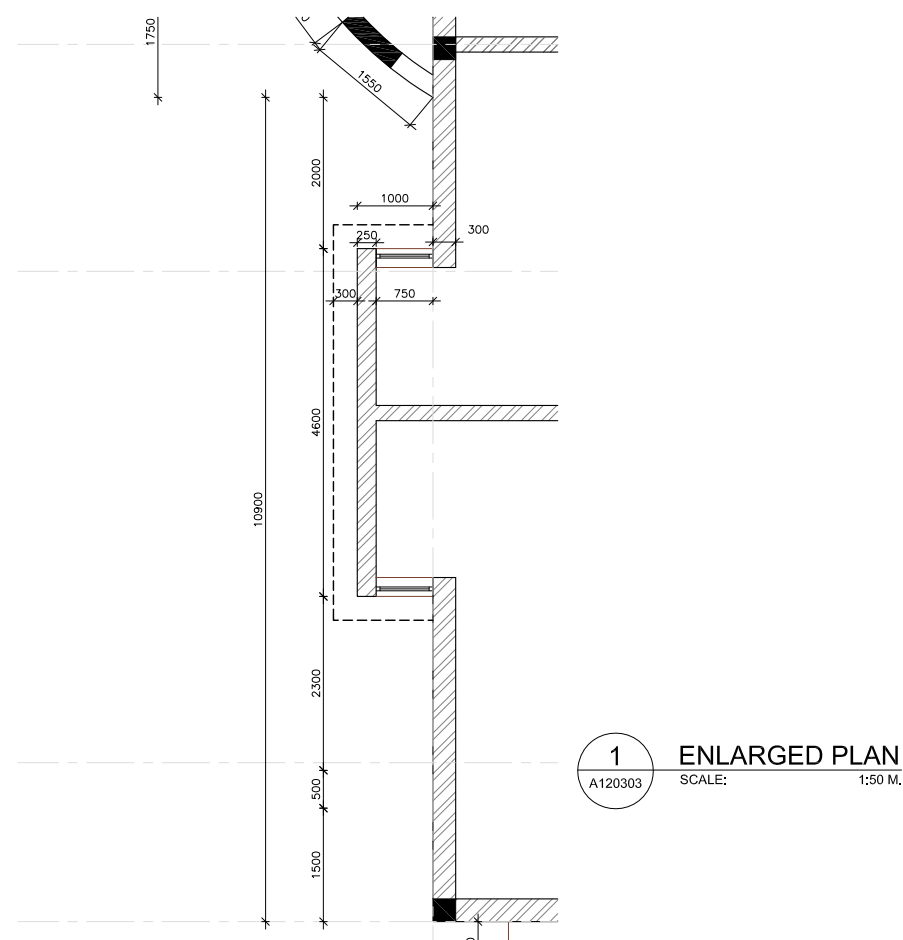

REV.	DATE	BY	DESCRIPTION

KEY PLAN

CONSULTANT



PROJECT

PRIVATE HOUSING COMPLEX
AL NAKHEEL / RIYADH - SAUDI ARABIA

OWNER

SHEET TITLE



EXISTING BUILDING DETAILS

TENDER DOCUMENTS

PROJECT NO. :	P0521	STAGE :	WORKING DRAW
DESIGNED BY :	Proportion Group	DRAWN BY :	CAD
DATE :	JAN. 2006	SCALE :	1:100M


A120303
ARCHITECTURAL

REVIS
0

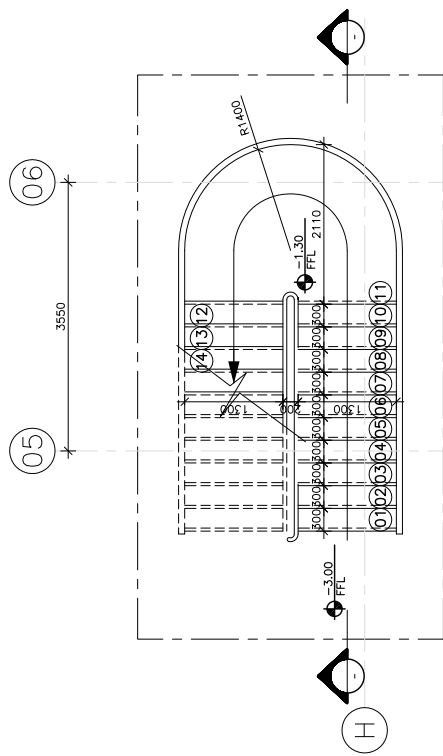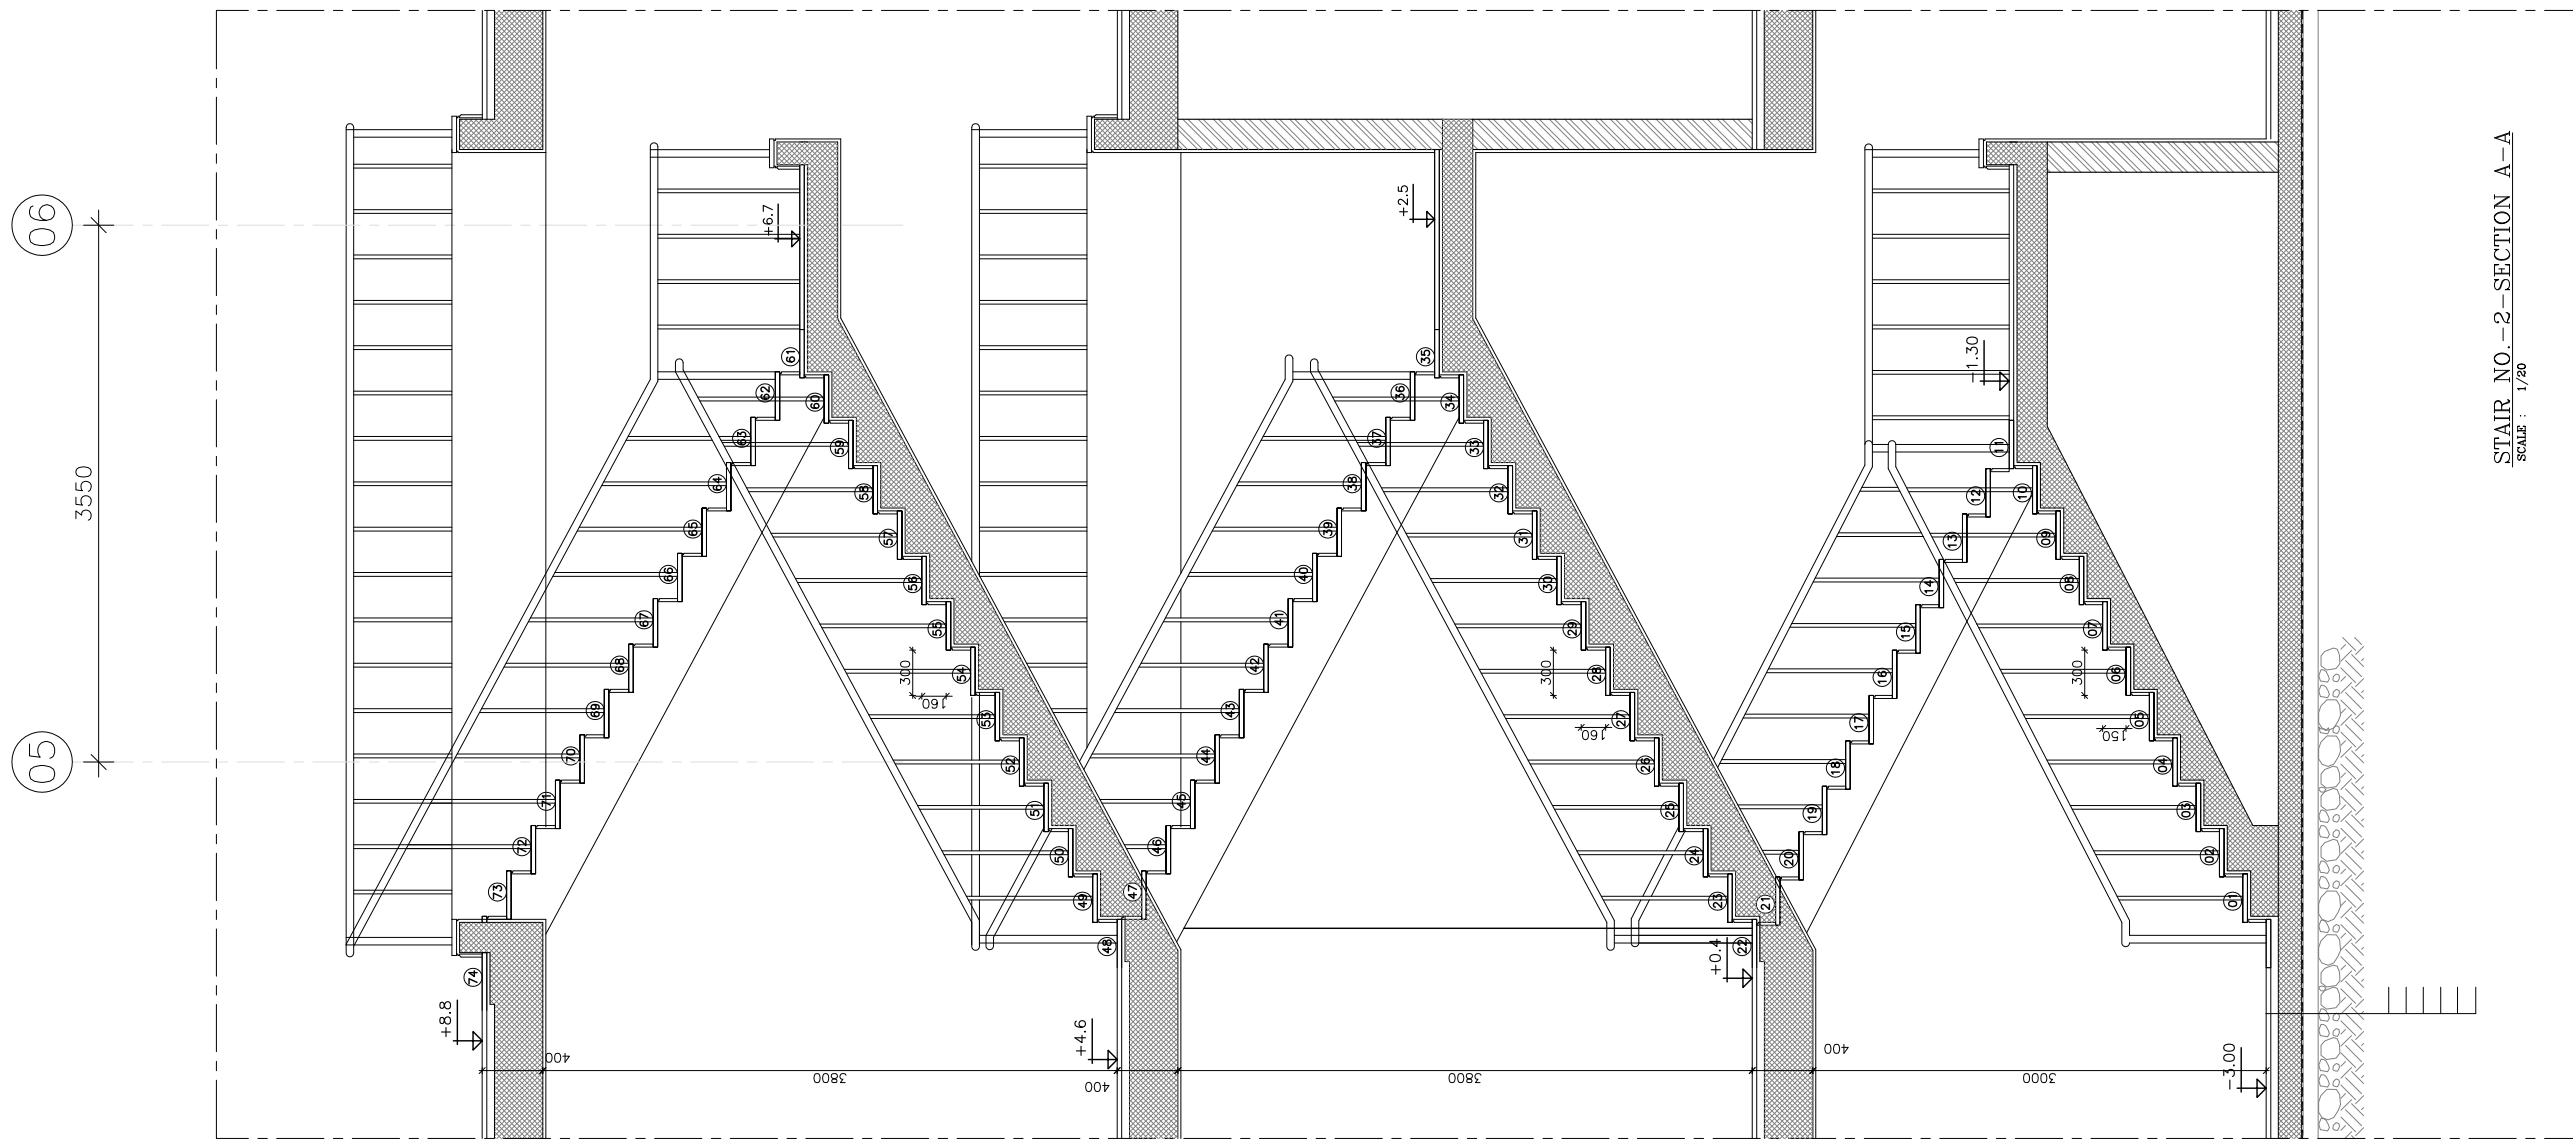


STAIR NO. -2-BASEMENT FLOOR PLAN

SCALE : 1/50

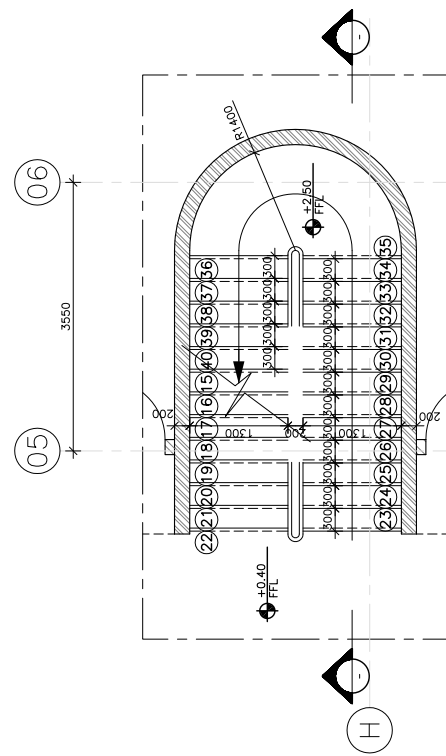


STAIR NO. -2-GROUND FLOOR PLAN

SCALE : 1/50

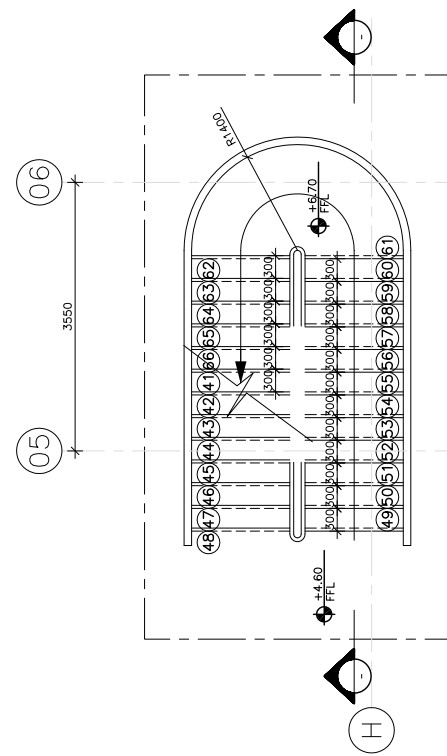

STAIR NO. -2-FIRST FLOOR PLAN

SCALE : 1/50

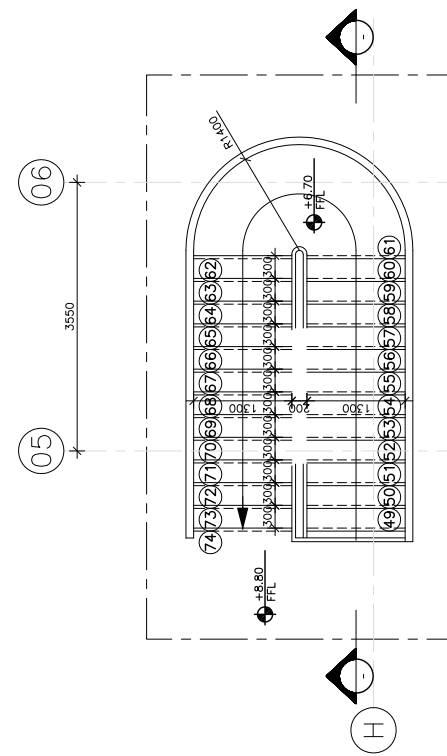

STAIR NO. -2-ROOF FLOOR PLAN


SCALE : 1/50

STAIR NO. -2-SECTION A-A


SCALE : 1/20

REV.	DATE	BY	DESCRIPTION
KEY PLAN			
CONSULTANT			
 النسب للإستشارات الهندسية Proportions Consulting Engineering Tel: 2792277, Fax: 2797722 P.O.Box 75453, Riyadh-11578			
PROJECT			
PRIVATE HOUSING COMPLEX AL NAKHEEL / RIYADH - SAUDI ARABIA			
OWNER			
SHEET TITLE			
ARCHITECTURAL STAIR NO 2			
TENDER DOCUMENTS			
PROJECT NO. :	P0521	STAGE :	WORKING DRAWINGS
DESIGNED BY :	Proportion Group	DRAWN BY :	CAD
DATE :	JAN. 2008	SCALE :	1/25 1/50
A040502 ARCHITECTURAL			REVISION 0




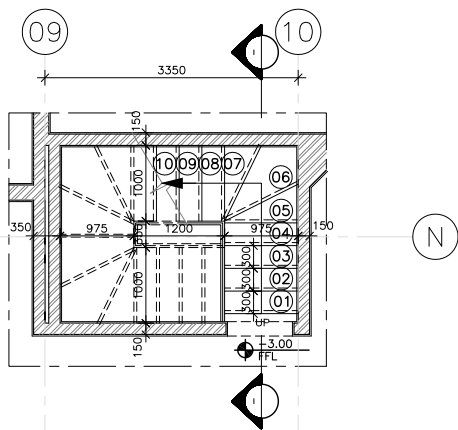


STAIR NO.-3-BASEMENT FLOOR PLAN
SCALE : 1/50

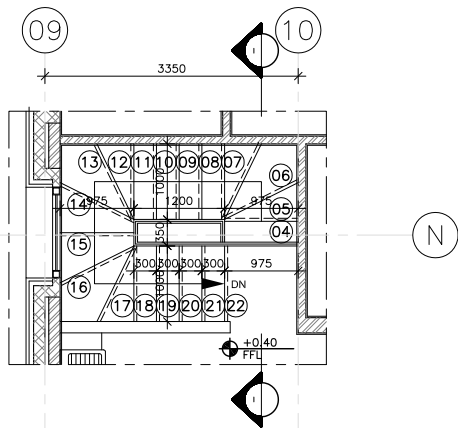


STAIR NO.-3-GROUND FLOOR PLAN
SCALE : 1/50

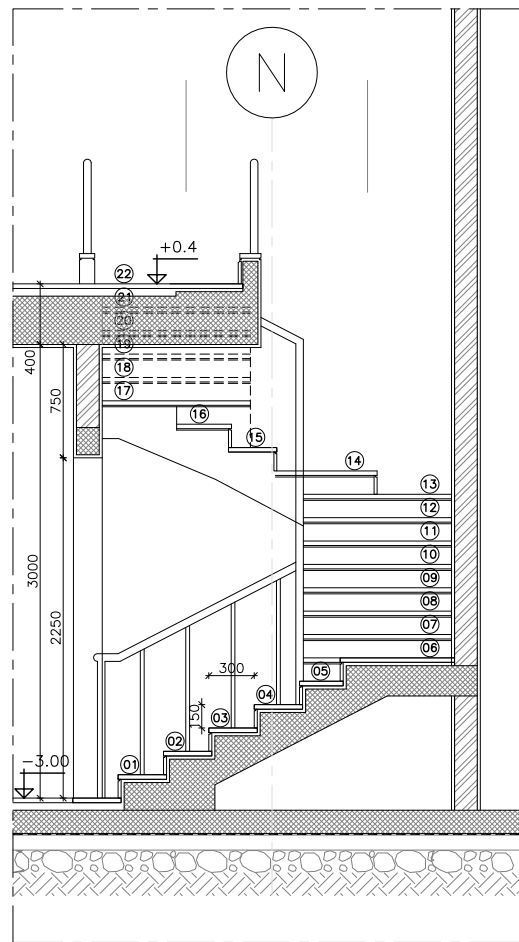


STAIR NO.-3-SECTION A-A
SCALE : 1/20

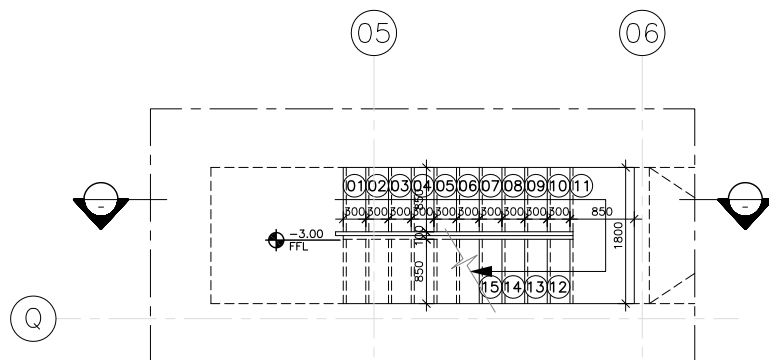

STAIR NO.-6-BASEMENT FLOOR PLAN
SCALE : 1/50

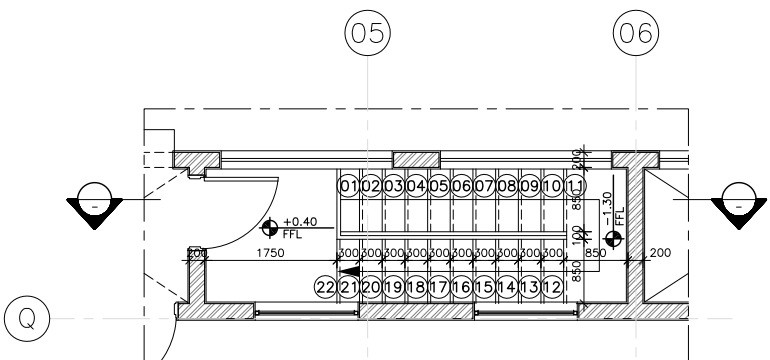

STAIR NO.-6-GROUND FLOOR PLAN
SCALE : 1/50

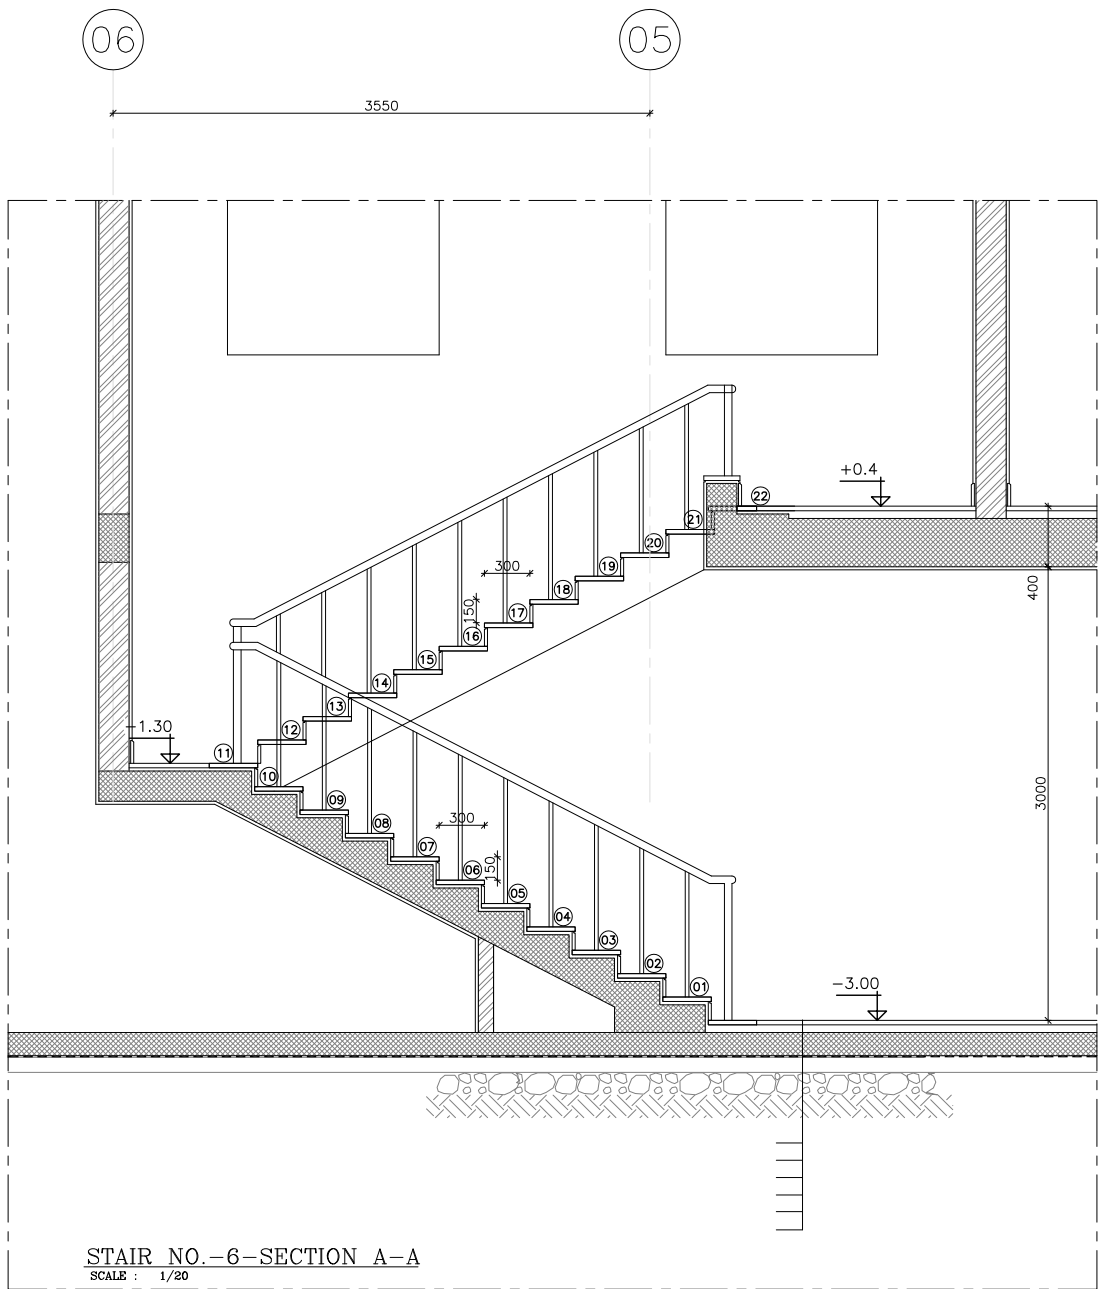

STAIR NO.-6-SECTION A-A
SCALE : 1/20



REV.	DATE	BY	DESCRIPTION

KEY PLAN

CONSULTANT



PROJECT

PRIVATE HOUSING COMPLEX
AL NAKHEEL / RIYADH - SAUDI ARABIA

OWNER

SHEET TITLE


ARCHITECTURAL
STAIR 3 & 6

TENDER DOCUMENTS


PROJECT NO. :	P0521	STAGE :	WORKING DRAWINGS
DESIGNED BY :	Proportion Group	DRAWN BY :	CAD
DATE :	JAN. 2008	SCALE :	1:100M

A040503
ARCHITECTURAL


REVISION
0

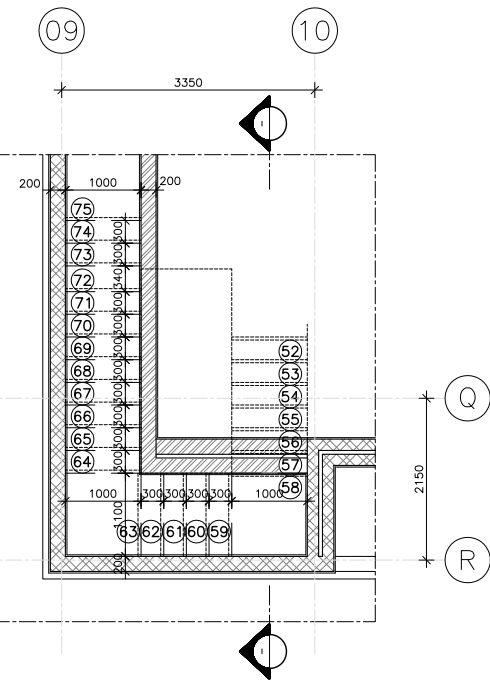


STAIR NO.-4-ROOF FLOOR PLAN
SCALE : 1/50

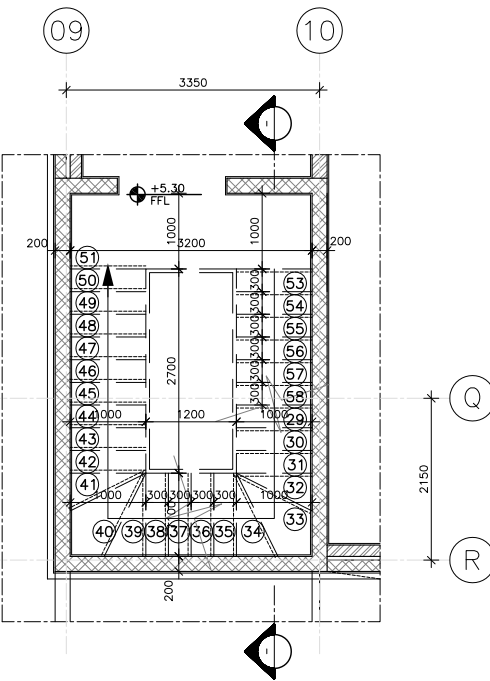


STAIR NO.-4-FIRST FLOOR PLAN
SCALE : 1/50

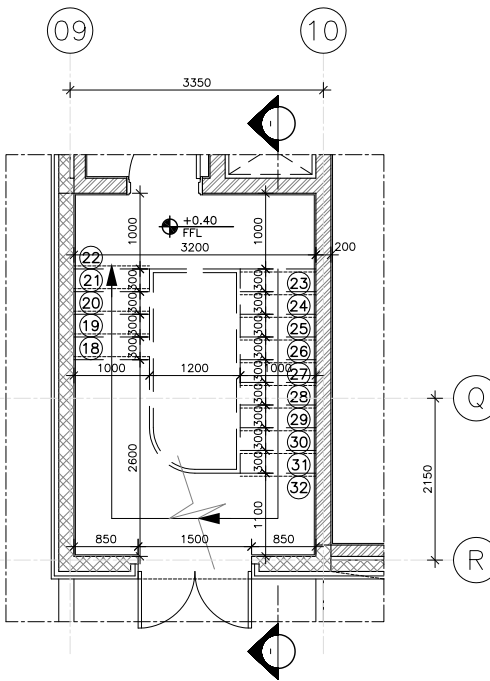

STAIR NO.-4-GROUND FLOOR PLAN
SCALE : 1/50




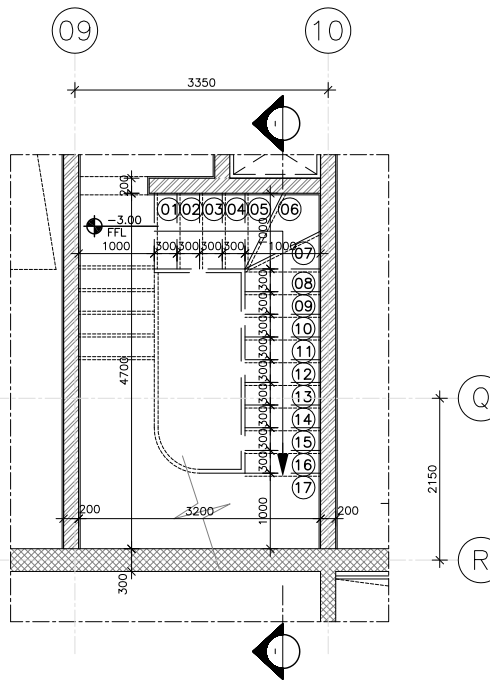


STAIR NO.-4-BASEMENT FLOOR PLAN
SCALE : 1/50

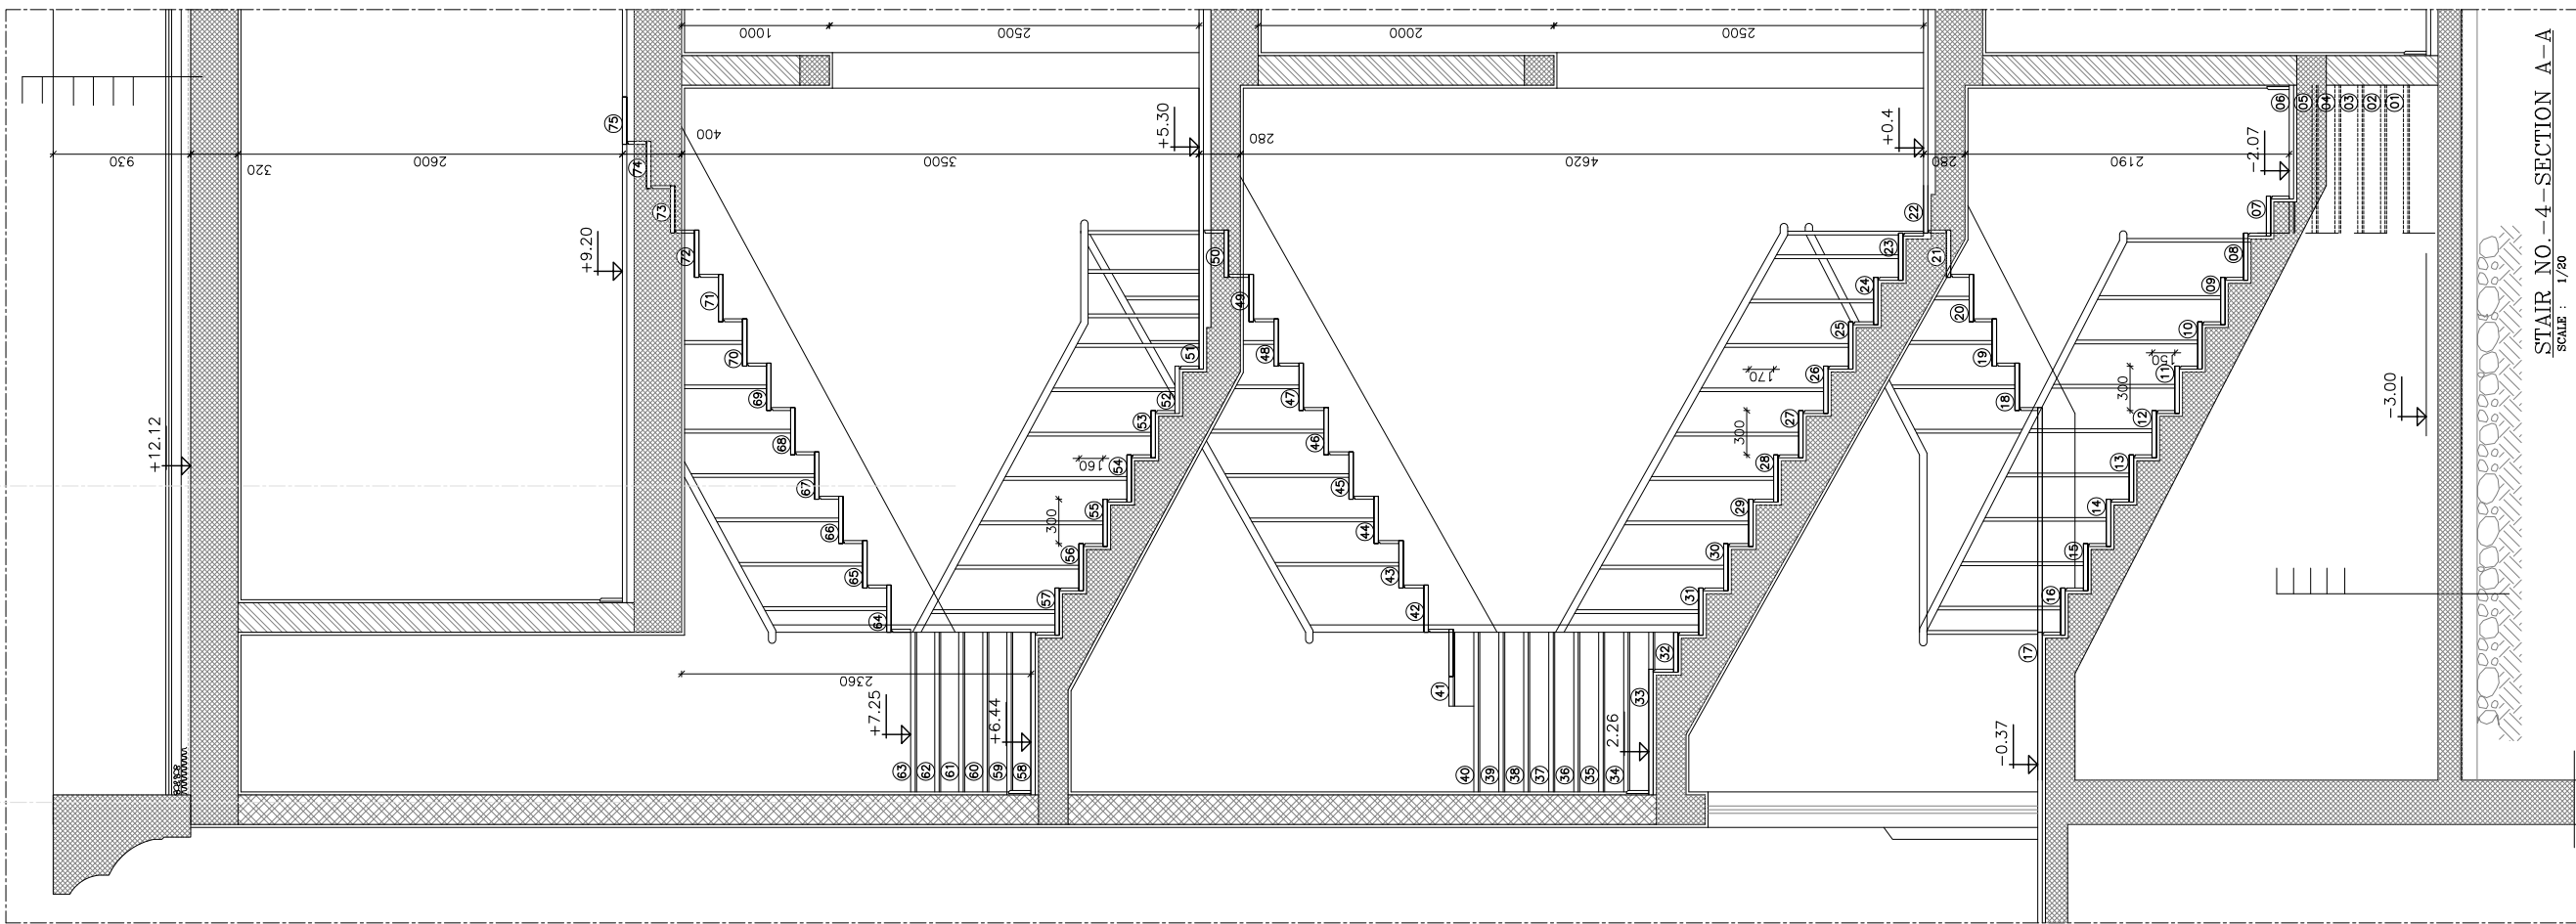


STAIR NO.-4-SECTION A-A
SCALE : 1/20

REV.	DATE	BY	DESCRIPTION
KEY PLAN			
CONSULTANT			
 النسب للإستشارات الهندسية Proportions Consulting Engineering Tel: 2792277, Fax: 2797722 P.O.Box 75453, Riyadh-11578			
PROJECT			
PRIVATE HOUSING COMPLEX AL NAKHEEL / RIYADH - SAUDI ARABIA			
OWNER			
SHEET TITLE			
ARCHITECTURAL STAIR NO 4			
TENDER DOCUMENTS			
PROJECT NO. :	P0521	STAGE :	WORKING DRAWINGS
DESIGNED BY :	Proportion Group	DRAWN BY :	CAD
DATE :	JAN. 2008	SCALE :	1/25 1/50
A040504 ARCHITECTURAL			REVISION 0

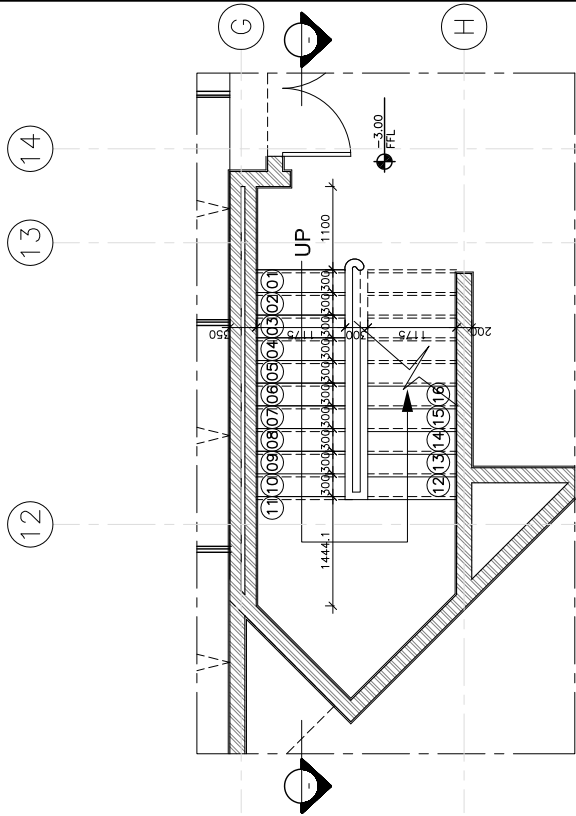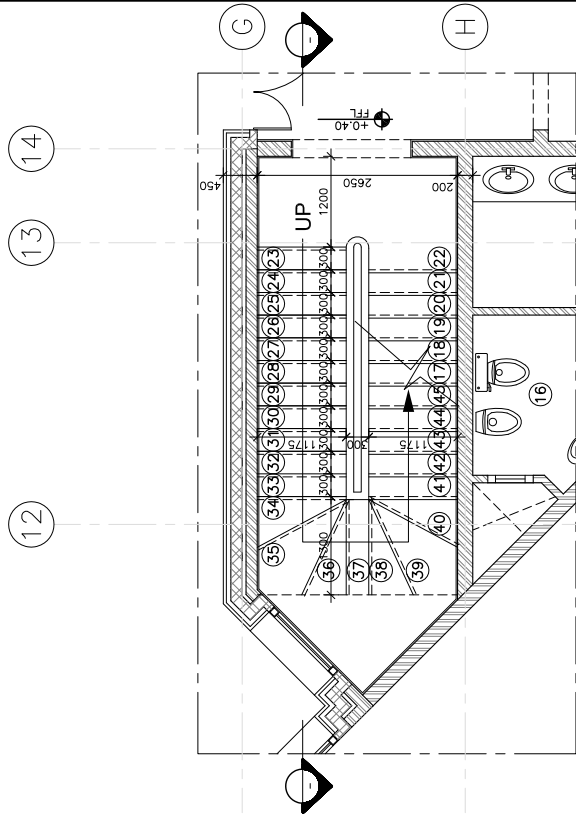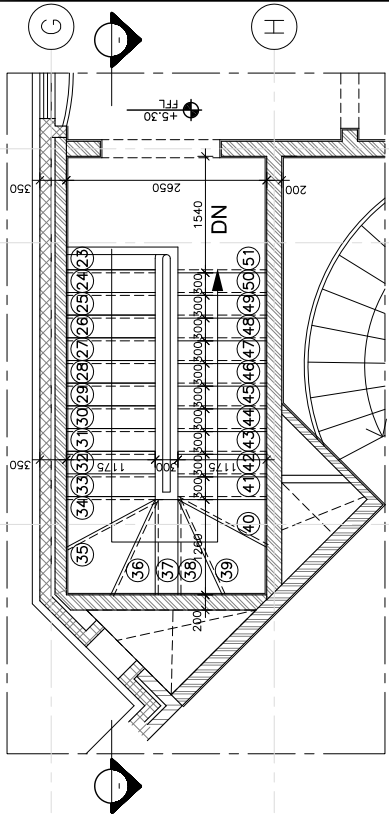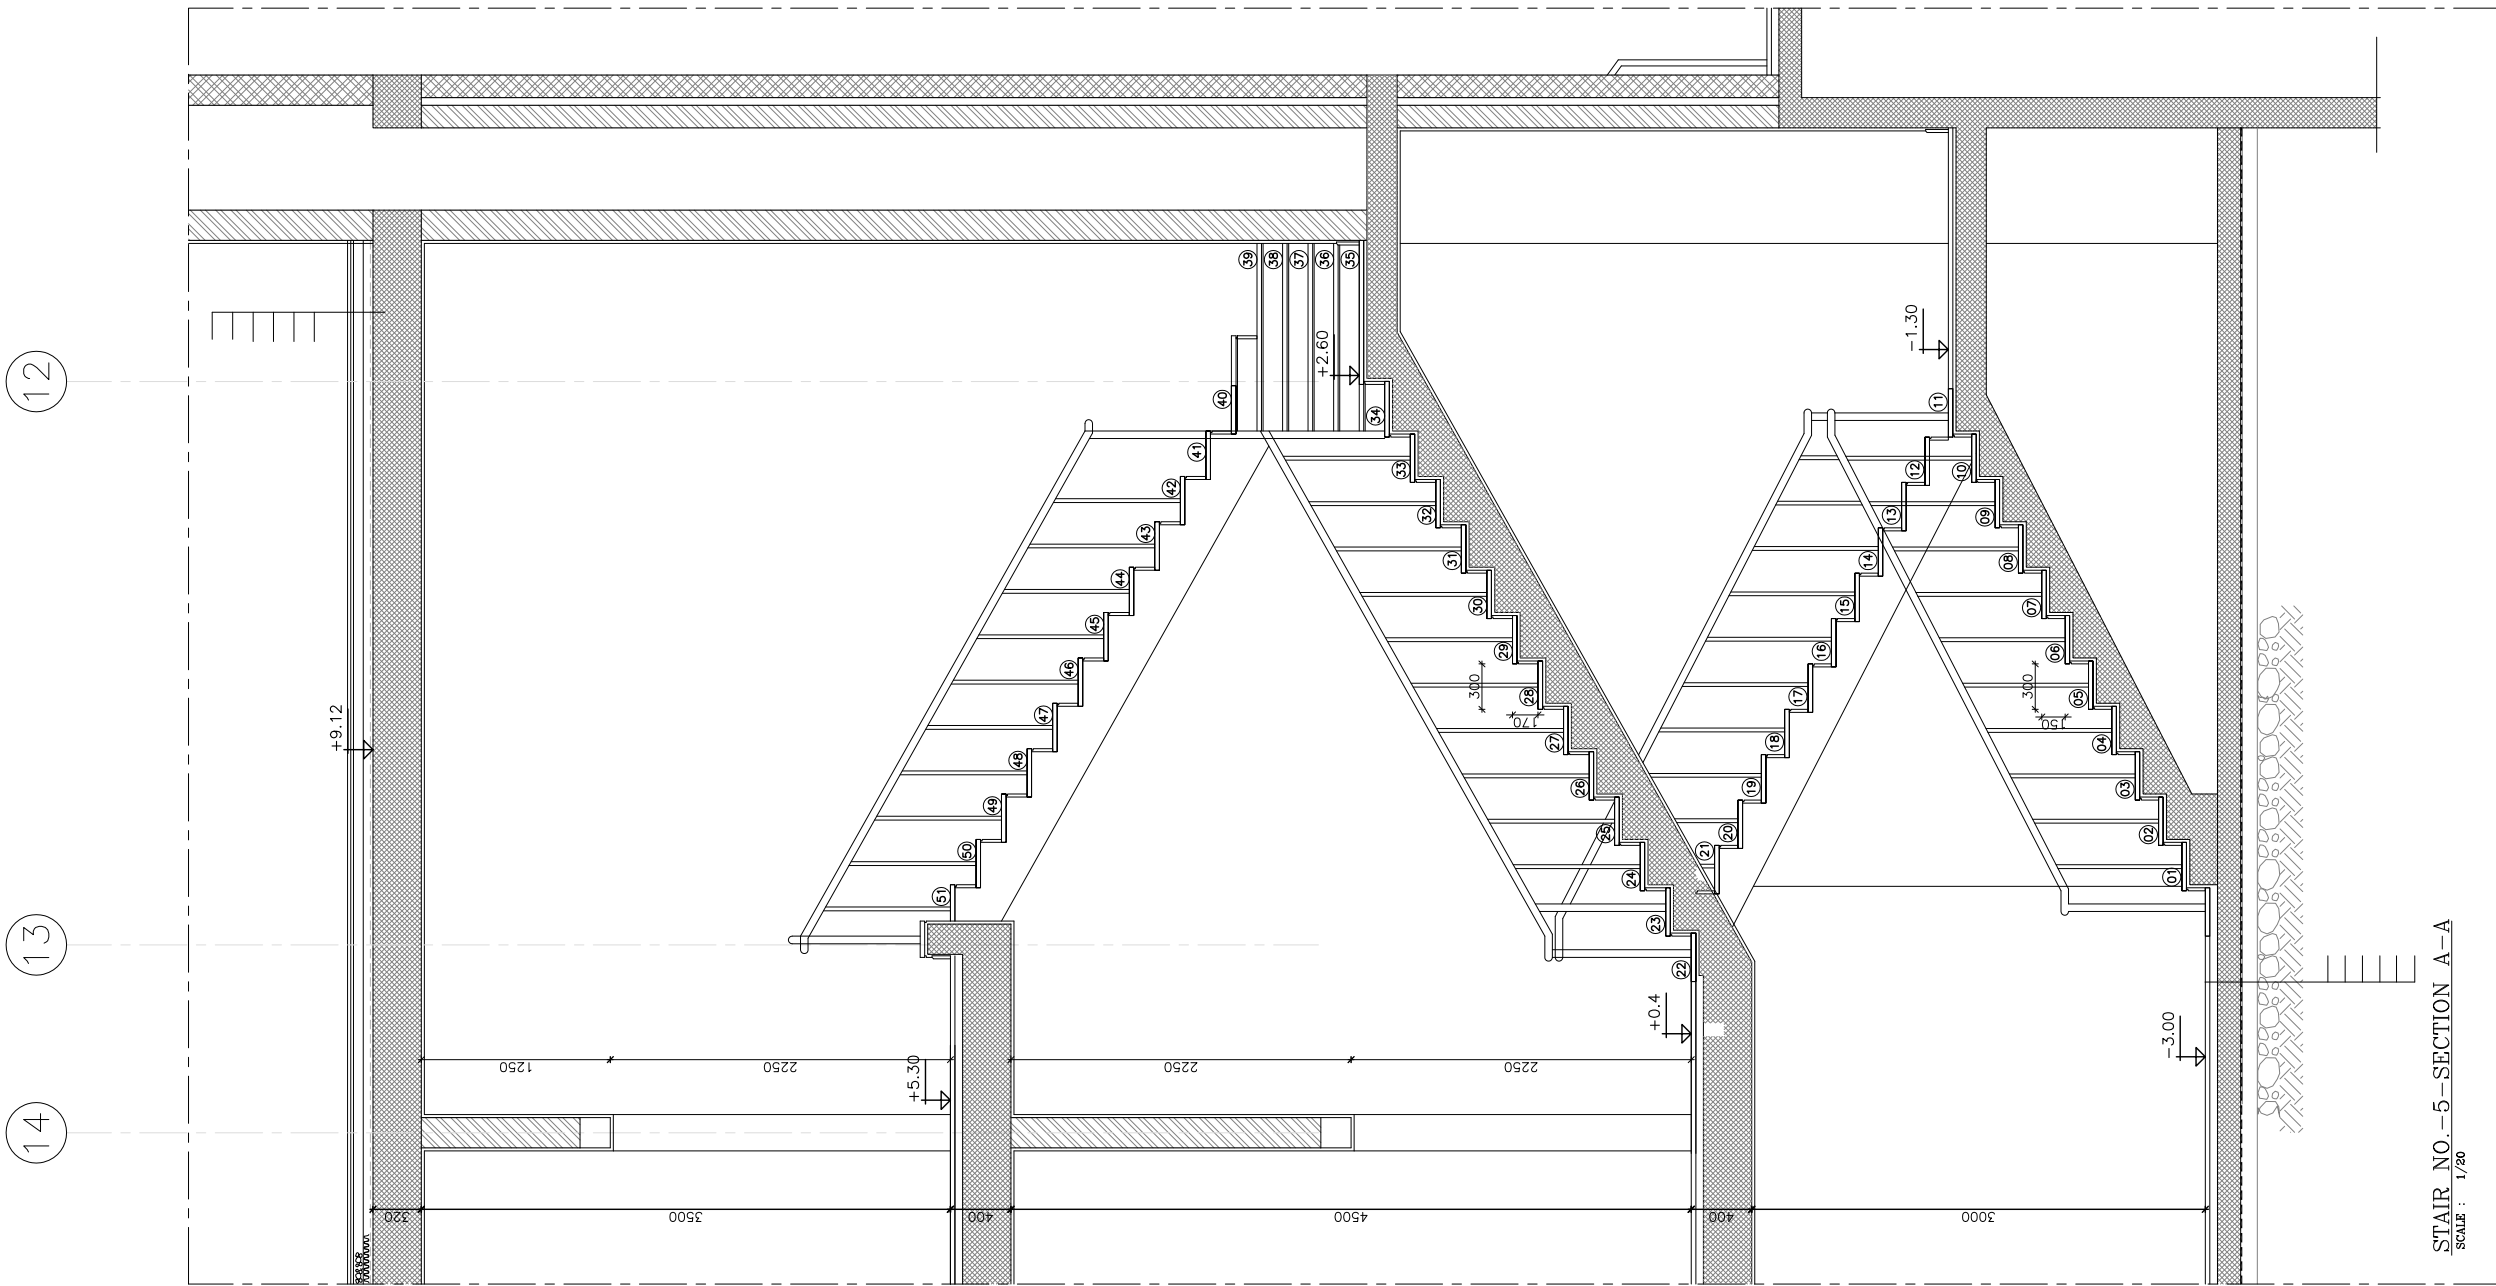

REV.	DATE	BY	DESCRIPTION
KEY PLAN			
CONSULTANT			
 النسب للإستشارات الهندسية Proportions Consulting Engineering Tel: 2792277, Fax: 2797722 P.O.Box 75453, Riyadh-11578			
PROJECT			
PRIVATE HOUSING COMPLEX AL NAKHEEL / RIYADH - SAUDI ARABIA			
OWNER			
SHEET TITLE			
ARCHITECTURAL STAIR NO 5			
TENDER DOCUMENTS			
PROJECT NO. :	P0521	STAGE :	WORKING DRAWINGS
DESIGNED BY :	Proportion Group	DRAWN BY :	CAD
DATE :	JAN. 2006	SCALE :	1/25 1/50
A040505 ARCHITECTURAL			REVISION 0

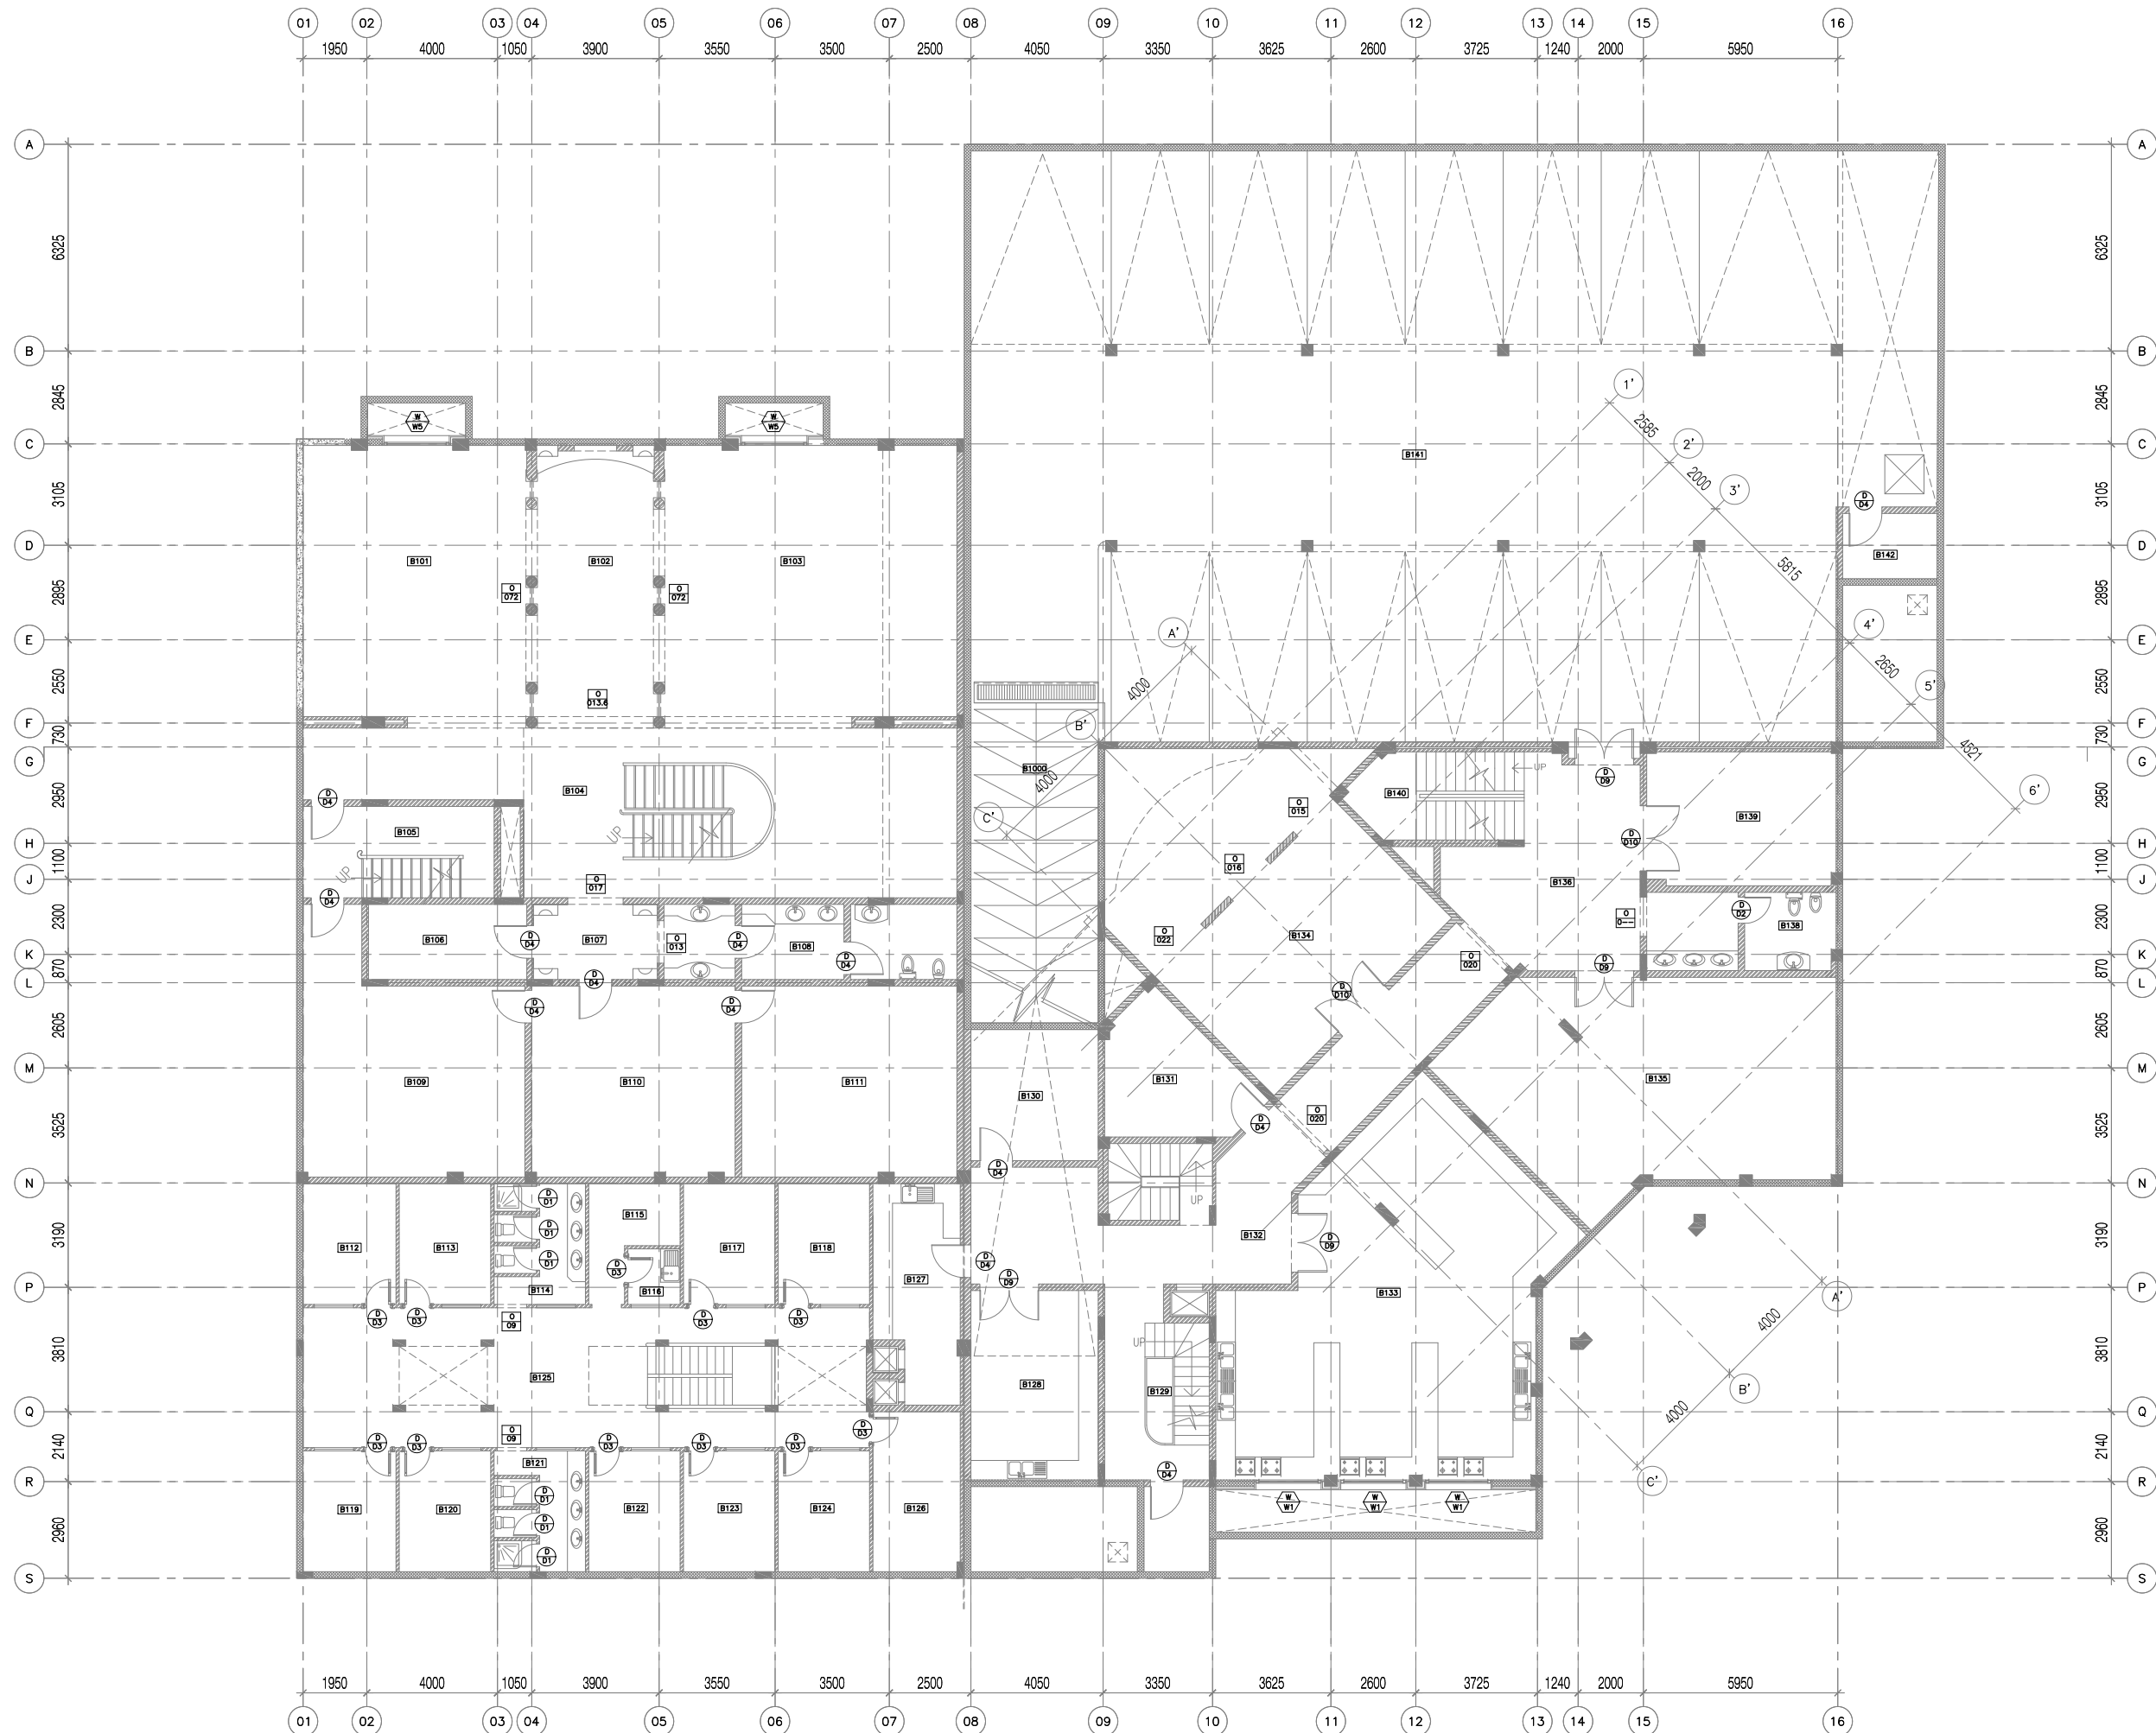

REV.	DATE	BY	DESCRIPTION

KEY PLAN

CONSULTANT

النسب للإستشارات الهندسية
Proportions Consulting Engineering
Tel: 2752277, Fax: 2757722 P.O.Box 75453, Riyadh-11578

PROJECT

PRIVATE HOUSING COMPLEX
AL NAKHEEL / RIYADH - SAUDI ARABIA

OWNER


SHEET TITLE

**ARCHITECTURAL
BASEMENT FLOOR PLAN
ANNOTATION LAYOUT**



TENDER DOCUMENTS			
PROJECT NO. :	P0521	STAGE :	WORKING DRAWINGS
DESIGNED BY :	Proportion Group	DRAWN BY :	CAD
DATE :	JAN. 2008	SCALE :	1:100M

A050001
ARCHITECTURAL



REVISION
0

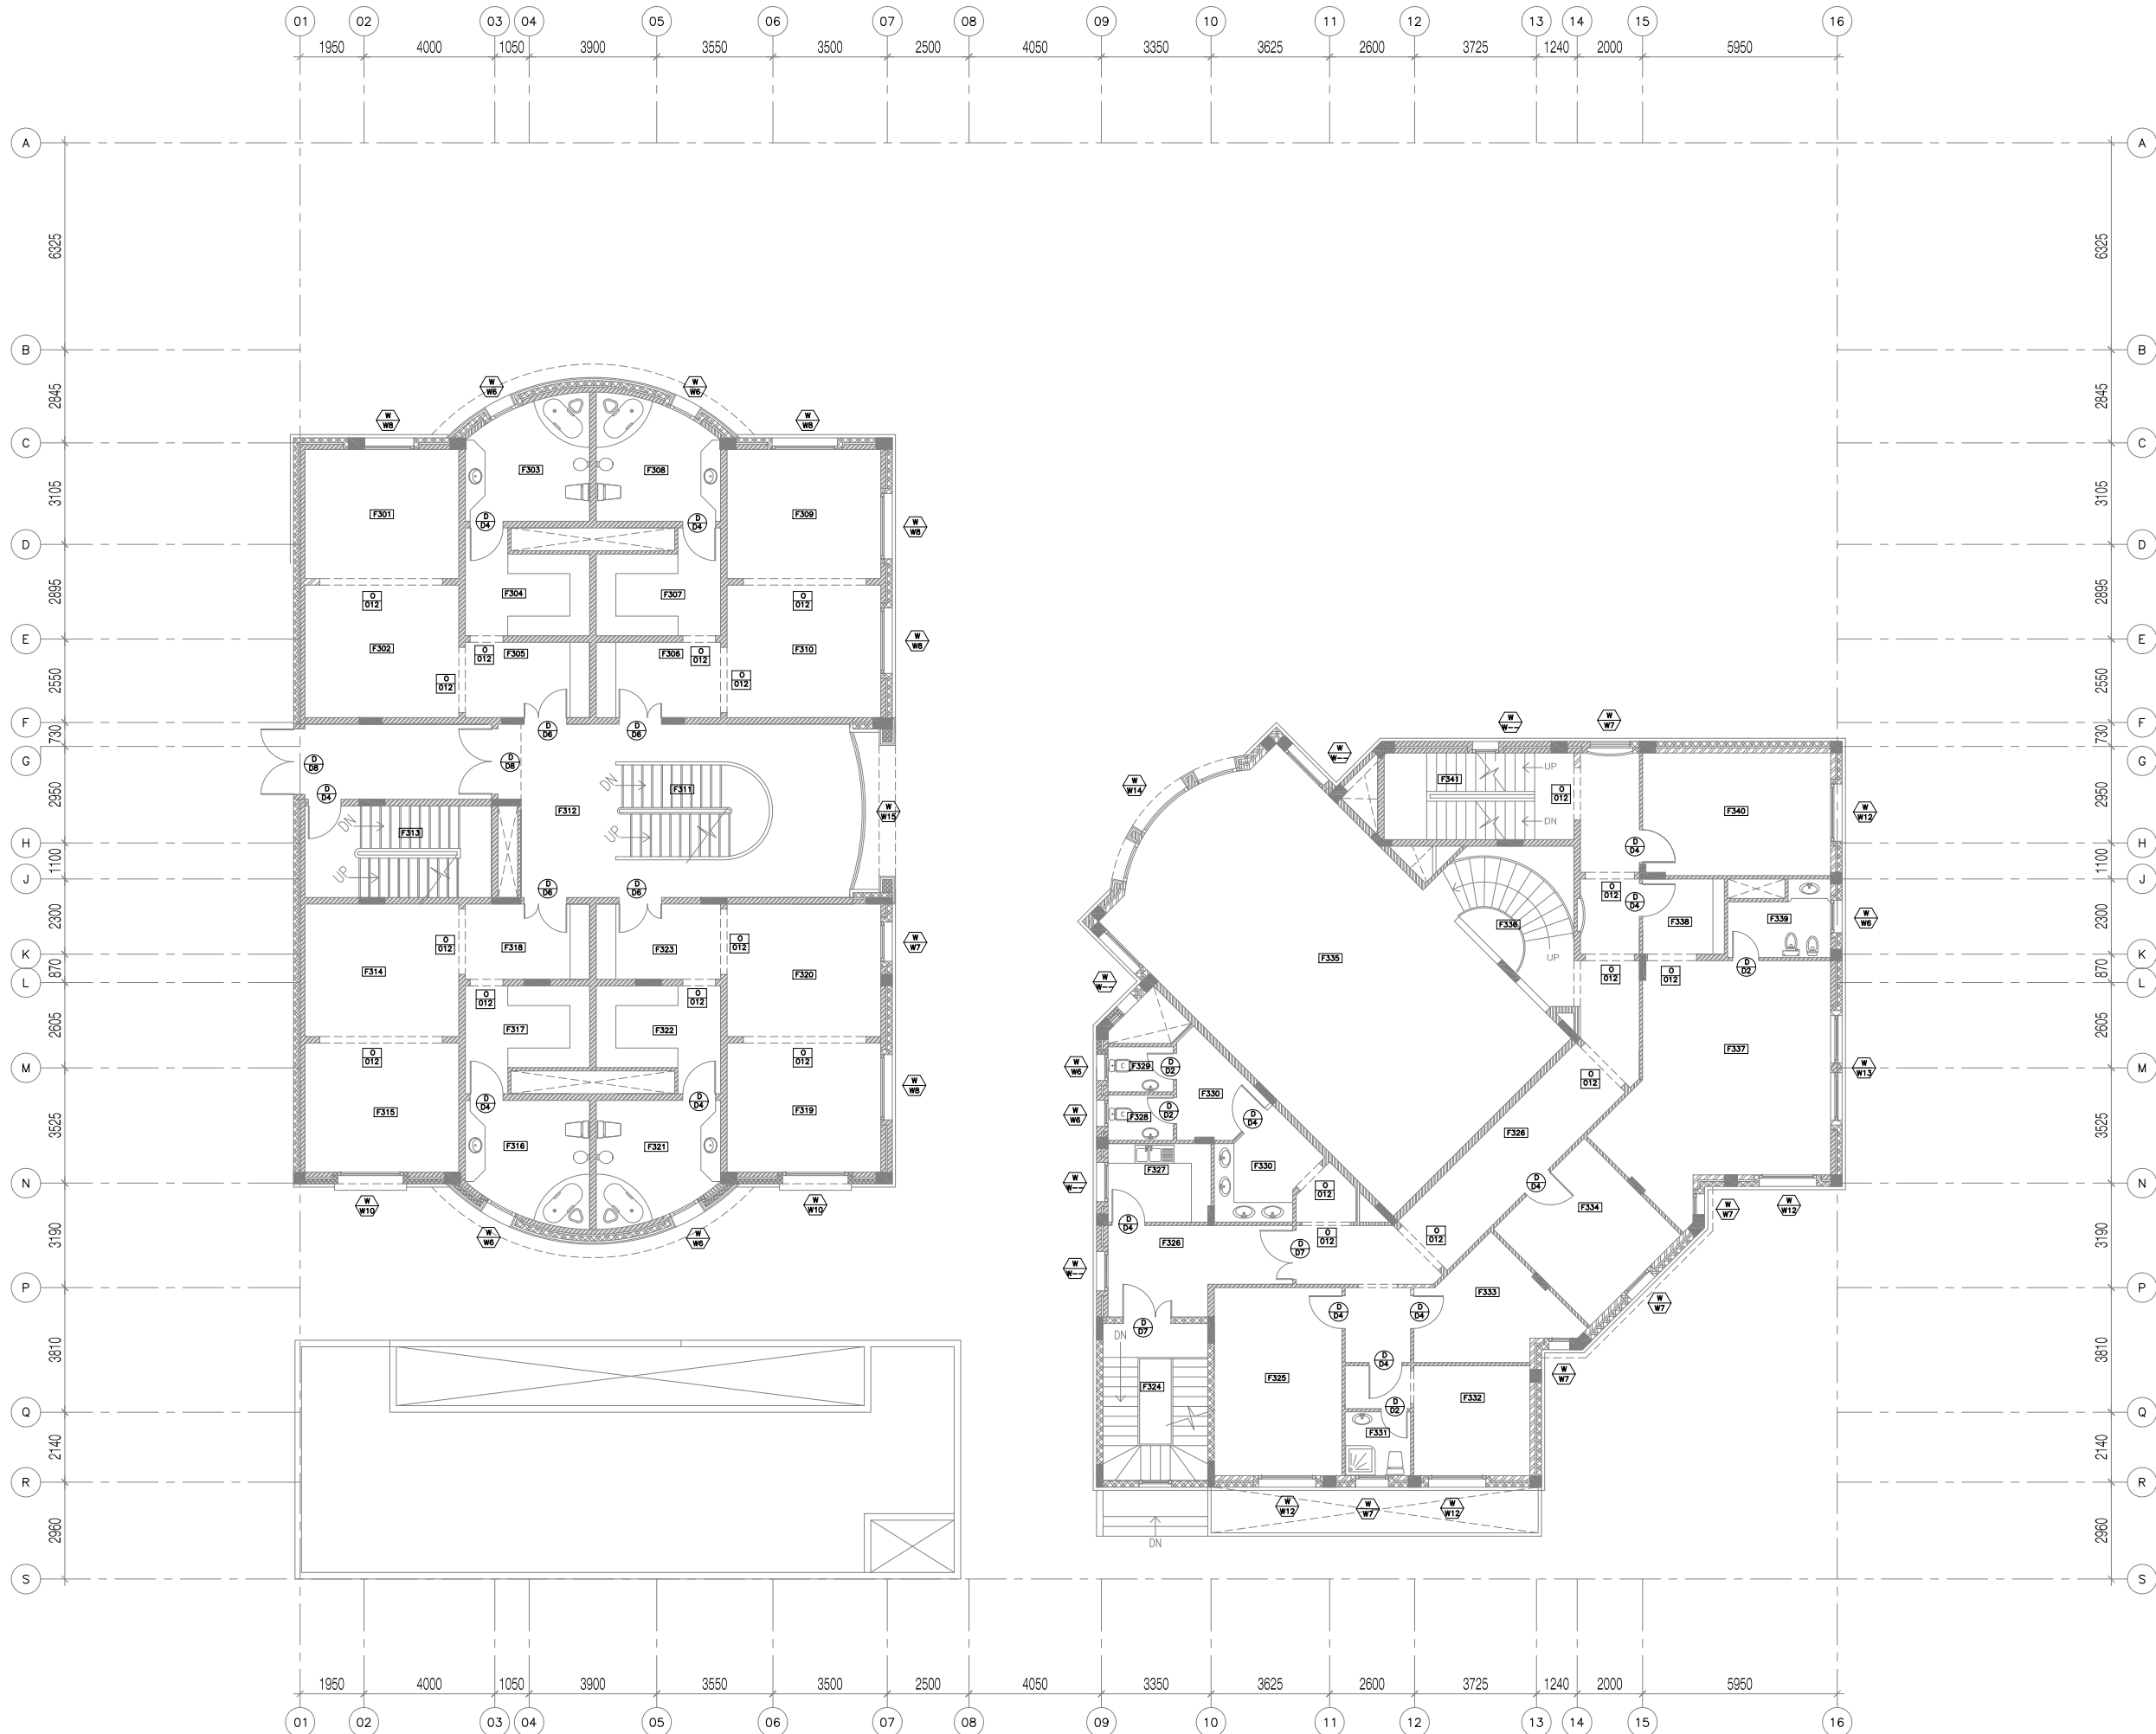

REV.	DATE	BY	DESCRIPTION
KEY PLAN			
CONSULTANT			
 النسب للإستشارات الهندسية Proportions Consulting Engineering Tel: 2752277, Fax: 2757722 P.O.Box 75453, Riyadh-11578			
PROJECT			
PRIVATE HOUSING COMPLEX AL NAKHEEL / RIYADH - SAUDI ARABIA			
OWNER			
SHEET TITLE			
ARCHITECTURAL FIRST FLOOR PLAN ANNOTATION LAYOUT			
TENDER DOCUMENTS			
PROJECT NO. :	P0521	STAGE :	WORKING DRAWINGS
DESIGNED BY :	Proportion Group	DRAWN BY :	CAD
DATE :	JAN. 2008	SCALE :	1:100M
A050201 ARCHITECTURAL			REVISION 0

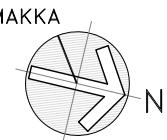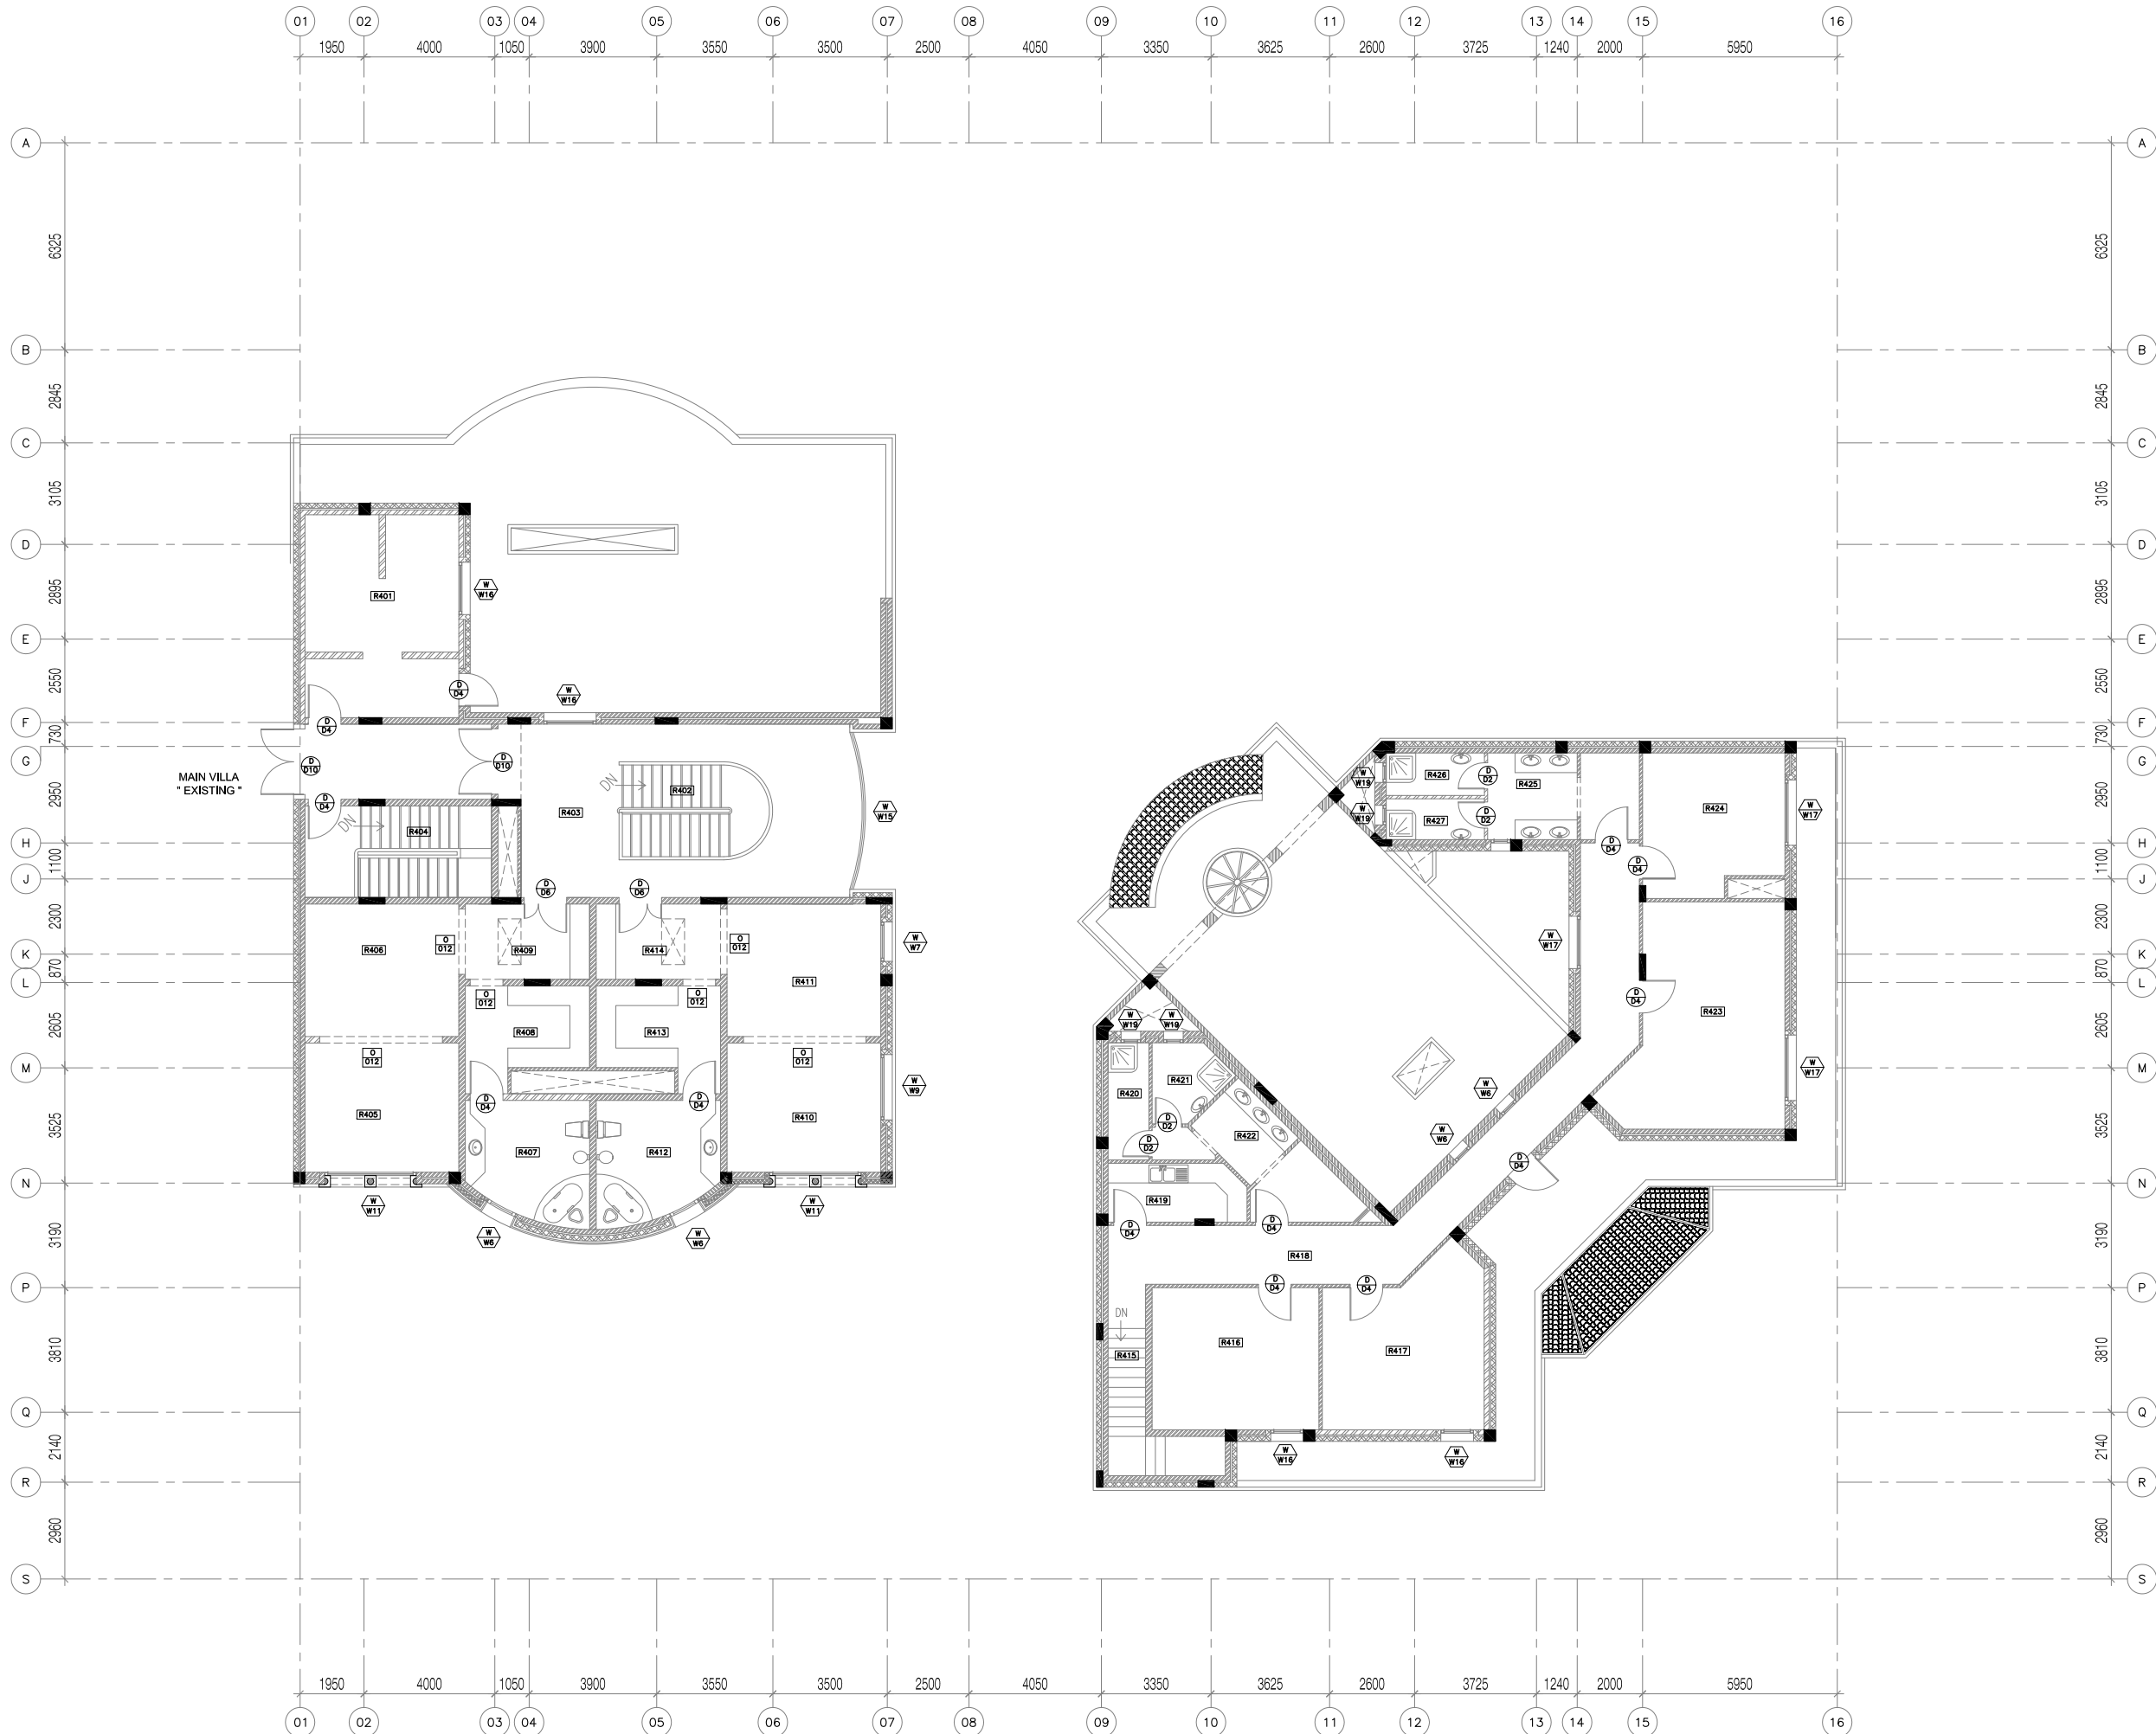

REV. DATE BY DESCRIPTION			
KEY PLAN			
CONSULTANT			
 النسب للاستشارات الهندسية Proportions Consulting Engineering Tel: 2752277, Fax: 2757722 P.O.Box 75453, Riyadh-11578			
PROJECT			
PRIVATE HOUSING COMPLEX AL NAKHEEL / RIYADH - SAUDI ARABIA			
OWNER			
SHEET TITLE			
ARCHITECTURAL R40F FLOOR PLAN ANNOTATION LAYOUT			
TENDER DOCUMENTS			
PROJECT NO. :	P0521	STAGE :	WORKING DRAWINGS
DESIGNED BY :	PR4aportion GR4up	DRAWN BY :	CAD
DATE :	JAN. 2008	SCALE :	1:100M
A050301 ARCHITECTURAL			REVISION 0

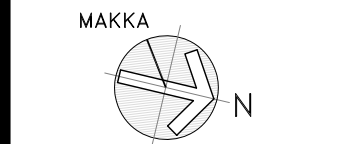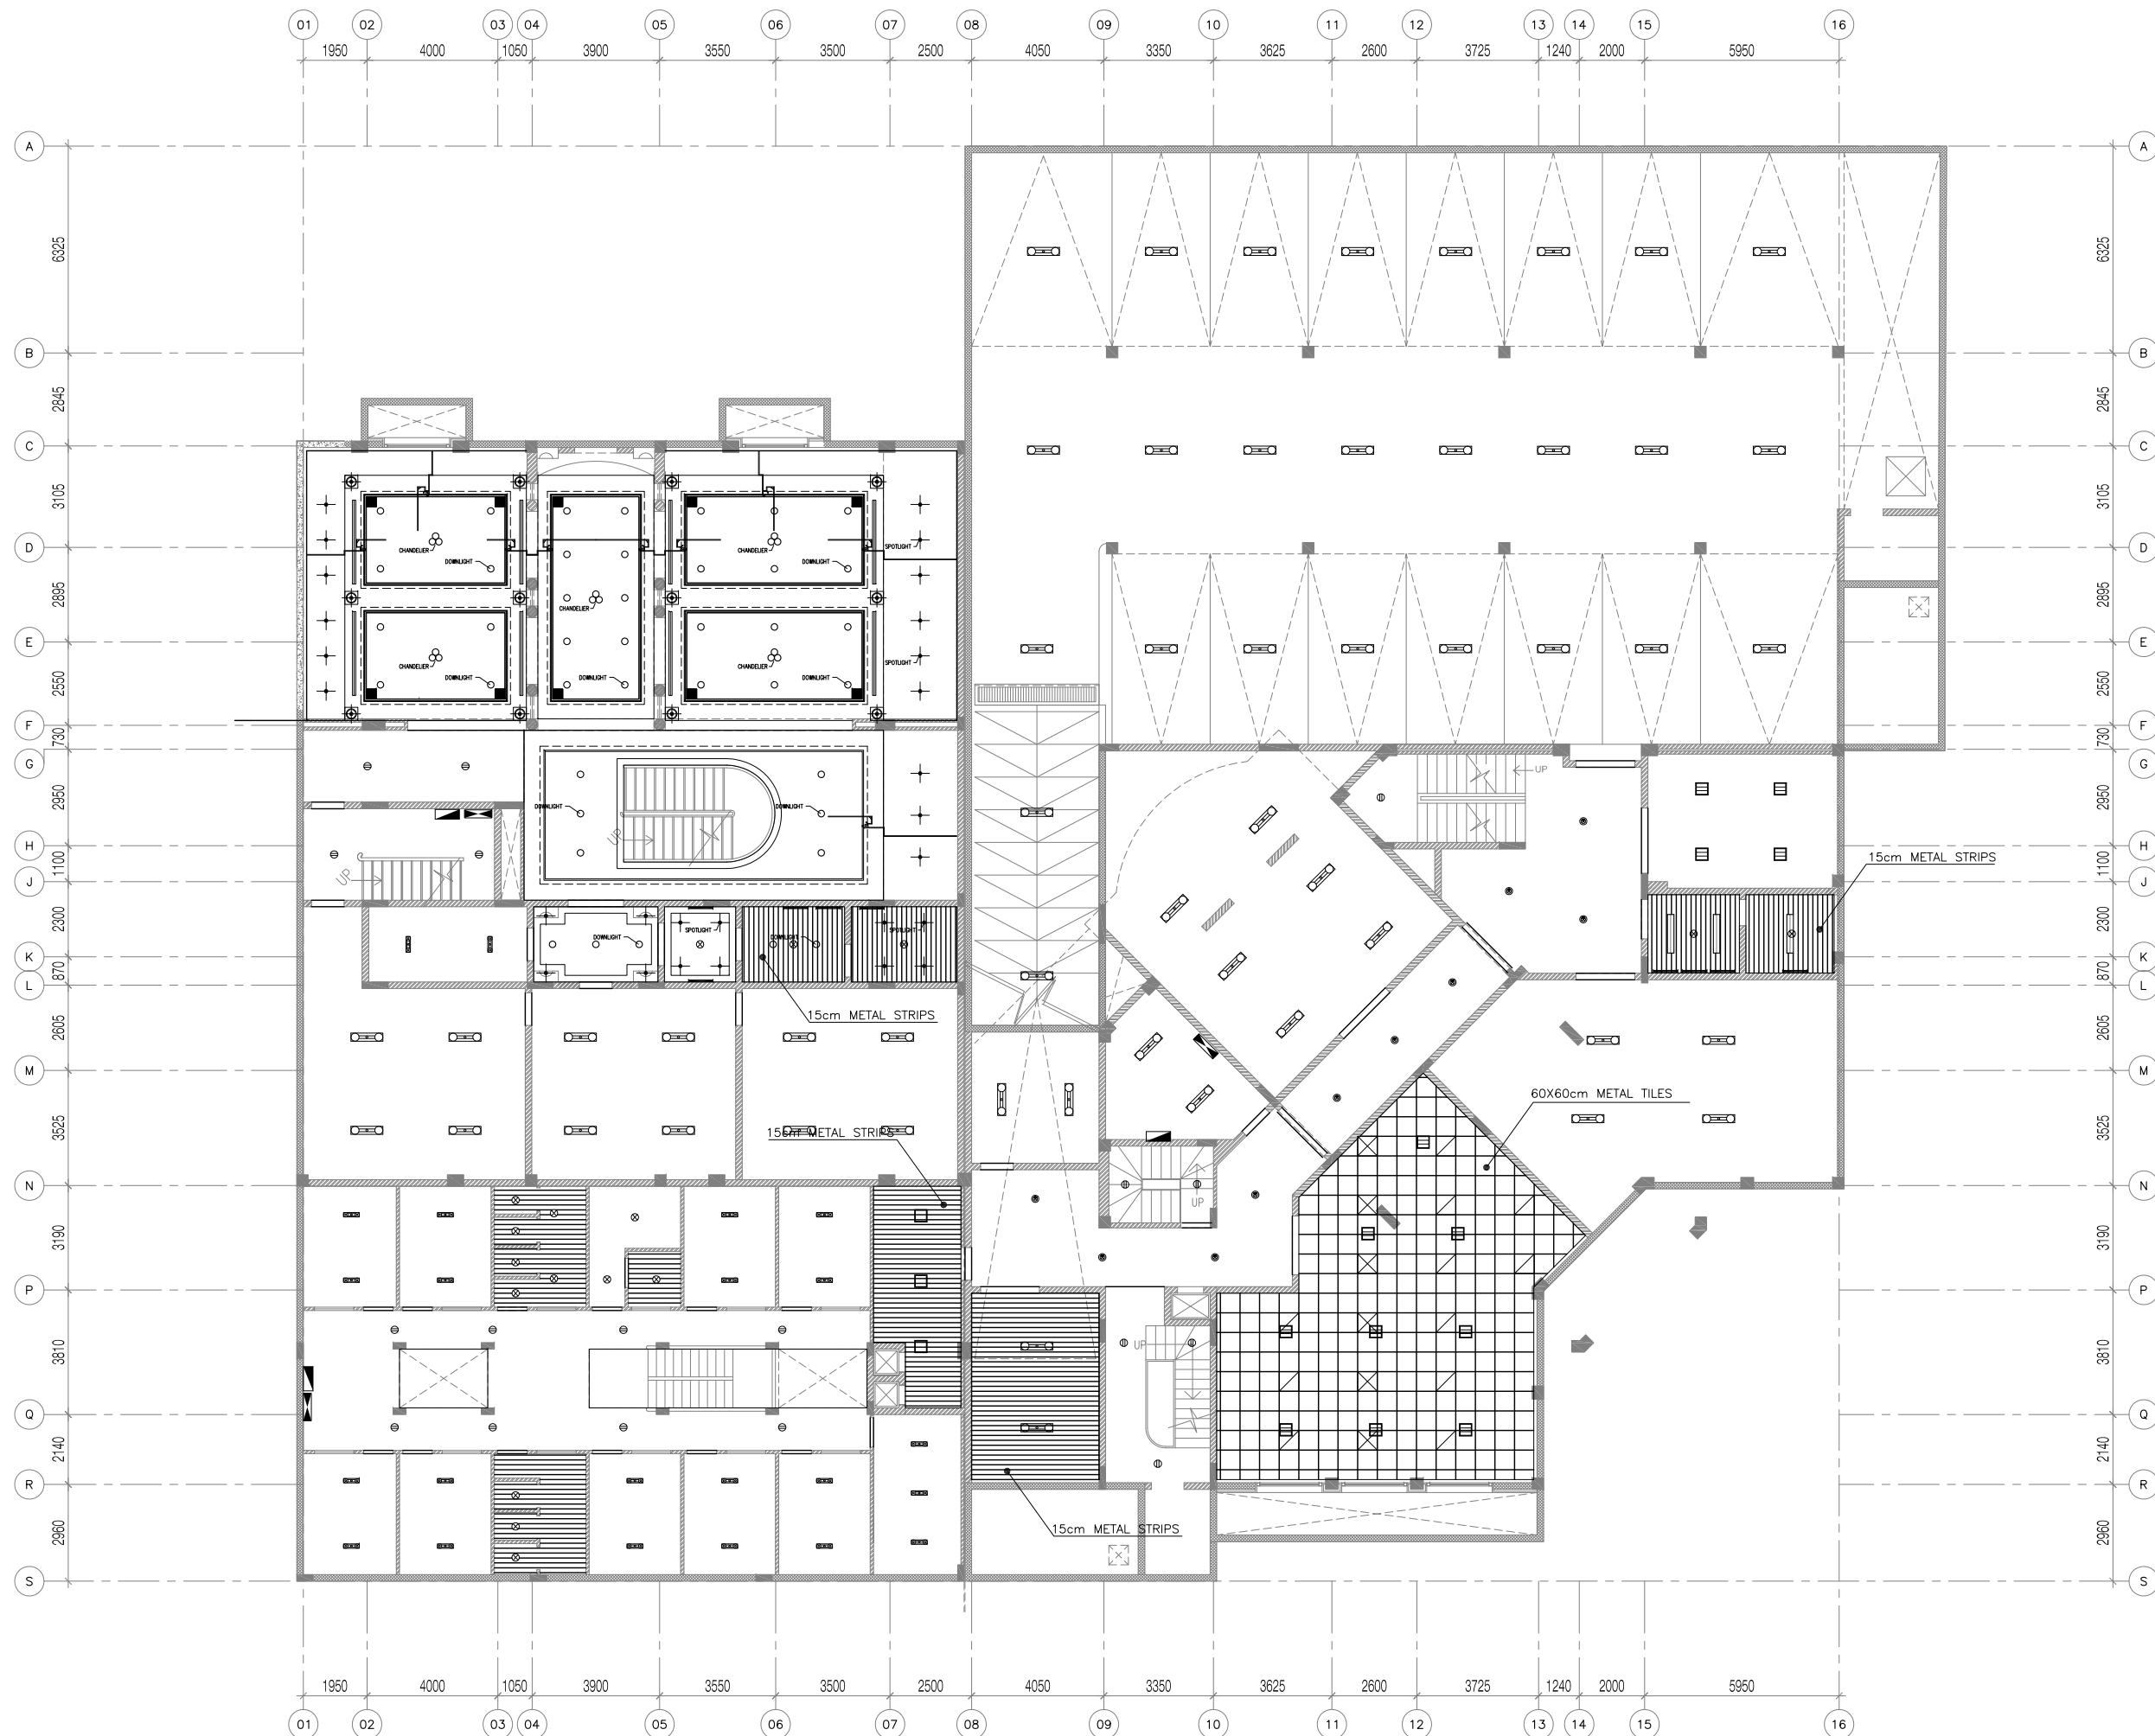

- * ACTUAL DIMENSIONS MUST BE VERIFIED FROM SITE.
- * C.H.=CEILING HEIGHT.
- * S.P.=STARTING POINT (FOR GYPSUM GRIDS).
- * CL= CENTER LINE.
- * GYPSUM BOARD.
- * (60X60cm) PERFORATED METAL TILE
- * (8)HALOGEN SPOT LIGHT.
- * COMPACTED FLORESCENT LIGHT
- * L.S.G.= LINEAR SUPPLY GRILL.
- * L.R.G.=LINEAR RETURN GRILL.
- * SUPPLY DIFFUSER.
- * RETURN DIFFUSER.
- * 60X60 FLORESCENT LIGHT
- * FLORESCENT LIGHT
- * CHANDELIER

REV.	DATE	BY	DESCRIPTION

KEY PLAN



PROJECT

PRIVATE HOUSING COMPLEX
AL NAKHEEL / RIYADH - SAUDI ARABIA

OWNER

SHEET TITLE

ARCHITECTURAL
GROUND FLOOR PLAN
REFLECTED CEILING LAYOUT

TENDER DOCUMENTS



PROJECT NO. :	P0521	STAGE :	WORKING DRAWINGS
DESIGNED BY :	Proportion Group	DRAWN BY :	CAD
DATE :	JAN. 2008	SCALE :	1:100M

A060001
ARCHITECTURAL

REVISION
0

1
A060001

BASEMENT FLOOR PLAN REFLECTED CEILING LAYOUT
SCALE: 1:100 M.

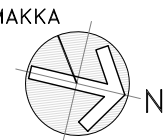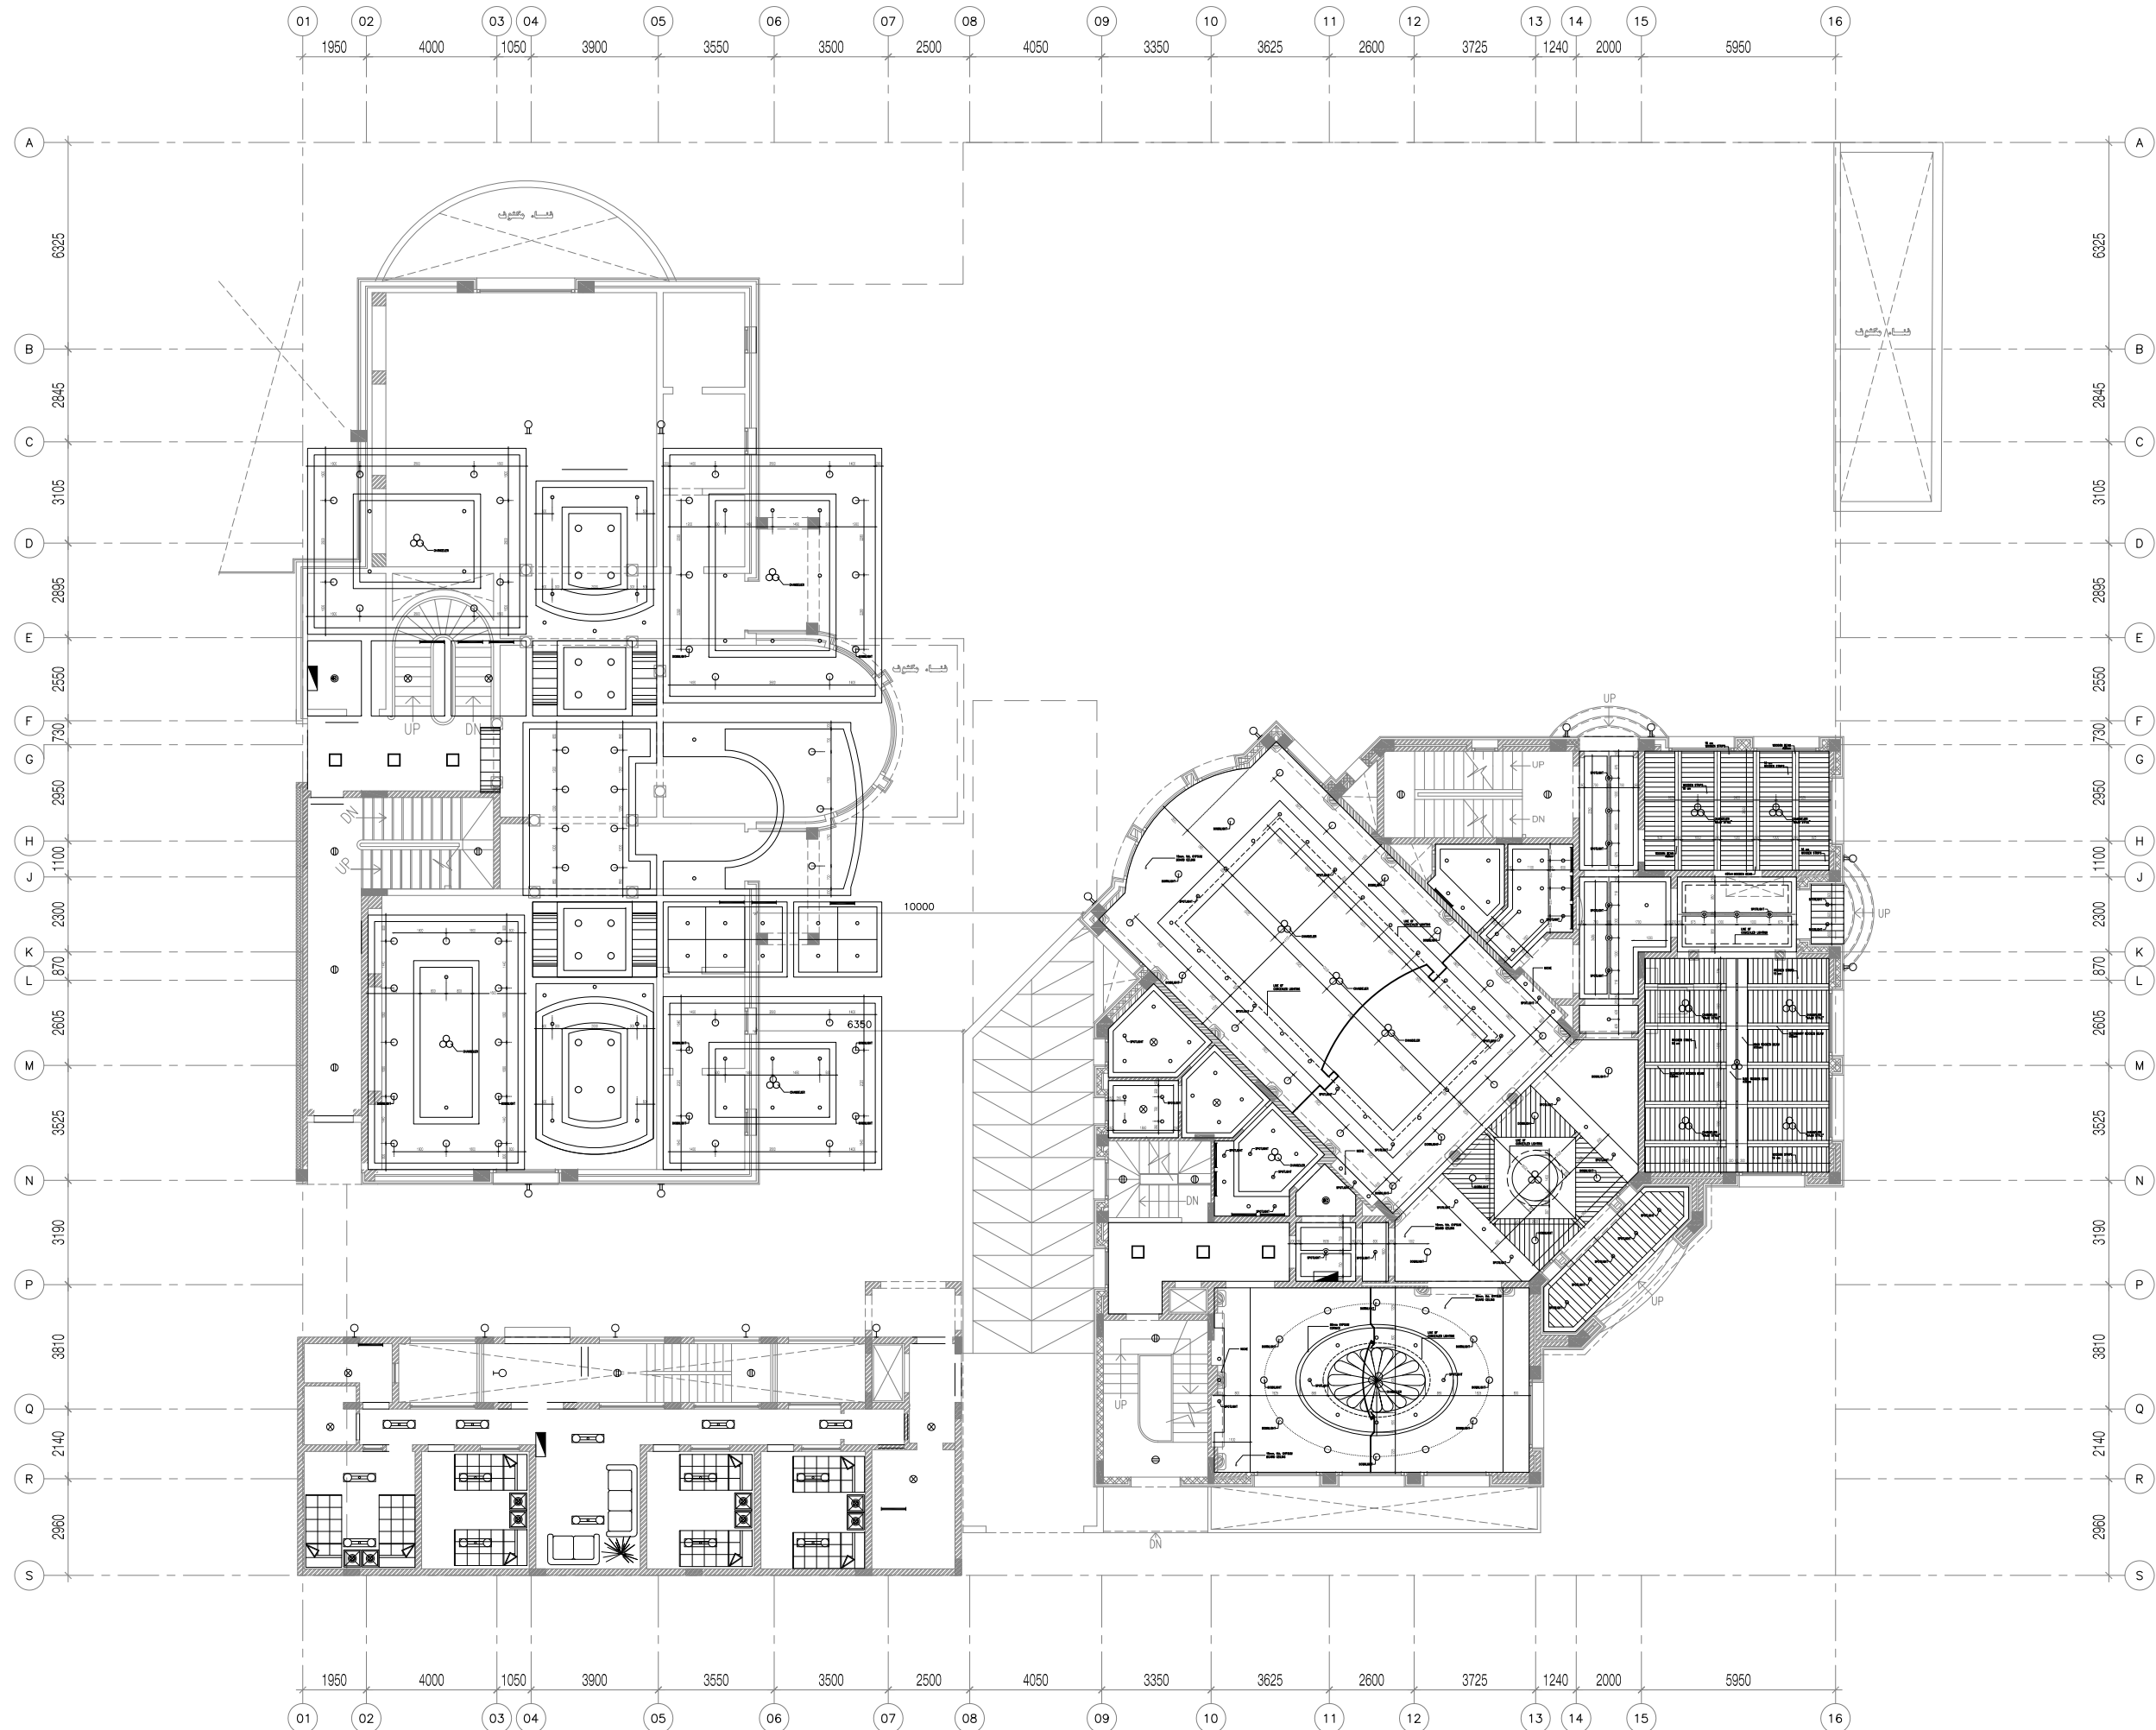

1 GROUND FLOOR PLAN REFLECTED CEILING LAYOUT
A060101 SCALE: 1:100 M.

REV.	DATE	BY	DESCRIPTION

KEY PLAN

CONSULTANT

النسب للإستشارات الهندسية
Proportions Consulting Engineering
Tel: 2792277, Fax: 2797722 P.O.Box 75453, Riyadh-11578

PROJECT

PRIVATE HOUSING COMPLEX
AL NAKHEEL / RIYADH - SAUDI ARABIA

OWNER

SHEET TITLE


ARCHITECTURAL
GROUND FLOOR PLAN
REFLECTED CEILING LAYOUT

TENDER DOCUMENTS

PROJECT NO. :	P0521	STAGE :	WORKING DRAWINGS
DESIGNED BY :	Proportion Group	DRAWN BY :	CAD
DATE :	JAN. 2008	SCALE :	1:100M

A060101
ARCHITECTURAL

REVISION
0

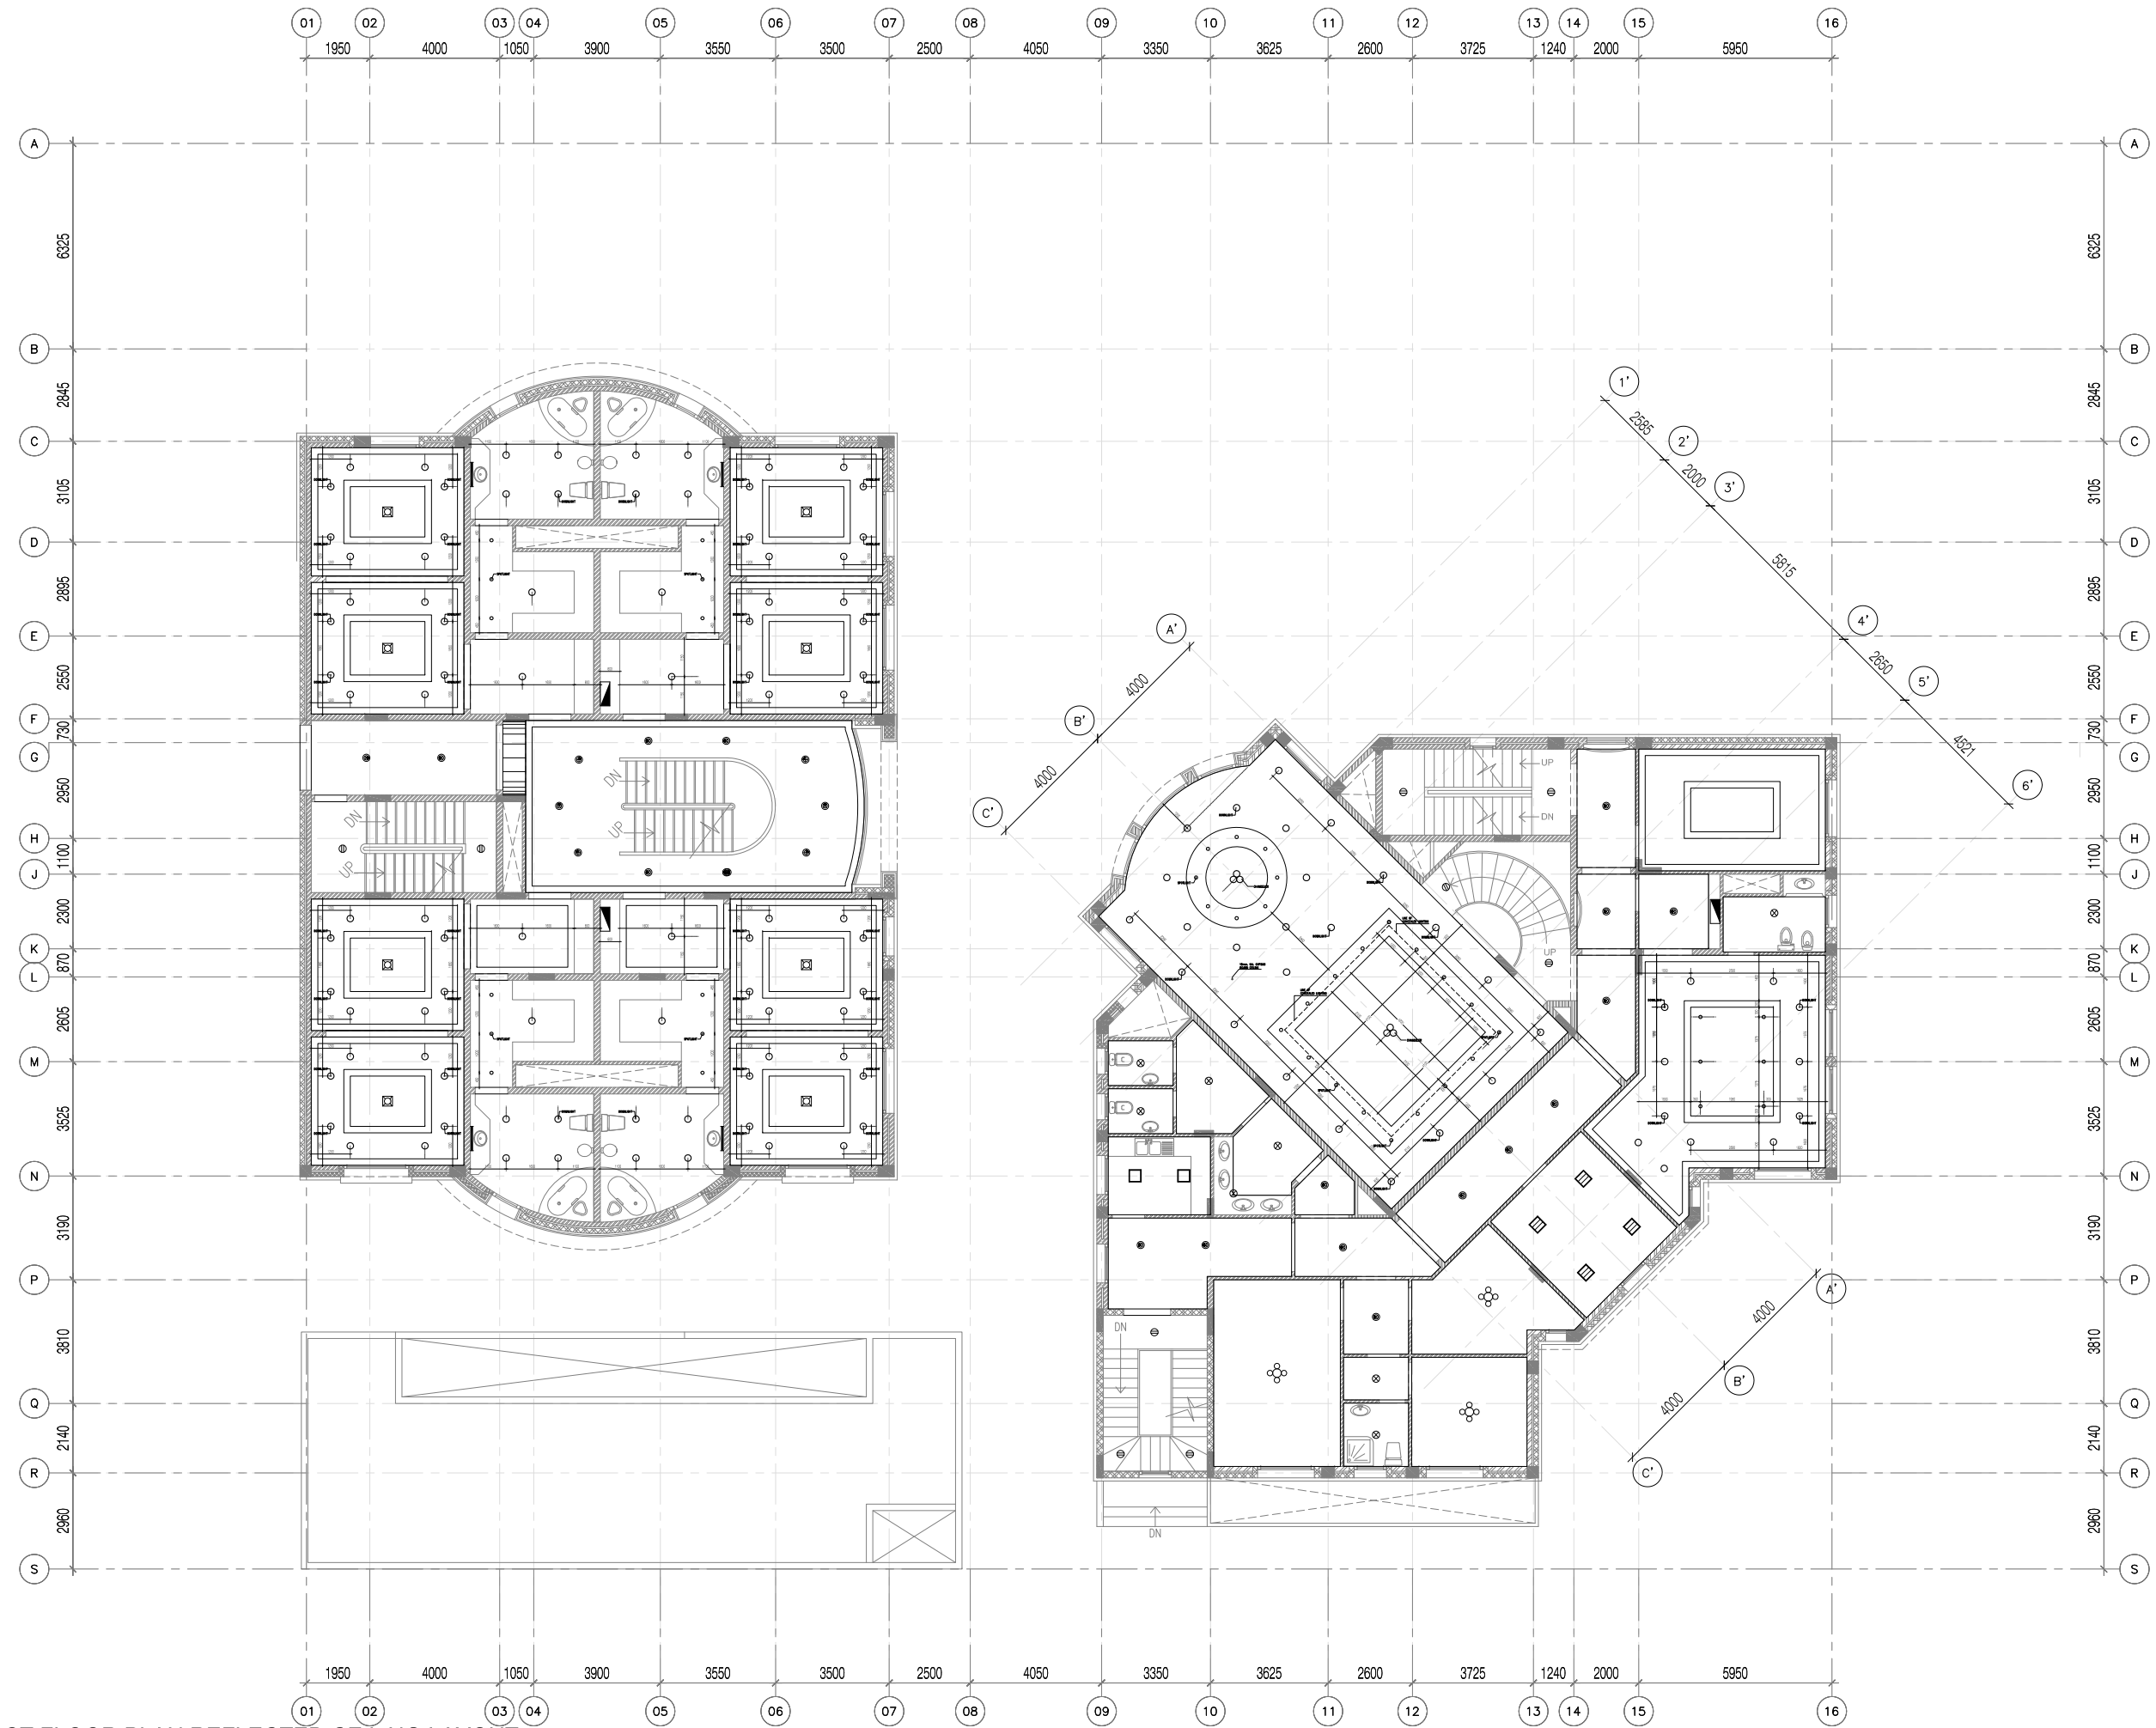

REV.	DATE	BY	DESCRIPTION

KEY PLAN

CONSULTANT

النسب للإستشارات الهندسية
Proportions Consulting Engineering
Tel: 2792277, Fax: 2797722 P.O.Box 75453, Riyadh-11578

PROJECT

PRIVATE HOUSING COMPLEX
AL NAKHEEL / RIYADH - SAUDI ARABIA

OWNER


SHEET TITLE

**ARCHITECTURAL
FIRST FLOOR PLAN
TILING LAYOUT**


TENDER DOCUMENTS			
PROJECT NO. :	P0521	STAGE :	WORKING DRAWINGS
DESIGNED BY :	Proportion Group	DRAWN BY :	CAD
DATE :	JAN. 2008	SCALE :	1:100M

A060201
ARCHITECTURAL


REVISION
0

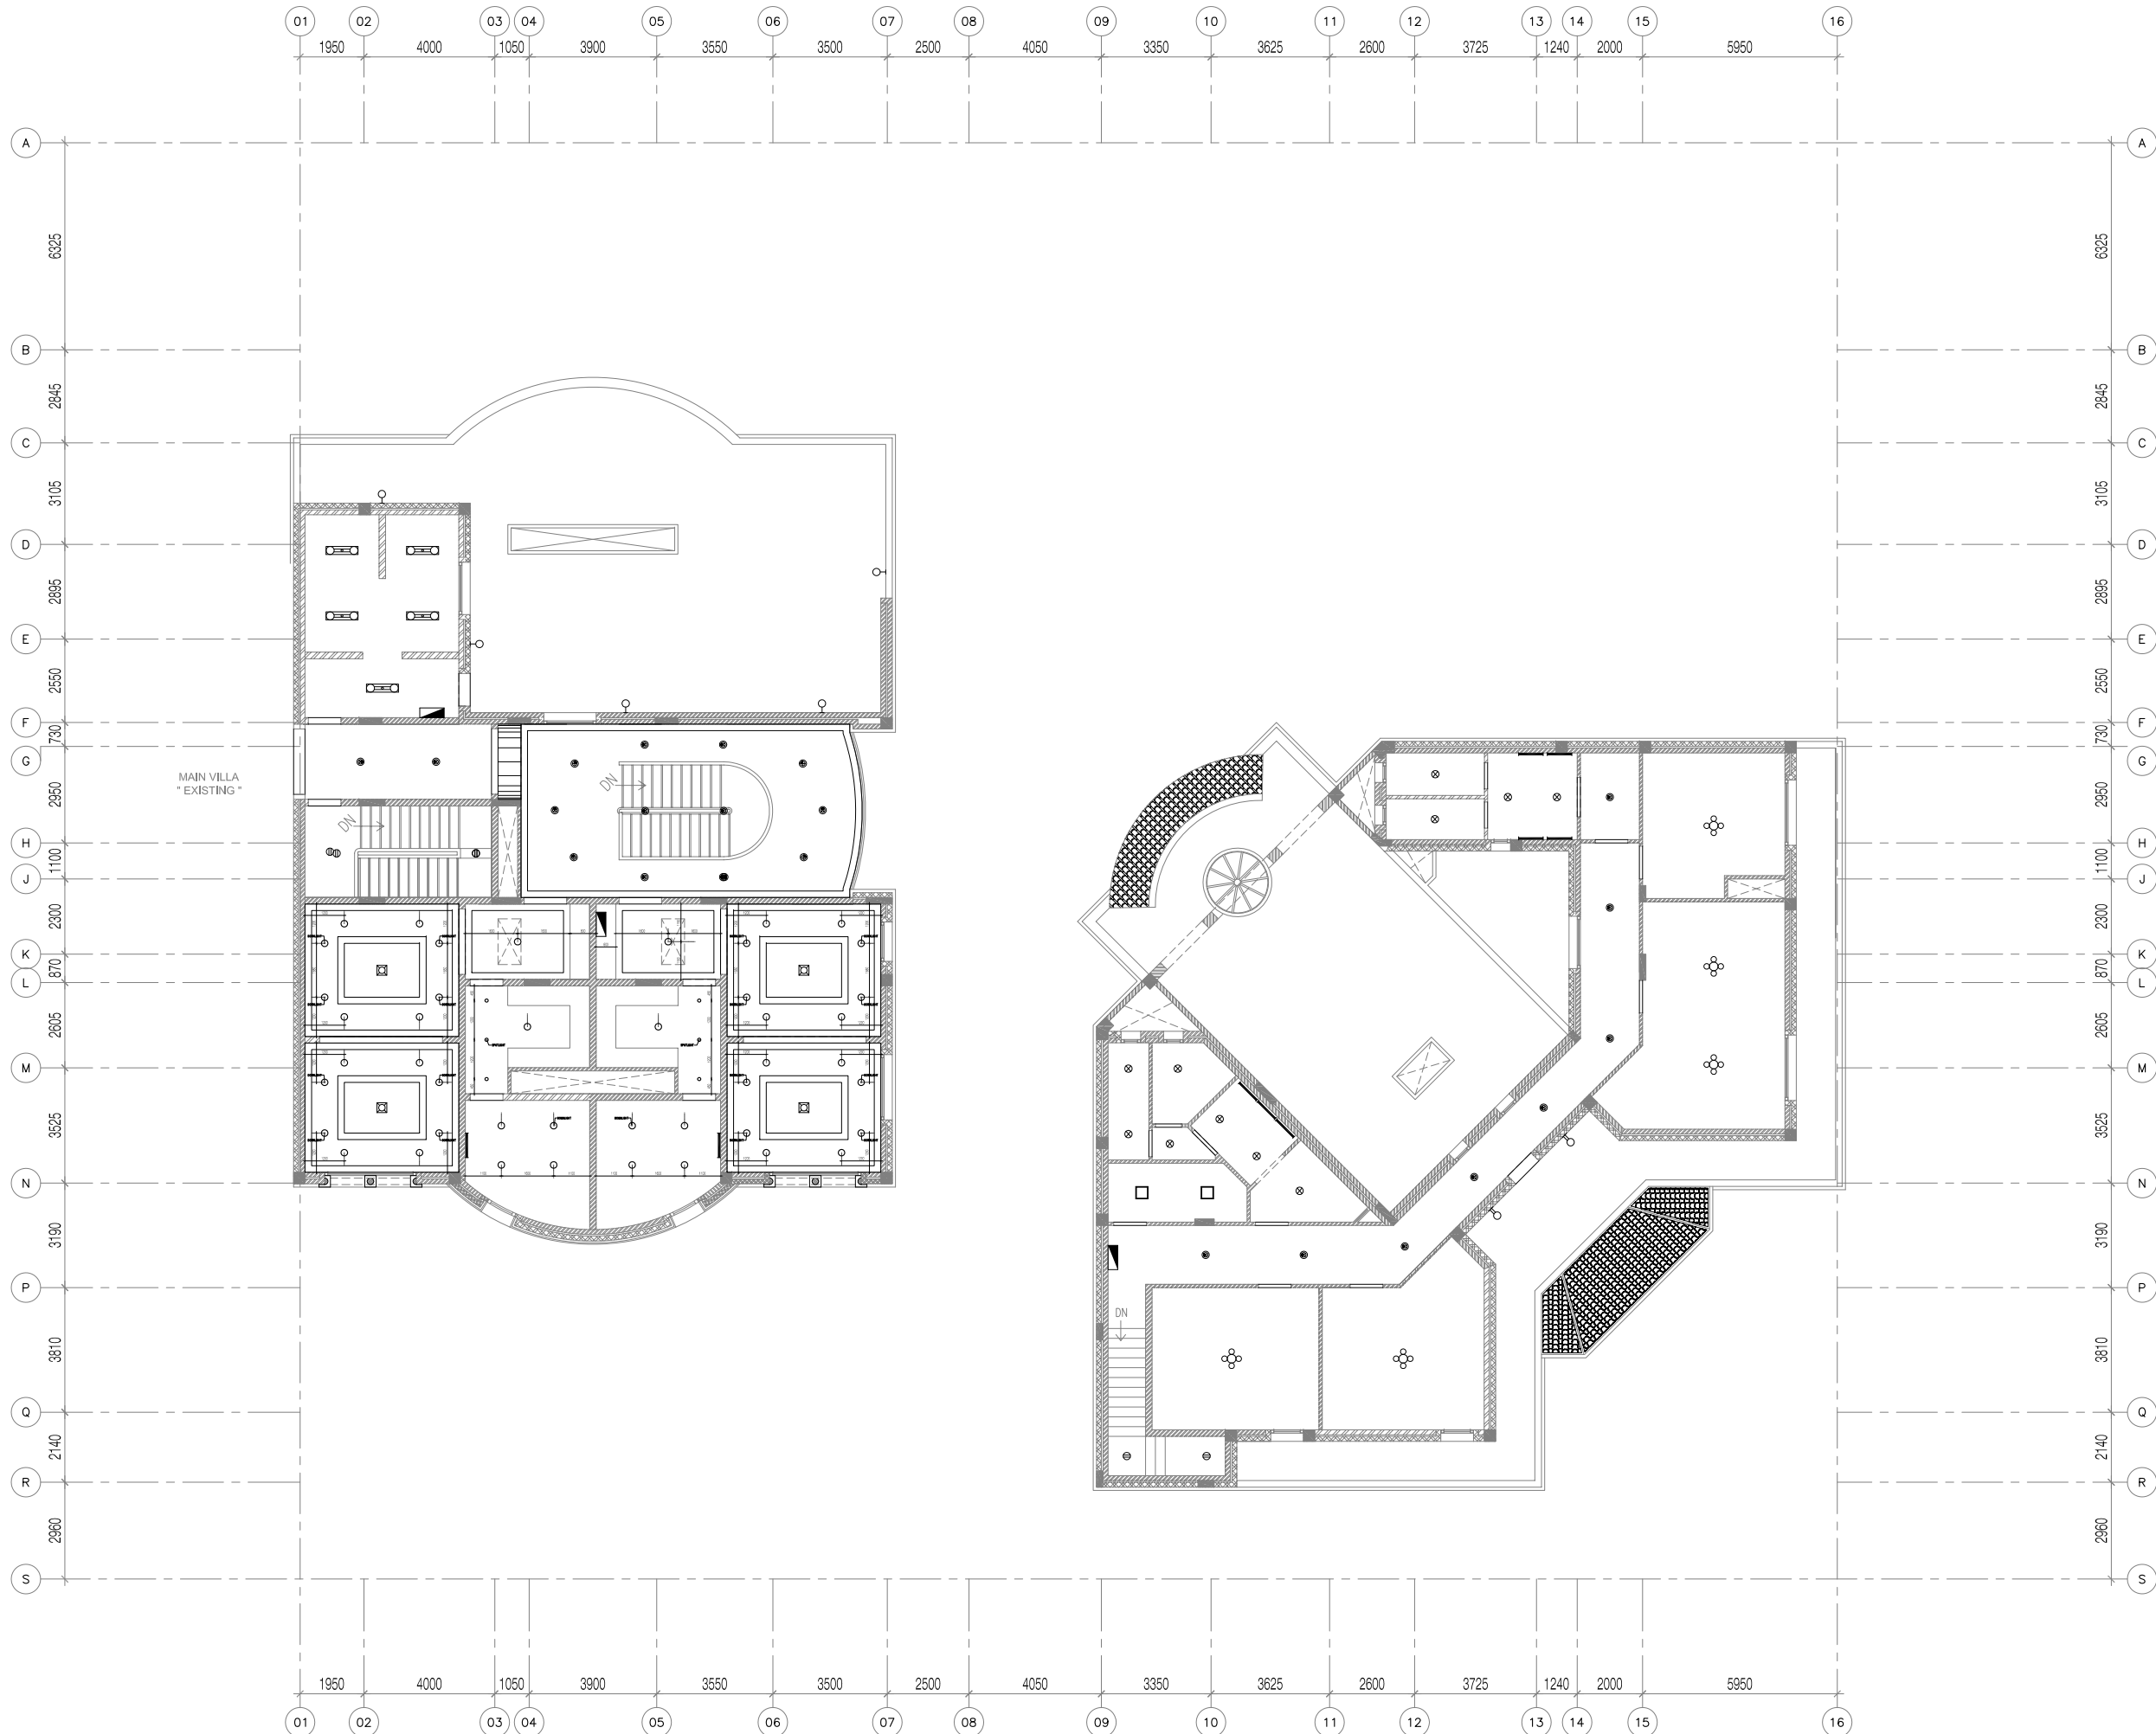


REV.	DATE	BY	DESCRIPTION
KEY PLAN			
CONSULTANT			
 النسب للإستشارات الهندسية Proportions Consulting Engineering Tel: 2792277, Fax: 2797722 P.O.Box 75453, Riyadh-11578			
PROJECT			
PRIVATE HOUSING COMPLEX AL NAKHEEL / RIYADH - SAUDI ARABIA			
OWNER			
SHEET TITLE			
ARCHITECTURAL ROOF FLOOR PLAN TILING LAYOUT			
TENDER DOCUMENTS			
PROJECT NO. :	P0521	STAGE :	WORKING DRAWINGS
DESIGNED BY :	Proportion Group	DRAWN BY :	CAD
DATE :	JAN. 2008	SCALE :	1:100M
A070301 ARCHITECTURAL			REVISION 0

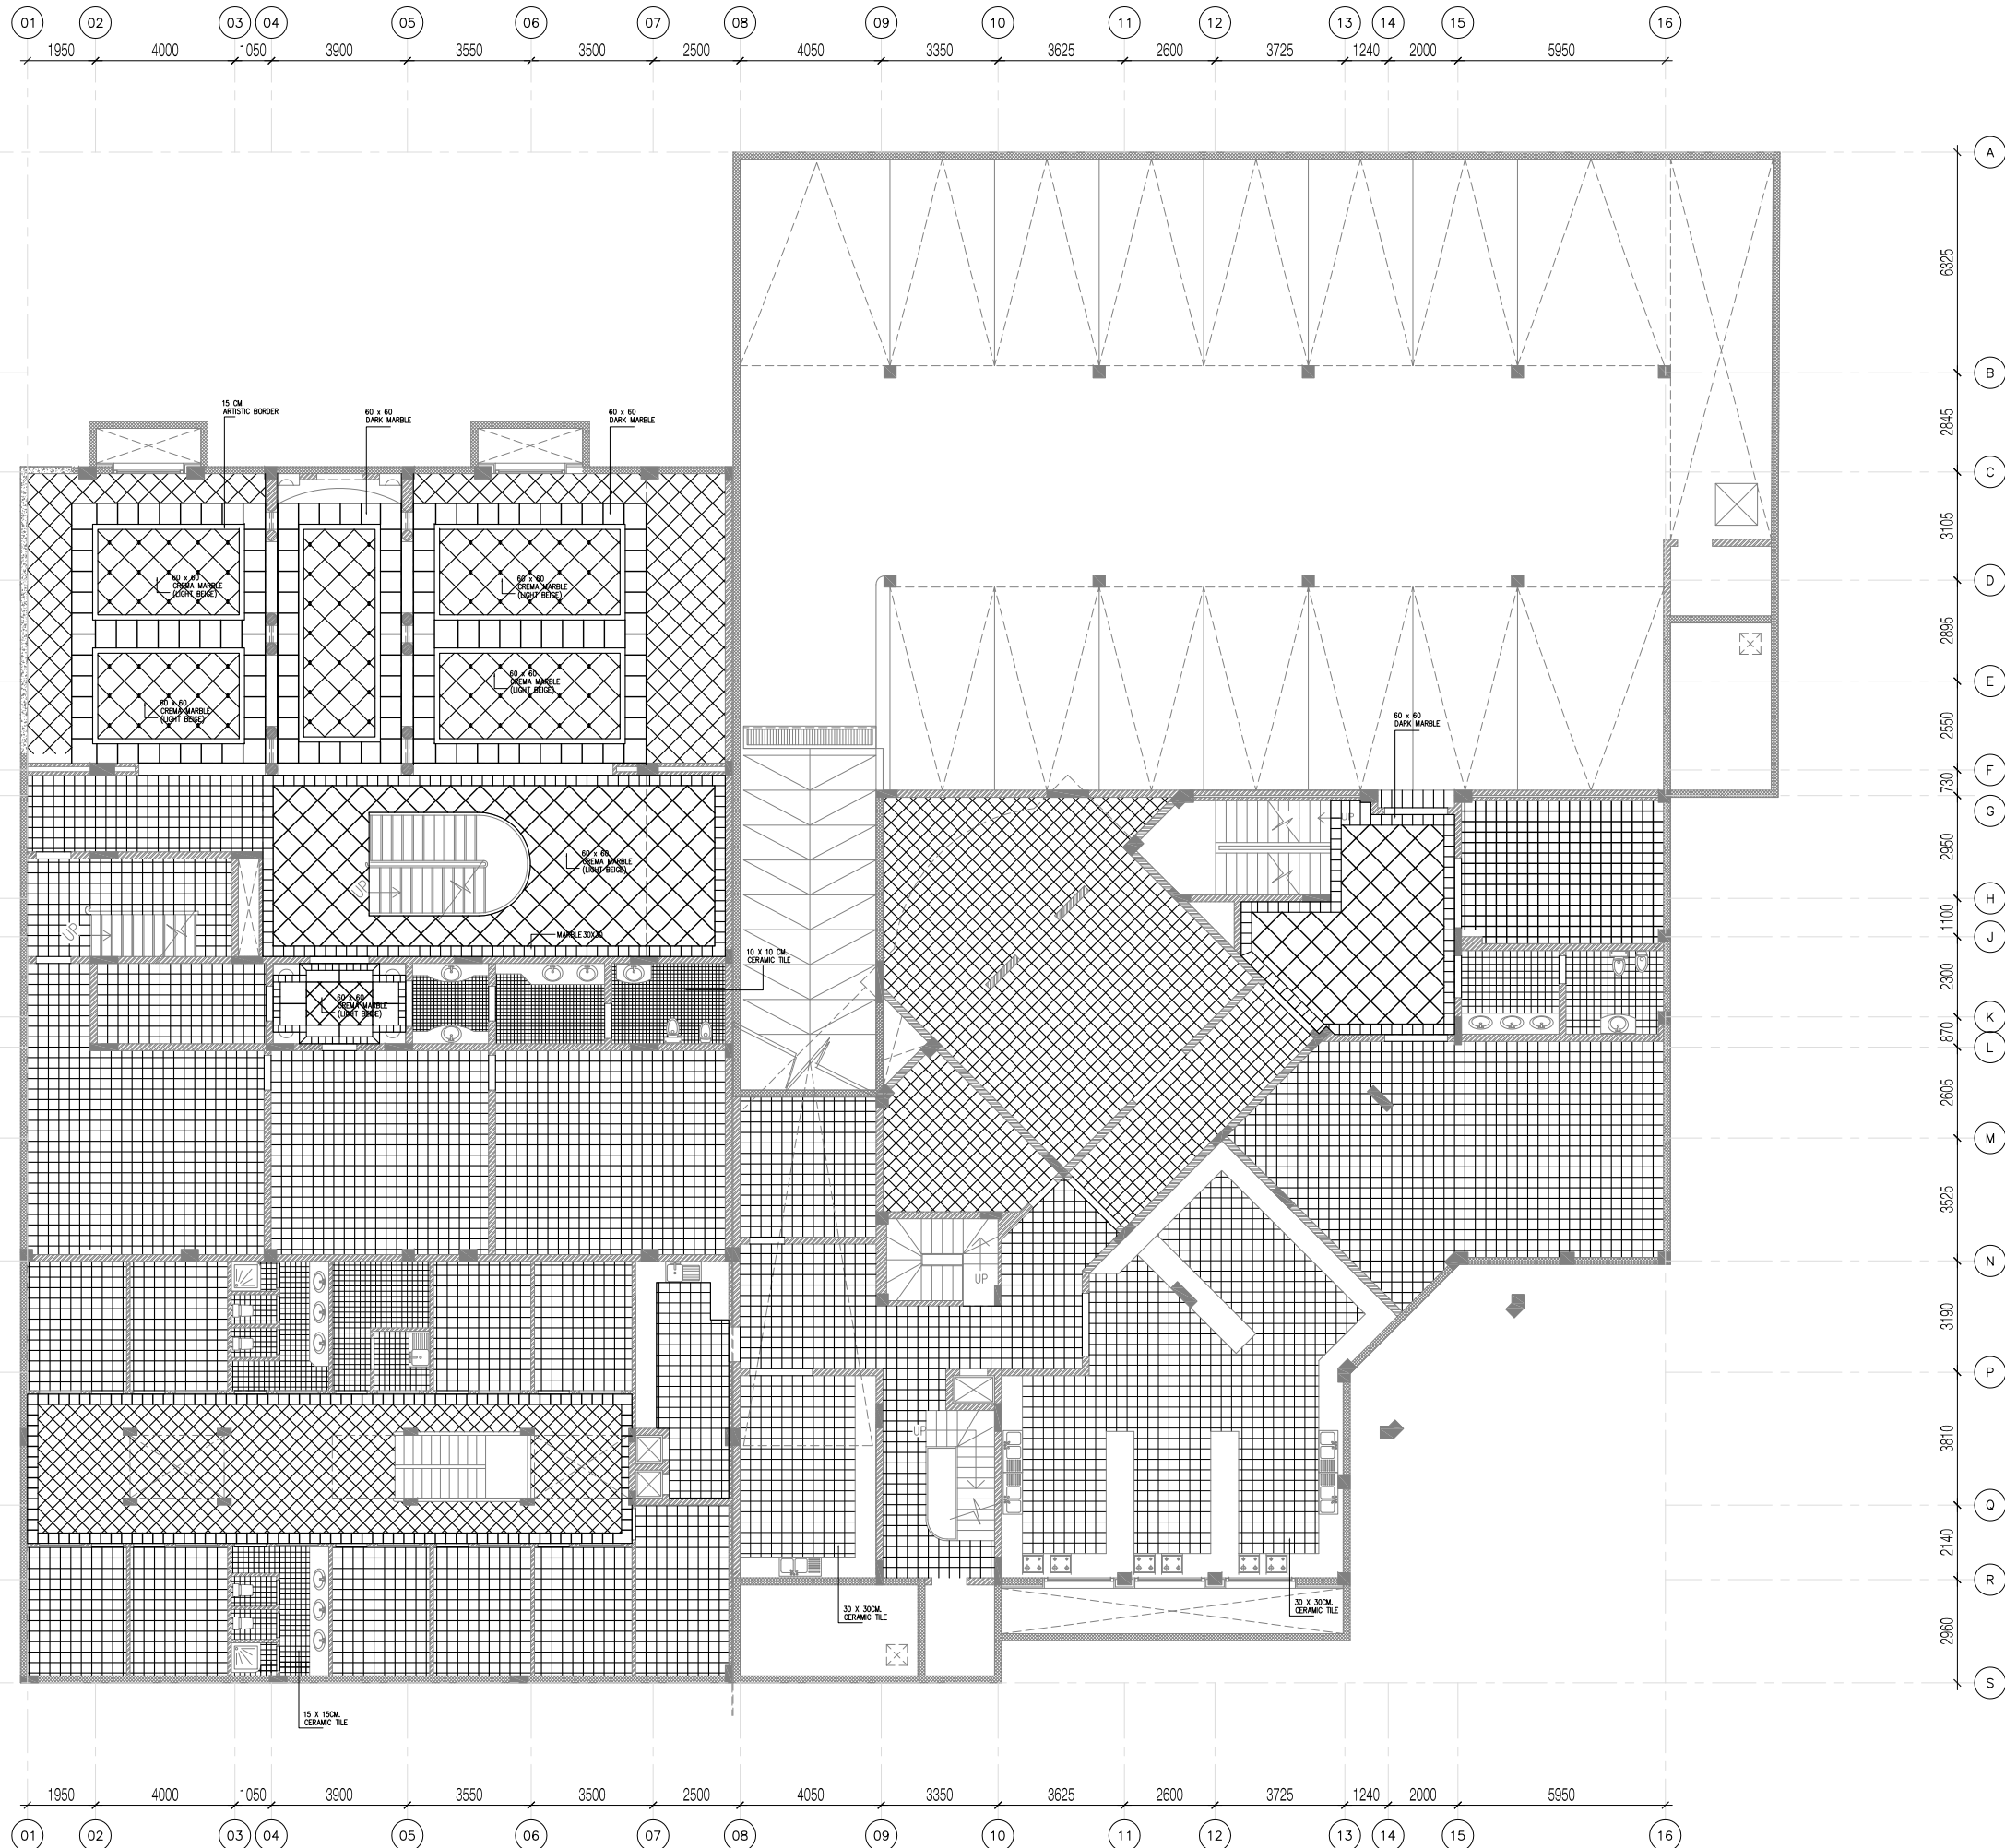

REV.	DATE	BY	DESCRIPTION
KEY PLAN			
CONSULTANT			
 النسب للإستشارات الهندسية Proportions Consulting Engineering Tel: 2792277, Fax: 2797722 P.O.Box 75453, Riyadh-11578			
PROJECT			
PRIVATE HOUSING COMPLEX AL NAKHEEL / RIYADH - SAUDI ARABIA			
OWNER			
SHEET TITLE			
ARCHITECTURAL GROUND FLOOR PLAN TILING LAYOUT			
TENDER DOCUMENTS			
PROJECT NO. :	P0521	STAGE :	WORKING DRAWINGS
DESIGNED BY :	Proportion Group	DRAWN BY :	CAD
DATE :	JAN. 2008	SCALE :	1:100M
A070001 ARCHITECTURAL			REVISION 0

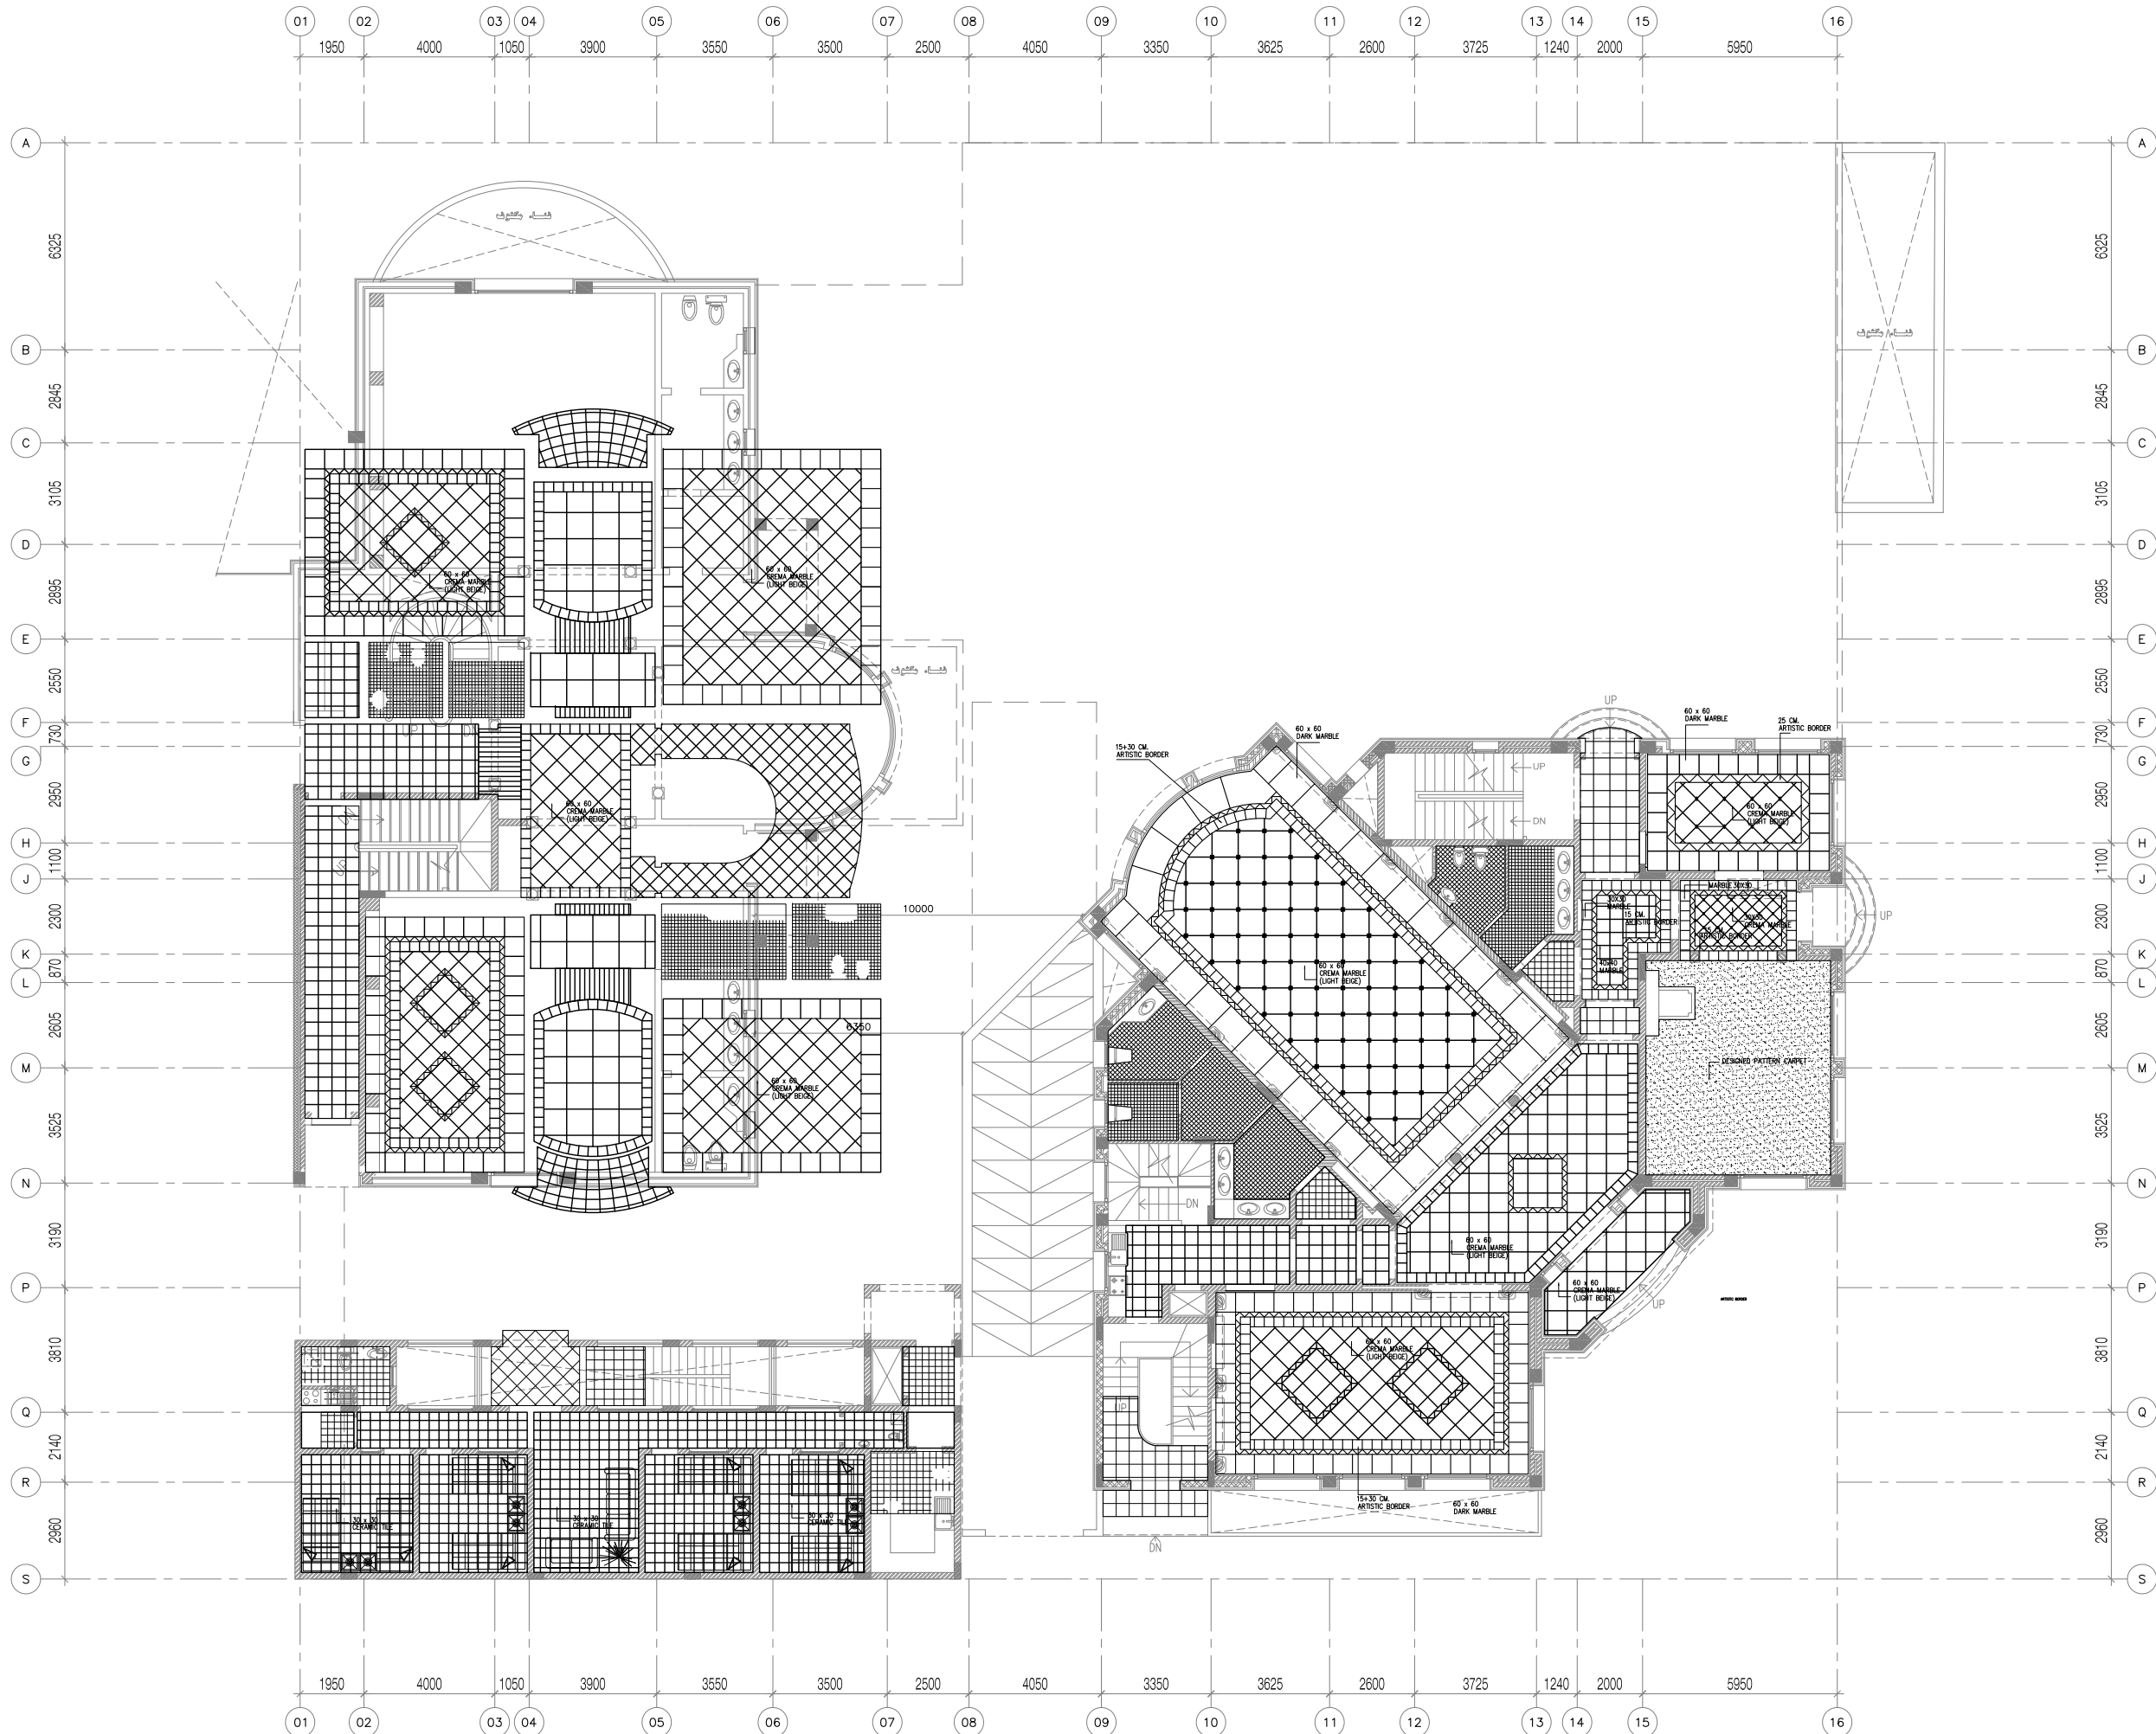

REV.	DATE	BY	DESCRIPTION
KEY PLAN			
CONSULTANT			
 النسب للإستشارات الهندسية Proportions Consulting Engineering Tel: 2792277, Fax: 2797722 P.O.Box 75453, Riyadh-11578			
PROJECT			
PRIVATE HOUSING COMPLEX AL NAKHEEL / RIYADH - SAUDI ARABIA			
OWNER			
SHEET TITLE			
ARCHITECTURAL GROUND FLOOR PLAN TILING LAYOUT			
TENDER DOCUMENTS			
PROJECT NO. :	P0521	STAGE :	WORKING DRAWINGS
DESIGNED BY :	Proportion Group	DRAWN BY :	CAD
DATE :	JAN. 2008	SCALE :	1:100M
A070101 ARCHITECTURAL			REVISION 0

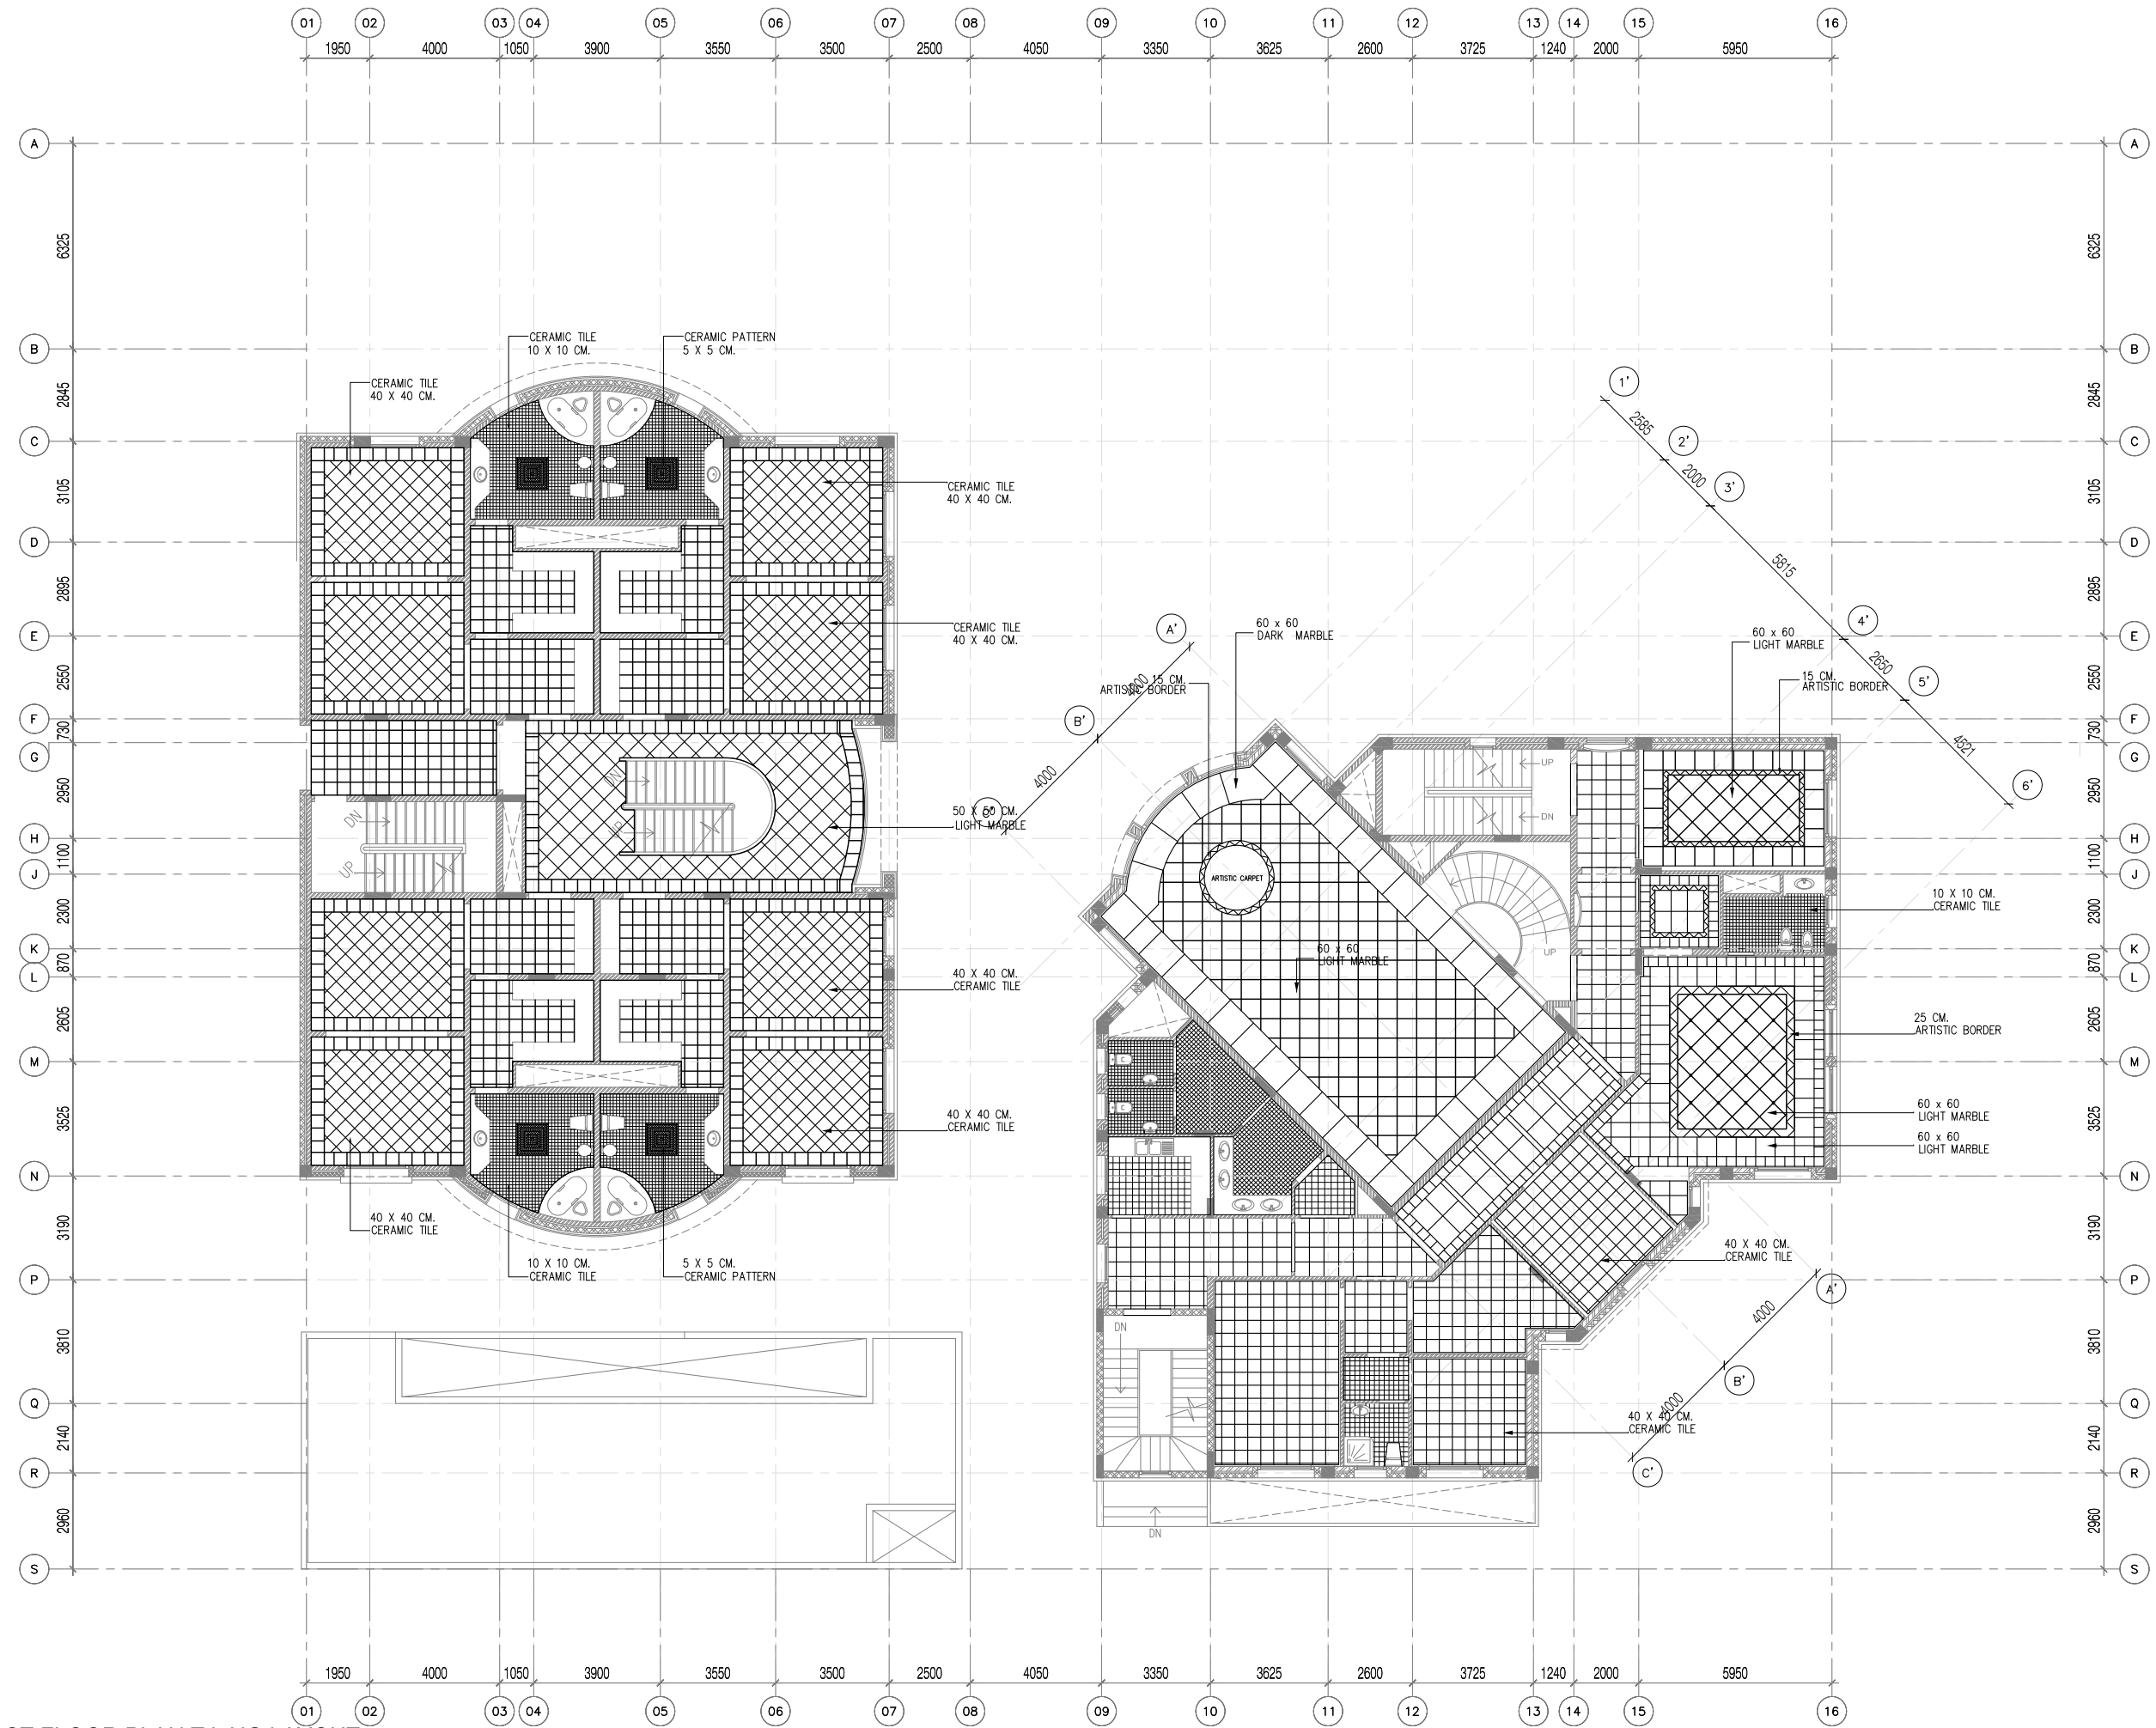

1 FIRST FLOOR PLAN TILING LAYOUT
SCALE: 1:100 M.

REV.	DATE	BY	DESCRIPTION

KEY PLAN

CONSULTANT

النسب للإستشارات الهندسية
Proportions Consulting Engineering
Tel: 2792277, Fax: 2797722 P.O.Box 75453, Riyadh-11578

PROJECT

PRIVATE HOUSING COMPLEX
AL NAKHEEL / RIYADH - SAUDI ARABIA

OWNER

SHEET TITLE



ARCHITECTURAL
FIRST FLOOR PLAN
TILING LAYOUT

TENDER DOCUMENTS


PROJECT NO. :	P0521	STAGE :	WORKING DRAWINGS
DESIGNED BY :	Proportion Group	DRAWN BY :	CAD
DATE :	JAN. 2008	SCALE :	1:100M

A070201
ARCHITECTURAL


REVISION
0

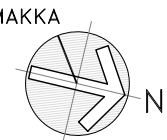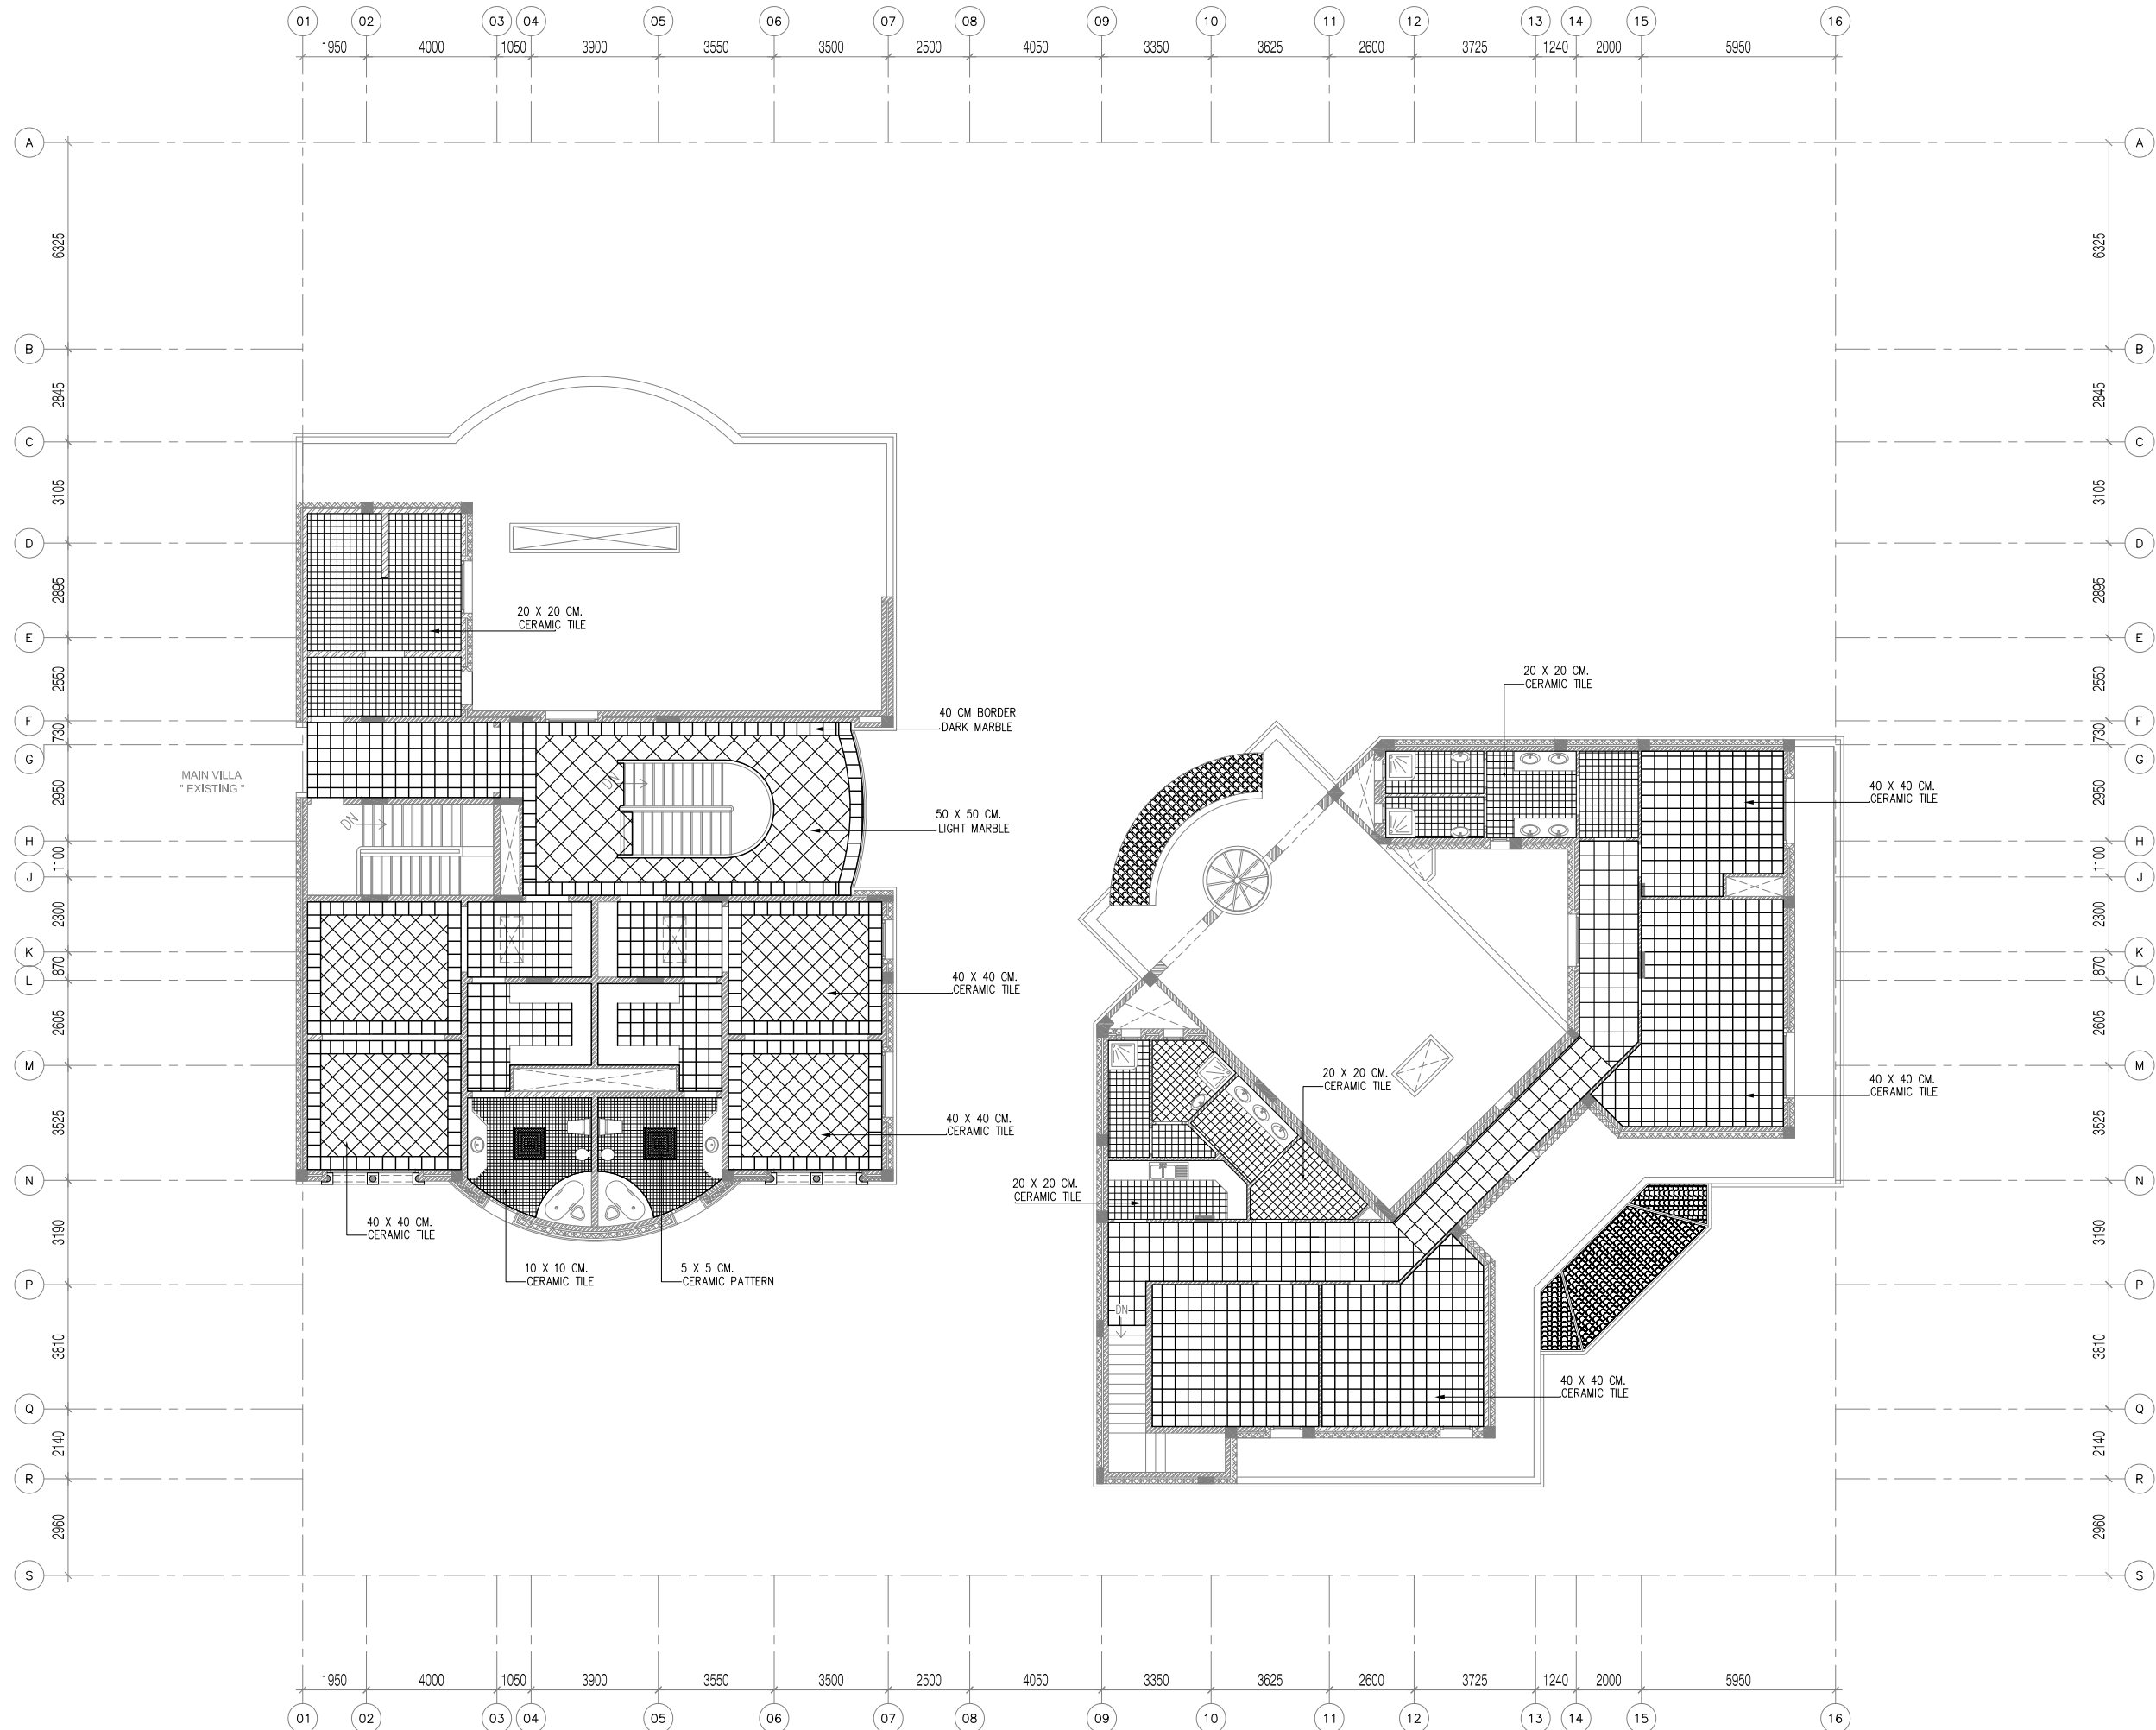

REV.	DATE	BY	DESCRIPTION
KEY PLAN			
CONSULTANT			
 النسب للإستشارات الهندسية Proportions Consulting Engineering Tel: 2792277, Fax: 2797722 P.O.Box 75453, Riyadh-11578			
PROJECT			
PRIVATE HOUSING COMPLEX AL NAKHEEL / RIYADH - SAUDI ARABIA			
OWNER			
SHEET TITLE			
ARCHITECTURAL ROOF FLOOR PLAN TILING LAYOUT			
TENDER DOCUMENTS			
PROJECT NO. :	P0521	STAGE :	WORKING DRAWINGS
DESIGNED BY :	Proportion Group	DRAWN BY :	CAD
DATE :	JAN. 2008	SCALE :	1:100M
A070301 ARCHITECTURAL			REVISION 0

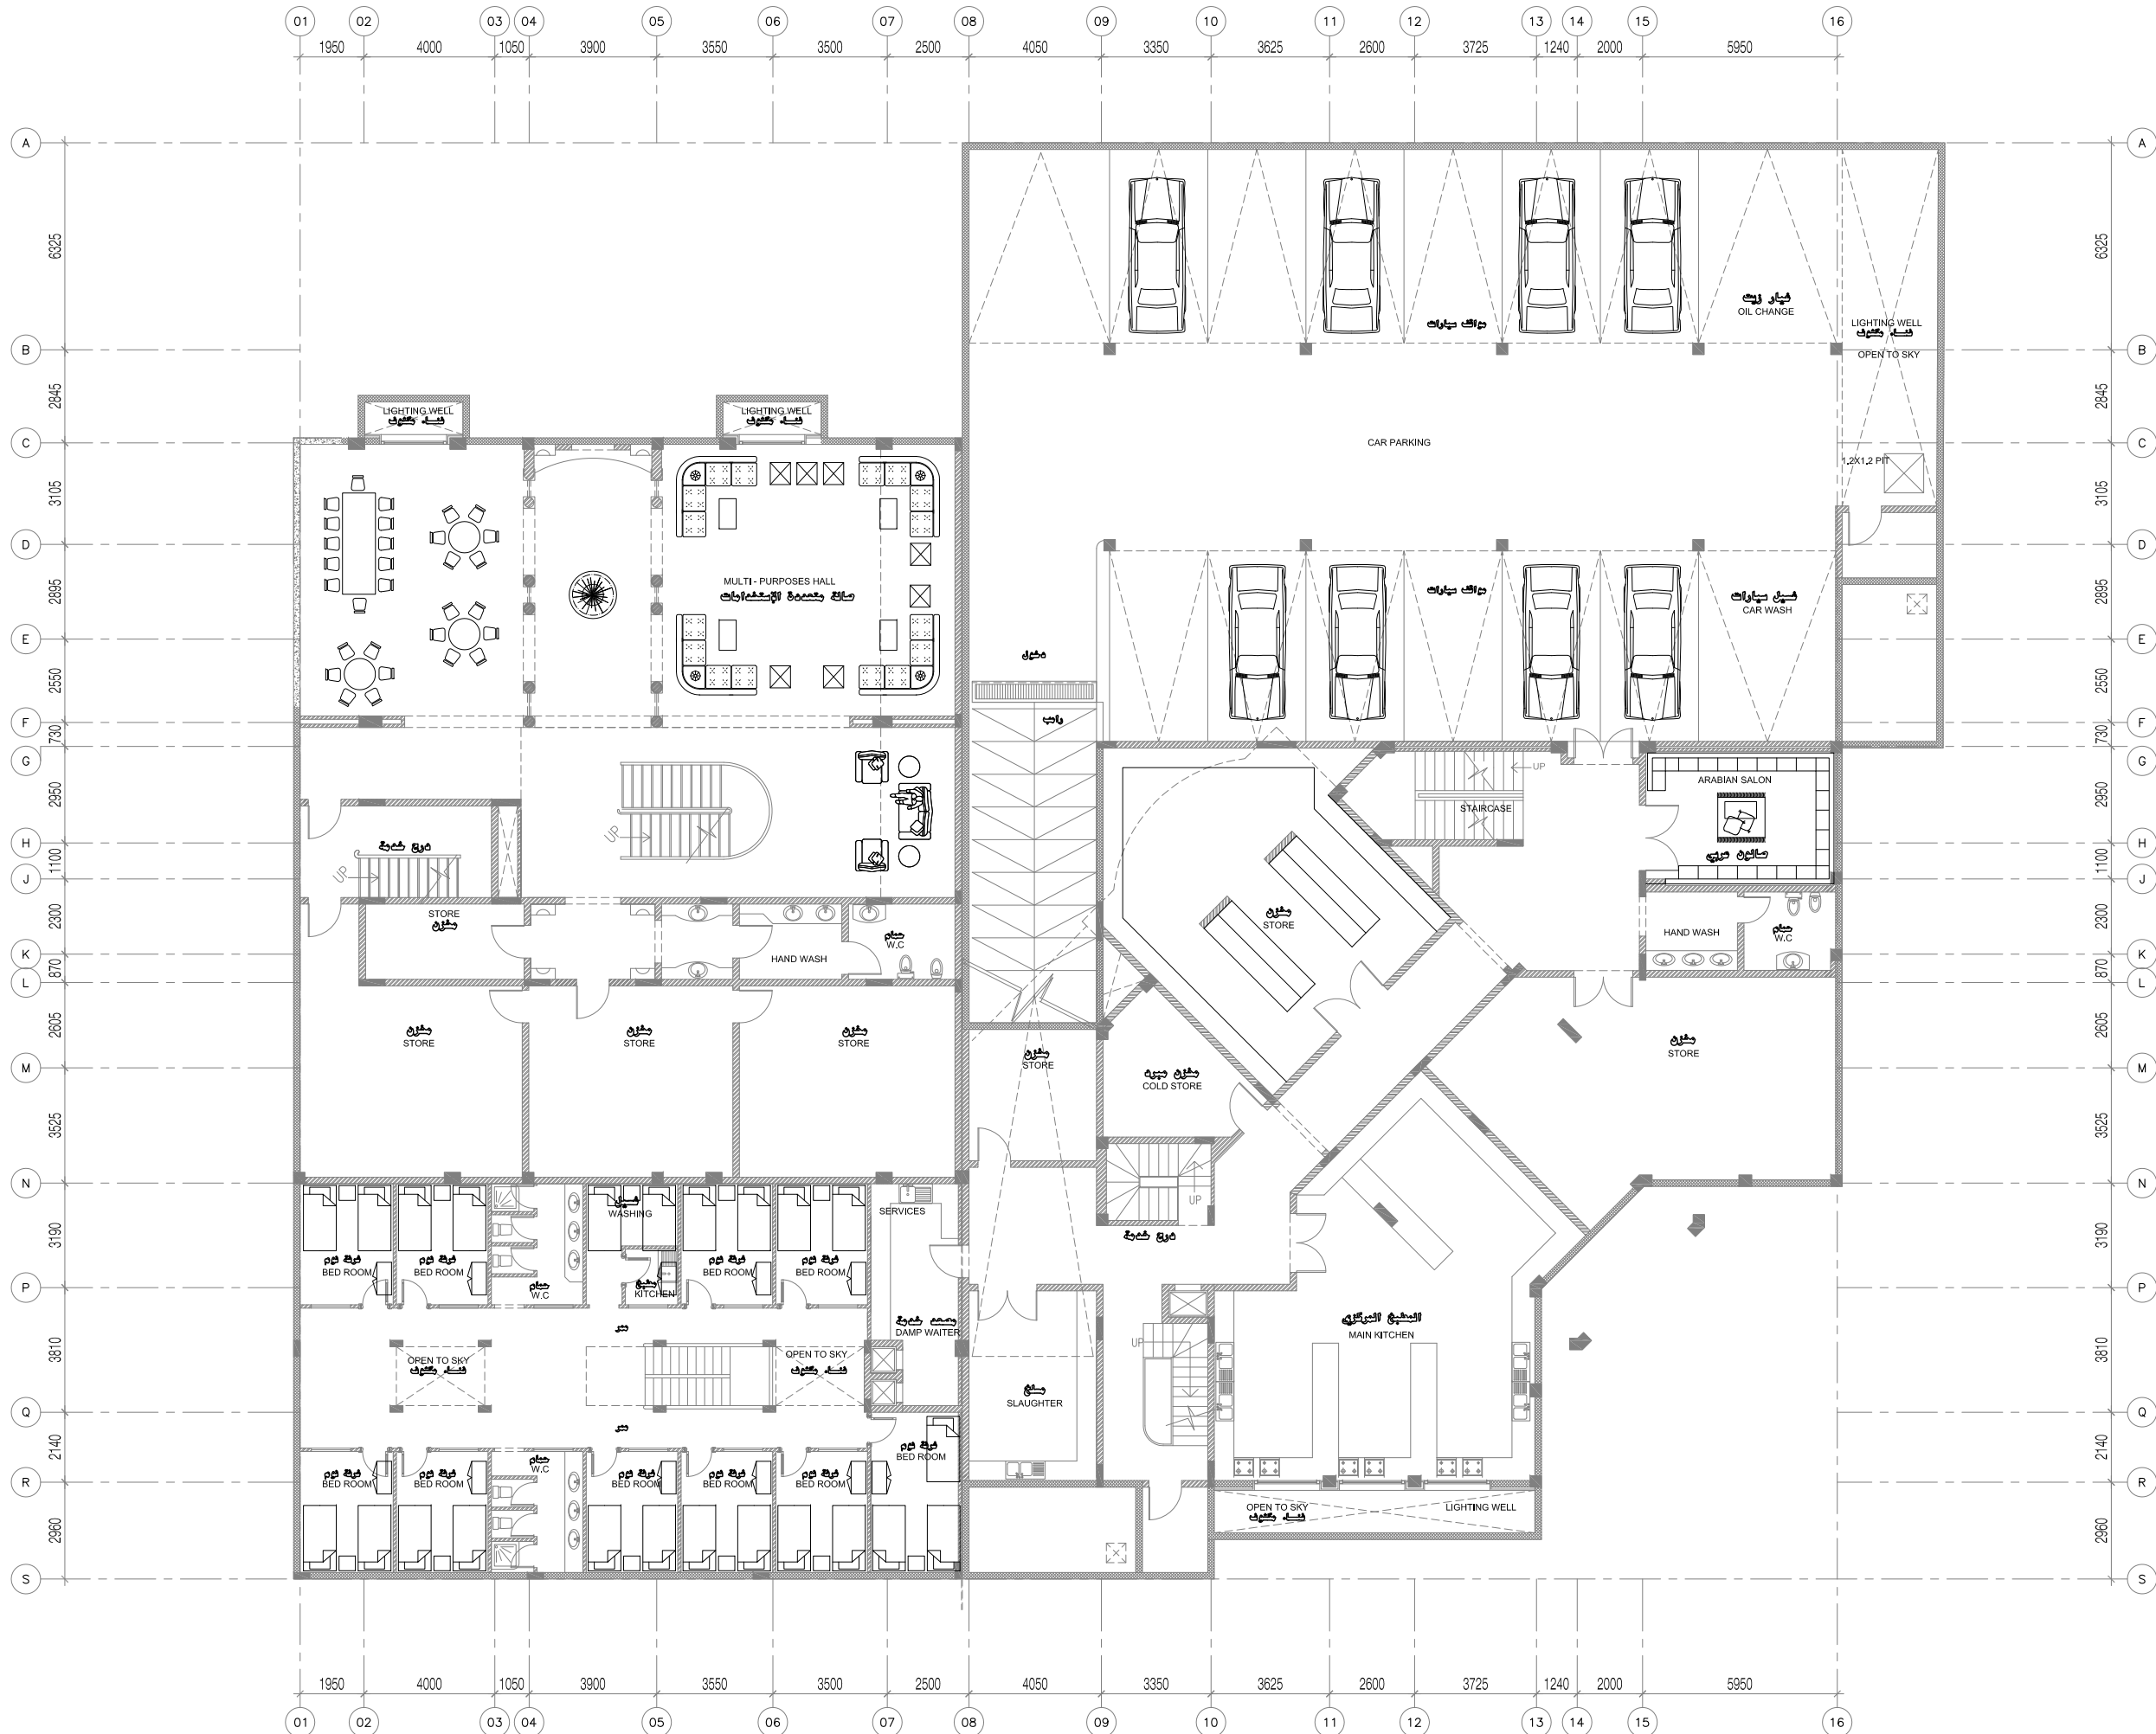

REV.	DATE	BY	DESCRIPTION
KEY PLAN			
CONSULTANT			
 النسب للاستشارات الهندسية Proportions Consulting Engineering Tel: 2792277, Fax: 2797722 P.O.Box 75453, Riyadh-11578			
PROJECT			
PRIVATE HOUSING COMPLEX AL NAKHEEL / RIYADH - SAUDI ARABIA			
OWNER			
SHEET TITLE			
ARCHITECTURAL GROUND FLOOR PLAN FURNITURE LAYOUT			
TENDER DOCUMENTS			
PROJECT NO. :	P0521	STAGE :	WORKING DRAWINGS
DESIGNED BY :	Proportion Group	DRAWN BY :	CAD
DATE :	JAN. 2008	SCALE :	1:100M
A080001 ARCHITECTURAL			REVISION 0

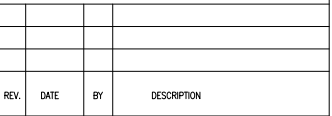

CONSULTANT



OWNER

SHEET TITLE

TENDER DOCUMENTS

PROJECT NO. :	P0521	STAGE :	WORKING DRAWINGS
DESIGNED BY :	Proportion Group	DRAWN BY :	CAD
DATE :	JAN. 2006	SCALE :	1:100M

REVISION
O



REV.	DATE	BY	DESCRIPTION

KEY PLAN

CONSULTANT

النسب للإستشارات الهندسية
Proportions Consulting Engineering
Tel: 2792277, Fax: 2797722 P.O.Box 75453, Riyadh-11578

PROJECT

PRIVATE HOUSING COMPLEX
AL NAKHEEL / RIYADH - SAUDI ARABIA

OWNER



SHEET TITLE

**ARCHITECTURAL
FIRST FLOOR PLAN
FURNITURE LAYOUT**

TENDER DOCUMENTS			
PROJECT NO. :	P0521	STAGE :	WORKING DRAWINGS
DESIGNED BY :	Proportion Group	DRAWN BY :	CAD
DATE :	JAN. 2008	SCALE :	1:100M

A080201
ARCHITECTURAL

REVISION
0

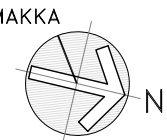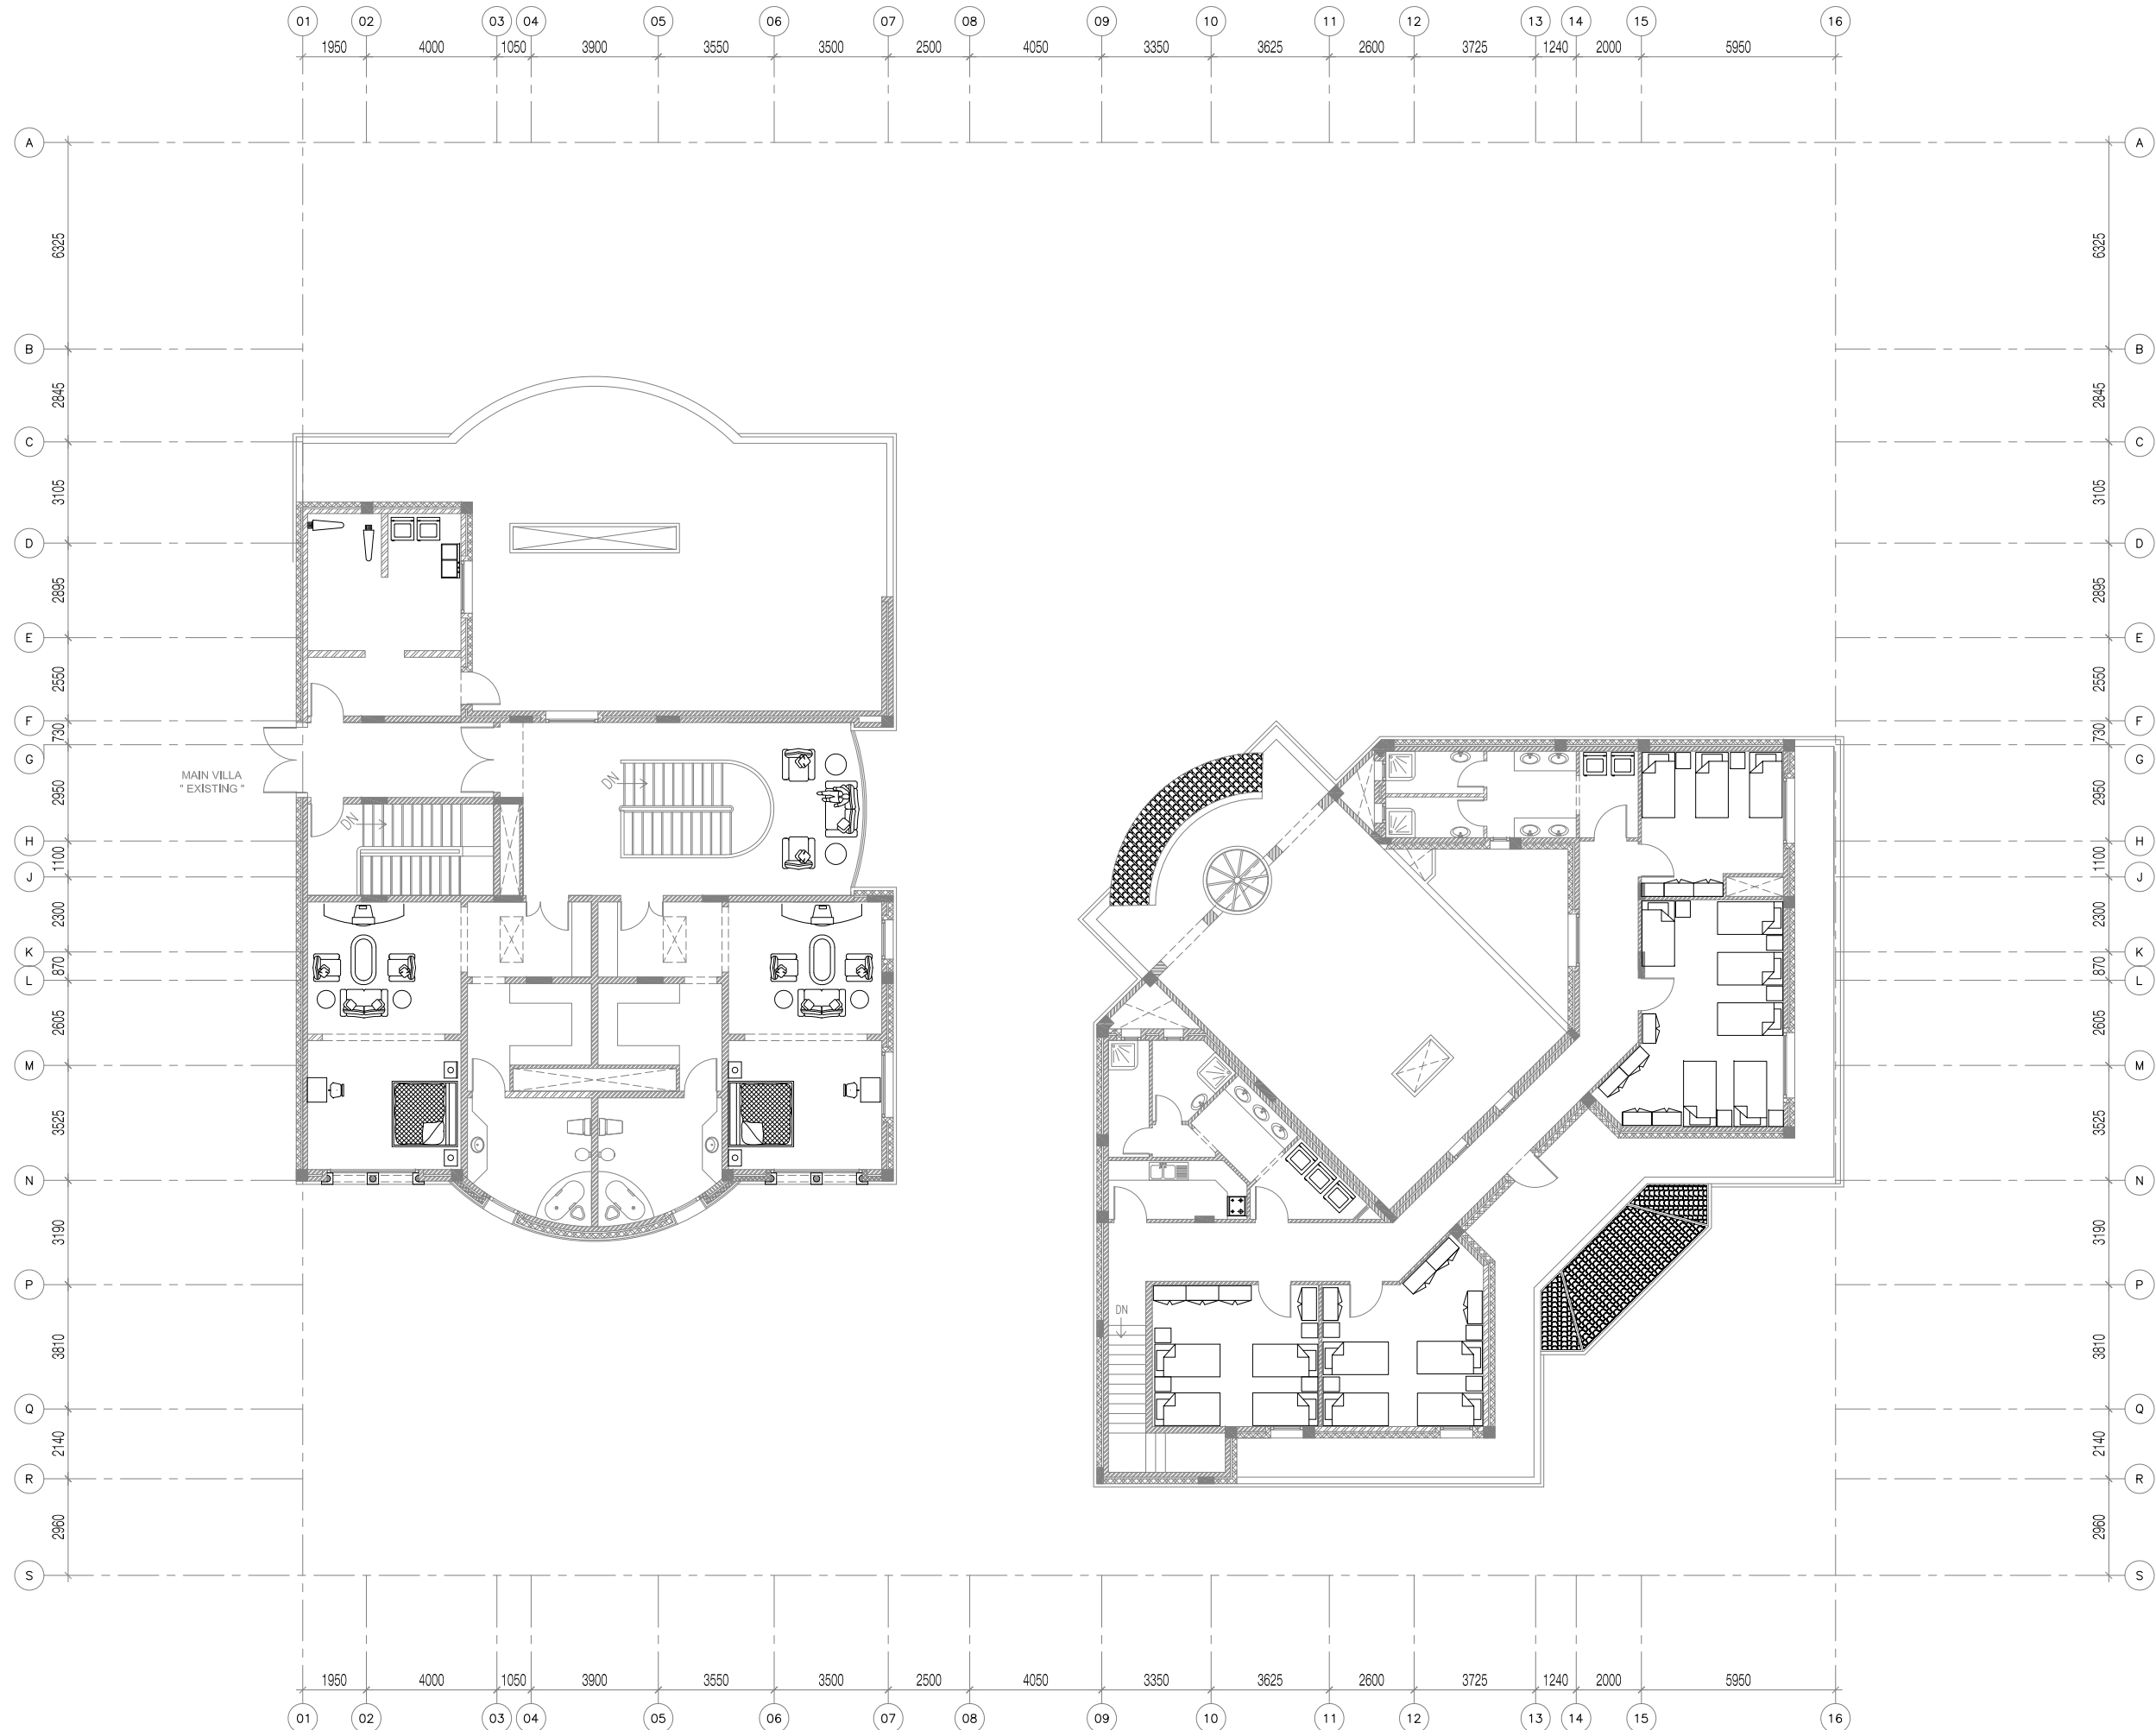

REV.	DATE	BY	DESCRIPTION

KEY PLAN

CONSULTANT



النسب للإستشارات الهندسية
Proportions Consulting Engineering
Tel: 2792277, Fax: 2797722 P.O.Box 75453, Riyadh-11578

PROJECT

PRIVATE HOUSING COMPLEX
AL NAKHEEL / RIYADH - SAUDI ARABIA

OWNER



SHEET TITLE



ARCHITECTURAL
ROOF FLOOR PLAN
FURNITURE LAYOUT



TENDER DOCUMENTS			
PROJECT NO. :	P0521	STAGE :	WORKING DRAWINGS
DESIGNED BY :	Proportion Group	DRAWN BY :	CAD
DATE :	JAN. 2008	SCALE :	1:100M



A080301
ARCHITECTURAL



REVISION
0

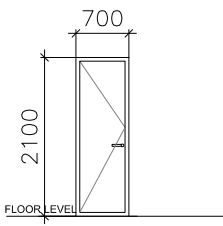
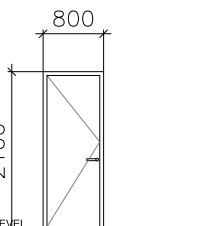
Doors Schedule	
D1	Description
	Quantities
	BASEMENT : 6
	Total Quantity : 06
Single Side Hinged Wooden Door	
D2	Description
	Quantities
	BASEMENT 1 GROUND 15 FIRST 4 ROOF 4
	Total Quantity : 24
Single Side Hinged Wooden Door	

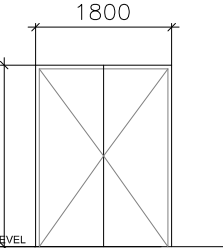
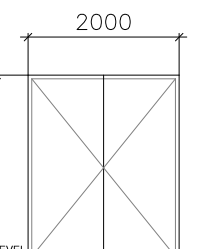
Doors Schedule	
D9	Description
	Quantities
	BASEMENT 4 GROUND - FIRST - ROOF -
	Total Quantity : 04
Double Side Hinged Wooden Door	
D10	Description
	Quantities
	BASEMENT 2 GROUND 2 FIRST - ROOF 1
	Total Quantity : 05
Double Side Hinged Wooden Door	

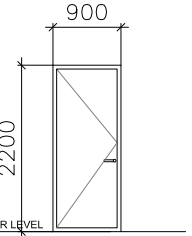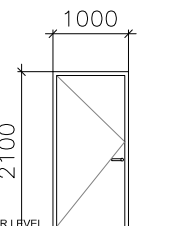
Doors Schedule	
D3	Description
	Quantities
	BASEMENT 11 GROUND 3 FIRST - ROOF -
	Total Quantity : 14
Single Side Hinged Wooden Door	
D4	Description
	Quantities
	BASEMENT 13 GROUND 12 FIRST 12 ROOF 13
	Total Quantity : 51
Single Side Hinged Wooden Door	

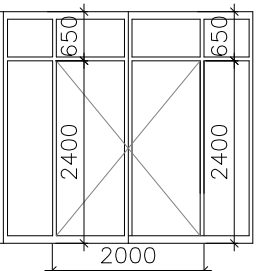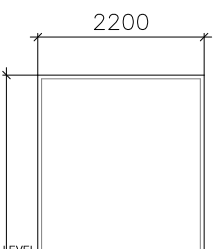Doors Schedule	
D11	Description
	Quantities
	BASEMENT - GROUND 1 FIRST - ROOF -
	Total Quantity : 01
Double Side Hinged Wooden Door	
D12	Description
	Quantities
	BASEMENT - GROUND 1 FIRST - ROOF -
	Total Quantity : 01
Sliding Door Wooden	

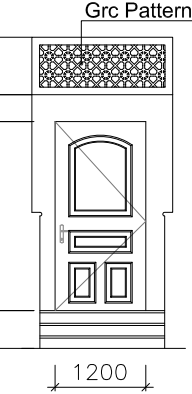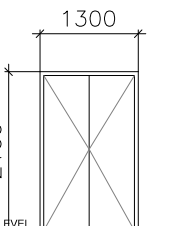Doors Schedule	
D5	Description
	Quantities
	BASEMENT - GROUND 1 FIRST - ROOF -
	Total Quantity : 1
Single Side Hinged Wooden Door	
D6	Description
	Quantities
	BASEMENT - GROUND - FIRST 4 ROOF 2
	Total Quantity : 08
Double Side Hinged Wooden Door	

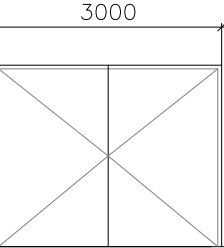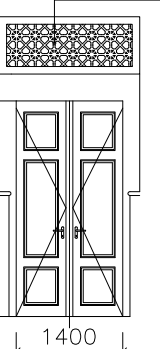Doors Schedule	
D13	Description
	Quantities
	BASEMENT - GROUND 1 FIRST - ROOF -
	Total Quantity : 01
Double Side Hinged Steel Door	
D14	Description
	Quantities
	BASEMENT - GROUND 1 FIRST - ROOF -
	Total Quantity : 01
Double Side Hinged Wooden Door	

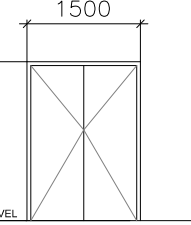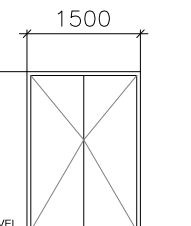Doors Schedule	
D7	Description
	Quantities
	BASEMENT - GROUND 1 FIRST 2 ROOF -
	Total Quantity : 06
Double Side Hinged Wooden Door	
D8	Description
	Quantities
	BASEMENT - GROUND 1 FIRST 1 ROOF -
	Total Quantity : 02
Double Side Hinged Wooden Door	

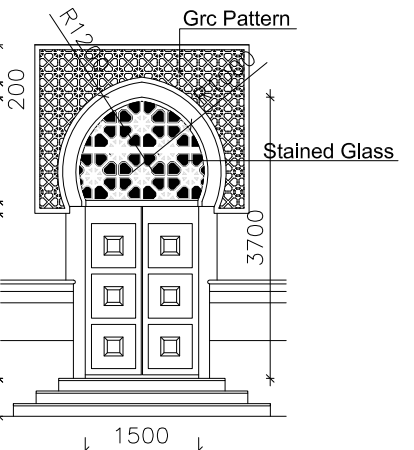Doors Schedule	
D15	Description
	Quantities
	GROUND 2
	Total Quantity : 2
Double Side Hinged Wooden Door	



REV.	DATE	BY	DESCRIPTION

KEY PLAN

CONSULTANT



النسب للإستشارات الهندسية
Proportions Consulting Engineering
Tel: 2752277, Fax: 2757722 P.O.Box 75453, Riyadh-11578

PROJECT

PRIVATE HOUSING COMPLEX
AL NAKHEEL / RIYADH - SAUDI ARABIA

OWNER

SHEET TITLE

DOORS SCHEDULE


TENDER DOCUMENTS			
PROJECT NO. :	P0521	STAGE :	WORKING DRAWINGS
DESIGNED BY :	Proportion Group	DRAWN BY :	CAD
DATE :	JAN. 2008	SCALE :	1:100M

A100101
ARCHITECTURAL


0

Window Schedule


W1 (Wooden Frame with Glazed panel
Fixed With Sliding Window) 13 SETS

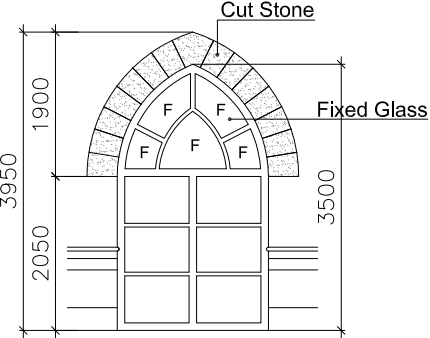


W2 (Wooden Frame with Glazed panel
Fixed With Sliding Window) 01 SETS

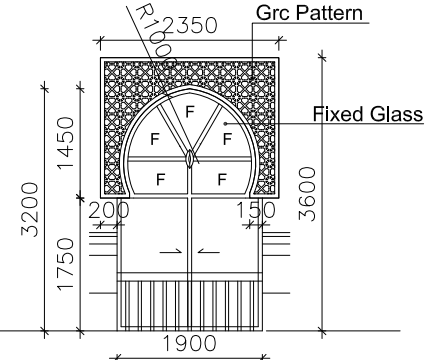

W3 (Wooden Frame with Glazed panel
Double Side Sliding Window) 02 SETS

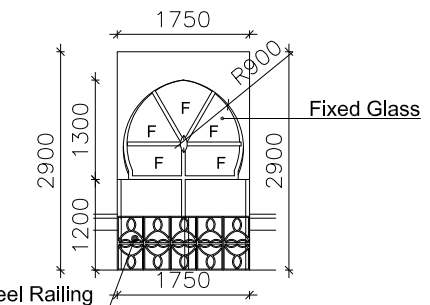


W4 (Wooden Frame with Glazed panel
Fixed With Swing Type Window) 01 SETS

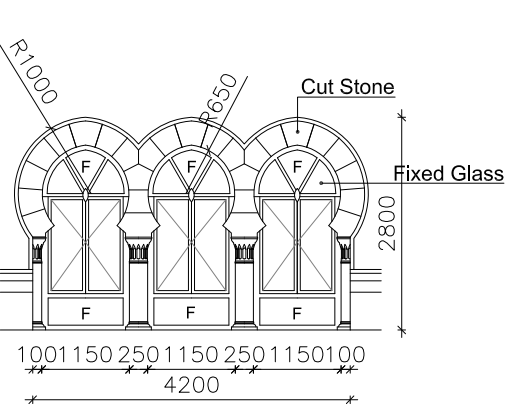


Window Schedule


W5 (Wooden Frame with Glazed panel
Fixed With Sliding Window) 06 SETS

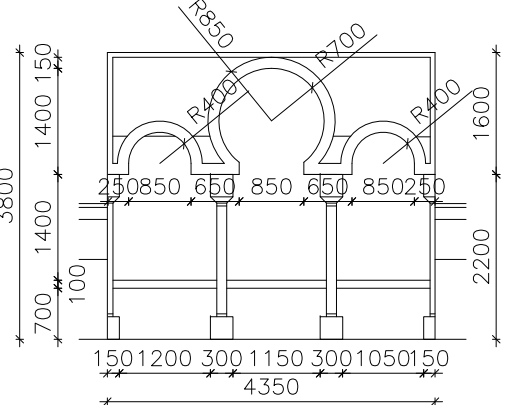


W6 (Wooden Frame with Glazed panel
Fixed Type Window) 14 SETS

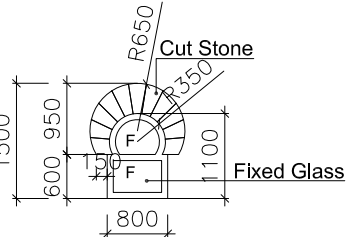

W7 (Wooden Frame with Glazed panel
Fixed With Swing Type Window) 07 SETS

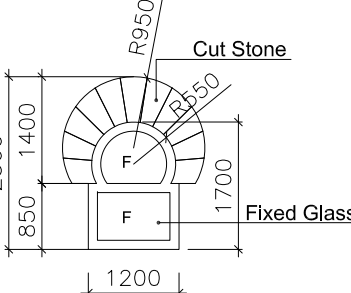


W8 (Wooden Frame with Glazed panel
Fixed With Swing Type Window) 05 SETS

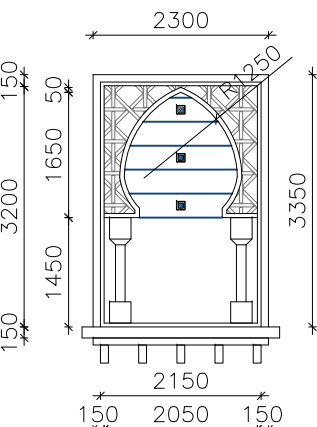


Window Schedule


W9 (Wooden Frame with Glazed panel
Fixed With Sliding Window) 01 SET

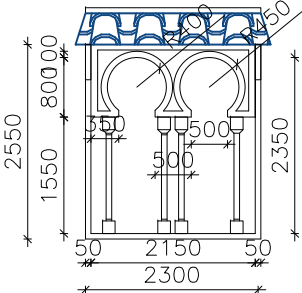


W10 (Wooden Frame with Glazed panel)
Double Side Sliding Window 02 SETS

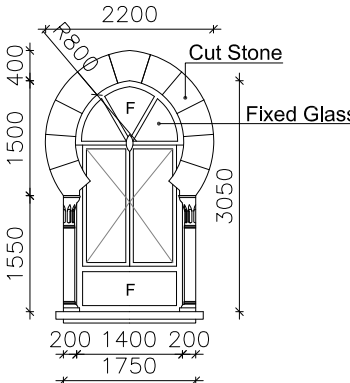

W11 (Wooden Frame with Glazed panel
Fixed With Sliding Window) 02 SETS

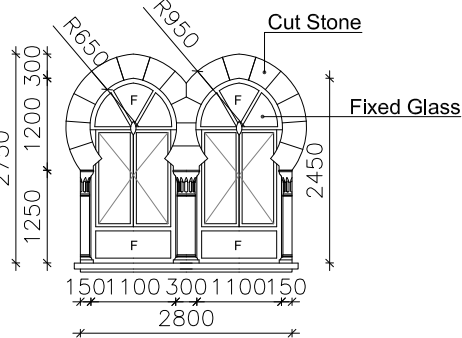


W12 (Wooden Frame with Glazed panel
With Sliding Window) 04 SETS

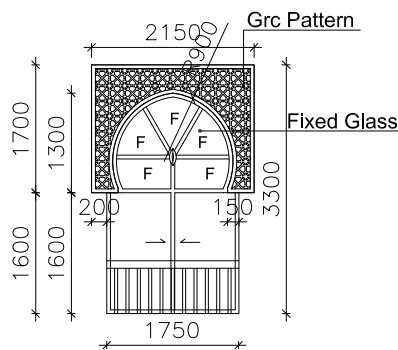


Window Schedule

W15 (Wooden Frame with Glazed panel
Fixed With Sliding Window) 01 SETS

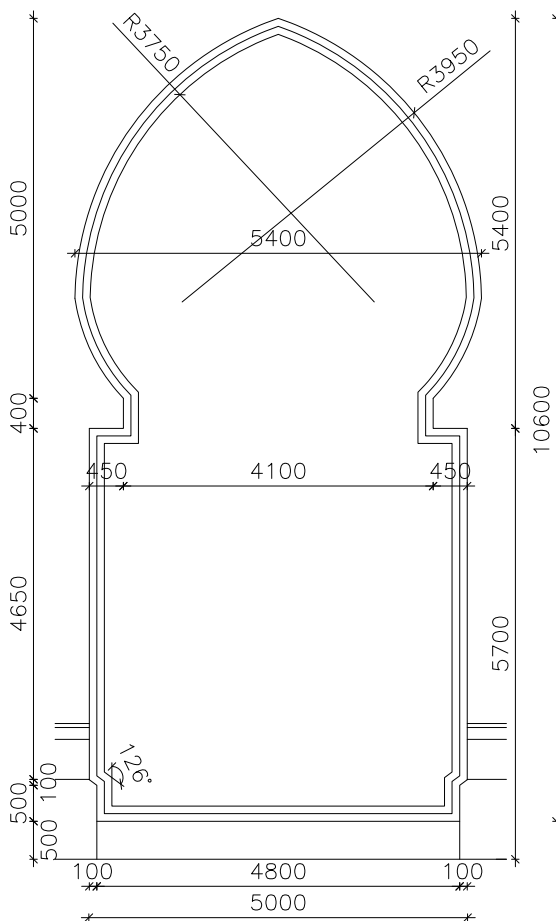

W13 (Wooden Frame with Glazed panel
Fixed With Sliding Window) 01 SETS

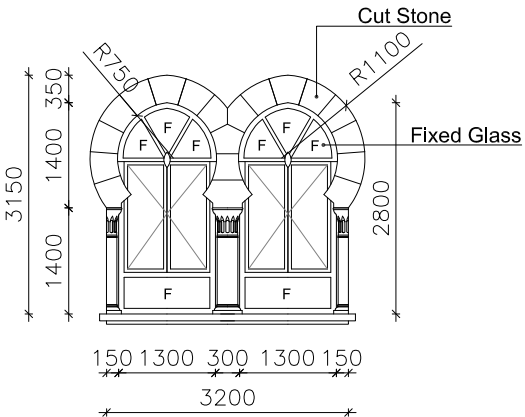

REV.	DATE	BY	DESCRIPTION

CONSULTANT
النسب للإستشارات الهندسية
Proportions Consulting Engineering
Tel: 2752277, Fax: 2757722 P.O.Box 75453, Riyadh-11578

PROJECT
PRIVATE HOUSING COMPLEX
AL NAKHEEL / RIYADH - SAUDI ARABIA


SHEET TITLE
WINDOWS SCHEDULE

TENDER DOCUMENTS			
PROJECT NO. :	P0521	STAGE :	WORKING DRAWINGS
DESIGNED BY :	Proportion Group	DRAWN BY :	CAD
DATE :	JAN. 2008	SCALE :	1:100M

A100201
ARCHITECTURAL
0


Window Schedule

W14 (Wooden Frame with Glazed panel
Fixed With Sliding Window) 01 SETS

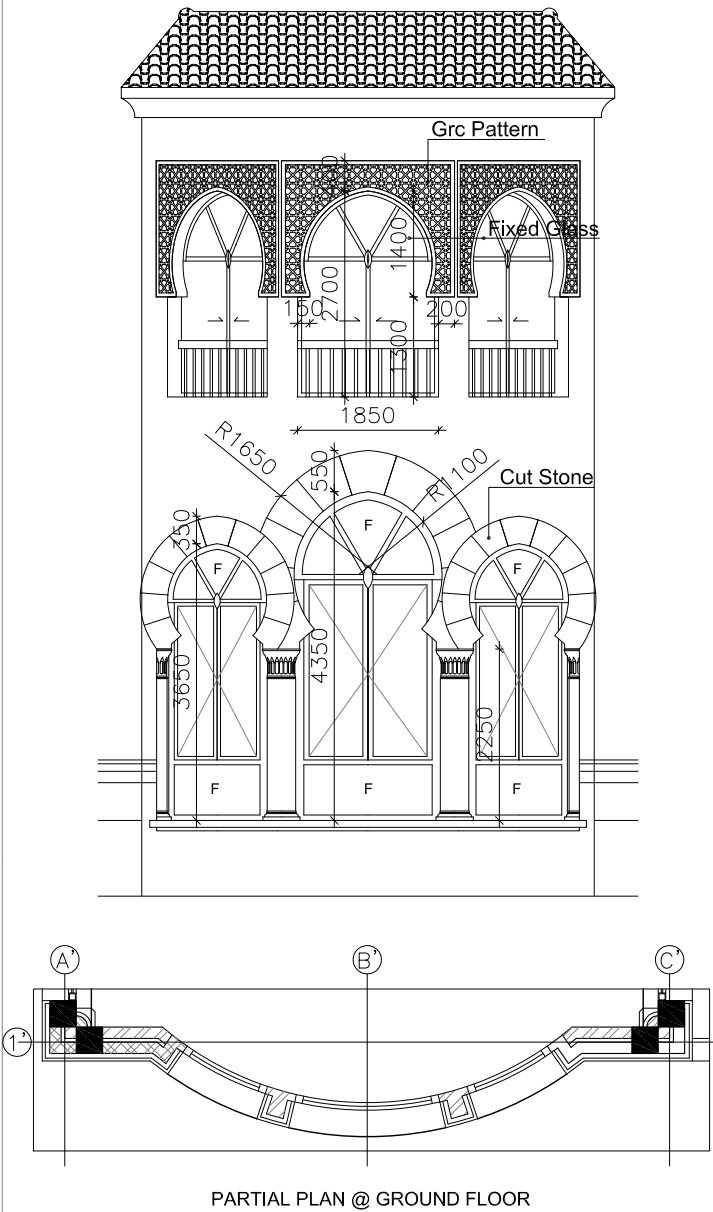


Window Schedule

W17 (Wooden Frame with Glazed panel)
Double Side Sliding Window 07 SETS

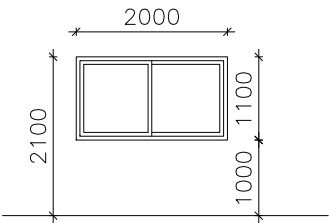


W16 (Wooden Frame with Glazed panel
Fixed Type Window) 04 SETS

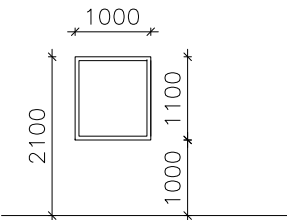


Window Schedule

W18 (Wooden Frame with Glazed panel)
Double Side Sliding Window 08 SETS

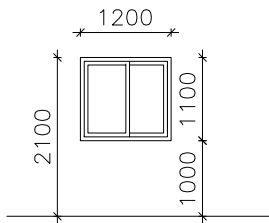


W19 (Wooden Frame with Glazed panel
Fixed Type Window) 07 SETS

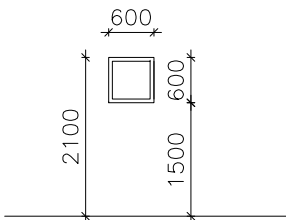


Window Schedule




REV.	DATE	BY	DESCRIPTION
KEY PLAN			
CONSULTANT			
 النسب للإستشارات الهندسية Proportions Consulting Engineering Tel: 2752277, Fax: 2757722 P.O.Box 75453, Riyadh-11578			
PROJECT			
PRIVATE HOUSING COMPLEX AL NAKHEEL / RIYADH - SAUDI ARABIA			
OWNER			
SHEET TITLE			
WINDOWS SCHEDULE			
TENDER DOCUMENTS			
PROJECT NO. :	P0521	STAGE :	WORKING DRAWINGS
DESIGNED BY :	Proportion Group	DRAWN BY :	CAD
DATE :	JAN. 2008	SCALE :	1:100M
A100202 ARCHITECTURAL			REVISION 0

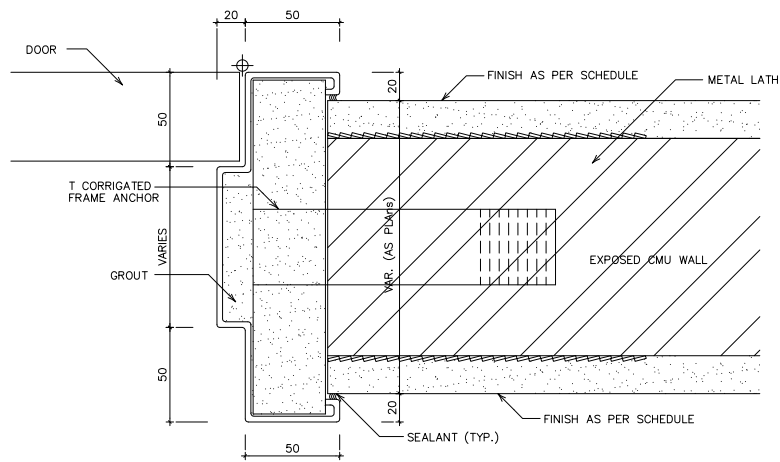


1 DOOR FIXING DETAIL
A110100 SCALE: 1:2 M.

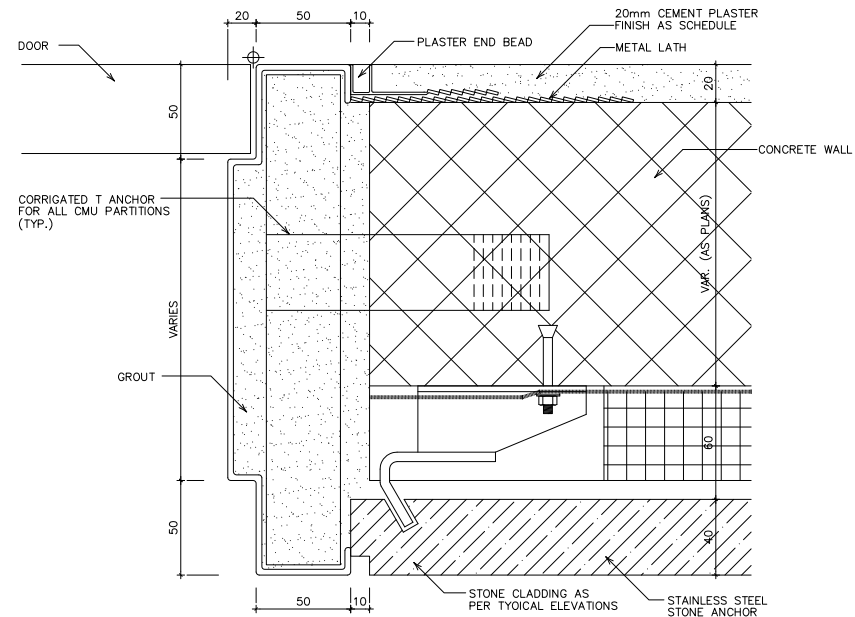


2 DOOR FIXING DETAIL
A110100 SCALE: 1:2 M.

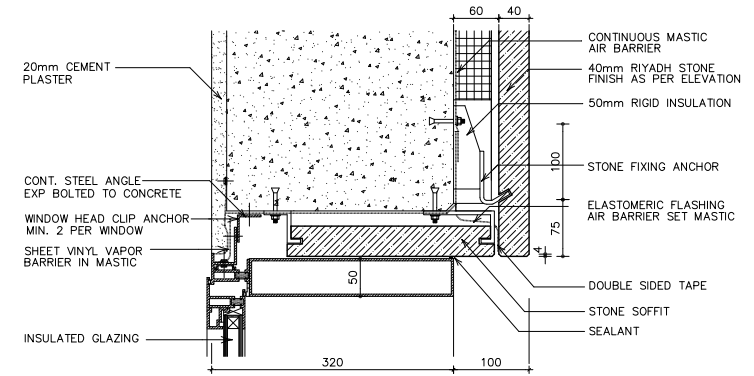


3 WINDOW HEAD DETAIL
A110100 SCALE: 1:5 M.

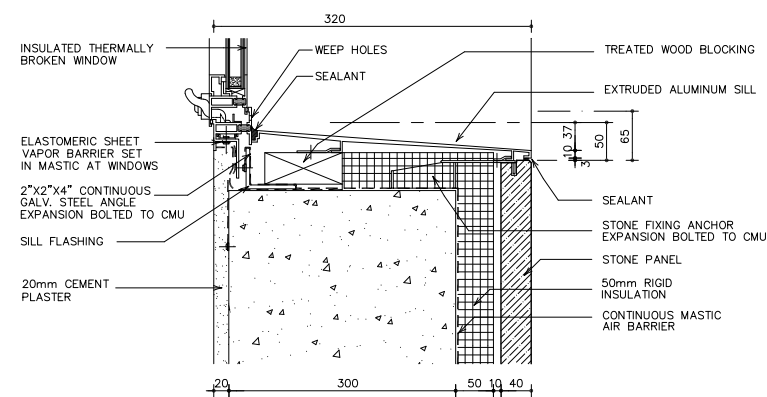


4 WINDOW SILL DETAIL
A110100 SCALE: 1:5 M.

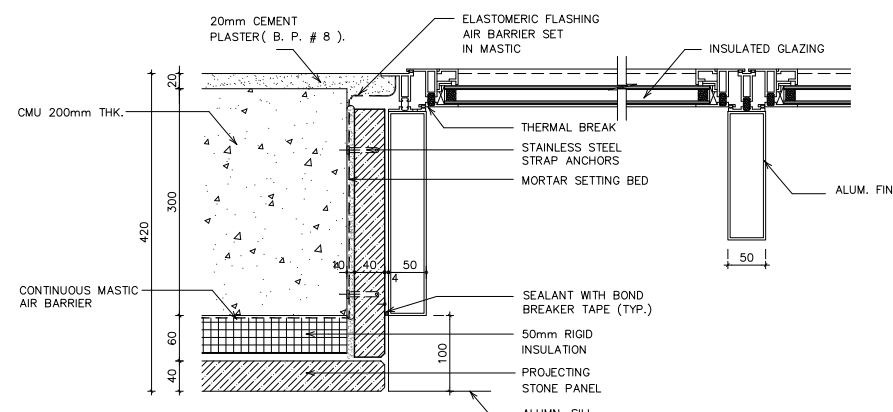

5 WINDOW JAMB DETAIL
A110100 SCALE: 1:5 M.

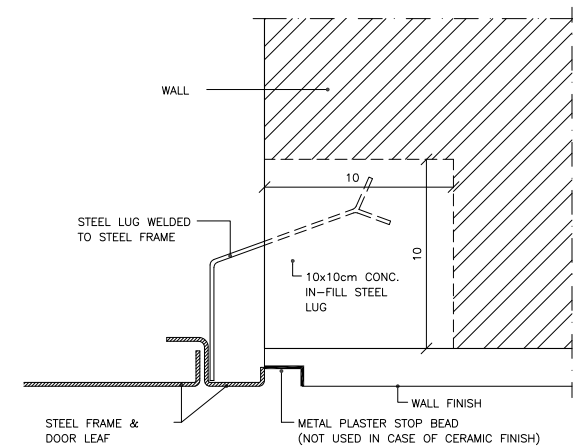

6 ACCESS DOOR JAMB, SILL OR HEAD
A110100 SCALE: 1:5 M.

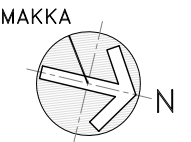

REV.	DATE	BY	DESCRIPTION

KEY PLAN

CONSULTANT
النسب للإستشارات الهندسية
Proportions Consulting Engineering
Tel: 2792277, Fax: 2797722 P.O.Box 75453, Riyadh-11578





PROJECT
PRIVATE HOUSING COMPLEX
AL NAKHEEL / RIYADH - SAUDI ARABIA

OWNER

SHEET TITLE
MISCELLANEOUS DETAIL
DOOR AND WINDOW DETAIL

TENDER DOCUMENTS			
PROJECT NO. :	0502	STAGE :	TENDER DOCUMENT
DESIGNED BY :	A. AL NAKHEEL	DRAWN BY :	A. A
DATE :	FEB.2006	SCALE :	AS SHOWN




A110100 0

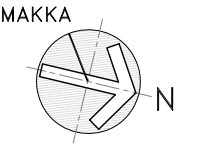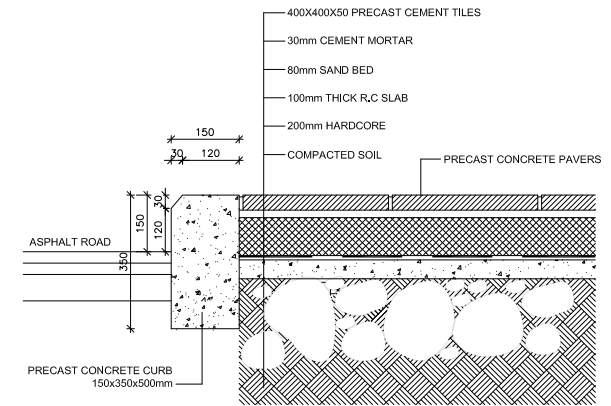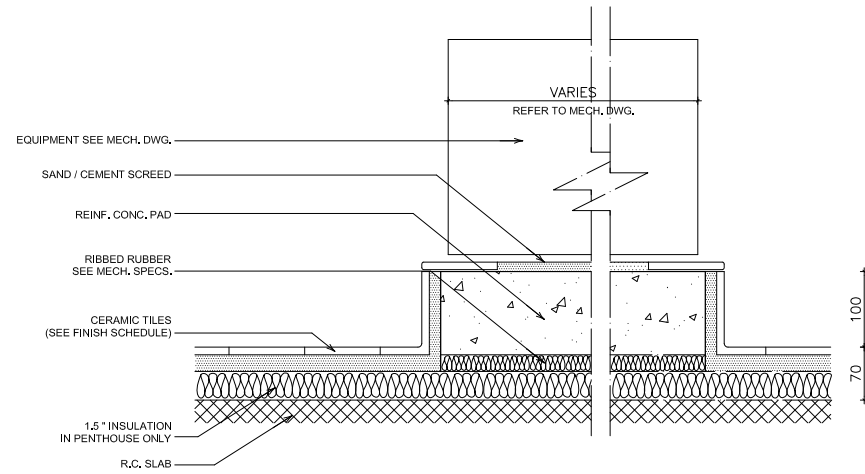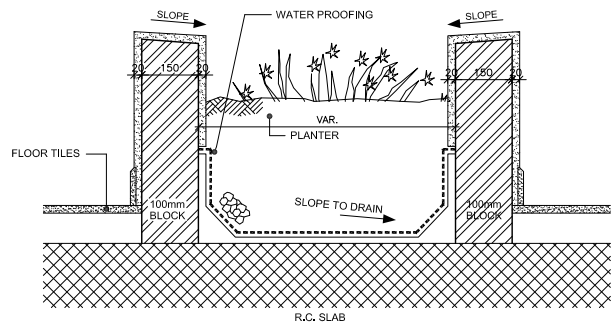

1 FLOWER BED DETAILS
A110200 SCALE: 1:10 M.

2 CONCRETE PAD FOR MECH. EQUIPMENT
A110200 SCALE: 1:5 M.

3 TYPICAL EXTERNAL CURB DETAIL
A110200 SCALE: 1:10 M.

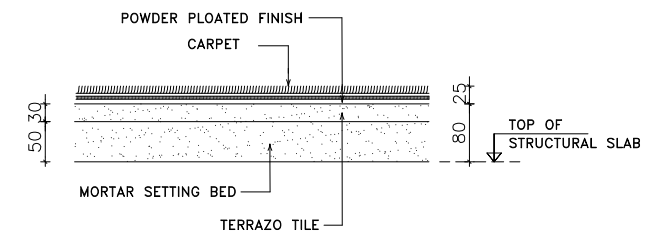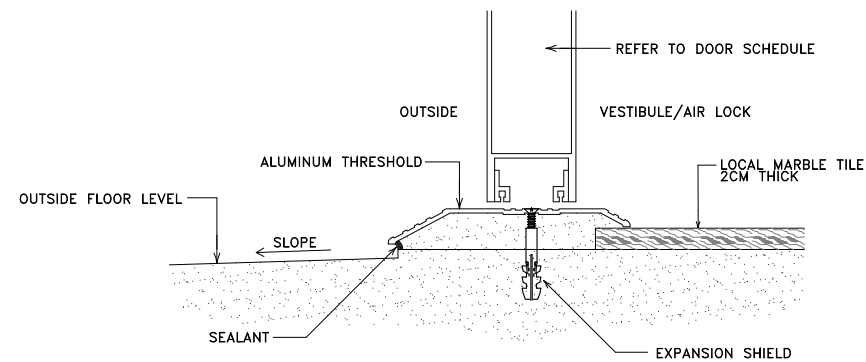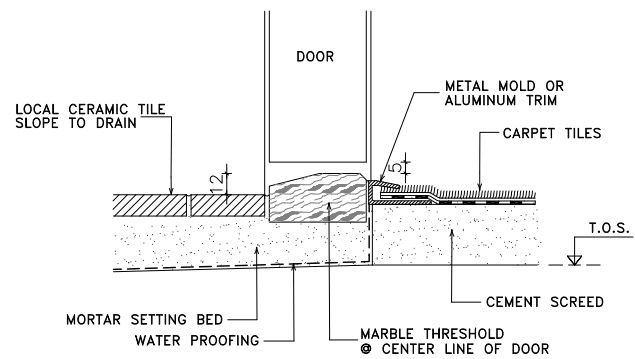

4 CERAMIC/CARPET TRANSITION
A110200 SCALE: 1:4 M.

5 TYPICAL CARPET FINISH
A110200 SCALE: 1:4 M.

6 ENTRANCE THRESHOLD
A110200 SCALE: 1:4 M.

REV.	DATE	BY	DESCRIPTION

KEY PLAN

CONSULTANT



PROJECT

PRIVATE HOUSING COMPLEX
AL NAKHEEL / RIYADH - SAUDI ARABIA

OWNER


SHEET TITLE

MISCELLANEOUS DETAIL
THRESHOLD DETAIL


TENDER DOCUMENTS

PROJECT NO. :	0502	STAGE :	TENDER DOCUMENT
DESIGNED BY :	A. AL NAKHEEL	DRAWN BY :	A - A
DATE :	FEB. 2008	SCALE :	AS SHOWN


A110200 0

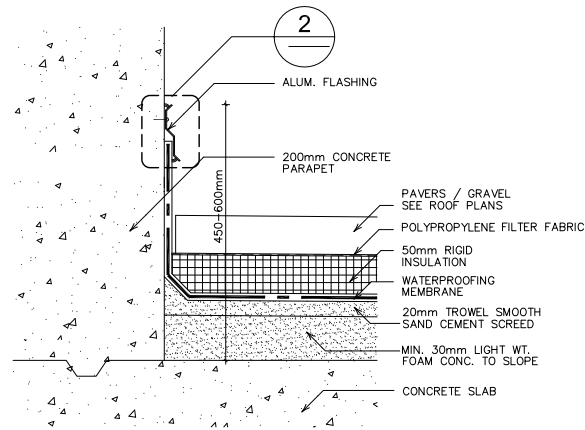


1 TYPICAL ROOFING DETAIL AT PARAPET
A110400 SCALE: 1:5 M.

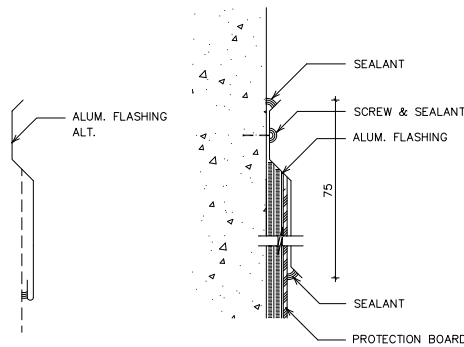


2 TYPICAL FLASHING DETAIL
A110400 SCALE: 1:1 M.

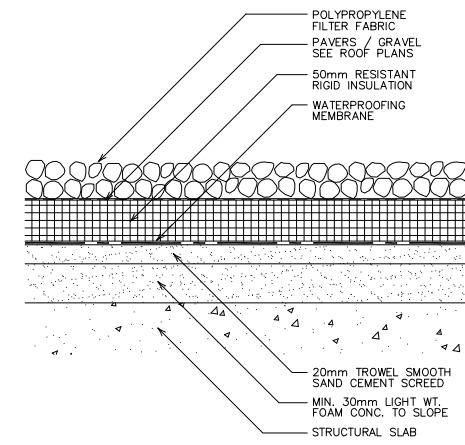


3 TYPICAL ROOFING DETAIL
A110400 SCALE: 1:5 M.

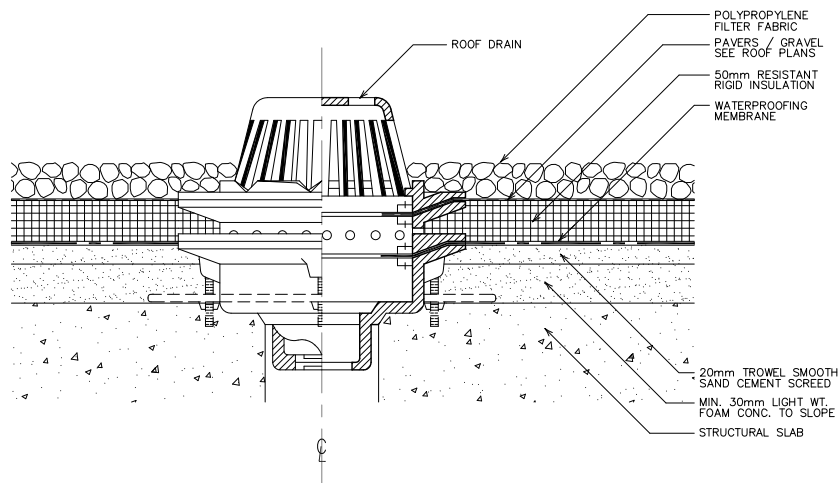


4 TYPICAL ROOFING DETAIL AT ROOF DRAIN
A110400 SCALE: 1:5 M.

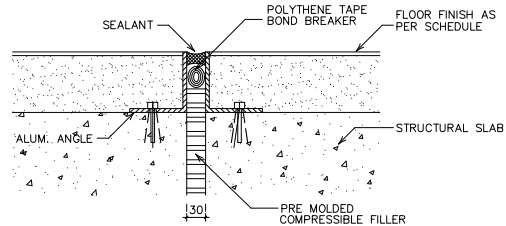


5 EXPANSION JOINT AT FLOOR FINISH
A110400 SCALE: 1:5 M.

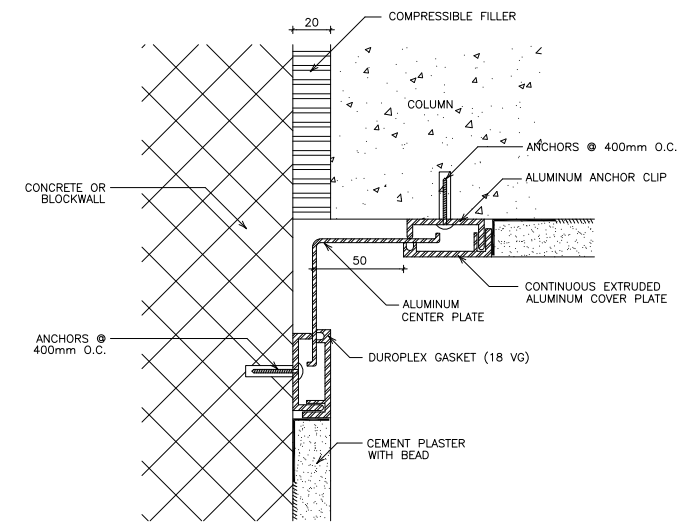


6 EXPANSION JOINT BETWEEN COLUMNS
A110400 SCALE: 1:2 M.

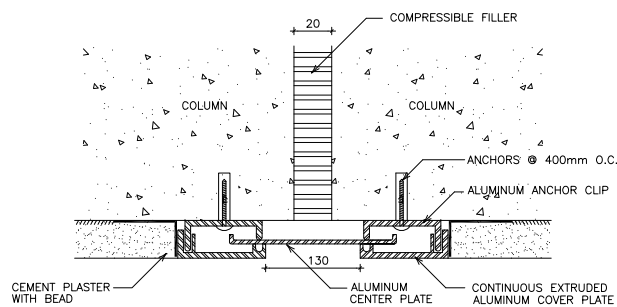

7 EXPANSION JOINT AT BASE
A110400 SCALE: 1:2 M.

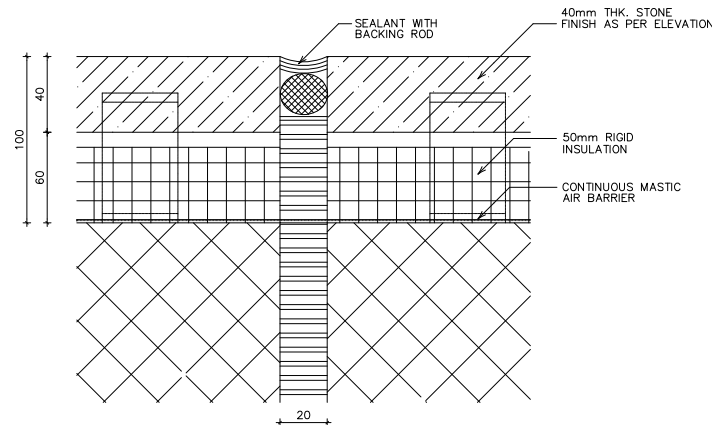

8 EXPANSION JOINT AT EXTERNAL STONE FINISH
A110400 SCALE: 1:2 M.

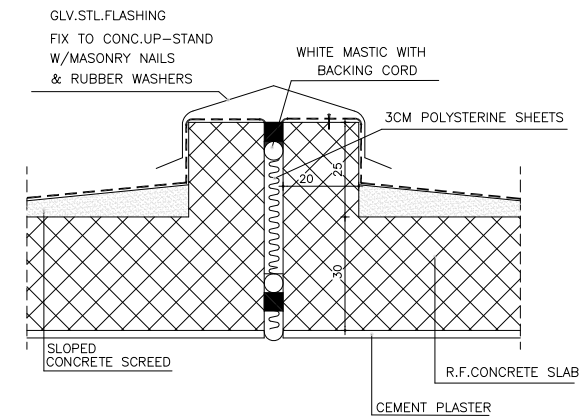

9 EXPANSION JOINT AT ROOF
A110400 SCALE: 1:10 M.



REV.	DATE	BY	DESCRIPTION

KEY PLAN

CONSULTANT



PROJECT

PRIVATE HOUSING COMPLEX
AL NAKHEEL / RIYADH - SAUDI ARABIA

OWNER




SHEET TITLE

MISCELLANEOUS DETAIL
EXPANSION JOINT DETAILS


TENDER DOCUMENTS

PROJECT NO. :	0502	STAGE :	TENDER DOCUMENT
DESIGNED BY :	A. AL RUKHAI	DRAWN BY :	A - A
DATE :	FEB/2006	SCALE :	AS SHOWN

A110400 0

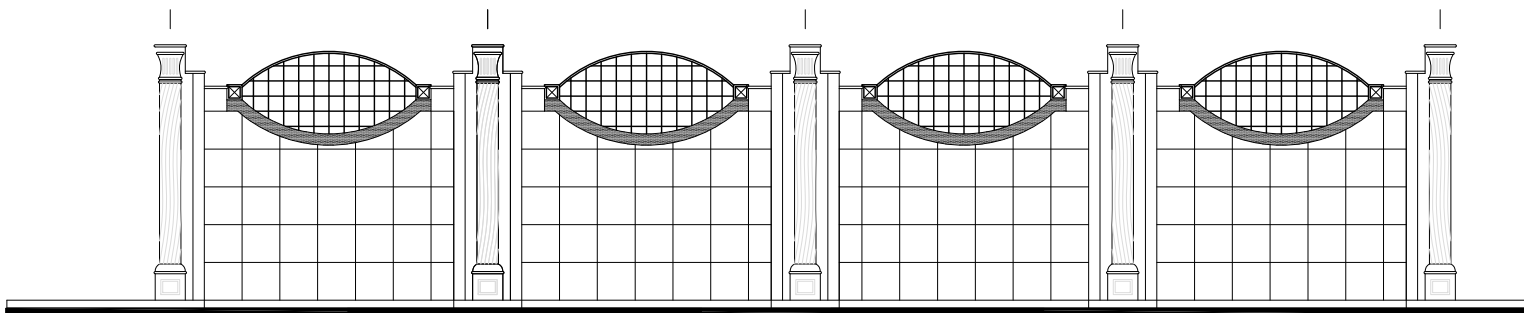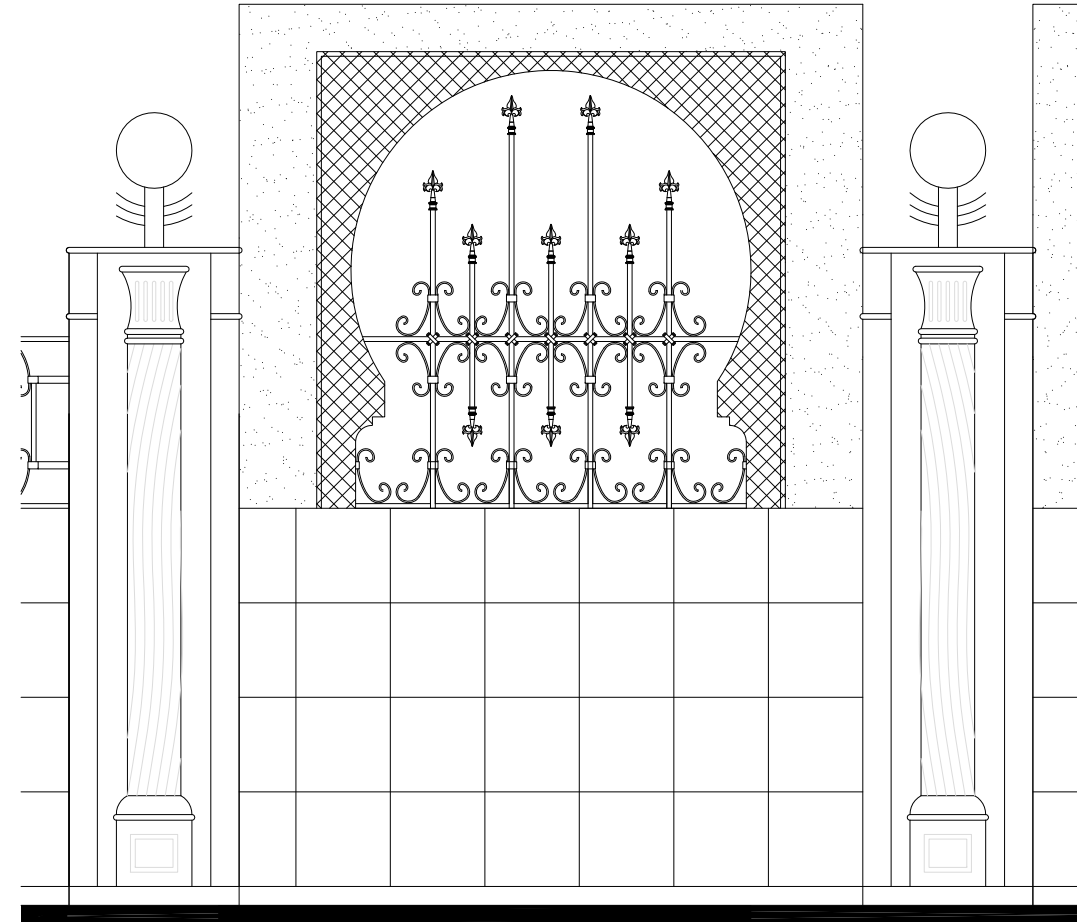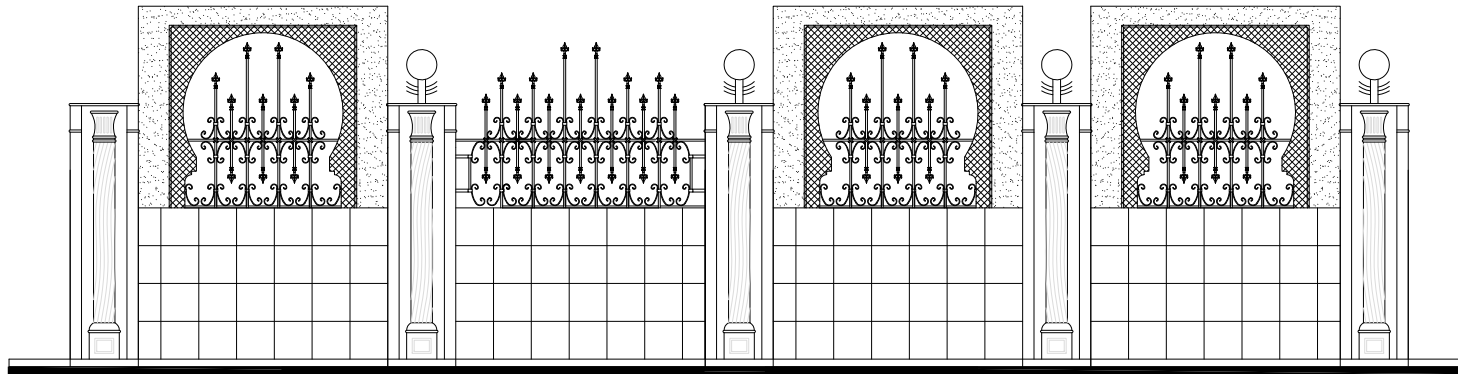

E:\0521 nakheel villa\OLD\in-out\NAKHEEL PALACE\EXISTING VILLA\pics\DSC00070.JPG

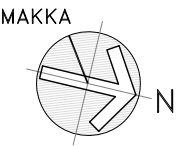

REV.	DATE	BY	DESCRIPTION

KEY PLAN

CONSULTANT



PROJECT

PRIVATE HOUSING COMPLEX
AL NAKHEEL / RIYADH - SAUDI ARABIA

OWNER

SHEET TITLE






ARCHITECTURAL
FENCE DETAILS
PROPOSED

TENDER DOCUMENTS


PROJECT NO. :	P0521	STAGE :	WORKING DRAWINGS
DESIGNED BY :	Proportion Group	DRAWN BY :	CAD
DATE :	JAN. 2008	SCALE :	1:100M

A110600
ARCHITECTURAL


REVISION
0

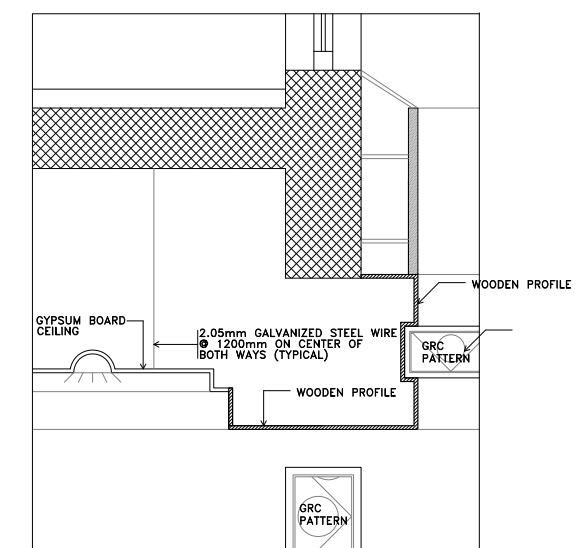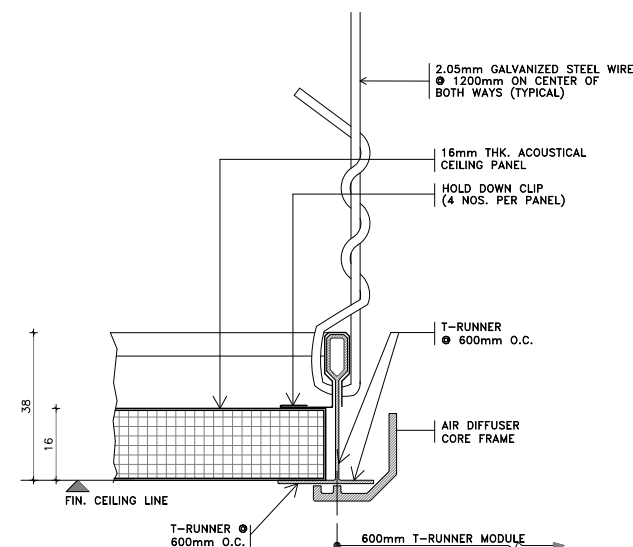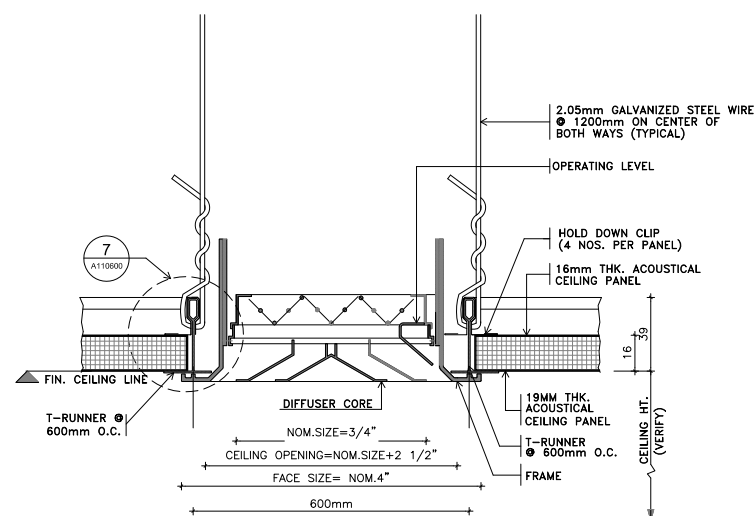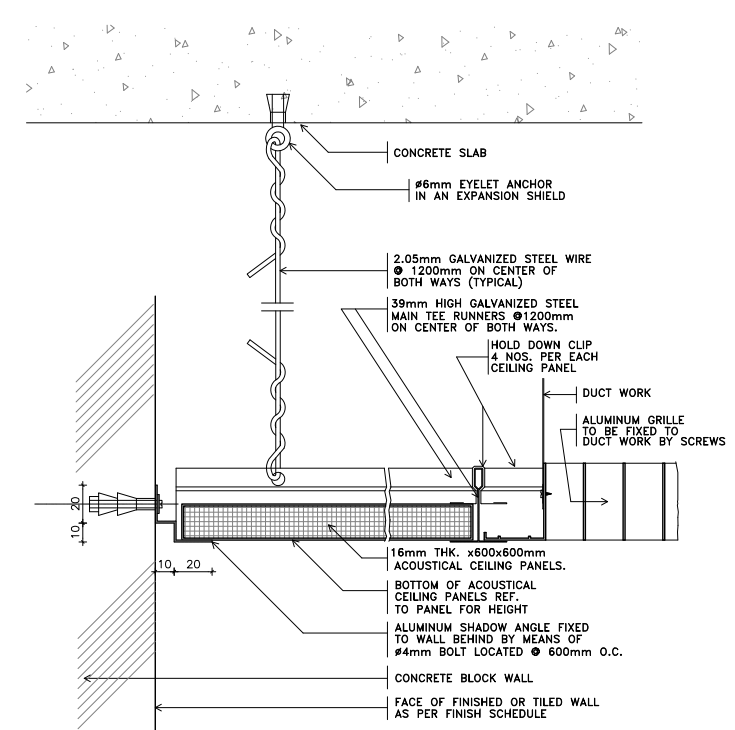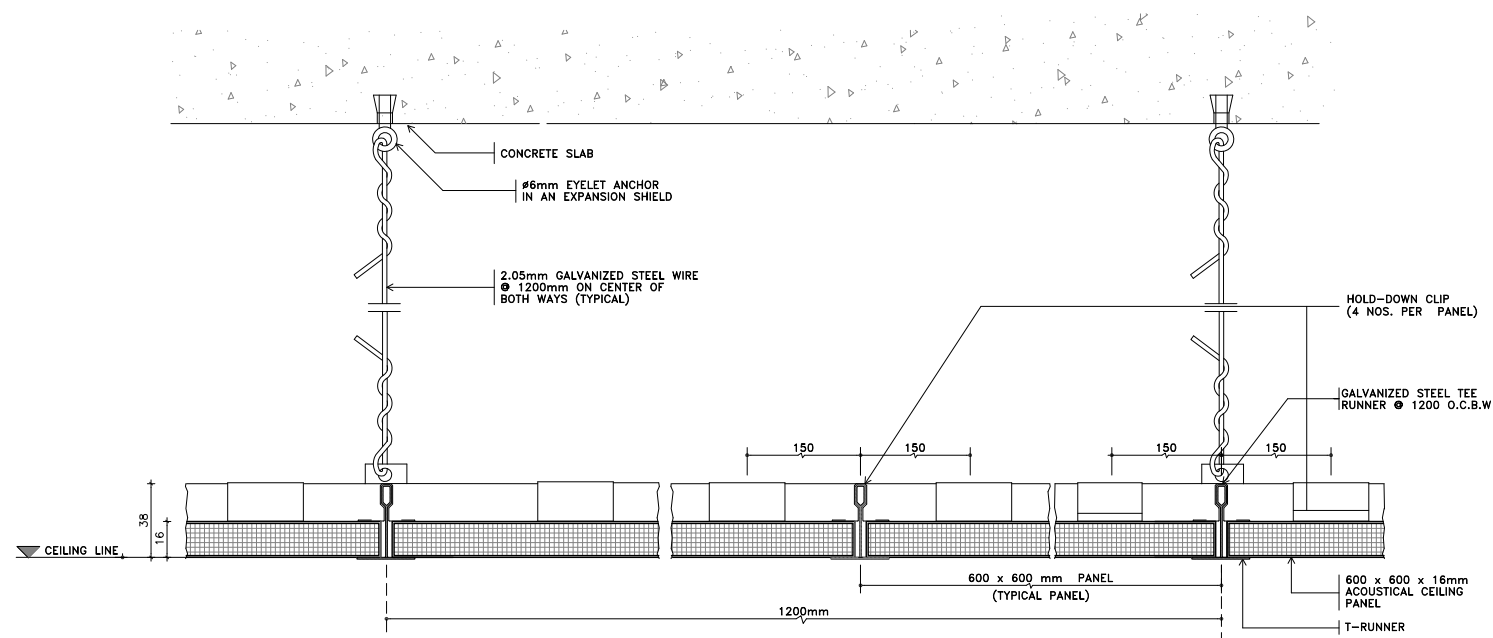


REV.	DATE	BY	DESCRIPTION		
KEY PLAN					
CONSULTANT					
 الشب الإستشارات الهندسية Proportions Consulting Engineering Tel: 2752277, Fax: 2757722 P.O.Box 75453, Riyadh-11578					
PROJECT					
PRIVATE HOUSING COMPLEX AL NAKHEEL / RIYADH - SAUDI ARABIA					
OWNER					
SHEET TITLE					
MISCELLANEOUS DETAIL FALSE CEILING DETAILS 2					
TENDER DOCUMENTS					
PROJECT NO. :	0502	STAGE :	TENDER	DOCUMENT	
DESIGNED BY :	A. AL RUMMAN	DRAWN BY :	A	A	
DATE :	FEB.2008	SCALE :	AS SHOWN	REVISION	
A110800				0	

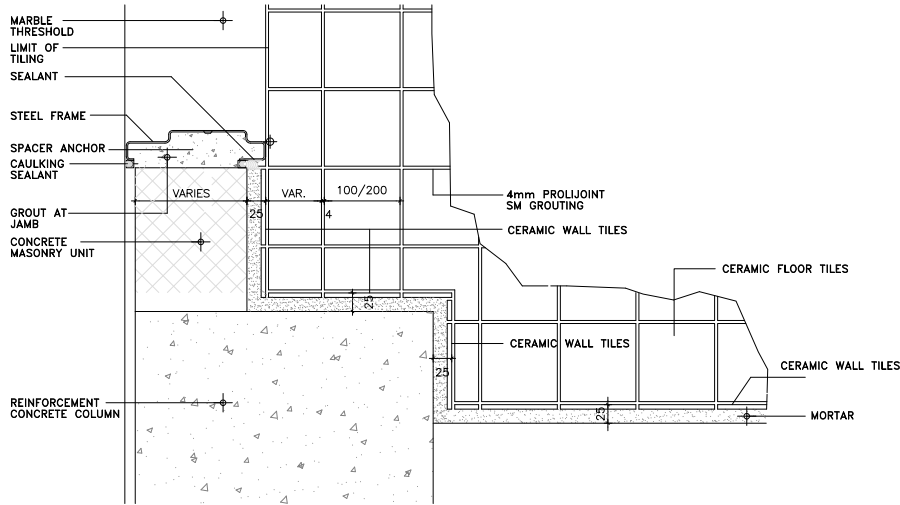


1 DETAIL AT CORNERS AND DOOR JAMB
SCALE: 1:5 M.

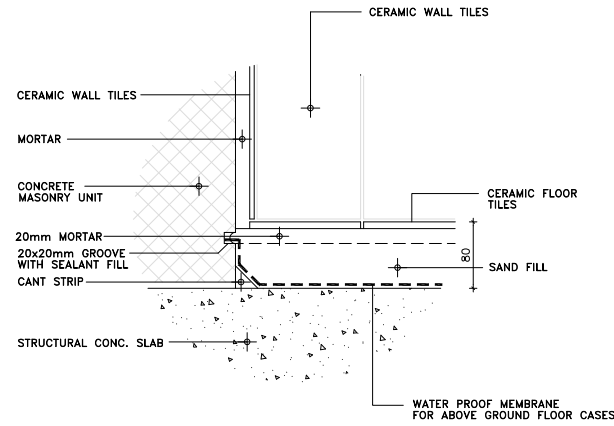


2 SECTION DETAIL FOR BASE TILES
SCALE: 1:5 M.

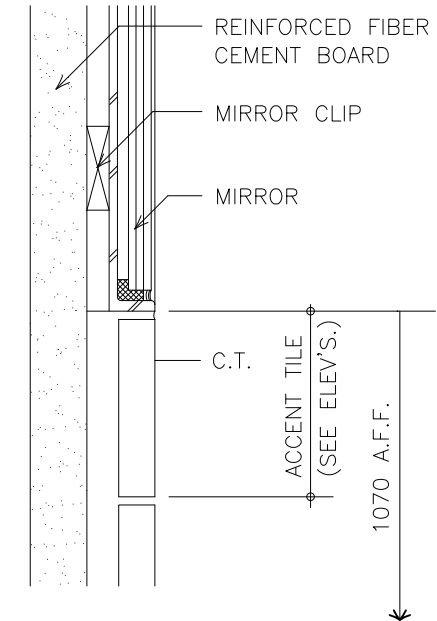


3 MIRROR SECTION
SCALE: N.T.S.

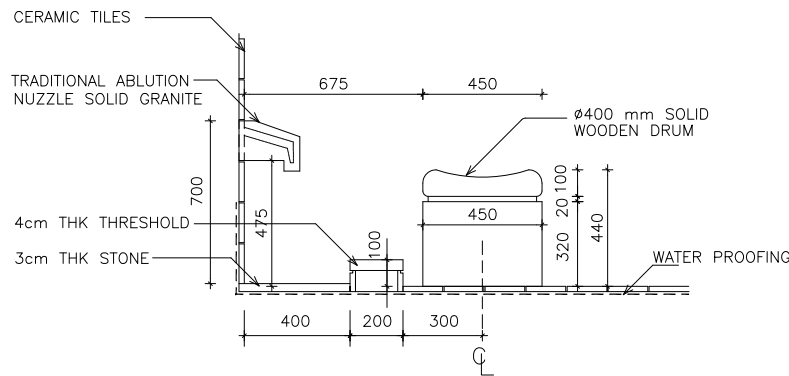


4 SECTION AT ABLUTION
SCALE: N.T.S.

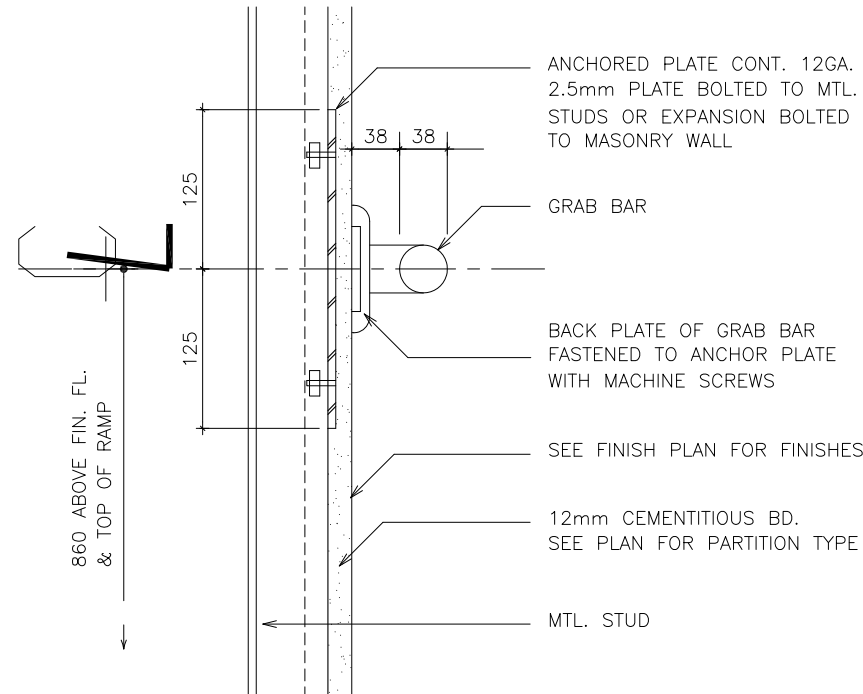

5 GRAB BAR FIXING DETAIL
SCALE: N.T.S.

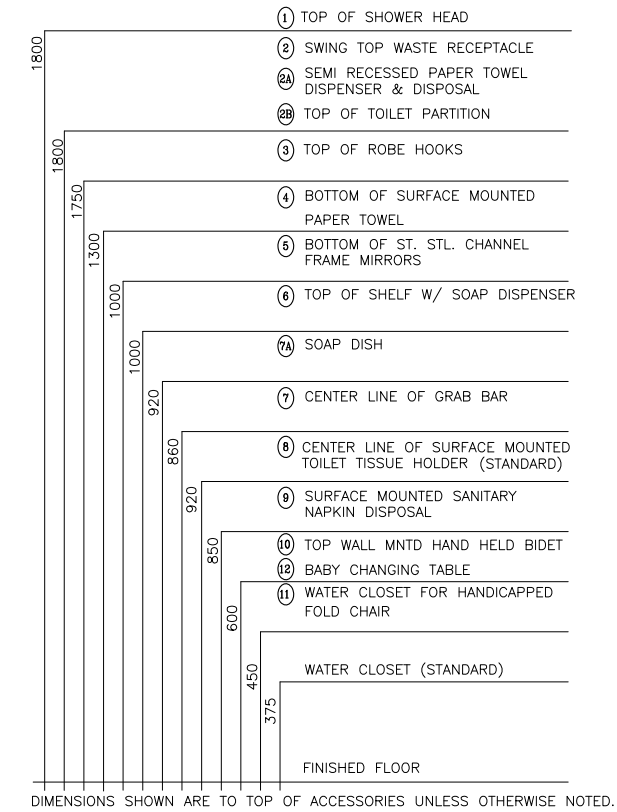

6 TOILET ACCESSORIES & FIXTURE MOUNTING HEIGHT
SCALE: N.T.S.

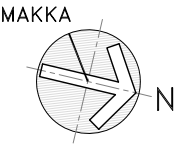

REV.	DATE	BY	DESCRIPTION

KEY PLAN

CONSULTANT
النسب للإستشارات الهندسية
Proportions Consulting Engineering
Tel: 2752277, Fax: 2757722 P.O.Box 75453, Riyadh-11578


PROJECT
PRIVATE HOUSING COMPLEX
AL NAKHEEL / RIYADH - SAUDI ARABIA

OWNER




SHEET TITLE
MISCELLANEOUS DETAIL
WET AREAS DETAILS

TENDER DOCUMENTS			
PROJECT NO.:	0502	STAGE:	TENDER DOCUMENT
DESIGNED BY:	A. AL RUDHAN	DRAWN BY:	A - A
DATE:	FEB.2008	SCALE:	AS SHOWN

A110900 0

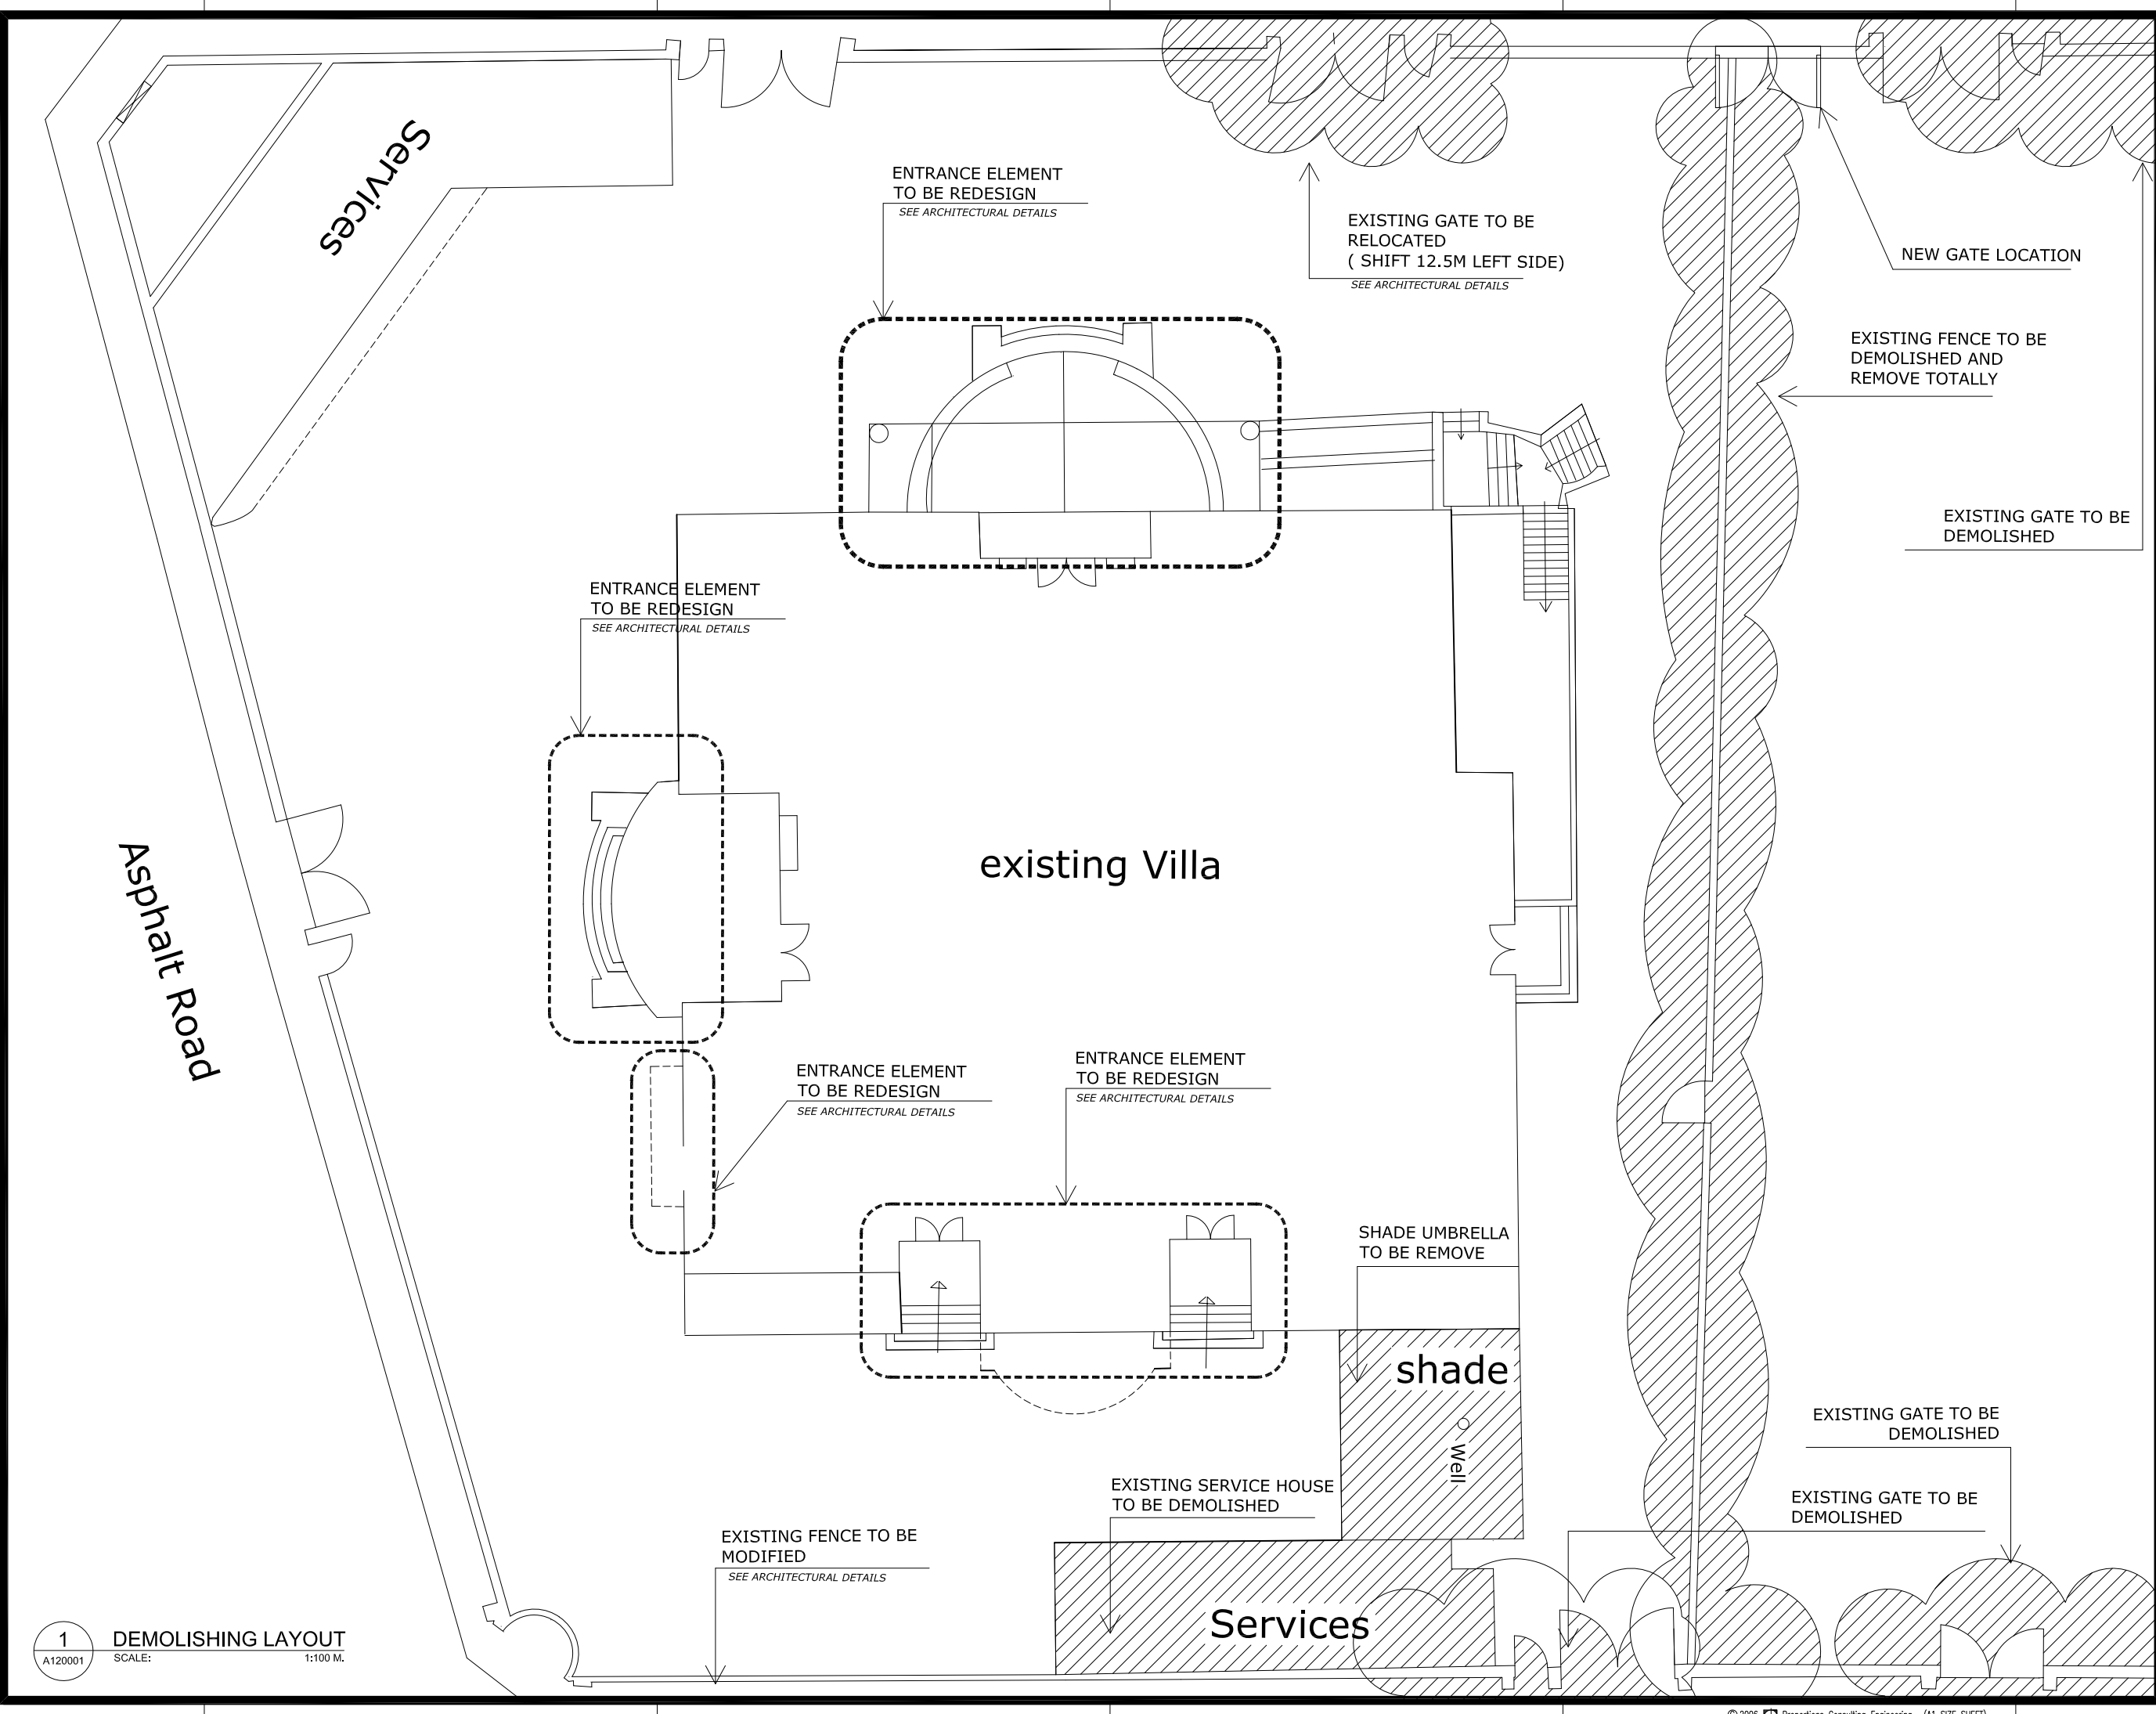

REV.	DATE	BY	DESCRIPTION
KEY PLAN			
CONSULTANT			
 النسب للإستشارات الهندسية Proportions Consulting Engineering Tel: 2752277, Fax: 2757722 P.O.Box 75453, Riyadh-11578			
PROJECT			
PRIVATE HOUSING COMPLEX AL NAKHEEL / RIYADH - SAUDI ARABIA			
OWNER			
SHEET TITLE			
EXISTING BUILDING DEMOLISHING LAYOUT			
TENDER DOCUMENTS			
PROJECT NO. :	P0521	STAGE :	WORKING DRAWINGS
DESIGNED BY :	Proportion Group	DRAWN BY :	CAD
DATE :	JAN. 2008	SCALE :	1:100M
A120001 ARCHITECTURAL			REVISION 0

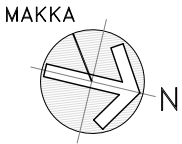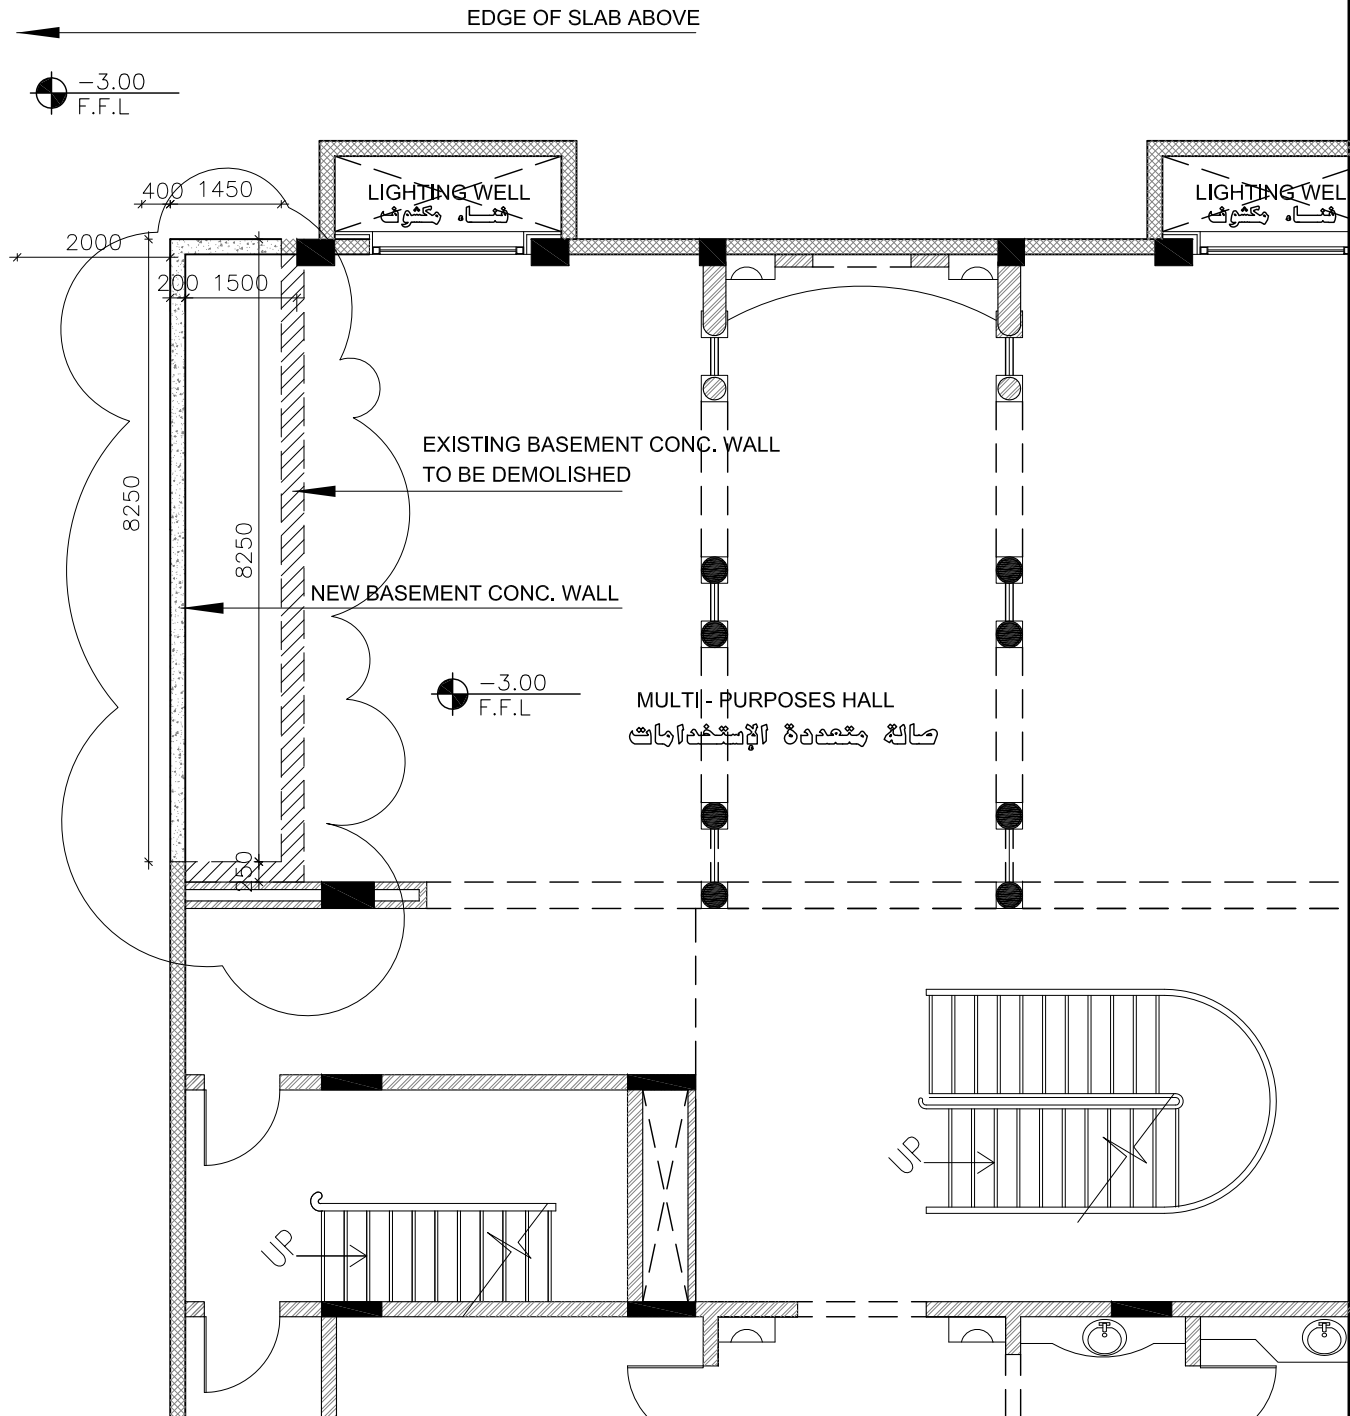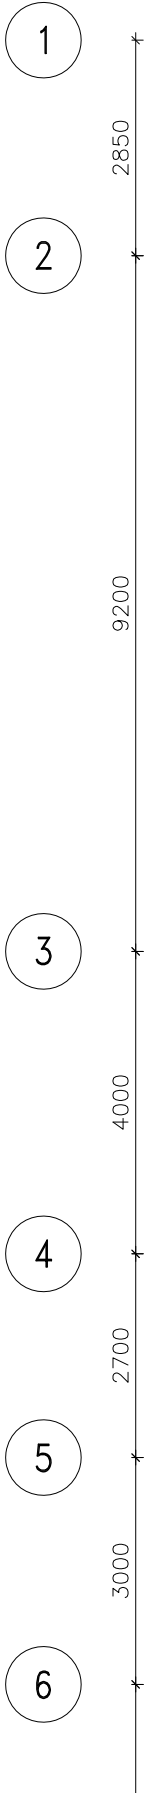

REV.	DATE	BY	DESCRIPTION

KEY PLAN

CONSULTANT



PROJECT

PRIVATE HOUSING COMPLEX
AL NAKHEEL / RIYADH - SAUDI ARABIA


OWNER

SHEET TITLE

EXISTING BUILDING
BASEMENT FLOOR PLAN

TENDER DOCUMENTS

PROJECT NO. :	P0521	STAGE :	WORKING DRAWINGS
DESIGNED BY :	Proportion Group	DRAWN BY :	CAD
DATE :	JAN. 2008	SCALE :	1:50M

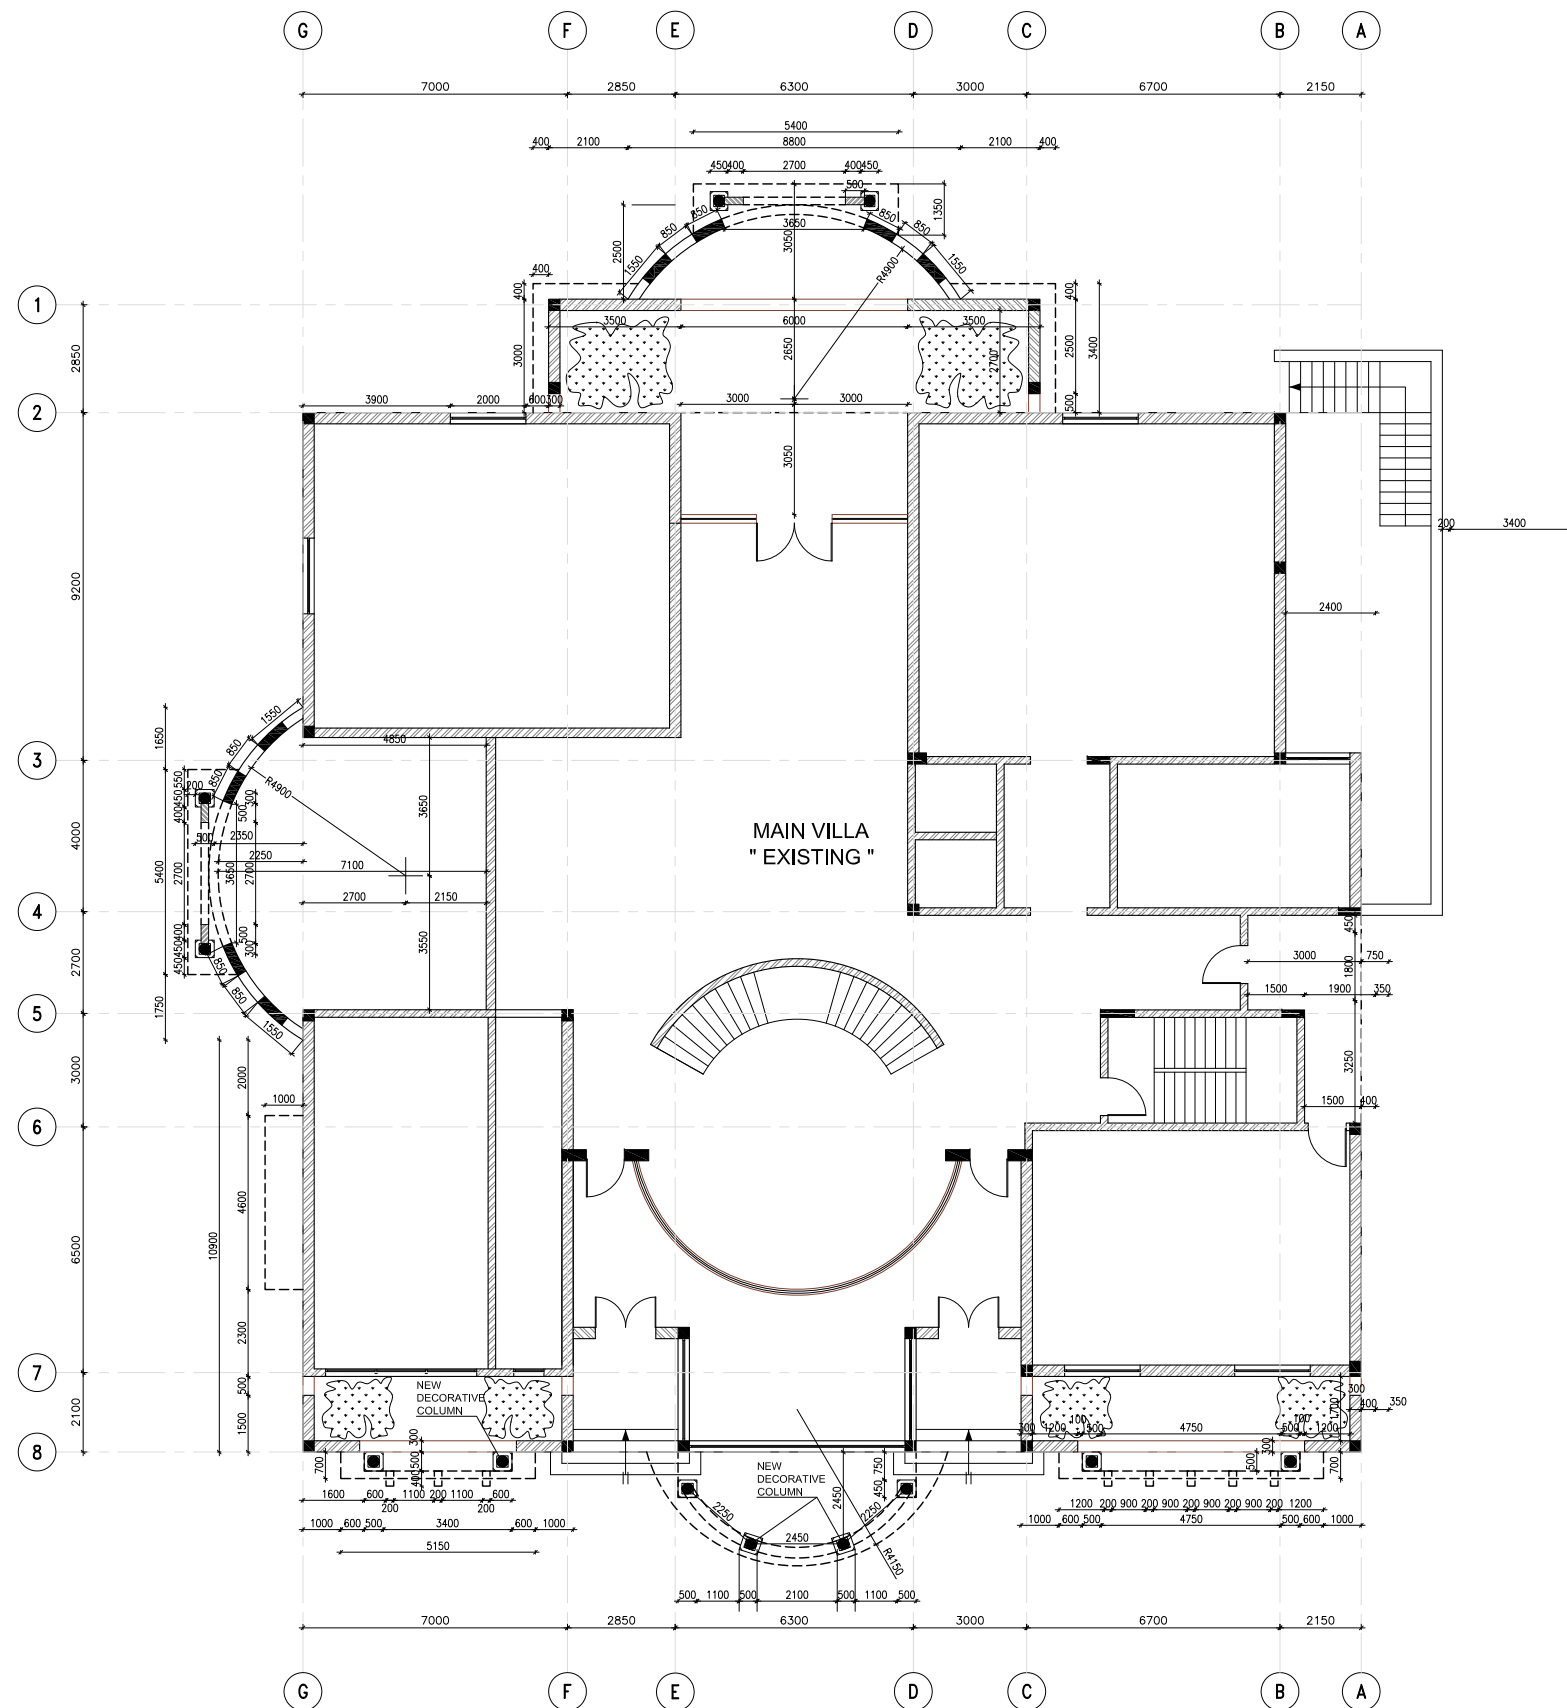

1 GROUND FLOOR PLAN
A120102 SCALE: 1:100 M.

REV.	DATE	BY	DESCRIPTION

KEY PLAN

CONSULTANT

النسب للإستشارات الهندسية
Proportions Consulting Engineering
Tel: 2792277, Fax: 2797722 P.O.Box 75453, Riyadh-11578

PROJECT

PRIVATE HOUSING COMPLEX
AL NAKHEEL / RIYADH - SAUDI ARABIA

OWNER


SHEET TITLE

EXISTING BUILDING
GROUND FLOOR PLAN

TENDER DOCUMENTS			
PROJECT NO. :	P0521	STAGE :	WORKING DRAWINGS
DESIGNED BY :	Proportion Group	DRAWN BY :	CAD
DATE :	JAN. 2008	SCALE :	1:100M


A120102
ARCHITECTURAL

REVISION
0

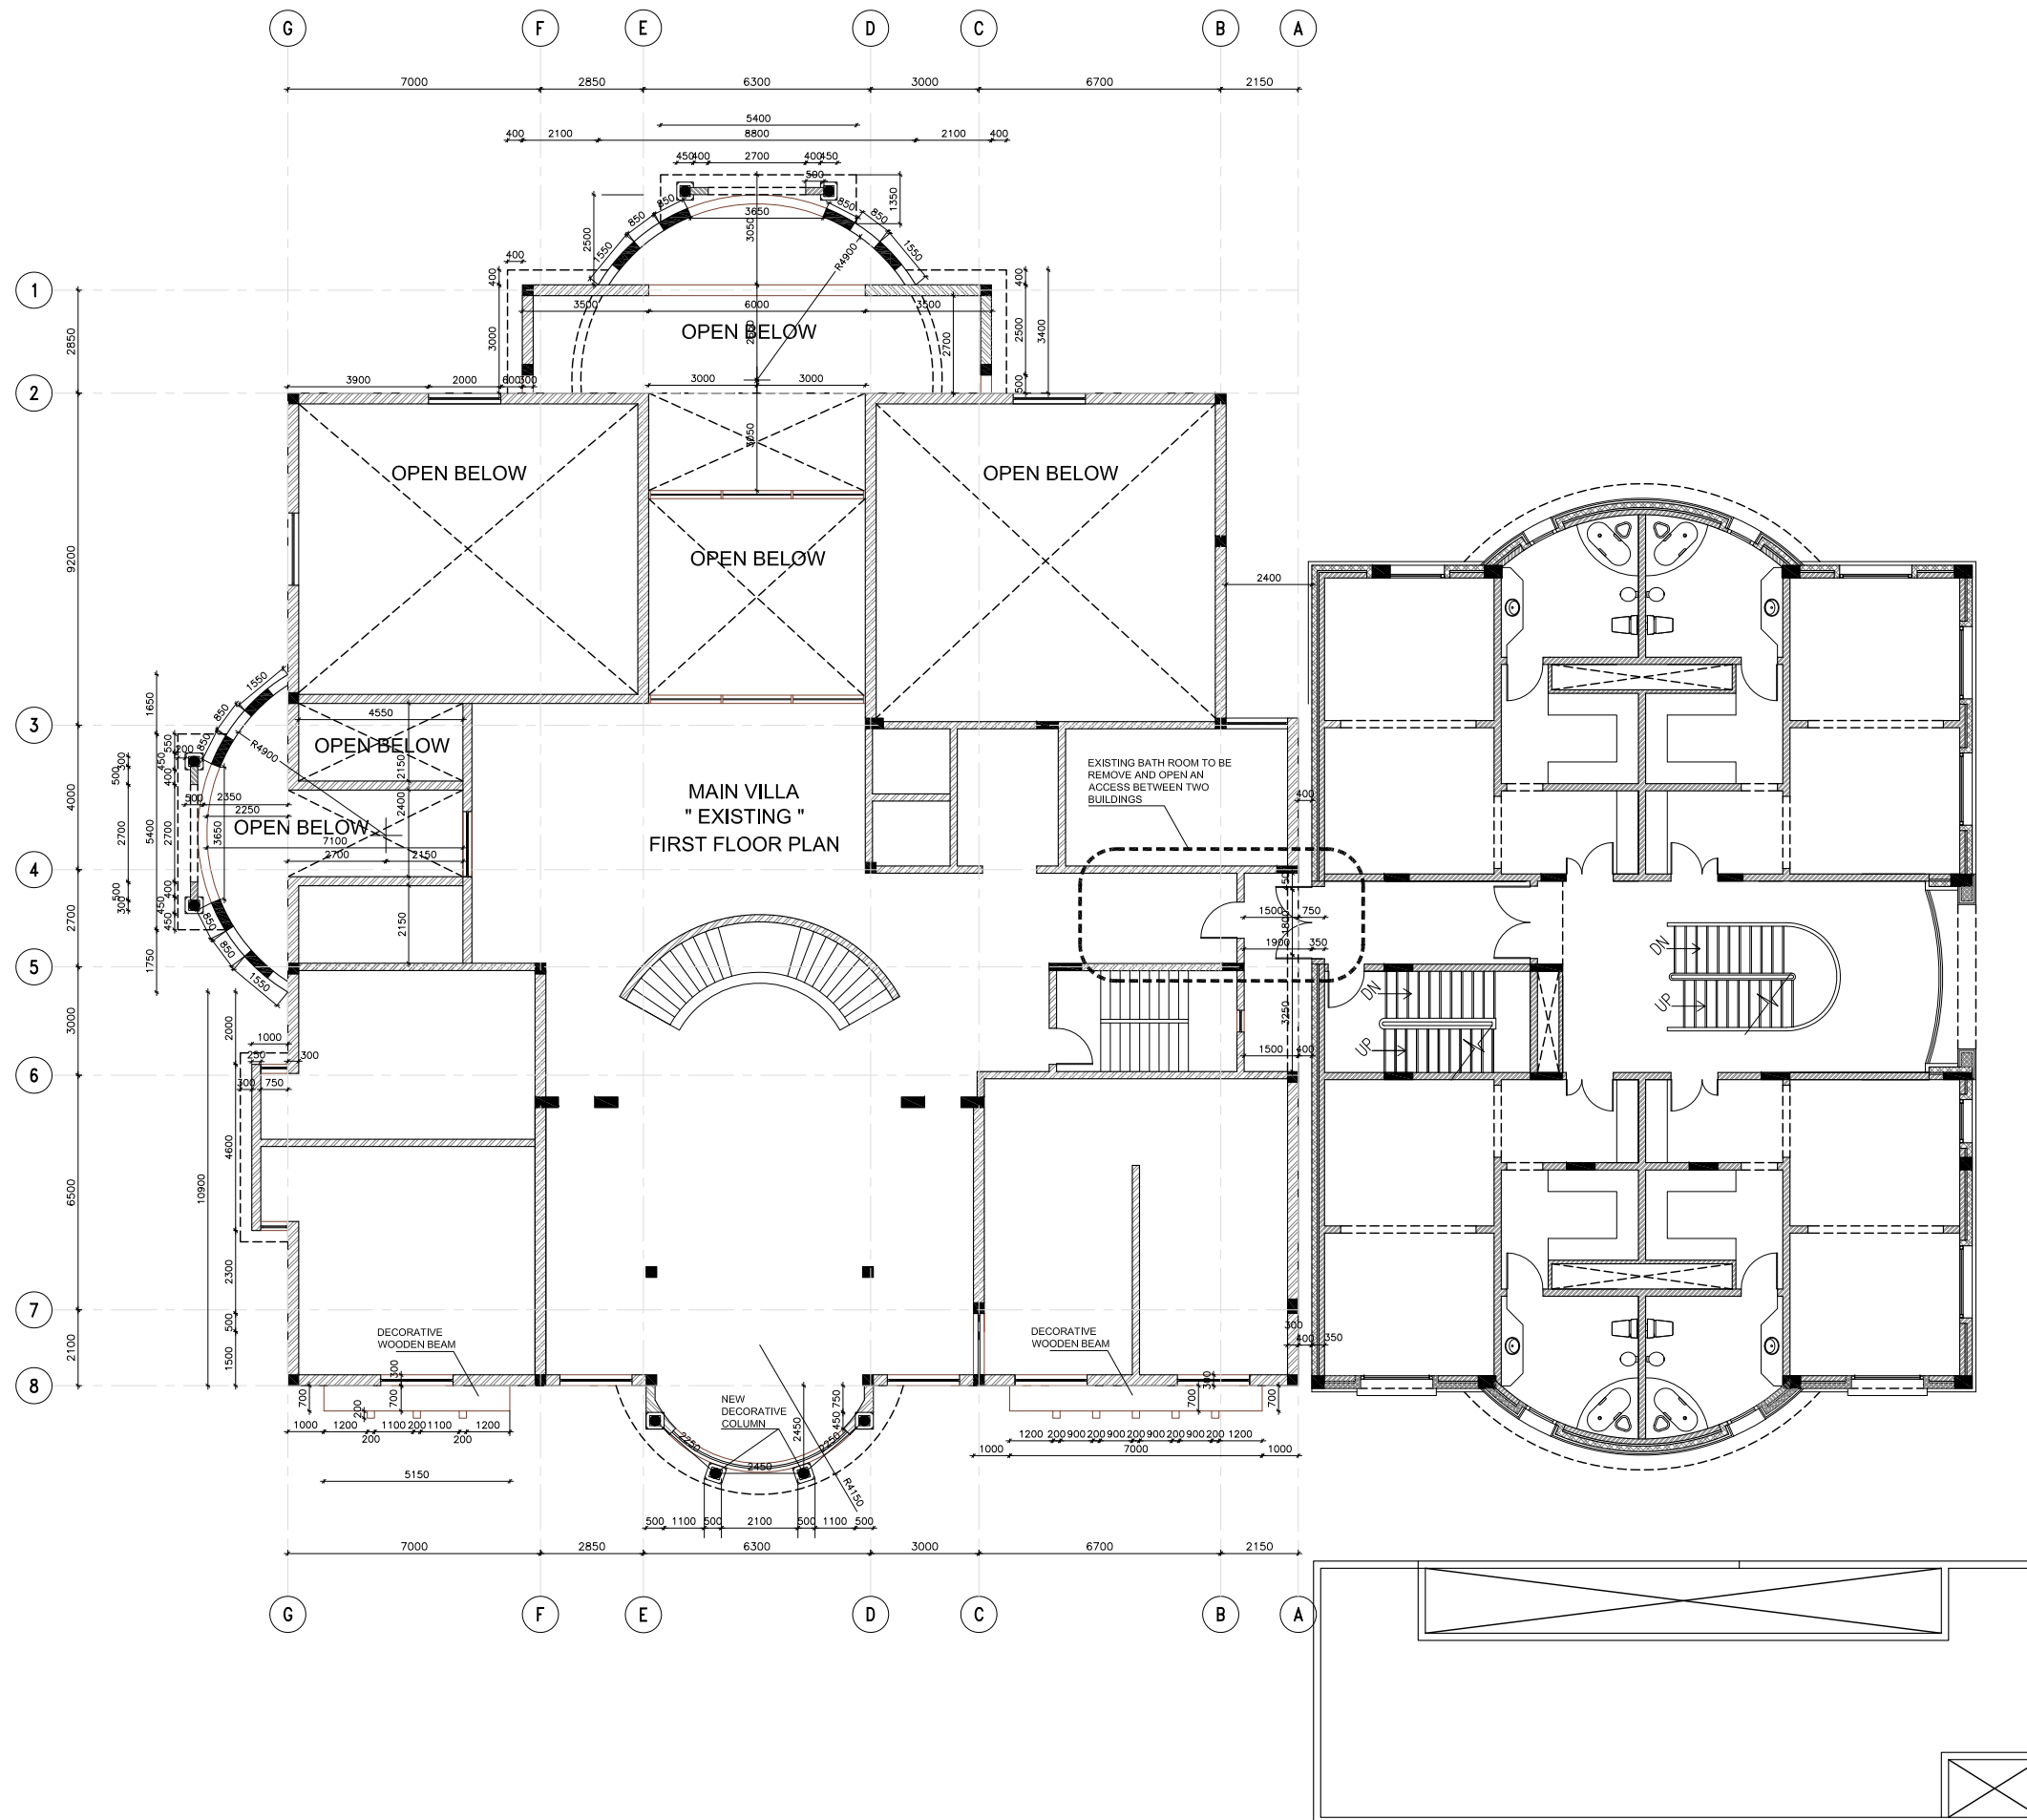

1 FIRST FLOOR PLAN
A120103 SCALE: 1:100 M.

REV.	DATE	BY	DESCRIPTION
KEY PLAN			
CONSULTANT			
 النسب للإستشارات الهندسية Proportions Consulting Engineering Tel: 2792277, Fax: 2797722 P.O.Box 75453, Riyadh-11578			
PROJECT			
PRIVATE HOUSING COMPLEX AL NAKHEEL / RIYADH - SAUDI ARABIA			
OWNER			
SHEET TITLE			
EXISTING BUILDING FIRST FLOOR PLAN			
TENDER DOCUMENTS			
PROJECT NO. :	P0521	STAGE :	WORKING DRAWINGS
DESIGNED BY :	Proportion Group	DRAWN BY :	CAD
DATE :	JAN. 2006	SCALE :	1:100M
A120103 ARCHITECTURAL			REVISION 0

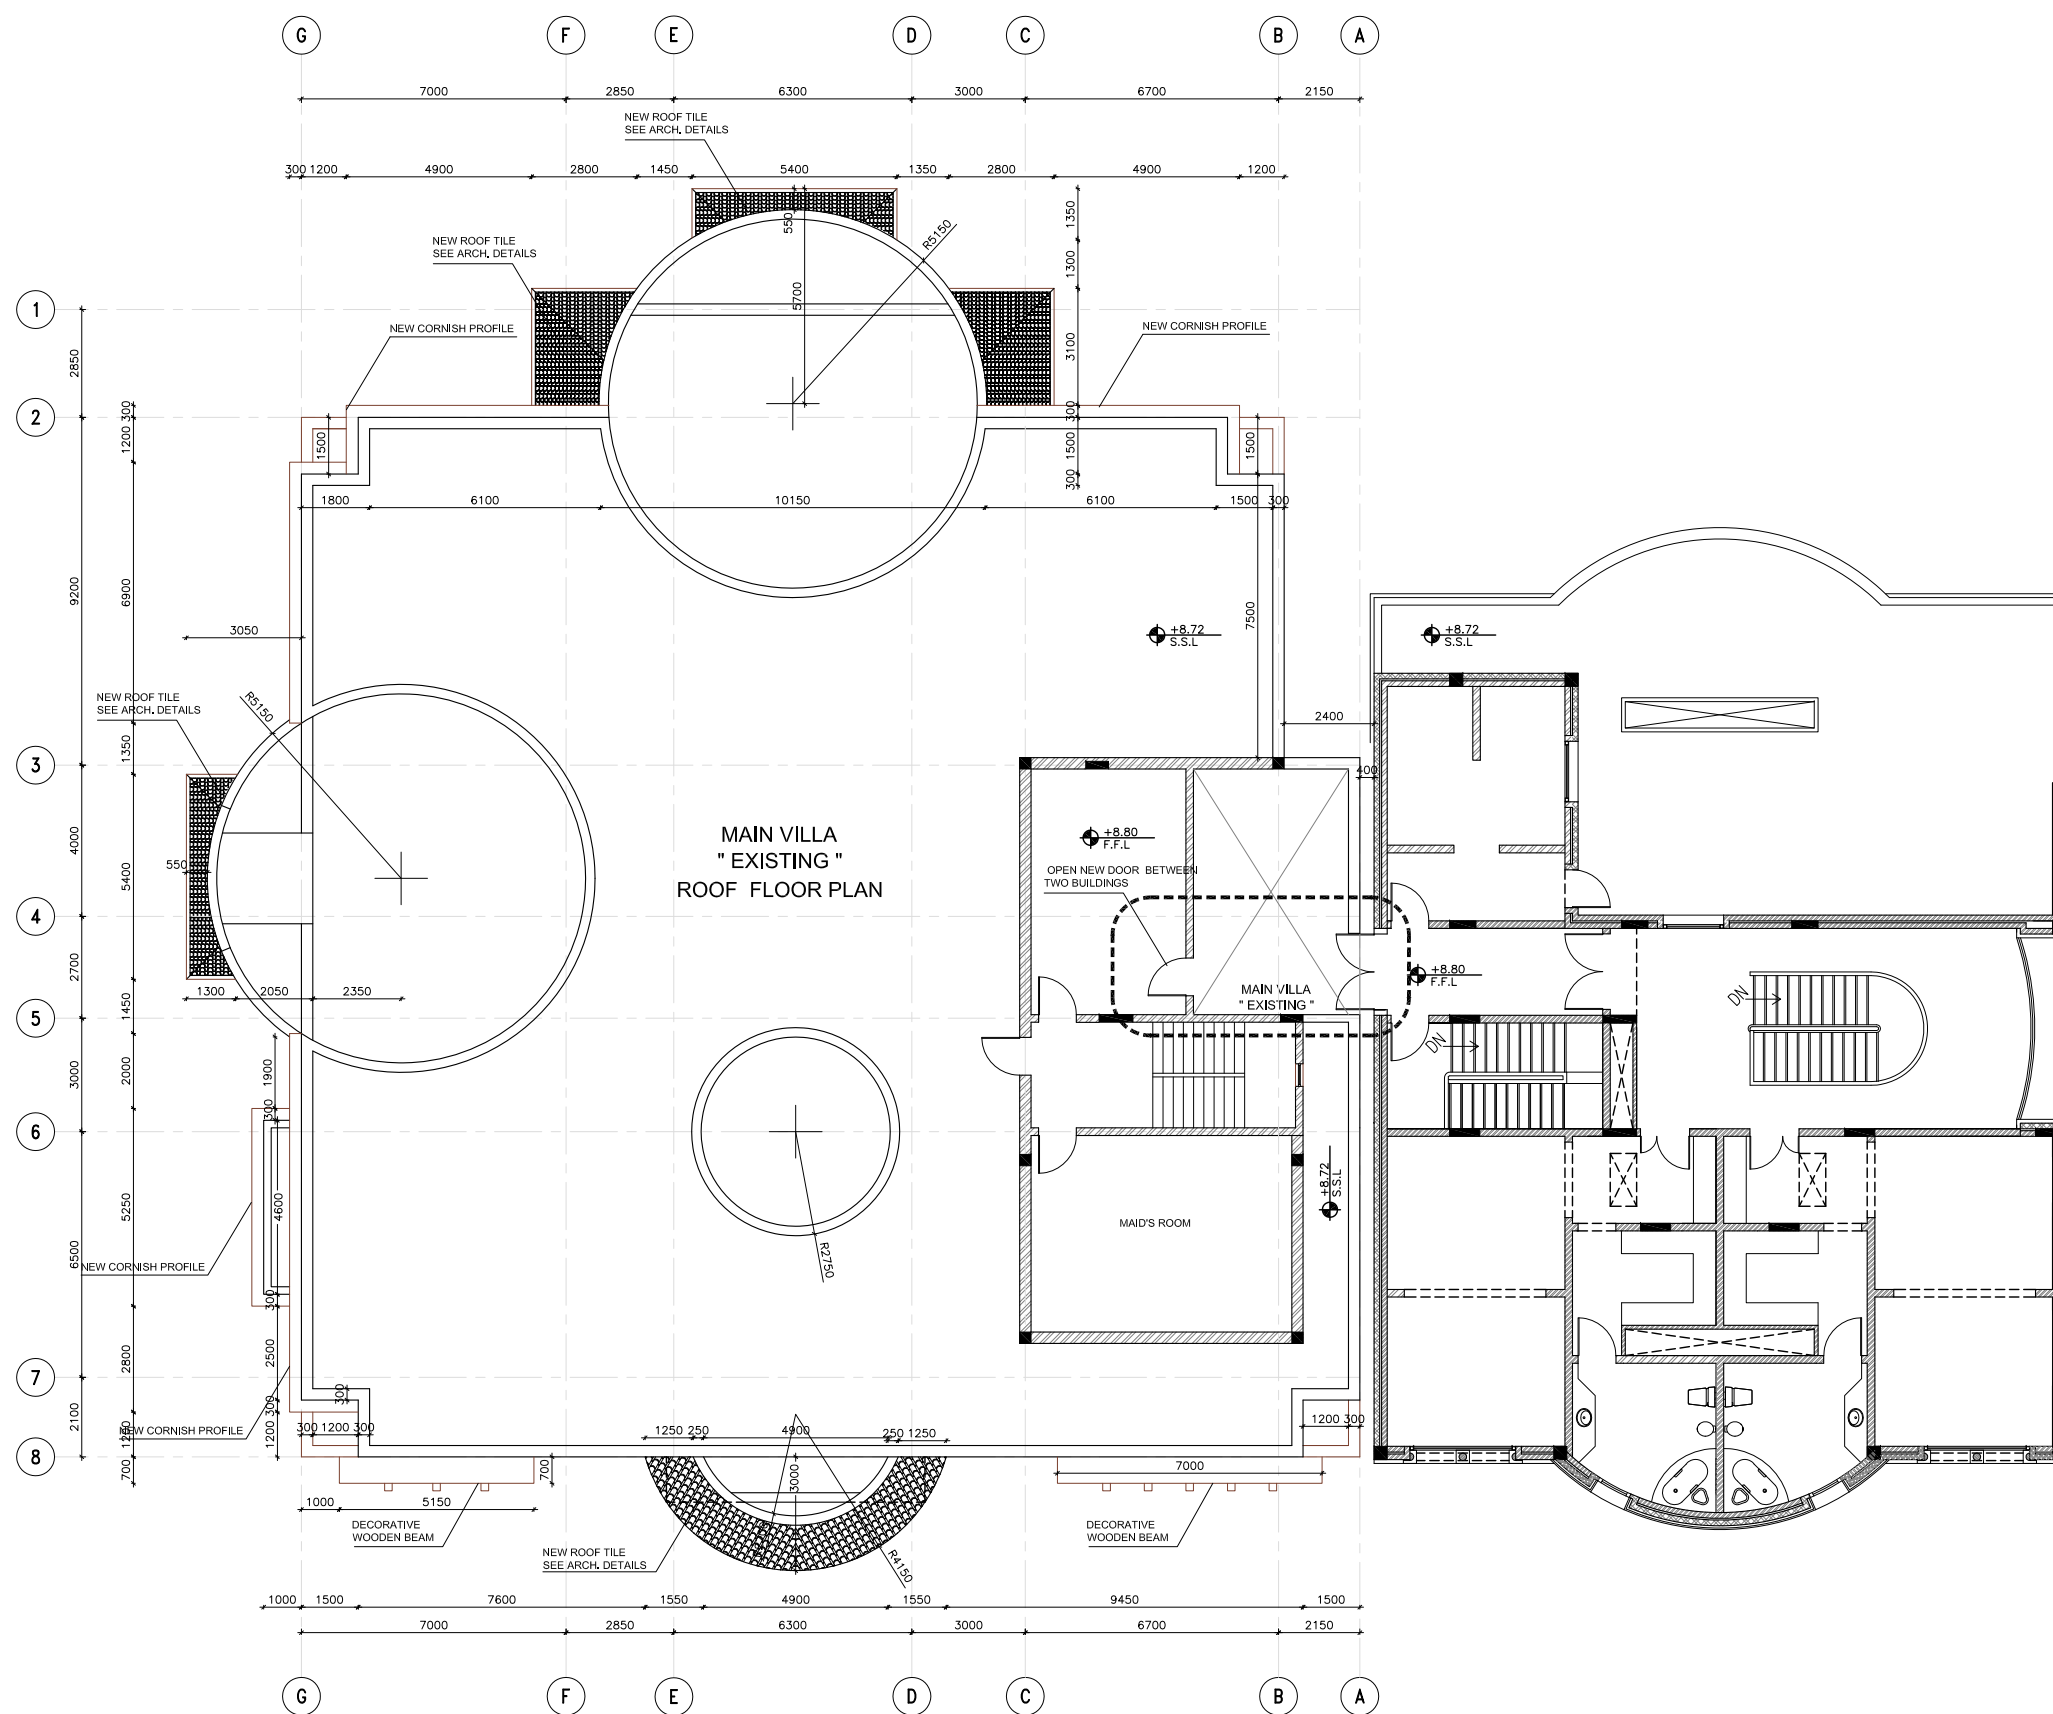

SCALE: 1:100 M.

REVIS	0
-------	---

FINISHING SCHEDULE



BASEMENT FLOOR		STRUCTURAL RM. DIMENSIONS / m			FLOOR										SKIRTING			WALLS						CEILING					PARTITIONS				NOTES	NOTES	
					CERAMIC TILE (50*50) cm	ANTI SLIP CERAMIC TILE (20*20)	CERAMIC TILE (30*30) cm	LOCAL MARBLE	TERRAZO TILES (30*30)	CEMENT TILES (40*40)	CEMENT SCREED	INTERLOCKING TILES	TERRACOTA TILES 300x300 DIAG	10cm. VINYL ROLL (P.V.C)	CERAMIC TILE (40*8) cm	10cm. VINYL ROLL (P.V.C)	LOCAL MARBLE	TERRAZO TILES (30*10)	TERRACOTA TILES	STONE	GLAZED CERAMIC TILE(20*20) cm	GLAZED CERAMIC TILE(30*30) cm	PAINTED PLASTER (SMOOTH)	ANTI FUNGUS, ANTI BACTERIAL	PAINTED PLASTER (SMOOTH)	FABRIC OR WALL PAPER	PAINTED GYPSUM BOARD	FABRIC OR WALL PAPER	ACOUSTICAL GYPSUM TILES(60x60)	WOODEN PANEL CEILING	PAINTED PLASTER (SMOOTH)	10cm METAL STRIPS				ANTI FUNGUS, ANTI BACTERIAL GYPSUM TILES(60x60)	TEMPERED GLASS	GYPSUM BOARD	GLASS BLOCK(10)CM	
ROOM NO.	ROOM NAME	LENGTH	WIDTH	CEILING HEIGHT	

- * ACTUAL DIMENSION MUST BE TAKEN ON SITE.
- * WALL PAINTED WITH EMULSION PAINT FOR COLORS REFER TO INTERIOR DESIGNER.
- * FOR DRAPERIES STYLE REFER TO INTERIOR DESIGNER.
- * # = IRREGULAR SHAPE

REV.	DATE	BY	DESCRIPTION

KEY PLAN

CONSULTANT



النسب للإستشارات الهندسية
Proportions Consulting Engineering
Tel: 2752277, Fax: 2757722 P.O.Box 75453, Riyadh-11578

PROJECT

PRIVATE HOUSING COMPLEX
AL NAKHEEL / RIYADH - SAUDI ARABIA

OWNER

SHEET TITLE

ARCHITECTURAL
FINISHING SCHEDULE

TENDER DOCUMENTS			
PROJECT NO. :	P0521	STAGE :	WORKING DRAWINGS
DESIGNED BY :	Proportion Group	DRAWN BY :	CAD
DATE :	FEB. 2006	SCALE :	1:100M

A050401
ARCHITECTURAL

0

FINISHING SCHEDULE



GROUND FLOOR		STRUCTURAL RM. DIMENSIONS / m			FLOOR								SKIRTING				WALLS						CEILING						PARTITIONS				NOTES	NOTES	
					CERAMIC TILE (50*50) cm	ANTI SLIP CERAMIC TILE (20*20)	CERAMIC TILE (30*30) cm	LOCAL MARBLE	TERRAZO TILES (30*30)	CEMENT TILES (40*40)	CEMENT SCREED	INTERLOCKING TILES	TERRACOTA TILES 300x300 DIAG	10cm. VINYL ROLL (P.V.C)	CERAMIC TILE (40*8) cm	10cm. VINYL ROLL (P.V.C)	LOCAL MARBLE	TERRAZO TILES (30*10)	TERRACOTA TILES	STONE	GLAZED CERAMIC TILE(20*20) cm	GLAZED CERAMIC TILE(30*30) cm	PAINTED PLASTER (SMOOTH)	ANTI FUNGUS, ANTI BACTERIAL	PAINTED PLASTER (SMOOTH)	FABRIC OR WALL PAPER	PAINTED GYPSUM BOARD	FABRIC OR WALL PAPER	ACOUSTICAL GYPSUM TILES(60x60)	WOODEN PANEL CEILING	PAINTED PLASTER (SMOOTH)	10cm METAL STRIPS			ANTI FUNGUS, ANTI BACTERIAL GYPSUM TILES(60x60)	TEMPERED GLASS	GYPSUM BOARD	GLASS BLOCK(10)CM	
ROOM NO.	ROOM NAME	LENGTH	WIDTH	CEILING HEIGHT	</

- * ACTUAL DIMENSION MUST BE TAKEN ON SITE.
- * WALL PAINTED WITH EMULSION PAINT FOR COLORS REFER TO INTERIOR DESIGNER.
- * FOR DRAPERIES STYLE REFER TO INTERIOR DESIGNER.
- * # = IRREGULAR SHAPE

REV.

DATE

BY

DESCRIPTION

KEY PLAN

CONSULTANT

النسب للإستشارات الهندسية

Proportions Consulting Engineering

Tel: 2752277, Fax: 2757722 P.O.Box 75453, Riyadh-11578

PROJECT

PRIVATE HOUSING COMPLEX
AL NAKHEEL / RIYADH - SAUDI ARABIA

OWNER

SHEET TITLE

ARCHITECTURAL
FINISHING SCHEDULE

TENDER DOCUMENTS

PROJECT NO. : P0521

STAGE : WORKING DRAWINGS

DESIGNED BY : Proportion Group

DRAWN BY : CAD

DATE : FEB. 2006


SCALE : 1:100M

A050402
ARCHITECTURAL

0

REVISION


FINISHING SCHEDULE

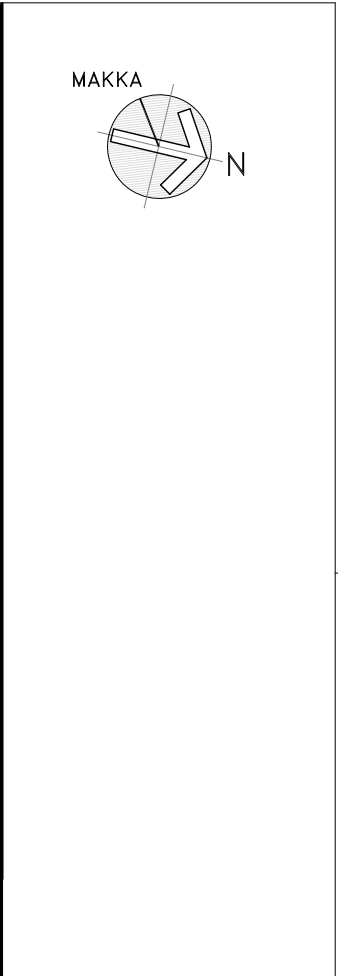


		STRUCTURAL RM. DIMENSIONS / m			FLOOR										SKIRTING		WALLS		CEILING		PARTITIONS		NOTES	
					CERAMIC TILE (50*50) cm	ANTI SLIP CERAMIC TILE (20*20)	CERAMIC TILE (30*30) cm	LOCAL MARBLE	TERRAZO TILES (30*30)	CEMENT TILES (40*40)	CEMENT SCREED	INTERLOCKING TILES	TERRACOTA TILES 300x300 DIAG	10cm. VINYL ROLL (P.V.C)	CERAMIC TILE (40*8) cm	10cm. VINYL ROLL (P.V.C)	LOCAL MARBLE	TERRAZO TILES (30*10)	TERRACOTA TILES	STONE	GLAZED CERAMIC TILE(20*20) cm	GLAZED CERAMIC TILE(30*30) cm		PAINTED PLASTER (SMOOTH)	ANTI FUNGUS, ANTI BACTERIAL	PAINTED PLASTER (SMOOTH)	10cm METAL STRIPS	ANTI FUNGUS, ANTI BACTERIAL GYPSUM TILES(60x60)	TEMPERED GLASS	GYPSUM BOARD	GLASS BLOCK(10)CM	
FIRST FLOOR		LENGTH	WIDTH	CEILING HEIGHT	

REV.	DATE	BY	DESCRIPTION	
KEY PLAN				
CONSULTANT				
 النسب الإستشارات الهندسية Proportions Consulting Engineering Tel. 2752277, Fax. 2757722 P.O.Box 75453, Riyadh-11578				
PROJECT				
PRIVATE HOUSING COMPLEX AL NAKHEEL / RIYADH - SAUDI ARABIA				
OWNER				
SHEET TITLE				
ARCHITECTURAL FINISHING SCHEDULE				
TENDER DOCUMENTS				
PROJECT NO. :	P0521	STAGE :	WORKING DRAWINGS	
DESIGNED BY :	Proportion Group	DRAWN BY :	CAD	
DATE :	FEB. 2006	SCALE :	1:100M	
A050403 ARCHITECTURAL				REVISION 0

FINISHING SCHEDULE

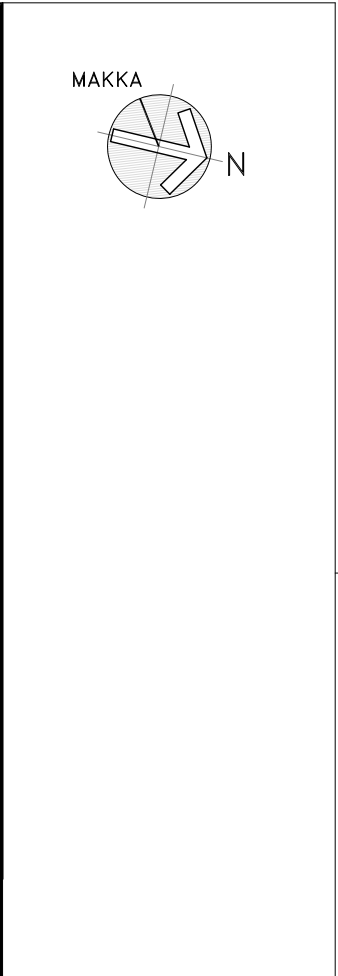
[illegible]

REV.	DATE	BY	DESCRIPTION	
KEY PLAN				
CONSULTANT				
 النسب الإستشارات الهندسية Proportions Consulting Engineering Tel. 2752377, Fax: 2757722 P.O.Box 75453, Riyadh-11578				
PROJECT				
PRIVATE HOUSING COMPLEX AL NAKHEEL / RIYADH - SAUDI ARABIA				
OWNER				
SHEET TITLE				
ARCHITECTURAL FINISHING SCHEDULE				
TENDER DOCUMENTS				
PROJECT NO. :	P0521	STAGE :	WORKING DRAWINGS	
DESIGNED BY :	Proportion Group	DRAWN BY :	CAD	
DATE :	FEB. 2006	SCALE :	1:100M	
A050404 ARCHITECTURAL				REVISION 0

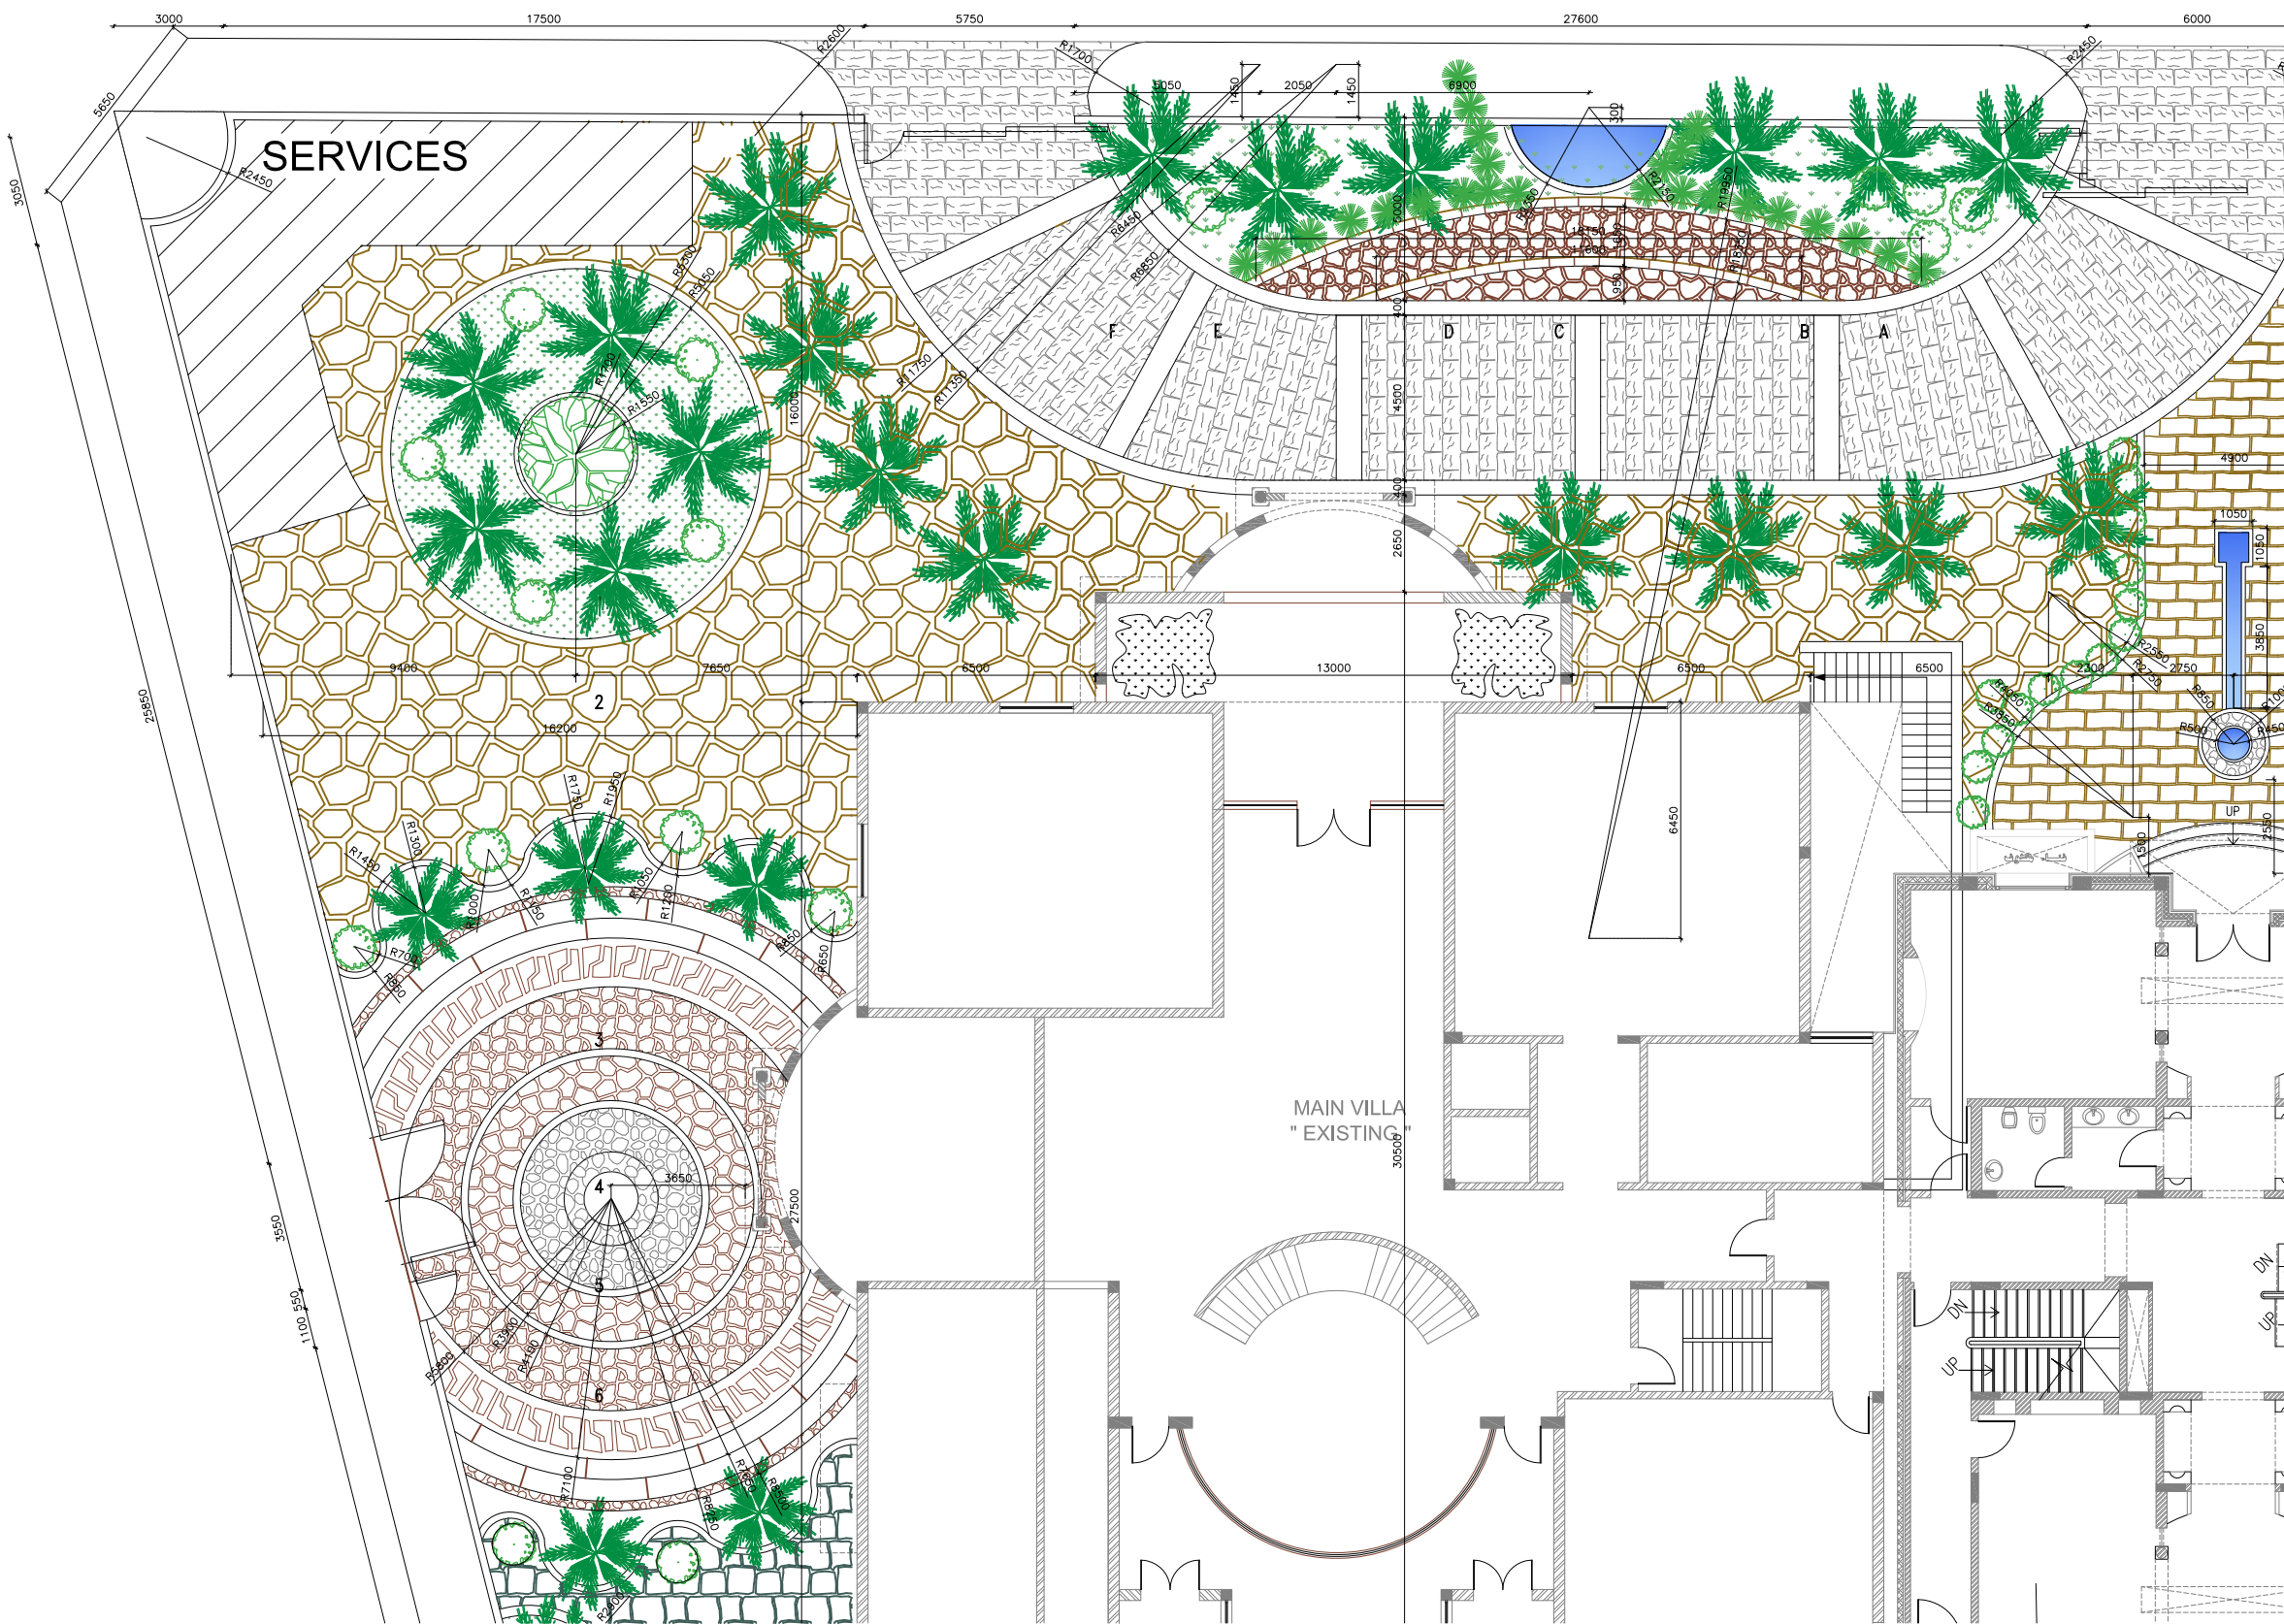

REV.	DATE	BY	DESCRIPTION
KEY PLAN			
Associated Consulting Engineers International - ACE			
CONSULTANT			
PROJECT			
PRIVATE HOUSING COMPLEX			
AL NAKHEEL / RIYADH - SAUDI ARABIA			
OWNER			
SHEET TITLE			
LANDSCAPE PACKAGE			
LANDSCAPE DIMENSION LAYOUT			
PART 1 / 4			
TENDER DOCUMENTS			
PROJECT NO. :	P0521	STAGE :	WORKING DRAWINGS
DESIGNED BY :	Proportion Group	DRAWN BY :	CAD
DATE :	MARCH 2006	SCALE :	1:200M
A130101			REVISION
A130101			0

1 LANDSCAPE DIMENSION LAYOUT PART 1/4
SCALE: 1:100 M.

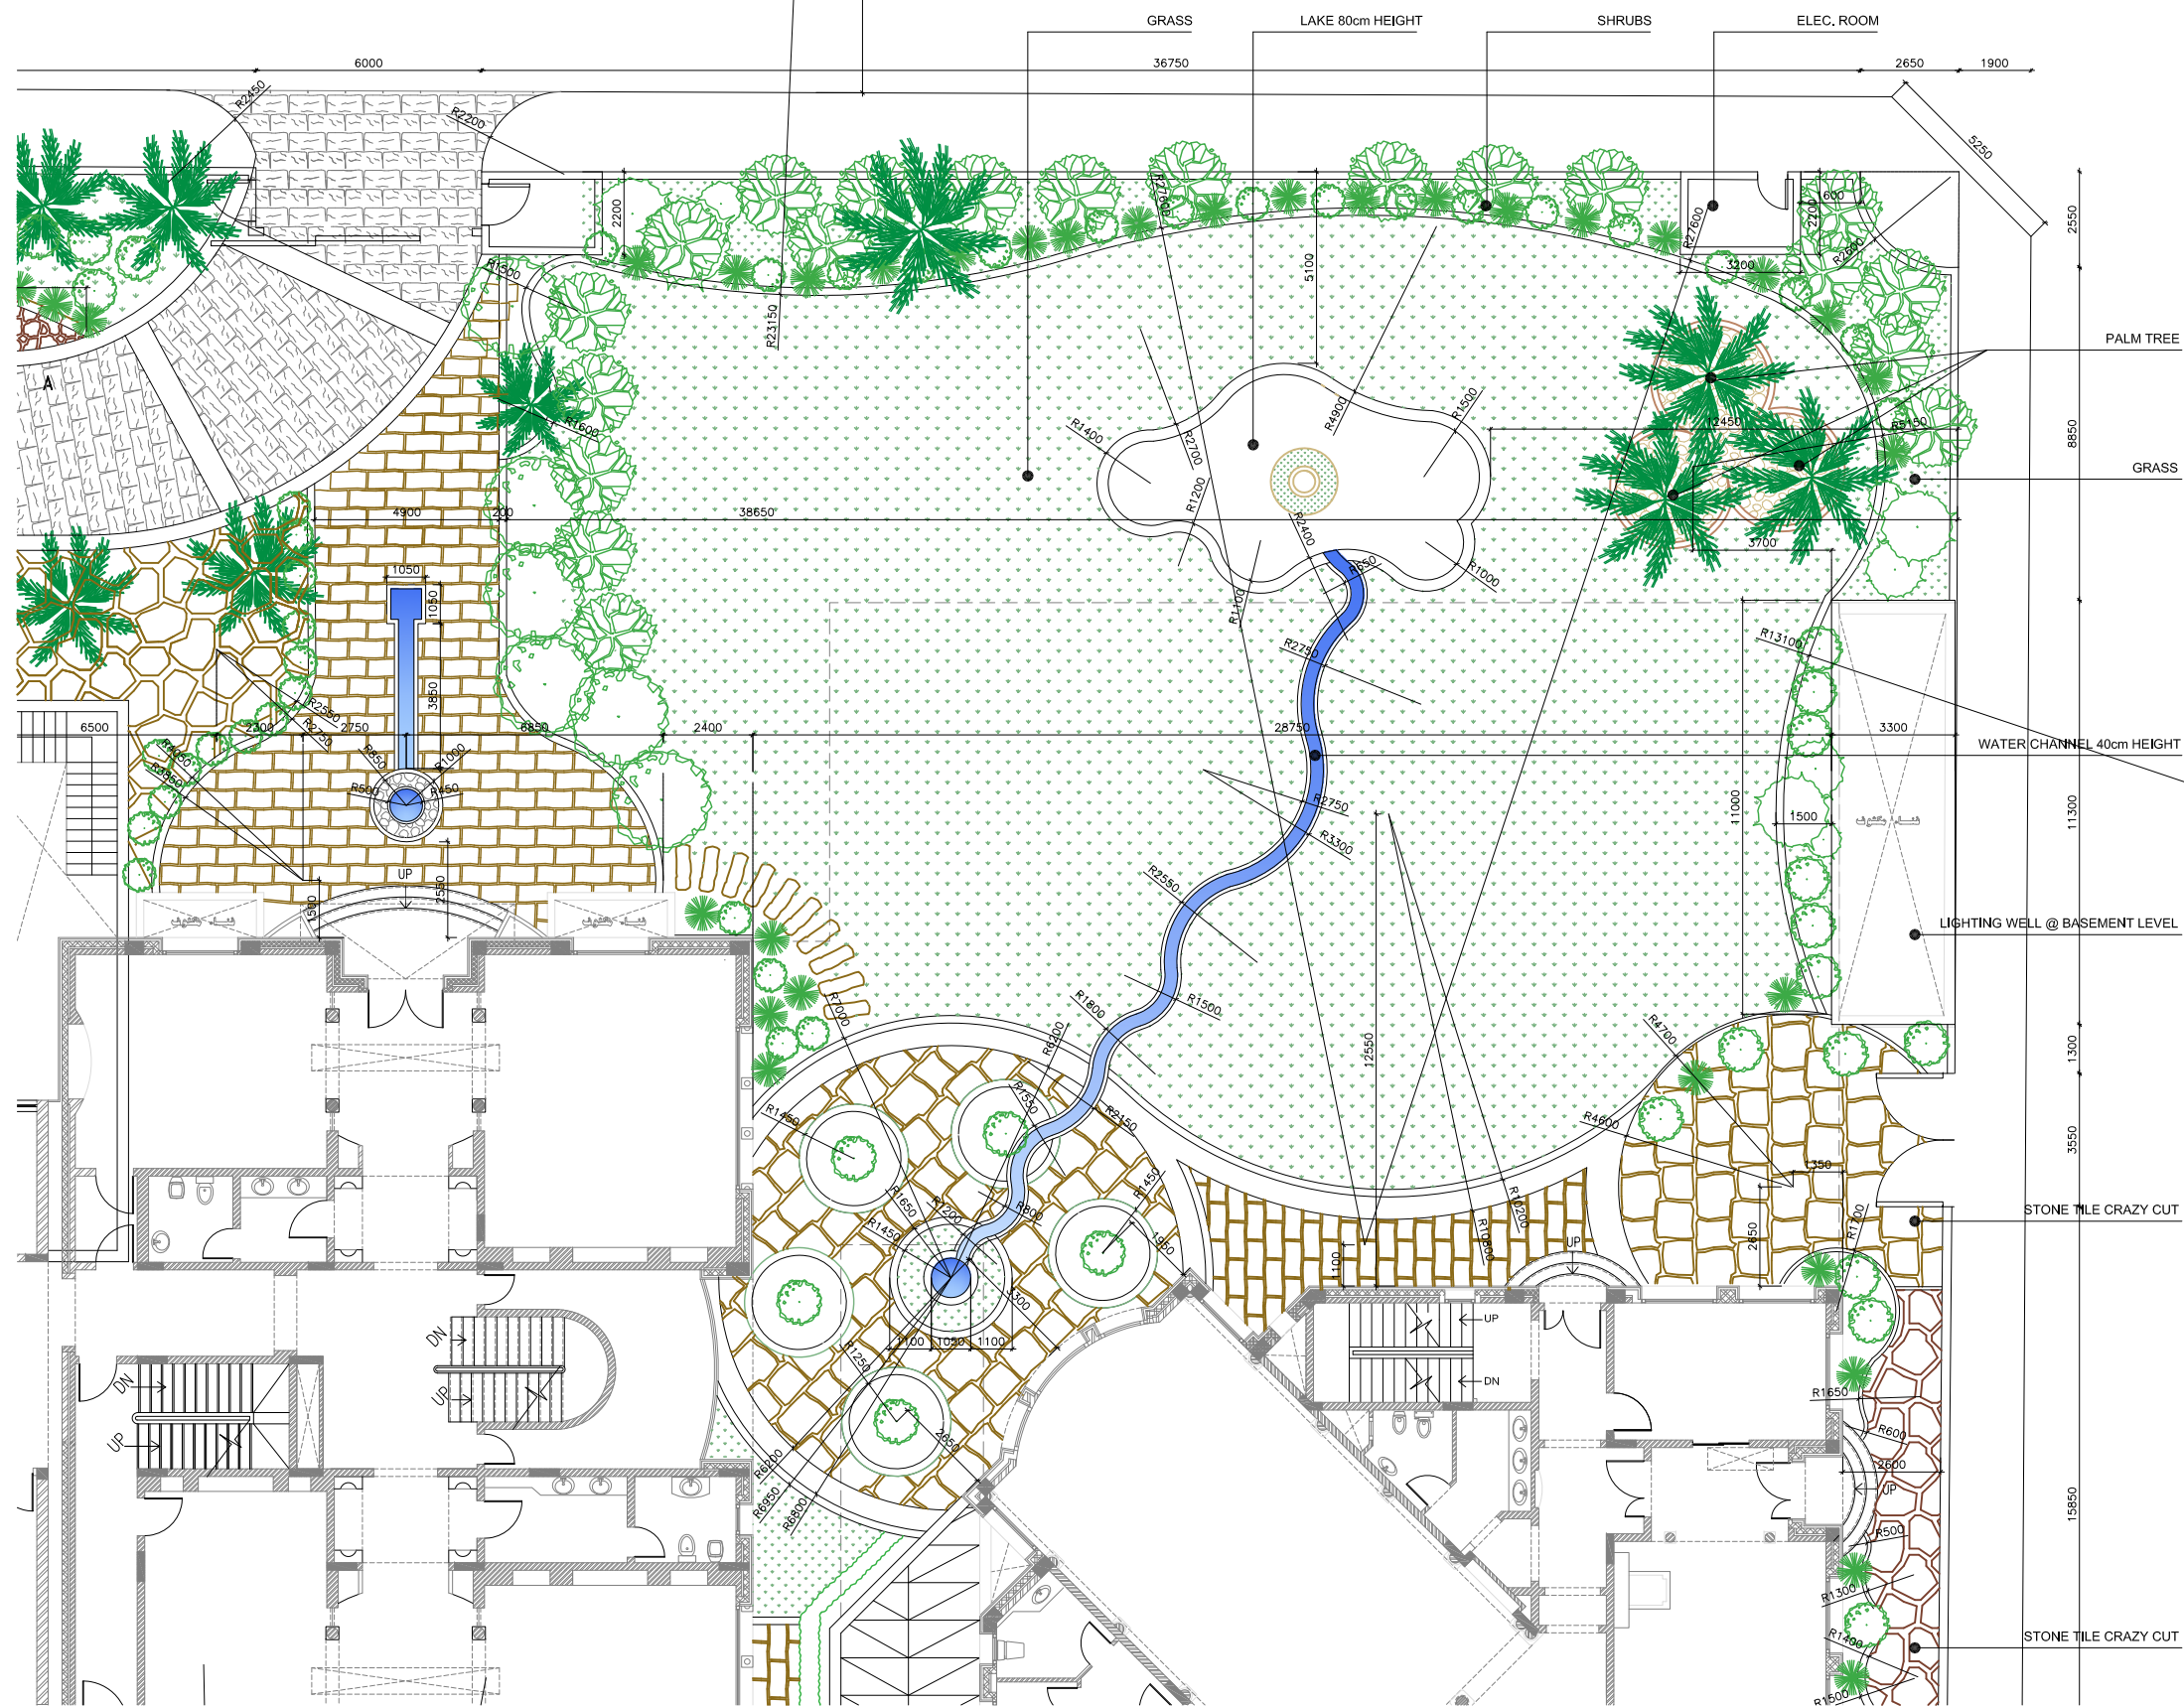

REV.	DATE	BY	DESCRIPTION

KEY PLAN



CONSULTANT



PROJECT
PRIVATE HOUSING COMPLEX
AL NAKHEEL / RIYADH - SAUDI ARABIA

OWNER

SHEET TITLE

LANDSCAPE PACKAGE
LANDSCAPE DIMENSION LAYOUT
PART 2/4


TENDER DOCUMENTS

PROJECT NO. :	P0521	STAGE :	WORKING DRAWINGS
DESIGNED BY :	Proportion Group	DRAWN BY :	CAD
DATE :	MARCH 2006	SCALE :	1:200M

A130102
A130101

REVISION
0

1 LANDSCAPE DIMENSION LAYOUT PART 2/4
A130102 SCALE: 1:100 M.

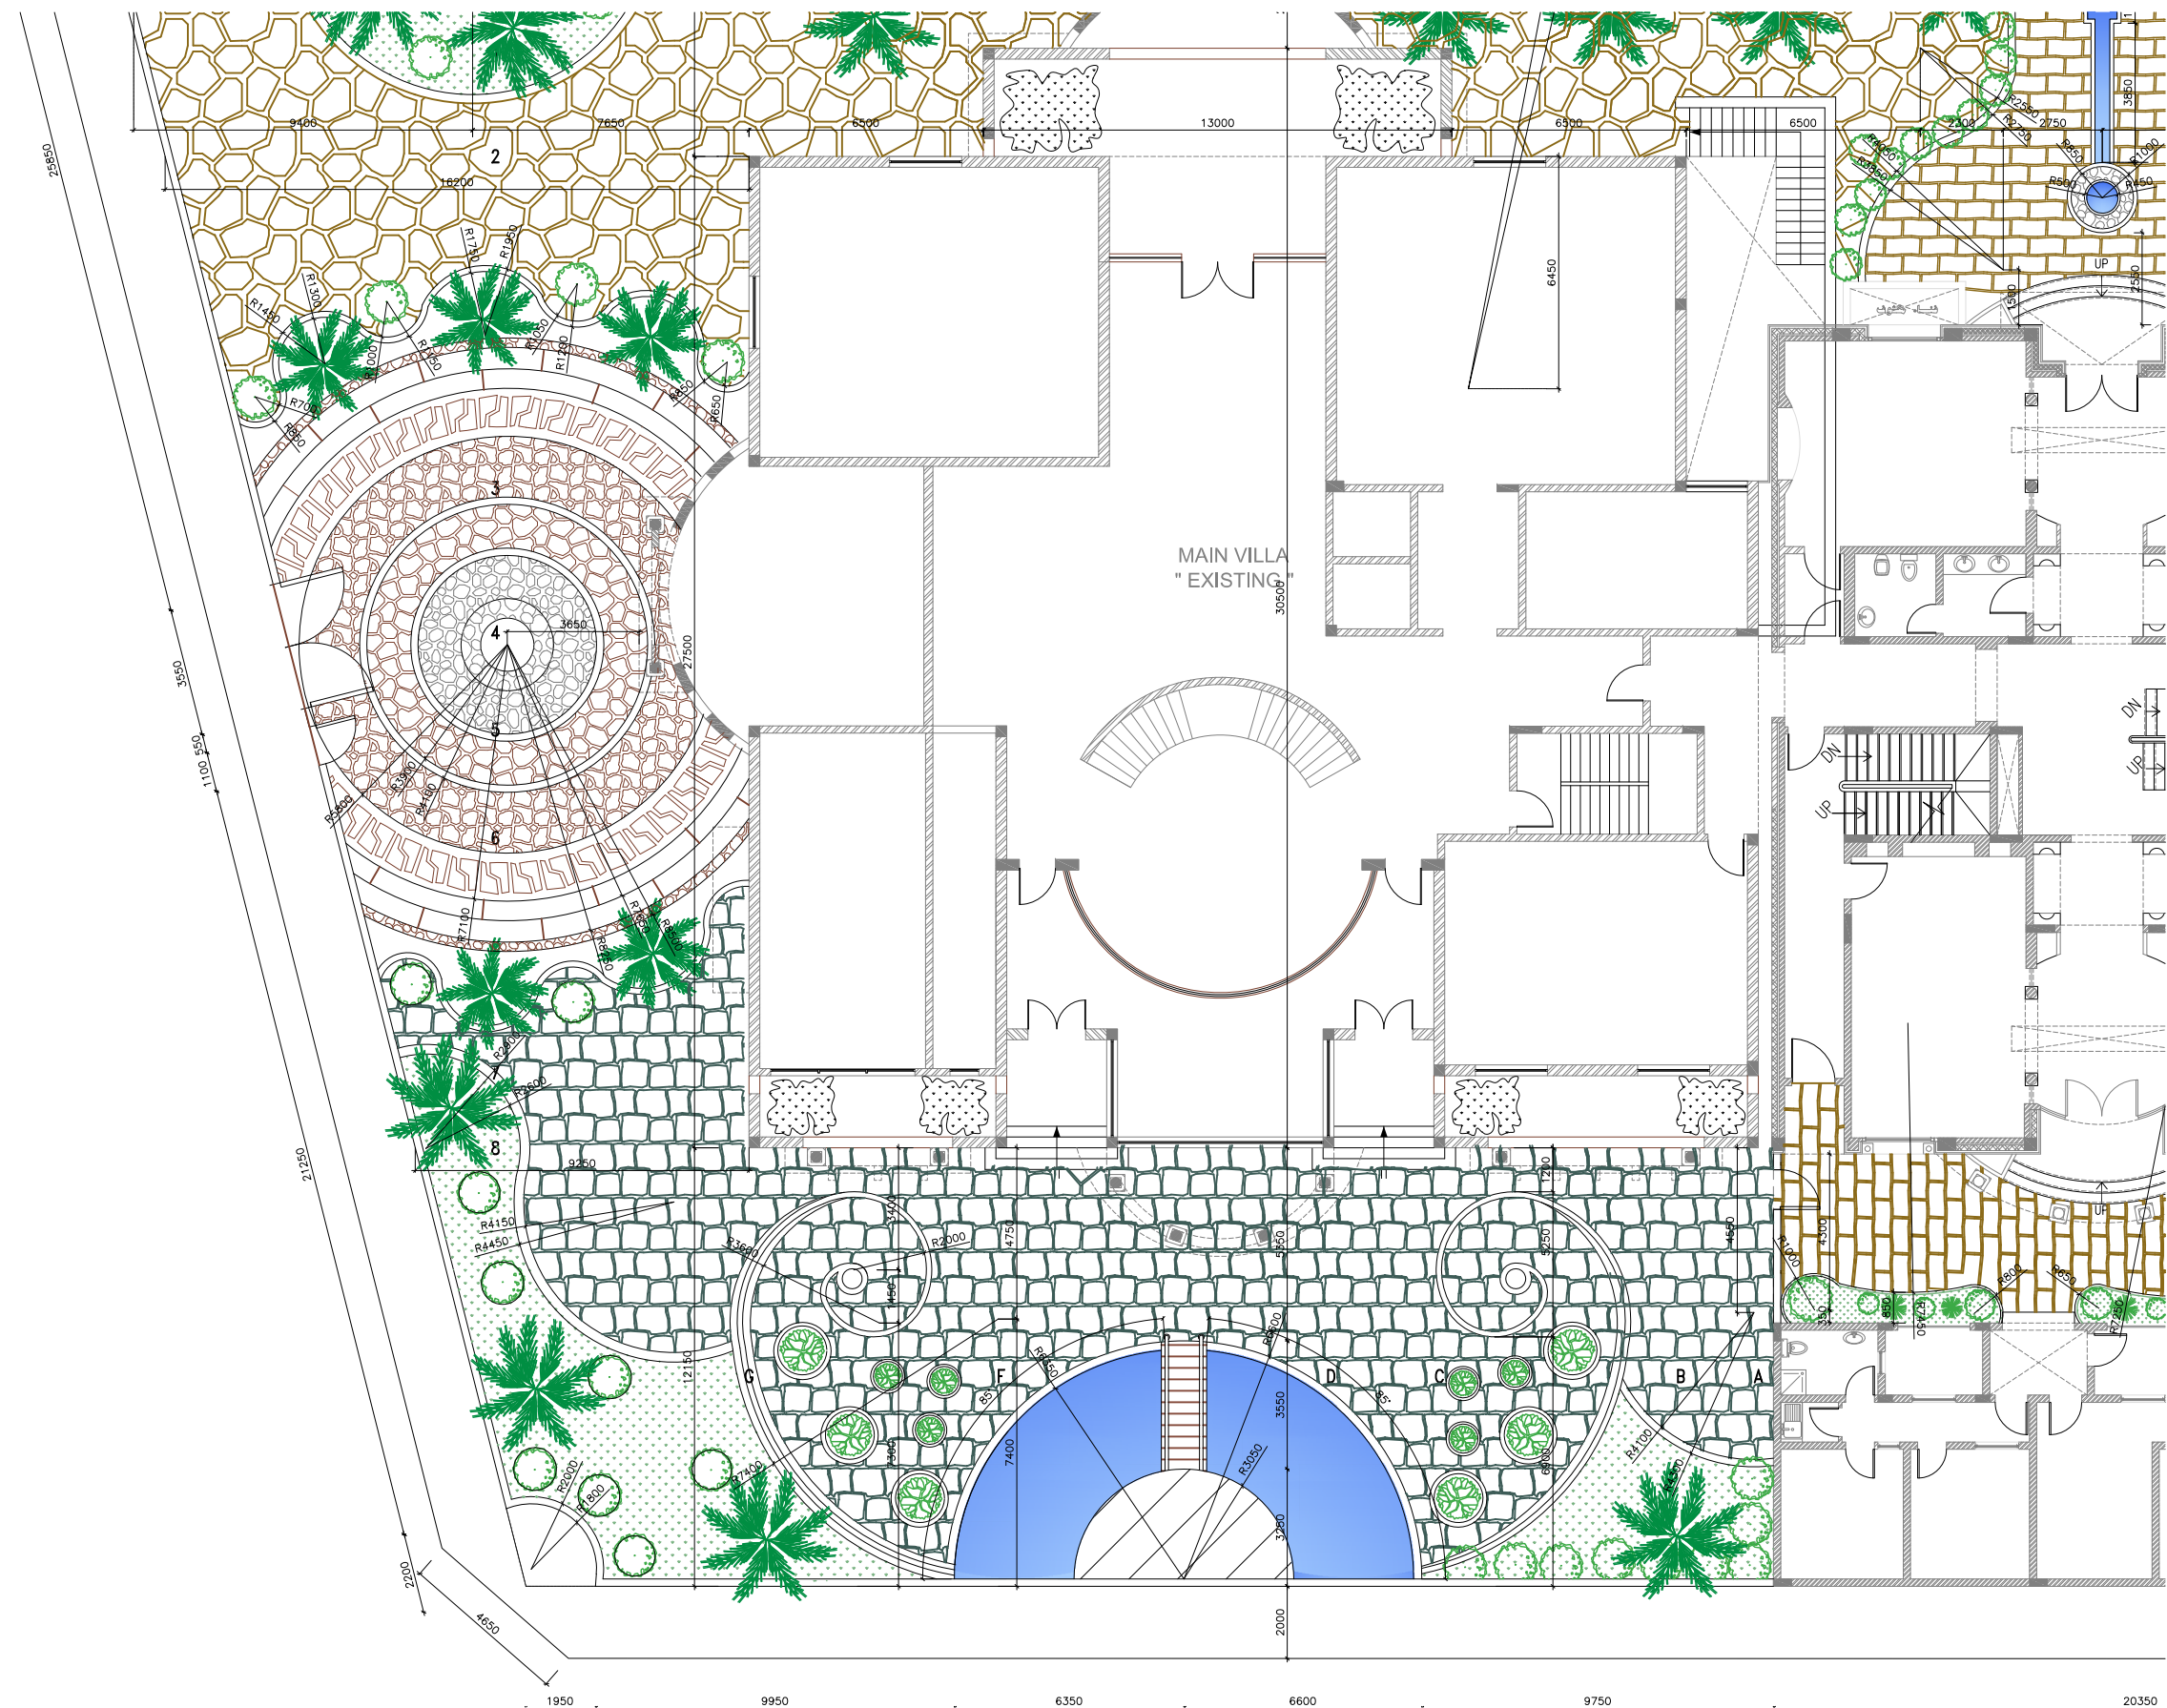

REV.	DATE	BY	DESCRIPTION

KEY PLAN



Associated Consulting Engineers International - ACE



Proportions Consulting Engineering
Tel: 2752277, Fax: 2757722 P.O.Box 75453, Riyadh-11578

PROJECT

PRIVATE HOUSING COMPLEX
AL NAKHEEL / RIYADH - SAUDI ARABIA

OWNER

SHEET TITLE

LANDSCAPE PACKAGE
LANDSCAPE DIMENSION LAYOUT
PART 3/4


TENDER DOCUMENTS

PROJECT NO. :	P0521	STAGE :	WORKING DRAWINGS
DESIGNED BY :	Proportion Group	DRAWN BY :	CAD
DATE :	MARCH 2006	SCALE :	1:200M

A130103
A130101

REVISION
0

1 LANDSCAPE DIMENSION LAYOUT PART 3/4
SCALE: 1:100 M.

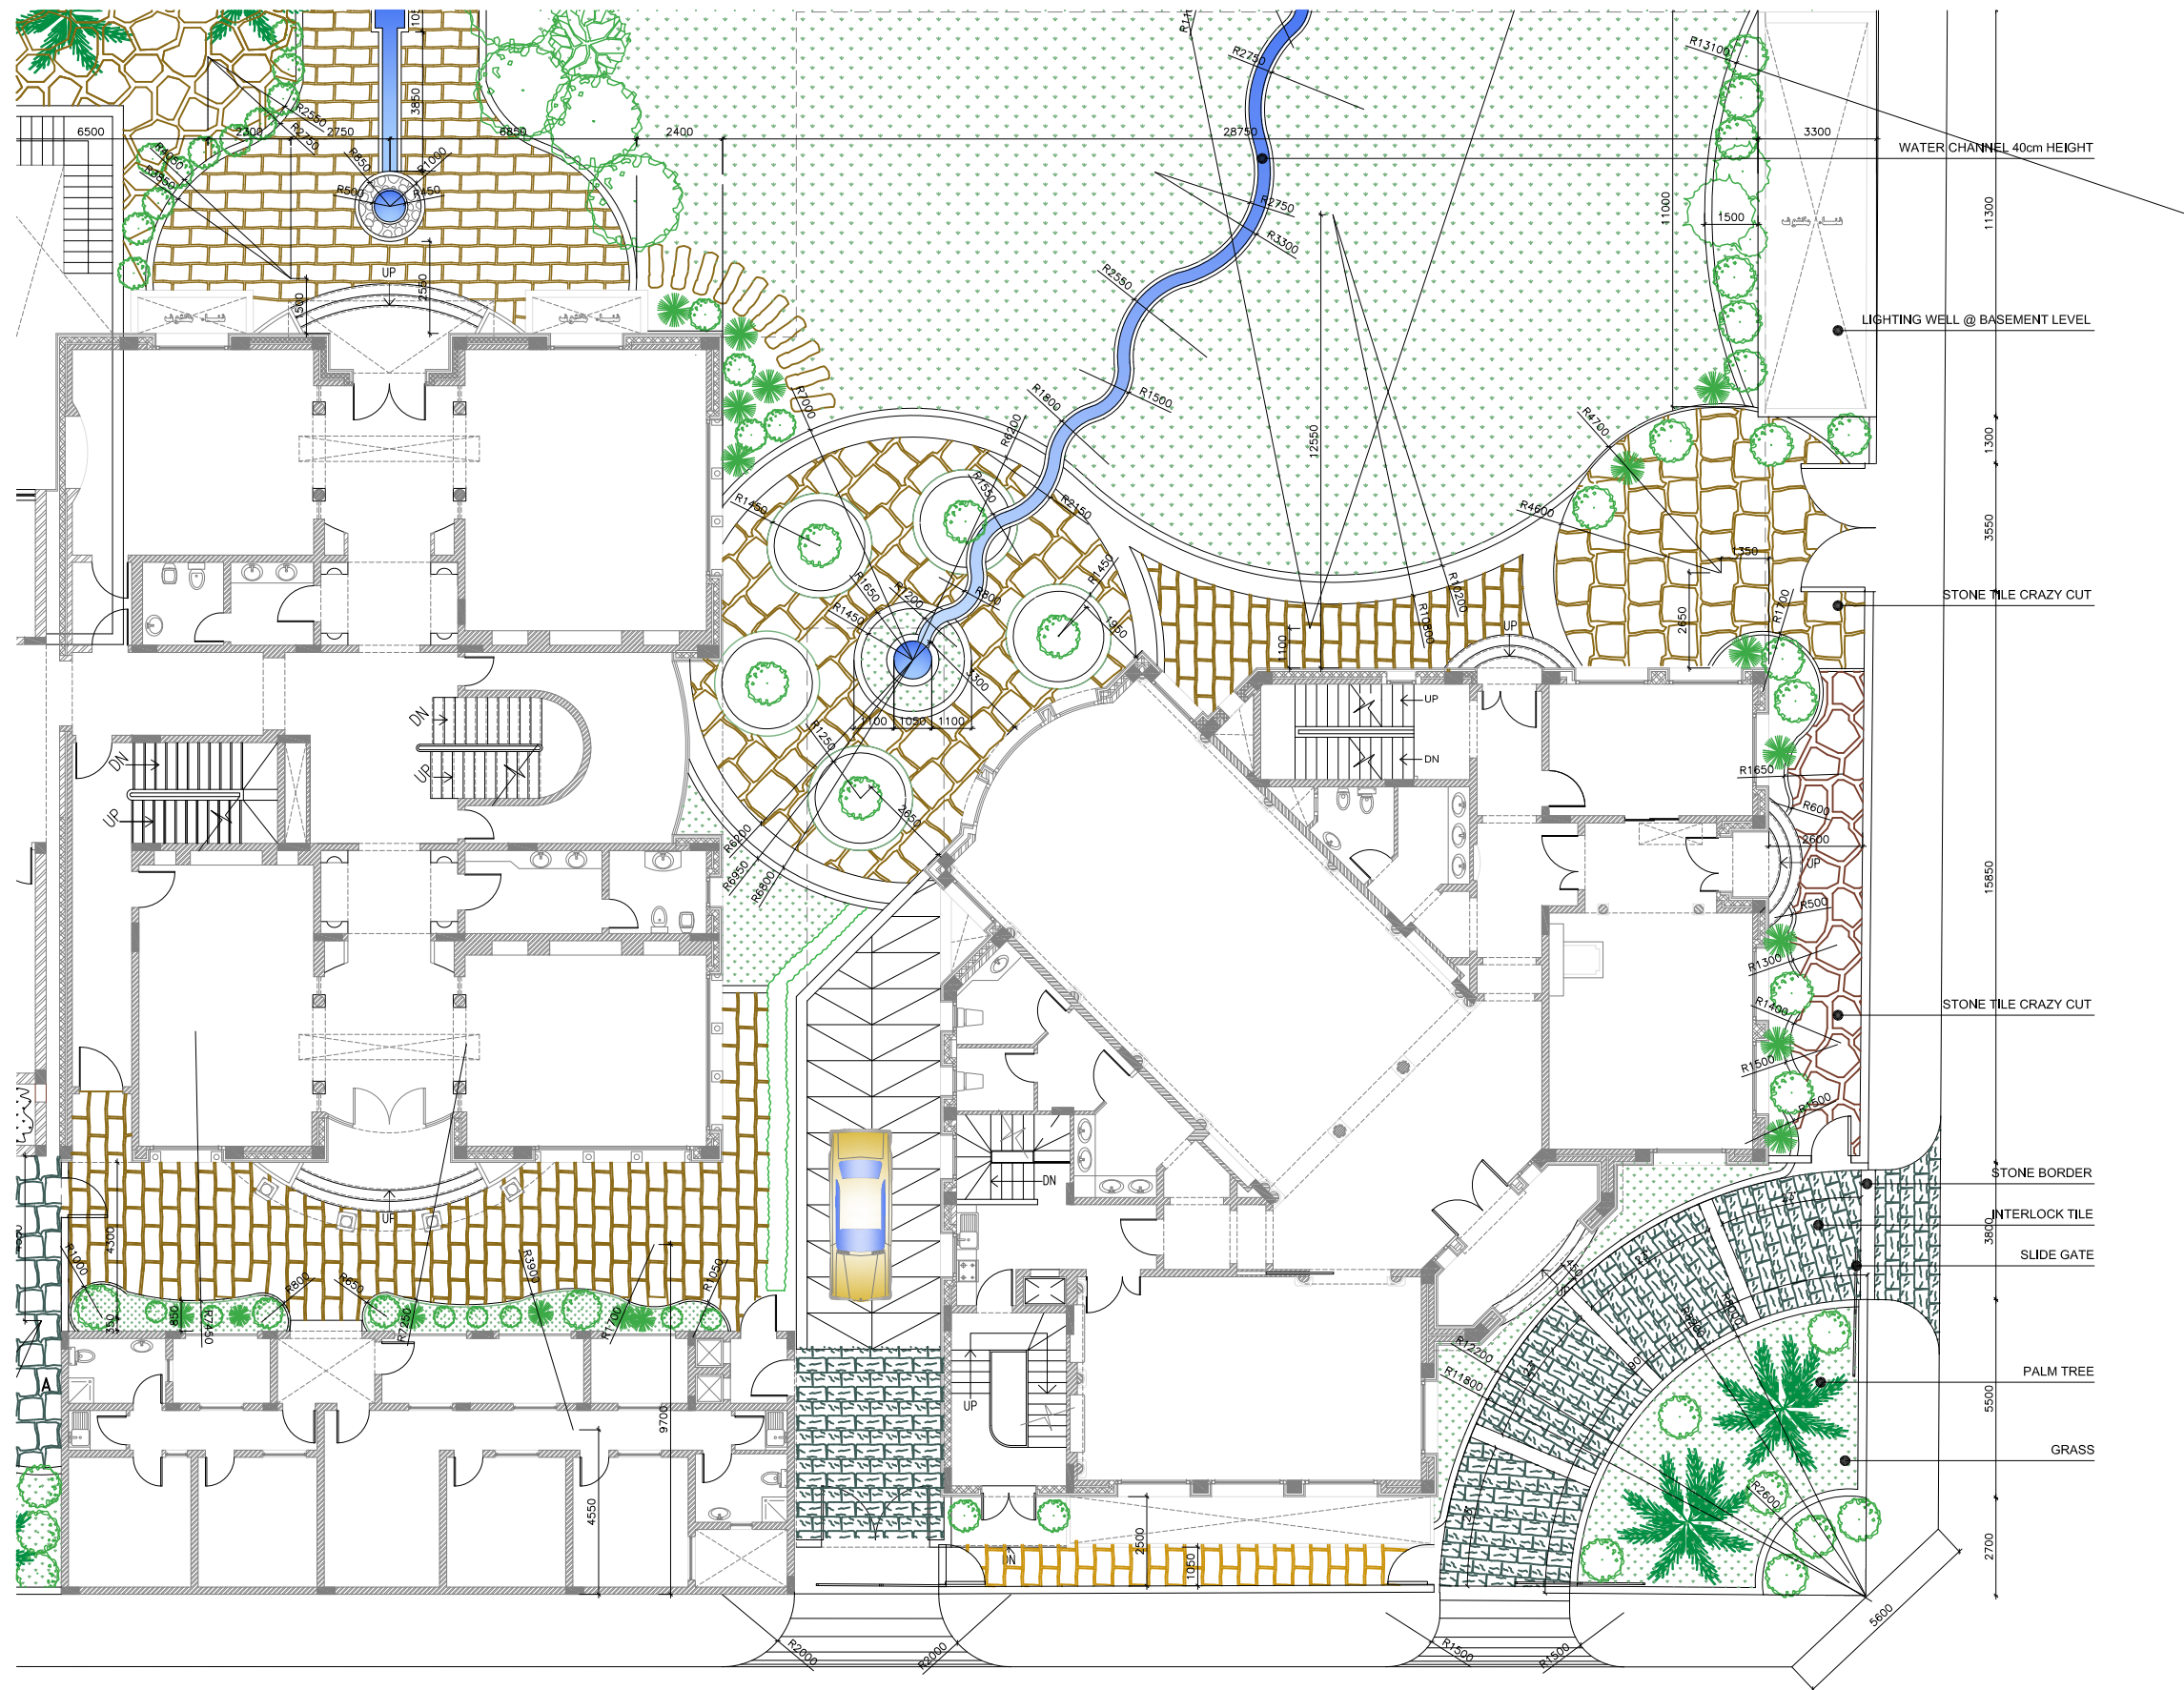

REV.	DATE	BY	DESCRIPTION

KEY PLAN

STONE TILE CRAZY CUT

STONE TILE CRAZY CUT

STONE BORDER

INTERLOCK TILE

SLIDE GATE

PALM TREE

GRASS

STONE TILE CRAZY CUT

STONE TILE CRAZY CUT

STONE TILE CRAZY CUT

STONE TILE CRAZY CUT

STONE TILE CRAZY CUT

STONE TILE CRAZY CUT

STONE TILE CRAZY CUT

STONE TILE CRAZY CUT

STONE TILE CRAZY CUT

STONE TILE CRAZY CUT

STONE TILE CRAZY CUT

STONE TILE CRAZY CUT

STONE TILE CRAZY CUT

STONE TILE CRAZY CUT

STONE TILE CRAZY CUT

STONE TILE CRAZY CUT

STONE TILE CRAZY CUT

STONE TILE CRAZY CUT

STONE TILE CRAZY CUT

STONE TILE CRAZY CUT

STONE TILE CRAZY CUT

STONE TILE CRAZY CUT

STONE TILE CRAZY CUT

STONE TILE CRAZY CUT

STONE TILE CRAZY CUT

STONE TILE CRAZY CUT

STONE TILE CRAZY CUT

STONE TILE CRAZY CUT

STONE TILE CRAZY CUT

STONE TILE CRAZY CUT

STONE TILE CRAZY CUT

STONE TILE CRAZY CUT

STONE TILE CRAZY CUT

STONE TILE CRAZY CUT

STONE TILE CRAZY CUT

STONE TILE CRAZY CUT

STONE TILE CRAZY CUT

STONE TILE CRAZY CUT

1 LANDSCAPE DIMENSION LAYOUT PART 4/4
SCALE: 1:100 M.

LANDSCAPE PACKAGE
LANDSCAPE DIMENSION LAYOUT
PART 4 / 4

TENDER DOCUMENTS

PROJECT NO. : P0521 STAGE : WORKING DRAWINGS

DESIGNED BY : Proportion Group DRAWN BY : CAD


DATE : MARCH 2006 SCALE : 1:200M

REVISION

A130104



A130101

0

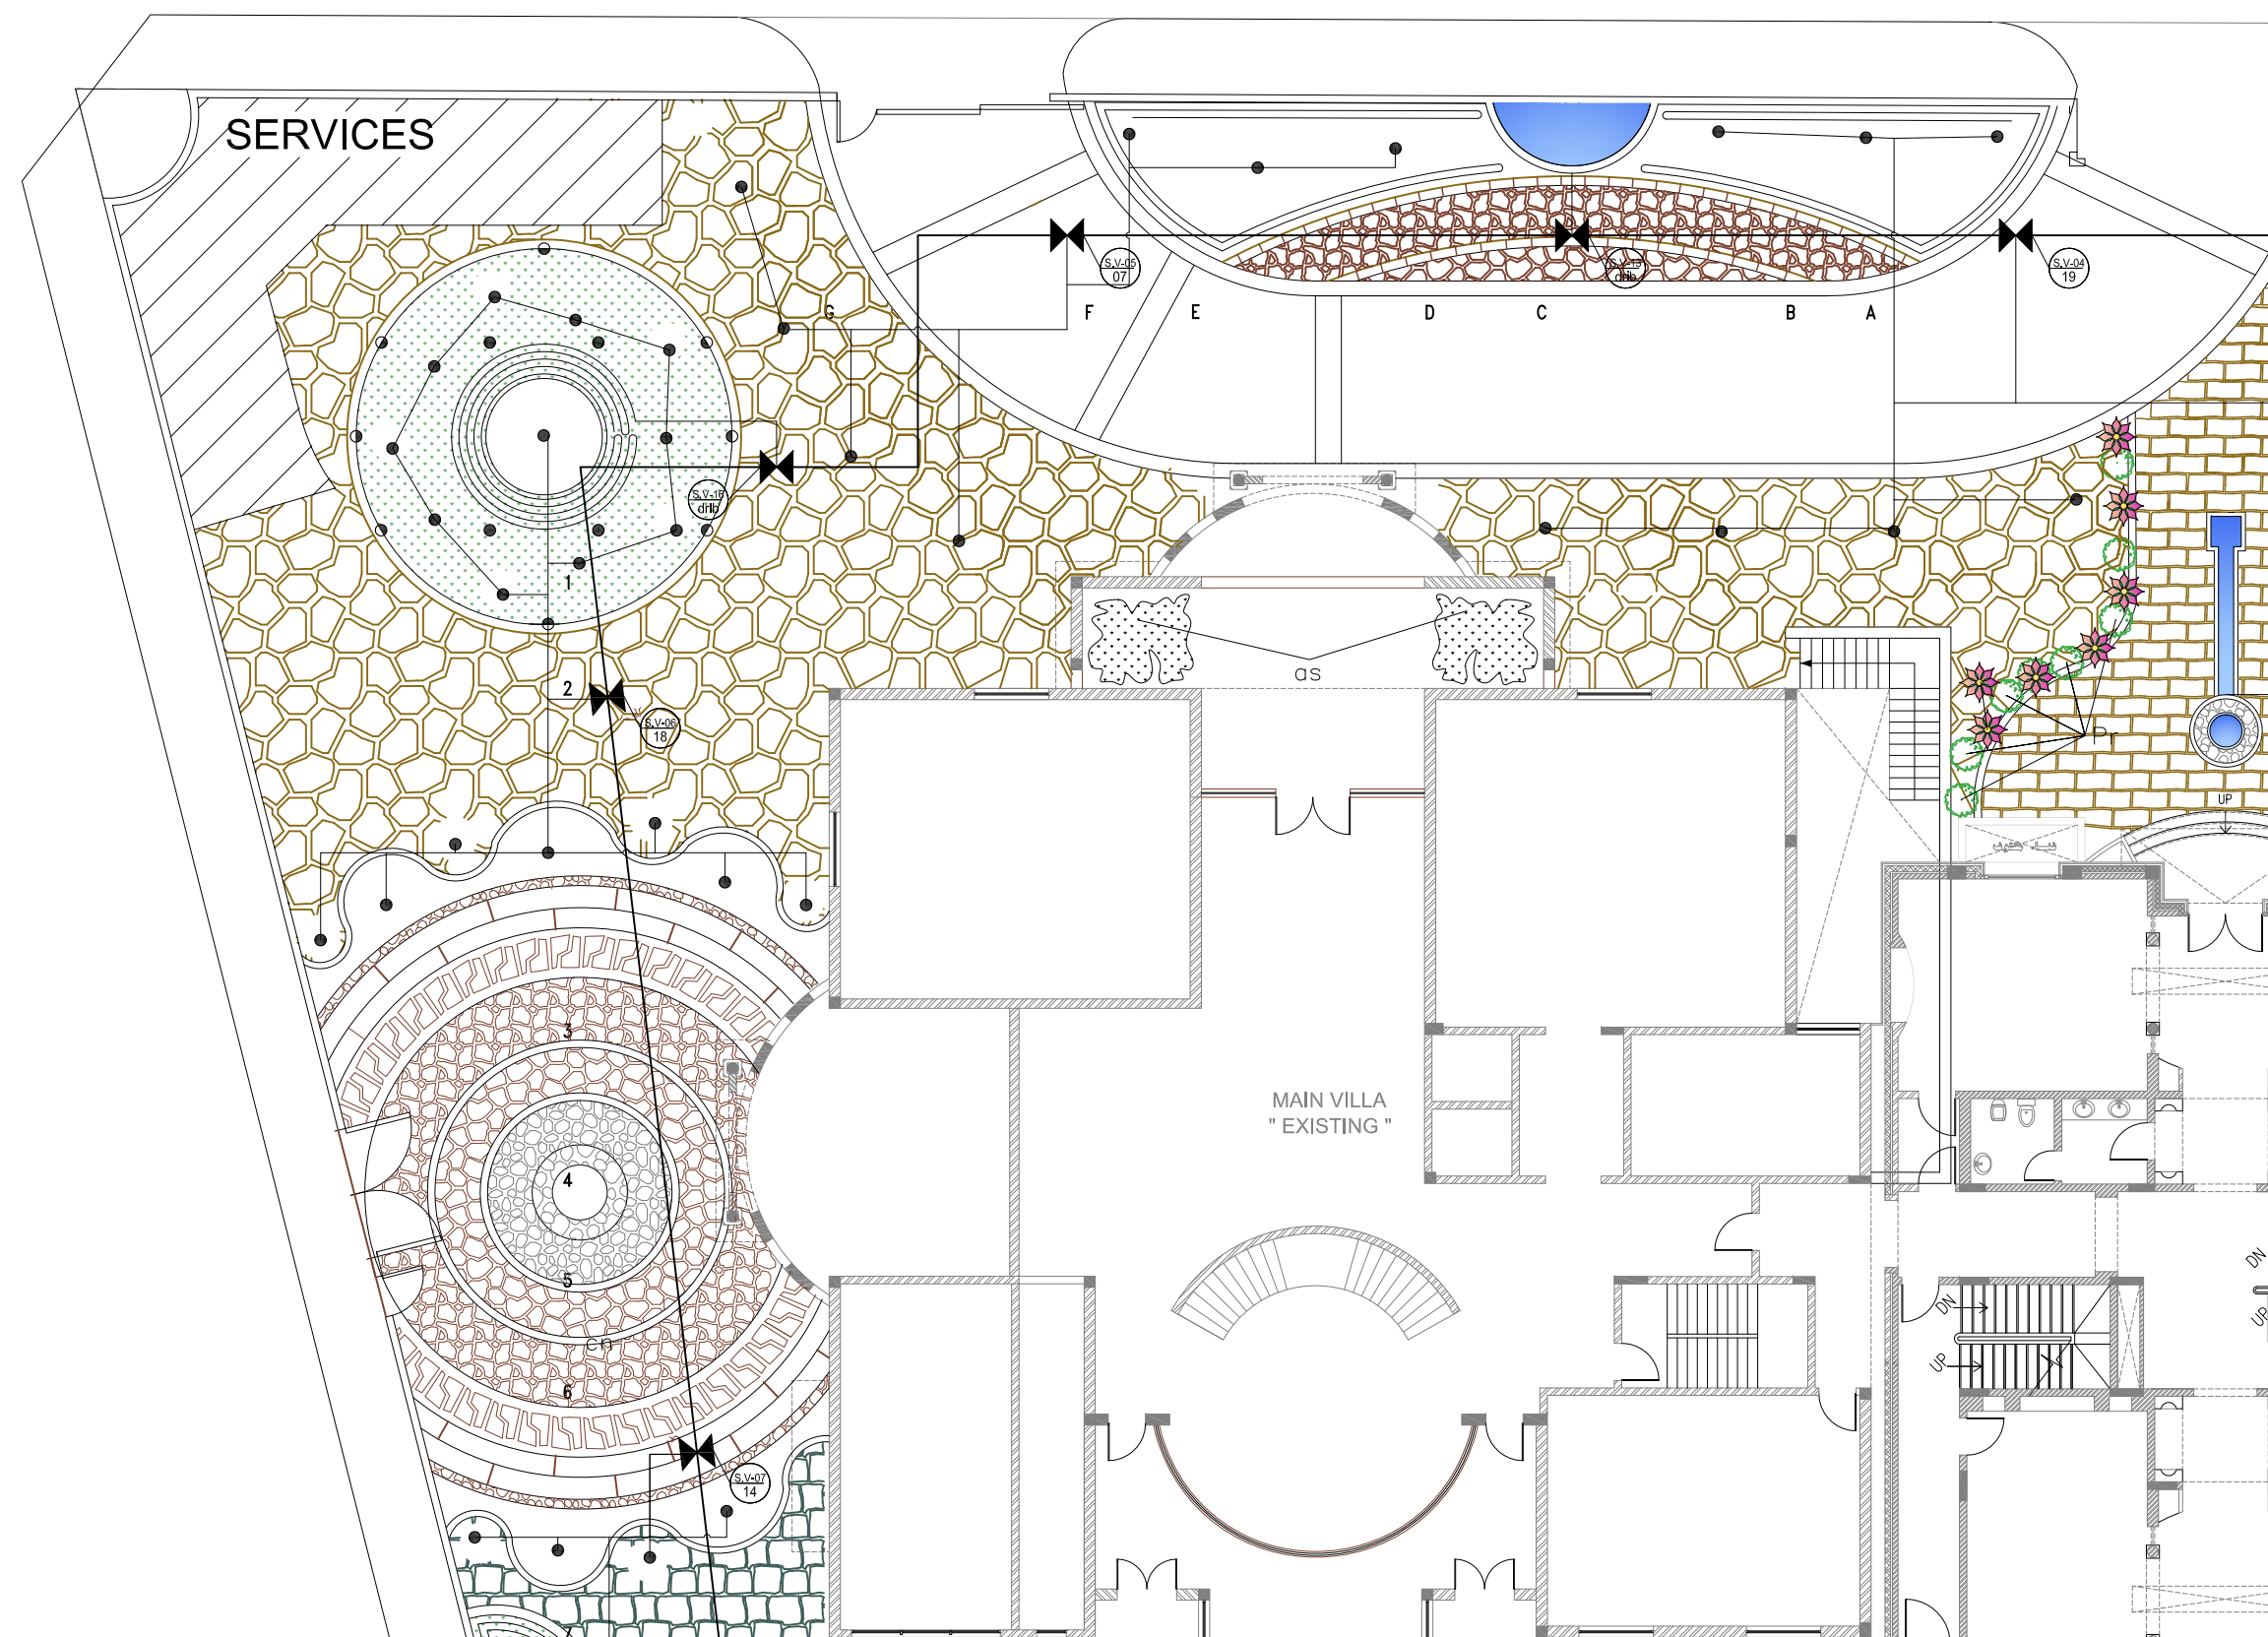

1:100 M.

© 2006  Proportions Consulting Engineering (A1 SIZE SHEET)

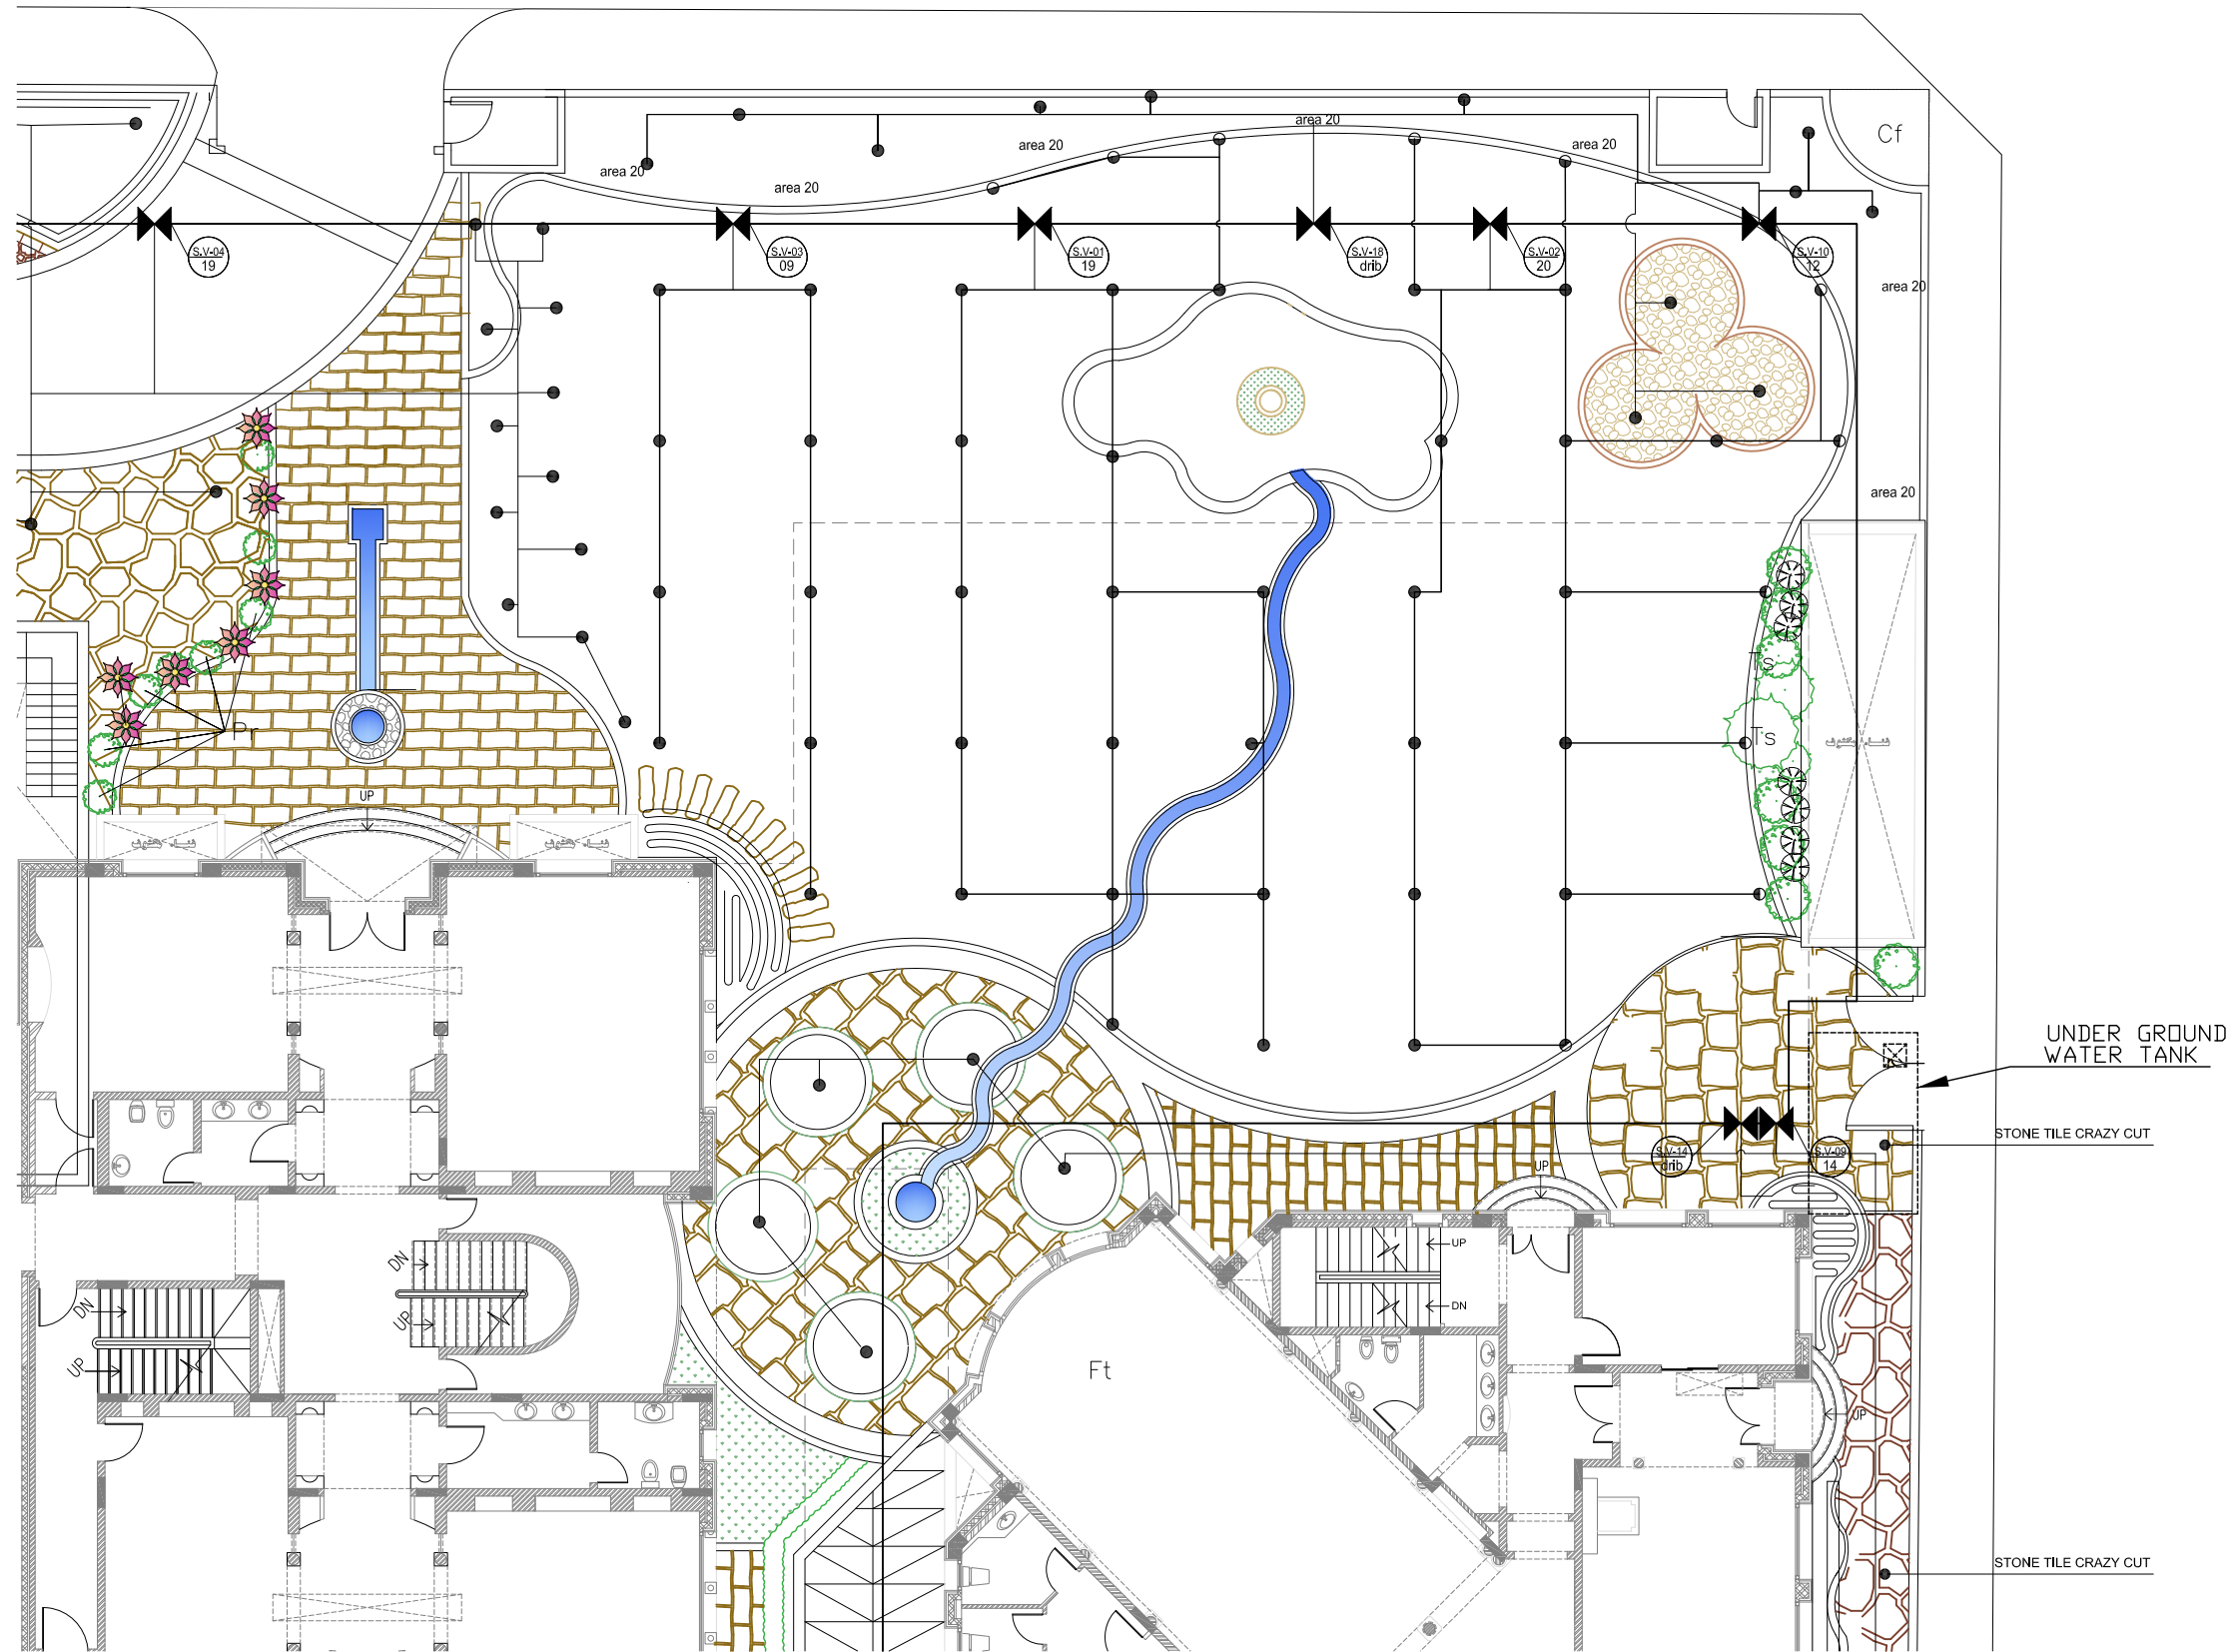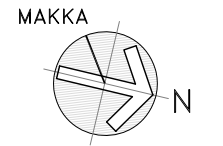


1 LANDSCAPE DIMENSION LAYOUT PART 2/4
A130102 SCALE: 1:100 M.

REV.	DATE	BY	DESCRIPTION
KEY PLAN			
 Associated Consulting Engineers International - ACE			
CONSULTANT			
 النسب للإستشارات الهندسية Proportions Consulting Engineering Tel: 2752277, Fax: 2757722 P.O.Box 75453, Riyadh-11578			
PROJECT			
PRIVATE HOUSING COMPLEX AL NAKHEEL / RIYADH - SAUDI ARABIA			
OWNER			
SHEET TITLE			
LANDSCAPE IRRIGATION LYOUT PART 2/4			
TENDER DOCUMENTS			
PROJECT NO. :	P0521	STAGE :	WORKING DRAWINGS
DESIGNED BY :	Proportion Group	BY :	CAD
DATE :	MARCH 2006	SCALE :	1:200M
A130202			REVISION 0



A130203	REVISION 0
---------	---------------

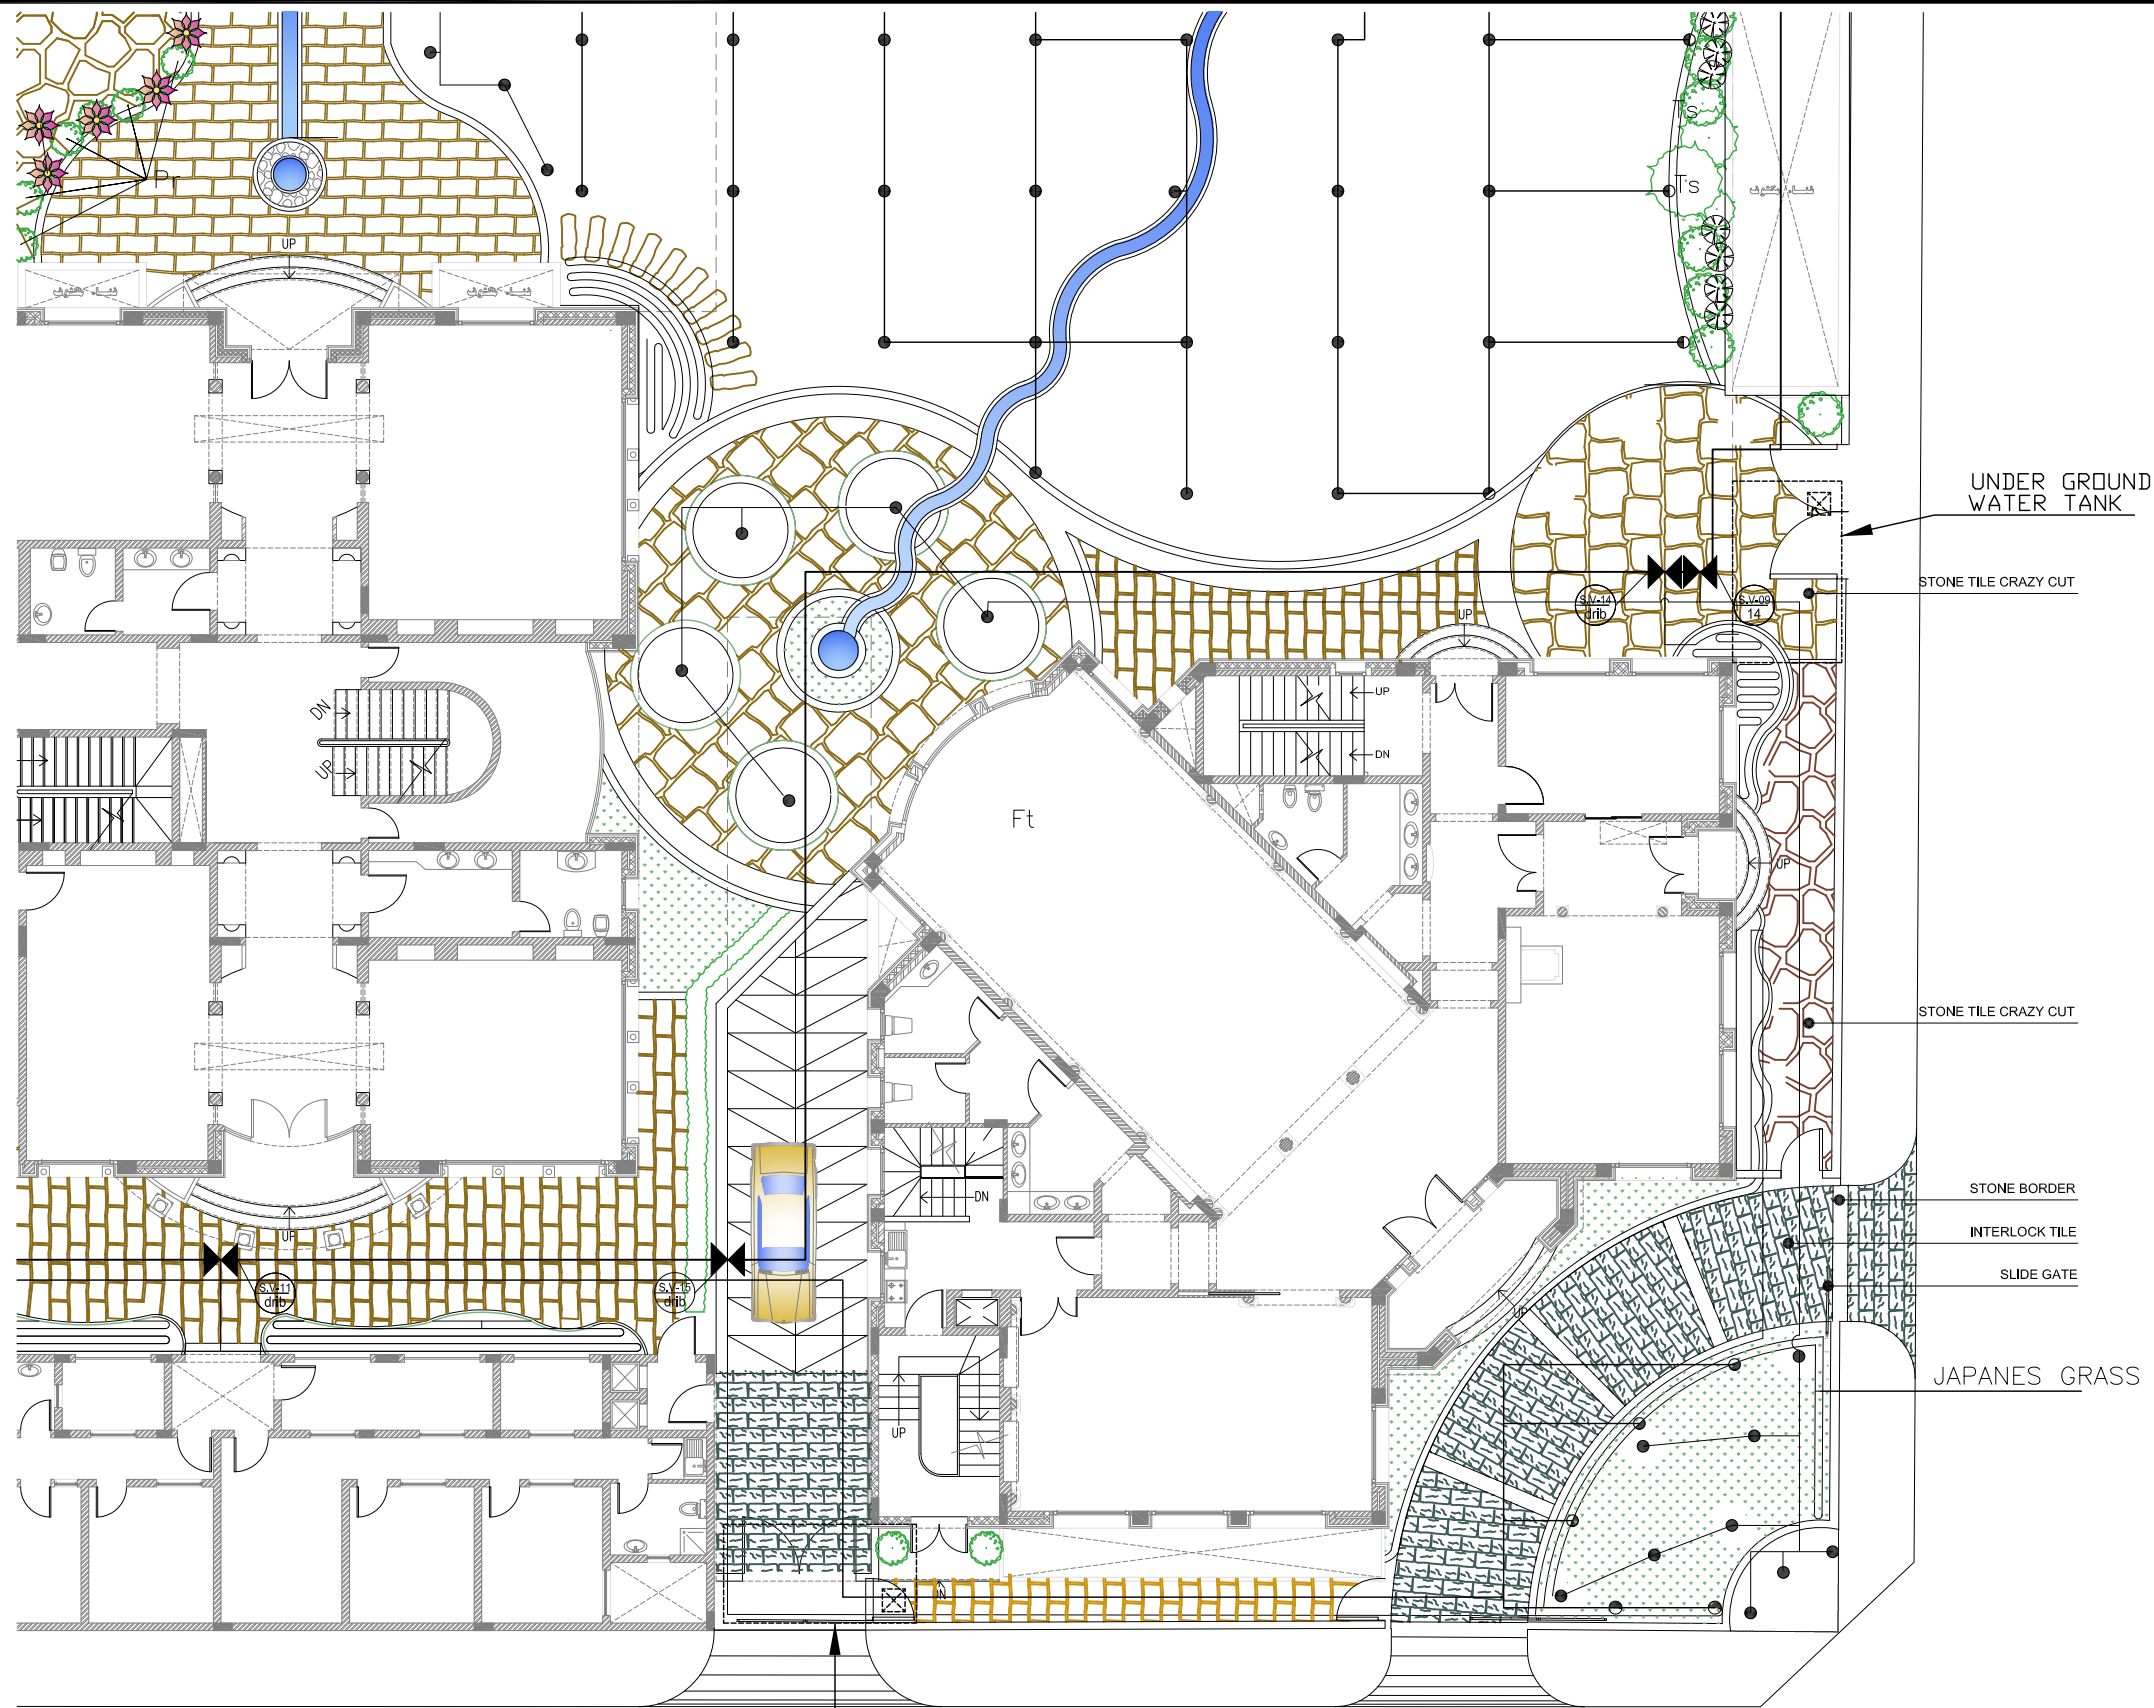

(LOGIC 2 Decoder



REV.	DATE	BY	DESCRIPTION

KEY PLAN

Associated Consulting Engineers International - ACE
CONSULTANT

النسب للإستشارات الهندسية
Proportions Consulting Engineering
Tel: 2752277, Fax: 2757722 P.O.Box 75453, Riyadh-11578

PROJECT

PRIVATE HOUSING COMPLEX
AL NAKHEEL / RIYADH - SAUDI ARABIA

OWNER

SHEET TITLE

LANDSCAPE
IRRIGATION LYOUT
PART 4 /4

TENDER DOCUMENTS			
PROJECT NO. :	P0521	STAGE :	WORKING DRAWINGS
DESIGNED BY :	Proportion Group	DRAWN BY :	CAD
DATE :	MARCH 2006	SCALE :	1:200M

A130204


0

1 LANDSCAPE DIMENSION LAYOUT PART 4/4
A130104 SCALE: 1:100 M.




Box Valve


Series 1320 (Jumbo) 12" High
Series 1320 (12" High Rectangular) (40 Per Pallet)

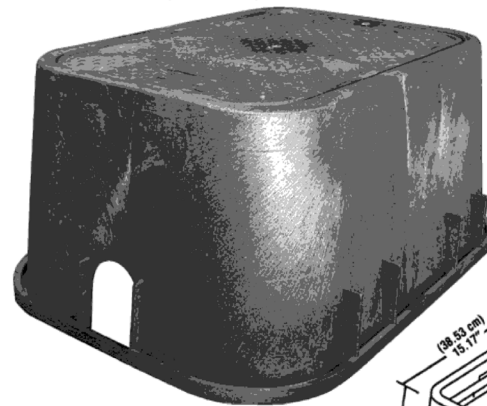


Series 1320-12" Body Dimension

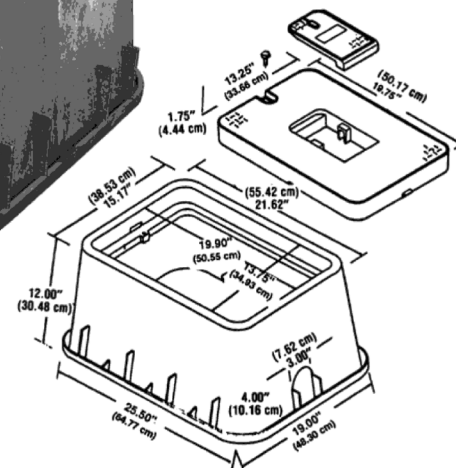



(1.5" Hit S.Valve)
(2" Hit S.Valve)
High Flow S.Valve

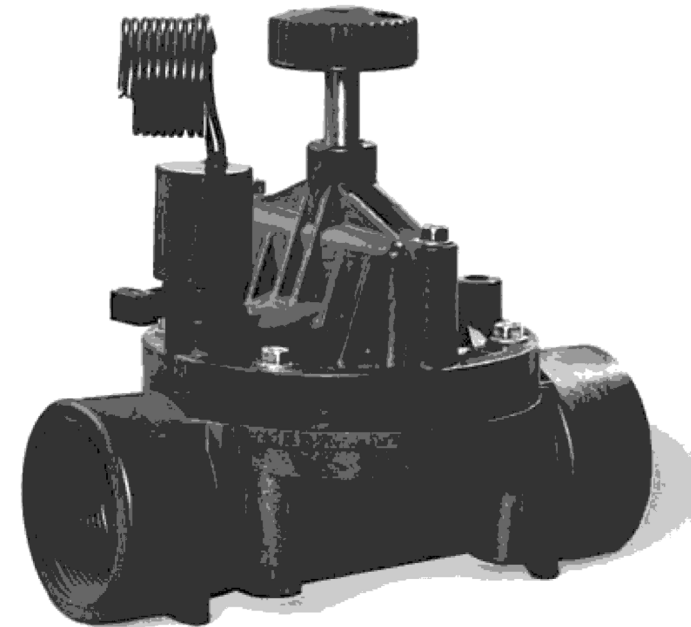

(LOGIC 2 Decoder
Controller 1-42 Staition)

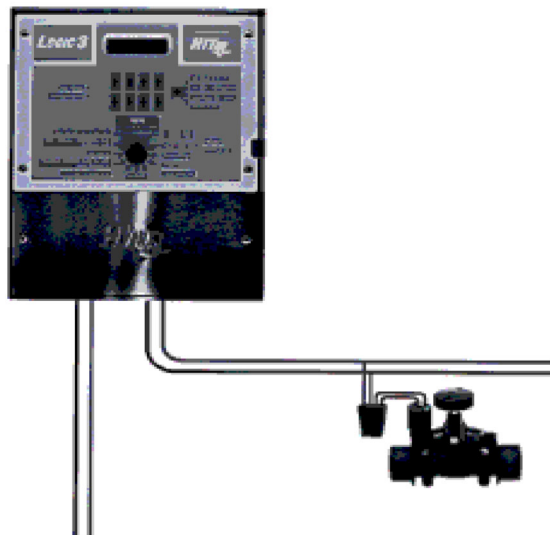


DRIP
(Micro Fillapper Emitter)

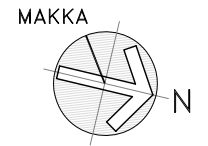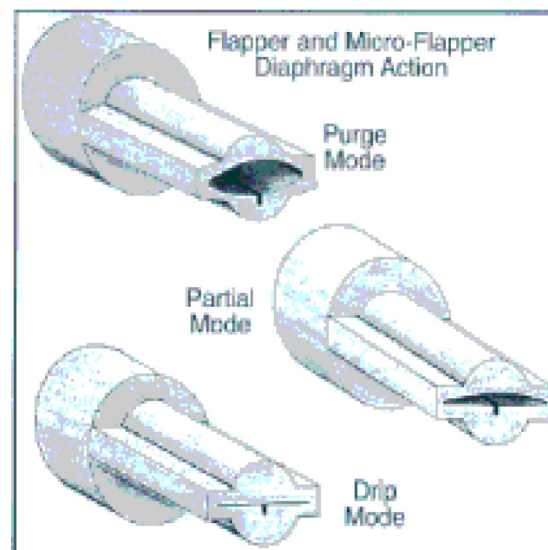

REV.	DATE	BY	DESCRIPTION

(Valve No.).	As Drawing	(Size).	(Items).	(Psc.).
(1).	Grass Area	2 "	Uni Spray	19
(2).	Grass Area	2 "	Uni Spray	20
(3).	Grass Area	2 "	Uni Spray	09
(4).	trees	2"	papler	19
(5).	trees	2 "	papler	07
(6).	trees	2 "	papler	18
(7).	trees	2 "	papler	14
(8).	trees	2 "	papler	20
(9).	trees	2 "	papler	14
(10).	trees	2 "	papler	12
(11).	trees	1.5 "	Drib	---
(12).	trees	1.5 "	Drib	---
(13).	trees	1.5 "	Drib	---
(14).	trees	1.5 "	Drib	---
(15).	trees	1.5 "	Drib	---
(16).	trees	1.5 "	Drib	---
(17).	Grass Area	2 "	Uni Spray	10
(18).	trees area 20	1.5 "	Drib	---

	SOLENOID VALVE
	GARDEN SPRINKLER (PRO-PLUS 12 M. RADIUS)
	MAIN RAW WATER SUPPLY PIPE LINE "6 PVC
	3" PVC PIPE
	2" PVC PIPE
	1.5" PVC PIPE
	"1 PVC PIPE

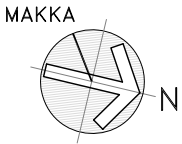

REV.	DATE	BY	DESCRIPTION
KEY PLAN			
 Associated Consulting Engineers International – ACE Riyadh - Jeddah - Dammam - Medina - Mecca - Dhahran - Bahrain - Kuwait - Muscat - Oman - Sharjah - UAE - Qatar - Doha - Kuwait - Riyadh - Saudi Arabia			
CONSULTANT			
 المكتب الاستشارات الهندسية Proportions Consulting Engineering Tel: 2752277, Fax: 2757722 P.O.Box 75453, Riyadh-11578			
PROJECT			
PRIVATE HOUSING COMPLEX AL NAKHEEL / RIYADH - SAUDI ARABIA			
OWNER			
SHEET TITLE			
LANDSCAPE IRRIGATION LEGEND			
TENDER DOCUMENTS			
PROJECT NO. :	P0521	STAGE :	WORKING DRAWINGS
DESIGNED BY :	Proportion Design	BY :	CAD
DATE :	MARCH 2006	SCALE :	1:200M
A130200			REVISION 0