



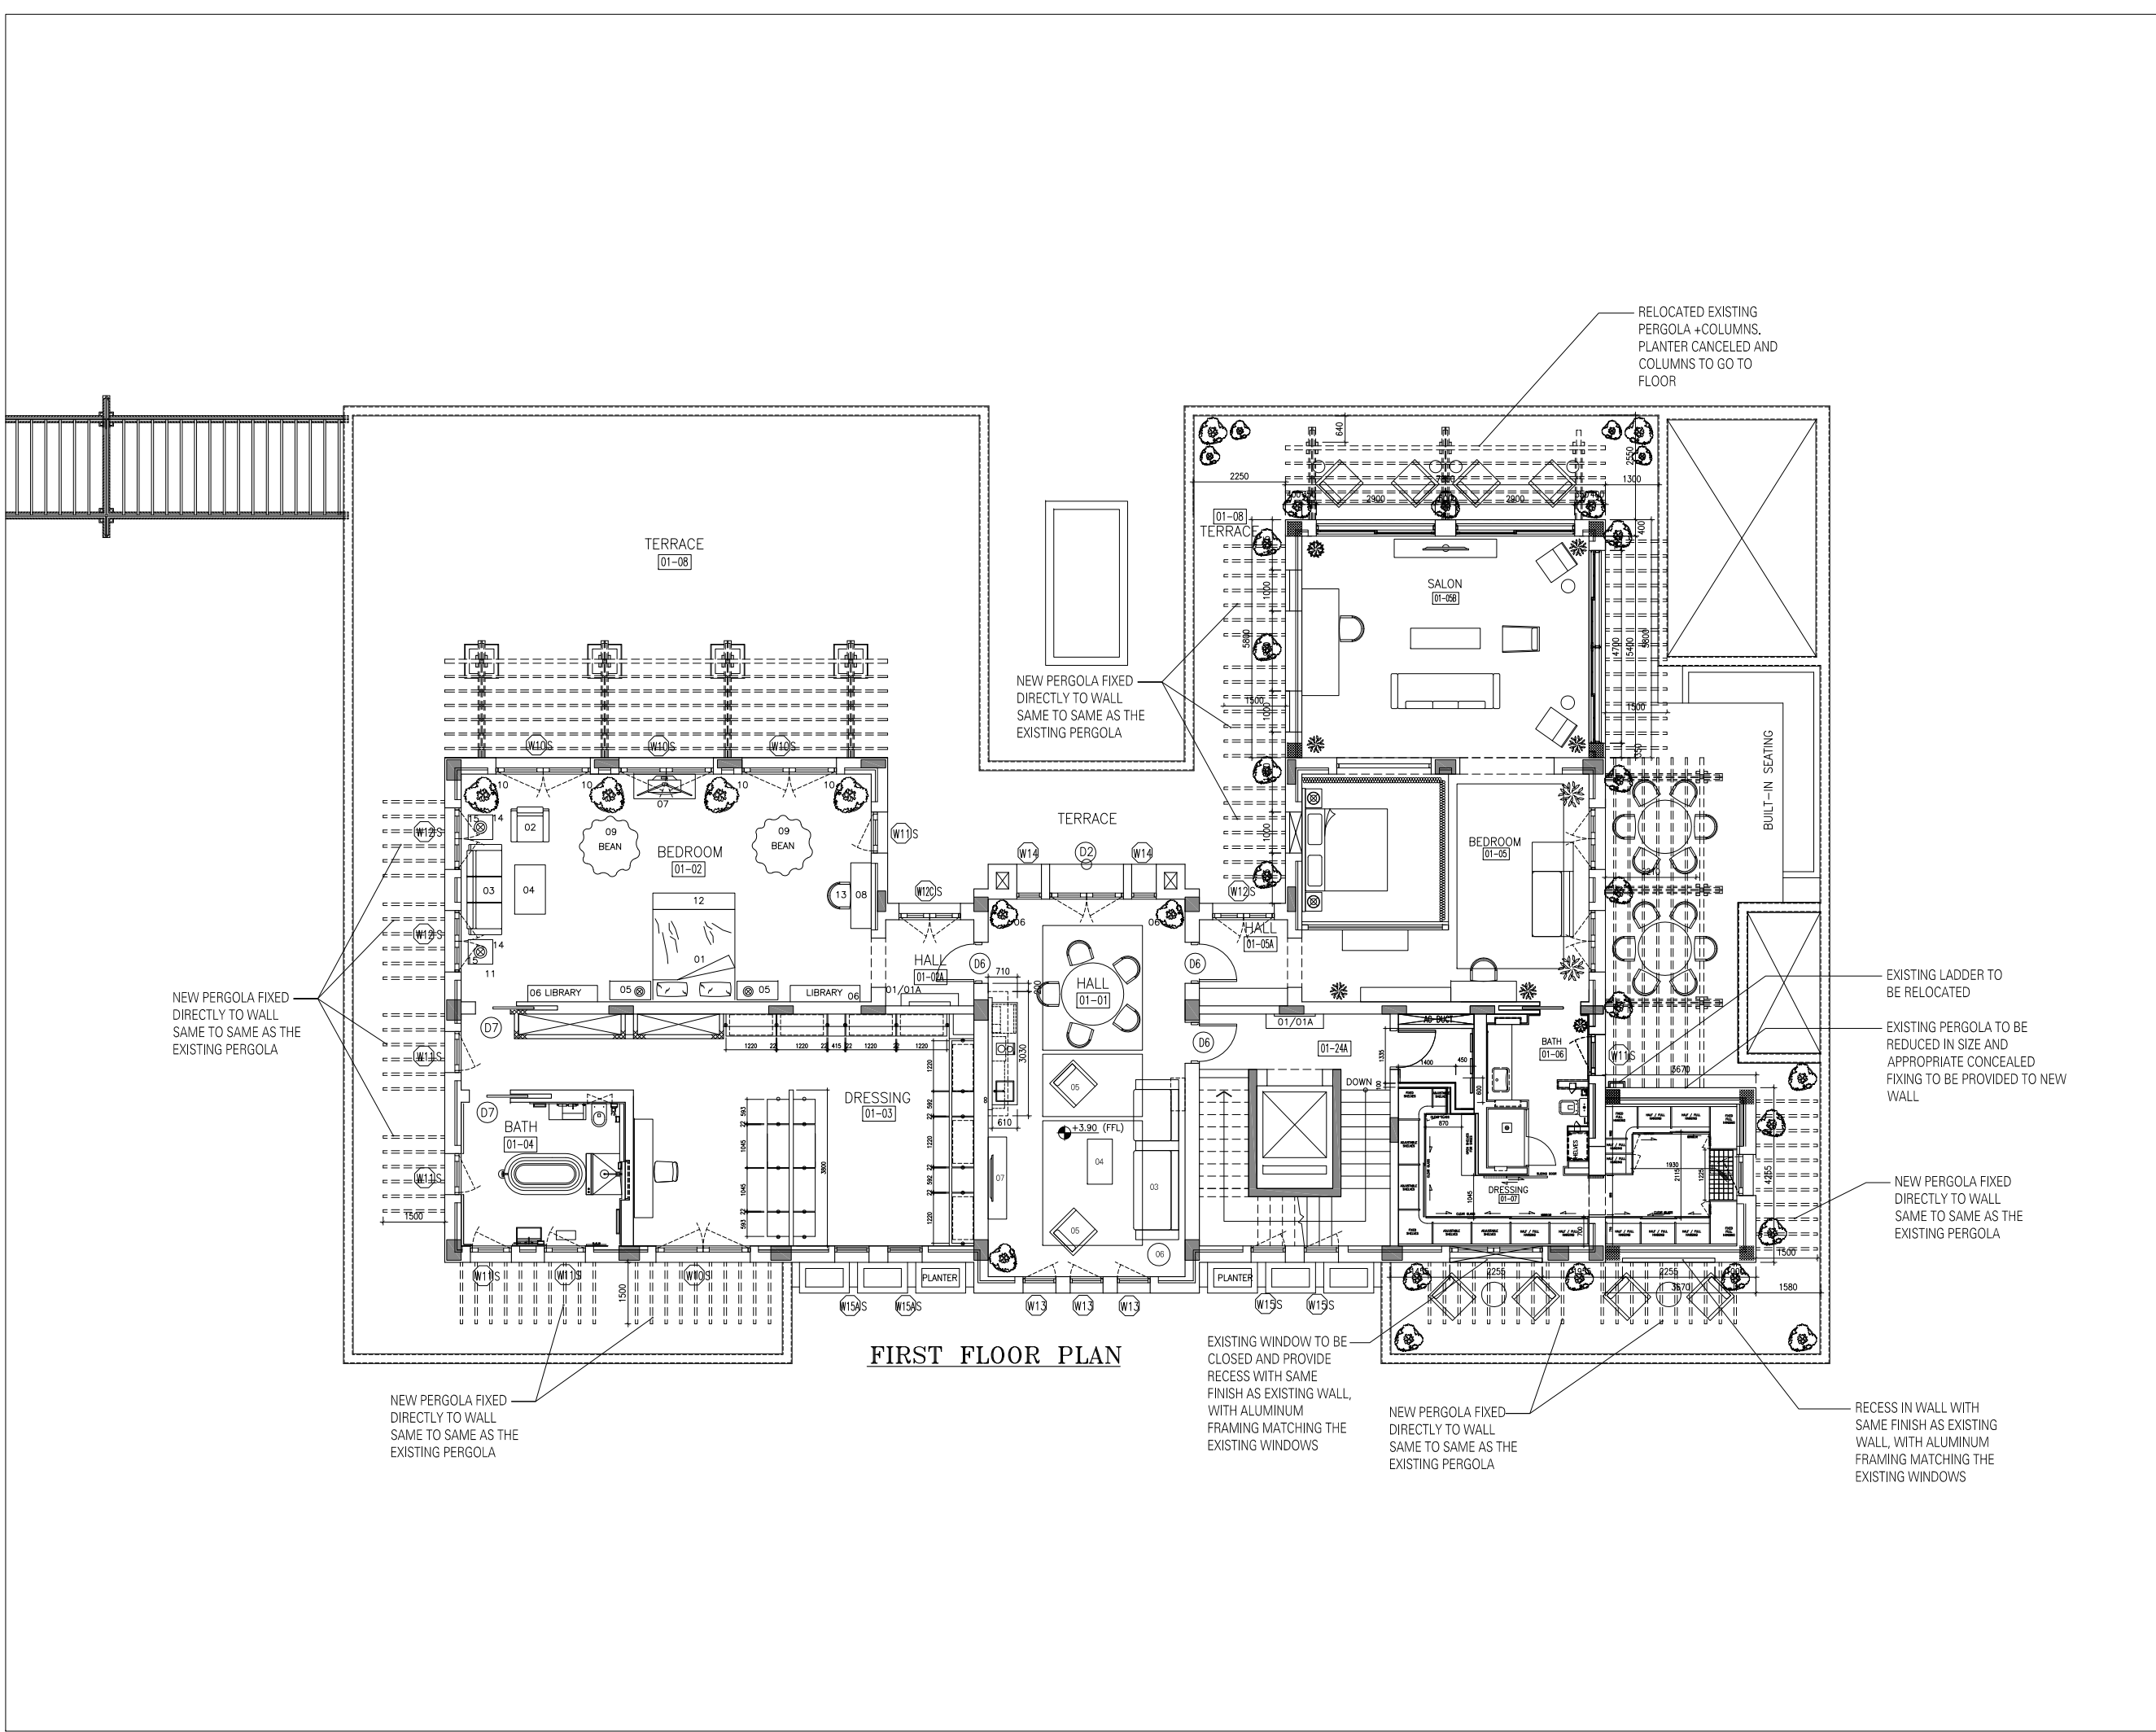

- GENERAL NOTES**
1. This drawing shall be read in conjunction with all other relevant architectural, structural & electrical drawings including those of other consultants.
 2. It is the responsibility of contractors & manufacturers to check all relevant site dimensions prior to the start of construction or manufacture.
 3. All materials and components must be installed on site in accordance with manufacturer's instructions, shop drawings and standard details.
 4. All dimensions are in millimeters unless noted otherwise.
 5. Full working drawings, specifications and samples are to be provided by Contractor/Supplier for approval prior to manufacture.

KEY PLAN

REV.	DESCRIPTION	BY	CHKD	APPD	DATE
C	GENERAL REV.	MP	AM	SM	2024.07.04
B	GENERAL REV.	MP	AM	SM	2024.07.01
X	INITIAL ISSUE	AC	AM	AM	2024.06.21
REV.#	GENERAL NOTES	DRAWN BY	CHECKED BY	APPROVED BY	DATE
PROJECT TITLE					REFERENCE
SAF-RIYADH					SAF01 G
DRAWING TITLE					
FIRST FLOOR PLAN					
DRAWING NUMBER					REVISION
SK-123					B
SCALE	FORMAT	ADDITIONAL NOTES	DESIGN DEVELOPMENT		
1:50	A1				
SIMA MALAK + ALSSAMOURE DESIGN ASSOCIATES					
P.O. Box 15707 - Riyadh 11454 KSA Tel. 01 441 4963 - Fax. 01 441 3867 simals@simals.com					
©SIMA MALAK + ALSSAMOURE DESIGN ASSOCIATES (شركة) 2003 This document including all drawing and text is the property and copyright of SIMA MALAK + ALSSAMOURE DESIGN ASSOCIATES for use solely with respect to this Project and shall not be copied or reproduced by any means except by agreement in writing from SIMA MALAK + ALSSAMOURE DESIGN ASSOCIATES.					

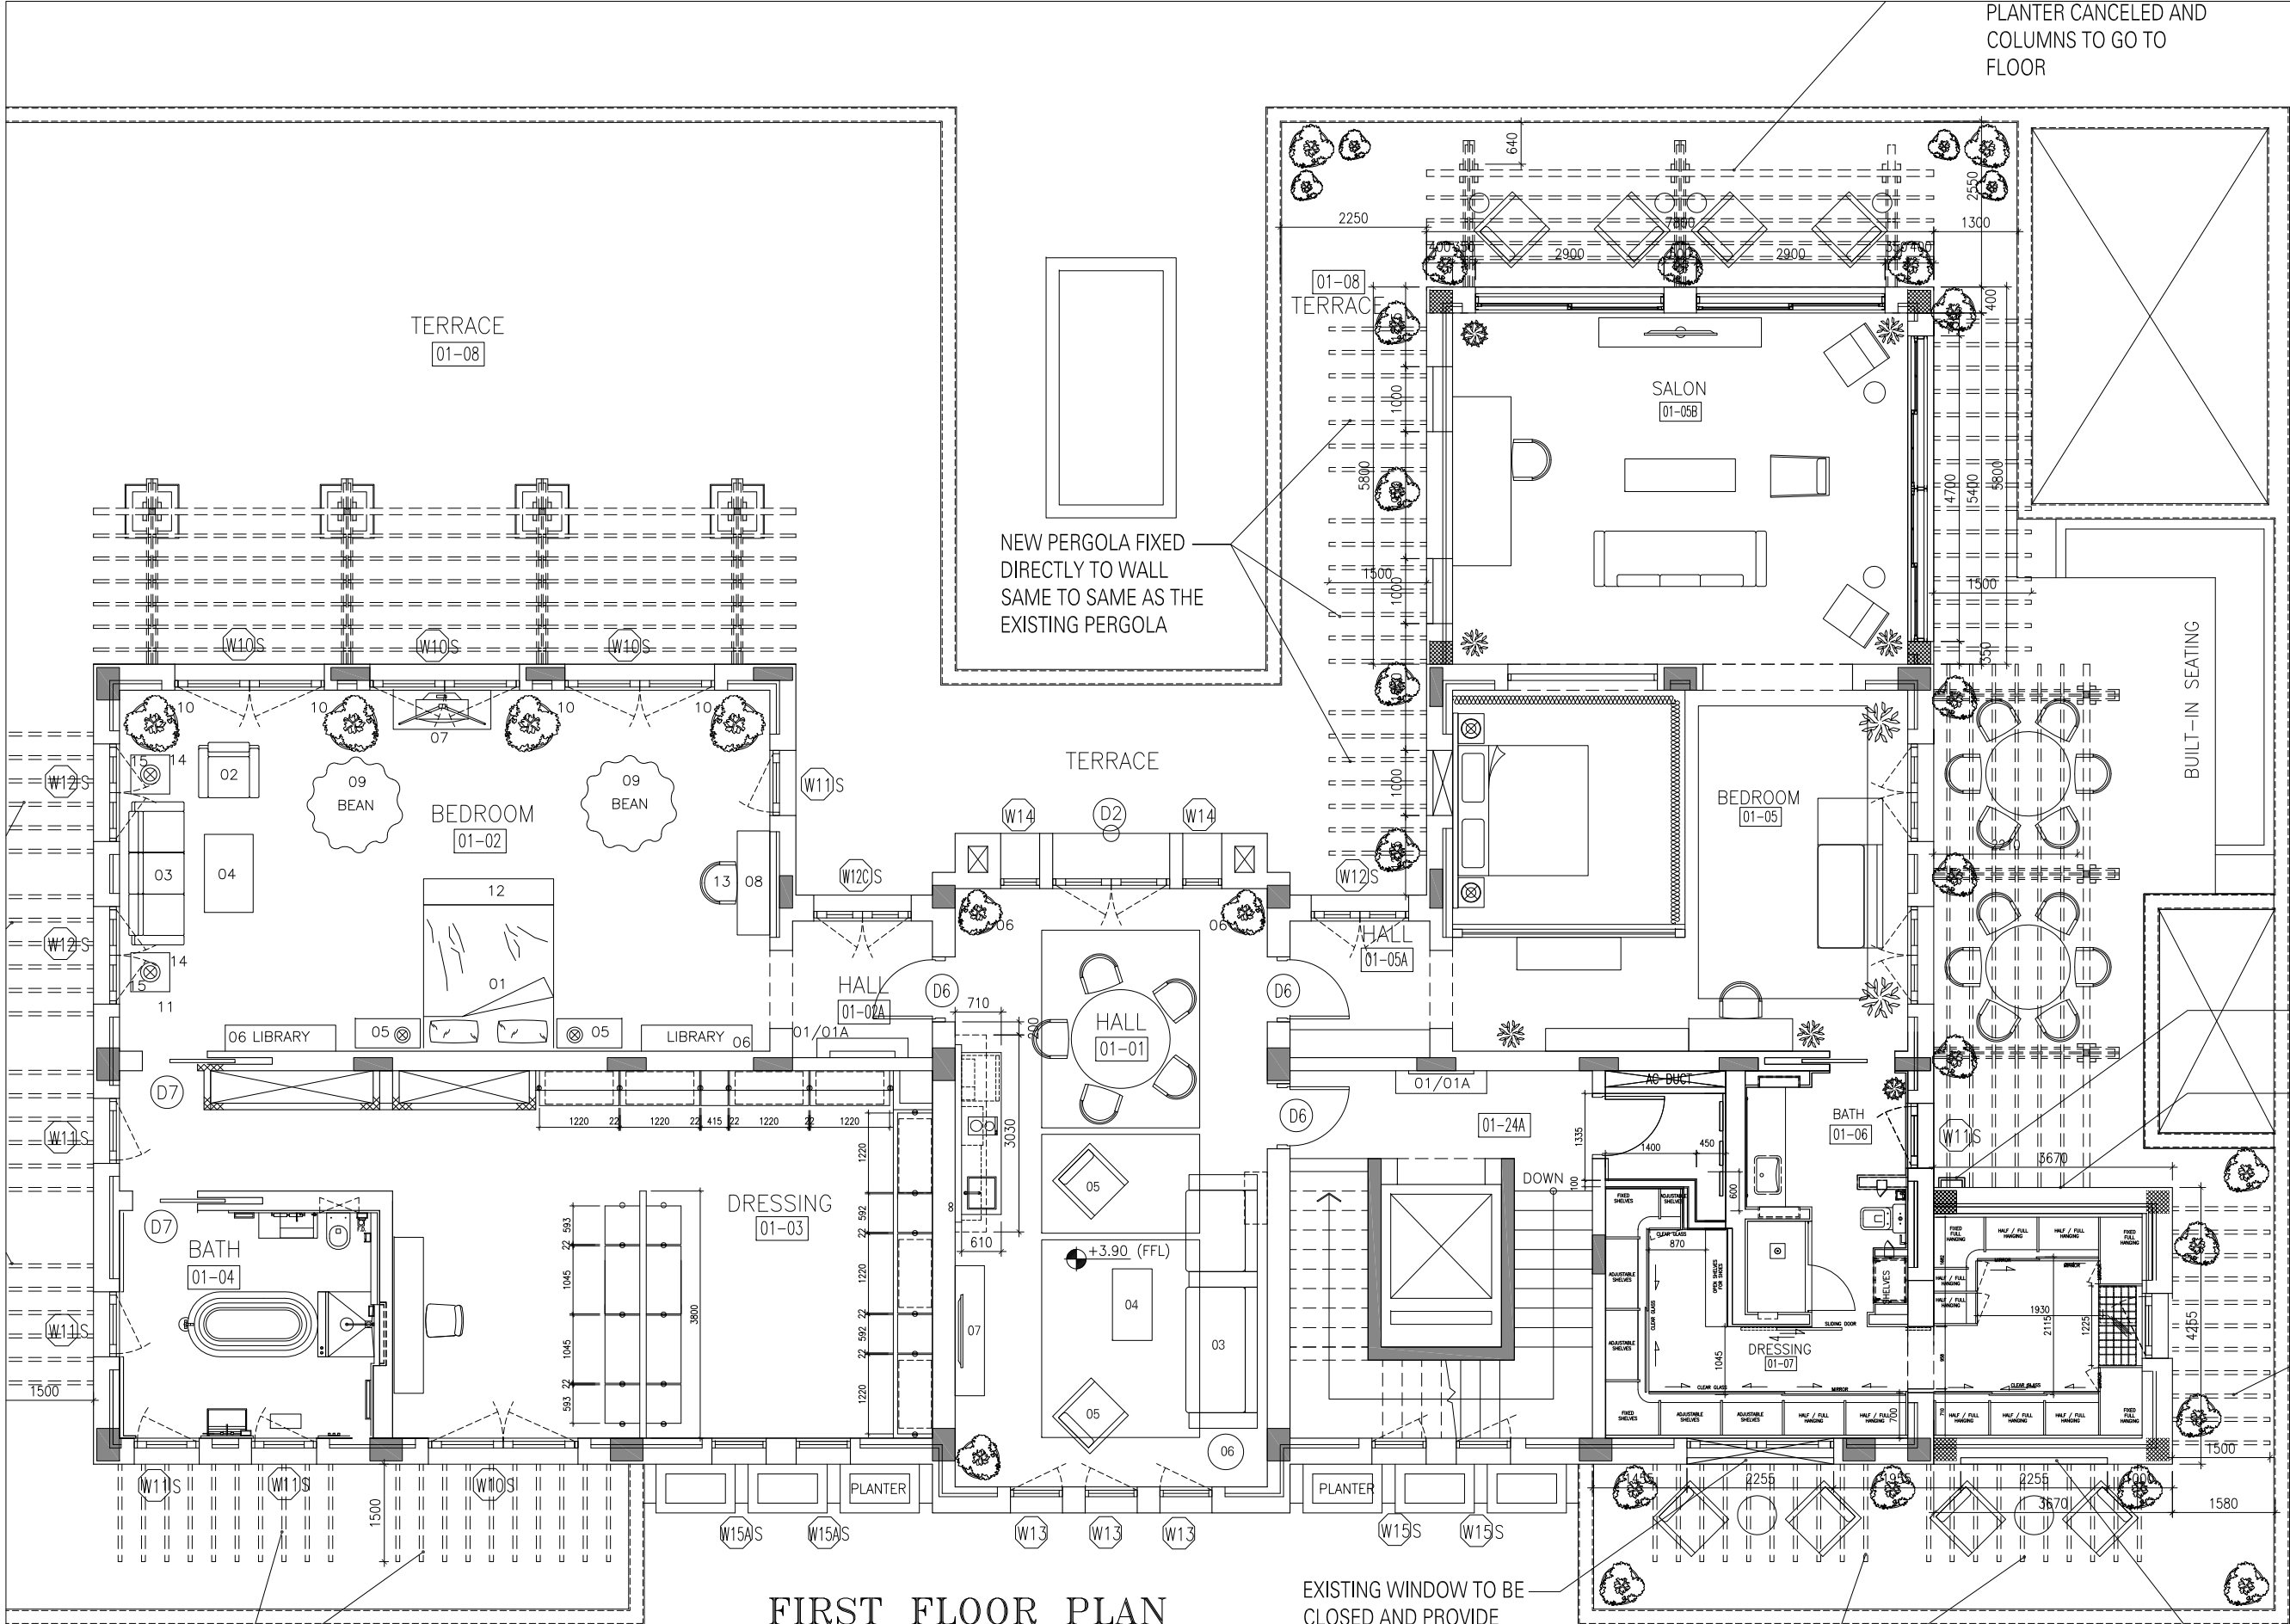

NEW PERGOLA FIXED
DIRECTLY TO WALL
SAME TO SAME AS THE
EXISTING PERGOLA

NEW PERGOLA FIXED
DIRECTLY TO WALL
SAME TO SAME AS THE
EXISTING PERGOLA

EXISTING WINDOW TO BE
CLOSED AND PROVIDE
RECESS WITH SAME
FINISH AS EXISTING WALL,
WITH ALUMINUM
FRAMING MATCHING THE
EXISTING WINDOWS

NEW PERGOLA FIXED
DIRECTLY TO WALL
SAME TO SAME AS THE
EXISTING PERGOLA

PLANTER CANCELED AND
COLUMNS TO GO TO
FLOOR

GENERAL NOTES

1. This drawing shall be read in conjunction with all other relevant architectural, structural & electrical drawings including those of other consultants.
2. It is the responsibility of contractors & manufacturers to check all relevant site dimensions prior to the start of construction or manufacture.
3. All materials and components must be installed on site in accordance with manufacturer's instructions, shop drawings and standard details.
4. All dimensions are in millimeters unless noted otherwise.
5. Full working drawings, specifications and samples are to be provided by Contractor/Supplier for approval prior to manufacture.


KEY PLAN

B	GENERAL REV.	MP	AM	SM	2024.07.01
X	INITIAL ISSUE	AC	AM	AM	2024.08.21
REV.#	GENERAL NOTES	DRAWN BY	CHECKED BY	APPROVED BY	DATE
PROJECT TITLE					REFERENCE
SAF-RIYADH					SAF01 G

DRAWING TITLE		REVISION	
FIRST FLOOR PLAN		A	
DRAWING NUMBER		SK-123	
SCALE	FORMAT	ADDITIONAL NOTES	DESIGN DEVELOPMENT
1:50	AT		

SIMA MALAK + ALSSAMOURÉ
DESIGN ASSOCIATES
P.O. Box 15707 - Riyadh 11454 KSA
Tel. 01 441 4963 - Fax. 01 441 3867
simas@simas.com

©SIMA MALAK + ALSSAMOURÉ DESIGN ASSOCIATES () 2003
This document including all drawing and text is the property and
copyright of SIMA MALAK + ALSSAMOURÉ DESIGN ASSOCIATES for
use solely with respect to this Project and shall not be copied or
reproduced by any means except by agreement in writing from
SIMA MALAK + ALSSAMOURÉ DESIGN ASSOCIATES.

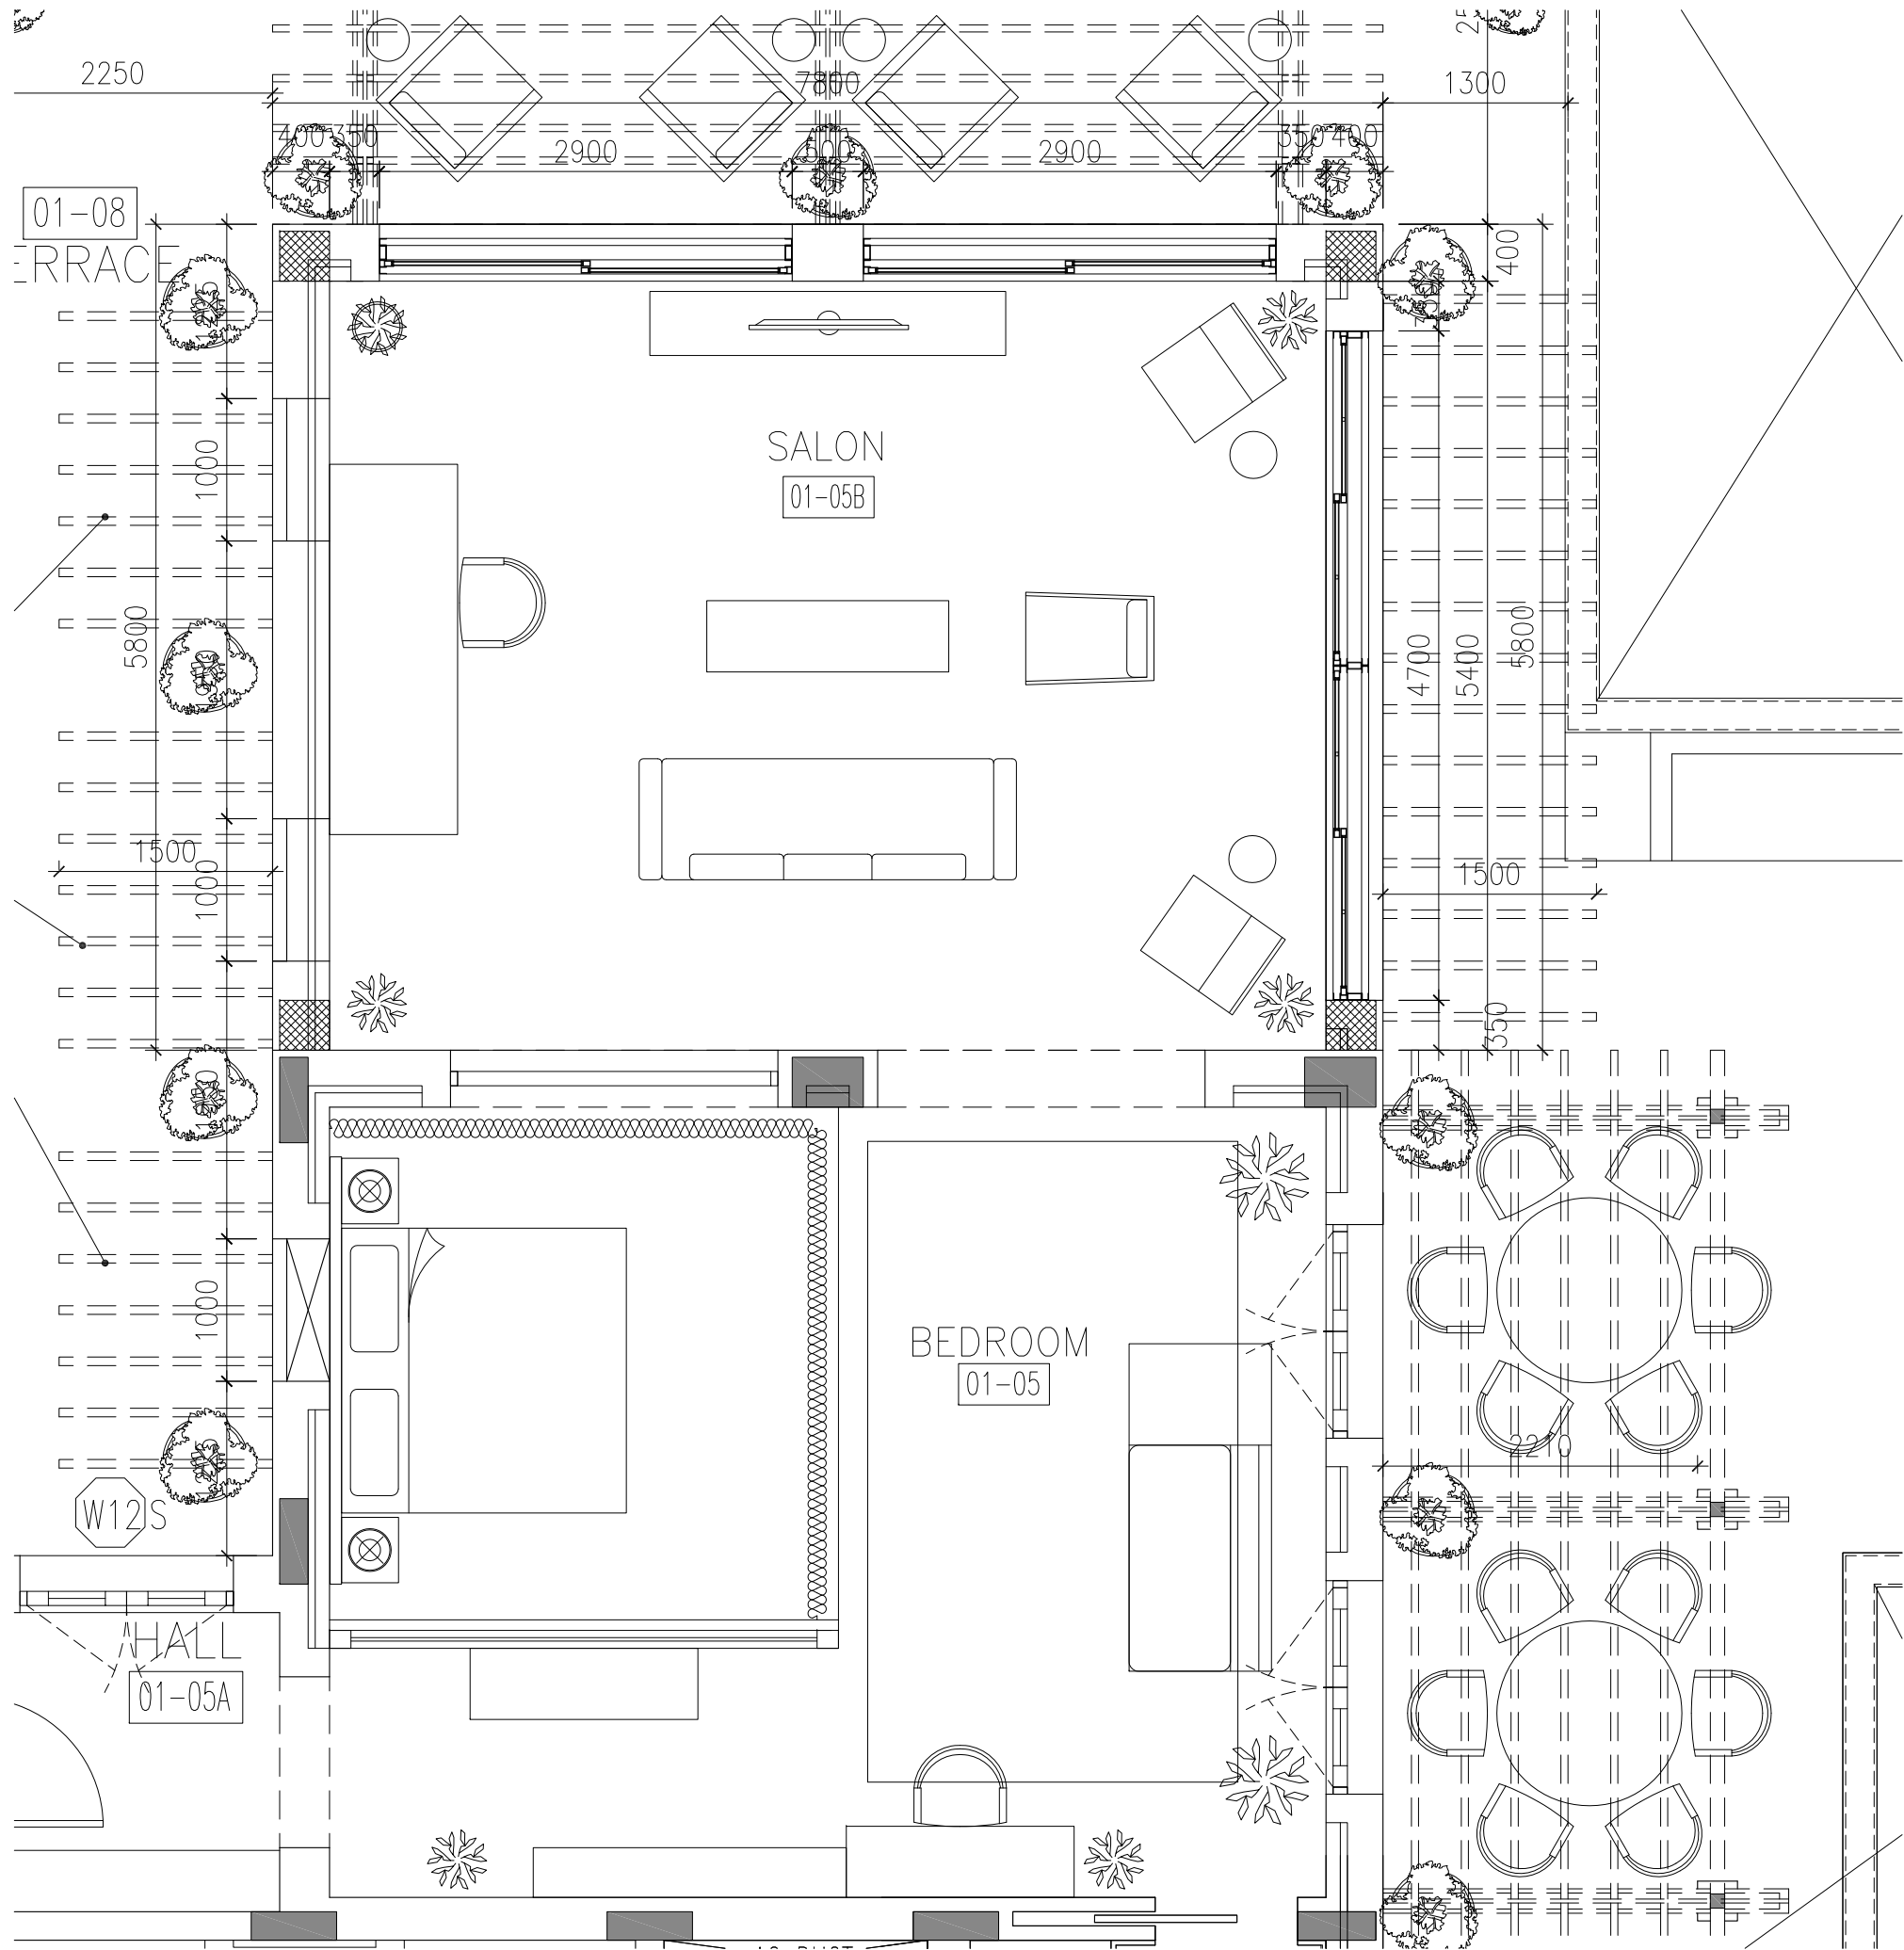

GENERAL NOTES

1. This drawing shall be read in conjunction with all other relevant architectural, structural & electrical drawings including those of other consultants.
2. It is the responsibility of contractors & manufacturers to check all relevant site dimensions prior to the start of construction or manufacture.
3. All materials and components must be installed on site in accordance with manufacturer's instructions, shop drawings and standard details.
4. All dimensions are in millimeters unless noted otherwise.
5. Full working drawings, specifications and samples are to be provided by Contractor/Supplier for approval prior to manufacture.

KEY PLAN

☒	INITIAL ISSUE	AC/MP	AM	AM	2024.06.10
REV.#	GENERAL NOTES	DRAWN BY	CHECKED BY	APPROVED BY	DATE

PROJECT TITLE	REFERENCE
---------------	-----------

SAF-RIYADH	SAF01 G
------------	------------

DRAWING TITLE

PROPOSED FIRST FLOOR
BEDROOM (01-05)+ SALON EXTENSION
LAYOUT

DRAWING NUMBER	REVISION
----------------	----------


SK-132	-
--------	---

SCALE 1:25	FORMAT A1	ADDITIONAL NOTES	DESIGN DEVELOPMENT
---------------	--------------	---------------------	--------------------




**SIMA MALAK + ALSSAMOURE
DESIGN ASSOCIATES**
P.O. Box 15707 - Riyadh 11454 KSA
Tel. 01 441 4963 - Fax. 01 441 3867
simals@simals.com

©SIMA MALAK + ALSSAMOURE DESIGN ASSOCIATES () 2003
This document including all drawing and text is the property and
copyright of SIMA MALAK + ALSSAMOURE DESIGN ASSOCIATES for
use solely with respect to this Project and shall not be copied or
reproduced by any means except by agreement in writing from
SIMA MALAK + ALSSAMOURE DESIGN ASSOCIATES.

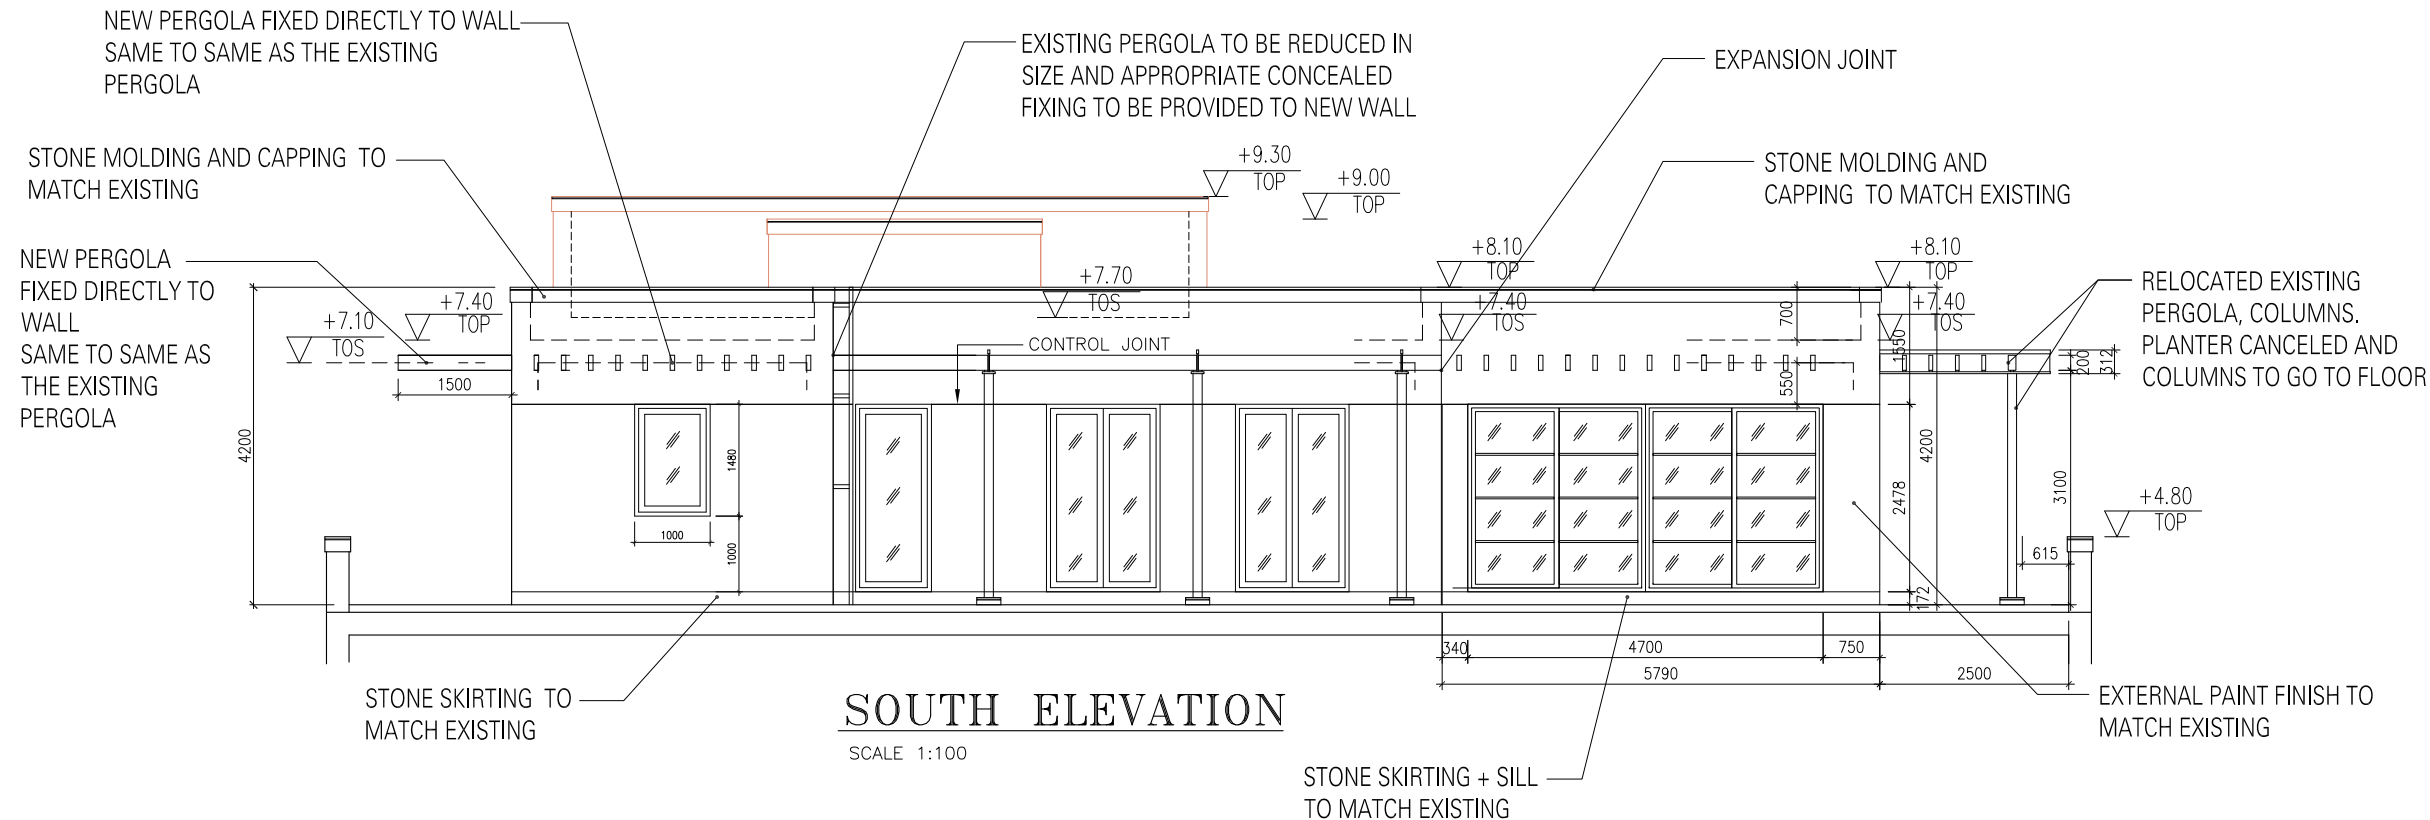

SOUTH ELEVATION
SCALE 1:100

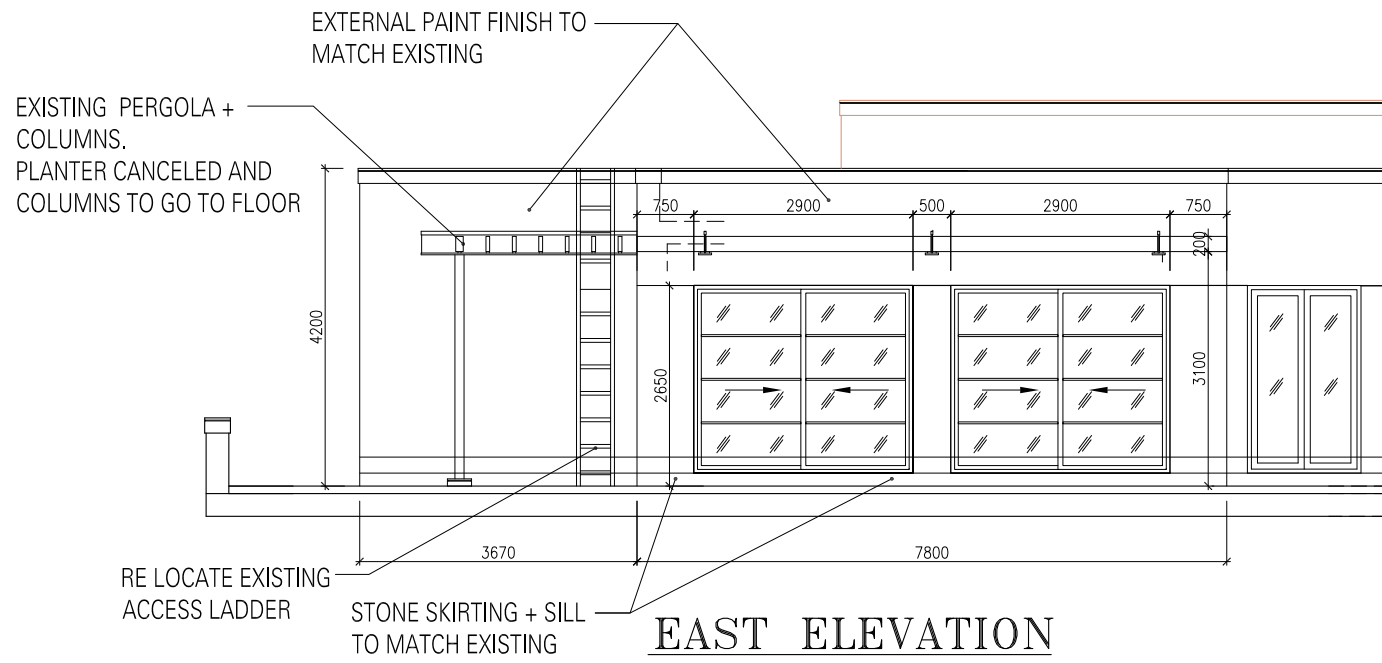

EAST ELEVATION
SCALE 1:100

GENERAL NOTES

1. This drawing shall be read in conjunction with all other relevant architectural, structural & electrical drawings including those of other consultants.
2. It is the responsibility of contractors & manufacturers to check all relevant site dimensions prior to the start of construction or manufacture.
3. All materials and components must be installed on site in accordance with manufacturer's instructions, shop drawings and standard details.
4. All dimensions are in millimeters unless noted otherwise.
5. Full working drawings, specifications and samples are to be provided by Contractor/Supplier for approval prior to manufacture.

KEY PLAN



REV.#	GENERAL NOTES	AC	AM	AM	2024.08.21
PROJECT TITLE	SAF-RIYADH	DATE	DATE	DATE	DATE
REFERENCE	SAF01	DATE	DATE	DATE	DATE

DRAWING TITLE	REVISION
FIRST FLOOR ELEVATIONS	-
DRAWING NUMBER	SK-126
SCALE	1:50
FORMAT	AT
ADDITIONAL NOTES	DESIGN DEVELOPMENT

SIMA MALAK + ALSSAMOURE DESIGN ASSOCIATES
P.O. Box 15707 - Riyadh 11454 KSA
Tel. 01 441 4963 - Fax. 01 441 3867
simals@simals.com

©SIMA MALAK + ALSSAMOURE DESIGN ASSOCIATES (شركة) 2003
This document including all drawing and text is the property and copyright of SIMA MALAK + ALSSAMOURE DESIGN ASSOCIATES for use solely with respect to this Project and shall not be copied or reproduced by any means except by agreement in writing from SIMA MALAK + ALSSAMOURE DESIGN ASSOCIATES.



+9.00
TOP

+8.10
TOP

+7.40
TOP

CONTROL JOINT

STONE MOLDING AND CAPPING TO MATCH EXISTING


EXISTING WINDOW TO BE CLOSED AND PROVIDE RECESS WITH SAME FINISH AS EXISTING WALL, WITH ALUMINUM FRAMING MATCHING THE EXISTING WINDOWS

RECESS IN WALL WITH SAME FINISH AS EXISTING WALL, WITH ALUMINUM FRAMING MATCHING THE EXISTING WINDOWS

WEST ELEVATION


DETAIL SHOWING RECESS + ALUMINUM FRAMING

©SIMA MALAK + ALSSAMOURI DESIGN ASSOCIATES (شركة) 2003
This document including all drawing and text is the property and
copyright of SIMA MALAK + ALSSAMOURI DESIGN ASSOCIATES for
use solely with respect to this Project and shall not be copied or
reproduced by any means except by agreement in writing from
SIMA MALAK + ALSSAMOURI DESIGN ASSOCIATES.

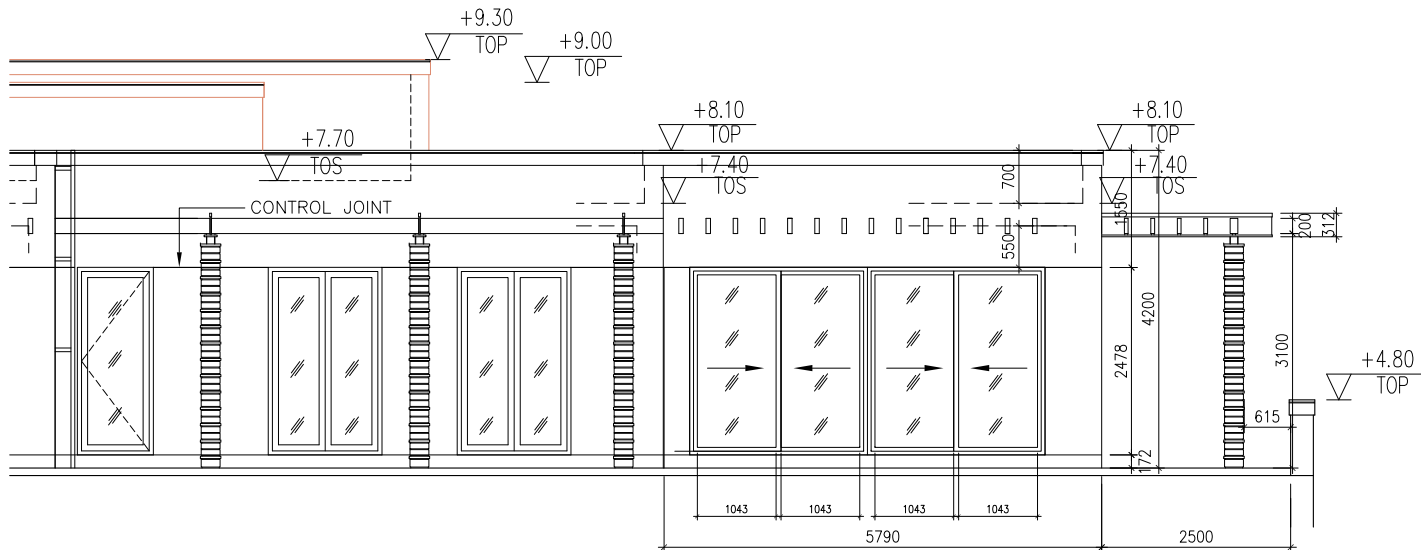


SOUTH ELEVATION OPTION-3

SCALE 1:100

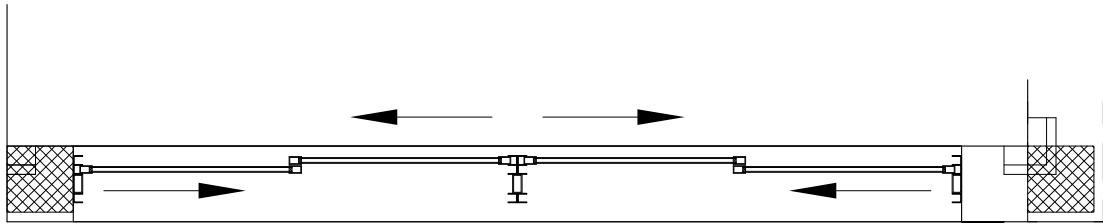


WINDOW KEY PLAN

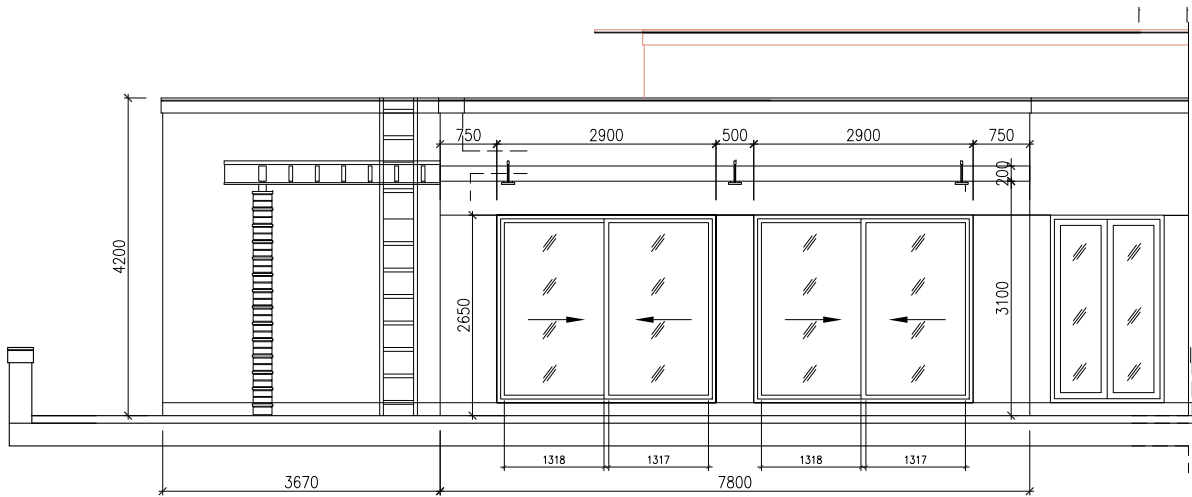

EAST ELEVATION (OPTION-3)

SCALE 1:100

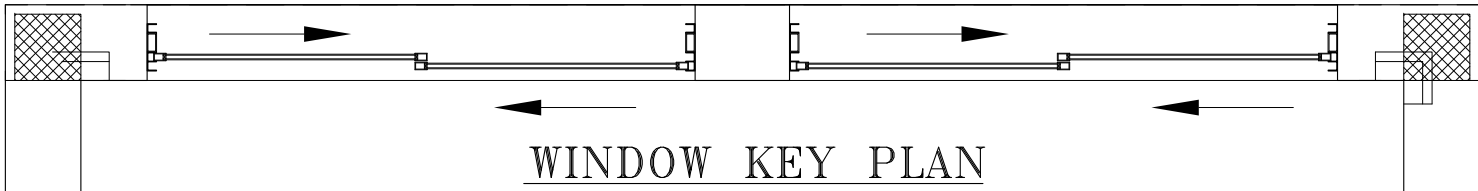

WINDOW KEY PLAN

GENERAL NOTES

1. This drawing shall be read in conjunction with all other relevant architectural, structural & electrical drawings including those of other consultants.
2. It is the responsibility of contractors & manufacturers to check all relevant site dimensions prior to the start of construction or manufacture.
3. All materials and components must be installed on site in accordance with manufacturer's instructions, shop drawings and standard details.
4. All dimensions are in millimeters unless noted otherwise.
5. Full working drawings, specifications and samples are to be provided by Contractor/Supplier for approval prior to manufacture.

KEY PLAN

INITIAL ISSUE	AC	AM	AM	2025.02.20
REV.#	GENERAL NOTES	DRAWN BY	CHECKED BY	APPROVED BY

PROJECT TITLE	REFERENCE
SAF-RIYADH	SAF01 G

DRAWING TITLE	REVISION
FIRST FLOOR ELEVATIONS OPTION-3	-

DRAWING NUMBER	REVISION
SK-137	-

SCALE	FORMAT	ADDITIONAL NOTES	DESIGN DEVELOPMENT
1:50	A1		

SIMA MALAK + ALSSAMOURE DESIGN ASSOCIATES

P.O. Box 15707 - Riyadh 11454 KSA
Tel. 01 441 4963 - Fax. 01 441 3867
simals@simals.com

©SIMA MALAK + ALSSAMOURE DESIGN ASSOCIATES (شركة) 2003
This document including all drawing and text is the property and copyright of SIMA MALAK + ALSSAMOURE DESIGN ASSOCIATES for use solely with respect to this Project and shall not be copied or reproduced by any means except by agreement in writing from SIMA MALAK + ALSSAMOURE DESIGN ASSOCIATES.