


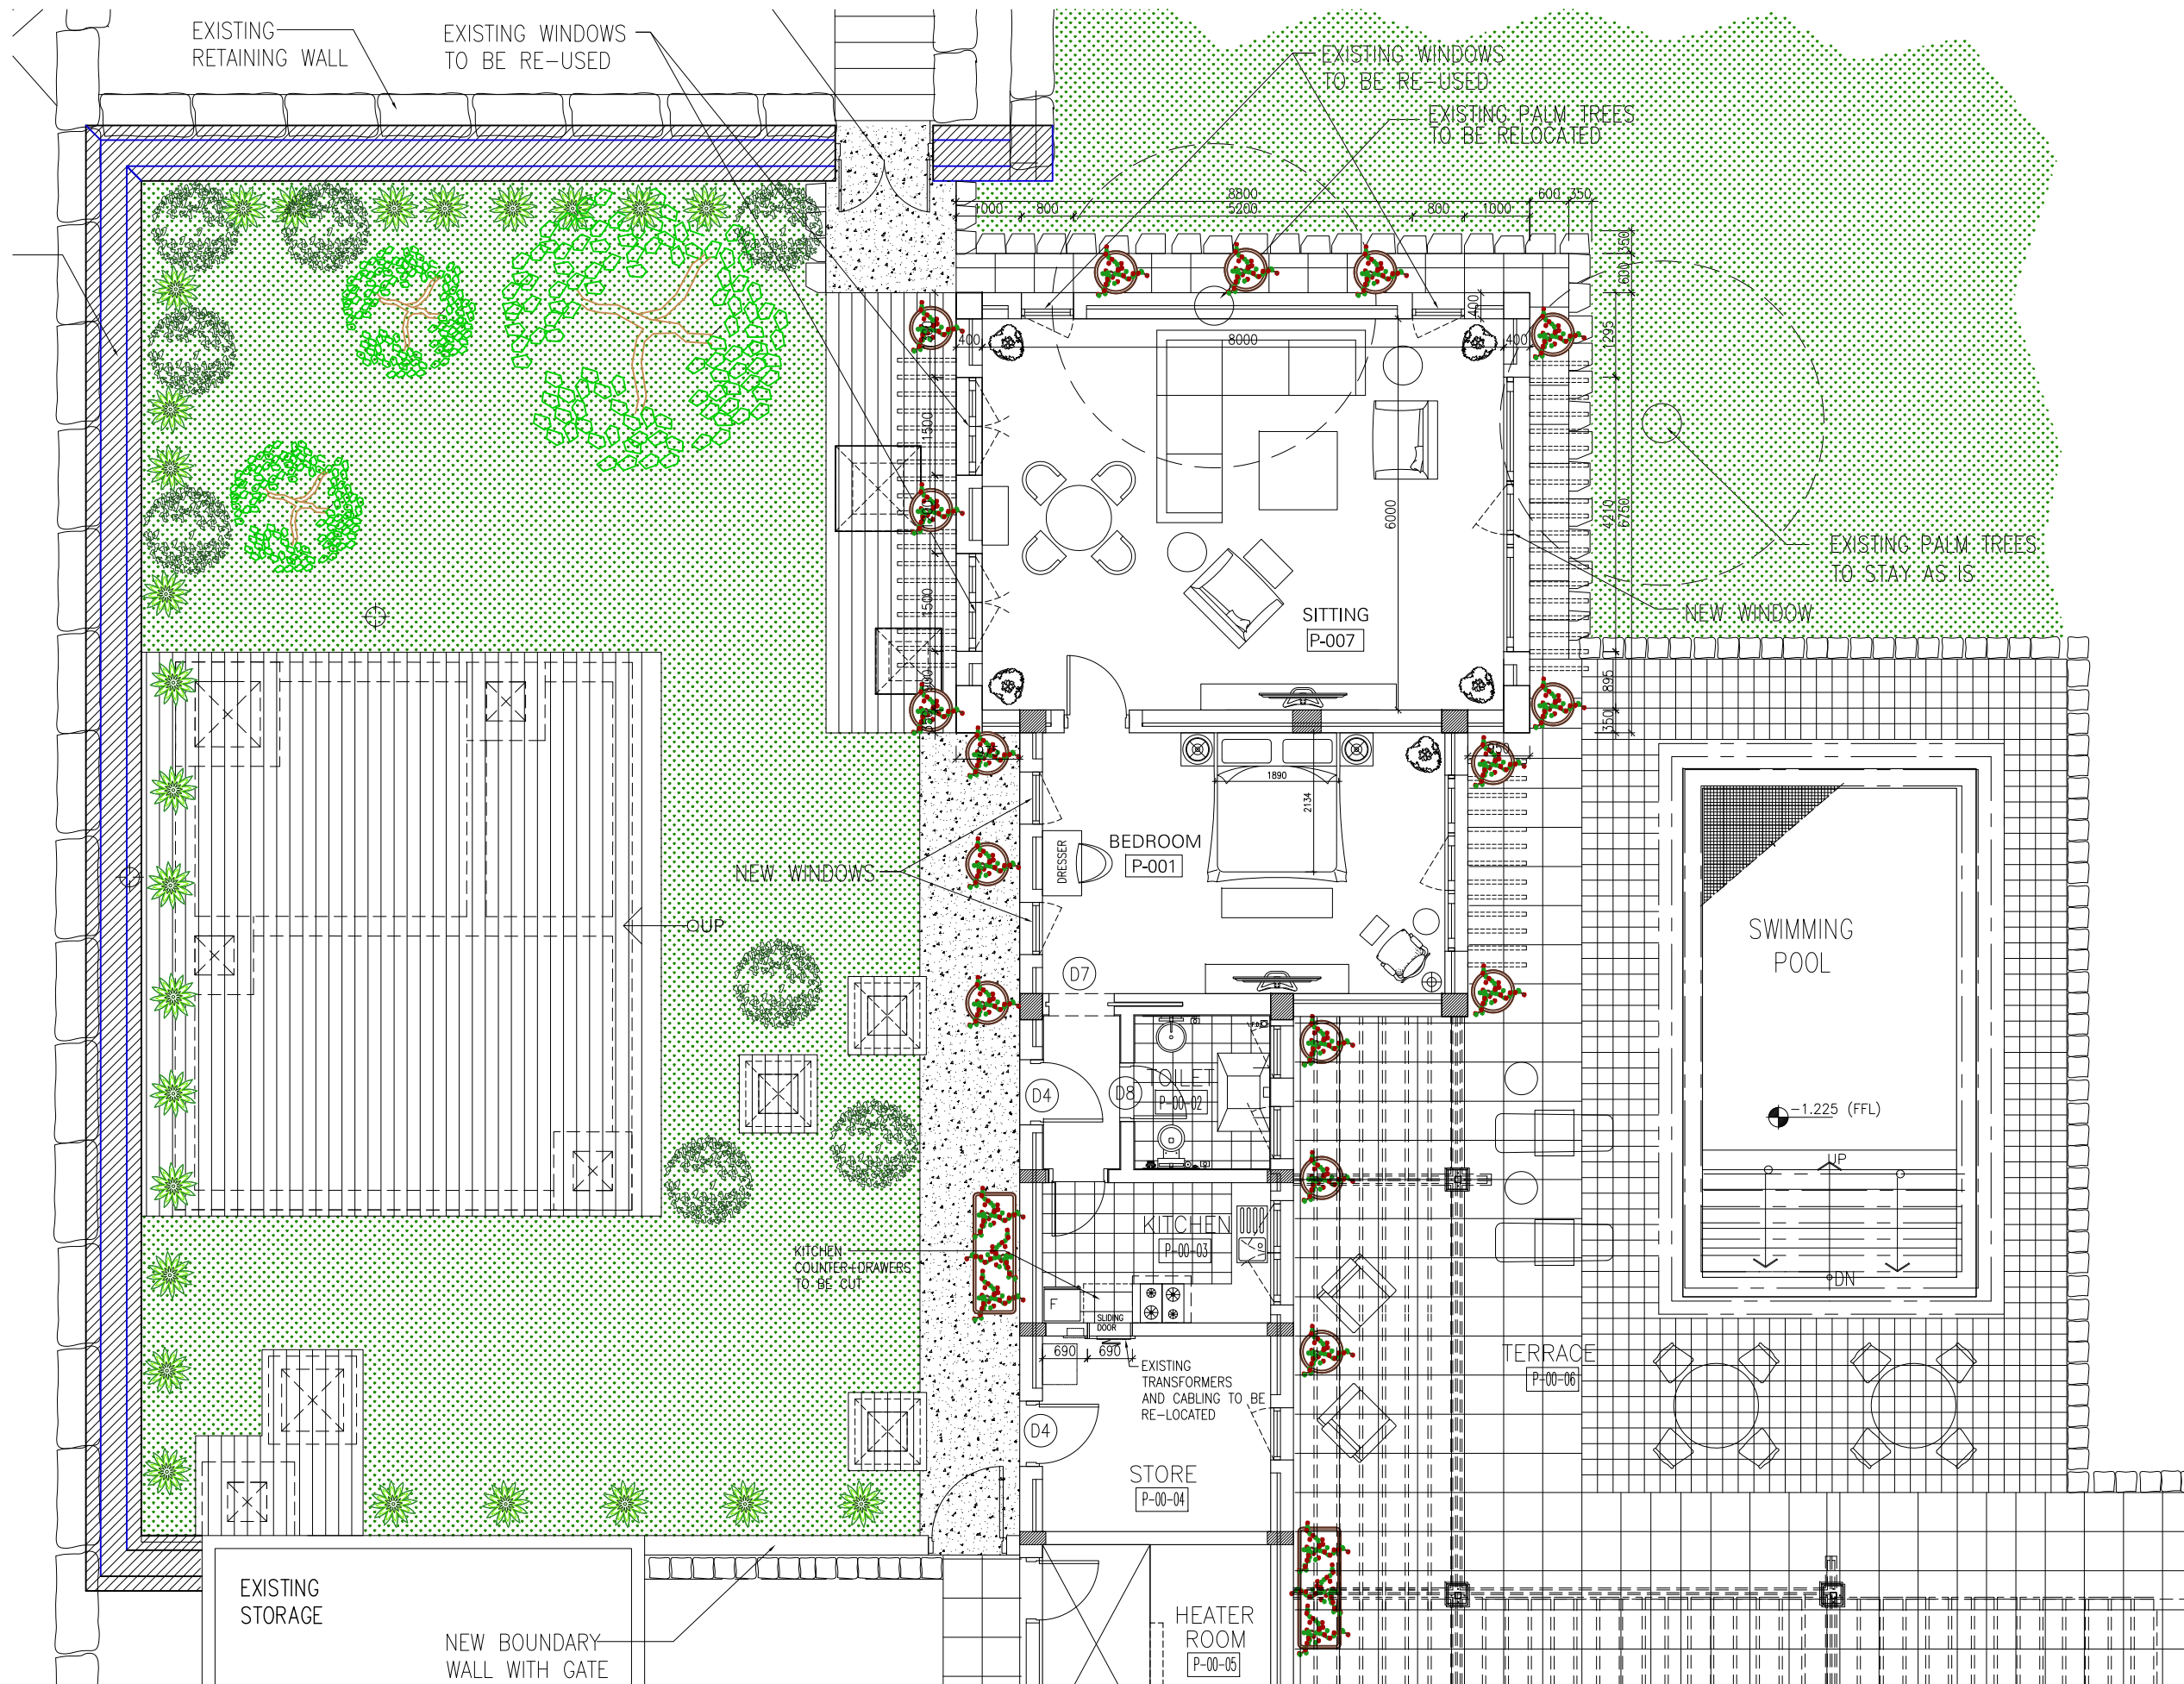

GENERAL NOTES

1. This drawing shall be read in conjunction with all other relevant architectural, structural & electrical drawings including those of other consultants.
2. It is the responsibility of contractors & manufacturers to check all relevant site dimensions prior to the start of construction or manufacture.
3. All materials and components must be installed on site in accordance with manufacturer's instructions, shop drawings and standard details.
4. All dimensions are in millimeters unless noted otherwise.
5. Full working drawings, specifications and samples are to be provided by Contractor/Supplier for approval prior to manufacture.

KEY PLAN

Q	GENERAL REV.	MP	AM	SM	2024.02.19
P	GENERAL REV.	MP	AM	SM	2024.02.12
O	GENERAL REV.	MP	AM	SM	2024.02.11
N	GEN. REV.	AC	AM	SM	2024.02.01
M	GENERAL REV.	MP	AM	SM	2024.01.28
L	GENERAL REV.	MP	AM	SM	2024.01.24
K	GENERAL REV.	MP	AM	SM	2024.01.23
J	GENERAL REV.	MP	AM	SM	2024.01.22
H	GENERAL REV.	MP	AM	SM	2024.01.15
G	GENERAL REV.	MP	AM	SM	2024.01.11
F	GENERAL REV.	MP	AM	SM	2024.01.10
E	GENERAL REV.	MP	AM	SM	2024.01.08
D	GENERAL REV.	MP	AM	SM	2024.01.07
C	GEN. REV.	AC	AM	SM	2023.12.17
B	GENERAL REV.	MP	AM	SM	2023.08.10
A	GEN. REV.	AC	AM	SM	2023.05.30
X	INITIAL ISSUE	AC	AM	SM	2023.05.22

REV.#	GENERAL NOTES	DRAWN BY	CHECKED BY	APPROVED BY	DATE
PROJECT TITLE	REFERENCE				

SAF - RIYADH	SAF01
	G

DRAWING TITLE

PROPOSED
POOL BLDG EXTENSION
GROUND FLOOR PLAN

DRAWING NUMBER

SK-94

SCALE
1:50

FORMAT
A1




ADDITIONAL
NOTES

DESIGN DEVELOPMENT

**SIMA MALAK + ALSSAMOURE
DESIGN ASSOCIATES**

P.O. Box 15707 - Riyadh 11454 KSA
Tel. 01 441 4963 - Fax. 01 441 3867
simas@simas.com

©SIMA MALAK + ALSSAMOURE DESIGN ASSOCIATES () 2003
This document including all drawing and text is the property and
copyright of SIMA MALAK + ALSSAMOURE DESIGN ASSOCIATES for
use solely with respect to this Project and shall not be copied or
reproduced by any means except by agreement in writing from
SIMA MALAK + ALSSAMOURE DESIGN ASSOCIATES.

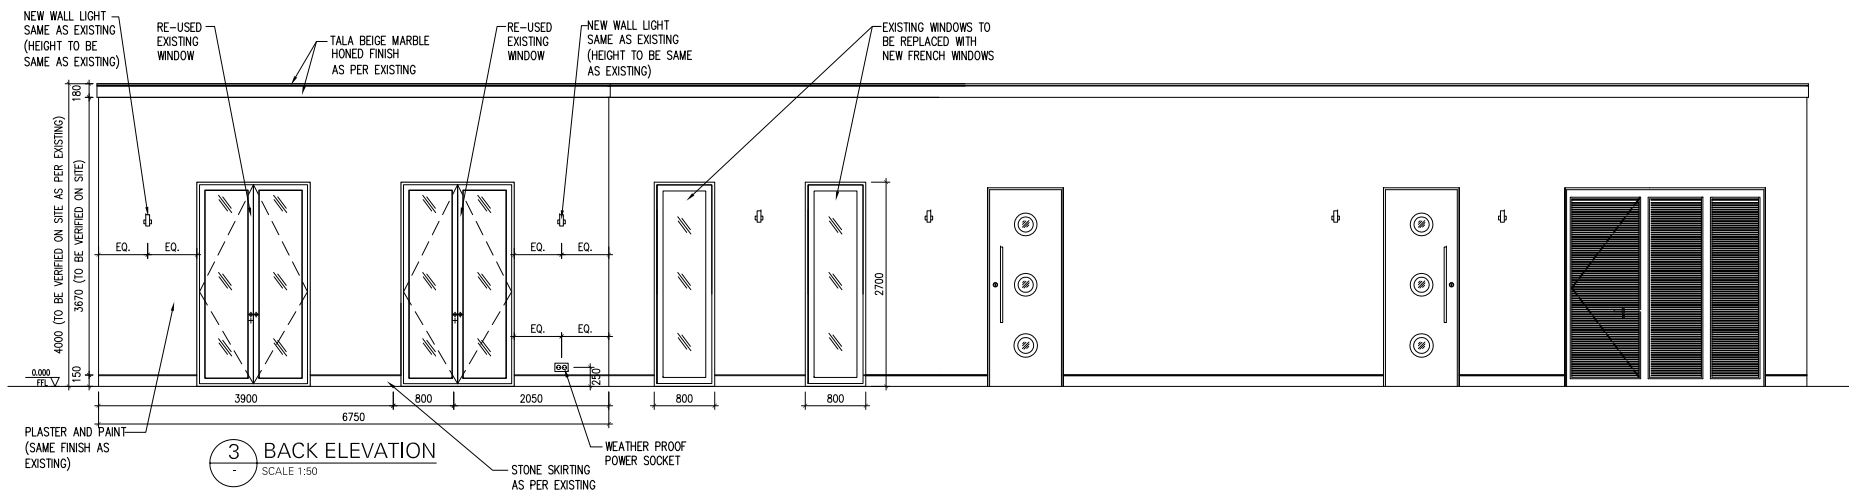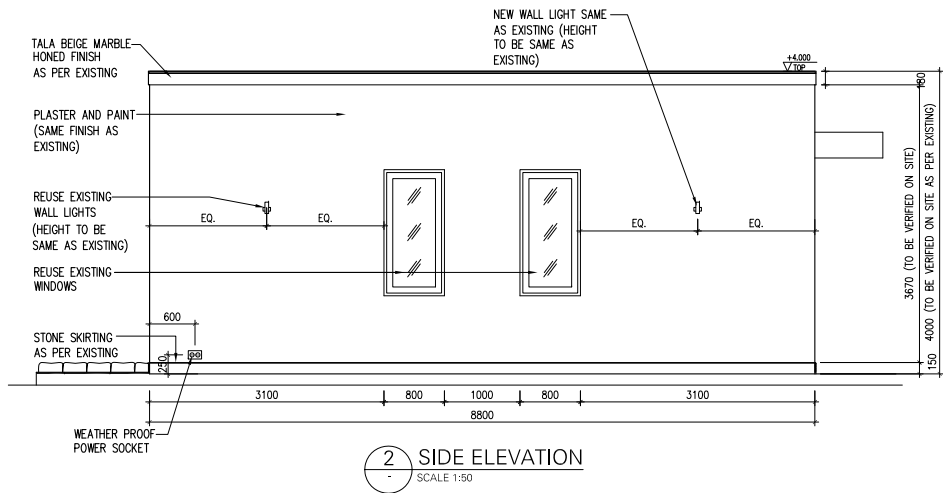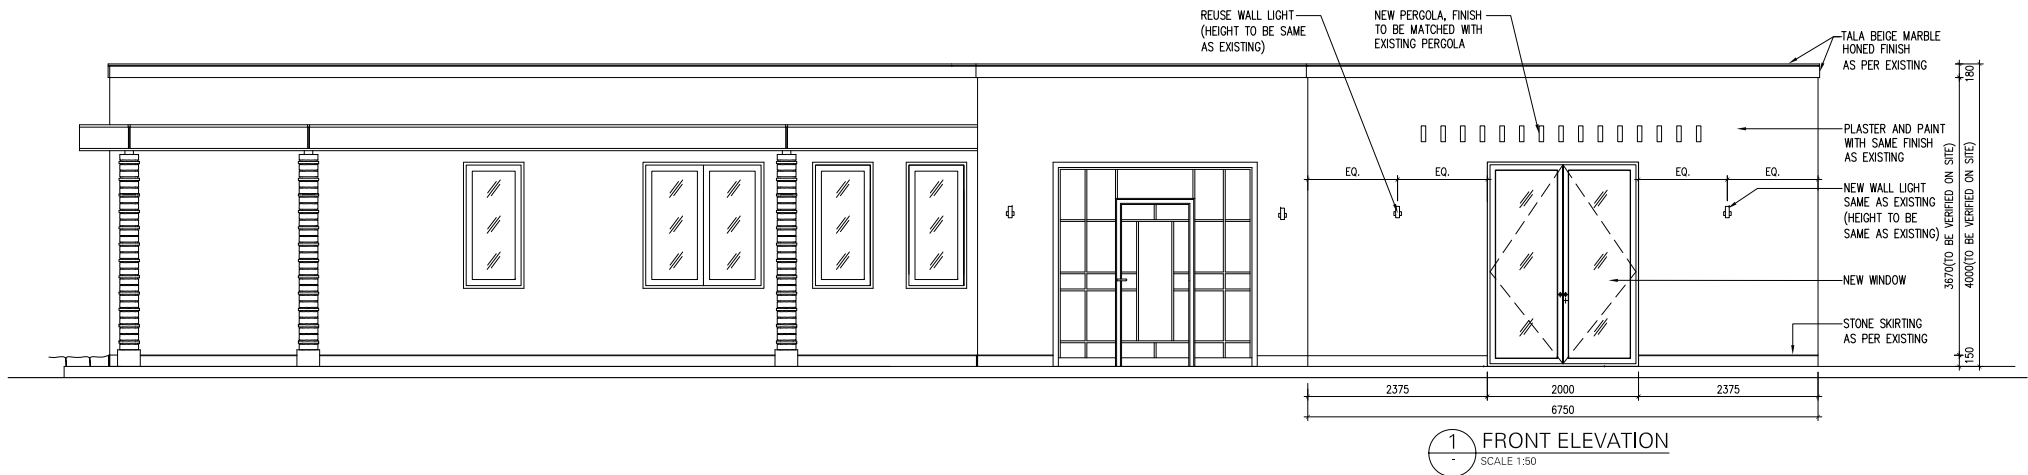

GENERAL NOTES

1. This drawing shall be read in conjunction with all other relevant architectural, structural & electrical drawings including those of other consultants.
2. It is the responsibility of contractors & manufacturers to check all relevant site dimensions prior to the start of construction or manufacture.
3. All materials and components must be installed on site in accordance with manufacturer's instructions, shop drawings and standard details.
4. All dimensions are in millimeters unless noted otherwise.
5. Full working drawings, specifications and samples are to be provided by Contractor/Supplier for approval prior to manufacture.

KEY PLAN

I	GENERAL REV.	MP	AM	SM	2024.02.12
H	GENERAL REV.	MP	AM	SM	2024.02.11
G	GEN REV.	AC	AM	SM	2024.02.04
F	GENERAL REV.	MP	AM	SM	2024.01.28
E	GENERAL REV.	MP	AM	SM	2024.01.23
D	GENERAL REV.	MP	AM	SM	2024.01.14
C	GENERAL REV.	MP	AM	SM	2023.12.17
B	GENERAL REV.	MP	AM	SM	2023.07.04
A	GENERAL REV.	MP	AM	SM	2023.06.25
X	INITIAL ISSUE	AC	AM	SM	2023.06.22
REV.#	GENERAL NOTES	DRAWN BY	CHECKED BY	APPROVED BY	DATE

PROJECT TITLE	REFERENCE
SAF - RIYADH	SAF01 G

DRAWING TITLE

POOL BLDG EXTENSION ELEVATIONS

DRAWING NUMBER




SK-95

SCALE	FORMAT	ADDITIONAL NOTES	DESIGN DEVELOPMENT
1:50	A1		



**SIMA MALAK + ALSSAMOURE
DESIGN ASSOCIATES**
P.O. Box 15707 - Riyadh 11454 KSA
Tel. 01 441 4963 - Fax. 01 441 3867
simals@simals.com

©SIMA MALAK + ALSSAMOURE DESIGN ASSOCIATES (شركة) 2003
This document including all drawing and text is the property and
copyright of SIMA MALAK + ALSSAMOURE DESIGN ASSOCIATES for
use solely with respect to this Project and shall not be copied or
reproduced by any means except by agreement in writing from
SIMA MALAK + ALSSAMOURE DESIGN ASSOCIATES.

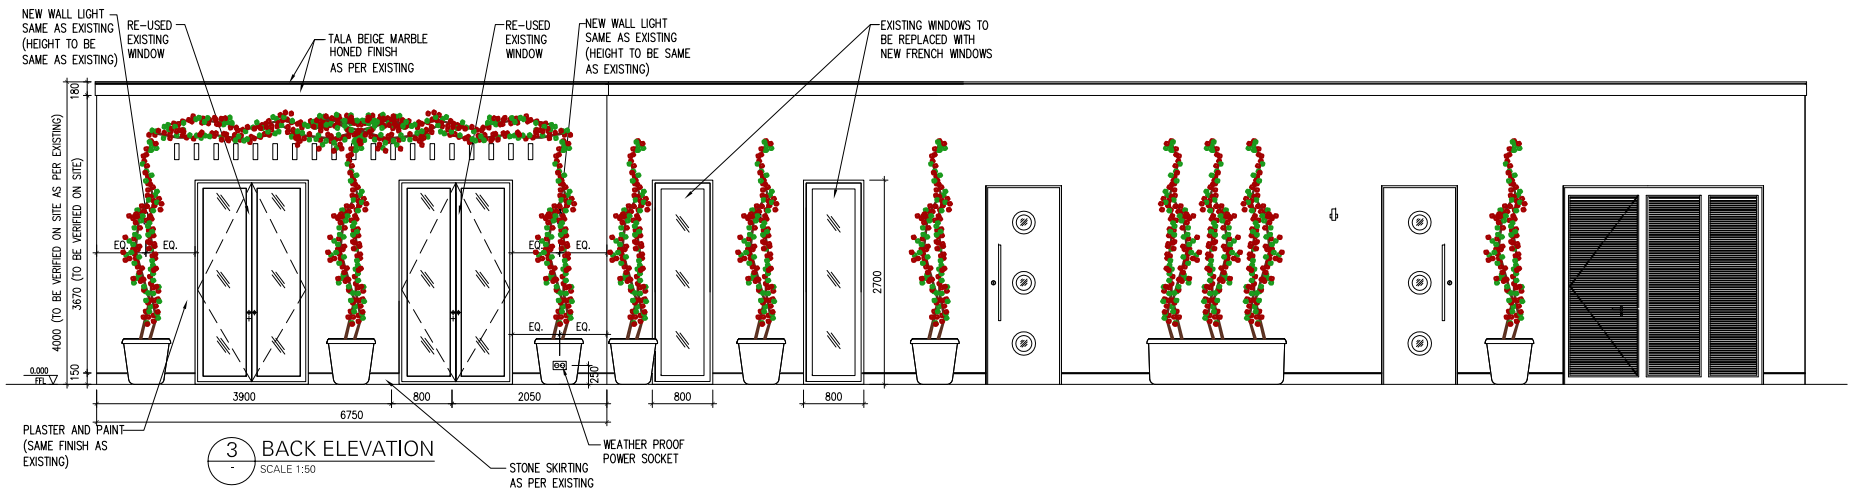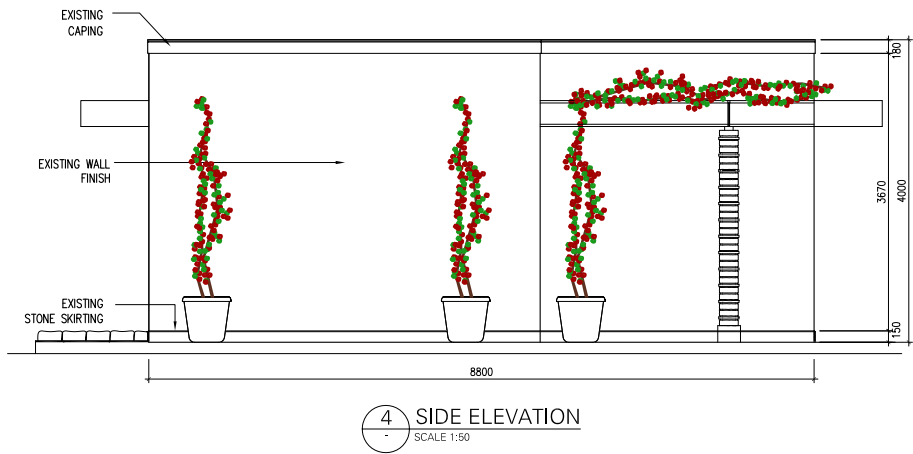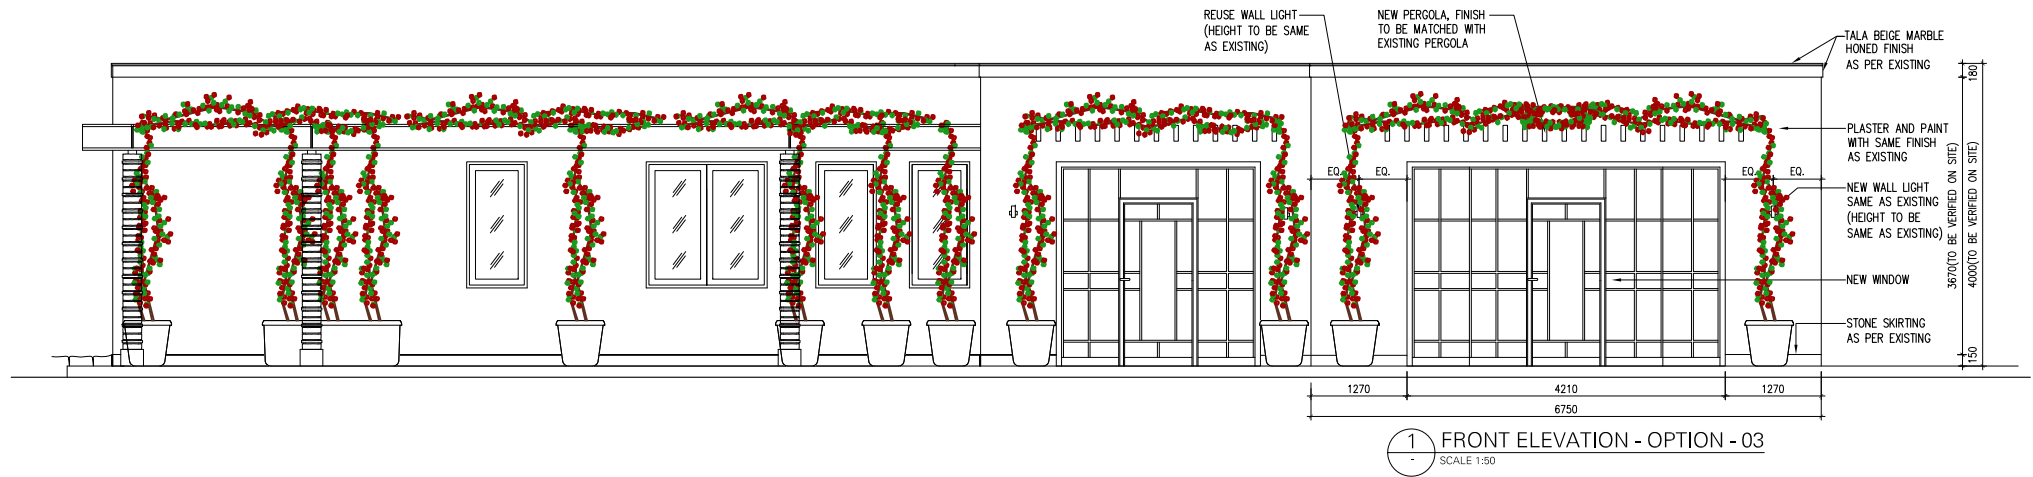

GENERAL NOTES

1. This drawing shall be read in conjunction with all other relevant architectural, structural & electrical drawings including those of other consultants.
2. It is the responsibility of contractors & manufacturers to check all relevant site dimensions prior to the start of construction or manufacture.
3. All materials and components must be installed on site in accordance with manufacturer's instructions, shop drawings and standard details.
4. All dimensions are in millimeters unless noted otherwise.
5. Full working drawings, specifications and samples are to be provided by Contractor/Supplier for approval prior to manufacture.

KEY PLAN

J	GENERAL REV.	MP	AM	SM	2024.02.27
I	GENERAL REV.	MP	AM	SM	2024.02.12
H	GENERAL REV.	MP	AM	SM	2024.02.11
G	GEN REV.	AC	AM	SM	2024.02.04
F	GENERAL REV.	MP	AM	SM	2024.01.28
E	GENERAL REV.	MP	AM	SM	2024.01.23
D	GENERAL REV.	MP	AM	SM	2024.01.14
C	GENERAL REV.	MP	AM	SM	2023.12.17
B	GENERAL REV.	MP	AM	SM	2023.07.04
A	GENERAL REV.	MP	AM	SM	2023.06.25
X	INITIAL ISSUE	AC	AM	SM	2023.06.22

REV.#	GENERAL NOTES	DRAWN BY	CHECKED BY	APPROVED BY	DATE

PROJECT TITLE	REFERENCE
SAF - RIYADH	SAF01 G

DRAWING TITLE

POOL BLDG EXTENSION ELEVATIONS

DRAWING NUMBER

SK-95

REVISION

J

SCALE

1:50

FORMAT

AT

ADDITIONAL NOTES

DESIGN DEVELOPMENT


SIMA MALAK + ALSSAMOURE
DESIGN ASSOCIATES

P.O. Box 15707 - Riyadh 11454 KSA


Tel. 01 441 4963 - Fax. 01 441 3867

simala@simala.com


©SIMA MALAK + ALSSAMOURE DESIGN ASSOCIATES (شركة) 2003
This document including all drawing and text is the property and
copyright of SIMA MALAK + ALSSAMOURE DESIGN ASSOCIATES for
use solely with respect to this Project and shall not be copied or
reproduced by any means except by agreement in writing from
SIMA MALAK + ALSSAMOURE DESIGN ASSOCIATES.

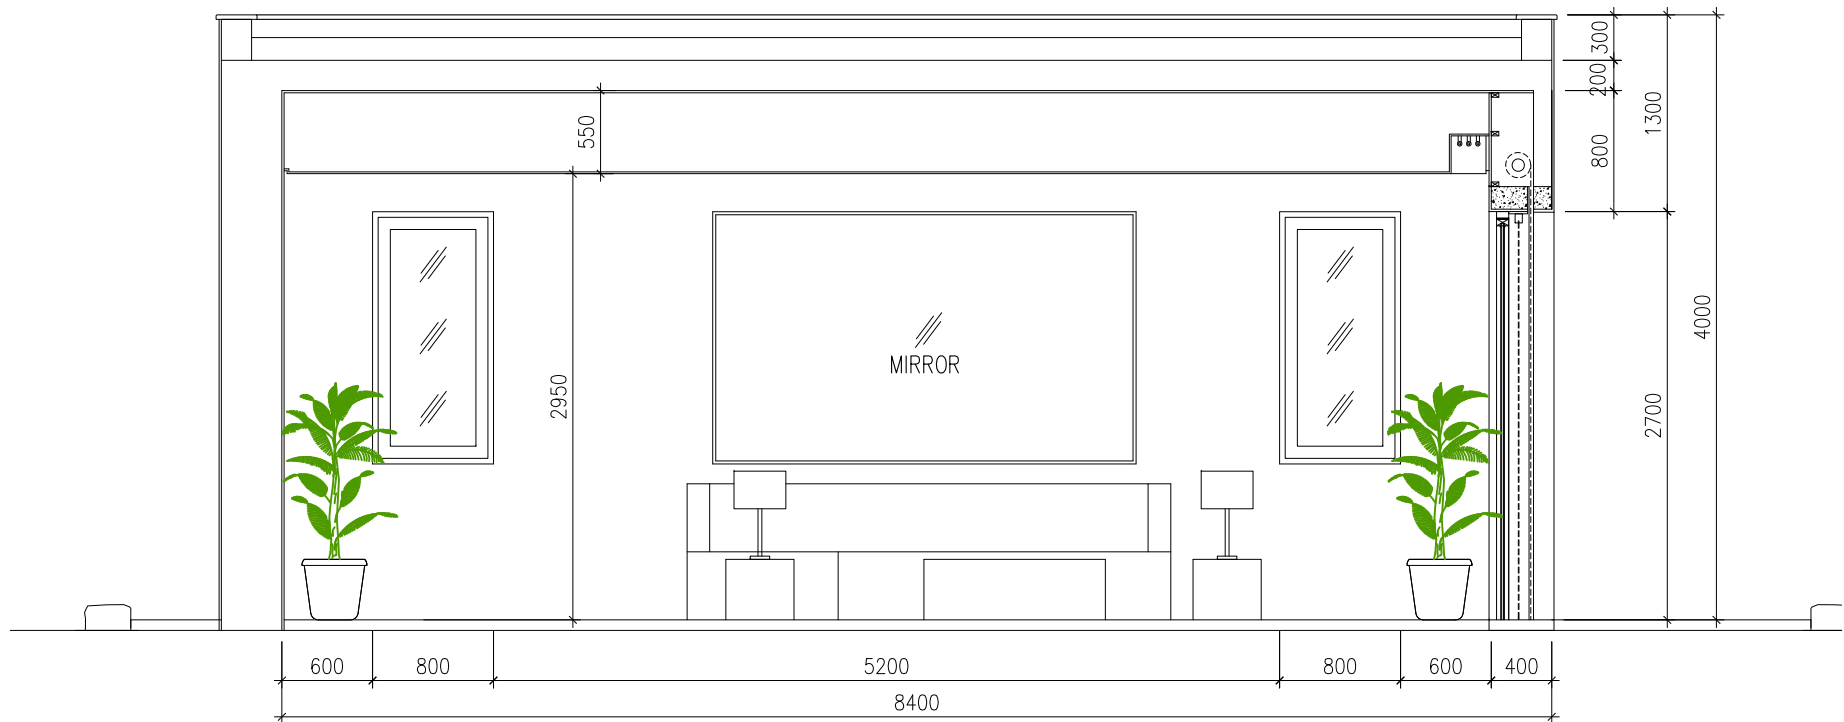

TYPICAL SECTION
SC.1:25

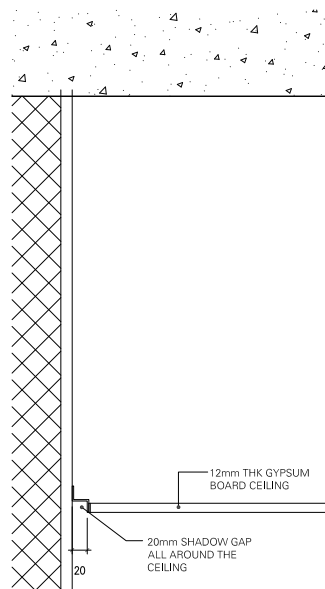

01 DETAIL-2
SC.1:5

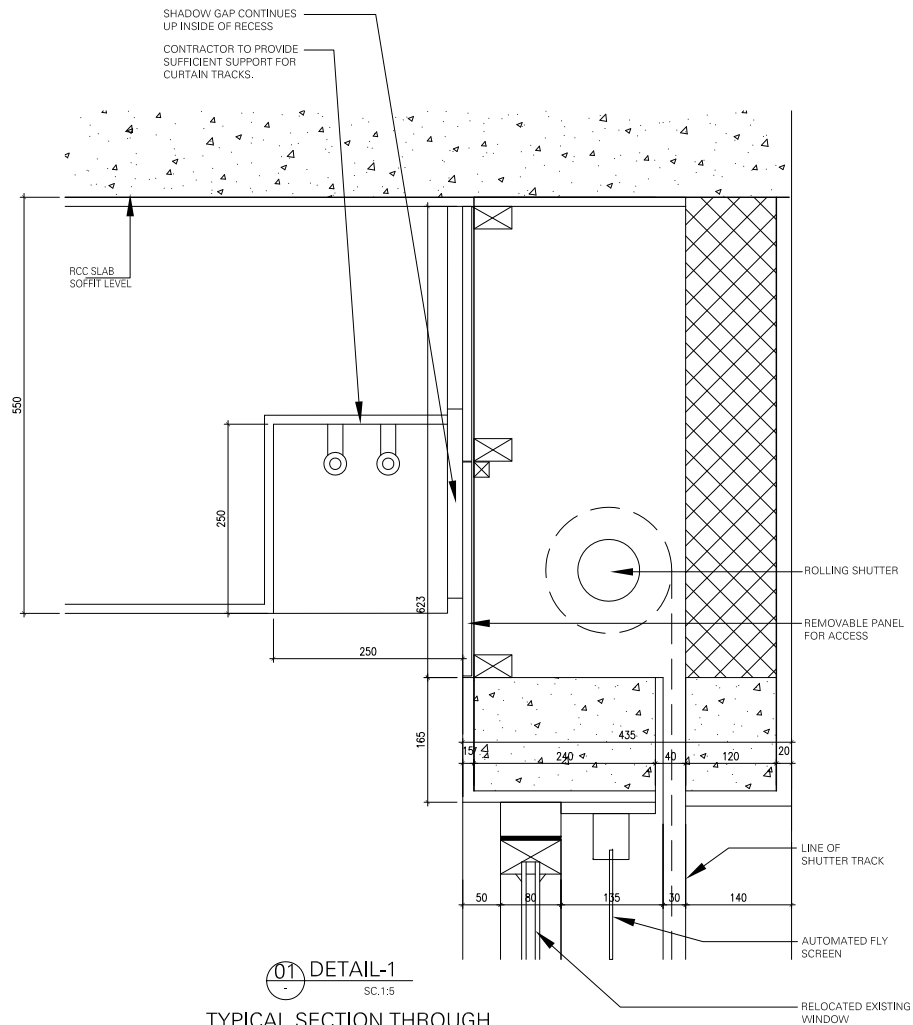

01 DETAIL-1
SC.1:5

**TYPICAL SECTION THROUGH
SHUTTER AND CURTAIN BOX**

GENERAL NOTES

1. This drawing shall be read in conjunction with all other relevant architectural, structural & electrical drawings including those of other consultants.
2. It is the responsibility of contractors & manufacturers to check all relevant site dimensions prior to the start of construction or manufacture.
3. All materials and components must be installed on site in accordance with manufacturer's instructions, shop drawings and standard details.
4. All dimensions are in millimeters unless noted otherwise.
5. Full working drawings, specifications and samples are to be provided by Contractor/Supplier for approval prior to manufacture.

KEY PLAN

REV.#	GENERAL NOTES	DRAWN BY	CHECKED BY	APPROVED BY	DATE
I	GENERAL REV.	MP	AM	SM	2024.02.27
H	GENERAL REV.	MP	AM	SM	2024.02.11
G	GEN REV.	AC	AM	SM	2024.02.04
F	GENERAL REV.	MP	AM	SM	2024.01.28
E	GENERAL REV.	MP	AM	SM	2024.01.23
D	GENERAL REV.	MP	AM	SM	2024.01.14
C	GENERAL REV.	MP	AM	SM	2023.12.17
B	GENERAL REV.	MP	AM	SM	2023.07.04
A	GENERAL REV.	MP	AM	SM	2023.06.25
X	INITIAL ISSUE	AC	AM	SM	2023.06.22

PROJECT TITLE	REFERENCE
SAF - RIYADH	SAF01 G

DRAWING TITLE

POOL BLDG EXTENSION
SECTION & DETAILS


DRAWING NUMBER	REVISION
SK-95-2	I

SCALE	FORMAT	ADDITIONAL NOTES	DESIGN DEVELOPMENT
1:50	A1		



**SIMA MALAK + ALSSAMOURE
DESIGN ASSOCIATES**
P.O. Box 15707 - Riyadh 11454 KSA
Tel. 01 441 4963 - Fax. 01 441 3867
simals@simals.com

©SIMA MALAK + ALSSAMOURE DESIGN ASSOCIATES (شركة) 2003
This document including all drawing and text is the property and
copyright of SIMA MALAK + ALSSAMOURE DESIGN ASSOCIATES for
use solely with respect to this Project and shall not be copied or
reproduced by any means except by agreement in writing from
SIMA MALAK + ALSSAMOURE DESIGN ASSOCIATES.

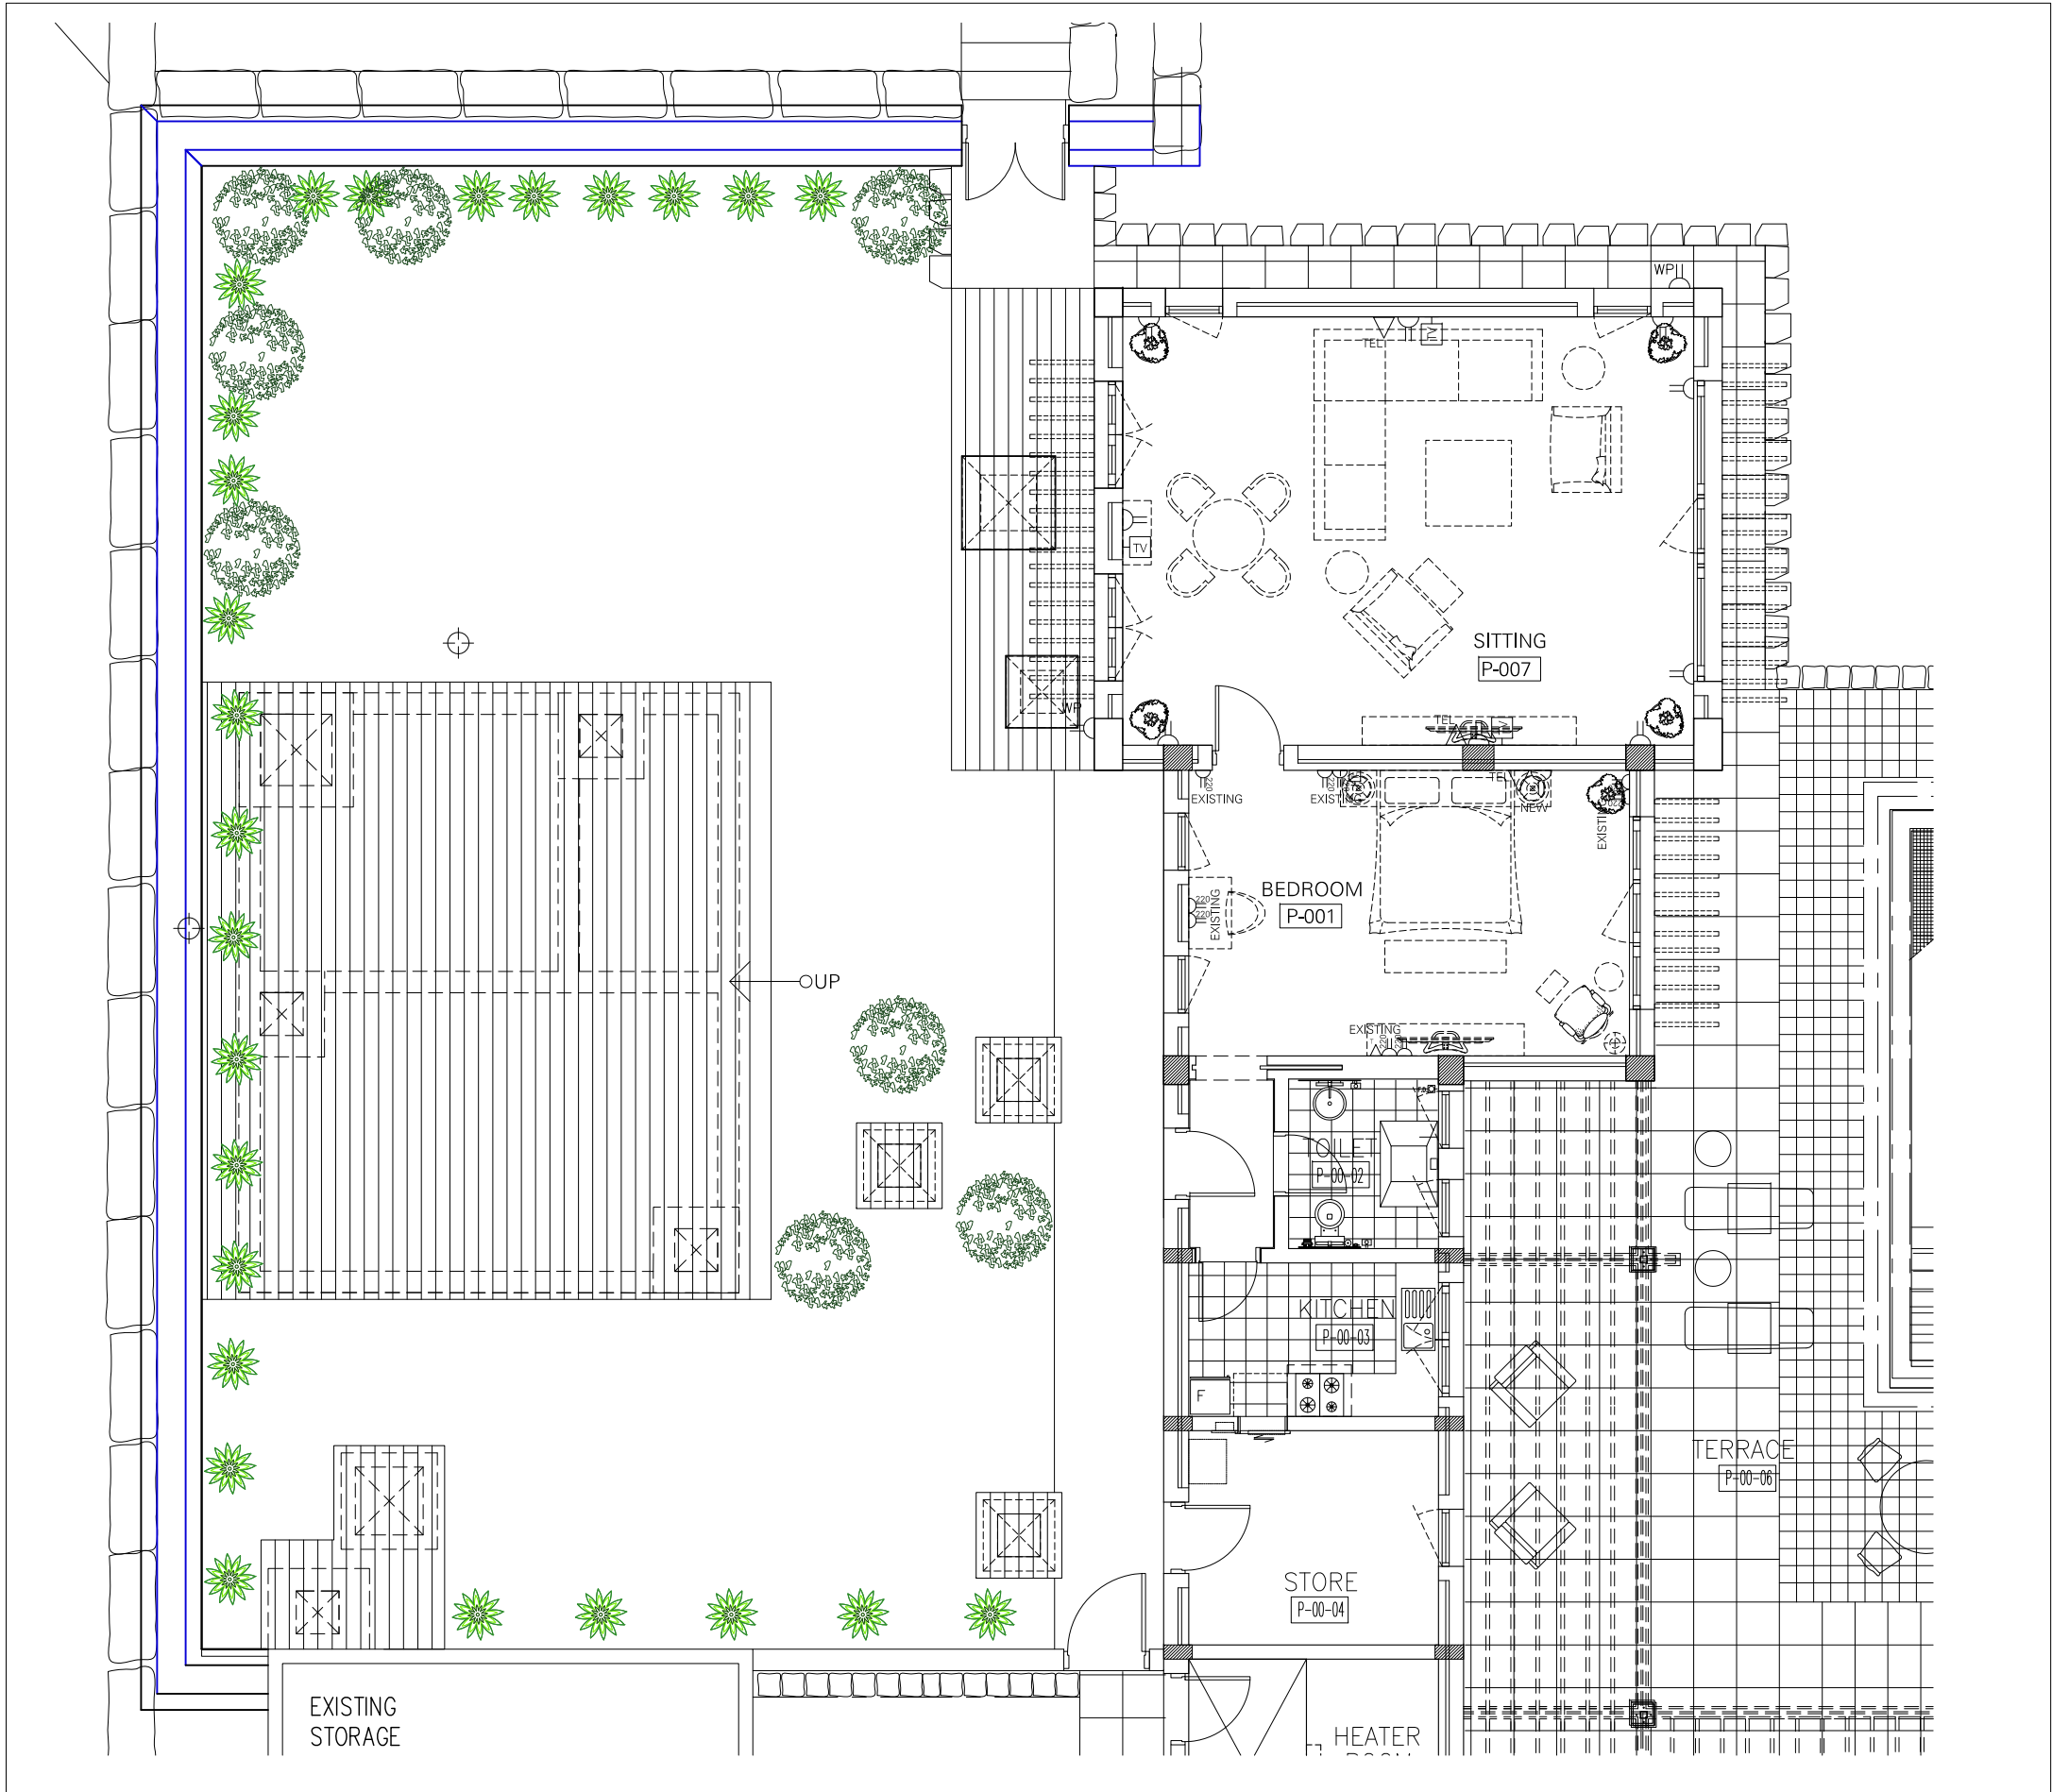

POWER + COMMUNICATION LAYOUT
SCALE 1:50

GENERAL NOTES

1. This drawing shall be read in conjunction with all other relevant architectural, structural & electrical drawings including those of other consultants.
2. It is the responsibility of contractors & manufacturers to check all relevant site dimensions prior to the start of construction or manufacture.
3. All materials and components must be installed on site in accordance with manufacturer's instructions, shop drawings and standard details.
4. All dimensions are in millimeters unless noted otherwise.
5. Full working drawings, specifications and samples are to be provided by Contractor/Supplier for approval prior to manufacture.

LEGEND :

- Double wall socket for satellite television system
- Wall socket power single
- Wall socket power single - Above Counter
- Wall socket power double
- Wall socket power in lighting circuit - single
- Wall socket power (Weather Proof)

KEY PLAN

F	GENERAL REV.	MP	AM	SM	2024.02.27
E	GENERAL REV.	MP	AM	SM	2024.01.17
D	GENERAL REV.	MP	AM	SM	2024.01.14
C	GEN. REV.	AC	AM	SM	2023.12.17
B	GEN. REV.	AC	AM	SM	2023.09.06
A	GENERAL REV.	AC	AM	SM	2023.05.23
X	INITIAL ISSUE	AC	AM	SM	2023.05.22
REV.#	GENERAL NOTES	DRAWN BY	CHECKED BY	APPROVED BY	DATE


PROJECT TITLE	REFERENCE
SAF - RIYADH	SAF01 G

DRAWING TITLE	REVISION
POOL BLDG EXTENSION LIGHTING AND POWER, COMM. LAYOUT	
DRAWING NUMBER	REVISION
SK-96-1	F

SCALE	FORMAT	ADDITIONAL NOTES	DESIGN DEVELOPMENT
1:50	A1		

SIMA MALAK + ALSSAMOURE
DESIGN ASSOCIATES
P.O. Box 15707 - Riyadh 11454 KSA
Tel. 01 441 4963 - Fax. 01 441 3867
simals@simals.com

©SIMA MALAK + ALSSAMOURE DESIGN ASSOCIATES (شركة) 2003
This document including all drawing and text is the property and
copyright of SIMA MALAK + ALSSAMOURE DESIGN ASSOCIATES for
use solely with respect to this Project and shall not be copied or
reproduced by any means except by agreement in writing from
SIMA MALAK + ALSSAMOURE DESIGN ASSOCIATES.

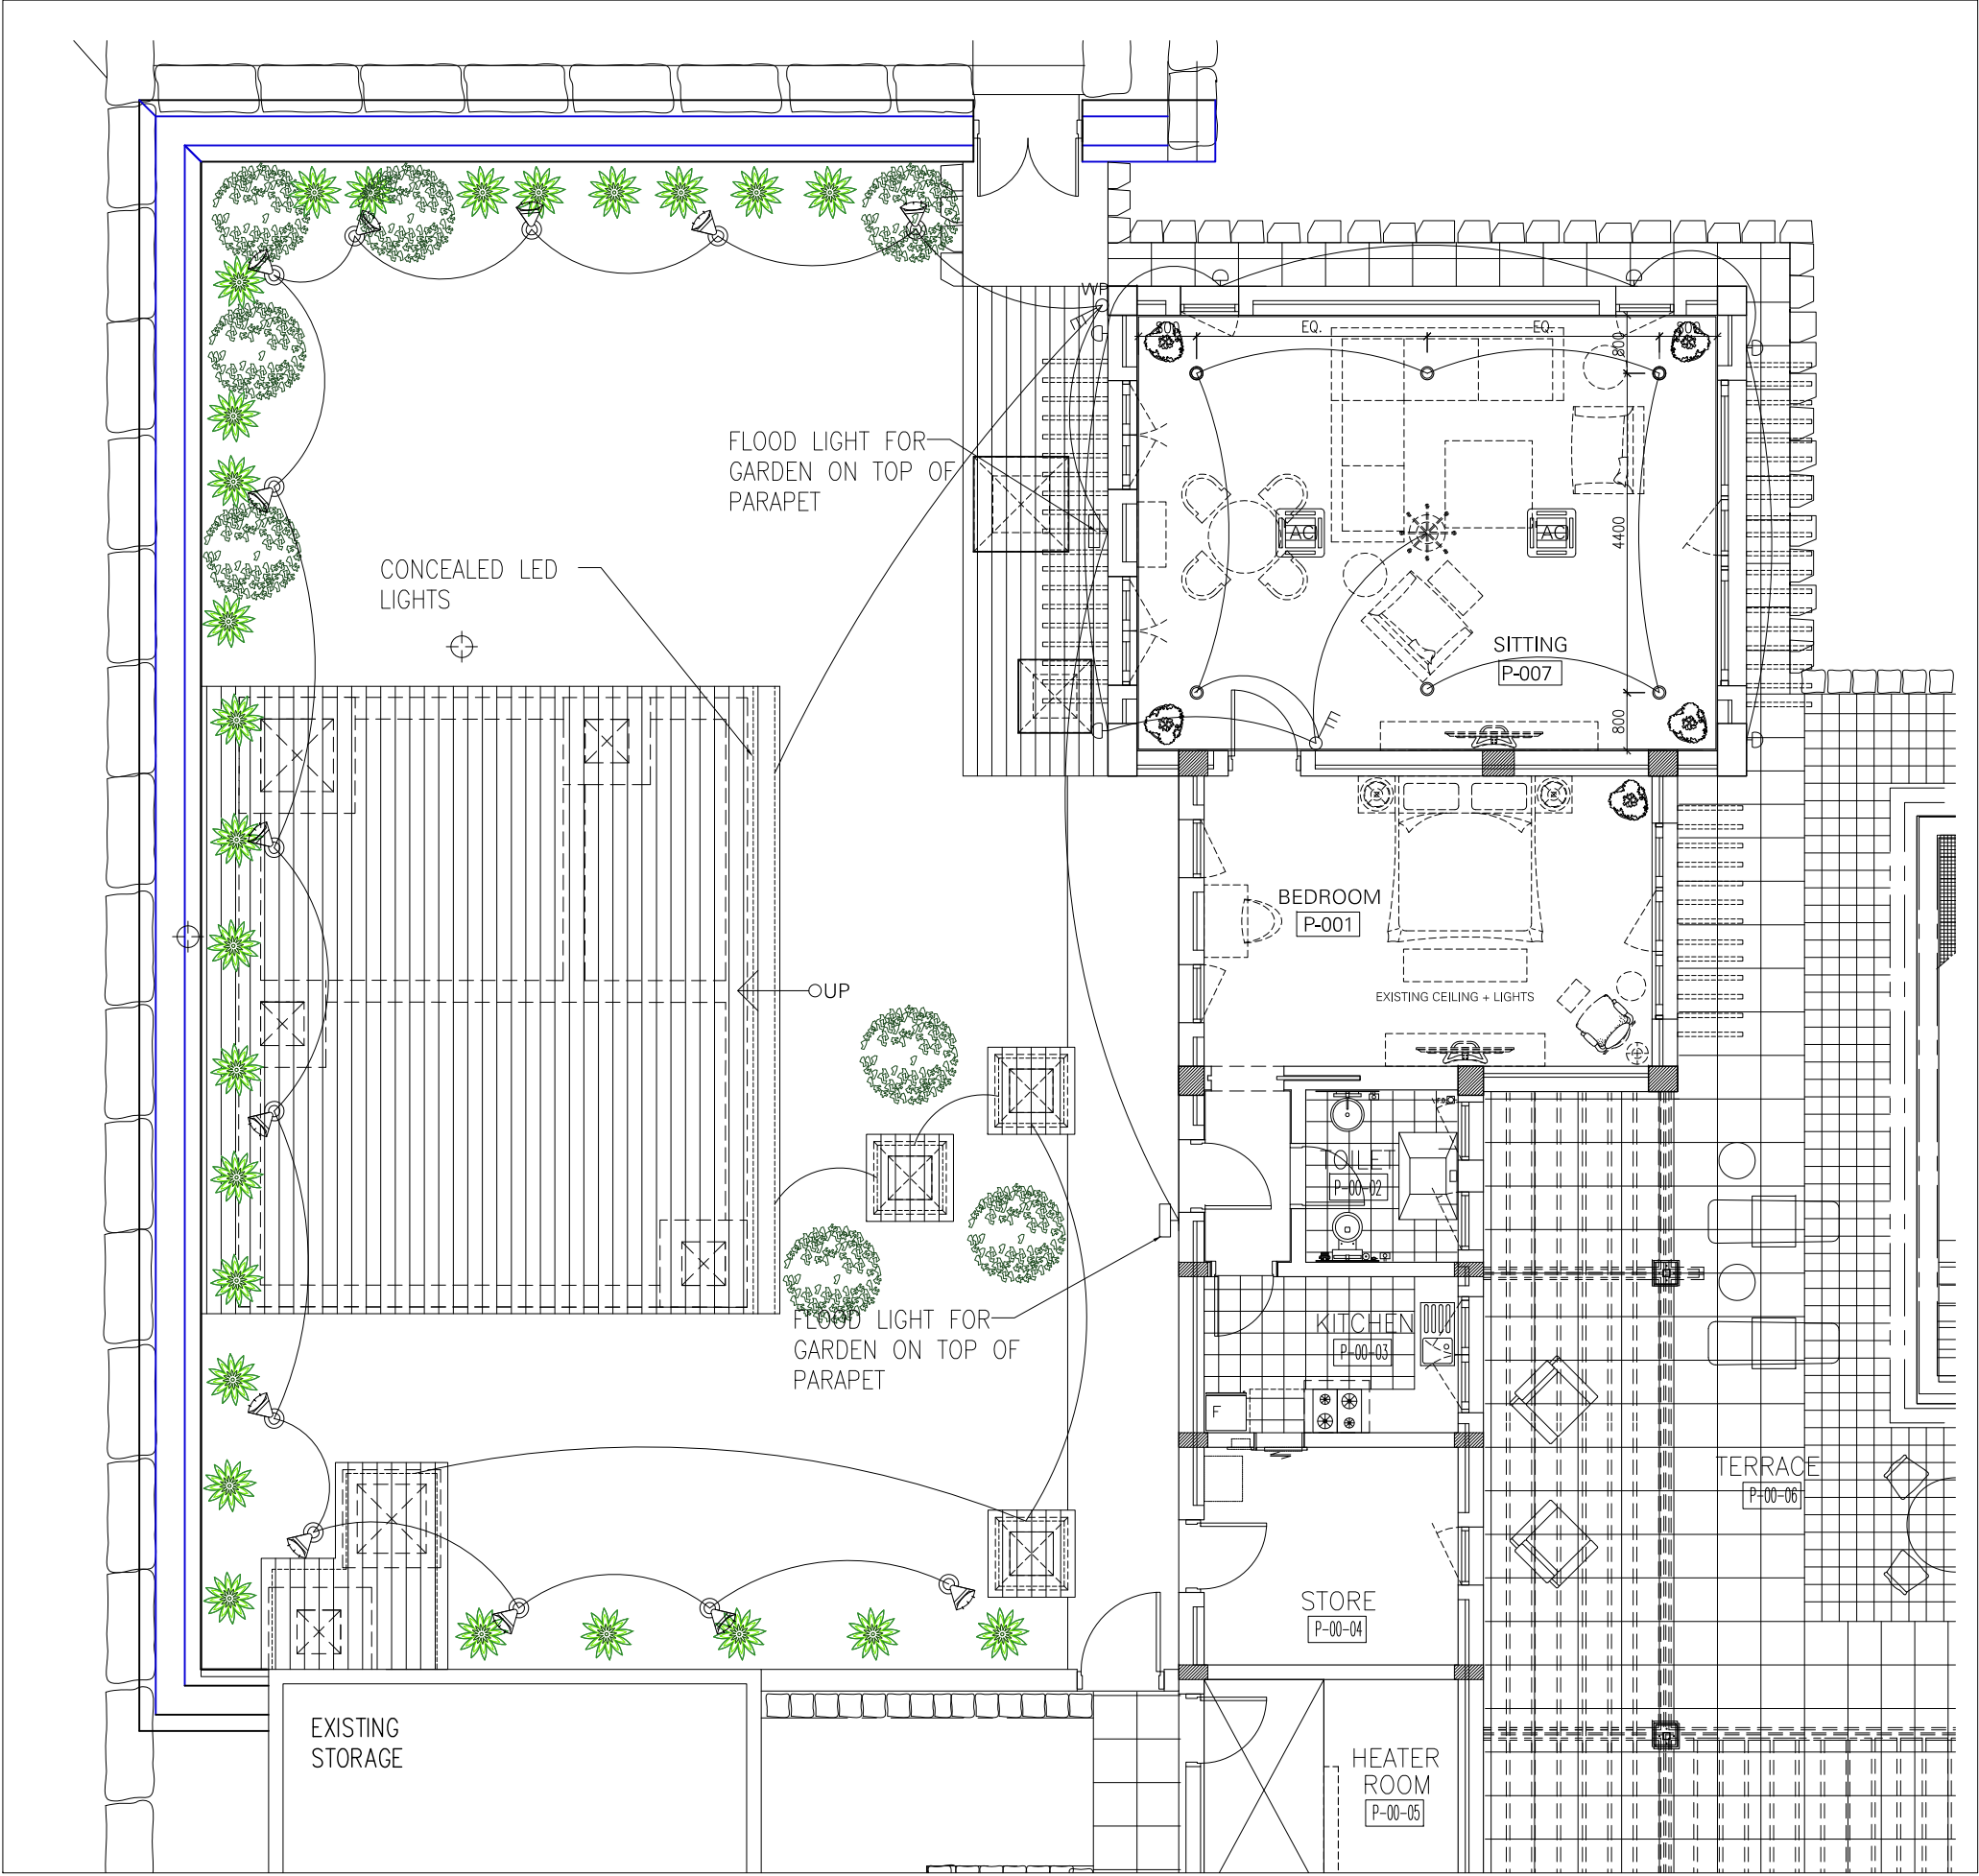

LIGHTING LAYOUT
SCALE 1:50

GENERAL NOTES

1. This drawing shall be read in conjunction with all other relevant architectural, structural & electrical drawings including those of other consultants.
2. It is the responsibility of contractors & manufacturers to check all relevant site dimensions prior to the start of construction or manufacture.
3. All materials and components must be installed on site in accordance with manufacturer's instructions, shop drawings and standard details.
4. All dimensions are in millimeters unless noted otherwise.
5. Full working drawings, specifications and samples are to be provided by Contractor/Supplier for approval prior to manufacture.

LEGEND :

- Recessed Downlight
- Recessed Downlight (Small)
- Square down light
- ⊕ External low wall light
- ↔ 2 Gang Switch
- ☼ WEATHER PROOF EXTERNAL DIRECTIONAL LARGE SPIKE LIGHT
- ⊗ CHANDELIER / PENDENT LIGHT
- ⌐ FLOOD LIGHT ON TOP OF PARAPET

KEY PLAN

F	GENERAL REV.	MP	AM	SM	2024.02.27
E	GENERAL REV.	MP	AM	SM	2024.01.17
D	GENERAL REV.	MP	AM	SM	2024.01.14
C	GEN. REV.	AC	AM	SM	2023.12.17
B	GEN. REV.	AC	AM	SM	2023.09.06
A	GENERAL REV.	AC	AM	SM	2023.06.23
X	INITIAL ISSUE	AC	AM	SM	2023.06.22
REV.#	GENERAL NOTES	DRAWN BY	CHECKED BY	APPROVED BY	DATE

PROJECT TITLE	REFERENCE
SAF - RIYADH	SAF01 G

DRAWING TITLE			
POOL BLDG EXTENSION LIGHTING AND POWER, COMM. LAYOUT			
DRAWING NUMBER			REVISION
SK-96-2			F
SCALE	FORMAT	ADDITIONAL NOTES	DESIGN DEVELOPMENT
1:50	A1		

**SIMA MALAK + ALSSAMOURE
DESIGN ASSOCIATES**
P.O. Box 15707 - Riyadh 11454 KSA
Tel. 01 441 4963 - Fax. 01 441 3867
simals@simals.com

©SIMA MALAK + ALSSAMOURE DESIGN ASSOCIATES () 2003
This document including all drawing and text is the property and
copyright of SIMA MALAK + ALSSAMOURE DESIGN ASSOCIATES for
use solely with respect to this Project and shall not be copied or
reproduced by any means except by agreement in writing from
SIMA MALAK + ALSSAMOURE DESIGN ASSOCIATES.