


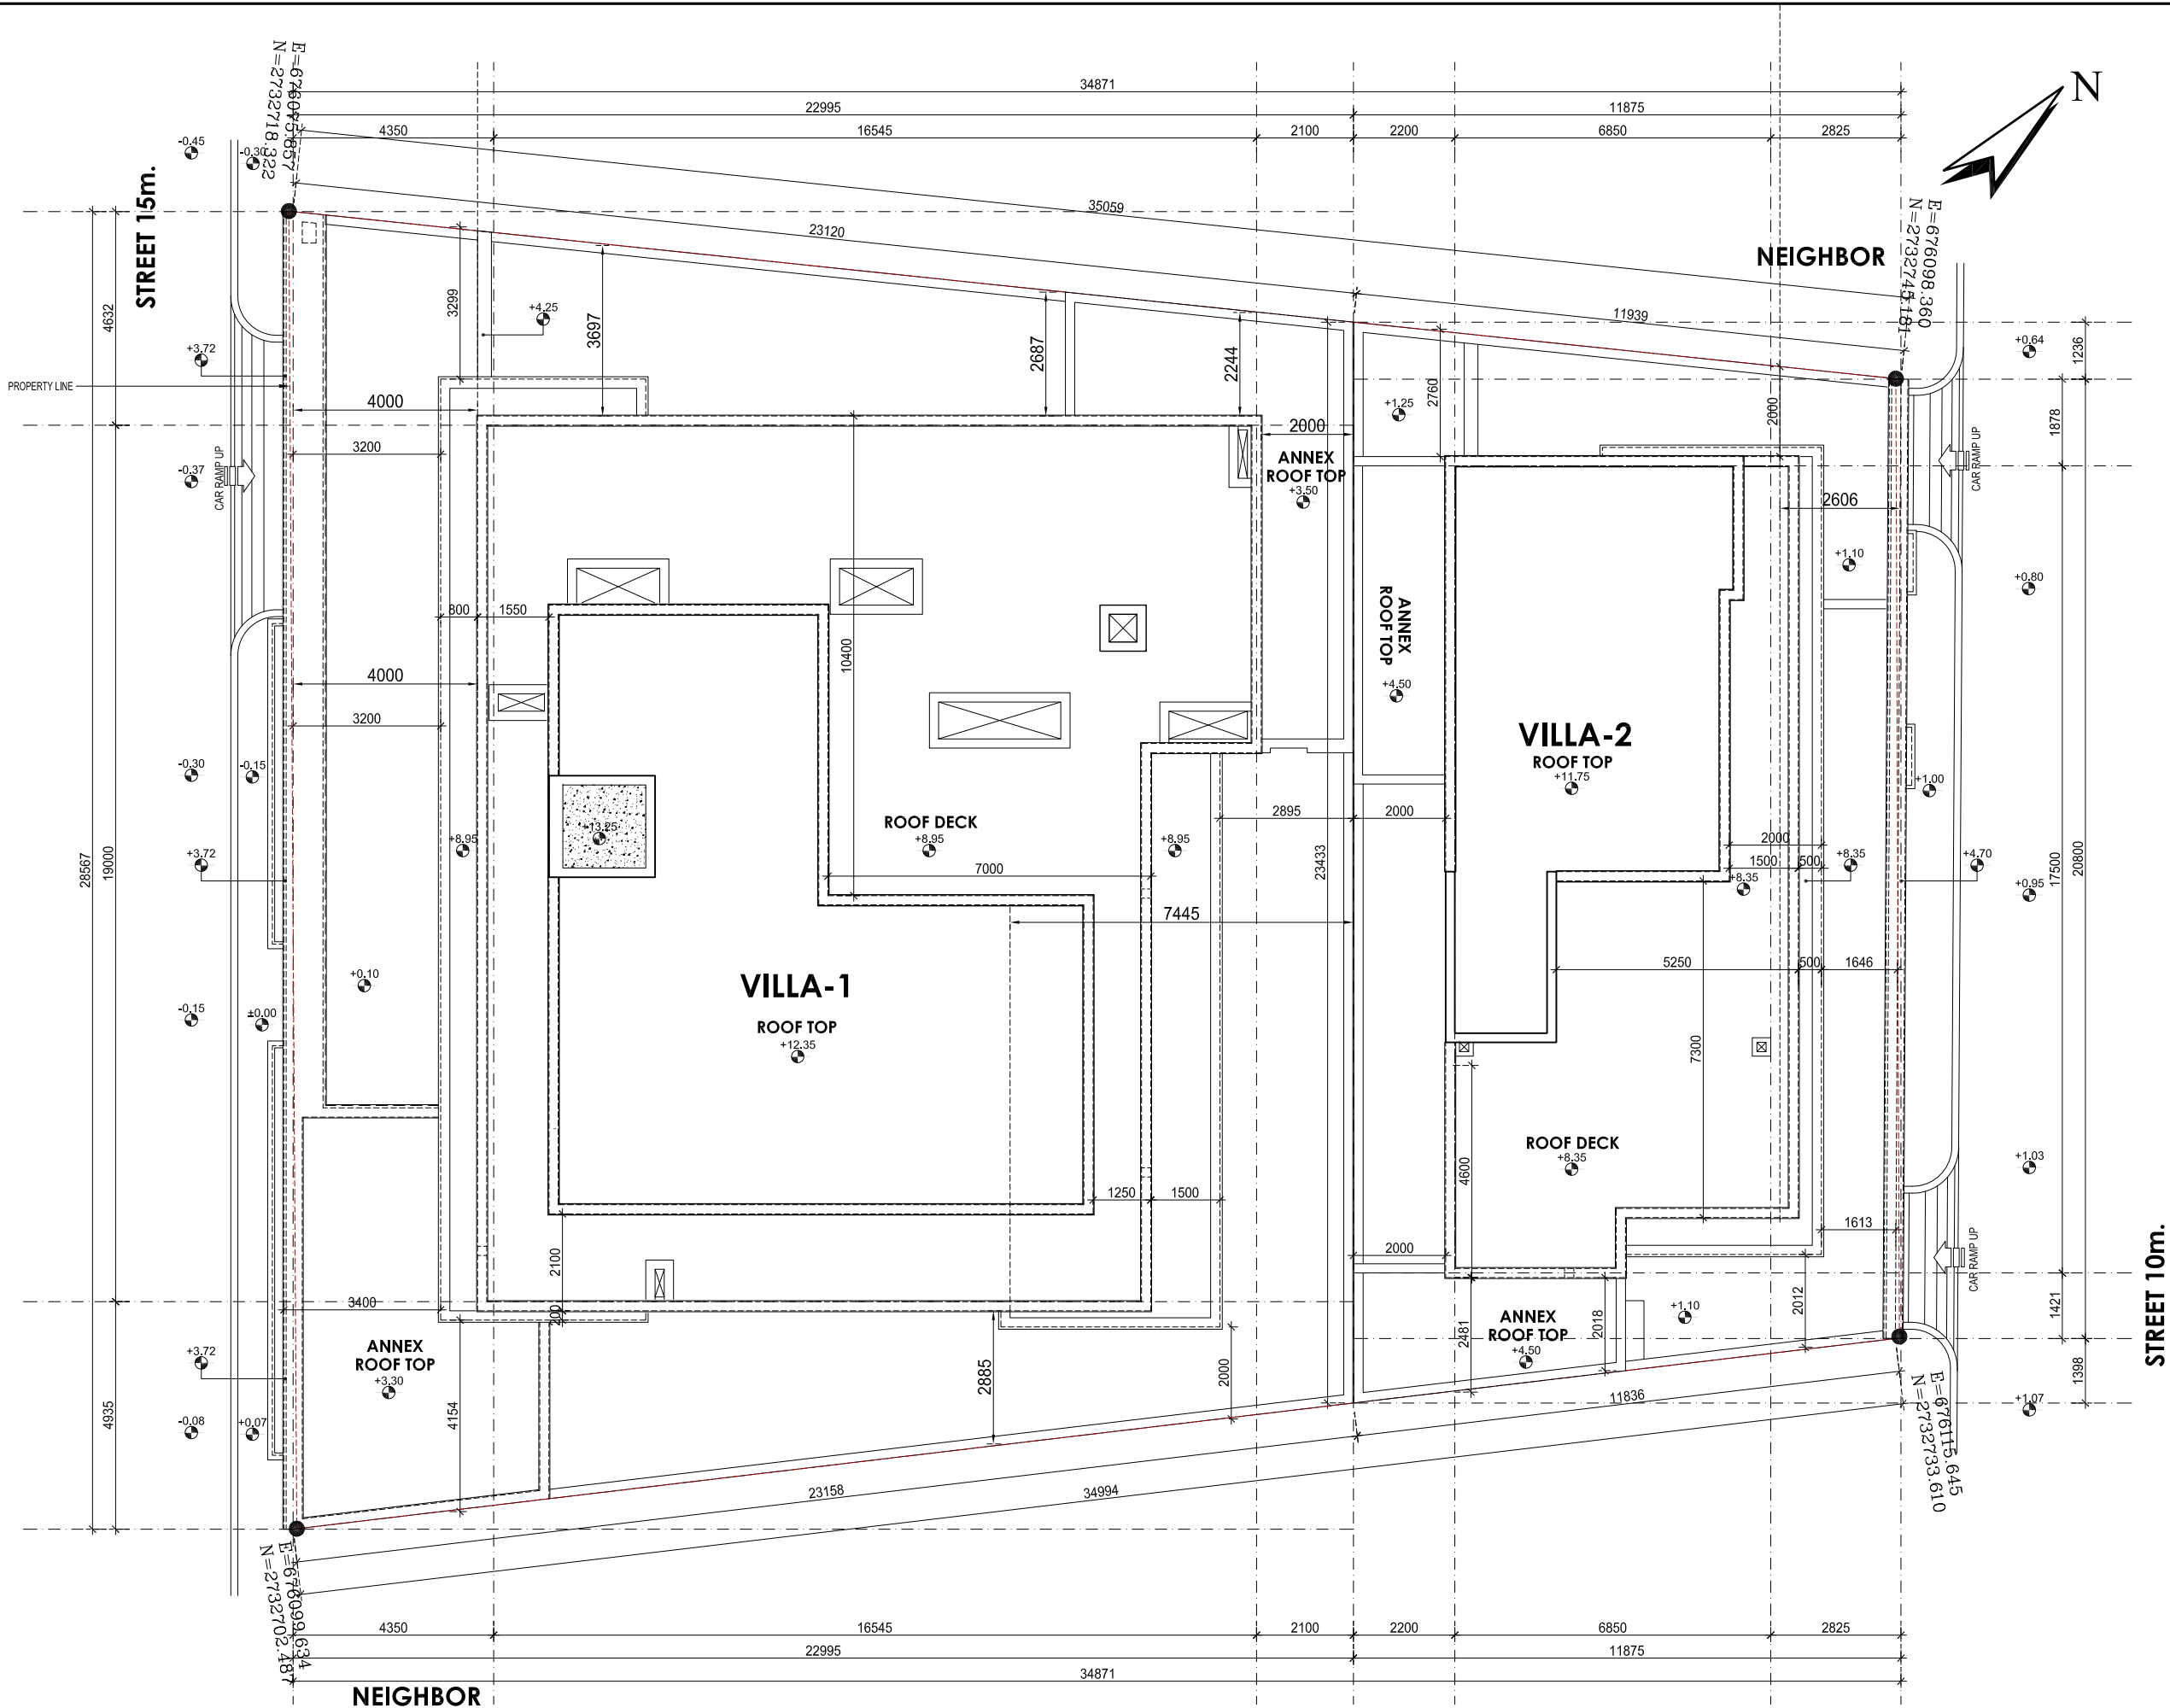

VILLA -1			مساحة الأرض
866.65 m ²			LAND AREA
PERCENTAGE %	AREA (m ²)	مساحة الأبنية	FLOOR AREA
30.71%	266.18	الأرض	GROUND FLOOR
36.68%	317.94	الاول	FIRST FLOOR
37.59%	119.53	سطح السطح	ROOF ANX
6.12%	53.11	ملاحق لربمة	ANNEXES
756.76			المجموع TOTAL

VILLA -2			مساحة الأرض
866.65 m ²			LAND AREA
PERCENTAGE %	AREA (m ²)	مساحة الأبنية	FLOOR AREA
15.10%	130.87	الأرض	GROUND FLOOR
15.65%	135.71	الاول	FIRST FLOOR
49.9%	67.73	سطح السطح	ROOF ANX
2.11%	18.30	ملاحق لربمة	ANNEXES
352.60			المجموع TOTAL

TOTAL VILLAS			مساحة الأرض
866.65 m ²			LAND AREA
PERCENTAGE %	AREA (m ²)	مساحة الأبنية	FLOOR AREA
45.81%	397.05	الأرض	GROUND FLOOR
52.34%	453.65	الاول	FIRST FLOOR
41.27%	187.26	سطح السطح	ROOF ANX
8.23%	71.41	ملاحق لربمة	ANNEXES
1,109.37			المجموع TOTAL

الضال	ممر مشاة عرض ١٠ م	٢,٦٠
NORTH		2.60
الشرق	قطعة رقم ١٣٩	٢,٠١
EAST		2.01
الغرب	قطعة رقم ١٤٢	٢,٢٠
WEST		2.30
الجنوب	شارع عرض ١٠ م	٤,٠٠
SOUTH		4.0

سماء سمیع الحق ملک	المالك
١٤١٠	القطعة
٨٥٦	المخطط
الربوة	الحي

SIMA MALAK + ALSSAMOURE
DESIGN ASSOCIATES

P.O. Box 15707 - Riyadh 11454 KSA
Tel. 01 441 4963 - Fax. 01 441 3867
simals@simals.com

المكتب الاستشاري الرئيسي

شركة المطورون العرب للاستشارات الهندسية

ترخيص رقم ٢٤٥٦-٥١١٠٠٠

الاعتماد	الدرجة	التخصص	المهندس
٢٧٥٩٦	مستشار	عمارة	محمد جليل اسماعيل
٣٧١٠	محترف	هندسة مدنية	غباري كايانيل
٣٠٣٧٨	رسم مخططات معمارية	اينس عماد جميل	كاتبان
٨٦٦١	تصميم كهربيا	اسامة طاهر سيد عرب	هندسة كهربيا
٧٥٣٣٢	تصميم ميكانيكا	اص على الفاضل	مسة ميكانيكا

2-01 DESIGN/STREET SIMA MALAK+ALSSAMOURE/RIYADH/2025/08/25-VILLA-1

PRIVATE VILLA
IN RIYADH, KSA

OWNER NAME

SIMA MALAK

SITE DEVELOPMENT
LAYOUT PLAN

PROJ. NO. P-2024-07

DWG. NO. AR-01

DATE. jun2024

SCALE: 1:100

1 DESIGN CONCEPT


2 PRELIM. DESIGN

3 DESIGN DEVELOP.

4 WORKING DWG.

5 SHOP DRAWING

6 AS BUILT DWG.

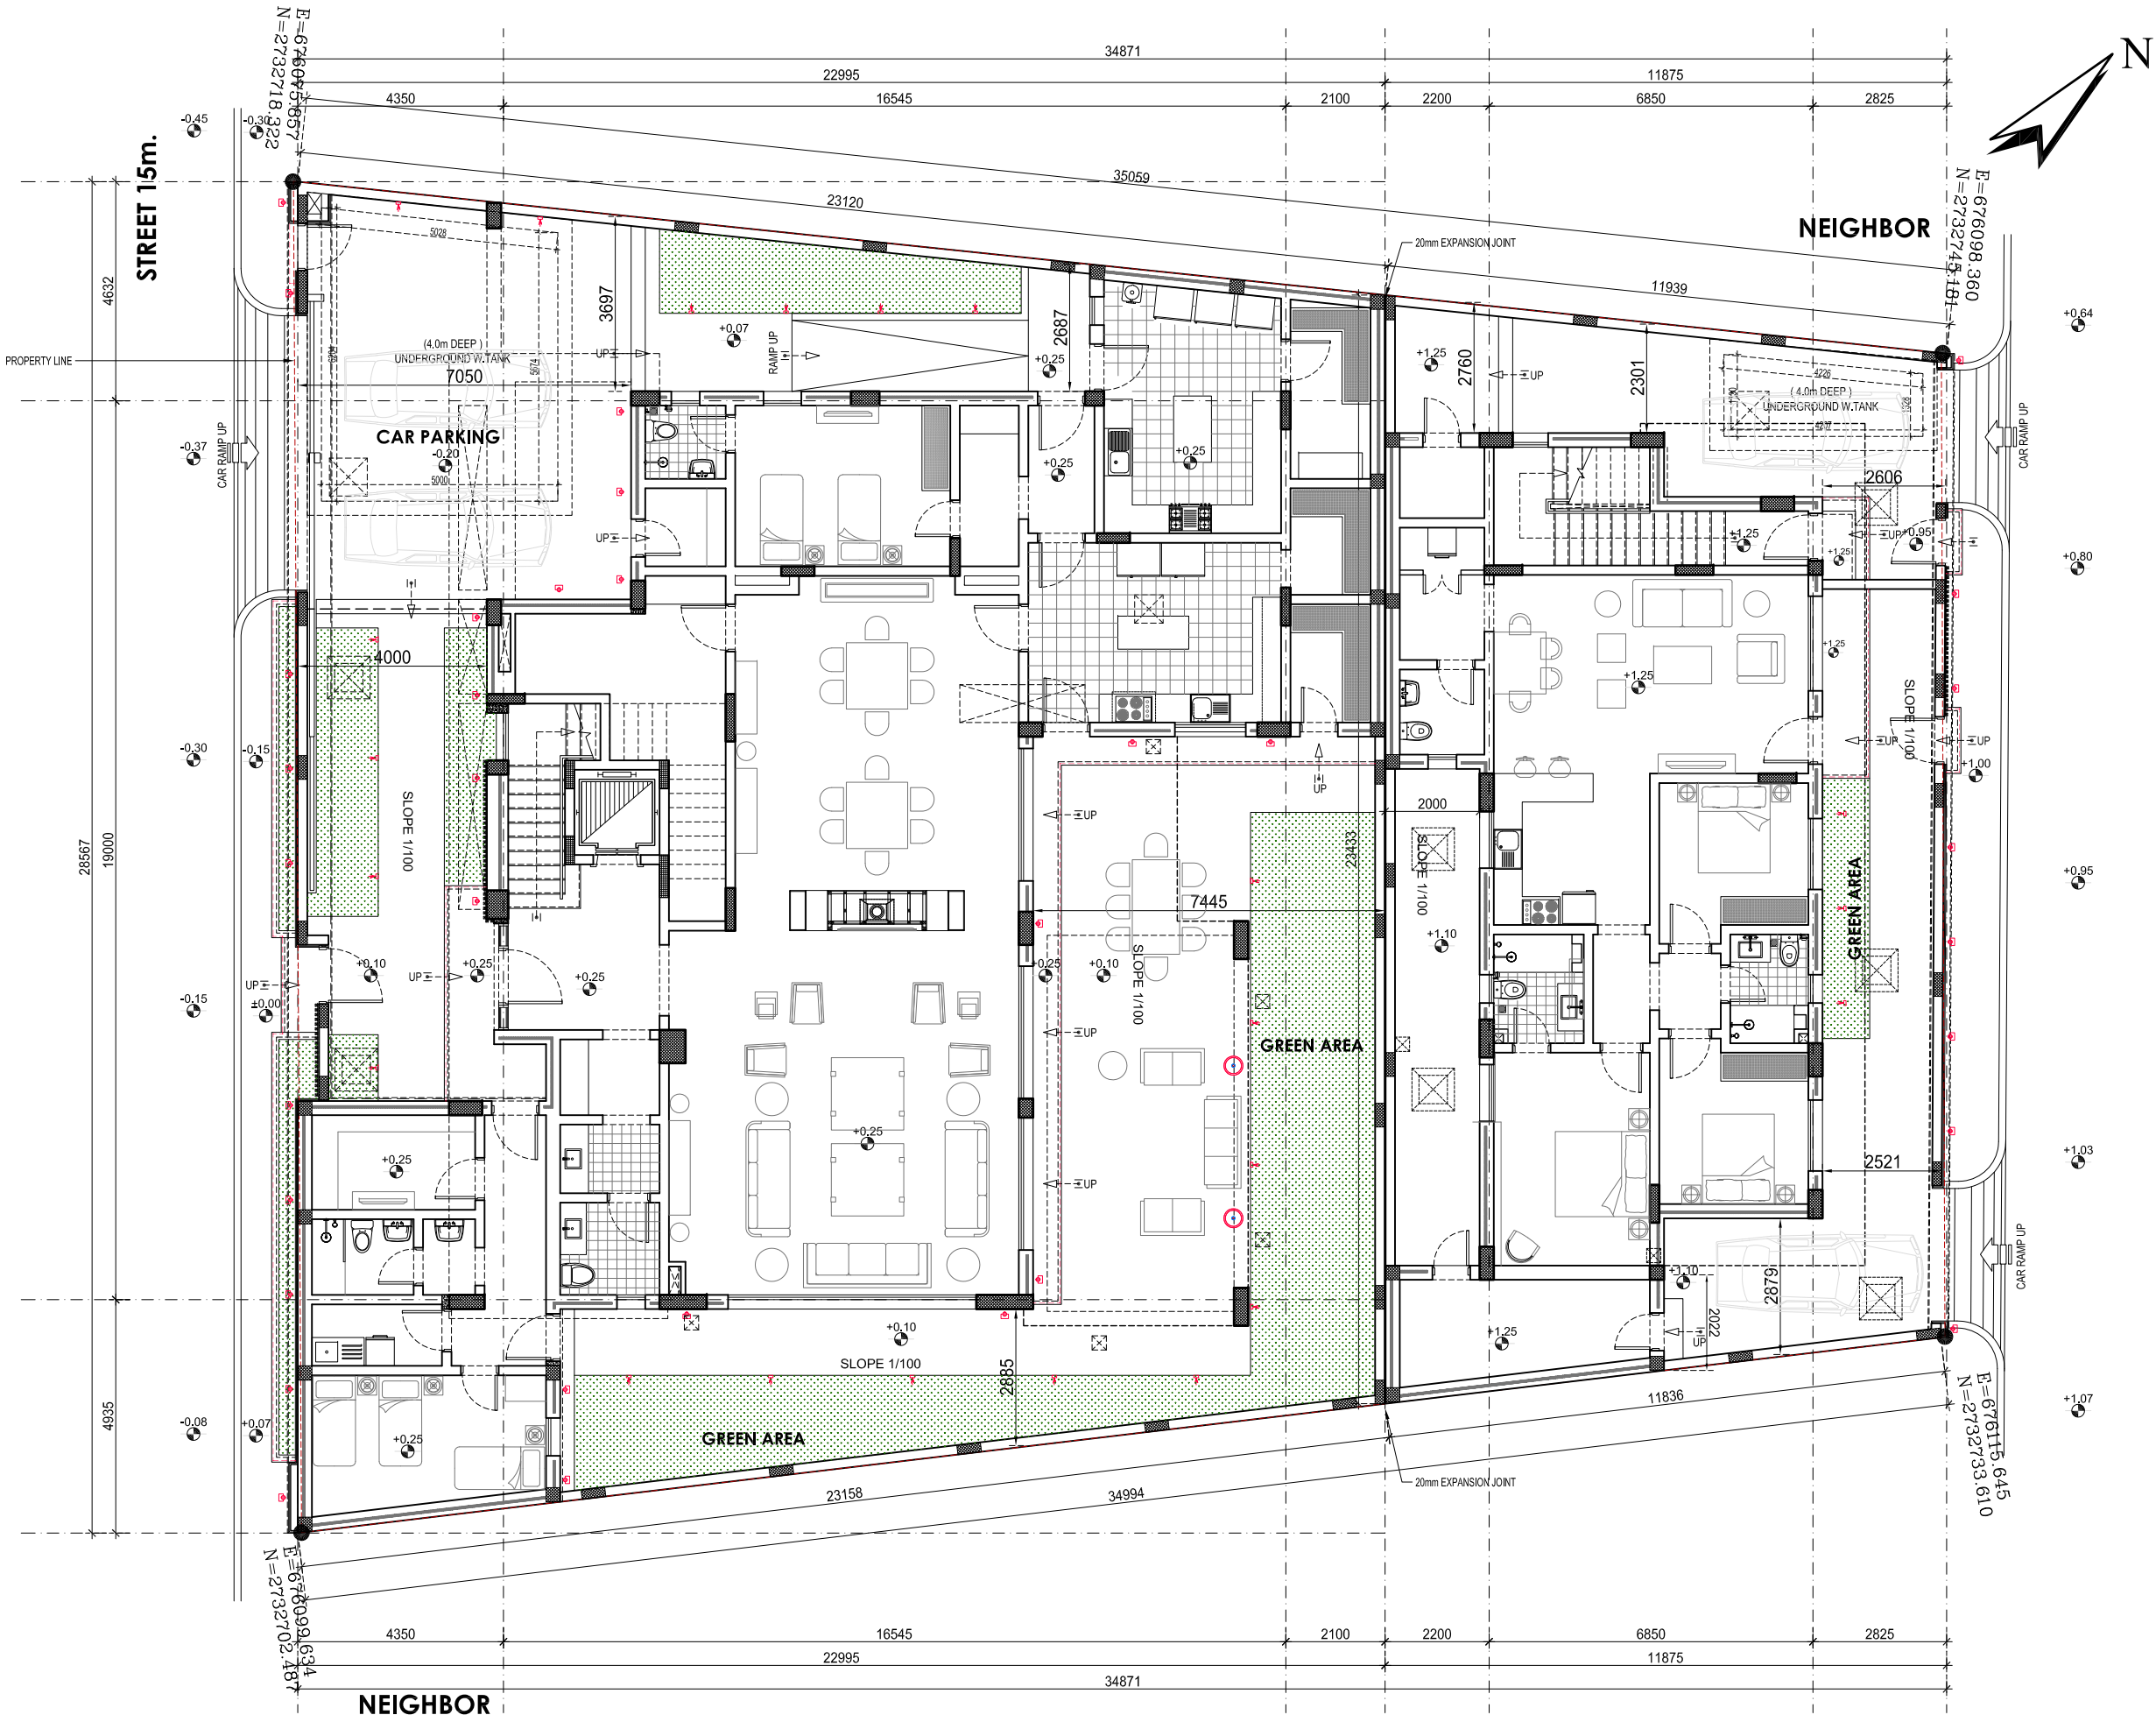

VILLA - 1		مساحة الأرض
866.65 m ²		LAND AREA
PERCENTAGE	AREA (m ²)	مساحة الأرض
30.71%	266.18	FLOOR AREA
36.68%	317.94	GROUND FLOOR
37.59%	119.53	FIRST FLOOR
6.12%	53.11	ROOF ANX
		ANNEXES
	756.76	TOTAL

VILLA - 2		مساحة الأرض
866.65 m ²		LAND AREA
PERCENTAGE	AREA (m ²)	مساحة الأرض
15.10%	130.87	FLOOR AREA
15.65%	135.71	GROUND FLOOR
49.9%	67.73	FIRST FLOOR
2.11%	18.30	ROOF ANX
		ANNEXES
	352.60	TOTAL

TOTAL VILLAS		مساحة الأرض
866.65 m ²		LAND AREA
PERCENTAGE	AREA (m ²)	مساحة الأرض
45.81%	397.05	FLOOR AREA
52.34%	453.65	GROUND FLOOR
41.27%	187.26	FIRST FLOOR
8.23%	71.41	ROOF ANX
		ANNEXES
	1,109.37	TOTAL

الضلع	المساحة	الاتجاه
2.60	2.60	شمال
2.01	2.01	شرق
2.30	2.30	غرب
4.0	4.0	جنوب

المالك	سيماه سميع الحق ملك
القطعة	١٤١ و ١٤٢
المخطط	٨٥٦
الحى	الريوة

SIMA MALAK + ALSSAMOURÉ
DESIGN ASSOCIATES
P.O. Box 15707 - Riyadh 11454 KSA
Tel. 01 441 4963 - Fax. 01 441 3867
simas@simas.com

المكتب الاستشاري الرئيسي
شركة المطورون العرب للاستشارات الهندسية
ترخيص رقم ٠١١-٢٤٥٦

التخصص	الدرجة	الاعتماد
تصميم معماري و تنفيذ	مهندس	٢٧٥٩٦
تصميم انشائي	مهندس	٣٧١٠
رسم مخططات معمارية	مهندس	٣٠٣٧٨
تصميم كهربائي	مهندس	٨١٣١
تصميم ميكانيكا	مهندس	٧٤٣٣

PRIVATE VILLA
IN RIYADH, KSA

OWNER NAME	1	DESIGN CONCEPT
SIMA MALAK	2	PRELIM. DESIGN
	3	DESIGN DEVELOP.
	4	WORKING DWG.
GENERAL SITE LAYOUT PLAN	5	SHOP DRAWING
	6	AS BUILT DWG.

PROJ. NO.	DWG. NO.	DATE	SCALE:
P-2024-07	AR-02	jun2024	1:100



GENERAL NOTES

- ALL LEVELS ARE SHOWN IN METERS AND RELATED TO DATUM LEVEL OF +0.00. (STREET LEVEL) IS EQUAL TO (RXX.X) OF CORRESPONDING LEVEL ON TOPOGRAPHICAL SURVEY DRAWING. DIMENSIONS ARE SHOWN IN MILLIMETERS.
- ALL INTERNAL PARTITIONS ARE 200mm THICK AND ALL EXTERNAL WALLS ARE 300mm THICK UNLESS OTHERWISE SPECIFIED.
- DETAIL DRAWINGS SHOWN IN CIRCLES IN THIS DRAWING SHALL BE REFERRED TO FOR MORE INFORMATION PERTAINING TO THE ENCIRCLED AREAS.
- WALL DIMENSIONS DO NOT INCLUDE RENDER, PLASTER FINISHES OR PRE-CAST CONCRETE PLINTH UNLESS OTHERWISE INDICATED.
- DOORS AND ARCHES ARE SET OUT:
A. ON THE CENTER OF THE WALL OR
B. FROM A 200mm NIB OR
C. AS DIMENSIONED
- ALL INTERNAL WALLS SHALL BE TAKEN TO THE UNDERSIDE OF THE SOFFIT OR BEAM UNLESS OTHERWISE INDICATED.
- ALL FALLS TO ROOFS, TERRACES INCLUDING THE FALL ON THE MAIN ENTRANCE WALKWAY SHALL BE 0.50% MINIMUM.
- ALL CHANGES IN DIRECTION OF PLASTER AND RENDER SHALL BE FORMED BY THE APPROPRIATE GALVANIZED METAL BEAD.
- LEVELS OF EXTERNAL FLOOR FINISHES ARE SHOWN AS NOMINAL. FINISHES ADJACENT TO BUILDING SHALL BE LAID TO FALL AWAY FROM THE BUILDING.
- ALL SHOP DRAWINGS, SAMPLES OR CATALOG CUTS TO BE APPROVED BY THE ARCHITECT BEFORE THE FINAL EXECUTION.
- THE CONTRACTOR SHALL SUBMIT SAMPLES & SHOP DRAWINGS FOR ALL EXTERIOR CLADDING FINISHES PRIOR TO ANY INSTALLATIONS.

SYMBOL & LEGEND

	300mm THK EXTERNAL CONCRETE BLOCK WALL (INSULATED)
	200mm THK INTERNAL CONCRETE BLOCK WALL
	100mm THK INTERNAL CONCRETE BLOCK WALL
	LOW HEIGHT PARTITION WALL
	REINFORCED CONCRETE
	SAND, SCREED
	PLASTER OR RENDER
	PAINTED
	LEVEL ON PLAN
	LEVEL ON SECTIONS AND ELEVATIONS
	UP LIGHT
	FLOOR LIGHT
	OUTDOOR FLOOR LAMP
	STRIP LIGHT @ ROOF, STEP, PLANTER BOX ETC.
	LEVEL INDICATION
	ROOM NUMBERING
	BUILDING NUMBER
	DOOR TYPE
	WINDOW TYPE
	EXTERNAL FINISHING
	STRUCTURAL COLUMN
	OPENING ABOVE


SIMA MALAK + ALSSAMOURÉ
DESIGN ASSOCIATES
P.O. Box 15707 - Riyadh 11454 KSA
Tel. 01 441 4963 - Fax. 01 441 3867
simas@simas.com

المكتب الاستشاري الرئيسي
شركة المطورون العرب للاستشارات الهندسية
ترخيص رقم ٠١١٠٠٠٢٤٥٦

الاعتماد	الدرجة	التخصص	المهندس	تصميم معماري و تخطيط
٢٧٩٩٦	مستشار	عمارة	محمد جميل اساميل	
٣٧١٠	محترف	هندسة مدنية	غيداردو كايانيليا كايانيلان	تصميم انشائي
٣٠٣٧٨	رسم مخططات معمارية	هندسة معمارية	ابن عماد جميل	رسم مخططات معمارية
٨٦٦١	مستشار	هندسة كهربائية	اسامة طاهر سيد عرب هندسة كهربائية	تصميم كهربائي
٧٤٣٣٢	محترف	هندسة ميكانيكية	احسان علي الفاضل	تصميم ميكانيكا

PRIVATE VILLA
IN RIYADH, KSA

OWNER NAME		1 DESIGN CONCEPT	
SIMA MALAK		2 PRELIM. DESIGN	
		3 DESIGN DEVELOPMENT	
		4 WORKING DRAWING	
(VILLA-1) GROUND FLOOR LAYOUT PLAN		DRAWING TITLE	
		5 SHOP DRAWING	
		6 AS BUILT DRAWING	
PROJ. NO. 2024-07	DWG. NO. AR-03	DATE jun2024	SCALE: 1:100

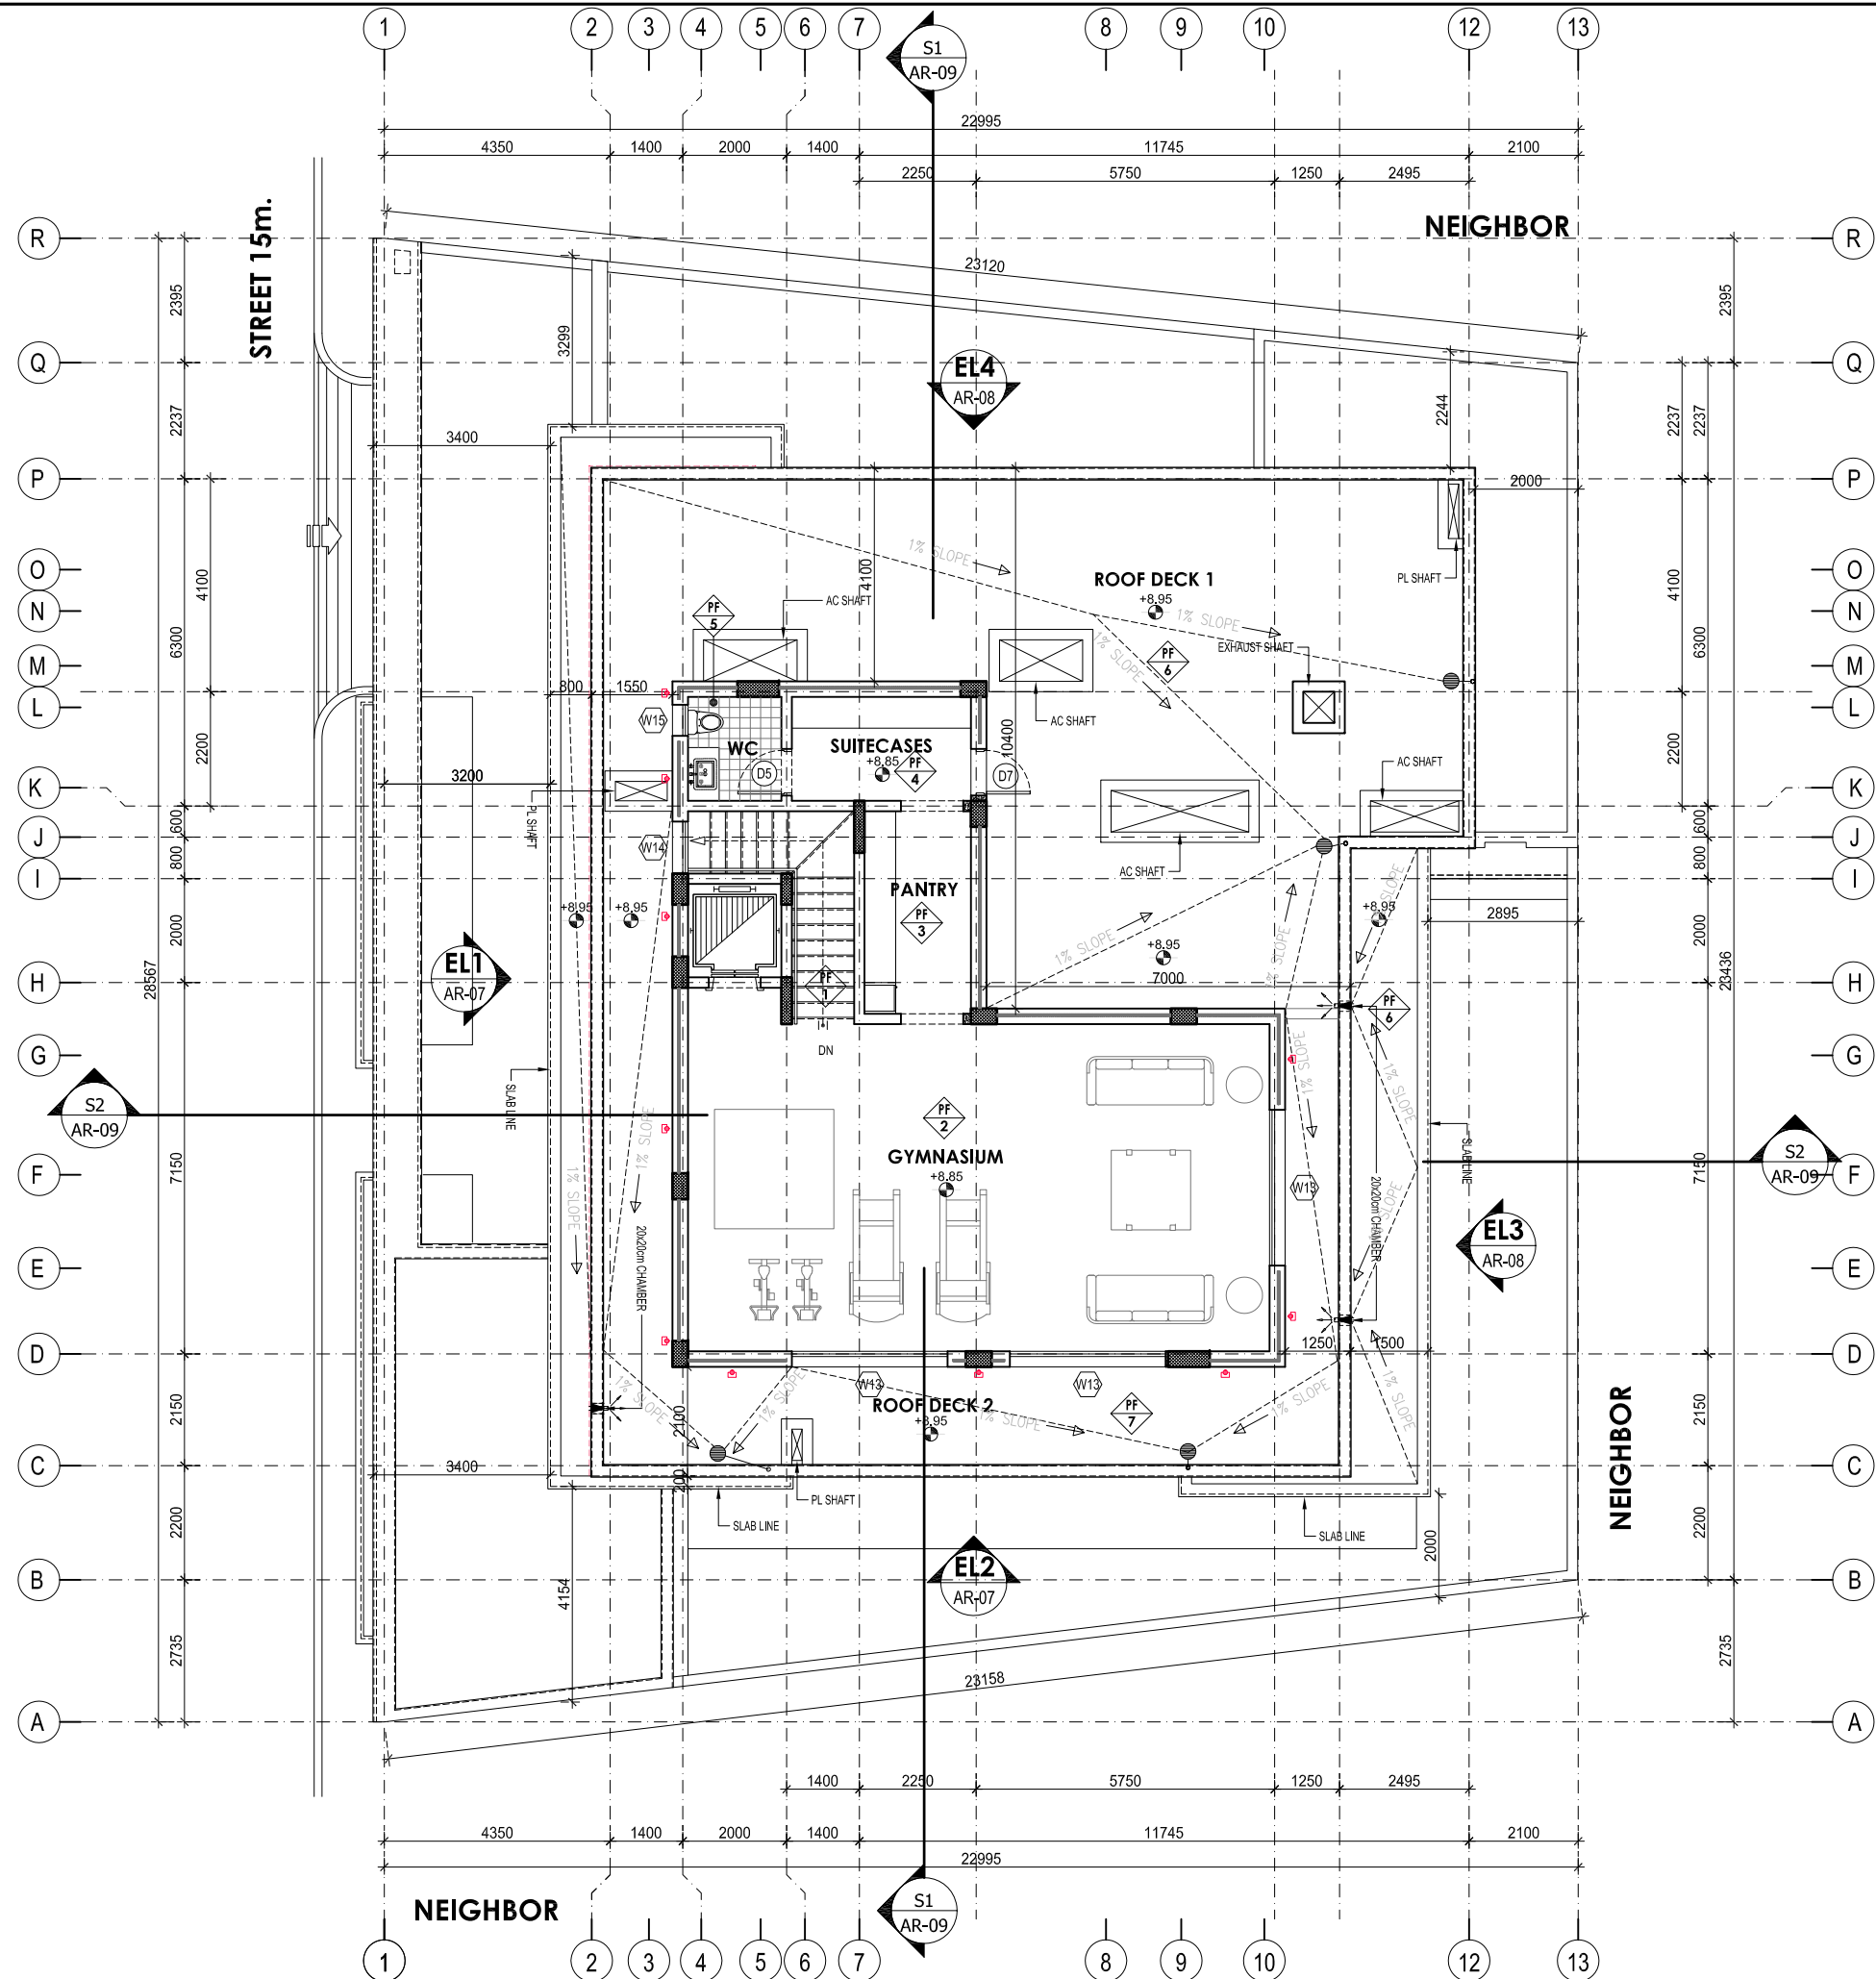

GENERAL NOTES

- ALL LEVELS ARE SHOWN IN METERS AND RELATED TO DATUM LEVEL OF +0.00 (STREET LEVEL) IS EQUAL TO (R.S.S.) OF CORRESPONDING LEVEL ON TOPOGRAPHICAL SURVEY DRAWING. DIMENSIONS ARE SHOWN IN MILLIMETERS.
- ALL INTERNAL PARTITIONS ARE 200mm THICK AND ALL EXTERNAL WALLS ARE 300mm THICK UNLESS OTHERWISE SPECIFIED.
- DETAIL DRAWINGS SHOWN IN CIRCLES IN THIS DRAWING SHALL BE REFERRED TO FOR MORE INFORMATION PERTAINING TO THE ENCIRCLED AREAS.
- WALL DIMENSIONS DO NOT INCLUDE RENDER, PLASTER FINISHES OR PRE-CAST CONCRETE PLINTH UNLESS OTHERWISE INDICATED.
- DOORS AND ARCHES ARE SET OUT:
A. ON THE CENTER OF THE WALL OR
B. FROM A 200mm NIB OR
C. AS DIMENSIONED
- ALL INTERNAL WALLS SHALL BE TAKEN TO THE UNDERSIDE OF THE SOFFIT OR BEAM UNLESS OTHERWISE INDICATED.
- ALL FALLS TO ROOFS, TERRACES INCLUDING THE FALL ON THE MAIN ENTRANCE WALKWAY SHALL BE 0.50% MINIMUM.
- ALL CHANGES IN DIRECTION OF PLASTER AND RENDER SHALL BE FORMED BY THE APPROPRIATE GALVANIZED METAL BEAD.
- LEVELS OF EXTERNAL FLOOR FINISHES ARE SHOWN AS NOMINAL. FINISHES ADJACENT TO BUILDING SHALL BE LAID TO FALL AWAY FROM THE BUILDING.
- ALL SHOP DRAWINGS, SAMPLES OR CATALOG CUTS TO BE APPROVED BY THE ARCHITECT BEFORE THE FINAL EXECUTION.
- THE CONTRACTOR SHALL SUBMIT SAMPLES & SHOP DRAWINGS FOR ALL EXTERIOR CLADDING FINISHES PRIOR TO ANY INSTALLATIONS.

SYMBOL & LEGEND

300mm THK EXTERNAL CONCRETE BLOCK WALL (INSULATED)	LEVEL INDICATION B1- BASEMENT FLOOR G1- GROUND FLOOR F1- FIRST FLOOR
200mm THK INTERNAL CONCRETE BLOCK WALL	ROOM NUMBERING BUILDING NUMBER
100mm THK INTERNAL CONCRETE BLOCK WALL	DOOR TYPE
LOW HEIGHT PARTITION WALL	WINDOW TYPE
REINFORCED CONCRETE	EXTERNAL FINISHING
SAND, SCREED	STRUCTURAL COLUMN
PLASTER OR RENDER PAINTED	OPENING ABOVE
LEVEL ON PLAN LEVEL ON SECTIONS AND ELEVATIONS	
UP LIGHT	
FLOOR LIGHT	
OUTDOOR FLOOR LAMP	
STRIP LIGHT @ ROOF, STEP, PLANTER BOX ETC.	

SIMA MALAK + ALSSAMOURÉ
DESIGN ASSOCIATES

P.O. Box 15707 - Riyadh 11454 KSA
Tel. 01 441 4963 - Fax. 01 441 3867
simas@simas.com

المكتب الاستشاري الرئيسي

شركة المطورون العرب للاستشارات الهندسية

ترخيص رقم ٠١١٠٠٠٢٤٥٦


الاعتماد	الدرجة	التخصص	المهندس	تصميم معماري و تخطيط
٢٧٠٩٦	مستشار	عمارة	محمد جميل اساميل	
٣٧١٠	محترف	هندسة مدنية	غباري كاسانيل	تصميم انشائي
٣٠٣٧٨	رسم مخططات معمارية	هندسة معمارية	ابن عماد جميل	رسم مخططات معمارية
٨٦٦١	مستشار	هندسة كهربائية	اسامة طاهر سيد عرب	تصميم كهربائي
٧٤٣٠٢	محترف	هندسة ميكانيكية	احسان علي الفاضل	تصميم ميكانيكا

2-01 DESIGN SHEET SIMA MALAK + ALSSAMOURÉ ARCHITECTS VILLA-1 (R.S.S.)

PRIVATE VILLA
IN RIYADH, KSA

OWNER NAME	1	DESIGN CONCEPT
SIMA MALAK	2	PRELIM. DESIGN
	3	DESIGN DEVELOP.
	4	WORKING DWG.
(VILLA-1) PENTHOUSE FLOOR LAYOUT PLAN	5	SHOP DRAWING
	6	AS BUILT DWG.

PROJ. NO.	DWG. NO.	DATE	SCALE:
P-2024-07	AR-05	jun2024	1:100

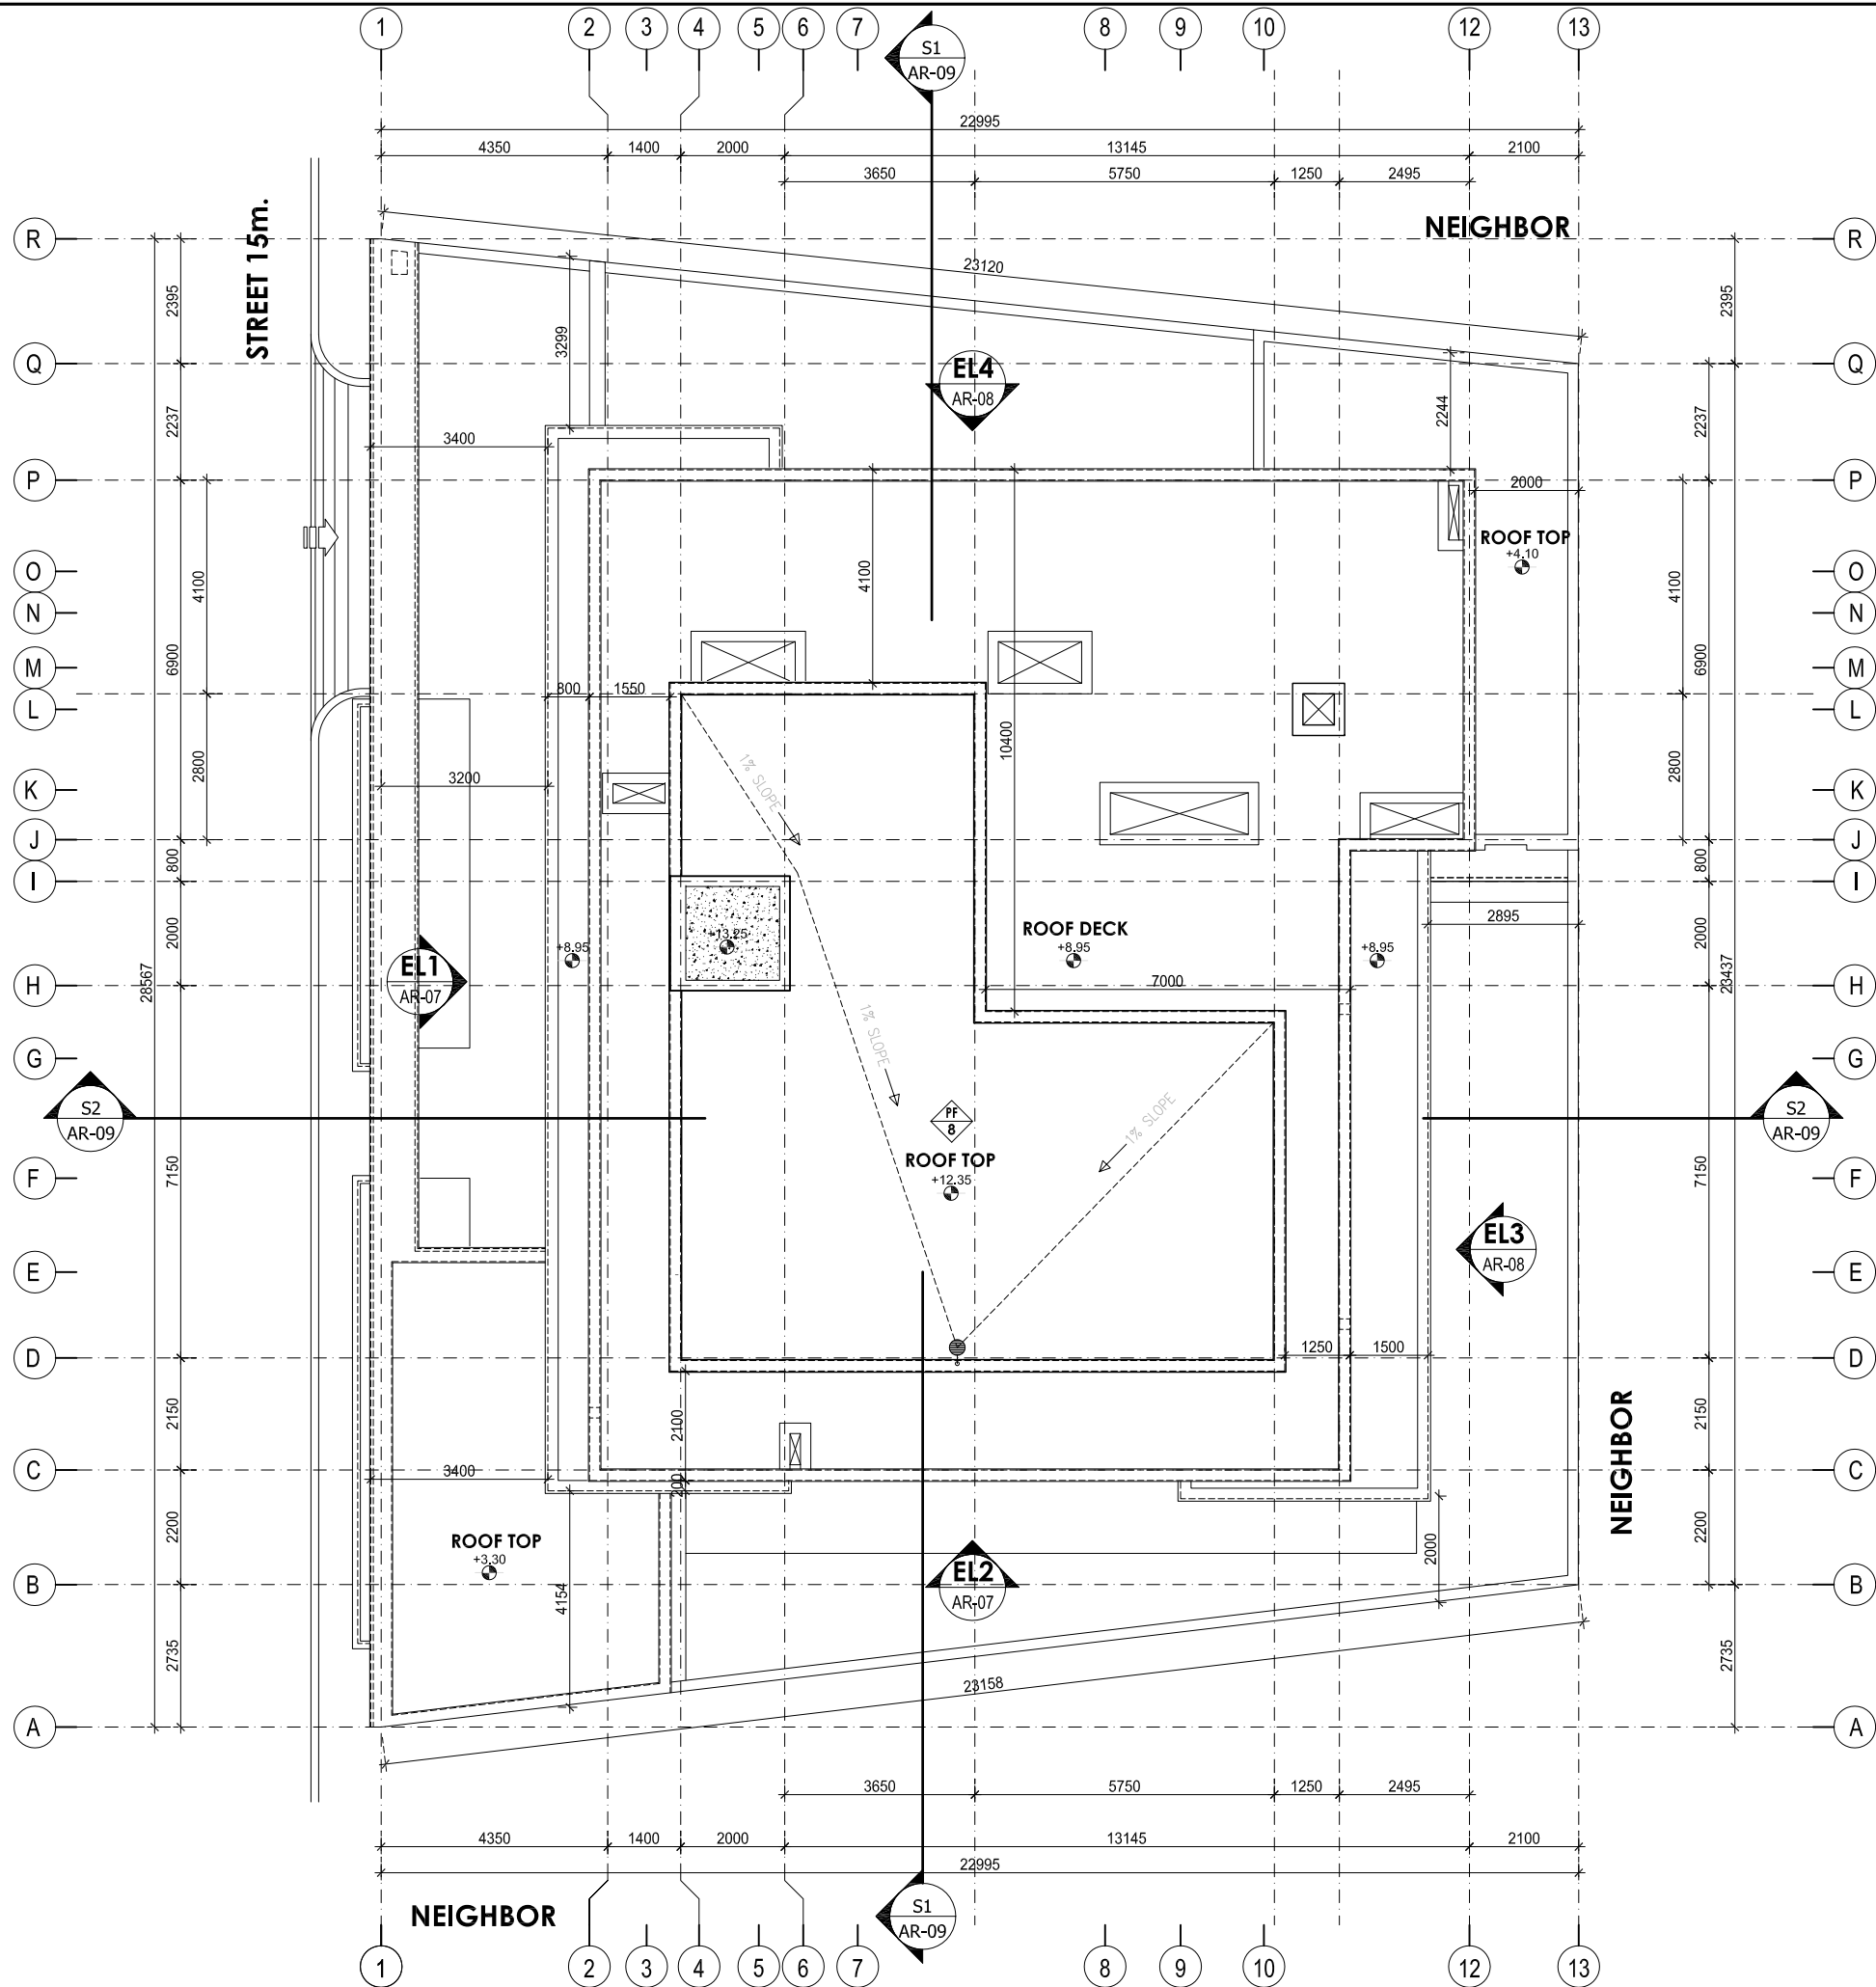

GENERAL NOTES

- ALL LEVELS ARE SHOWN IN METERS AND RELATED TO DATUM LEVEL OF +0.00. (STREET LEVEL) IS EQUAL TO (xxx.xx) OF CORRESPONDING LEVEL ON TOPOGRAPHICAL SURVEY DRAWING. DIMENSIONS ARE SHOWN IN MILLIMETERS.
- ALL INTERNAL PARTITIONS ARE 200mm THICK AND ALL EXTERNAL WALLS ARE 300mm THICK UNLESS OTHERWISE SPECIFIED.
- DETAIL DRAWINGS SHOWN IN CIRCLES IN THIS DRAWING SHALL BE REFERRED TO FOR MORE INFORMATION PERTAINING TO THE ENCIRCLED AREAS.
- WALL DIMENSIONS DO NOT INCLUDE RENDER, PLASTER FINISHES OR PRE-CAST CONCRETE PLINTH UNLESS OTHERWISE INDICATED.
- DOORS AND ARCHES ARE SET OUT:
A. ON THE CENTER OF THE WALL OR
B. FROM A 200mm NIB OR
C. AS DIMENSIONED
- ALL INTERNAL WALLS SHALL BE TAKEN TO THE UNDERSIDE OF THE SOFFIT OR BEAM UNLESS OTHERWISE INDICATED.
- ALL FALLS TO ROOFS, TERRACES INCLUDING THE FALL ON THE MAIN ENTRANCE WALKWAY SHALL BE 0.50% MINIMUM.
- ALL CHANGES IN DIRECTION OF PLASTER AND RENDER SHALL BE FORMED BY THE APPROPRIATE GALVANIZED METAL BEAD.
- LEVELS OF EXTERNAL FLOOR FINISHES ARE SHOWN AS NOMINAL. FINISHES ADJACENT TO BUILDING SHALL BE LAID TO FALL AWAY FROM THE BUILDING.
- ALL SHOP DRAWINGS, SAMPLES OR CATALOG CUTS TO BE APPROVED BY THE ARCHITECT BEFORE THE FINAL EXECUTION.
- THE CONTRACTOR SHALL SUBMIT SAMPLES & SHOP DRAWINGS FOR ALL EXTERIOR CLADDING FINISHES PRIOR TO ANY INSTALLATIONS.

SYMBOL & LEGEND

- | | |
|--|---|
| 300mm THK EXTERNAL CONCRETE BLOCK WALL (INSULATED) | LEVEL INDICATION
B1- BASEMENT FLOOR
G1- GROUND FLOOR
F1- FIRST FLOOR |
| 200mm THK INTERNAL CONCRETE BLOCK WALL | ROOM NUMBERING
BUILDING NUMBER |
| 100mm THK INTERNAL CONCRETE BLOCK WALL | DOOR TYPE |
| LOW HEIGHT PARTITION WALL | WINDOW TYPE |
| REINFORCED CONCRETE | EXTERNAL FINISHING |
| SAND, SCREED | STRUCTURAL COLUMN |
| PLASTER OR RENDER
PAINTED | OPENING ABOVE |
| LEVEL ON PLAN
LEVEL ON SECTIONS
AND ELEVATIONS | |
| UP LIGHT | |
| FLOOR LIGHT | |
| OUTDOOR FLOOR LAMP | |
| STRIP LIGHT @ ROOF, STEP,
PLANTER BOX ETC. | |

SIMA MALAK + ALSSAMOURÉ
DESIGN ASSOCIATES

P.O. Box 15707 - Riyadh 11454 KSA
Tel. 01 441 4963 - Fax. 01 441 3867
simas@simas.com

المكتب الاستشاري الرئيسي

شركة المطورون العرب للاستشارات الهندسية



ترخيص رقم ٢٤٥٦-٥١١٠٠٠

الاعتماد	الدرجة	التخصص	المهندس	تصميم معماري و تخطيط
٢٧٥٩٦	مستشار	عمارة	محمد جميل اسمايل	
٣٧١٠١	محترف	هندسة مدنية	غيداردو كايانيل كايانيل	تصميم انشائي
٣٠٣٧٨	مستشار	هندسة معمارية	امين عماد جميل	رسم مخططات معمارية
٨١٢١١	مستشار	هندسة كهربائية	اسامة طاهر سيد عرب	تصميم كهربائي
٧٤٣٧٢	محترف	هندسة ميكانيكية	احسان علي الفاضل	تصميم ميكانيكا

2-01 DESIGNER: SIMA MALAK + ALSSAMOURÉ
2-02 DESIGNER: SIMA MALAK + ALSSAMOURÉ
2-03 DESIGNER: SIMA MALAK + ALSSAMOURÉ


PRIVATE VILLA
IN RIYADH, KSA

OWNER NAME		1 DESIGN CONCEPT	
SIMA MALAK		2 PRELIM. DESIGN	
		3 DESIGN DEVELOPMENT	
		4 WORKING DRAWINGS	
(VILLA-1) UPPER ROOF LAYOUT PLAN		5 SHOP DRAWINGS	
		6 AS BUILT DOCUMENTS	
		DRAWING TITLE	
PROJ. NO.	DWG. NO.	DATE:	SCALE/DWG.
P-2024-07	AR-06	jun2024	1:100

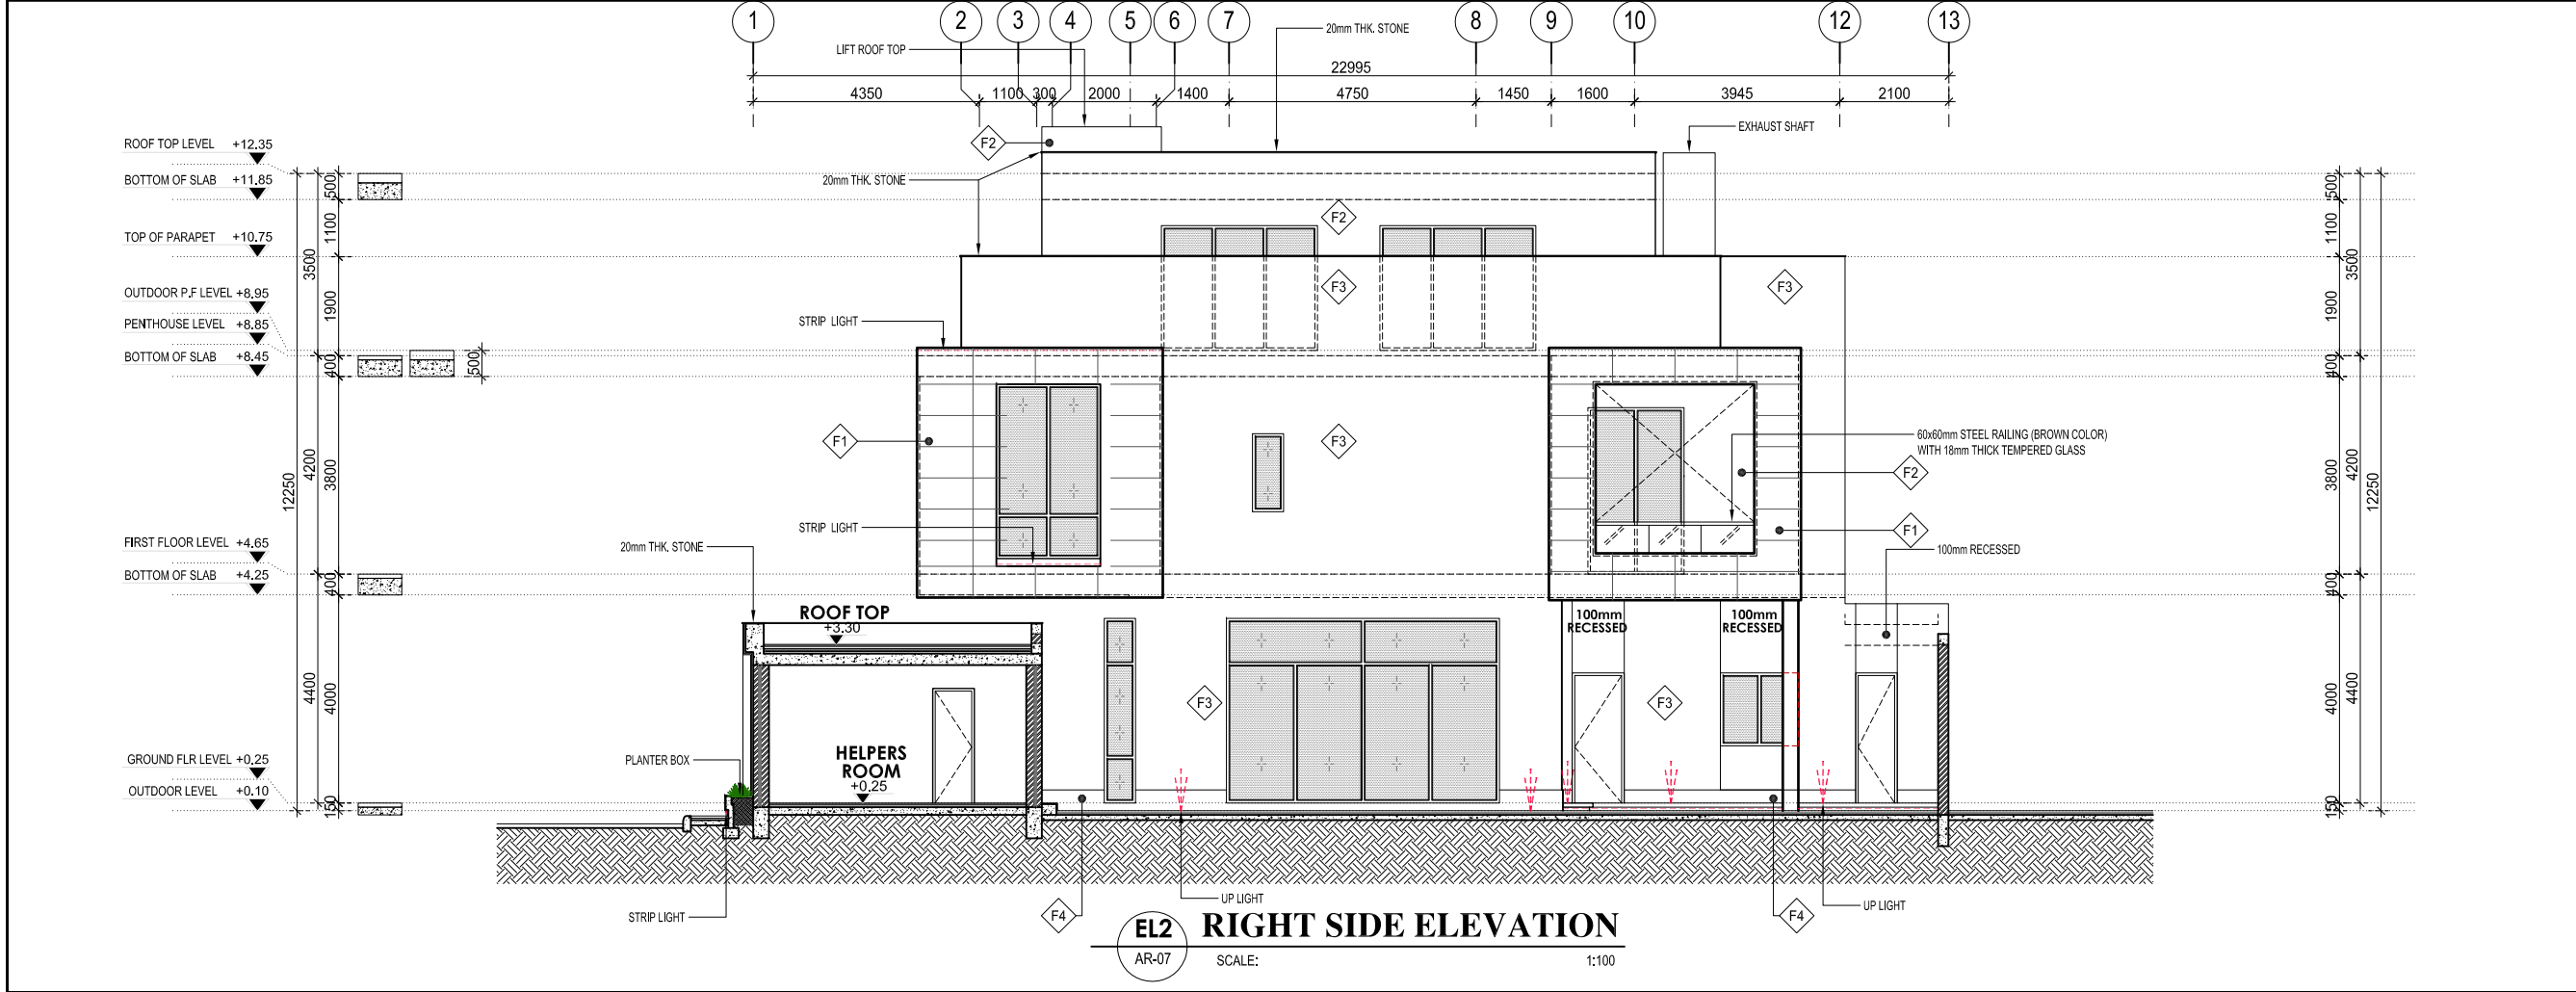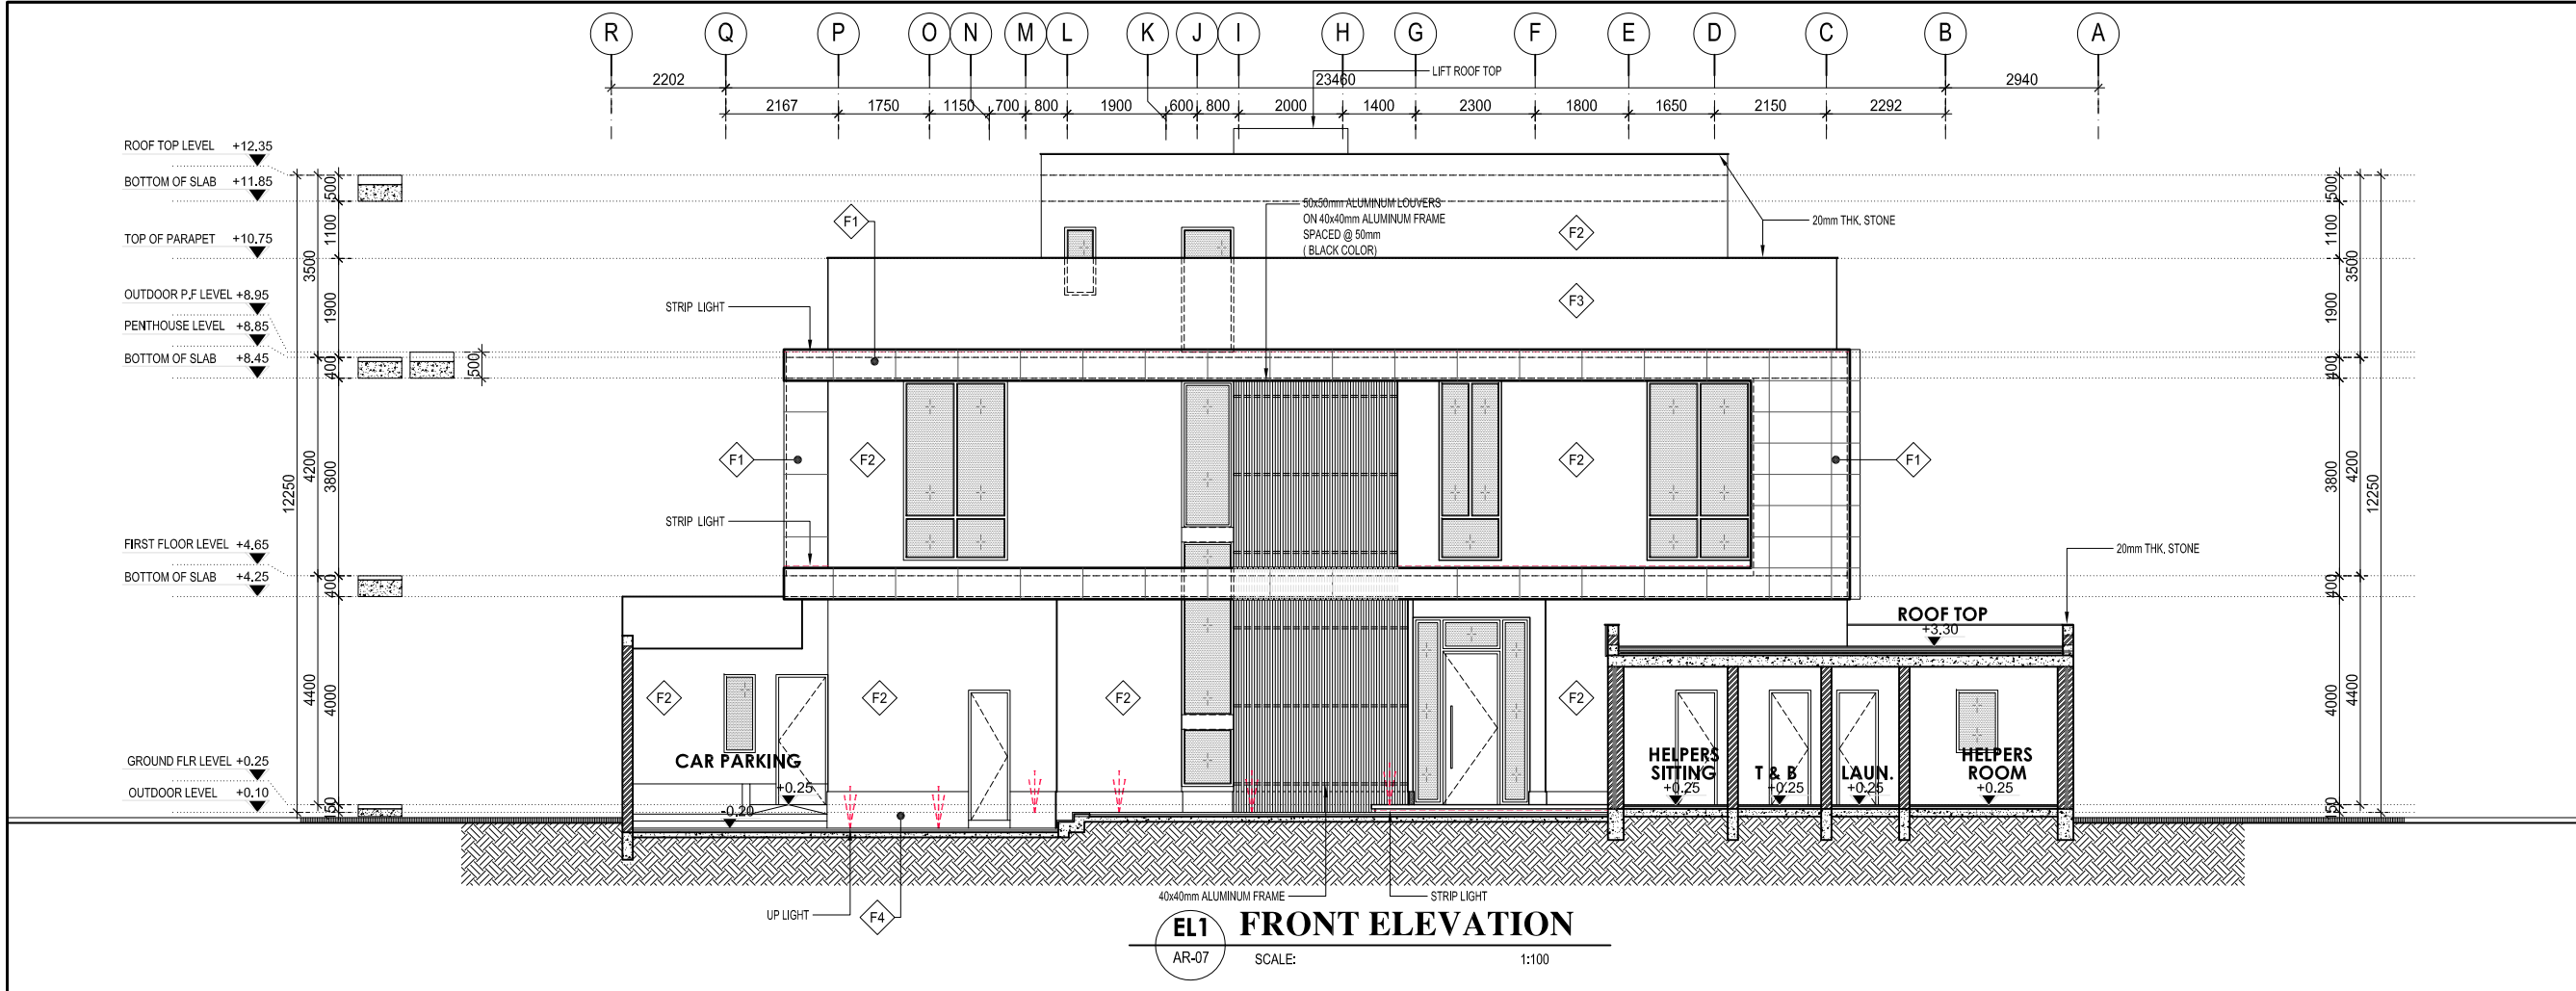

FINISHING LEGEND :

- F1 600 x 1200 x 20mm THICK TRAVERTINE MARBLE OR PORCELAIN TILE TRAVERTINE EFFECT
- F2 TEXTURED PAINT ON CEMENT (COLOR IVORY WHITE OR AS SPECIFIED)
- F3 TEXTURED PAINT ON CEMENT (COLOR GRAY OR AS SPECIFIED)
- F4 1200 x 2000 x 20mm THICK GRAY COLOR MARBLE STONE OR PORCELAIN TILE STONE EFFECT

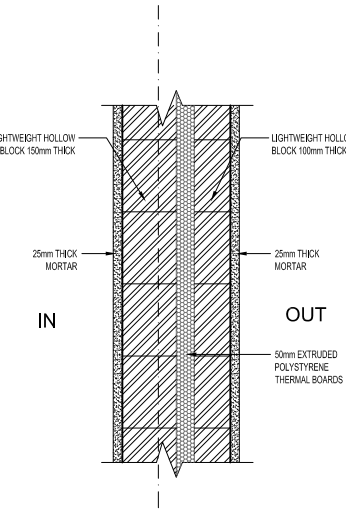

WALL SECTION DETAIL
WALL THK = 350mm
U VALUE FOR THE WALL=0.382

1
AR-07
SCALE: 1:15

SIMA MALAK + ALSSAMOURÉ
DESIGN ASSOCIATES
P.O. Box 15707 - Riyadh 11454 KSA
Tel. 01 441 4963 - Fax. 01 441 3867
simals@simals.com



المكتب الاستشاري الرئيسي
شركة المطورون العرب للاستشارات الهندسية
ترخيص رقم ٢٤٥٦-٠١١

الاعتماد	الدرجة	التخصص	المهندس	تصميم معماري و تخطيط
٢٧٥٩٦	مستشار	عمارة	محمد جميل اساميل	تصميم معماري و تخطيط
٣٧١٠	مختبر	هندسة مدنية	غيداردو كاريانيلو كاتيانان	تصميم انشائي
٣٠٣٧٨	مختبر	هندسة معمارية	ابن عماد جميل	رسم مخططات معمارية
٨١٣١	مستشار	هندسة معمارية	اسامة طاهر سيد عرب هندسة كيريا	تصميم كيريا
٧٤٣٧٢	مختبر	هندسة ميكانيكية	احمد علي الفاضل	تصميم ميكانيكا

2-384 KESKONAP SECRET SIMA MALAK+ALSSAMOURÉ DESIGN ASSOCIATES



PRIVATE VILLA
IN RIYADH, KSA

OWNER NAME	1	DESIGN CONCEPT
SIMA MALAK	2	PRELIM. DESIGN
	3	DESIGN DEVELOP.
	4	WORKING DWG.
(VILLA-1) FRONT ELEVATION RIGHT SIDE ELEVATION	5	SHOP DRAWING
	6	AS BUILT DWG.
PROJ. NO. P-2024-07	DWG. NO. AR-07	DATE jun2024
		SCALE: 1:100

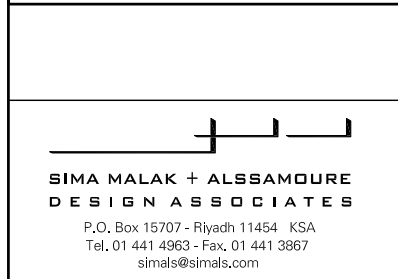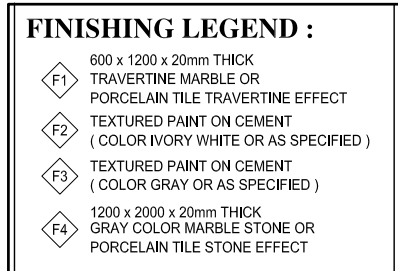

Z-101 DEEPSEA-P-000067-SHMA HMLA006 WORKING DRAWING-YELLA-FLOCSOP

OWNER NAME		1	DESIGN CONCEPT
SIMA MALAK		2	PRELIM. DESIGN
		3	DESIGN DEVELOP.
(VILLA-1) REAR ELEVATION LEFT SIDE ELEVATION		DRAWING TITLE	4
			WORKING DWG.
		5	SHOP DRAWING
		6	AS BUILT DWG.
PROJ. NO.	DWG. NO.	DATE:	SCALE:
P-2024-07	AR-08	jun2024	1:100

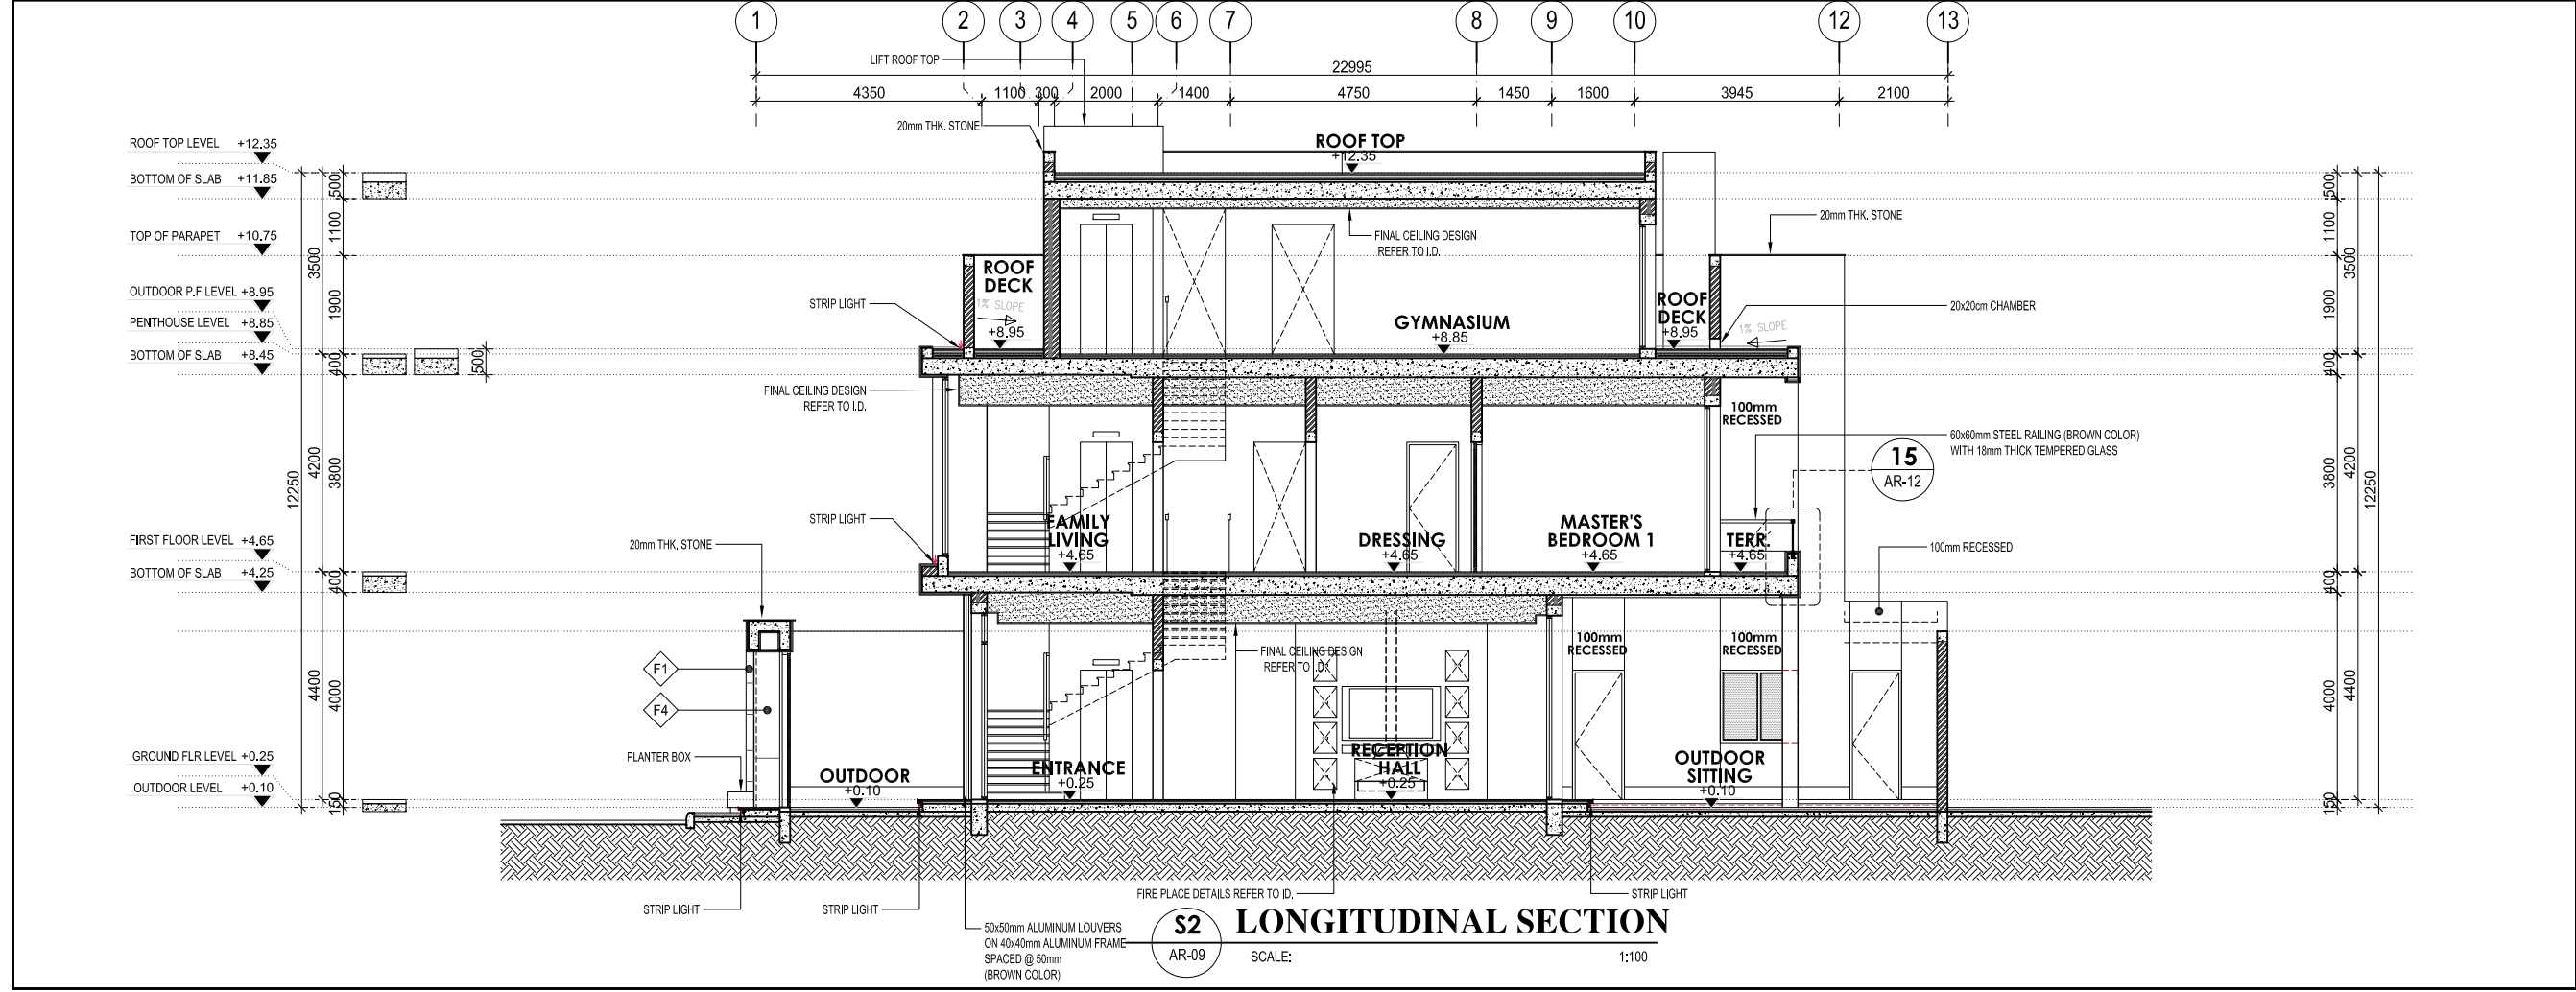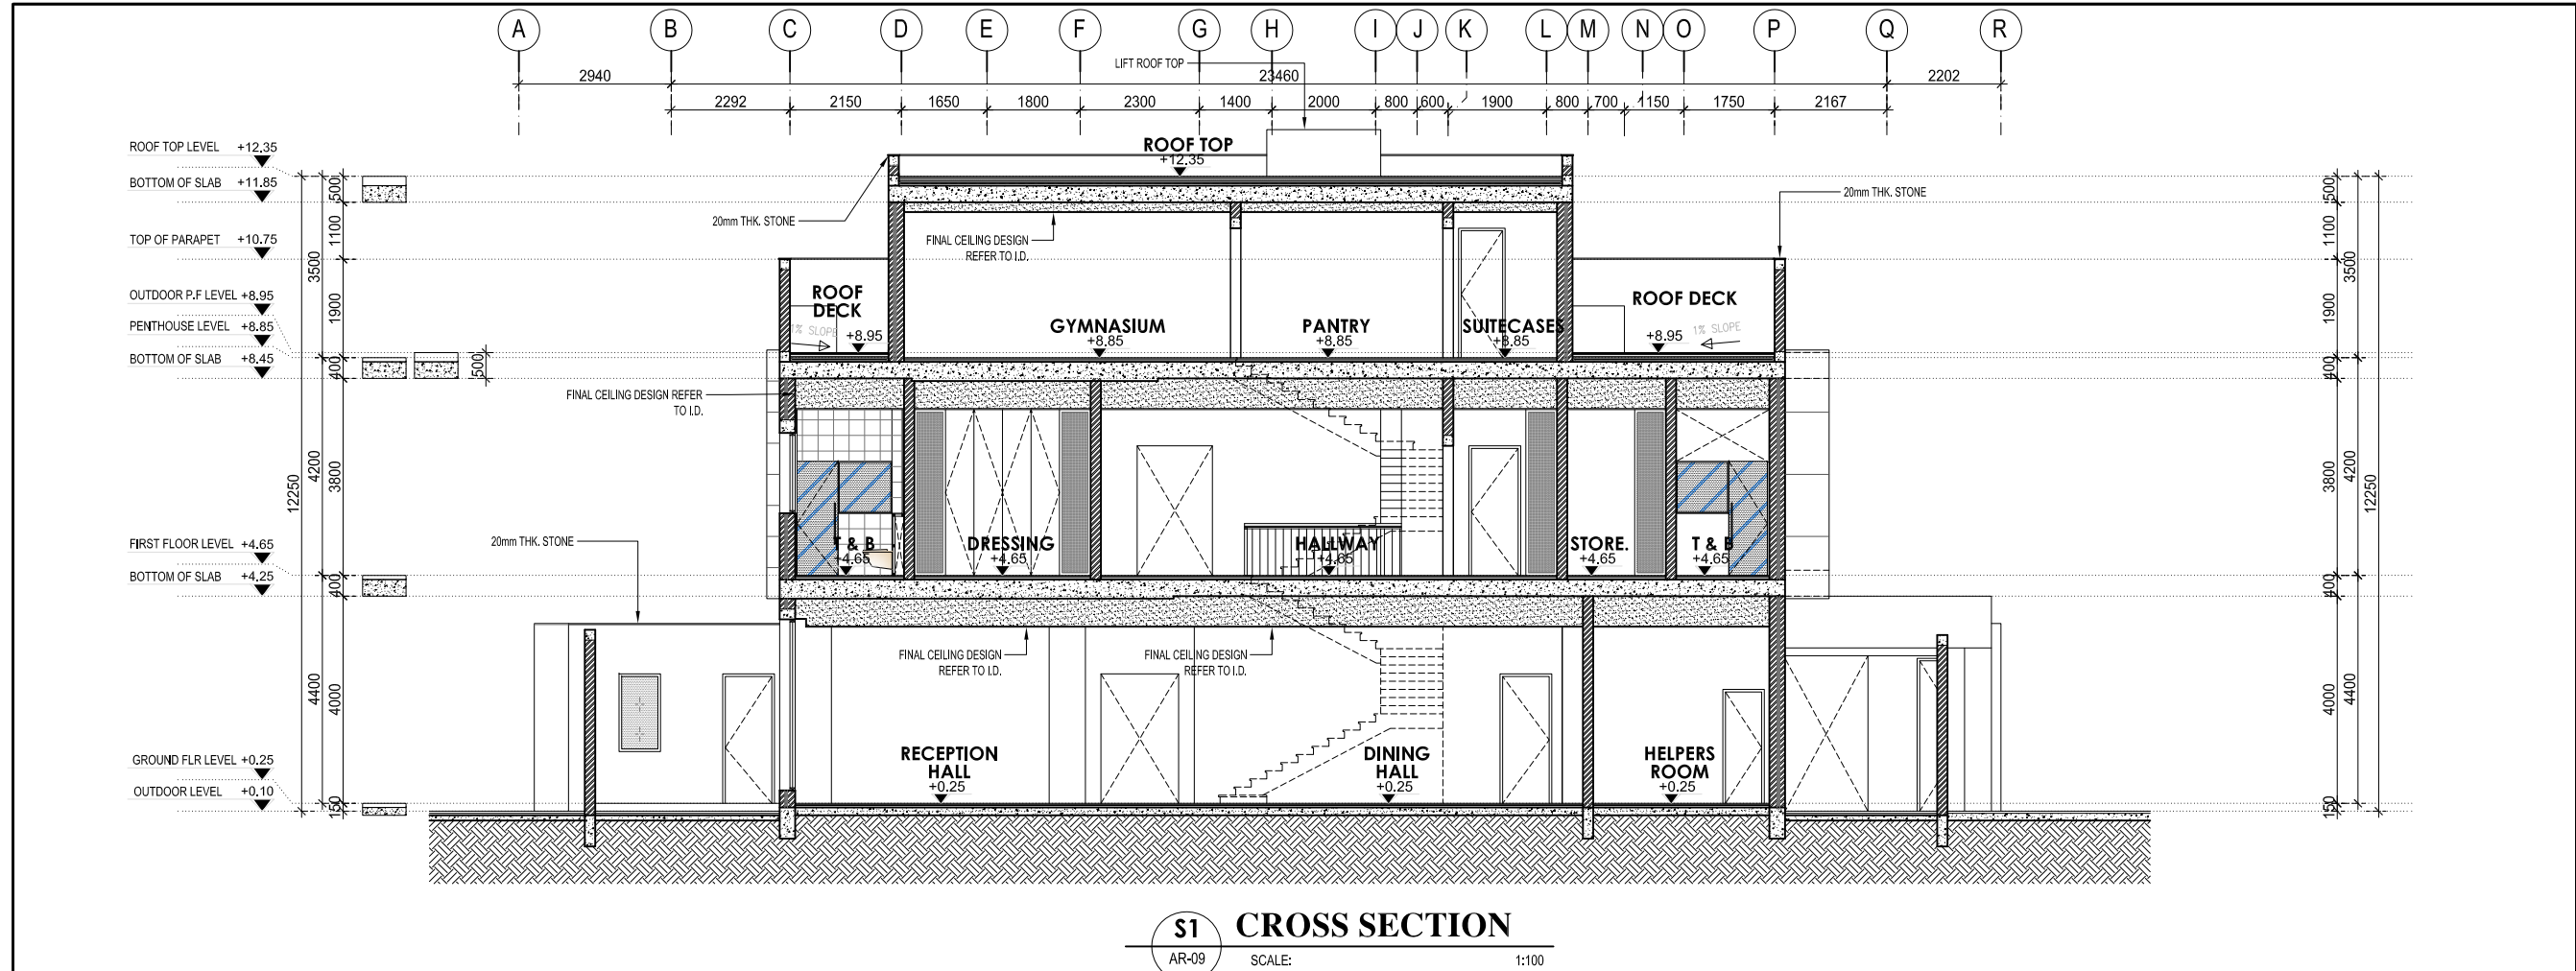

FINISHING LEGEND :

- F1 600 x 1200 x 20mm THICK TRAVERTINE MARBLE OR PORCELAIN TILE TRAVERTINE EFFECT
- F2 TEXTURED PAINT ON CEMENT (COLOR IVORY WHITE OR AS SPECIFIED)
- F3 TEXTURED PAINT ON CEMENT (COLOR GRAY OR AS SPECIFIED)
- F4 1200 x 2000 x 20mm THICK GRAY COLOR MARBLE STONE OR PORCELAIN TILE STONE EFFECT

WALL SECTION DETAIL
WALL THK = 350mm
U VALUE FOR THE WALL=0.382

1
AR-09

TYPICAL DETAIL

SCALE: 1:15

**SIMA MALAK + ALSSAMOURE
DESIGN ASSOCIATES**
P.O. Box 15707 - Riyadh 11454 KSA
Tel. 01 441 4963 - Fax. 01 441 3867
simals@simals.com

المكتب الاستشاري الرئيسي
شركة المطورون العرب للاستشارات الهندسية
ترخيص رقم ٠١١٠٠٠٢٤٥٦

الاعتماد	الدرجة	التخصص	المهندس	تصميم معماري و تنفيذ
٢٧٥٩٦	مستشار	عمارة	محمد جميل اسماعيل	
٣٧١٠١	محترف	هندسة مدنية	غيداردو كاباتيللا كاباتيلان	تصميم انشائي
٣٠٣٥٧٨	هندسة معمارية	هندسة معمارية	ابن عماد جميل	رسم مخططات معمارية
٨٦٦١	مستشار	هندسة كهربائية	اسامة طاهر سيد عرب هندسة كهربائية	تصميم كهربائي
٧٤٣٧٢	محترف	هندسة ميكانيكية	احسان علي الفاضل	تصميم ميكانيكا

**PRIVATE VILLA
IN RIYADH, KSA**

OWNER NAME

SIMA MALAK

1
DESIGN CONCEPT

2
PRELIM. DESIGN

3
DESIGN DEVELOP.

4
WORKING DWG.

5
SHOP DRAWING

6
AS BUILT DWG.

(VILLA-1)
CROSS SECTION
LONGITUDINAL SECTION

DRAWING TITLE






PROJ. NO.
P-2024-07

DWG. NO.
AR-09

DATE
jun2024

SCALE:
1:100

Copyright © 2024 SIMA MALAK + ALSSAMOURE DESIGN ASSOCIATES. All rights reserved. This drawing is the property of SIMA MALAK + ALSSAMOURE DESIGN ASSOCIATES and is not to be reproduced, stored in a retrieval system, or transmitted in any form or by any means, electronic, mechanical, photocopying, recording, or by any information storage and retrieval system, without the prior written permission of SIMA MALAK + ALSSAMOURE DESIGN ASSOCIATES.

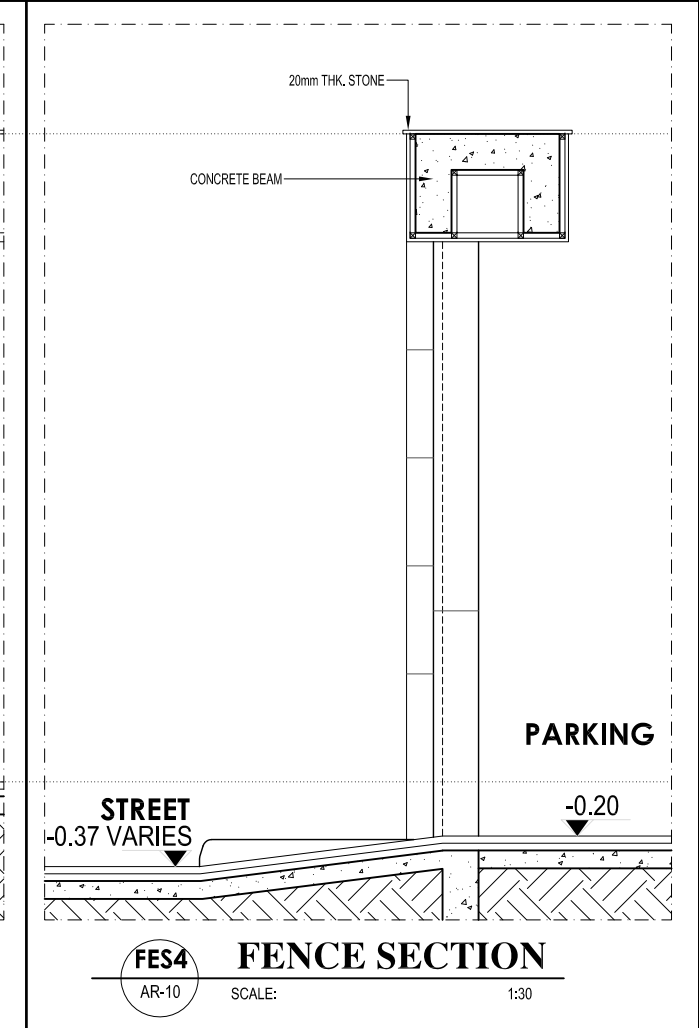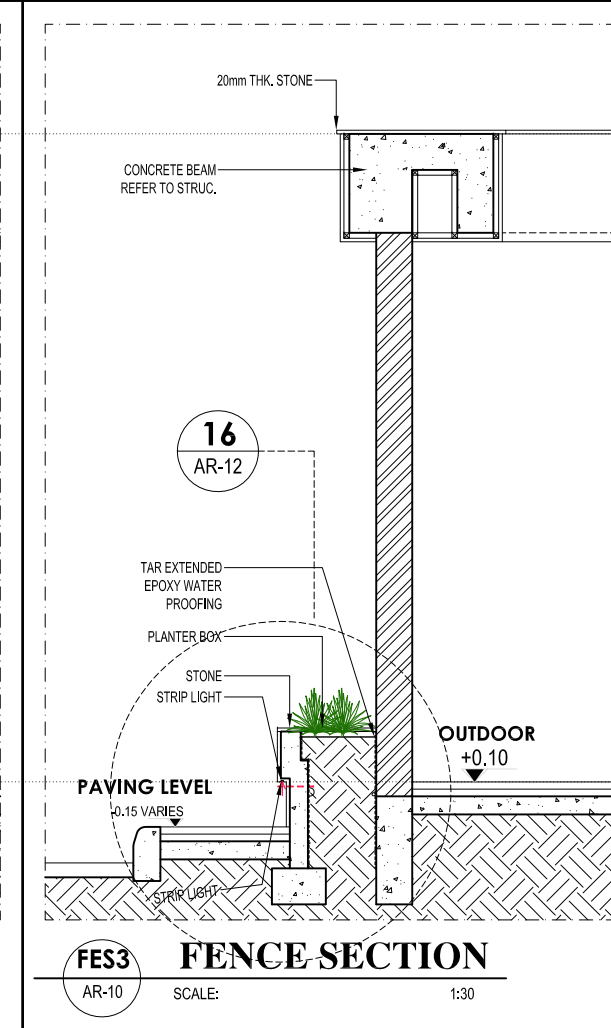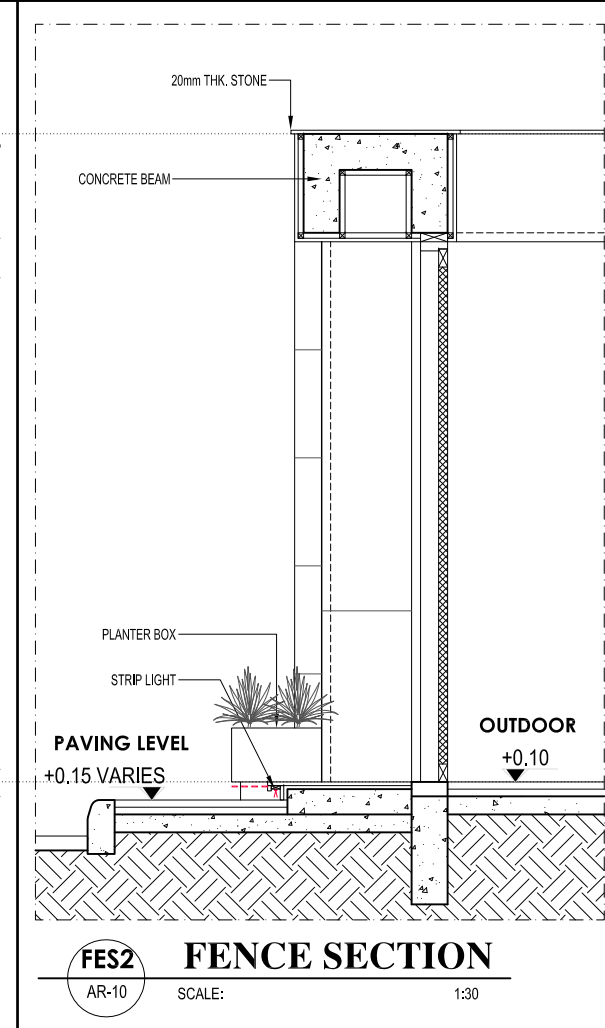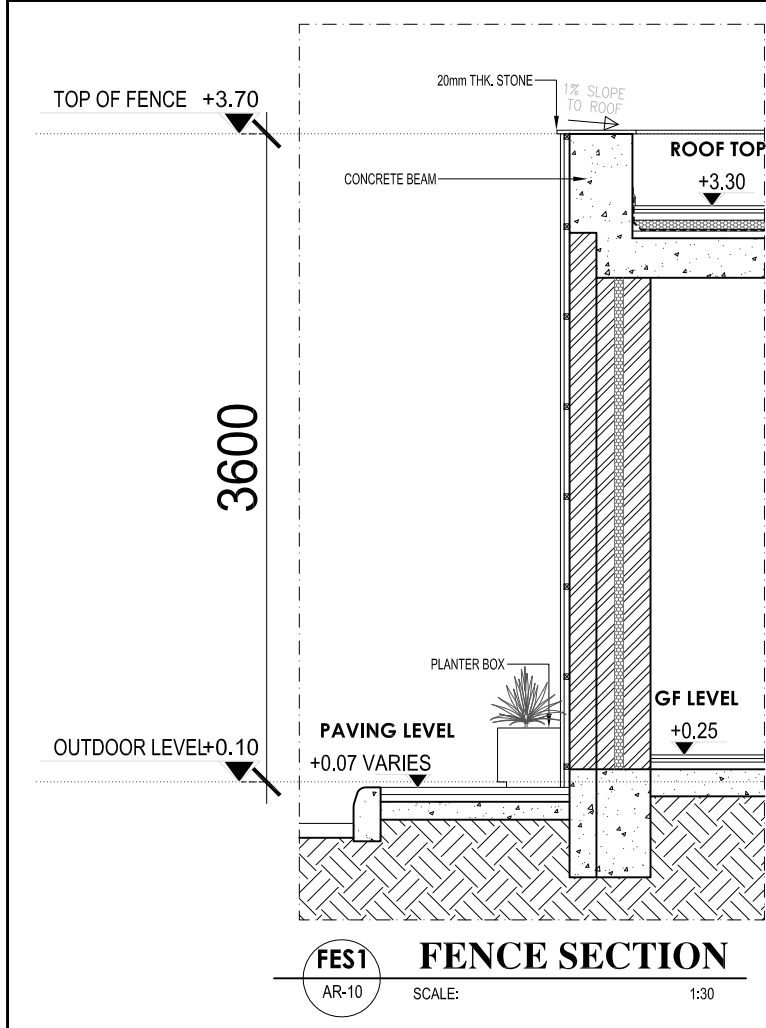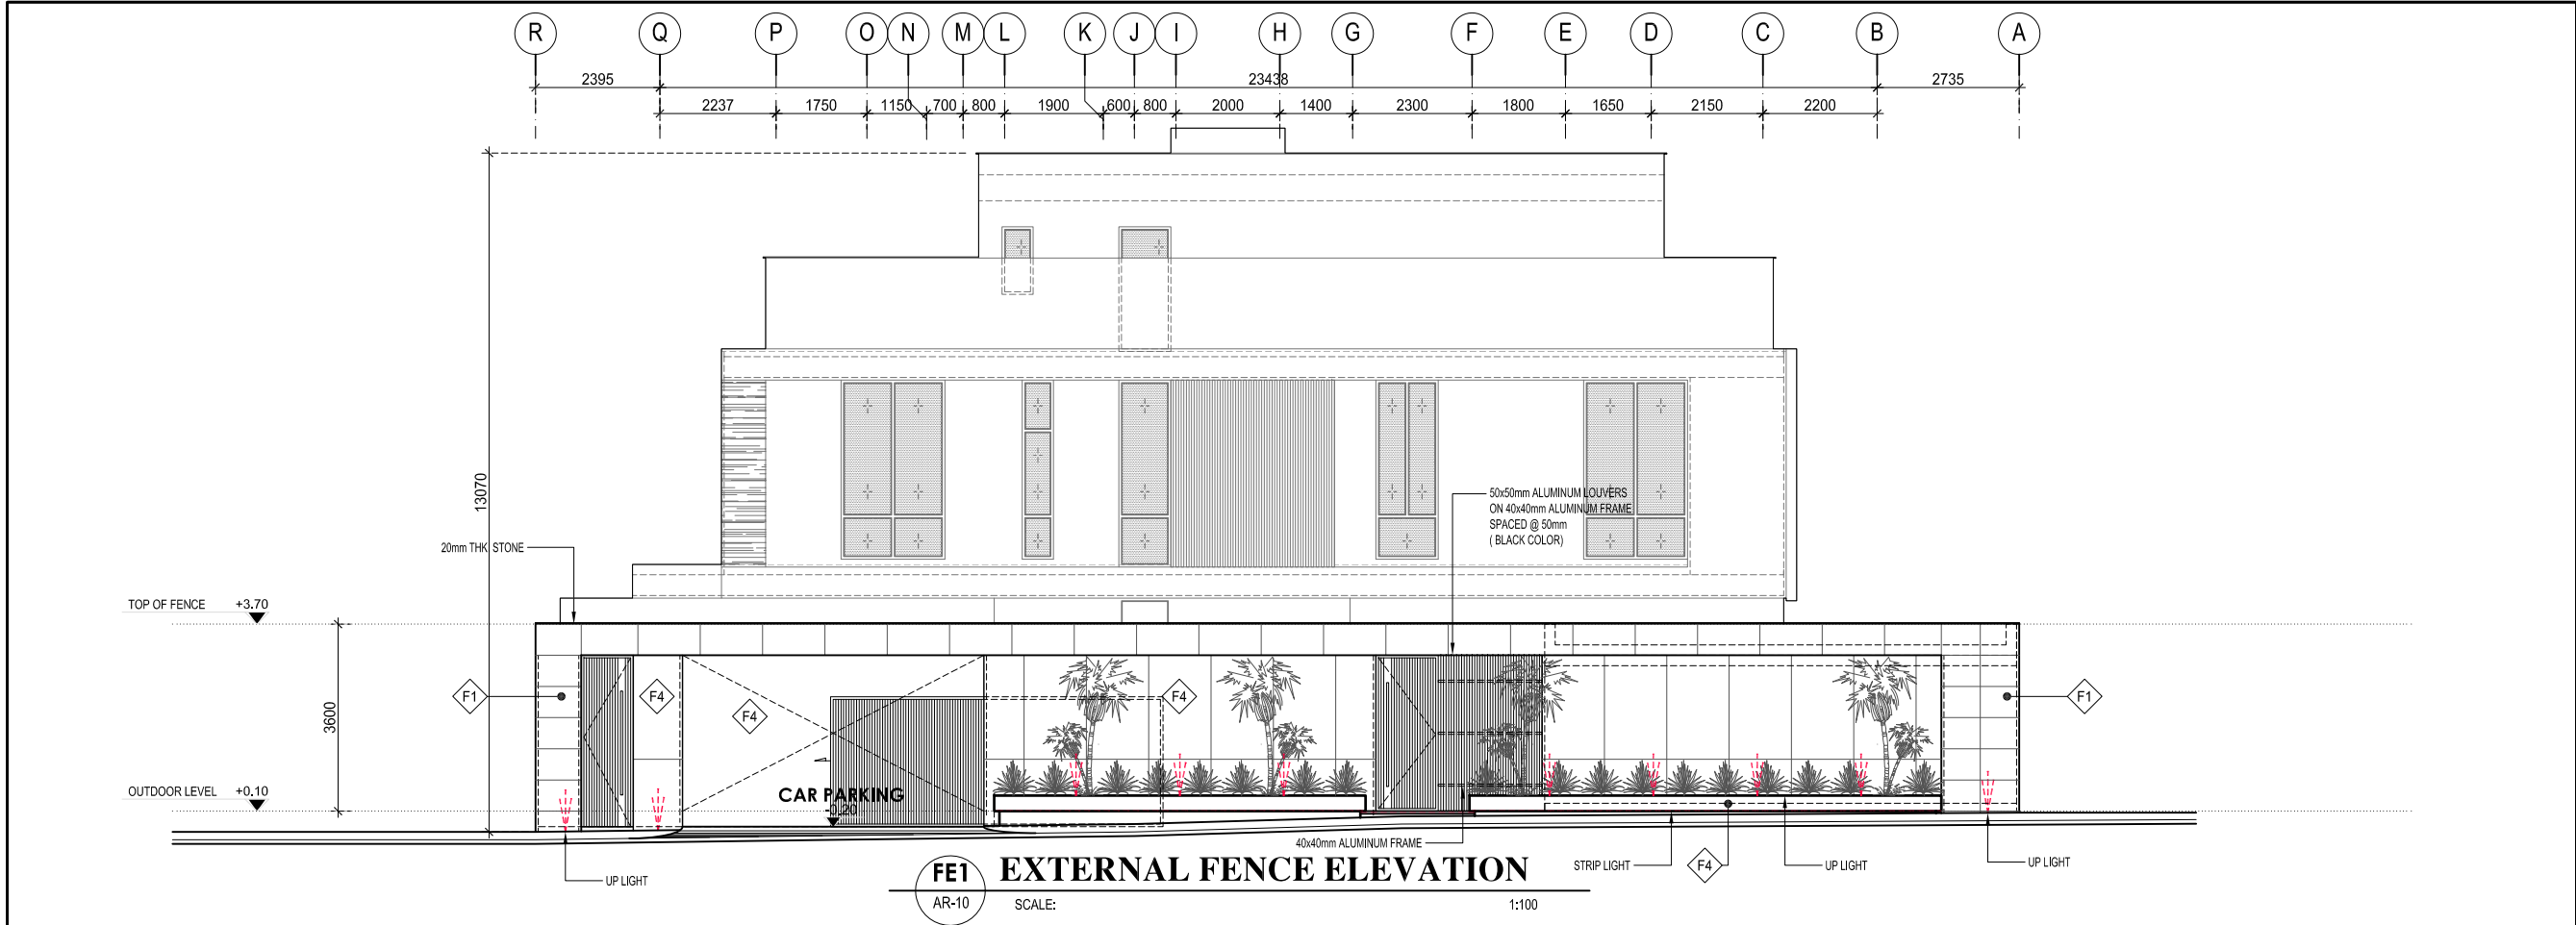


FINISHING LEGEND :	
F1	600 x 1200 x 20mm THICK TRAVERTINE MARBLE OR PORCELAIN TILE TRAVERTINE EFFECT
F2	TEXTURED PAINT ON CEMENT (COLOR IVORY WHITE OR AS SPECIFIED)
F3	TEXTURED PAINT ON CEMENT (COLOR GRAY OR AS SPECIFIED)
F4	1200 x 2000 x 20mm THICK GRAY COLOR MARBLE STONE OR PORCELAIN TILE STONE EFFECT

SIMA MALAK + ALSSAMOURÉ
DESIGN ASSOCIATES
P.O. Box 15707 - Riyadh 11454 KSA
Tel. 01 441 4963 - Fax. 01 441 3867
simals@simals.com


المكتب الاستشاري الرئيسي	
شركة المطورون العرب للاستشارات الهندسية	
ترخيص رقم ٠١١٠٠٠٢٤٥٦	
الاعتماد	المهندس
٢٧٥٩٦	ممد جليل اسماعيل
٣٧١٠١	غيداردو كايانيل
٣٠٣٧٨	ايمن عماد جميل
٨٦٦١	اسامة طاهر سيد عرب
٧٤٣٧٢	احمد علي الفاضل
٣٧١٠١	ممد جليل اسماعيل
٣٠٣٧٨	غيداردو كايانيل
٨٦٦١	اسامة طاهر سيد عرب
٧٤٣٧٢	احمد علي الفاضل

PRIVATE VILLA IN RIYADH, KSA	
OWNER NAME	1 DESIGN CONCEPT
SIMA MALAK	2 PRELIM. DESIGN
	3 DESIGN DEVELOP.
	4 WORKING DWG.
(VILLA-1) FENCE ELEVATION	5 SHOP DRAWING
	6 AS BUILT DWG.
ARCHITECTURAL DETAILS-1	
PROJ. NO. P-2024-07	DWG. NO. AR-10
DATE jun2024	SCALE: 1:100/30

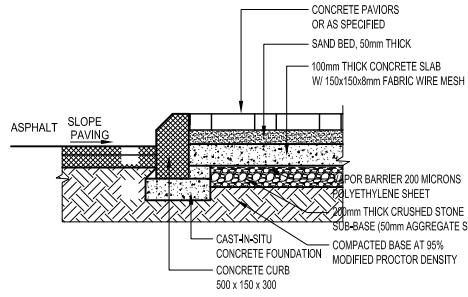


09 SIDEWALK SECTION DETAIL
TYPICAL DETAIL

AR-12 SCALE: 1:25

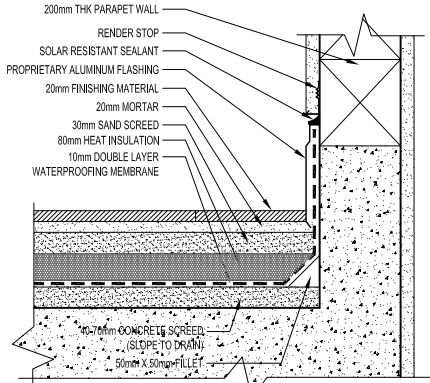


10 PARAPET WALL
TYPICAL DETAIL

AR-12 SCALE: 1:10

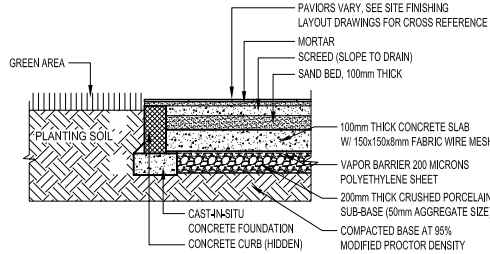


11 DETAIL AT GREEN AREA SECTION
TYPICAL DETAIL

AR-12 SCALE: 1:25

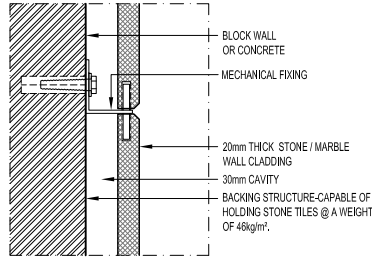


12 STONE / MARBLE
WALL CLADDING
TYPICAL DETAIL

AR-12 SCALE: 1:5

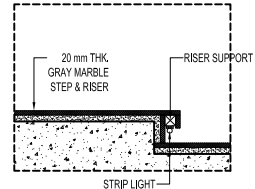


13 OUTDOOR STEP
ARCH'L DETAIL

AR-12 SCALE: 1:25

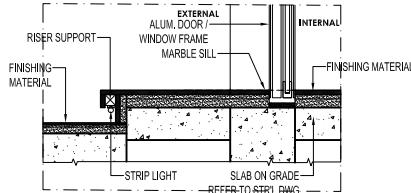


14 GROUND FLOOR WINDOW STEP
ARCH'L DETAIL

AR-12 SCALE: 1:25

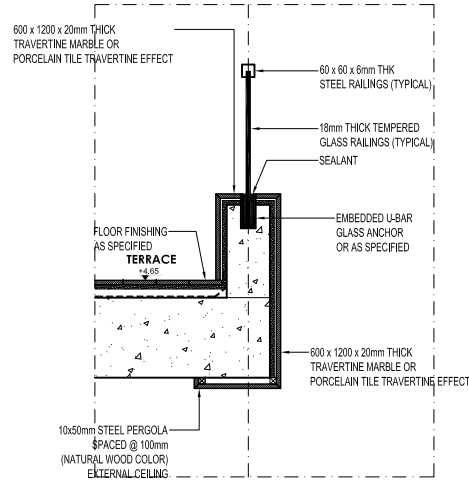


15 GLASS RAILING
ARCH'L DETAIL

AR-12 SCALE: 1:25

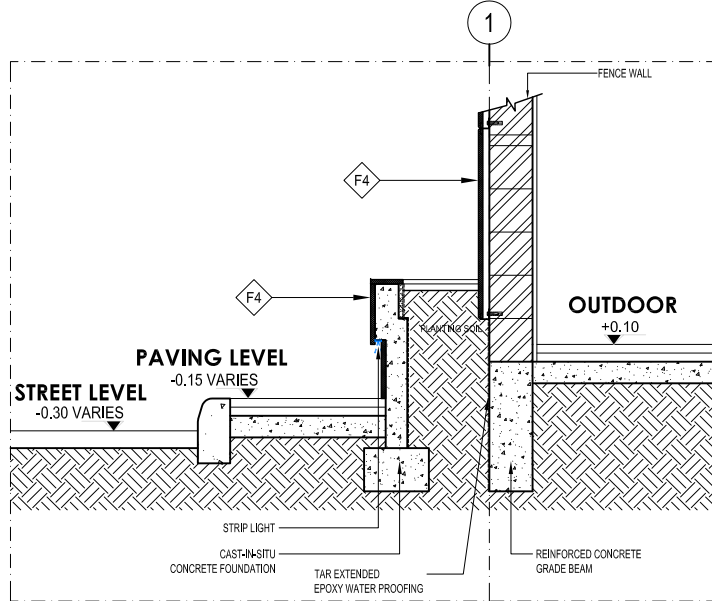


16 ARCH'L DETAIL

AR-12 SCALE: 1:25

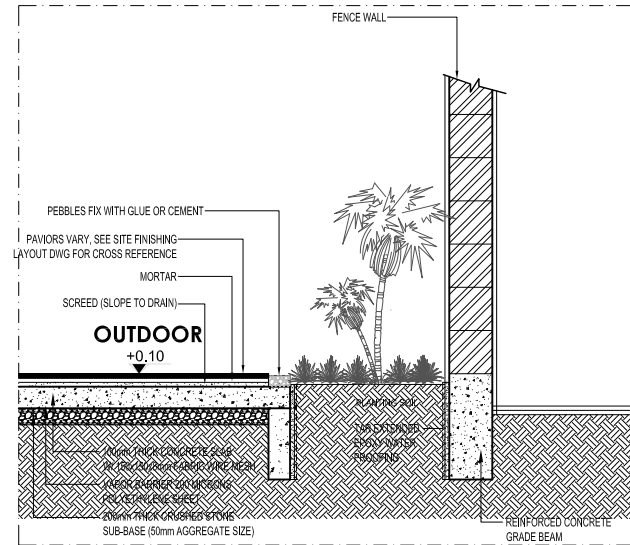


17 ARCH'L DETAIL

AR-12 SCALE: 1:25

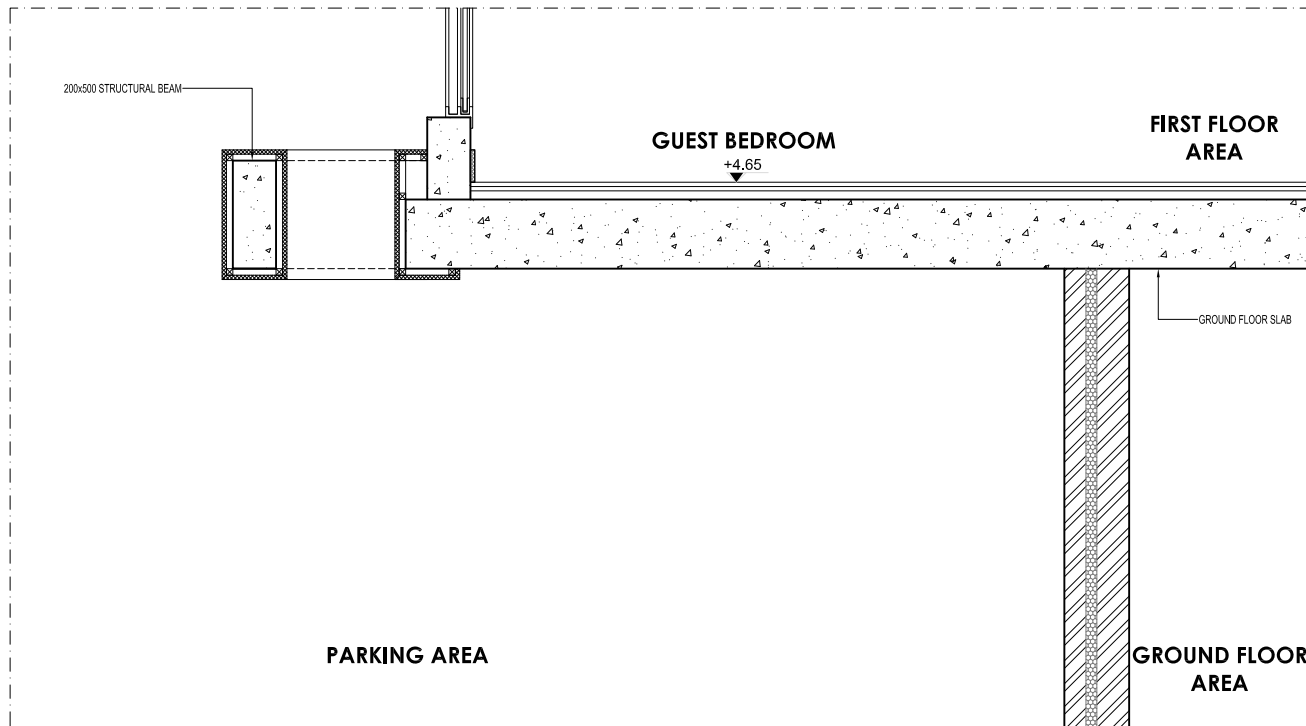

18 ARCH'L DETAIL

AR-12 SCALE: 1:25

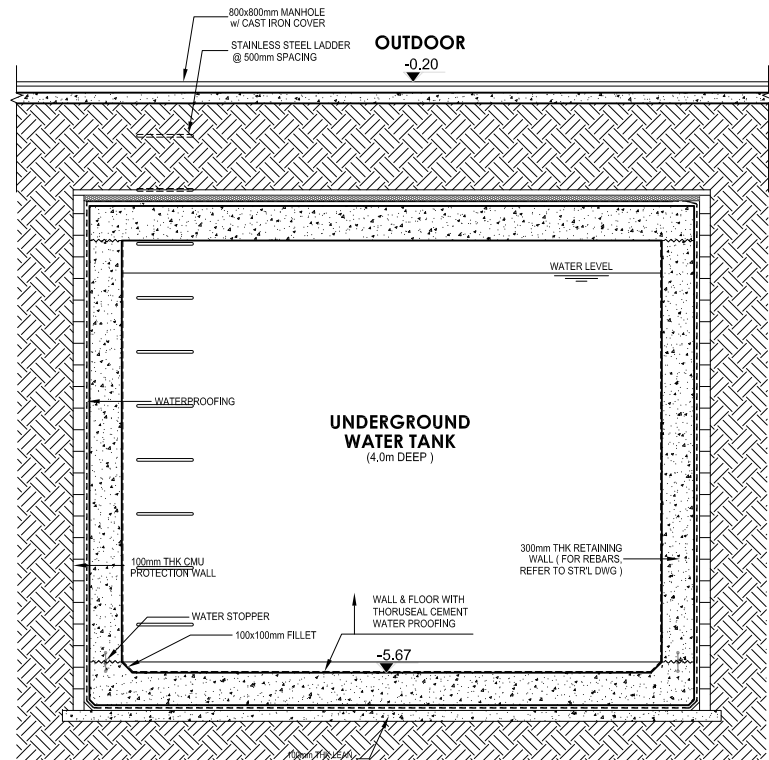

19 UNDERGROUND WATER TANK TYPICAL DETAIL

AR-12 SCALE: 1:50

FINISHING LEGEND :

- F1 600 x 1200 x 20mm THICK TRAVERTINE MARBLE OR PORCELAIN TILE TRAVERTINE EFFECT
- F2 TEXTURED PAINT ON CEMENT (COLOR IVORY WHITE OR AS SPECIFIED)
- F3 TEXTURED PAINT ON CEMENT (COLOR GRAY OR AS SPECIFIED)
- F4 1200 x 2000 x 20mm THICK GRAY COLOR MARBLE STONE OR PORCELAIN TILE STONE EFFECT

SIMA MALAK + ALSSAMOURE
DESIGN ASSOCIATES

P.O. Box 15707 - Riyadh 11454 KSA
Tel. 01 441 4963 - Fax. 01 441 3867
simals@simals.com

المكتب الاستشاري الرئيسي

شركة المطورون العرب للاستشارات الهندسية



ترخيص رقم ٠١١-٢٤٥٦

الاعتماد	الدرجة	التخصص	المهندس	تصميم معماري و تنفيذ
٢٧٥٩٦	مستشار	عمارة	محمد جميل اسماعيل	تصميم معماري و تنفيذ
٣٧١٠١	محترف	هندسة مدنية	غيداردو كاباتيللا كاباتيلان	تصميم انشائي
٣٠٣٧٨	مشار	هندسة معمارية	ابن عماد جميل	رسم مخططات معمارية
٨١٣١	مشار	هندسة كهربائية	اسامة طاهر سيد عرب	تصميم كهربائي
٧٤٣٠٢	محترف	هندسة ميكانيكية	احسان علي الفاضل	تصميم ميكانيكا



2-351 DESIGNER/ARCHITECT SIMA MALAK+ALSSAMOURE DESIGN ASSOCIATES VILLA-1 (Rt) (Aug 2024) (AR-12) - PLOTTED BY MIDASSAR - Sep 2025 - 2026pm

PRIVATE VILLA IN RIYADH, KSA



OWNER NAME	1	DESIGN CONCEPT
SIMA MALAK	2	PRELIM. DESIGN
(VILLA-1) ARCHITECTURAL DETAILS-2	3	DESIGN DEVELOP.
PROJ. NO. P-2024-07	4	WORKING DWG.
DWG. NO. AR-11	5	SHOP DRAWING
DATE jun2024	6	AS BUILT DWG.
SCALE: 1:50		

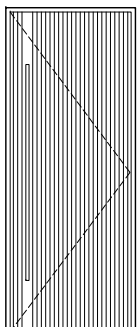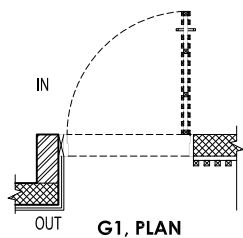



G1, ELEVATION		
DOOR NO.	G1	
DOOR TYPE	STEEL DOOR PANEL & FRAME SINGLE HINGED PANEL	
DIMENSION	3000mm (H) x 1200mm (W)	
QUANTITY	1 - SETS (VERIFY PLAN)	A=3,60m²
U-VALUE	---	
DESCRIPTION	HOLLOW CORE PANEL STEEL TUBE 40x40mm, STEEL SHEET 2mm 20x40mm PAINTED STEEL LOUVERS FROM BOTH SIDE IRONMONGERY BLACK 20x20mm HANDLE WITH STEEL PIVOTS 6 NO.	
OTHERS	INTERCOM LOCK SYSTEM	

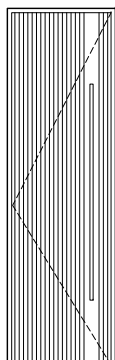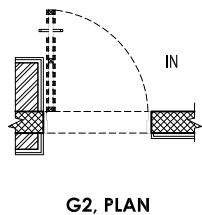



G2, ELEVATION		
DOOR NO.	G2	
DOOR TYPE	STEEL DOOR PANEL & FRAME SINGLE HINGED PANEL	
DIMENSION	3300mm (H) x 1000mm (W)	
QUANTITY	1 - SETS (VERIFY PLAN)	A=3.30m ²
U-VALUE	---	
DESCRIPTION	HOLLOW CORE PANEL STEEL TUBE 40x40mm, STEEL SHEET 2mm 20x40mm PAINTED STEEL LOUVERS FROM BOTH SIDE IRONMONGERY BLACK 20x20mm HANDLE WITH STEEL PIVOTS 6 NO.	

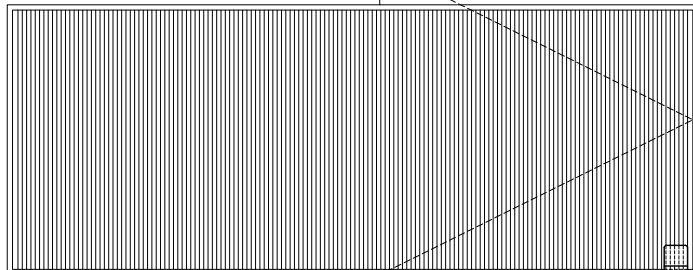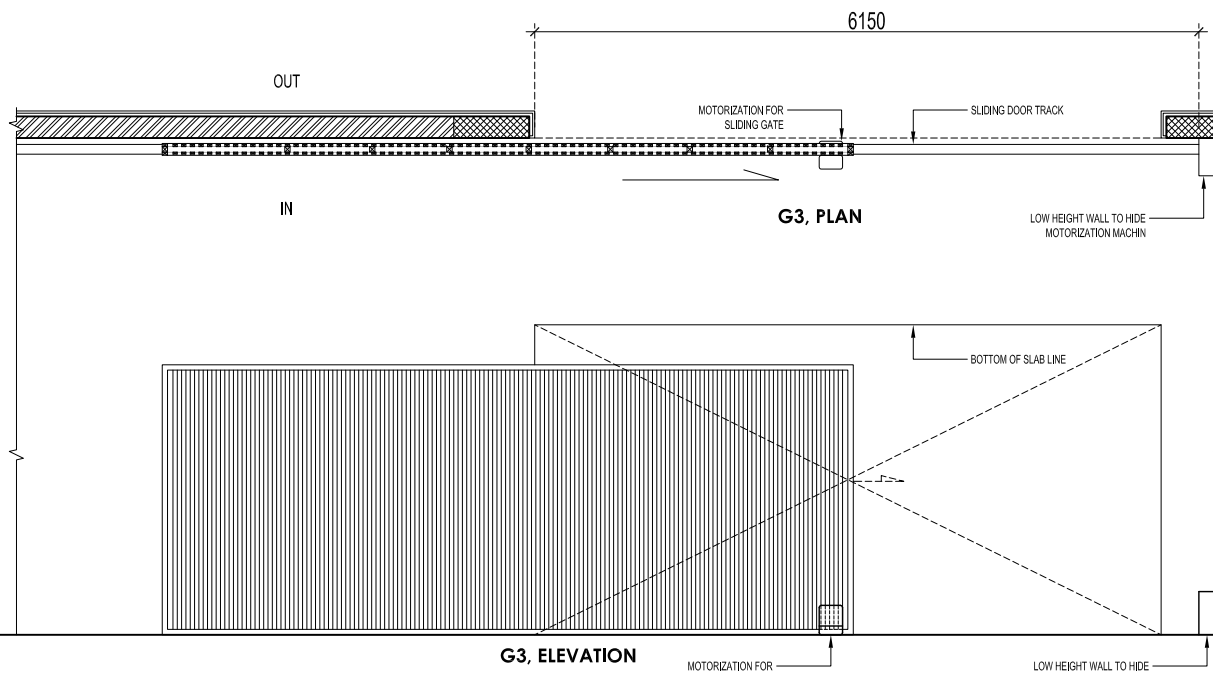



G3, ELEVATION		MOTORIZATION FOR SLIDING GATE
	DOOR NO.	G3
	DOOR TYPE	STEEL DOOR PANEL & FRAME SINGLE SLIDING PANEL
	DIMENSION	6400mm (H) x 1000mm (W)
	QUANTITY	1 - SETS (VERIFY PLAN) A=16,00m²
	U-V/VALUE	---
	DESCRIPTION	HOLLOW CORE PANEL STEEL TUBE 50x50mm, STEEL SHEET 3mm 20x40mm PAINTED STEEL LOUVERS FROM BOTH SIDE WITH SLIDING TRACK
	OTHERS	REMOTE CONTROLLED SYSTEM

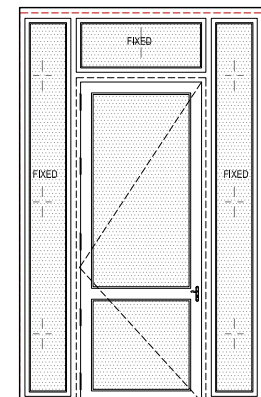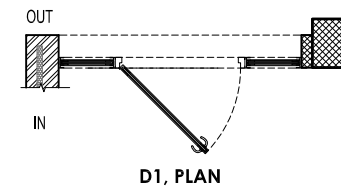



D1, ELEVATION		
DOOR NO.	D1	
DOOR TYPE	EXTERNAL DOOR SINGLE HINGED & 3 FIXED PANELS	
DIMENSION	3600mm (H) x 2250mm (W)	
QUANTITY	1 - SETS (VERIFY PLAN)	A=8,10m²
U-VALUE	2.595	
DESCRIPTION	BY I.D.	

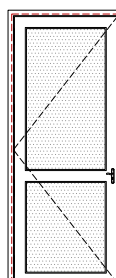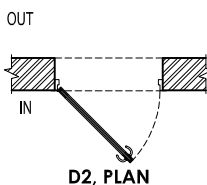



D2, ELEVATION		
DOOR NO.	D2	
DOOR TYPE	EXTERNAL ALUMINUM DOOR SINGLE HINGED PANEL	
DIMENSION	2500mm (H) x 1000mm (W)	
QUANTITY	5 - SETS (VERIFY PLAN)	A=2.50m ²
U-VALUE	2.595	
DESCRIPTION	POWDER COATED OR ANODIZED ALUMINUM FRAME (10x4cm) ALUMINUM PANEL DOOR 6x12x6mm DOUBLE GLAZE TINTED PANEL GLASS WITH ALUMINUM PIVOTS 4 NO. ALUMINUM IRONMONGERY (TO BE SPECIFIED)	

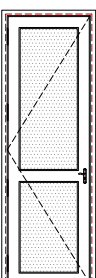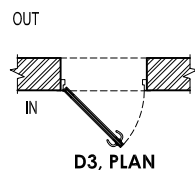



D3, ELEVATION		
DOOR NO.	D3	
DOOR TYPE	EXTERNAL ALUMINUM DOOR SINGLE HINGED PANEL	
DIMENSION	2500mm (H) x 800mm (W)	
QUANTITY	2 - SETS (VERIFY PLAN)	A=2.00m ²
U-VALUE	2.595	
DESCRIPTION	POWDER COATED OR ANODIZED ALUMINUM FRAME (10x4cm) ALUMINUM PANEL DOOR 6x12x6mm DOUBLE GLAZE TINTED PANEL GLASS WITH ALUMINUM PIVOTS 4 NO. ALUMINUM IRONMONGERY (TO BE SPECIFIED)	

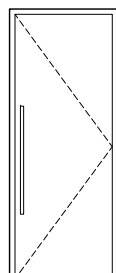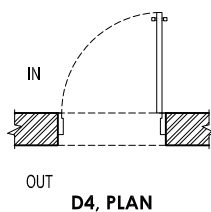



D4, ELEVATION		
DOOR NO.	D4	
DOOR TYPE	WOOD DOOR PANEL SINGLE HINGED PANEL	
DIMENSION	2500mm (H) x 1000mm (W)	A=2.50m ²
QUANTITY	6 - SETS (VERIFY PLAN)	
U-VALUE	2.595	
DESCRIPTION	BY I.D.	

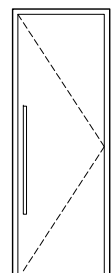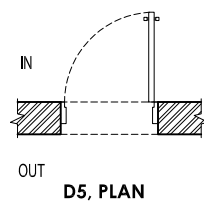

	D5, ELEVATION	
DOOR NO.	D5	
DOOR TYPE	WOOD DOOR PANEL SINGLE HINGED PANEL	
DIMENSION	2500mm (H) x 900mm (W)	A=2.25m²
QUANTITY	5 - SETS (VERIFY PLAN)	
U-VALUE	2.595	
DESCRIPTION	BY LD.	




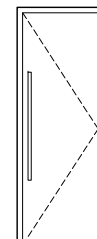
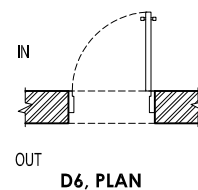


D6, ELEVATION		
DOOR NO.	D6	
DOOR TYPE	WOOD DOOR PANEL SINGLE HINGED PANEL	
DIMENSION	2200mm (H) x 800mm (W)	A=1.76m²
QUANTITY	7 - SETS (VERIFY PLAN)	
U-VALUE	2.595	
DESCRIPTION	BY I.D.	

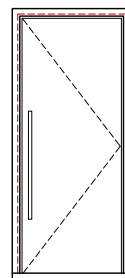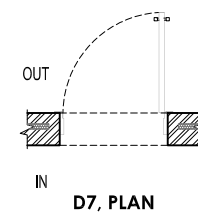

D7, ELEVATION		
DOOR NO.	D7	
DOOR TYPE	STEEL DOOR PANEL & FRAME SINGLE HINGED PANEL	
DIMENSION	2400mm (H) x 1000mm (W)	A=2.40m ²
QUANTITY	1 - SETS (VERIFY PLAN)	
U-VALUE	2.595	
DESCRIPTION	PRE ENGINEERED STEEL DOOR WITH STAINLESS STEEL PIVOTS 4 NO. AND STAINLESS STEEL HANDLE	

SIMA MALAK + ALSSAMOURÉ DESIGN ASSOCIATES P.O. Box 15707 - Riyadh 11454 KSA Tel. 01 441 4963 - Fax. 01 441 3867 simals@simals.com			
المكتب الاستشاري الرئيسي شركة المطورون العرب للاستشارات الهندسية ترخيص رقم ٥١١٠٠٠٢٤٥٦			
الاعتماد	الدرجة	التخصص	المهندس
٣٧٥٦٦	مستشار	عمارة	محمد جميل اسماعيل
٣٧٦٠١	محترف	هندسة مدنية	غيداردو كايانيل كانياغان
٣.٣٥٧٨	هندسة معمارية	هندسة معمارية	ابن عماد جميل
٨٢٢١	مستشار	تصميم كهربيا	اسامة طاهر سعيد عرب هندسة كهربيا
٧٤٢٥٣	محترف	تصميم ميكانيكا	اص على القامدس
2-104 DESIGNER: JESSIEBET SIMA MALAK/DESIGN ASSOCIATES/RIYADH-11454 KSA/15707			
PRIVATE VILLA IN RIYADH, KSA			
OWNER NAME SIMA MALAK		1	DESIGN CONCEPT
		2	PRELIM DESIGN
		3	DESIGN DEVELOP
(VILLA-1) DOOR DETAILS		4	WORKING DWG.
		5	SHOP DRAWING
		6	AS BUILT DWG.
PROJ. NO. P-2024-07	DWG. NO. AR-13	DATE: jun2024	SCALE: 1:50

     A rectangle with its two diagonals intersecting at the center. The rectangle is oriented horizontally. The diagonals are represented by thin black lines that cross each other at the exact center of the rectangle. The intersection point is located at the center of the image.

P.O. Box 15707 - Riyadh 11454 KSA
Tel. 01 441 4963 - Fax. 01 441 3867
simals@simals.com

المكتب الاستشاري الرئيسي

شركة المطورون العرب للاستشارات الهندسية

ترخيص رقم ٥١١...٢٤٥٦

المهندس	الدرجة	اللقب
معد جبيل اسماعيل	عمارة	مستشار ١٣٥٦
غيزارو كاكابازا كاكابازان	مدنية	مستشار ١٣٦١
اين صافير عرب	هندسة	مستشار ١٣٥٧أ
اسماء طاهر صير	هندسة كبريا	مستشار ١٣٦١
اسى طر الغامدي	هندسة ميكانيكية	مستشار ١٣٥٣

SIMA DESIGN P-202807-SIMA MALAKUD6-WORKING DRAWING-VILLA TLOCO 3

PRIVATE VILLA IN RIYADH, KSA

OWNER NAME	SIMA MALAK	1	DESIGN CONC
		2	PRELIM. DES
		3	DESIGN DEVEL
(VILLA-1) WINDOW DETAILS 2	DRAWING TITLE	4	WORKING DW
		5	SHOP DRAWING
		6	AS BUILT DW

PROJ. NO. P-2024-07	DWG. NO. AR-15	DATE: jun2024	SCALE/A2: 1:50
------------------------	--------------------------	------------------	-------------------



FINISHING LEGEND :

- F1 600 x 1200 x 20mm THICK TRAVERTINE MARBLE OR PORCELAIN TILE TRAVERTINE EFFECT
- F2 TEXTURED PAINT ON CEMENT (COLOR IVORY WHITE OR AS SPECIFIED)
- F3 TEXTURED PAINT ON CEMENT (COLOR GRAY OR AS SPECIFIED)
- F4 1200 x 2000 x 20mm THICK GRAY COLOR MARBLE STONE OR PORCELAIN TILE STONE EFFECT
- F5 600x1200mm PORCELAIN TILES (OR AS SPECIFIED)
- F6 PEBBLES (OR AS SPECIFIED)
- F7 300mm x 1200 JURUPA JP04 CAMP (MIRAGE) (OR AS SPECIFIED)
- F8 600x600mm PORCELAIN TILES (OR AS SPECIFIED)
- F9 100x100mm PAVING TILE (OR AS SPECIFIED)

ELECTRICAL LEGEND:

- UP LIGHT
- FLOOR LIGHT LIGHT
- STRIP LIGHT @ ROOF,STEP,PLANTER BOX ETC.
- OUTDOOR FLOOR LAMP

SIMA MALAK + ALSSAMOURÉ
DESIGN ASSOCIATES
P.O. Box 15707 - Riyadh 11454 KSA
Tel. 01 441 4963 - Fax. 01 441 3867
simals@simals.com

المكتب الاستشاري الرئيسي			
شركة المطورون العرب للاستشارات الهندسية			
ترخيص رقم ٠١١٠٠٠٢٤٥٦			
الاعتماد	الدرجة	التخصص	المهندس
٢٧٥٩٦	مستشار	عمارة	محمد جميل اساميل
٣٧١٠	محترف	هندسة مدنية	غيداردو كايانيل
٣٠٣٧٨	رسم مخططات معمارية	هندسة معمارية	ايمى عماد جميل كايانيل
٨٦٦١	تصميم كهرباء	اسماء طاهر سيد عرب هندسة كهرباء	مشار
٧٤٣٣٢	تصميم ميكانيكا	اص على العبدى	هندسة ميكانيكا

PRIVATE VILLA
IN RIYADH, KSA

OWNER NAME		1 DESIGN CONCEPT	
SIMA MALAK		2 PRELIM. DESIGN	
		3 DESIGN DEVELOP.	
		4 WORKING DWG.	
(VILLA-1&2) LANDSCAPE LAYOUT PLAN		5 SHOP DRAWING	
		6 AS BUILT DWG.	
PROJ. NO. P-2024-07	DWG. NO. AR-16	DATE jun2024	SCALE: 1:100