


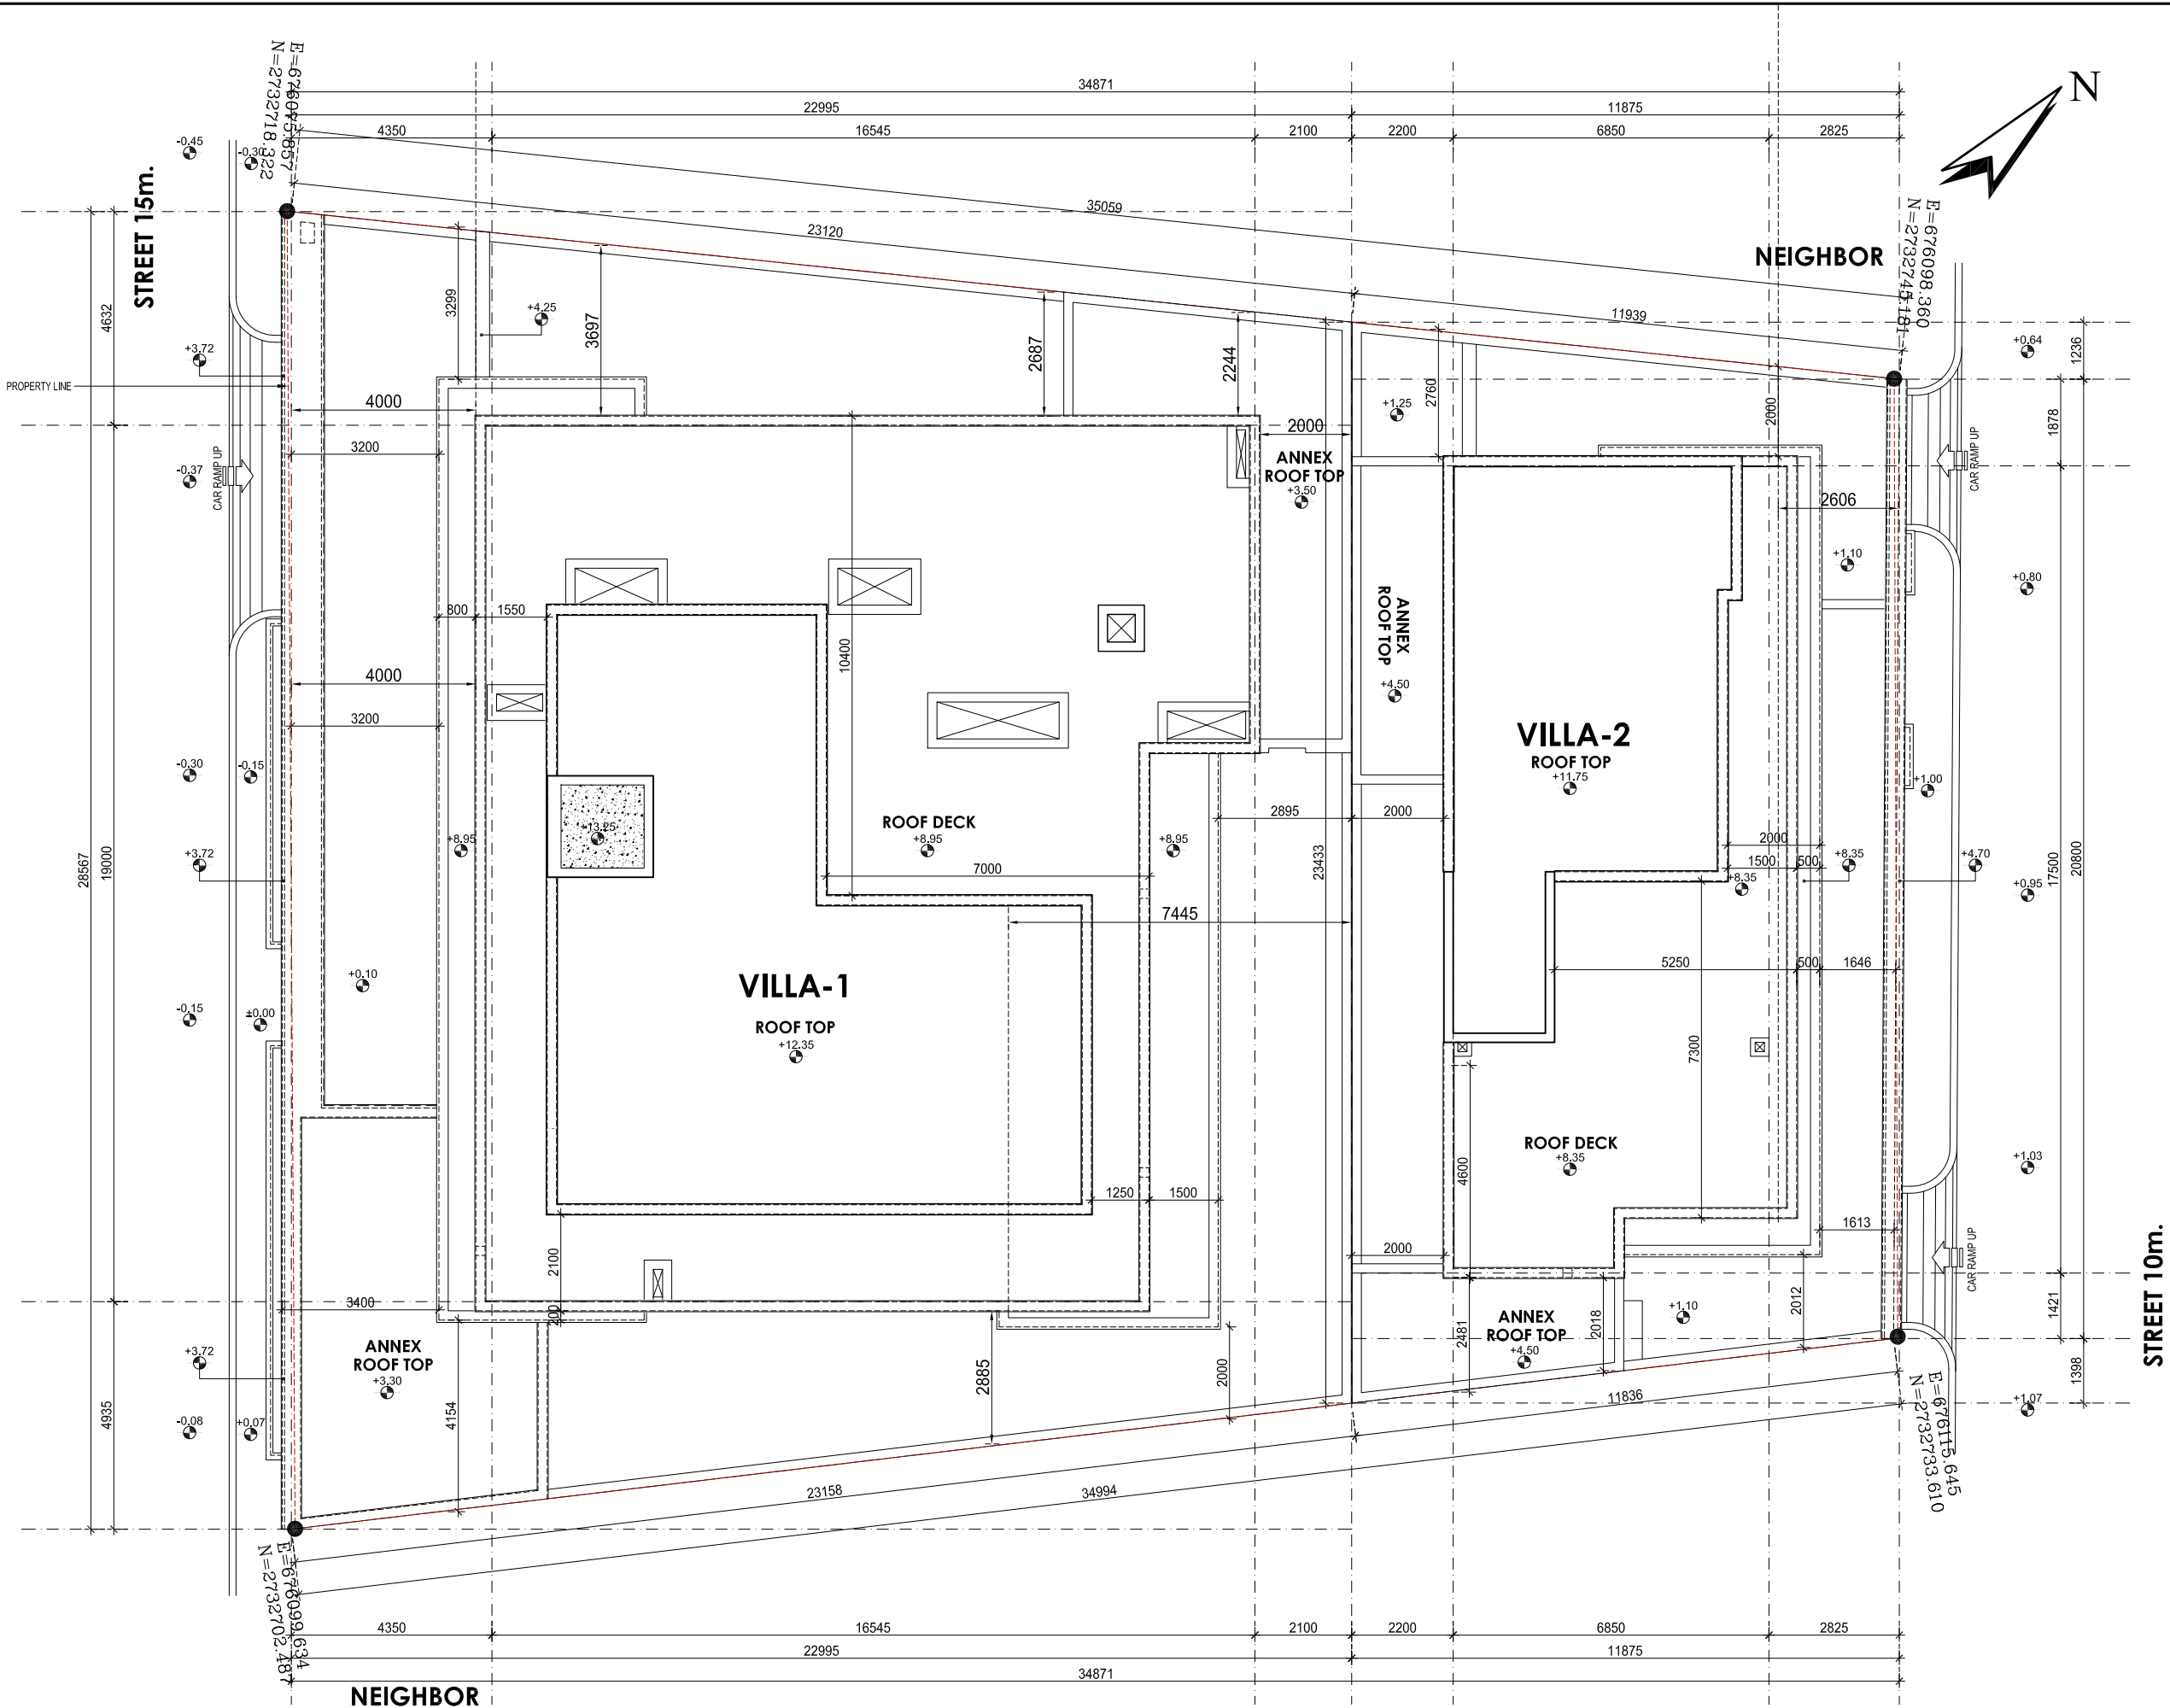

VILLA -1			مساحة الأرض
866.65 m ²			LAND AREA
PERCENTAGE	AREA (m ²)	مساحة الأرض	FLOOR AREA
30.71%	266.18	الأرض	GROUND FLOOR
36.68%	317.94	الاول	FIRST FLOOR
37.59%	119.53	سقف السطح	ROOF ANX
6.12%	53.11	الملاحق	ANNEXES
	756.76	المجموع	TOTAL

VILLA -2			مساحة الأرض
866.65 m ²			LAND AREA
PERCENTAGE	AREA (m ²)	مساحة الأرض	FLOOR AREA
15.10%	130.87	الأرض	GROUND FLOOR
15.65%	135.71	الاول	FIRST FLOOR
49.9%	67.73	سقف السطح	ROOF ANX
2.11%	18.30	الملاحق	ANNEXES
	352.60	المجموع	TOTAL

TOTAL VILLAS			مساحة الأرض
866.65 m ²			LAND AREA
PERCENTAGE	AREA (m ²)	مساحة الأرض	FLOOR AREA
45.81%	397.05	الأرض	GROUND FLOOR
52.34%	453.65	الاول	FIRST FLOOR
41.27%	187.26	سقف السطح	ROOF ANX
8.23%	71.41	الملاحق	ANNEXES
	1,109.37	المجموع	TOTAL

السمال	ممر مشاة عرض ١٠ م	٢,٦٠
الشرق	قطعة رقم ١٣٩	٢,٠١
الغرب	قطعة رقم ١٤٢	٢,٣٠
الجنوب	شارع عرض ١٠ م	٤,٠٠
NORTH		2.60
EAST		2.01
WEST		2.30
SOUTH		4.0

المالك	سماء سميع الحق ملك
القطعة	١٤١ أو ١٤٢
المخطط	٨٥٦
الحي	الرياض

SIMA MALAK + ALSSAMOURE
DESIGN ASSOCIATES

P.O. Box 15707 - Riyadh 11454 KSA
Tel. 01 441 4963 - Fax. 01 441 3867
simals@simals.com

المكتب الاستشاري الرئيسي

شركة المطورون العرب للاستشارات الهندسية

ترخيص رقم ٠١١-٢٤٥٦



الاعتماد	الدرجة	التخصص	المهندس
٢٧٥٩٦	مستشار	عمارة	محمد جميل اسماعيل
٣٧١٠١	مختبر	هندسة مدنية	غيداردو كاباتيللا كاباتيلان
٣٠٣٧٨	رسم مخططات معمارية	ايمى عماد جميل	هندسة معمارية
٨٦٦١	تصميم كهرباء	اسماء طاهر سيد عرب	هندسة كهرباء
٧٥٧٣٢	تصميم ميكانيكا	اص على الفهدى	هندسة ميكانيكا

2-01 DESIGN/SECURITY SIMA MALAK+ALSSAMOURE/RIYADH/RIYADH/AL-14/14/00000

PRIVATE VILLA
IN RIYADH, KSA

OWNER NAME	SIMA MALAK
DRAWING TITLE	SITE DEVELOPMENT LAYOUT PLAN
PROJ. NO.	P-2024-07
DWG. NO.	AR-01
DATE	jun2024
SCALE:	1:100

1	DESIGN CONCEPT
2	PRELIM. DESIGN
3	DESIGN DEVELOP.
4	WORKING DWG.
5	SHOP DRAWING
6	AS BUILT DWG.

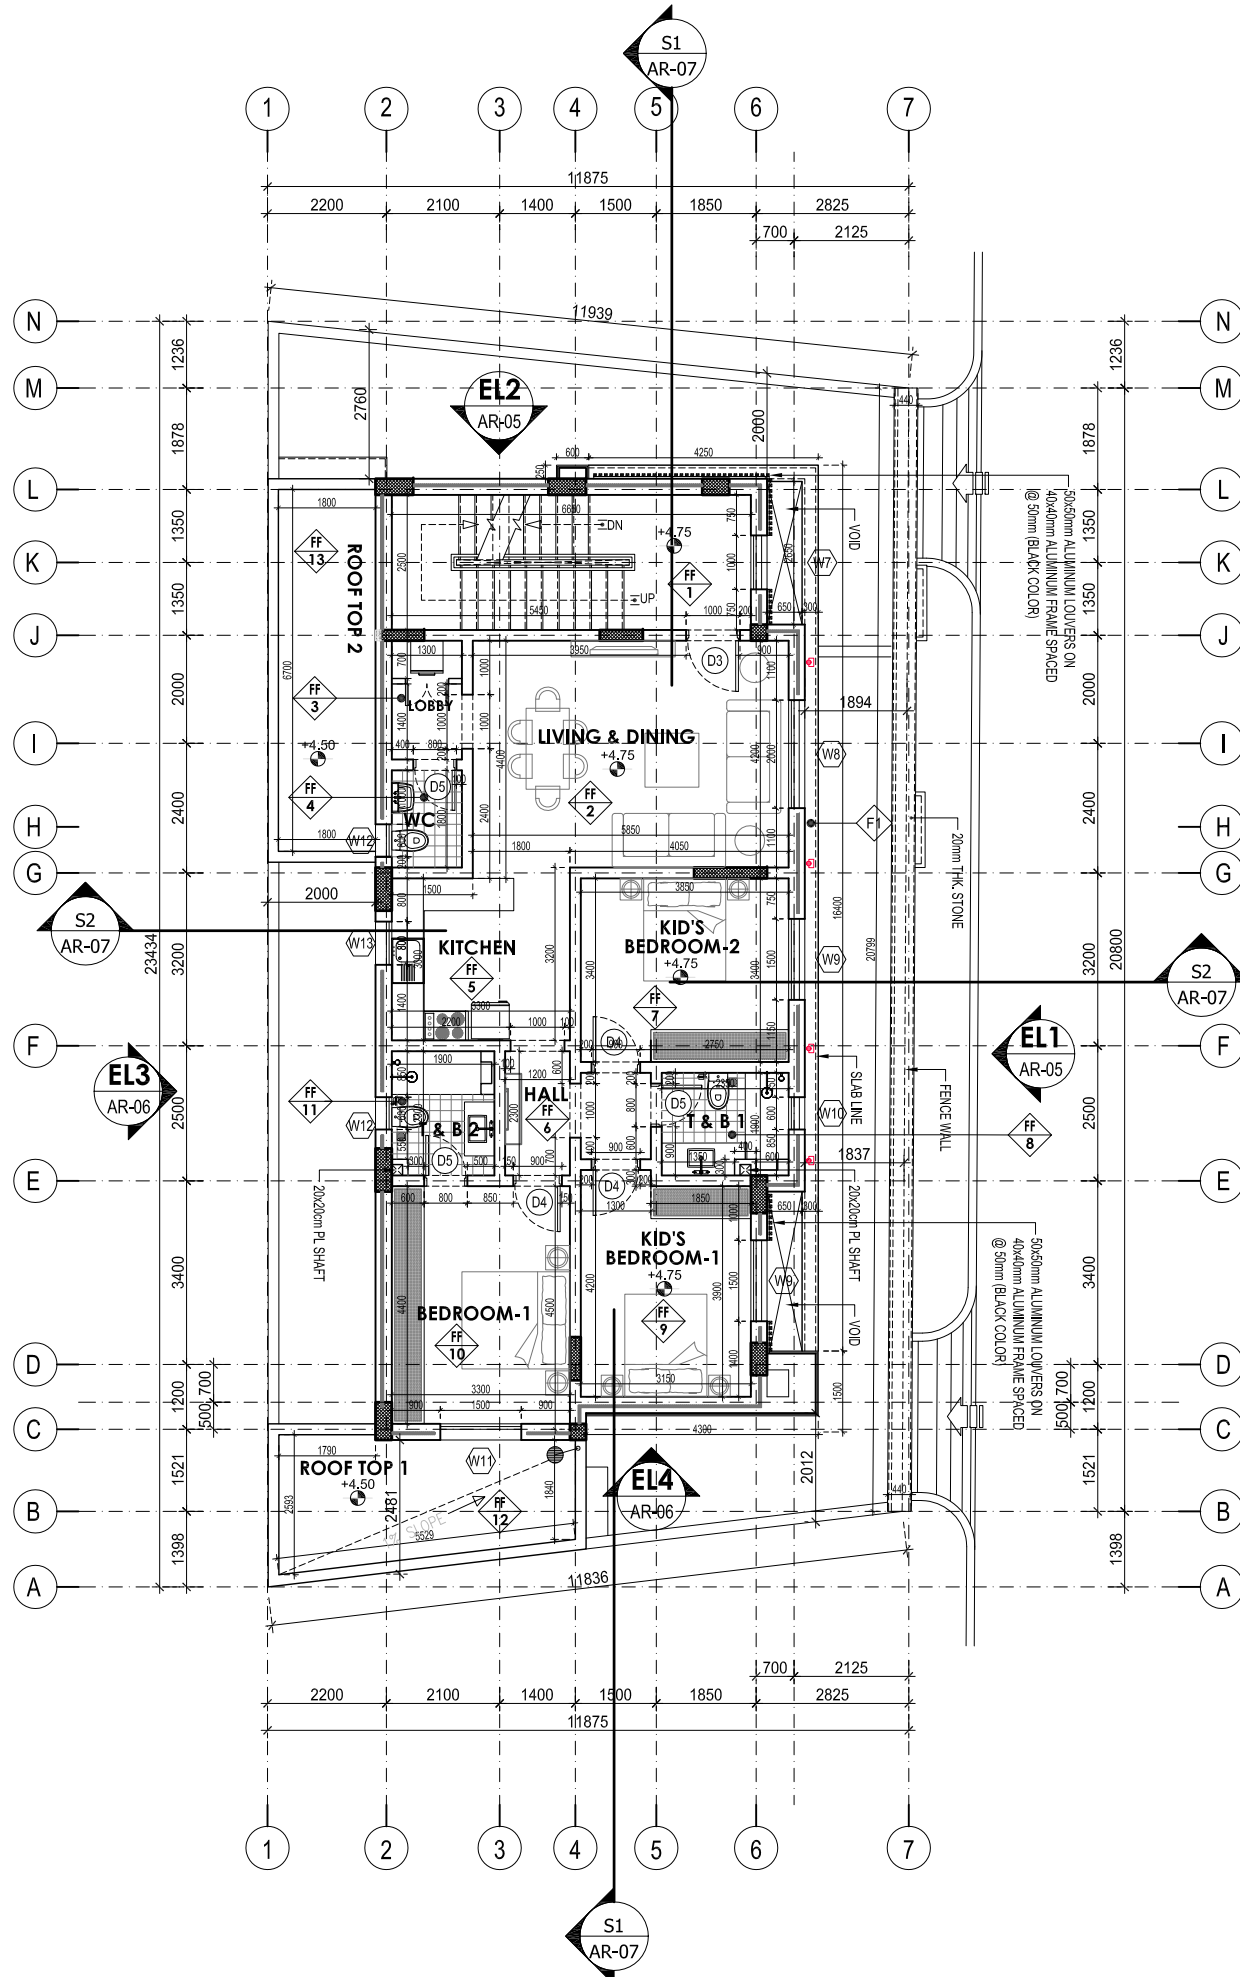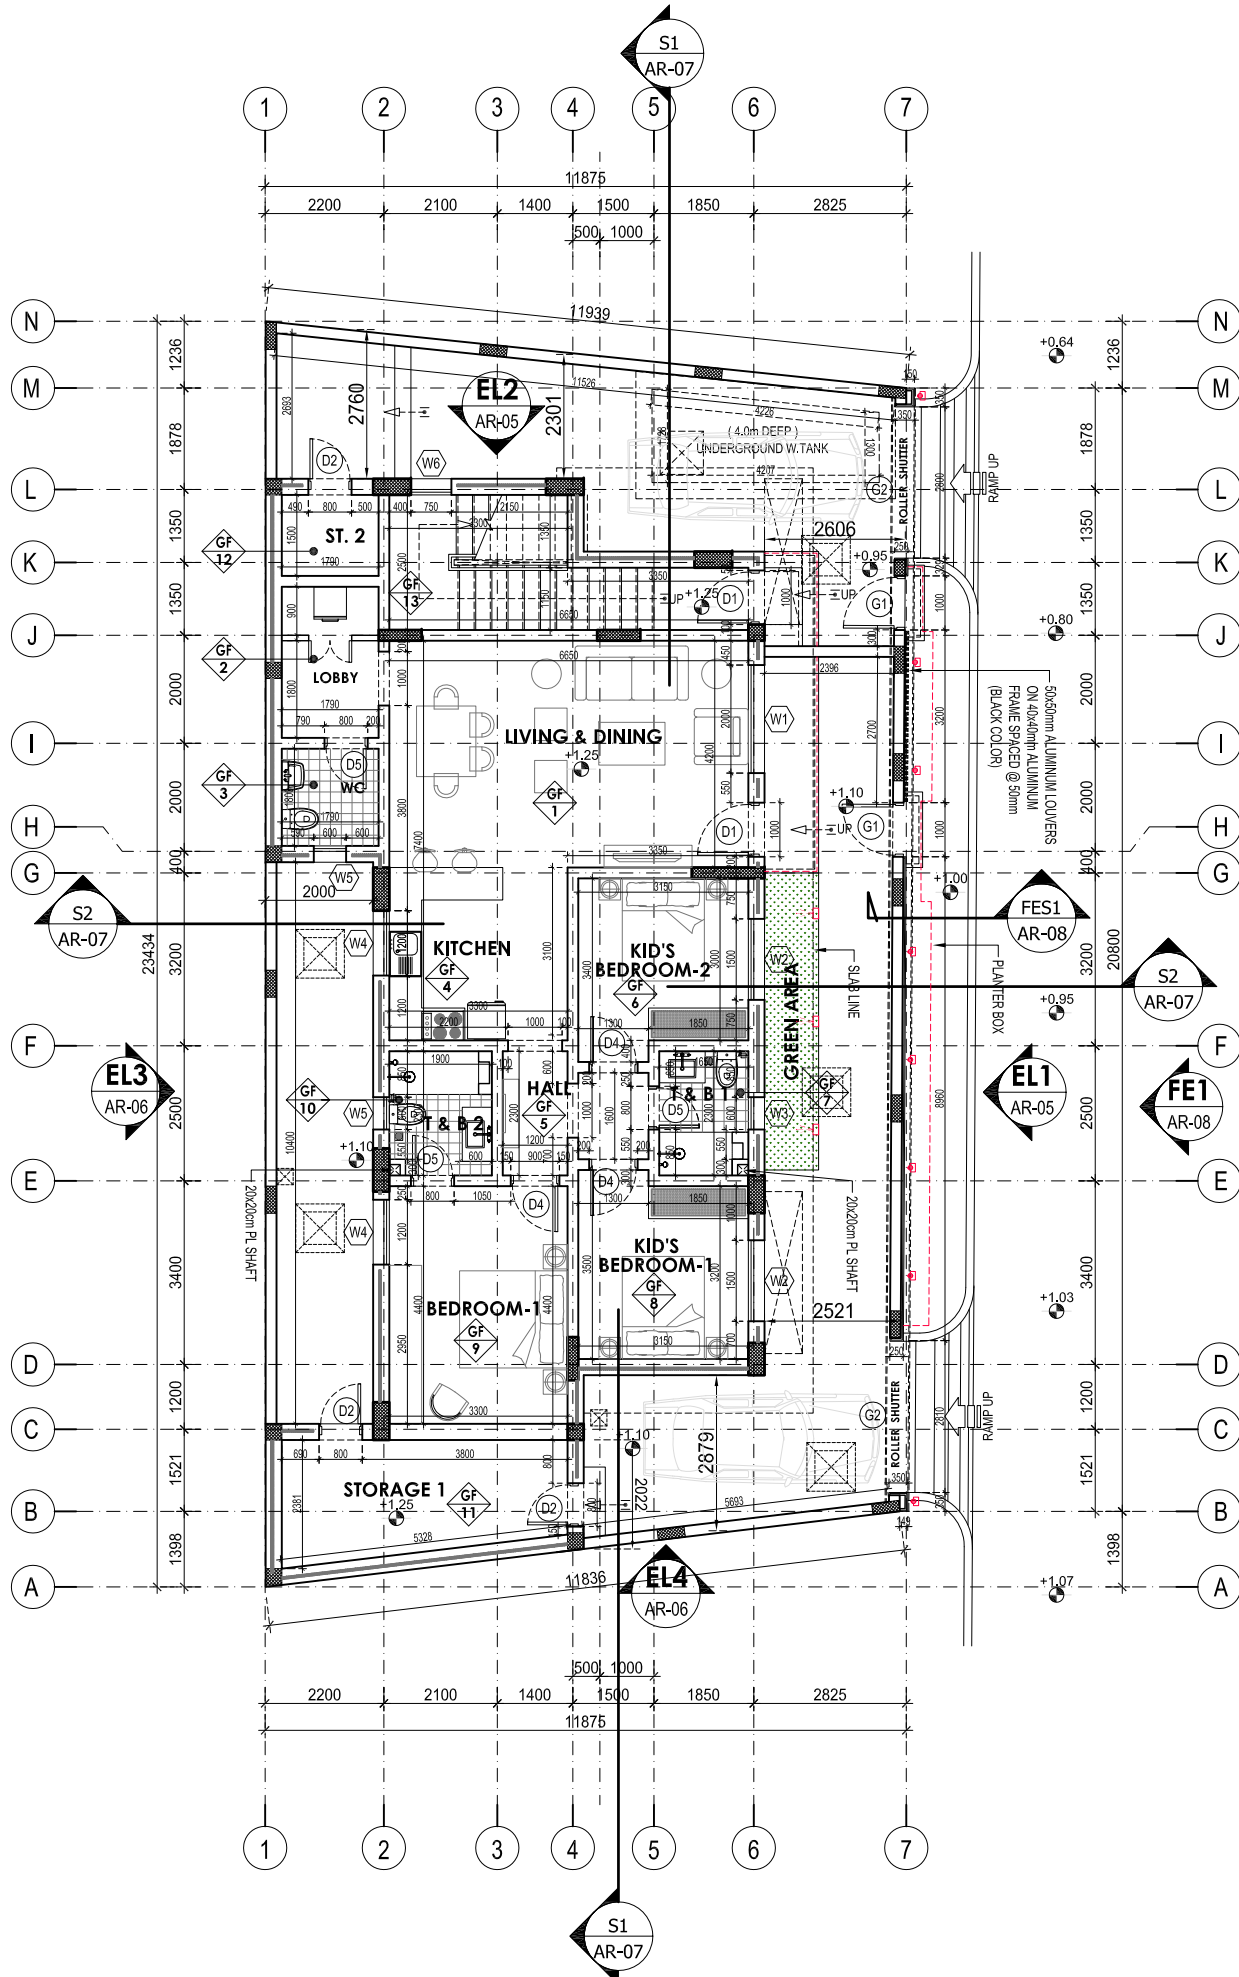

GENERAL NOTES

- ALL LEVELS ARE SHOWN IN METERS AND RELATED TO DATUM LEVEL OF +1.00 (STREET LEVEL) IS EQUAL TO (800.55) OF CORRESPONDING LEVEL ON TOPOGRAPHICAL SURVEY DRAWING. DIMENSIONS ARE SHOWN IN MILLIMETERS.
- ALL INTERNAL PARTITIONS ARE 200mm THICK AND ALL EXTERNAL WALLS ARE 450/350mm THICK UNLESS OTHERWISE SPECIFIED.
- DETAIL DRAWINGS SHOWN IN CIRCLES IN THIS DRAWING SHALL BE REFERRED TO FOR MORE INFORMATION PERTAINING TO THE ENCIRCLED AREAS.
- WALL DIMENSIONS DO NOT INCLUDE RENDER, PLASTER FINISHES OR PRE-CAST CONCRETE PLINTH UNLESS OTHERWISE INDICATED.
- DOORS AND ARCHES ARE SET OUT:
 - ON THE CENTER OF THE WALL OR
 - FROM A 200mm NIB OR
 - AS DIMENSIONED
- ALL INTERNAL WALLS SHALL BE TAKEN TO THE UNDERSIDE OF THE SOFFIT OR BEAM UNLESS OTHERWISE INDICATED.
- ALL FALLS TO ROOFS, TERRACES INCLUDING THE FALL ON THE MAIN ENTRANCE WALKWAY SHALL BE 0.50% MINIMUM.
- ALL CHANGES IN DIRECTION OF PLASTER AND RENDER SHALL BE FORMED BY THE APPROPRIATE GALVANIZED METAL BEAD.
- LEVELS OF EXTERNAL FLOOR FINISHES ARE SHOWN AS NOMINAL FINISHES ADJACENT TO BUILDING SHALL BE LAID TO FALL AWAY FROM THE BUILDING.
- ALL SHOP DRAWINGS, SAMPLES OR CATALOG CUTS TO BE APPROVED BY THE ARCHITECT BEFORE THE FINAL EXECUTION.
- THE CONTRACTOR SHALL SUBMIT SAMPLES & SHOP DRAWINGS FOR ALL EXTERIOR CLADDING FINISHES PRIOR TO ANY INSTALLATIONS.

SYMBOL & LEGEND

	LEVEL INDICATION
	FF- BASEMENT FLOOR
	GF- GROUND FLOOR
	FF- FIRST FLOOR
	ROOM NUMBERING
	BUILDING NUMBER
	D1- DOOR TYPE
	W1- WINDOW TYPE
	FF- EXTERNAL FINISHING
	STRUCTURAL COLUMN
	OPENING ABOVE

SIMA MALAK + ALSSAMOURÉ DESIGN ASSOCIATES

P.O. Box 15707 - Riyadh 11454 KSA
Tel. 01 441 4963 - Fax. 01 441 3867
simals@simals.com

المكتب الاستشاري الرئيسي

شركة المطورون العرب للاستشارات الهندسية

ترخيص رقم ٥١١-٢٤٥٦



الاعتماد	الدرجة	التخصص	المهندس
٢٧٩٦٦	مستشار	عمارة <td>محمد جميل اساميل</td>	محمد جميل اساميل
٣٧١٠١	محترف	هندسة مدنية <td>غيدارد كاتانيل</td>	غيدارد كاتانيل
٣٠٣٧٨	مستشار	هندسة معمارية <td>ابن عماد جميل</td>	ابن عماد جميل
٨٦٦١	مستشار	تصميم كهرباء <td>اسامة طاهر سيد عرب هندسة كهرباء</td>	اسامة طاهر سيد عرب هندسة كهرباء
٧٤٧٣٢	محترف	تصميم ميكانيكا <td>اص على العبدى هندسة ميكانيكا</td>	اص على العبدى هندسة ميكانيكا

PRIVATE VILLA IN RIYADH, KSA

OWNER NAME	1 DESIGN CONCEPT
SIMA MALAK	2 PRELIM. DESIGN
	3 DESIGN DEVELOP.
	4 WORKING DWG.
(VILLA-2) GROUND & FIRST FLOOR LAYOUT PLAN	5 SHOP DRAWING
	6 AS BUILT DWG.

PROJ. NO.	DWG. NO.	DATE	SCALE:
P-2024-07	AR-03	jun2024	1:100

GP/PROJECTS - CURRENT/ASPM111, DES-Designs/Drawings by others/1, Consultation/2025.08.25 - Add: (Asheh) - W/ASIMA MALAK VILLA/2024/VILLA-2-AR-03.dwg (AR-03), Plotted by Mudasar, Sep 28, 2025 - 2:25pm

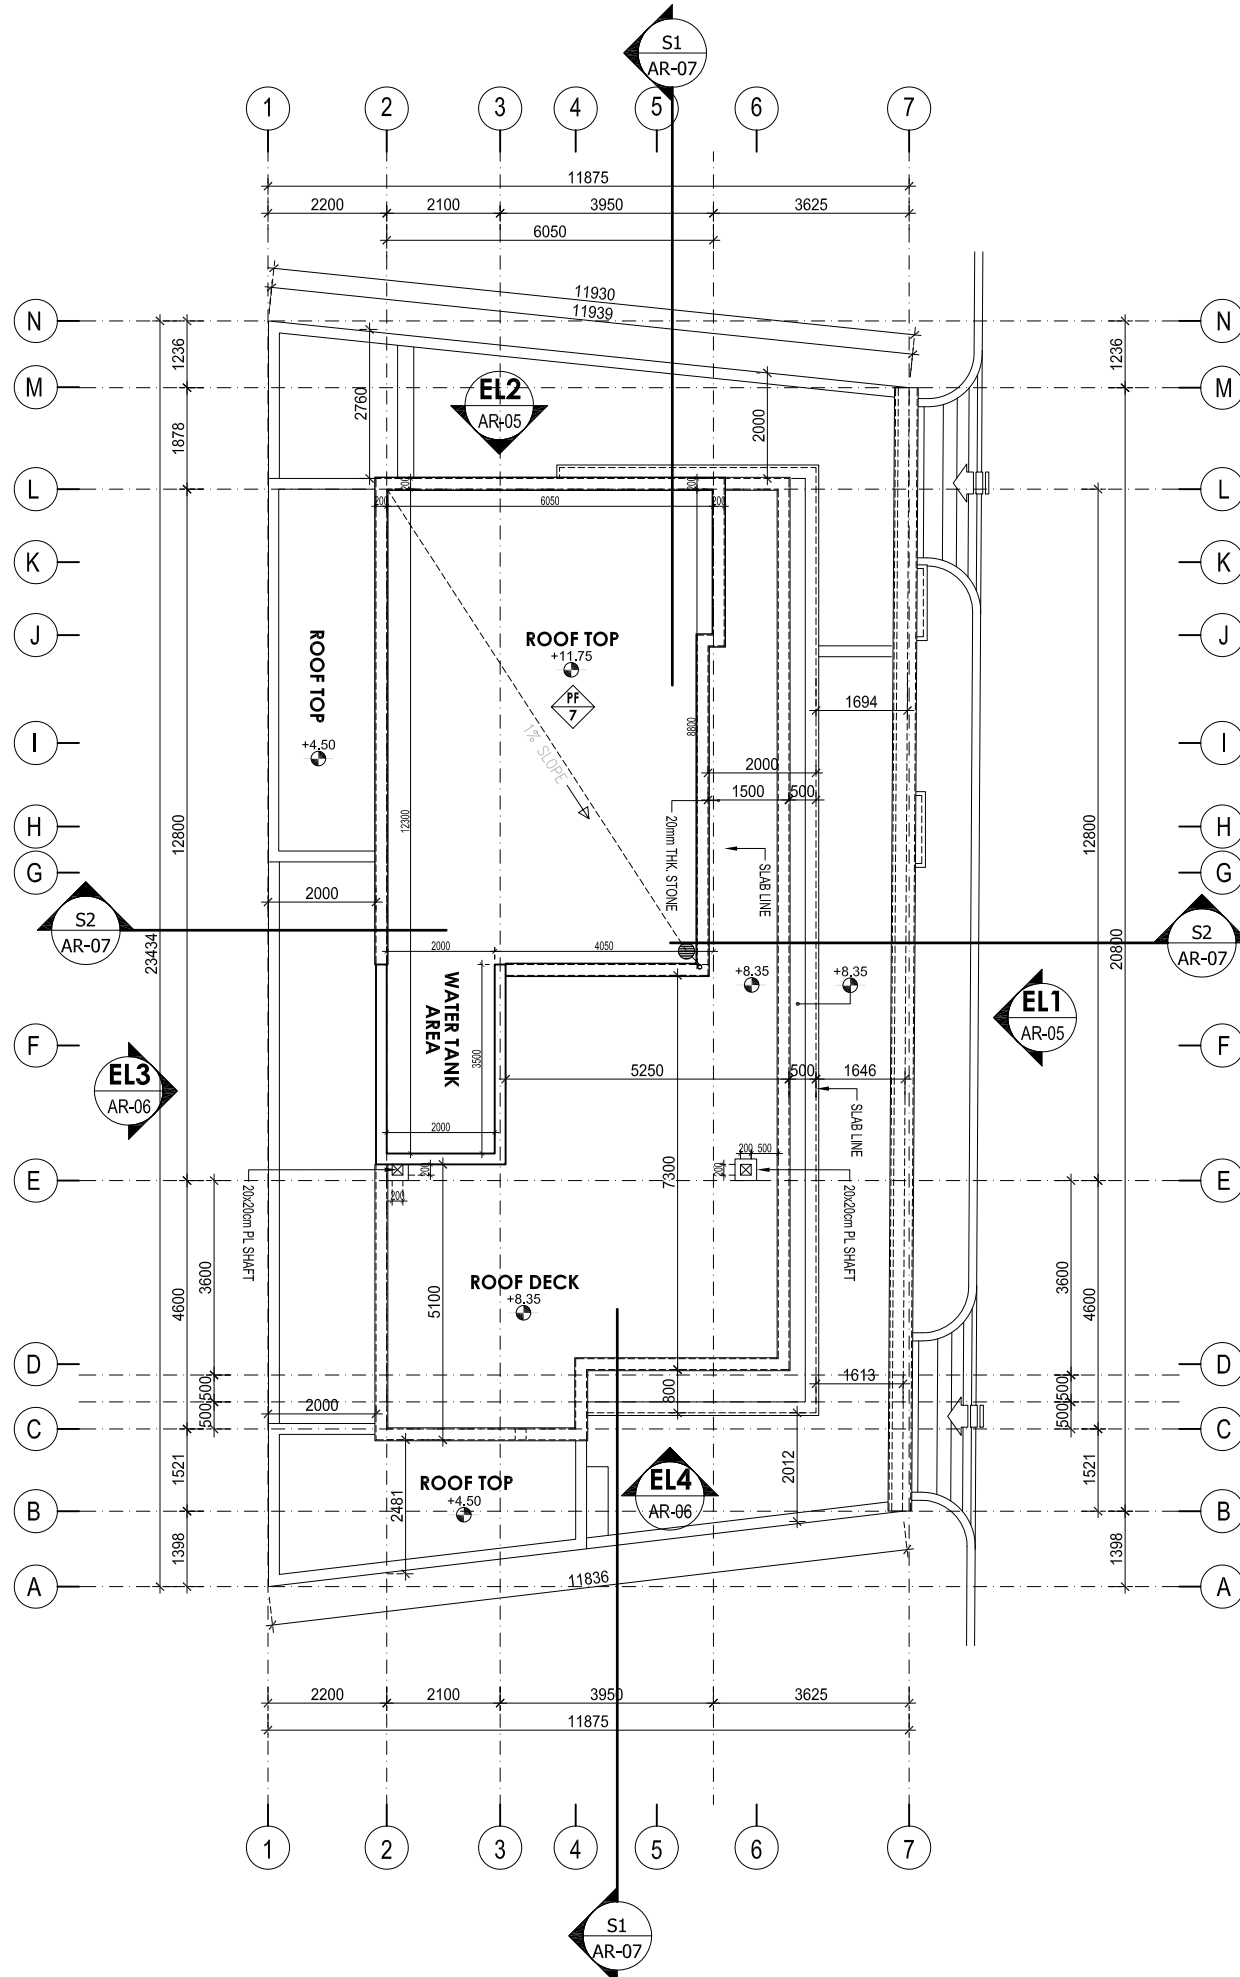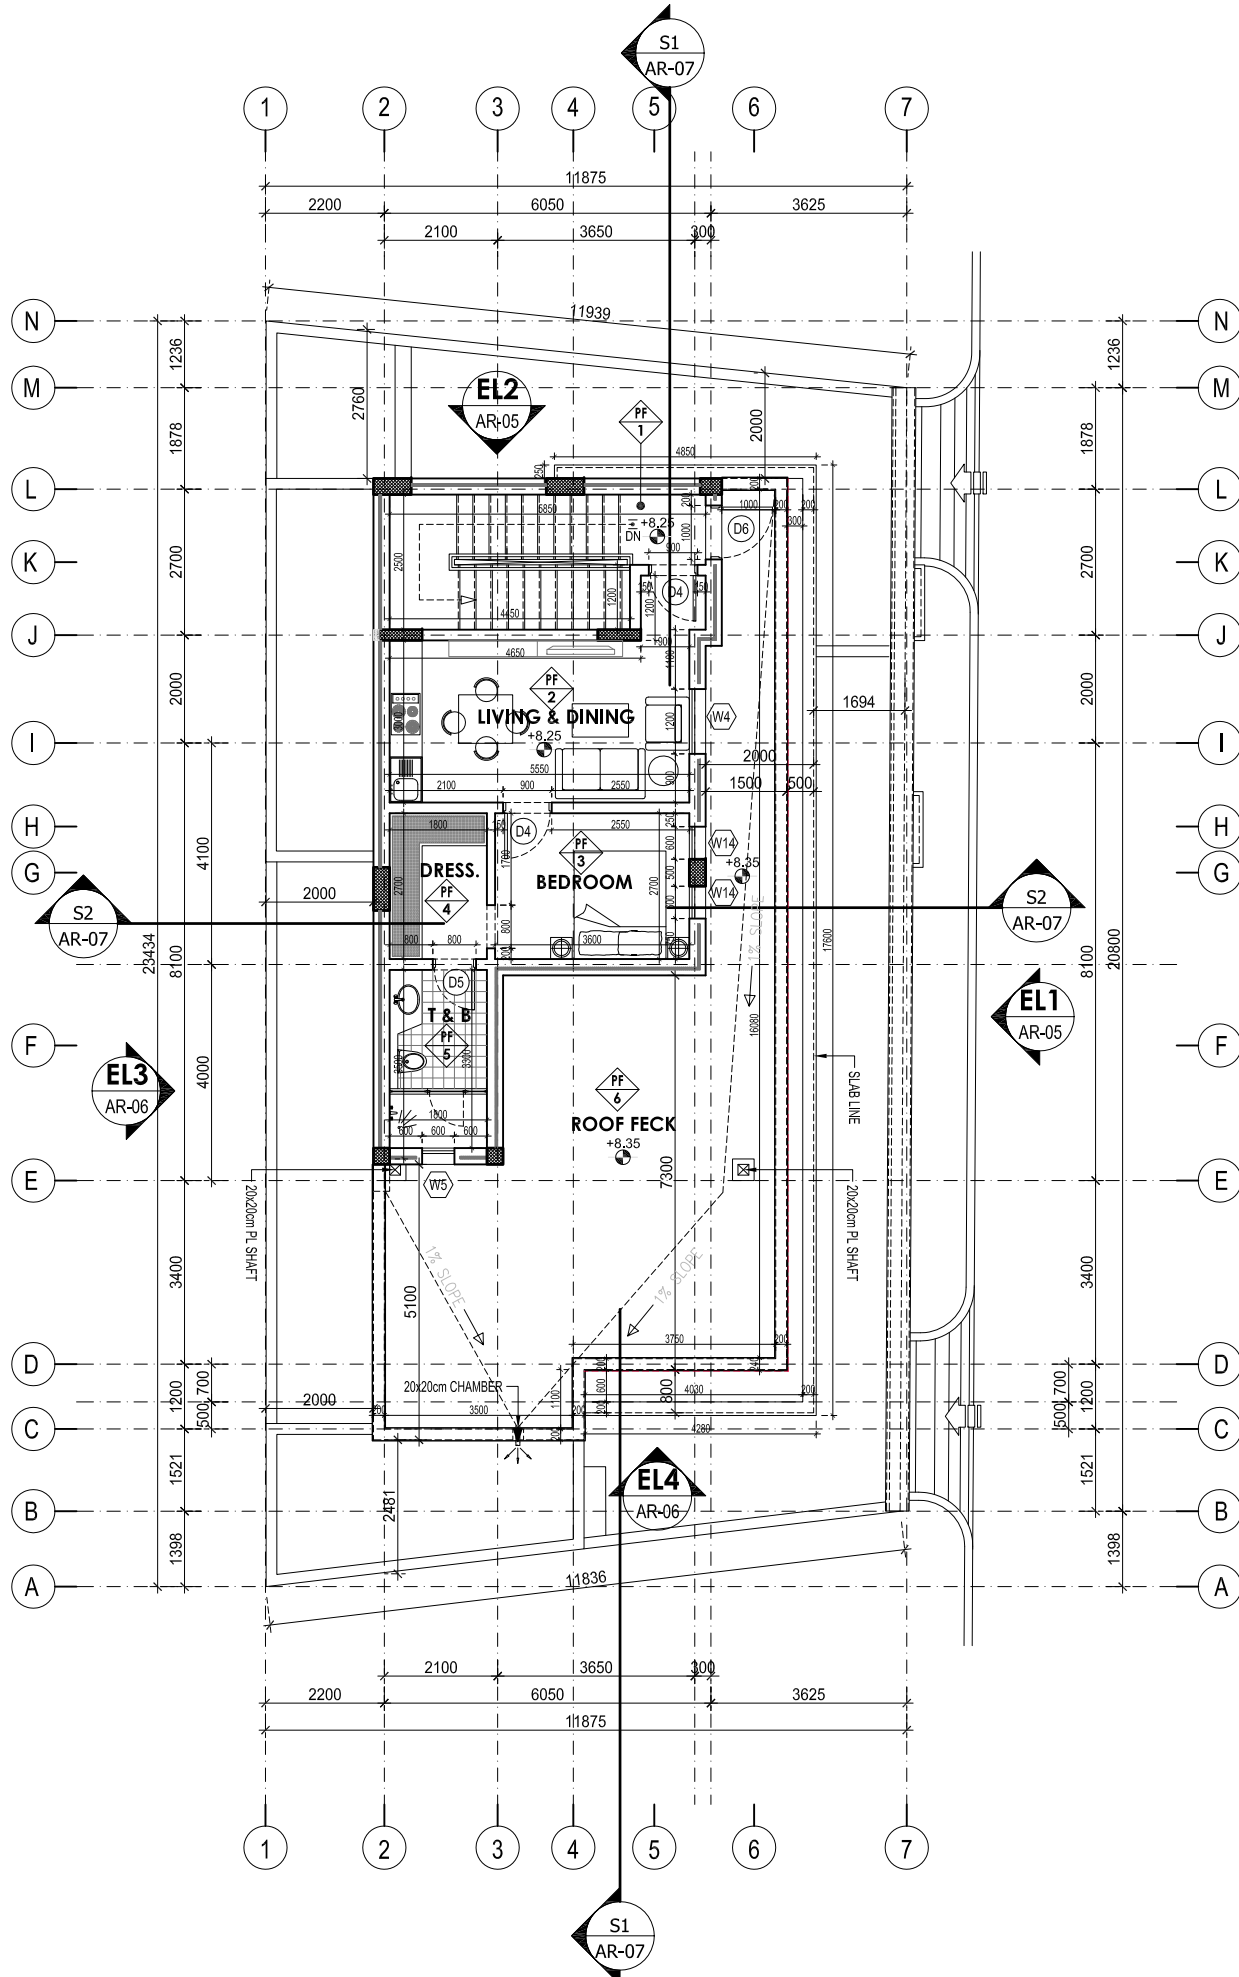

GENERAL NOTES

- ALL LEVELS ARE SHOWN IN METERS AND RELATED TO DATUM LEVEL OF +1.00 (STREET LEVEL) IS EQUAL TO (800.55) OF CORRESPONDING LEVEL ON TOPOGRAPHICAL SURVEY DRAWING. DIMENSIONS ARE SHOWN IN MILLIMETERS.
- ALL INTERNAL PARTITIONS ARE 200mm THICK AND ALL EXTERNAL WALLS ARE 450/350mm THICK UNLESS OTHERWISE SPECIFIED.
- DETAIL DRAWINGS SHOWN IN CIRCLES IN THIS DRAWING SHALL BE REFERRED TO FOR MORE INFORMATION PERTAINING TO THE ENCIRCLED AREAS.
- WALL DIMENSIONS DO NOT INCLUDE RENDER, PLASTER FINISHES OR PRE-CAST CONCRETE PLINTH UNLESS OTHERWISE INDICATED.
- DOORS AND ARCHES ARE SET OUT:
 - ON THE CENTER OF THE WALL OR
 - FROM A 200mm NIB OR
 - AS DIMENSIONED
- ALL INTERNAL WALLS SHALL BE TAKEN TO THE UNDERSIDE OF THE SOFFIT OR BEAM UNLESS OTHERWISE INDICATED.
- ALL FALLS TO ROOFS, TERRACES INCLUDING THE FALL ON THE MAIN ENTRANCE WALKWAY SHALL BE 0.50% MINIMUM.
- ALL CHANGES IN DIRECTION OF PLASTER AND RENDER SHALL BE FORMED BY THE APPROPRIATE GALVANIZED METAL BEAD.
- LEVELS OF EXTERNAL FLOOR FINISHES ARE SHOWN AS NOMINAL FINISHES ADJACENT TO BUILDING SHALL BE LAID TO FALL AWAY FROM THE BUILDING.
- ALL SHOP DRAWINGS, SAMPLES OR CATALOG CUTS TO BE APPROVED BY THE ARCHITECT BEFORE THE FINAL EXECUTION.
- THE CONTRACTOR SHALL SUBMIT SAMPLES & SHOP DRAWINGS FOR ALL EXTERIOR CLADDING FINISHES PRIOR TO ANY INSTALLATIONS.

SYMBOL & LEGEND

	300mm THK EXTERNAL CONCRETE BLOCK WALL (INSULATED)		LEVEL INDICATION
	200mm THK INTERNAL CONCRETE BLOCK WALL		BASEMENT FLOOR
	100mm THK INTERNAL CONCRETE BLOCK WALL		GROUND FLOOR
	LOW HEIGHT PARTITION WALL		FIRST FLOOR
	REINFORCED CONCRETE		ROOM NUMBERING
	SAND, SCREED		BUILDING NUMBER
	PLASTER OR RENDER		DOOR TYPE
	PAINTED		WINDOW TYPE
	LEVEL ON PLAN		EXTERNAL FINISHING
	LEVEL ON SECTIONS AND ELEVATIONS		STRUCTURAL COLUMN
	UP LIGHT		OPENING ABOVE
	FLOOR LIGHT		
	STRIP LIGHT @ ROOF, STEP, PLANTER BOX ETC.		

SIMA MALAK + ALSSAMOURÉ
DESIGN ASSOCIATES

P.O. Box 15707 - Riyadh 11454 KSA
Tel. 01 441 4963 - Fax. 01 441 3867
simals@simals.com

المكتب الاستشاري الرئيسي
شركة المطورون العرب للاستشارات الهندسية

ترخيص رقم ٢٤٥٦-٠١١


الاعتماد	الدرجة	التخصص	المهندس
٢٧٩٩٦	مستشار	عمارة	محمد جميل اساميل
٣٧١٠١	مختبر	هندسة مدنية	غيدارد كايتيلا
٣٠٣٧٨	رسم مخططات	هندسة معمارية	ابن عماد جميل
٨٦٦١	تصميم كهرباء	اسماء طاهر سعيد	مهندسة كهرباء
٧٤٣٧٢	مختبر	ميكانيكا	امس علي الفلدي

PRIVATE VILLA
IN RIYADH, KSA

OWNER NAME	1 DESIGN CONCEPT
SIMA MALAK	2 PRELIM. DESIGN
	3 DESIGN DEVELOP.
	4 WORKING DWG.
(VILLA-2)	5 SHOP DRAWING
	6 AS BUILT DWG.


FIRST & UPPER ROOF FLOOR LAYOUT PLAN

PROJ. NO.	DWG. NO.	DATE	SCALE:
P-2024-07	AR-04	jun2024	1:100

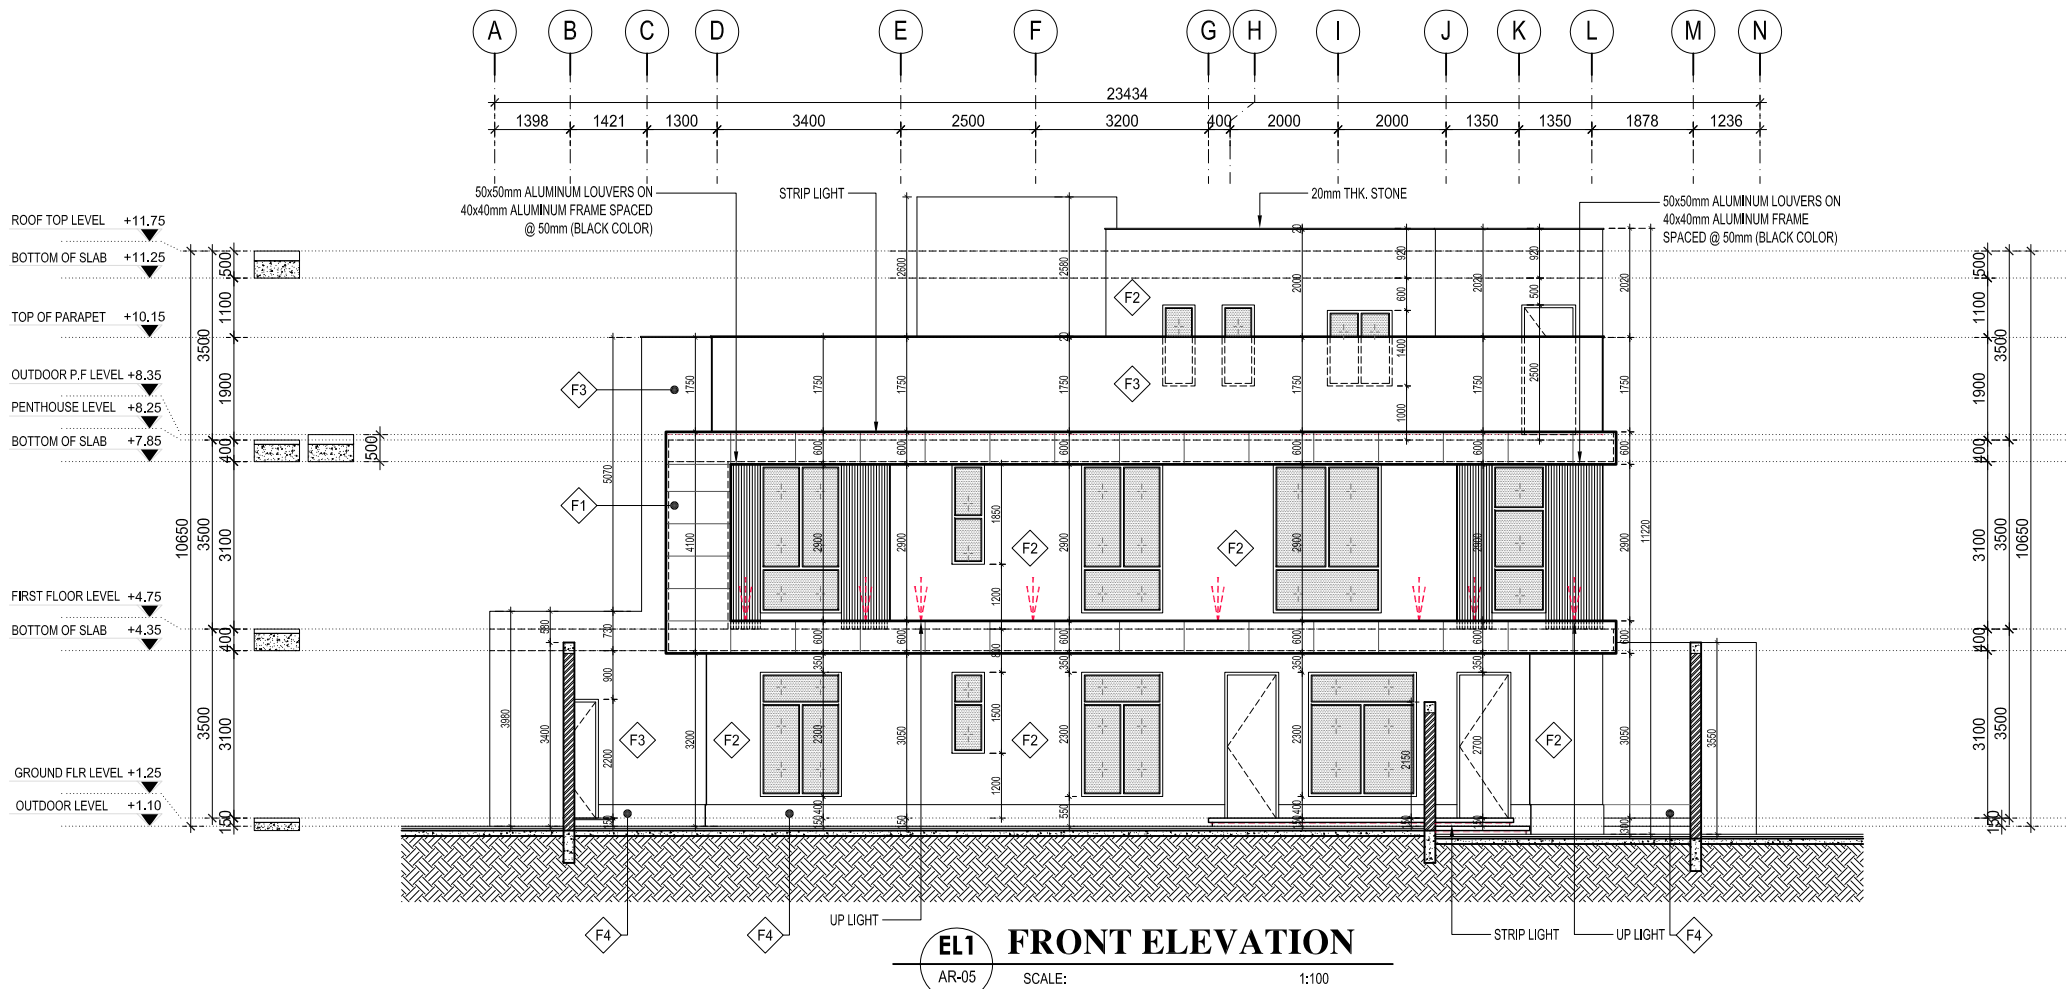

FINISHING LEGEND :

- F1 600 x 1200 x 20mm THICK TRAVERTINE MARBLE OR PORCELAIN TILE TRAVERTINE EFFECT
- F2 TEXTURED PAINT ON CEMENT (COLOR IVORY WHITE OR AS SPECIFIED)
- F3 TEXTURED PAINT ON CEMENT (COLOR GRAY OR AS SPECIFIED)
- F4 1200 x 2000 x 20mm THICK GRAY COLOR MARBLE STONE OR PORCELAIN TILE STONE EFFECT

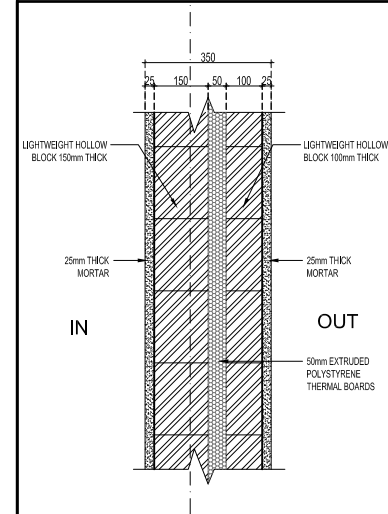

WALL SECTION DETAIL
WALL THK = 350mm
U VALUE FOR THE WALL=0.382

1 TYPICAL DETAIL
SCALE: 1:15


SIMA MALAK + ALSSAMOURÉ
DESIGN ASSOCIATES
P.O. Box 15707 - Riyadh 11454 KSA
Tel. 01 441 4963 - Fax. 01 441 3867
simals@simals.com


المكتب الاستشاري الرئيسي				
شركة المطورون العرب للاستشارات الهندسية				
ترخيص رقم ٥١١٠٠٠٢٤٥٦				
الاعتماد	الدرجة	التخصص	المهندس	تصميم معماري و تنفيذ
٢٧٥٩٦	مستشار	عمارة	محمد جميل اسماعيل	تصميم معماري و تنفيذ
٣٧١٠١	محترف	هندسة مدنية	غيداردو كايانيليا	تصميم انشائي
٣٠٣٥٧٨	مهندسة معمارية	هندسة معمارية	ايمى عماد جميل	رسم مخططات معمارية
٨٦٦١	مستشار	هندسة كهربائية	اسماء طاهر سعيد عرب	تصميم كهربائي
٧٤٣٧٢	محترف	هندسة ميكانيكية	احمد علي الفهدى	تصميم ميكانيكا

2-01 DESIGN/PROJECT SIMA MALAK+ALSSAMOURÉ ENGINEERING VILLA-2-01.dwg (AR-05) Plotted by Mudasar, Sep 28, 2025 - 22:25pm

PRIVATE VILLA IN RIYADH, KSA


OWNER NAME		1 DESIGN CONCEPT	
SIMA MALAK		2 PRELIM. DESIGN	
		3 DESIGN DEVELOPMENT	
		4 WORKING DRAWING	
(VILLA-2) FRONT ELEVATION RIGHT SIDE ELEVATION		5 SHOP DRAWING	
		6 AS BUILT DRAWING	
		DRAWING TITLE	
PROJ. NO. P-2024-07	DWG. NO. AR-05	DATE jun2024	SCALE: 1:100

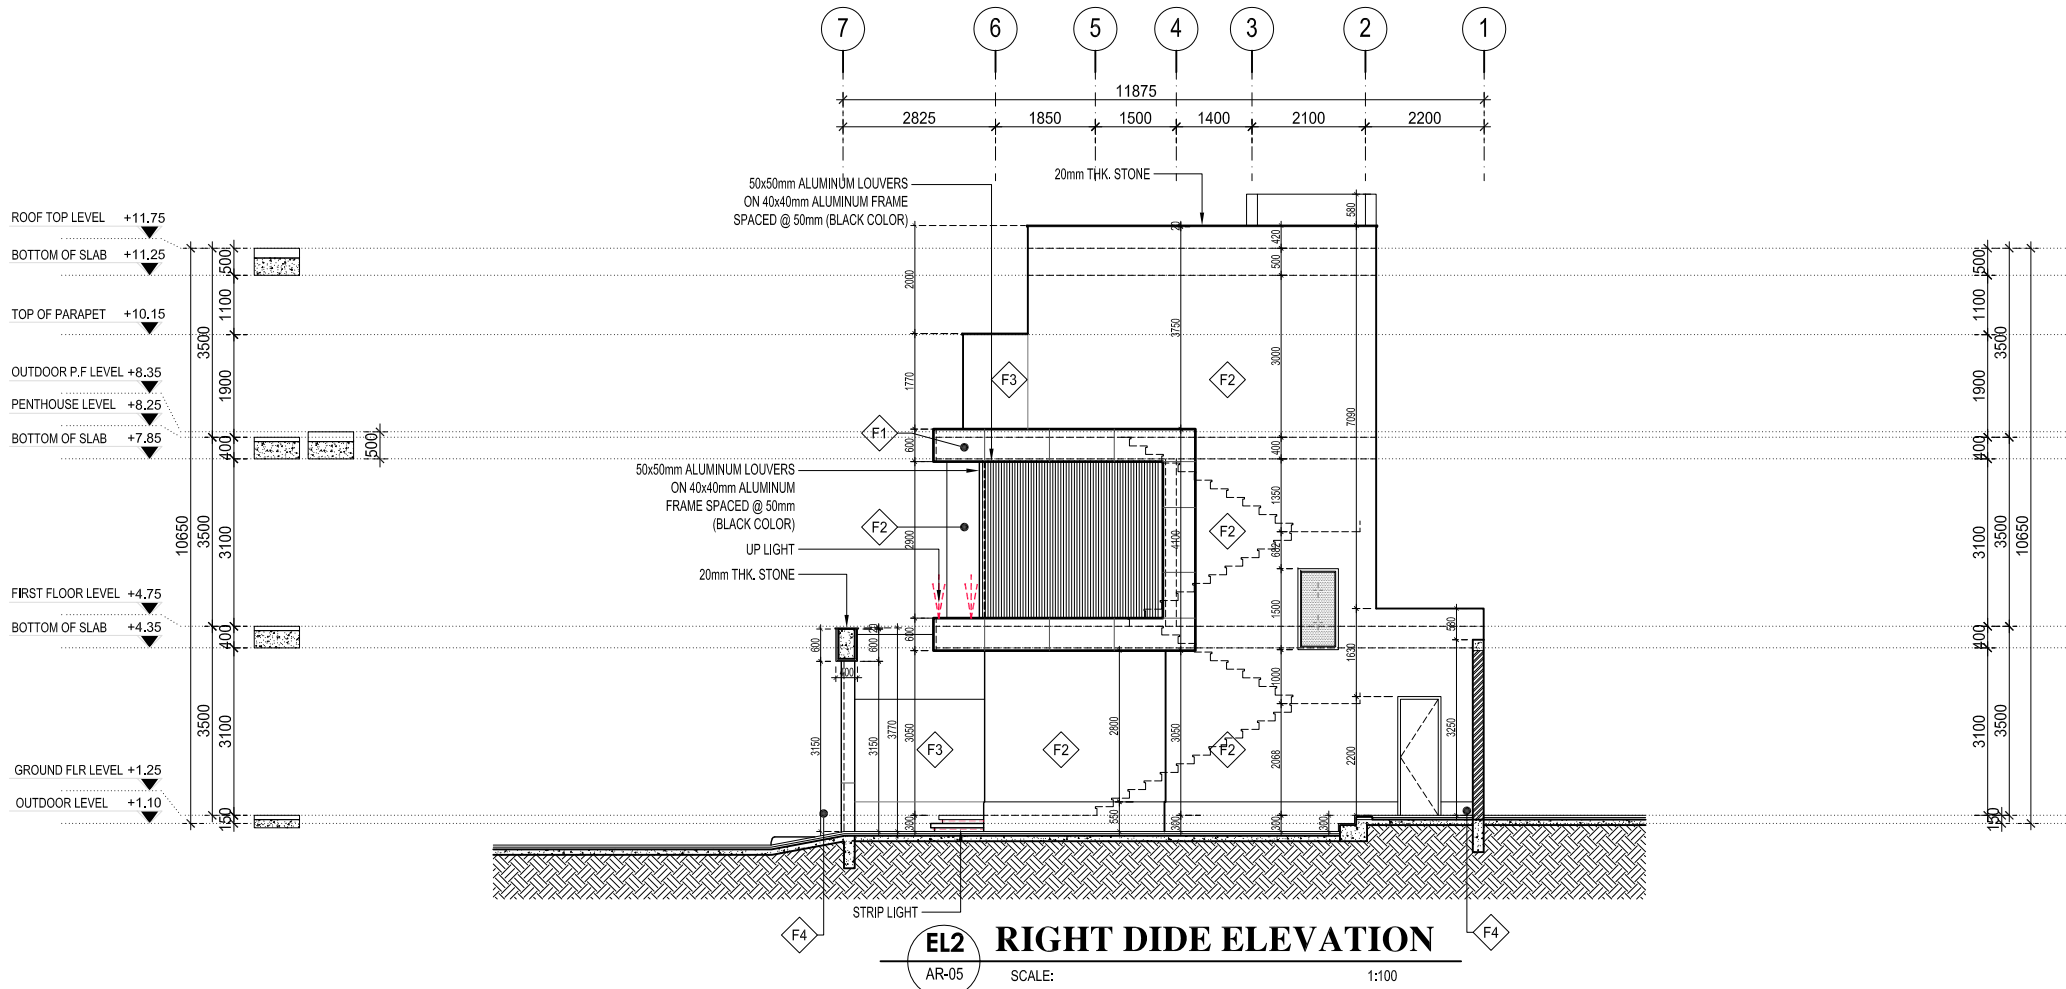

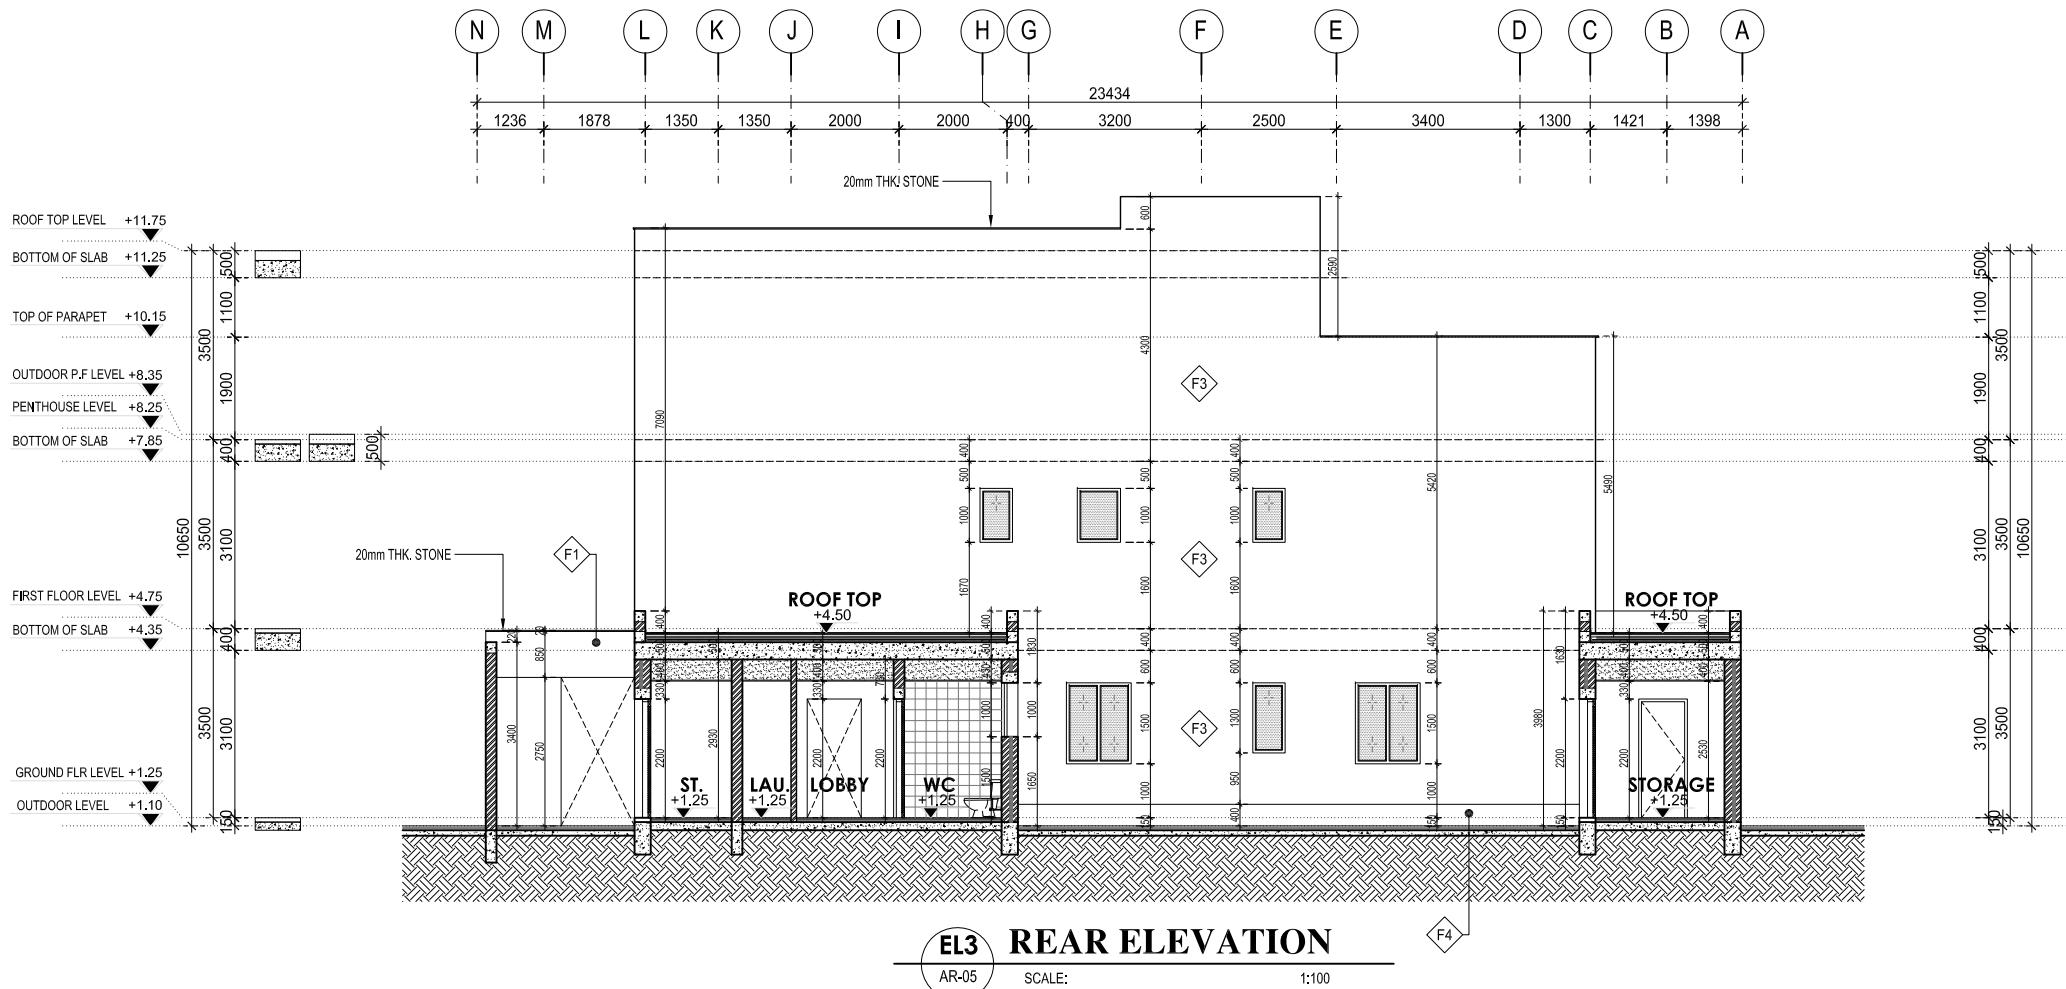

FINISHING LEGEND :

- F1 600 x 1200 x 20mm THICK TRAVERTINE MARBLE OR PORCELAIN TILE TRAVERTINE EFFECT
- F2 TEXTURED PAINT ON CEMENT (COLOR IVORY WHITE OR AS SPECIFIED)
- F3 TEXTURED PAINT ON CEMENT (COLOR GRAY OR AS SPECIFIED)
- F4 1200 x 2000 x 20mm THICK GRAY COLOR MARBLE STONE OR PORCELAIN TILE STONE EFFECT

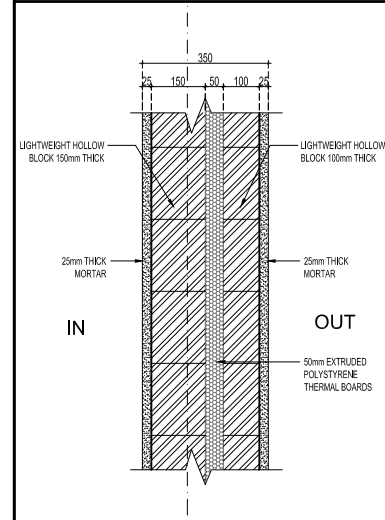

WALL THK = 350mm
U VALUE FOR THE WALL=0.382

1 TYPICAL DETAIL
SCALE: 1:15

SIMA MALAK + ALSSAMOURÉ
DESIGN ASSOCIATES
P.O. Box 15707 - Riyadh 11454 KSA
Tel. 01 441 4963 - Fax. 01 441 3867
simals@simals.com

المكتب الاستشاري الرئيسي


شركة المطورون العرب للاستشارات الهندسية

ترخيص رقم ٠١١٠٠٠٢٤٥٦


الاعتماد	الدرجة	التخصص	المهندس	تصميم معماري و تنفيذ
٢٧٥٩٦	مستشار	عمارة	محمد جميل اسماعيل	تصميم معماري و تنفيذ
٣٧١٠١	محترف	هندسة مدنية	غيداردو كايانيليا	تصميم انشائي
٣٠٣٥٧٨	مهندسة معمارية	هندسة معمارية	ابن عماد جميل	رسم مخططات معمارية
٨٦٦١	مستشار	هندسة كهربائية	اسامة طاهر سيد عرب	تصميم كهربائي
٧٤٣٧٢	محترف	هندسة ميكانيكية	اص على العبدى	تصميم ميكانيكا

PRIVATE VILLA
IN RIYADH, KSA

OWNER NAME		1	DESIGN CONCEPT
SIMA MALAK		2	PRELIMINARY DESIGN
		3	DESIGN DEVELOPMENT
		4	WORKING DRAWING
(VILLA-2) REAR ELEVATION LEFT SIDE ELEVATION		5	SHOP DRAWING
		6	AS BUILT DRAWING
		DRAWING TITLE	
PROJ. NO.	DWG. NO.	DATE:	SCALE:
P-2024-07	AR-06	jun2024	1:100

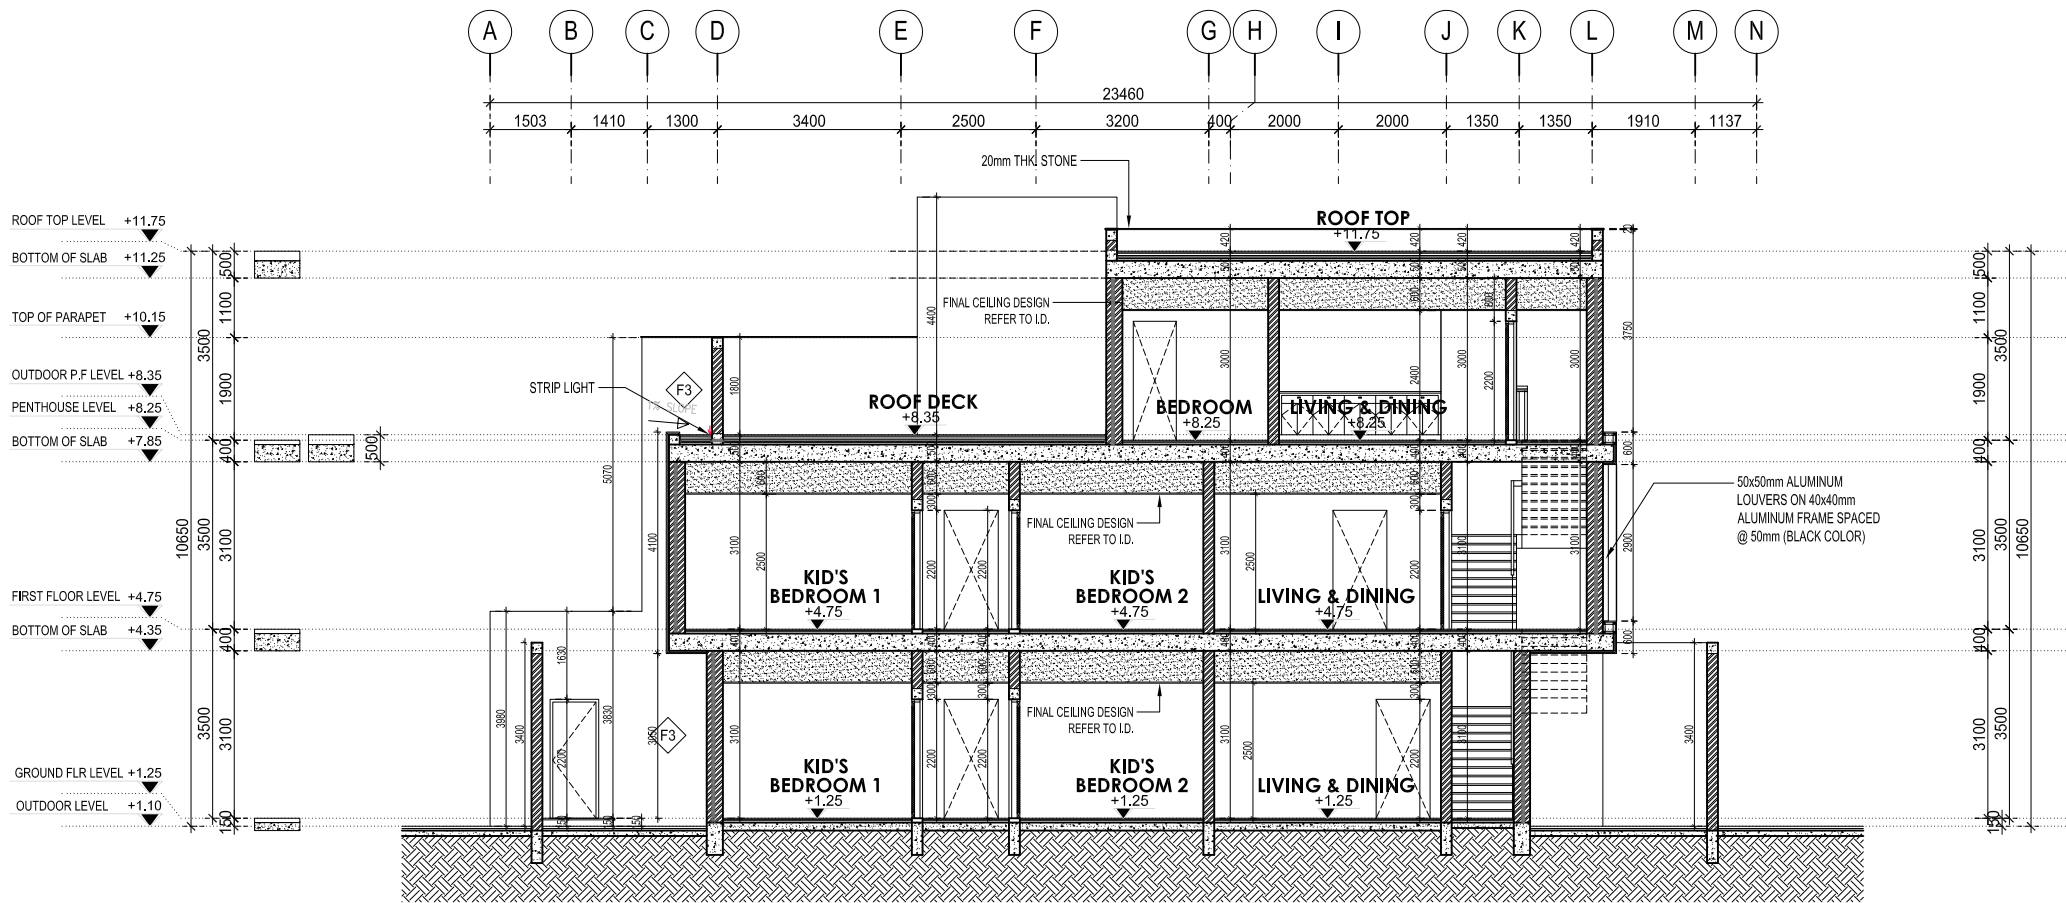


S1 CROSS SECTION
AR-07 SCALE: 1:100

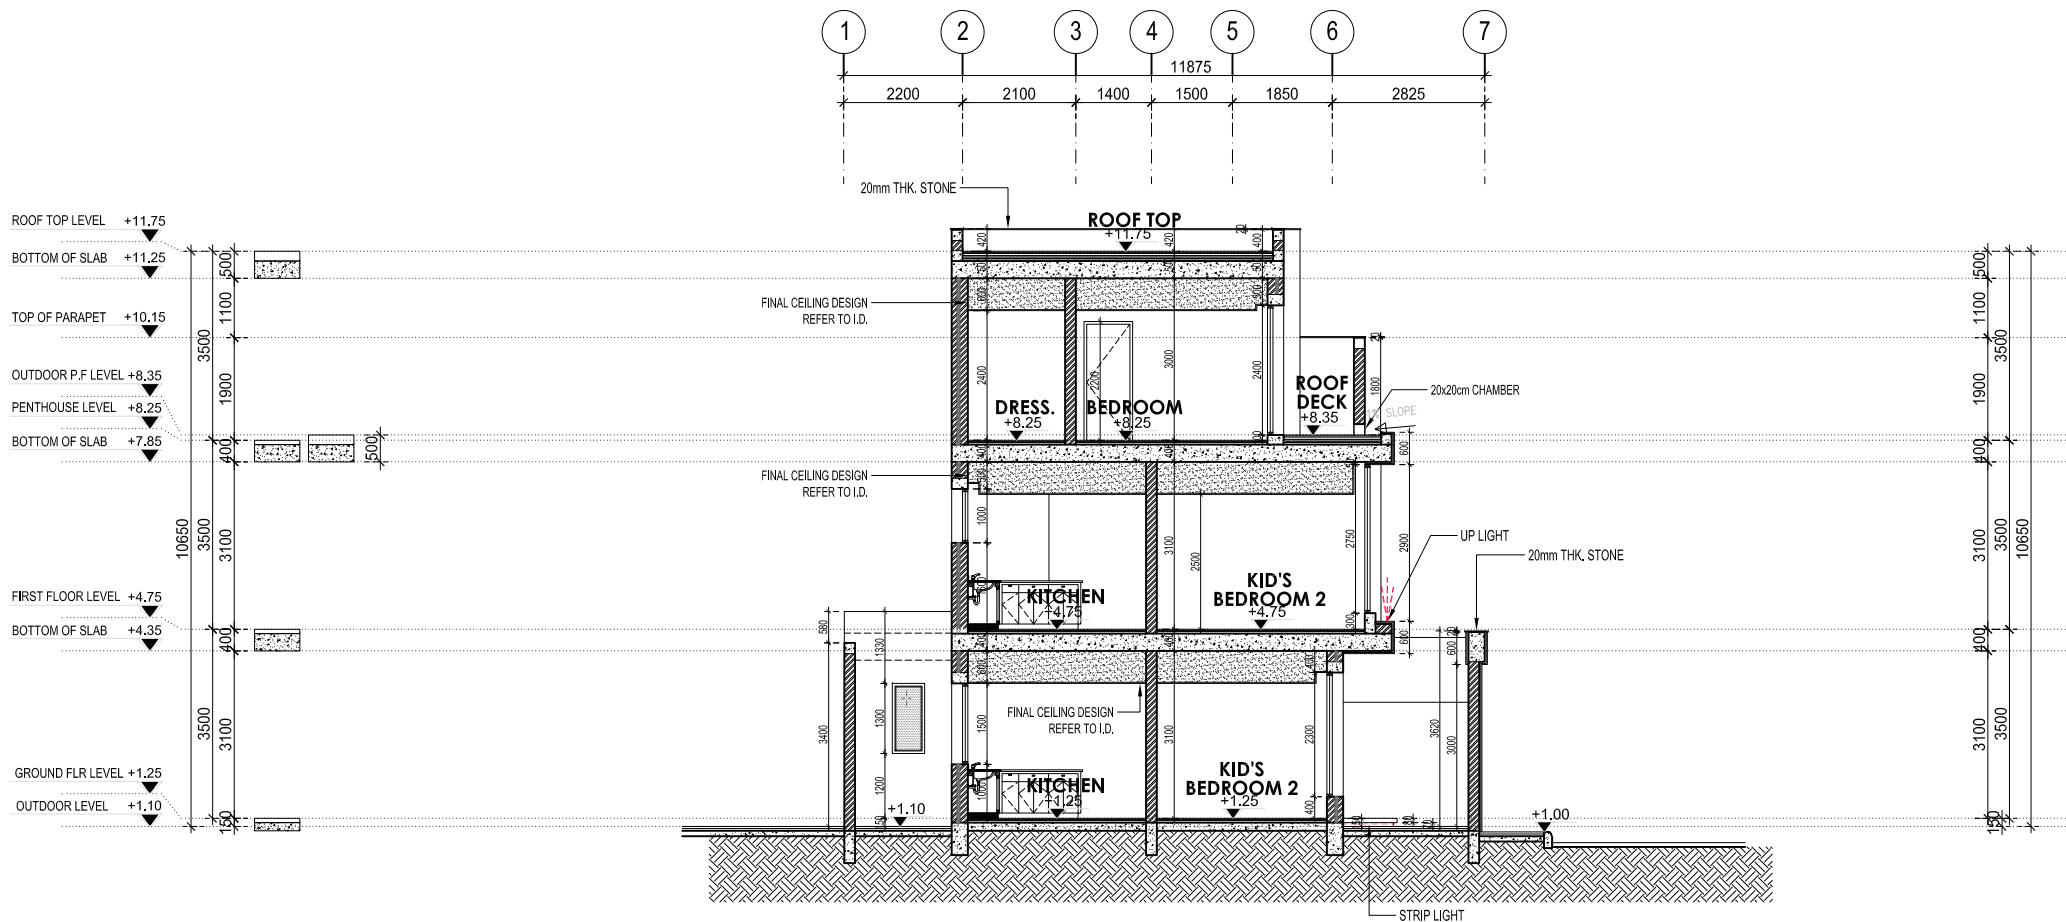

S2 LONGITUDINAL SECTION
AR-07 SCALE: 1:100

FINISHING LEGEND :

- F1 600 x 1200 x 20mm THICK TRAVERTINE MARBLE OR PORCELAIN TILE TRAVERTINE EFFECT
- F2 TEXTURED PAINT ON CEMENT (COLOR IVORY WHITE OR AS SPECIFIED)
- F3 TEXTURED PAINT ON CEMENT (COLOR GRAY OR AS SPECIFIED)
- F4 1200 x 2000 x 20mm THICK GRAY COLOR MARBLE STONE OR PORCELAIN TILE STONE EFFECT

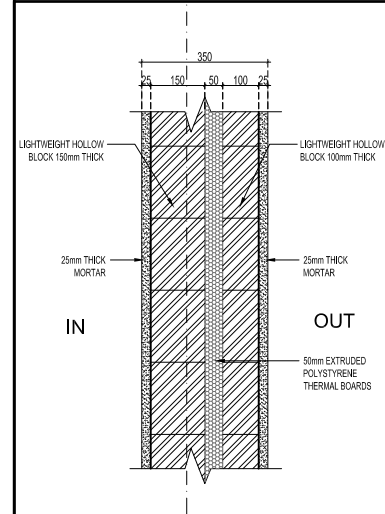

WALL SECTION DETAIL
WALL THK = 350mm
U VALUE FOR THE WALL=0.382

1 TYPICAL DETAIL
AR-06 SCALE: 1:15

SIMA MALAK + ALSSAMOURÉ
DESIGN ASSOCIATES
P.O. Box 15707 - Riyadh 11454 KSA
Tel. 01 441 4963 - Fax. 01 441 3867
simals@simals.com





المكتب الاستشاري الرئيسي
شركة المطورون العرب للاستشارات الهندسية
ترخيص رقم ٥١١٠٠٠٢٤٥٦

الاعتماد	الدرجة	التخصص	المهندس	تصميم معماري و تنفيذ
٢٧٥٩٦	مستشار	عمارة	محمد جميل اسمايل	تصميم معماري و تنفيذ
٣٧١٠١	محترف	هندسة مدنية	غيداردو كابانيليا	تصميم انشائي
٣٠٣٥٧٨	مهندسة معمارية	هندسة معمارية	ابن عماد جميل	رسم مخططات معمارية
٨٦٦١	مستشار	هندسة كهربائية	اسامة طاهر سيد عرب	تصميم كهربائي
٧٤٣٧٢	محترف	هندسة ميكانيكية	اص على الفاضل	تصميم ميكانيكا

2-011 DESIGN/SECURITY SIMA MALAK+ALSSAMOURÉ ENGINEERING & ARCHITECTURE

PRIVATE VILLA IN RIYADH, KSA

OWNER NAME		1 DESIGN CON	
SIMA MALAK		2 PRELIM: DE	
		3 DESIGN DEV	
		4 WORKING D	
(VILLA-2) CROSS SECTION LONGITUDINAL SECTION		5 SHOP DRAI	
		6 AS BUILT O	
PROJ. NO.	DWG. NO.	DATE:	SCALE: 1:
P-2024-07	AR-07	jun2024	1:100

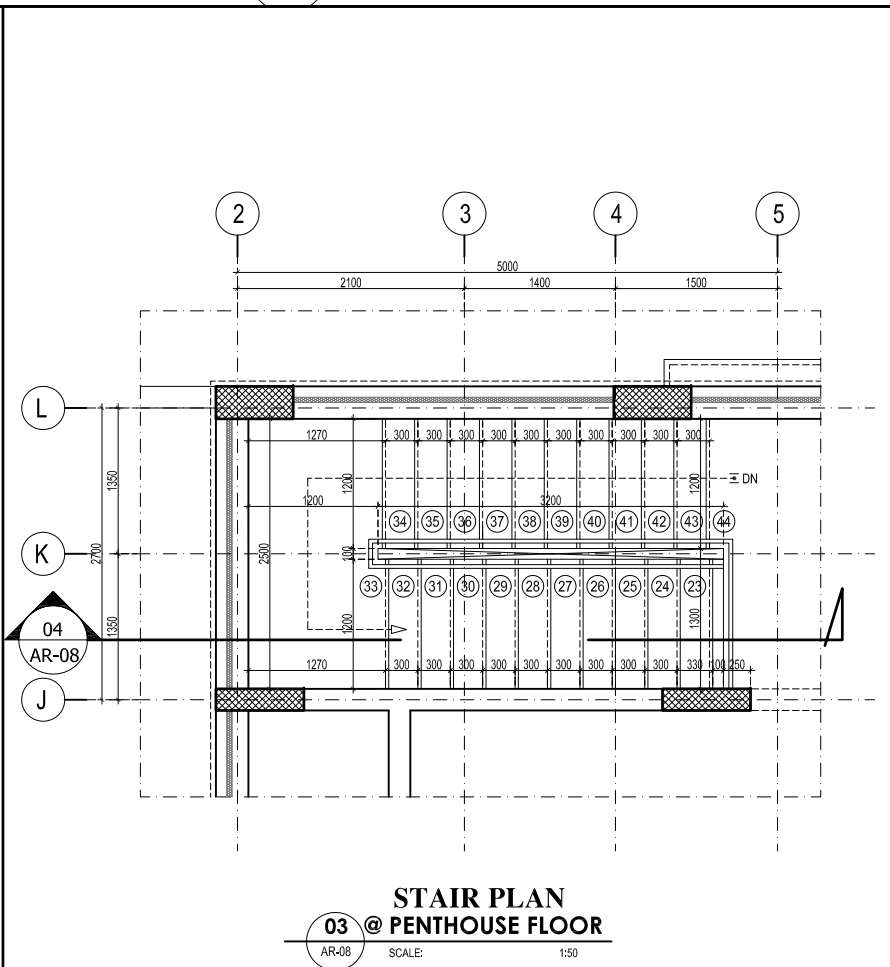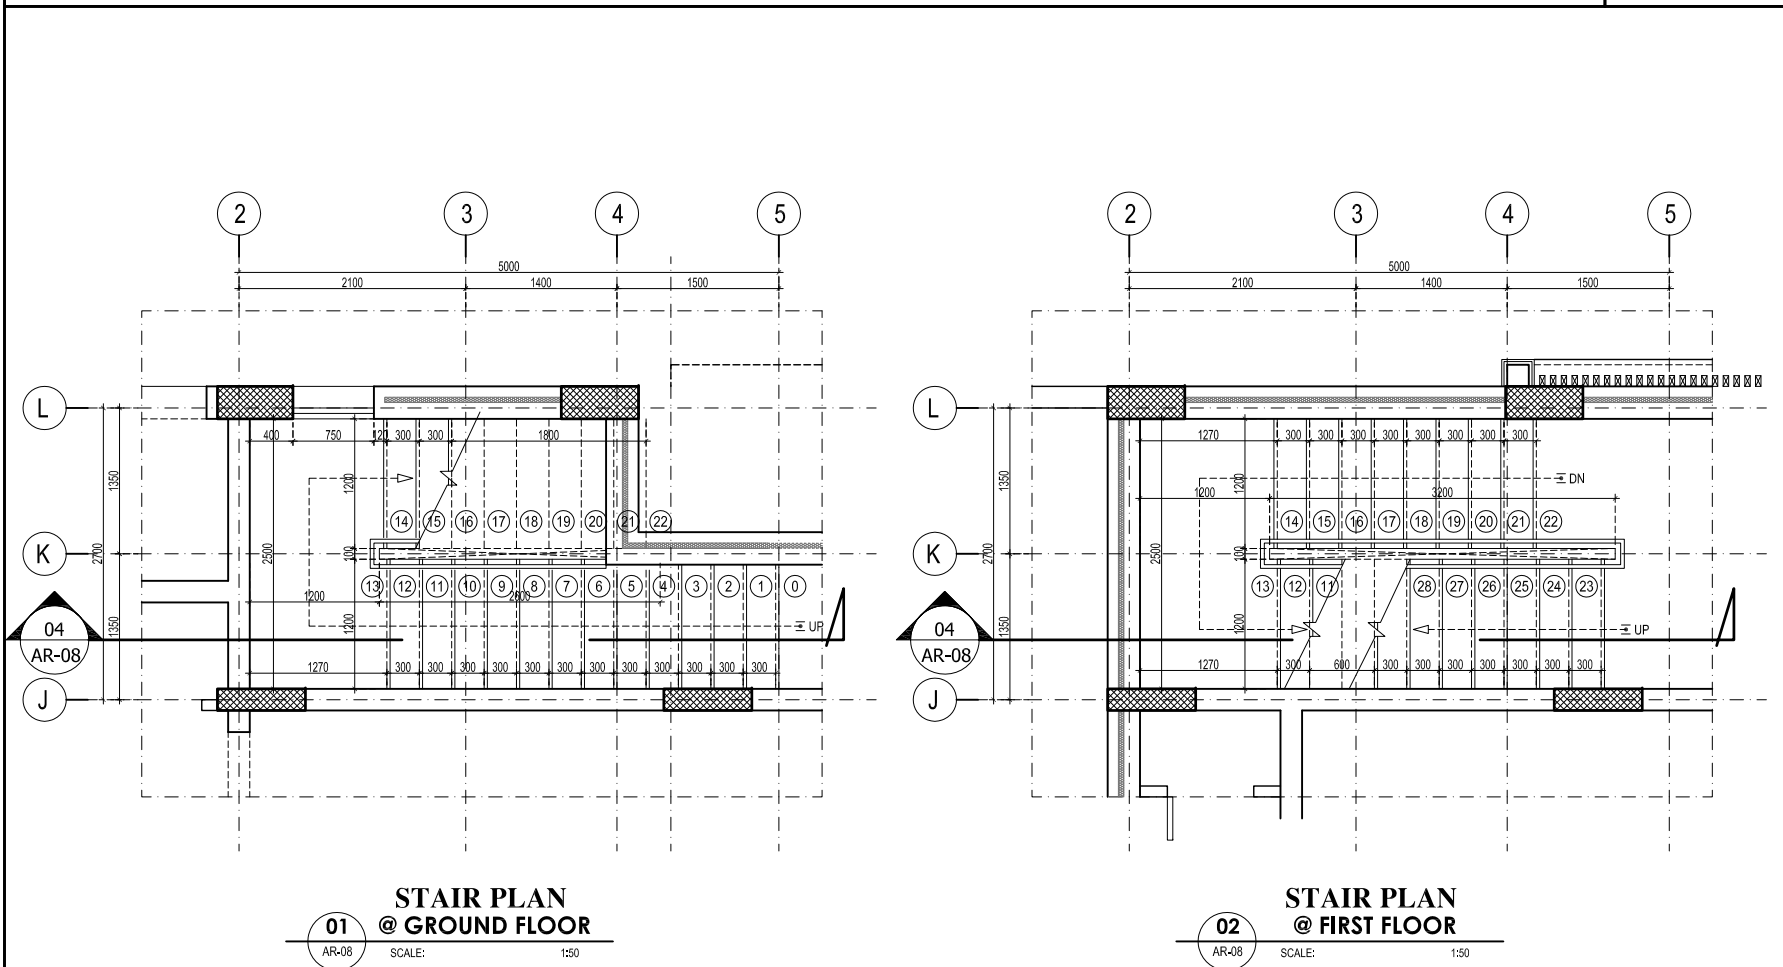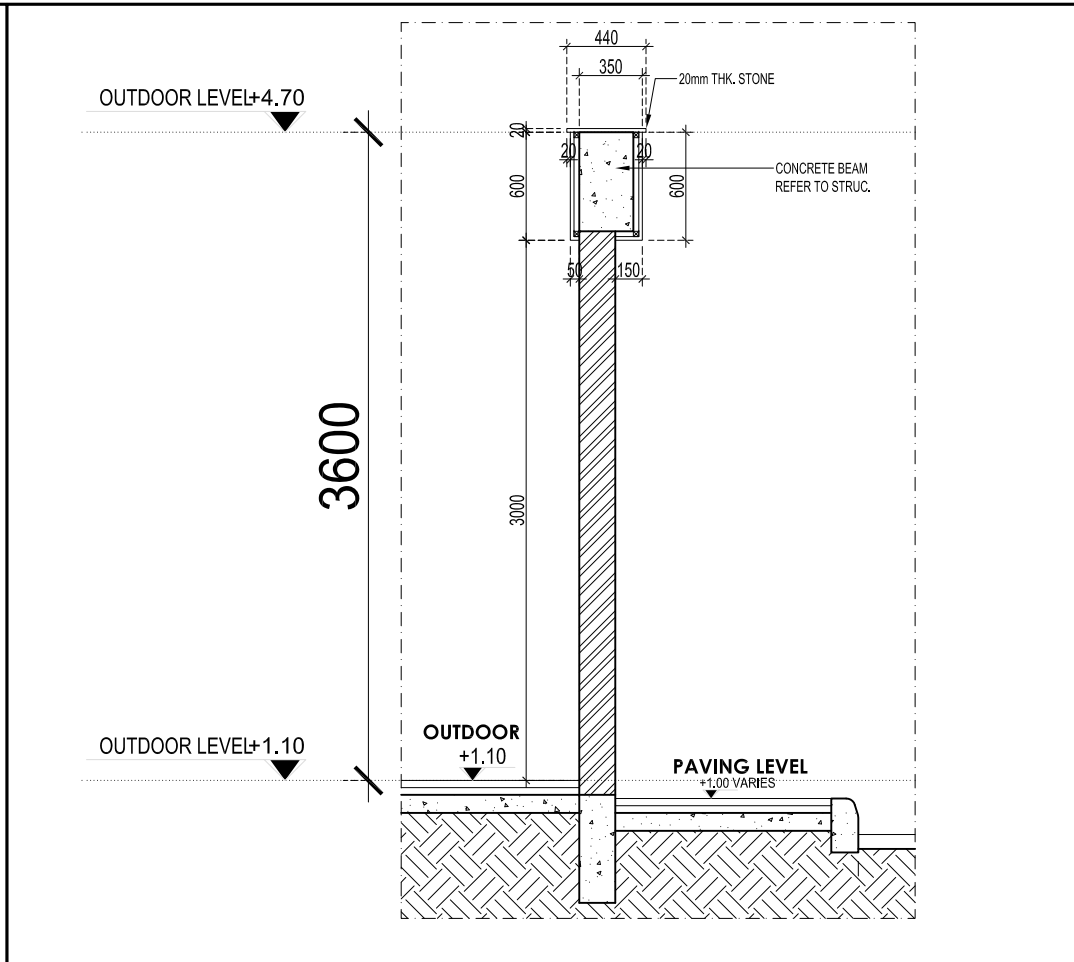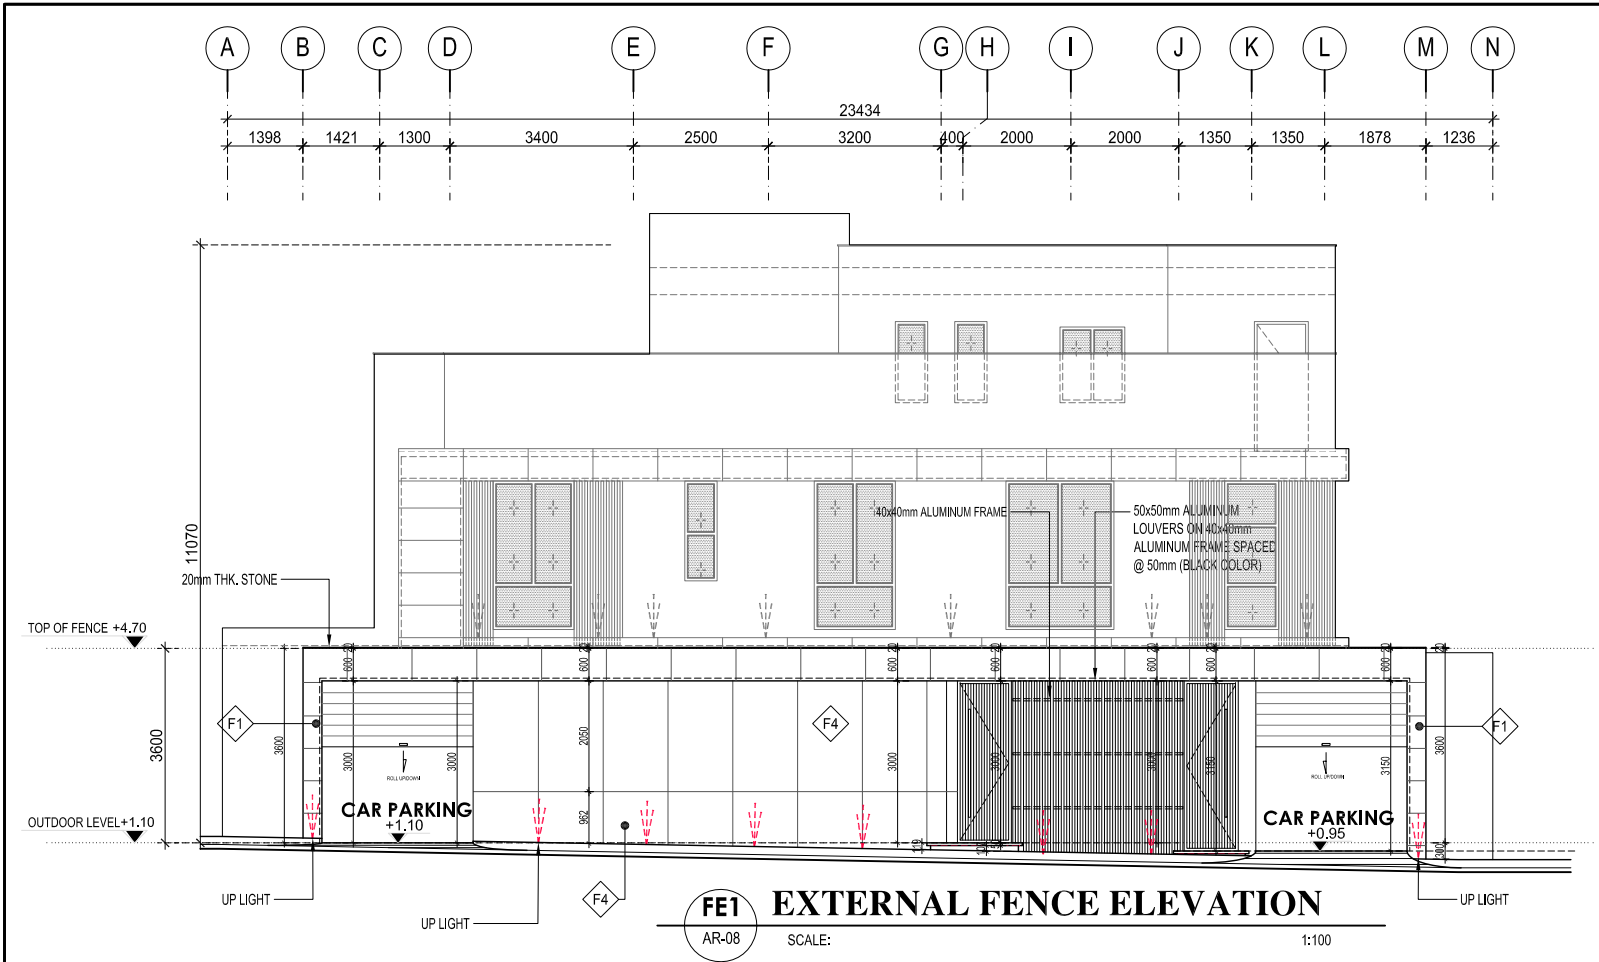

FINISHING LEGEND :

F1

600 x 1200 x 20mm THICK
TRAVERTINE MARBLE OR
PORCELAIN TILE TRAVERTINE EFFECT

F2

TEXTURED PAINT ON CEMENT
(COLOR IVORY WHITE OR AS SPECIFIED)

F3

TEXTURED PAINT ON CEMENT
(COLOR GRAY OR AS SPECIFIED)

F4

1200 x 2000 x 20mm THICK
GRAY COLOR MARBLE STONE OR
PORCELAIN TILE STONE EFFECT

SIMA MALAK + ALSSAMOURE
DESIGN ASSOCIATES

P.O. Box 15707 - Riyadh 11454 KSA
Tel. 01 441 4963 - Fax. 01 441 3867
simals@simals.com

المكتب الاستشاري الرئيسي

شركة المطورون العرب للاستشارات الهندسية

ترخيص رقم ٠١١٠٠٠٢٤٥٦

المهندس

التخصص الدرجة الاعتماد

تصميم معماري و تنفيذ

ممد جليل اسماعيل

عمارة

مستشار

٢٧٥٩٦

تصميم انشائي

غيداردو كايانيل

هندسة

محتفر

٣٧١٠١

رسم مخططات معمارية

ابن عماد جميل

هندسة معمارية

٣٠٣٥٧٨

تصميم كهربيا

اسماء طاهر سيد عرب هندسة كهربيا

مشتر

٨٢٢١

تصميم ميكانيكا

اص على الفلدي هندسة ميكانيكا

محتفر

٧٤٧٣٢

PRIVATE VILLA
IN RIYADH, KSA

OWNER NAME

SIMA MALAK

DRAWING TITLE

(VILLA-2)
FENCE ELEVATION
ARCHITECTURAL DETAILS-1

PROJ. NO.

P-2024-07

DWG. NO.

AR-08

DATE

jun2024

SCALE

AS SHOW

1

DESIGN CONCEPT

2

PRELIM. DESIGN

3

DESIGN DEVELOP.

4

WORKING DWG.

5



SHOP DRAWING

6

AS BUILT DWG.


C:\PROJECTS - CURRENT\SPM111 - DES-Designs\Drawings by others\1. Consultan\2025\08-25 - Adeb (Ashed) - WA\SIMA MALAK VILLA\AUGA-VILLA-2-AR-08.dwg (AR-08) Plotted by Mudassar, Sep 29, 2025 - 2:29pm

NOTE:
FOR STAIRCASE FINAL DESIGN,
PLEASE REFER TO INTERIOR
DESIGN PACKAGE IF THERE IS

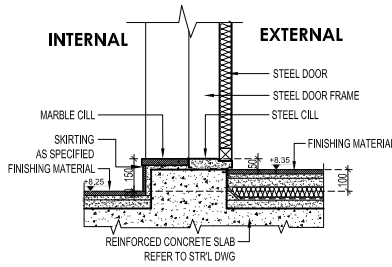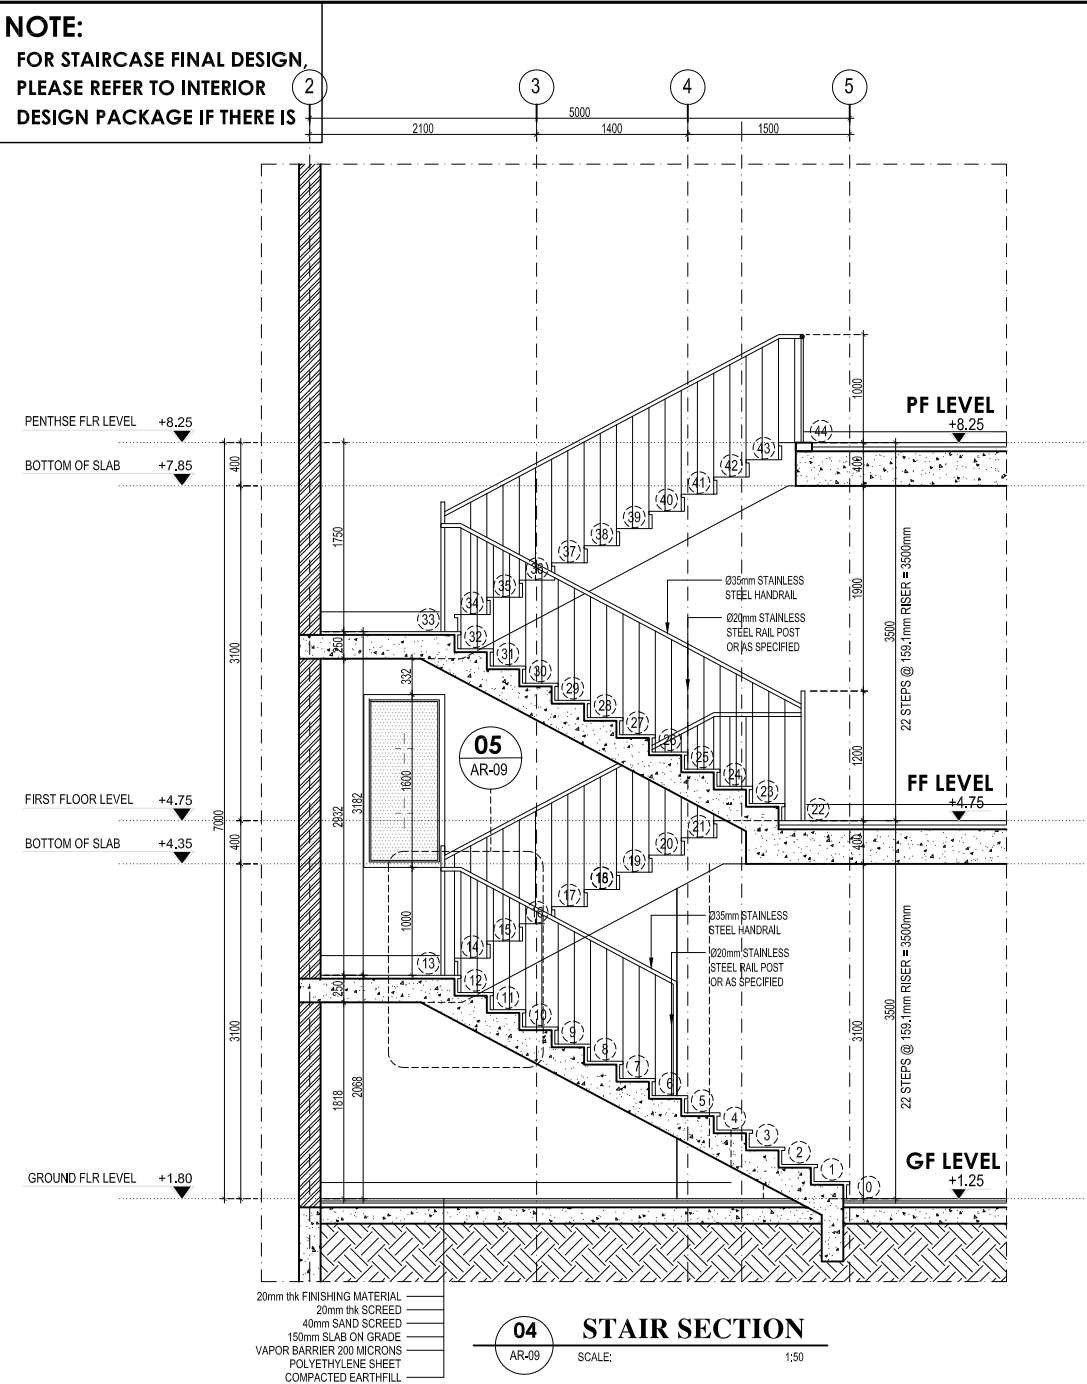


ROOF DOOR THRESHOLD

08 TYPICAL DETAIL
AR-09 SCALE: 1:25

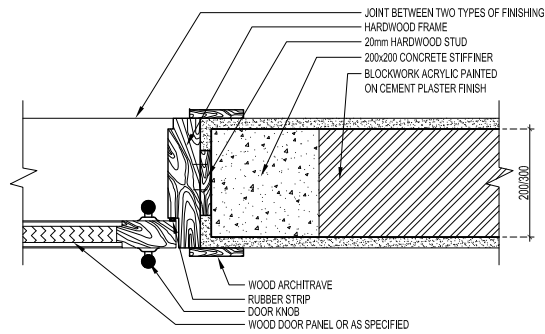


INTERNAL DOOR
TYPICAL DETAIL

09 AR-09 SCALE: 1:10

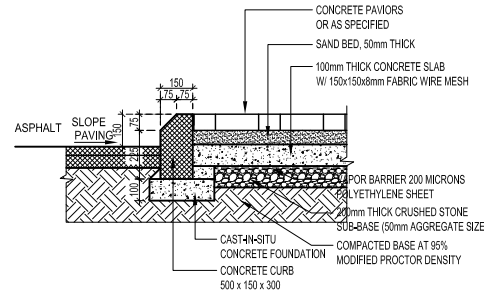


SIDEWALK SECTION DETAIL

10 TYPICAL DETAIL
AR-09 SCALE: 1:25

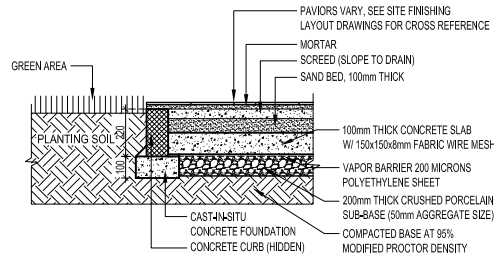


DETAIL AT GREEN AREA SECTION

11 TYPICAL DETAIL
AR-09 SCALE: 1:25

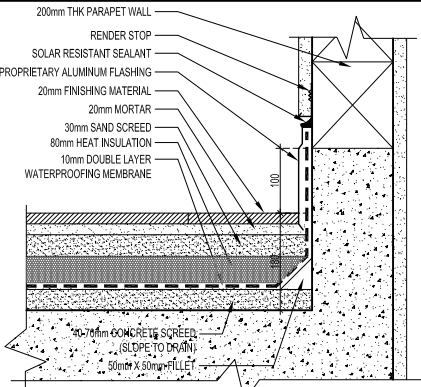

PARAPET WALL
TYPICAL DETAIL


13 AR-09 SCALE: 1:10

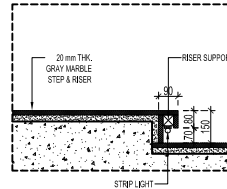

OUTDOOR STEP


14 TYPICAL DETAIL

AR-09 SCALE: 1:25

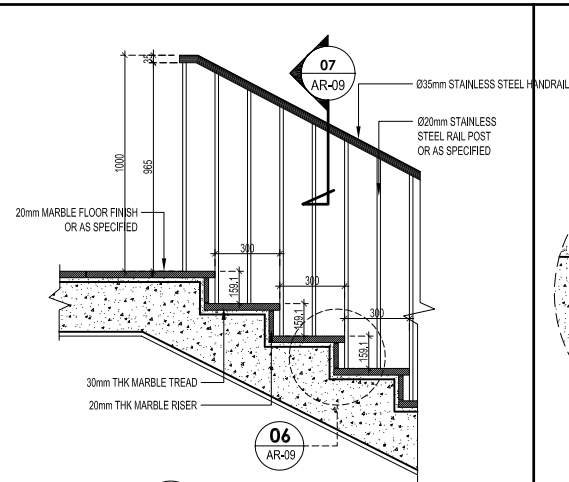


05 DETAIL

AR-09 SCALE: 1:25

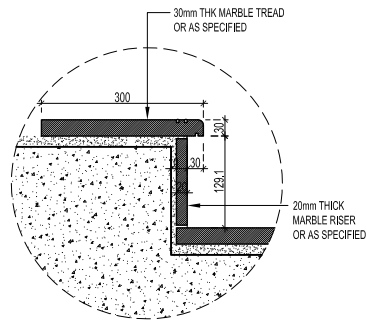


06 DETAIL

AR-09 SCALE: 1:10

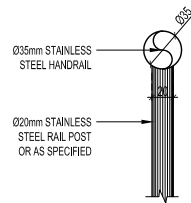

07 DETAIL

AR-09 SCALE: 1:5

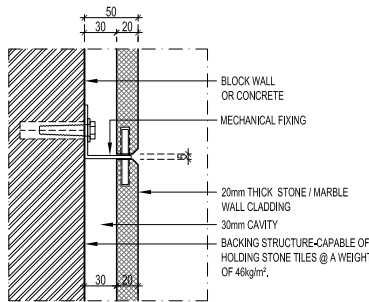

STONE / MARBLE
WALL CLADDING
TYPICAL DETAIL

15 AR-09 SCALE: 1:5

SIMA MALAK + ALSSAMOURE
DESIGN ASSOCIATES
P.O. Box 15707 - Riyadh 11454 KSA
Tel. 01 441 4963 - Fax. 01 441 3867
simals@simals.com

























المكتب الاستشاري الرئيسي
شركة المطورون العرب للاستشارات الهندسية
ترخيص رقم ٠١١٠٠٠٢٤٥٦

الاعتماد	الدرجة	التخصص	المهندس	تصميم معماري و تنفيذ
٢٧٥٩٦	مستشار	عمارة	محمد جميل اسماعيل	تصميم معماري و تنفيذ
٣٧١٠١	محترف	هندسة مدنية	غيداردو كاباتيللا كاتياغان	تصميم انشائي
٣٠٣٥٧٨	مهندسة معمارية	هندسة معمارية	ايمن عماد جميل	رسم مخططات معمارية
٨٦٦١	مستشار	هندسة كهرباء	اسامة طاهر سعيد عرب	تصميم كهرباء
٧٤٣٧٢	محترف	هندسة ميكانيكية	احمد علي الفيلسلي	تصميم ميكانيكا

2-011 DESIGN/PROJECT-SIMA MALAK+ALSSAMOURE DESIGN ASSOCIATES

PRIVATE VILLA
IN RIYADH, KSA

OWNER NAME	1	2	3	4	5	6
SIMA MALAK	DESIGN CONCEPT	PRELIM. DESIGN	DESIGN DEVELOP.	WORKING DWG.	SHOP DRAWING	AS BUILT DWG.
(VILLA-2) ARCHITECTURAL DETAILS-2	DRAWING TITLE					
PROJ. NO. P-2024-07	DWG. NO. AR-09	DATE jun2024	SCALE: AS SHOW			

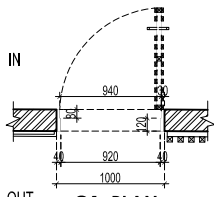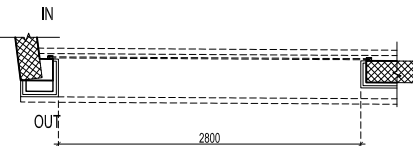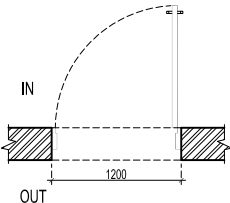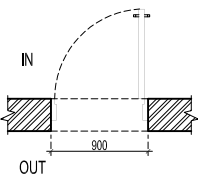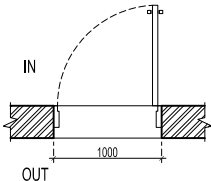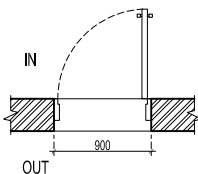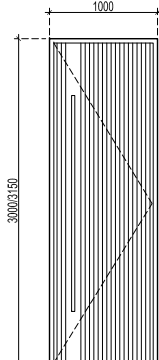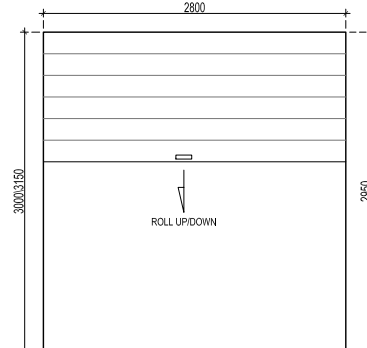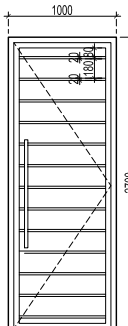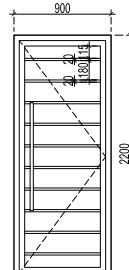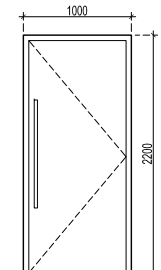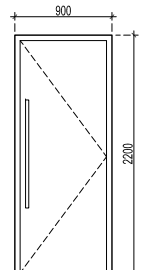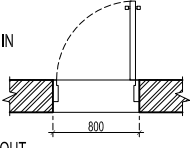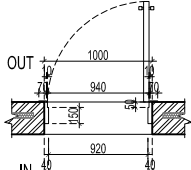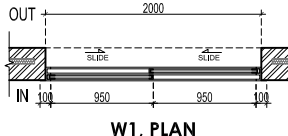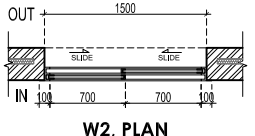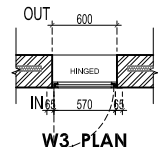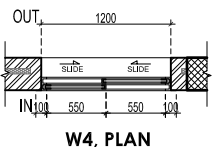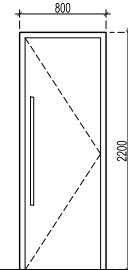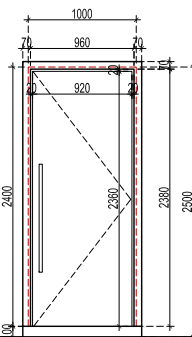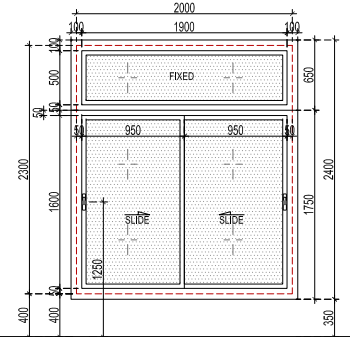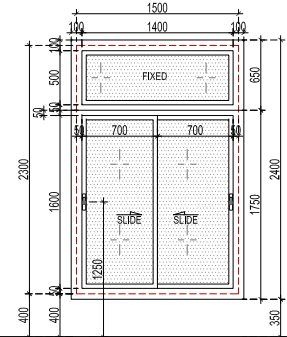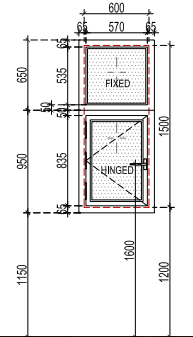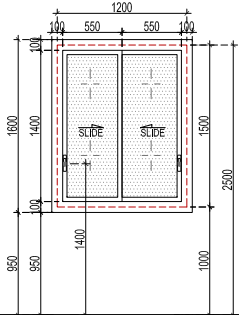											
											
G1, ELEVATION				D1, ELEVATION		D2, ELEVATION		D3, ELEVATION		D4, ELEVATION	
DOOR NO.	G1	DOOR NO.	G2	DOOR NO.	D1	DOOR NO.	D2	DOOR NO.	D3	DOOR NO.	D4
DOOR TYPE	STEEL DOOR PANEL & FRAME SINGLE HINGED PANEL	DOOR TYPE	MOTORIZED ROLL UP SHUTTER DOOR	DOOR TYPE	POWDER COATED STEEL DOOR FRAME & STEEL DOOR PANEL (P.COAT COLOR)	DOOR TYPE	POWDER COATED STEEL DOOR FRAME & STEEL DOOR PANEL (P.COAT COLOR)	DOOR TYPE	WOOD DOOR PANEL SINGLE HINGED PANEL	DOOR TYPE	WOOD DOOR PANEL SINGLE HINGED PANEL
DIMENSION	3000/3150mm (H) x 1000mm (W) A=3.00/3.15m²	DIMENSION	3000/3150mm (H) x 2800mm (W)	DIMENSION	2700mm (H) x 1000mm (W) A=2.70m²	DIMENSION	2200mm (H) x 900mm (W) A=1.98m²	DIMENSION	2200mm (H) x 1000mm (W) A=2.20m²	DIMENSION	2200mm (H) x 900mm (W) A=1.98m²
QUANTITY	2 - SETS (VERIFY PLAN)	QUANTITY	2 - SET (VERIFY PLAN)	QUANTITY	2 - SETS (VERIFY PLAN)	QUANTITY	3 - SETS (VERIFY PLAN)	QUANTITY	1 - SETS (VERIFY PLAN)	QUANTITY	7 - SETS (VERIFY PLAN)
U-VALUE	—	QUANTITY	2 - SET (VERIFY PLAN)	U-VALUE	2.595	U-VALUE	2.595	U-VALUE	2.595	U-VALUE	2.595
DESCRIPTION	HOLLOW CORE PANEL STEEL TUBE 40x40mm, STEEL SHEET 2mm 20x40mm PAINTED STEEL LOUVERS FROM BOTH SIDE IRONMONGERY BLACK 20x20mm HANDLE WITH STEEL PIVOTS 6 NO.	DESCRIPTION	REMOTE CONTROLLED	DESCRIPTION	POWDER COATED STEEL FRAME STEEL DOOR PANEL (POWDER COAT COLOR) WITH 20mm GROOVE STEEL IRONMONGERY STAINLESS STEEL HANDLE & LOCK SYSTEM	DESCRIPTION	POWDER COATED STEEL FRAME STEEL DOOR PANEL (POWDER COAT COLOR) WITH 20mm GROOVE STEEL IRONMONGERY STAINLESS STEEL HANDLE & LOCK SYSTEM	DESCRIPTION	OAK WOOD OR SIMILAR SOLID FRAME & ARCHITRAVE HOLLOW CORE PANEL WITH SOLID LIP WITH STAINLESS STEEL PIVOTS 4 NO. AND STAINLESS STEEL HANDLE (FINAL MATERIALS AND DESIGN TO BE BY I.D IF THERE IS)	DESCRIPTION	OAK WOOD OR SIMILAR SOLID FRAME & ARCHITRAVE HOLLOW CORE PANEL WITH SOLID LIP WITH STAINLESS STEEL PIVOTS 4 NO. AND STAINLESS STEEL HANDLE (FINAL MATERIALS AND DESIGN TO BE BY I.D IF THERE IS)
											
											
D5, ELEVATION		D6, ELEVATION		W1, ELEVATION		W2, ELEVATION		W3, ELEVATION		W4, ELEVATION	
DOOR NO.	D5	DOOR NO.	D6	WINDOW NO.	W1	WINDOW NO.	W2	WINDOW NO.	W3	WINDOW NO.	W4
DOOR TYPE	WOOD DOOR PANEL SINGLE HINGED PANEL	DOOR TYPE	STEEL DOOR PANEL & FRAME SINGLE HINGED PANEL	WINDOW TYPE	20mm DOUBLE GLASS WINDOW PANEL 2 SLIDING & 1 FIXED PANELS	WINDOW TYPE	20mm DOUBLE GLASS WINDOW PANEL 2 SLIDING & 1 FIXED PANELS	WINDOW TYPE	18mm DOUBLE GLASS WINDOW PANEL 1 HINGED & 1 FIXED PANELS	WINDOW TYPE	18mm DOUBLE GLASS WINDOW PANEL 2 SLIDING PANELS
DIMENSION	2200mm (H) x 800mm (W) A=1.76m²	DIMENSION	2400mm (H) x 1000mm (W) A=2.40m²	DIMENSION	2300mm (H) x 2000mm (W) A=4.60m²	DIMENSION	2300mm (H) x 1500mm (W) A=3.45m²	DIMENSION	1500mm (H) x 600mm (W) A=0.90m²	DIMENSION	1500mm (H) x 1200mm (W) A= 1.79m²
QUANTITY	7 - SETS (VERIFY PLAN)	QUANTITY	1 - SETS (VERIFY PLAN)	QUANTITY	1 - SETS (VERIFY PLAN) 35.33%	QUANTITY	2 - SETS (VERIFY PLAN) 34.77%	QUANTITY	1 - SETS (VERIFY PLAN) 19.35%	QUANTITY	3 - SETS (VERIFY PLAN) 12.83%
U-VALUE	2.595	U-VALUE	2.595	U-VALUE	2.38	U-VALUE	2.38	U-VALUE	2.67	U-VALUE	2.67
DESCRIPTION	OAK WOOD OR SIMILAR SOLID FRAME & ARCHITRAVE HOLLOW CORE PANEL WITH SOLID LIP WITH STAINLESS STEEL PIVOTS 4 NO. AND STAINLESS STEEL HANDLE (FINAL MATERIALS AND DESIGN TO BE BY I.D)	DESCRIPTION	PRE ENGINEERED STEEL DOOR WITH STAINLESS STEEL PIVOTS 4 NO. AND STAINLESS STEEL HANDLE	DESCRIPTION	UPVC FRAME 20mm DOUBLE GLASS - LOW E (8mm glass + 8mm air + 8mm glass) Single Surface with Low E coating	DESCRIPTION	UPVC FRAME 20mm DOUBLE GLASS - LOW E (8mm glass + 8mm air + 8mm glass) Single Surface with Low E coating	DESCRIPTION	UPVC FRAME 18mm DOUBLE GLASS - LOW E (6mm glass + 6mm air + 6mm glass) Single Surface with Low E coating	DESCRIPTION	UPVC FRAME 18mm DOUBLE GLASS - LOW E (6mm glass + 6mm air + 6mm glass) Single Surface with Low E coating

SIMA MALAK + ALSSAMOURE

DESIGN ASSOCIATES

P.O. Box 15707 - Riyadh 11454 KSA
Tel. 01 441 4963 - Fax. 01 441 3867
simals@simals.com

المكتب الاستشاري الرئيسي

شركة المطورون العرب للاستشارات الهندسية

ترخيص رقم ٢٤٥٦٠٠١١

الاعتماد	الدرجة	التخصص	المهندس	تصميم معماري و تنفيذ
٢٧٥٩٦	مستشار	عمارة	محمد جميل اسماعيل	
٣٧١٠١	محترف	هندسة مدنية	غيداردو كاباتيلا كاباتان	تصميم انشائي
٣٠٣٥٧٨	رئيس مخططات معمارية	هندسة معمارية	ايمين عماد جميل	رسم مخططات معمارية
٨٦٦١	مستشار	هندسة كهرباء	اسامة طاهر سعيد عرب	تصميم كهرباء
٧٤٧٣٢	محترف	هندسة ميكانيكية	احسان علي الفلدي	تصميم ميكانيكا

PRIVATE VILLA

IN RIYADH, KSA

OWNER NAME

SIMA MALAK

(VILLA-2)

DOOR & WINDOW

DETAILS

DRAWING TITLE

AR-10

DATE

jun2024

SCALE:

1:50

1 DESIGN CONCEPT

2 PRELIM. DESIGN













3 DESIGN DEVELOP.

4 WORKING DWG.









5 SHOP DRAWING

6 AS BUILT DWG.

C:\PROJECTS - CURRENT\SPM111 - DES-Designs\Drawings by others\11. Consultan\2025.08.25 - Addc (Ashley - WA)\SIMA MALAK VILLA\2024\11A-2\4963.dwg (AR-10). Plotted by Mubassar, Sep 26, 2025 - 12:27pm

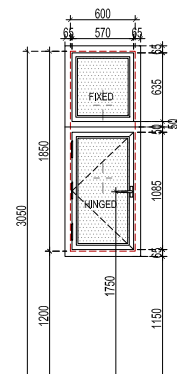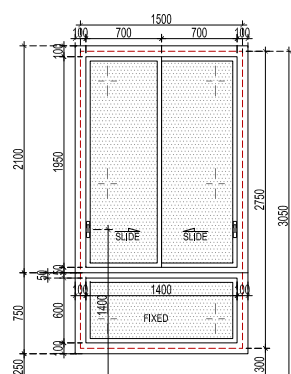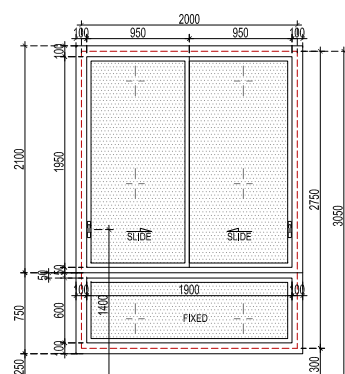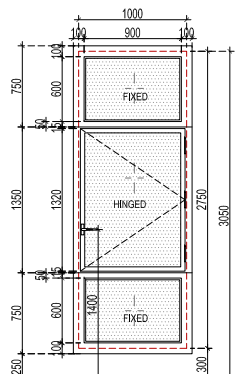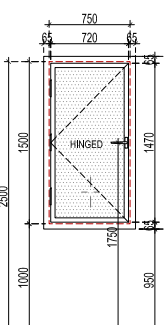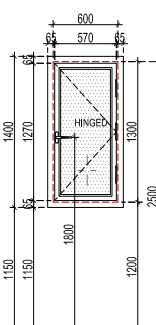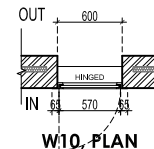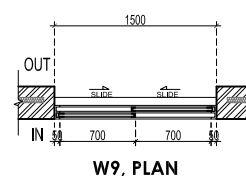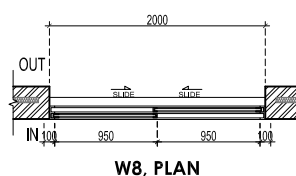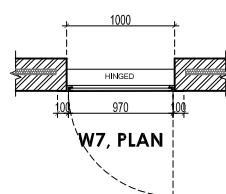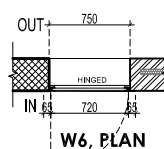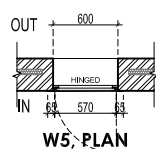

W5, ELEVATION			W6, ELEVATION			W7, ELEVATION			W8, ELEVATION			W9, ELEVATION			W10, ELEVATION		
WINDOW NO.	W5		WINDOW NO.	W6		WINDOW NO.	W7		WINDOW NO.	W8		WINDOW NO.	W9		WINDOW NO.	W10	
WINDOW TYPE	18mm DOUBLE GLASS WINDOW PANEL 1 AWNING PANEL & 1 FIXED		WINDOW TYPE	18mm DOUBLE GLASS WINDOW PANEL SINGLE FIXED PANEL		WINDOW TYPE	20mm DOUBLE GLASS WINDOW PANEL 1 HINGED & 2 FIXED PANELS		WINDOW TYPE	20mm DOUBLE GLASS WINDOW PANEL 2 SLIDING & 1 FIXED PANELS		WINDOW TYPE	20mm DOUBLE GLASS WINDOW PANEL 2 SLIDING & 1 FIXED PANELS		WINDOW TYPE	20mm DOUBLE GLASS WINDOW PANEL 1 HINGED & 1 FIXED PANELS	
DIMENSION	1300mm (H) x 600mm (W)	A=0.78m²	DIMENSION	1500mm (H) x 750mm (W)	A=1.12m²	DIMENSION	2750mm (H) x 1000mm (W)	A=2.75m²	DIMENSION	2750mm (H) x 2000mm (W)	A= 5.50m²	DIMENSION	2750mm (H) x 1500mm (W)	A= 4.12m²	DIMENSION	1850mm (H) x 600mm (W)	A=1.11m²
QUANTITY	3 - SETS (VERIFY PLAN)	10.93%	QUANTITY	1 - SET (VERIFY PLAN)	4.65%	QUANTITY	1 - SET (VERIFY PLAN)	28.00%	QUANTITY	1 - SETS (VERIFY PLAN)	44.54%	QUANTITY	2 - SETS (VERIFY PLAN)	41.24,33.41%	QUANTITY	1 - SETS (VERIFY PLAN)	29.54%
U-VALUE	2.67		U-VALUE	2.67		U-VALUE	2.38		U-VALUE	2.38		U-VALUE	2.38		U-VALUE	2.38	
DESCRIPTION	UPVC FRAME 18mm DOUBLE GLASS - LOW E (6mm glass + 6mm air + 6mm glass) Single Surface with Low E coating		DESCRIPTION	UPVC FRAME 18mm DOUBLE GLASS - LOW E (6mm glass + 6mm air + 6mm glass) Single Surface with Low E coating		DESCRIPTION	UPVC FRAME 20mm DOUBLE GLASS - LOW E (6mm glass + 8mm air + 6mm glass) Single Surface with Low E coating		DESCRIPTION	UPVC FRAME 20mm DOUBLE GLASS - LOW E (6mm glass + 8mm air + 6mm glass) Single Surface with Low E coating		DESCRIPTION	UPVC FRAME 20mm DOUBLE GLASS - LOW E (6mm glass + 8mm air + 6mm glass) Single Surface with Low E coating		DESCRIPTION	UPVC FRAME 20mm DOUBLE GLASS - LOW E (6mm glass + 8mm air + 6mm glass) Single Surface with Low E coating	

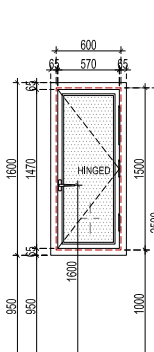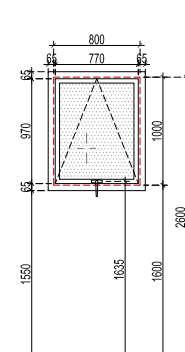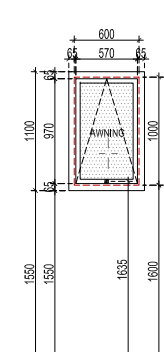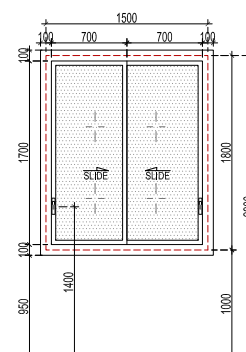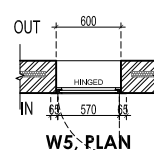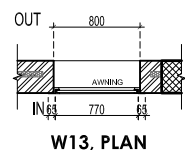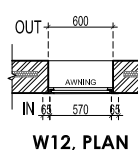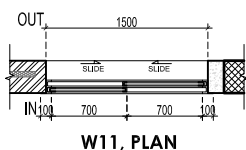

W11, ELEVATION			W12, ELEVATION			W13, ELEVATION			W14, ELEVATION		
WINDOW NO.	W11		WINDOW NO.	W12		WINDOW NO.	W13		WINDOW NO.	W14	
WINDOW TYPE	20mm DOUBLE GLASS WINDOW PANEL 2 SLIDING PANELS		WINDOW TYPE	18mm DOUBLE GLASS WINDOW PANEL 1 AWNING PANEL		WINDOW TYPE	18mm DOUBLE GLASS WINDOW PANEL 1 AWNING PANEL		WINDOW TYPE	18mm DOUBLE GLASS WINDOW PANEL SINGLE FIXED PANEL	
DIMENSION	1500mm (H) x 1500mm (W)	A= 2.69m²	DIMENSION	1000mm (H) x 600mm (W)	A=0.60m²	DIMENSION	800mm (H) x 1000mm (W)	A=0.79m²	DIMENSION	1500mm (H) x 600mm (W)	A=0.90m²
QUANTITY	1 - SETS (VERIFY PLAN) 26.29%		QUANTITY	2 - SETS (VERIFY PLAN) 8.41%		QUANTITY	1 - SETS (VERIFY PLAN) 16.02%		QUANTITY	2 - SET (VERIFY PLAN) 22.22%	
U-VALUE	2.38		U-VALUE	2.67		U-VALUE	2.67		U-VALUE	2.67	
DESCRIPTION	UPVC FRAME 20mm DOUBLE GLASS - LOW E (6mm glass + 8mm air + 6mm glass) Single Surface with Low E coating		DESCRIPTION	UPVC FRAME 18mm DOUBLE GLASS - LOW E (6mm glass + 6mm air + 6mm glass) Single Surface with Low E coating		DESCRIPTION	UPVC FRAME 18mm DOUBLE GLASS - LOW E (6mm glass + 6mm air + 6mm glass) Single Surface with Low E coating		DESCRIPTION	UPVC FRAME 18mm DOUBLE GLASS - LOW E (6mm glass + 6mm air + 6mm glass) Single Surface with Low E coating	

NOTE on WINDOW:	
PERCENTAGE	U-VALUE
0-25%	2.67
25-50%	2.38
50-100%	1.87
SKYLIGHT 0-3% of Roof	4.259

SIMA MALAK + ALSSAMOURÉ DESIGN ASSOCIATES P.O. Box 15707 - Riyadh 11454 KSA Tel, 01 441 4963 - Fax, 01 441 3867 simals@simals.com																															
المكتب الاستشاري الرئيسي شركة المتورون العرب للاستشارات الهندسية ترخيص رقم ٥١١٠٠٠٢٤٥٦ <table><tr><th>التخصص</th><th>الدرجة</th><th>الاعتماد</th><th>المهندس</th></tr><tr><td>عمارة</td><td>مستشار</td><td>١٧٥٩٦</td><td>محمد جهيل اسماعيل</td></tr><tr><td>هندسة مدنية</td><td>محترف</td><td>١٣٦٠١</td><td>غياراردو كايانيل كاتباعان</td></tr><tr><td>هندسة معمارية</td><td></td><td>٣٠٣٥٧٨</td><td>امين عماد جهيل</td></tr><tr><td>هندسة كهرباء</td><td>مستشار</td><td>٨٣٣١</td><td>امانة طاهر سعيد عرب</td></tr><tr><td>ميكانيكية</td><td>محترف</td><td>٢٤٣٢٢</td><td>اص علي الفارسي</td></tr><tr><td>ميكانيكا</td><td></td><td></td><td></td></tr></table>				التخصص	الدرجة	الاعتماد	المهندس	عمارة	مستشار	١٧٥٩٦	محمد جهيل اسماعيل	هندسة مدنية	محترف	١٣٦٠١	غياراردو كايانيل كاتباعان	هندسة معمارية		٣٠٣٥٧٨	امين عماد جهيل	هندسة كهرباء	مستشار	٨٣٣١	امانة طاهر سعيد عرب	ميكانيكية	محترف	٢٤٣٢٢	اص علي الفارسي	ميكانيكا			
التخصص	الدرجة	الاعتماد	المهندس																												
عمارة	مستشار	١٧٥٩٦	محمد جهيل اسماعيل																												
هندسة مدنية	محترف	١٣٦٠١	غياراردو كايانيل كاتباعان																												
هندسة معمارية		٣٠٣٥٧٨	امين عماد جهيل																												
هندسة كهرباء	مستشار	٨٣٣١	امانة طاهر سعيد عرب																												
ميكانيكية	محترف	٢٤٣٢٢	اص علي الفارسي																												
ميكانيكا																															
2-01-DESIGNING-CONCEPT-SIMA-MALAK-ALSSAMOURÉ-DRIVING-DESIGN-HELLA-TALOUCCIS																															
PRIVATE VILLA IN RIYADH, KSA																															
OWNER NAME		1	DESIGN CONCEPT																												
SIMA MALAK		2	PRELIM. DESIGN																												
		3	DESIGN DEVELOPMENT																												
(VILLA-2) WINDOW DETAILS		DRAWING TITLE	4	WORKING DWG.																											
			5	SHOP DRAWING																											
			6	AS BUILT DWG.																											
PROJ. NO.	DWG. NO.	DATE:	SCALE/1:2																												
P-2024-07	AR-11	jun2024	1:500																												