

Revisions	Issue Date
⚠	—

- Notes
- 1.
 - 2.
 - 3.




PHASE
EXEC DRAWINGS
TRADE
ARCHITECTURAL


Scale 1:100

AS-BUILT
PLAN AND SECTIONS

A-101

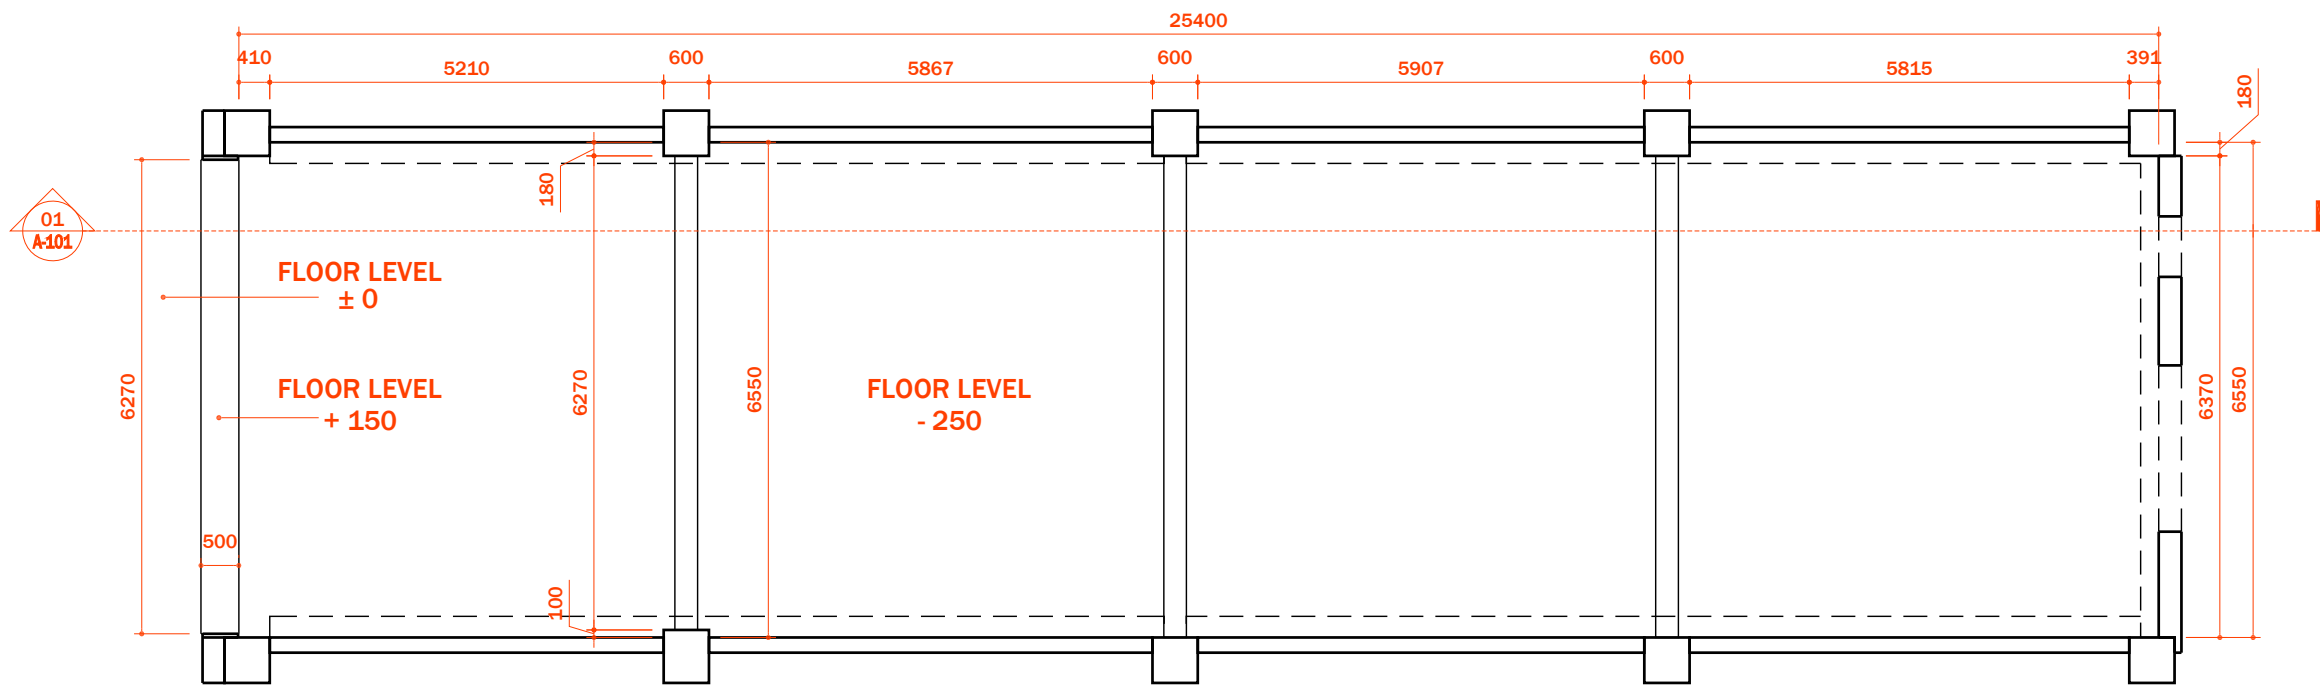

AS-BUILT LAYOUT
SCALE 1:100

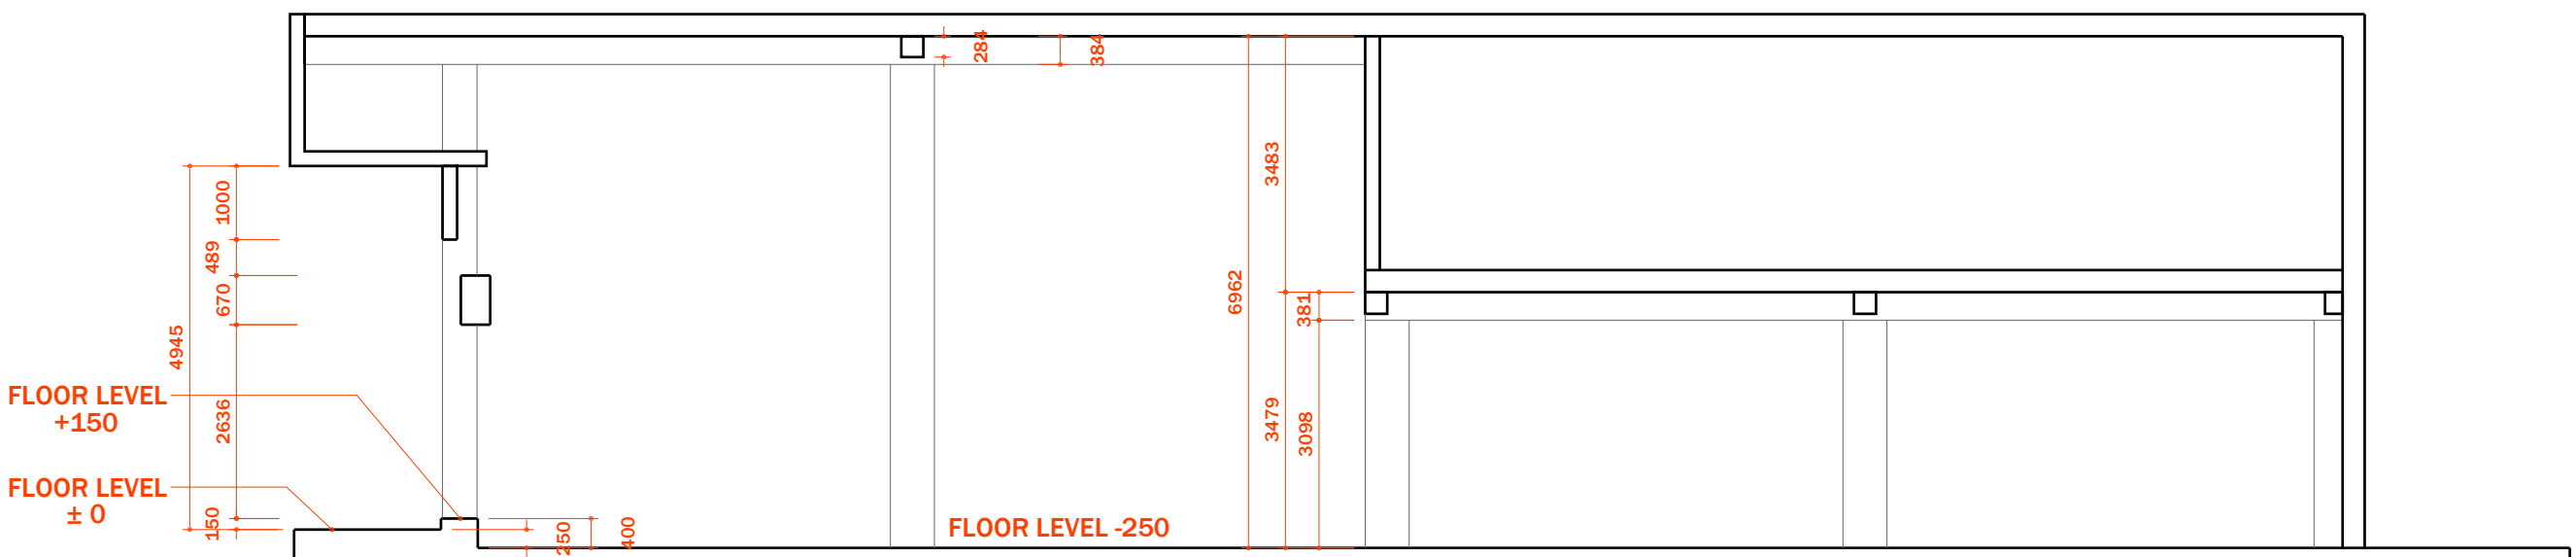

01 AS-BUILT SECTION
SCALE 1:100

Revisions	Issue Date
	—

Notes

1.
2.
3.

Project North




PHASE
EXEC DRAWINGS

TRADE
ARCHITECTURAL

Scale1:75

BLOCK WORK LAYOUT

A-102

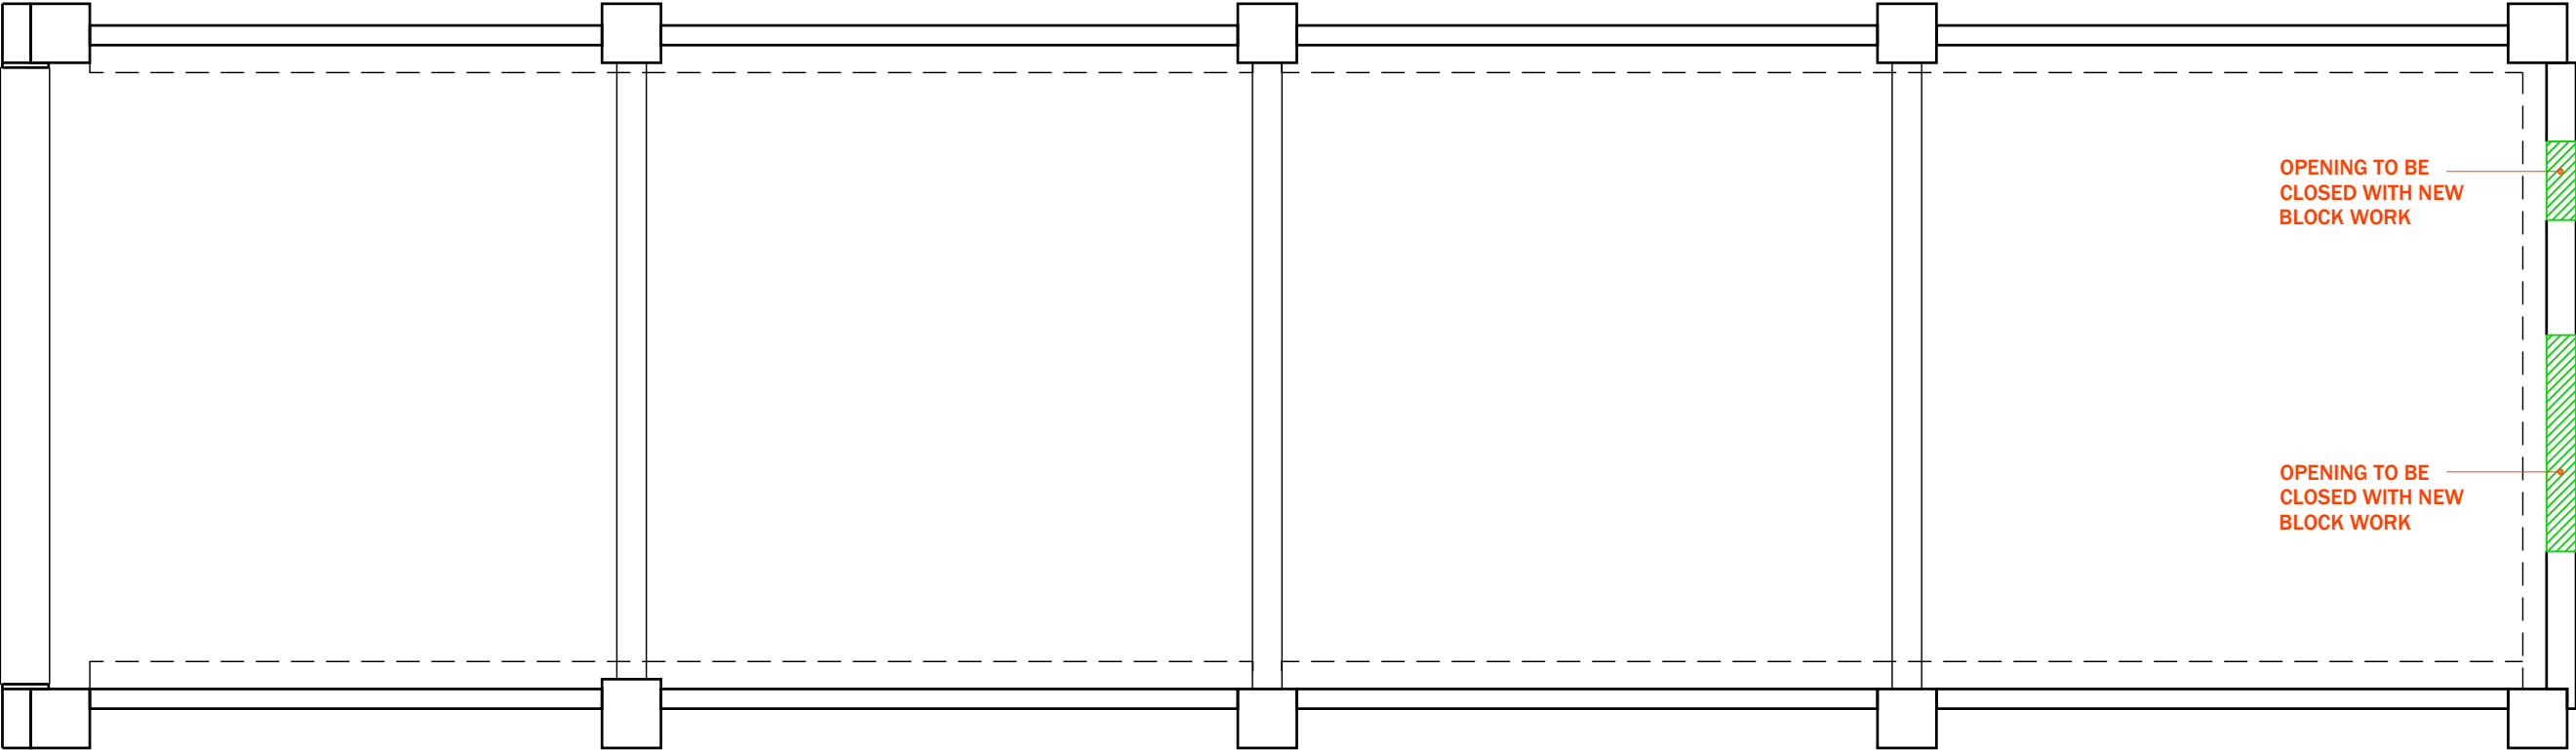

-


-

BLOCK WORK LAYOUT

SCALE 1:75

LEGEND:

NEW BLOCK WORK

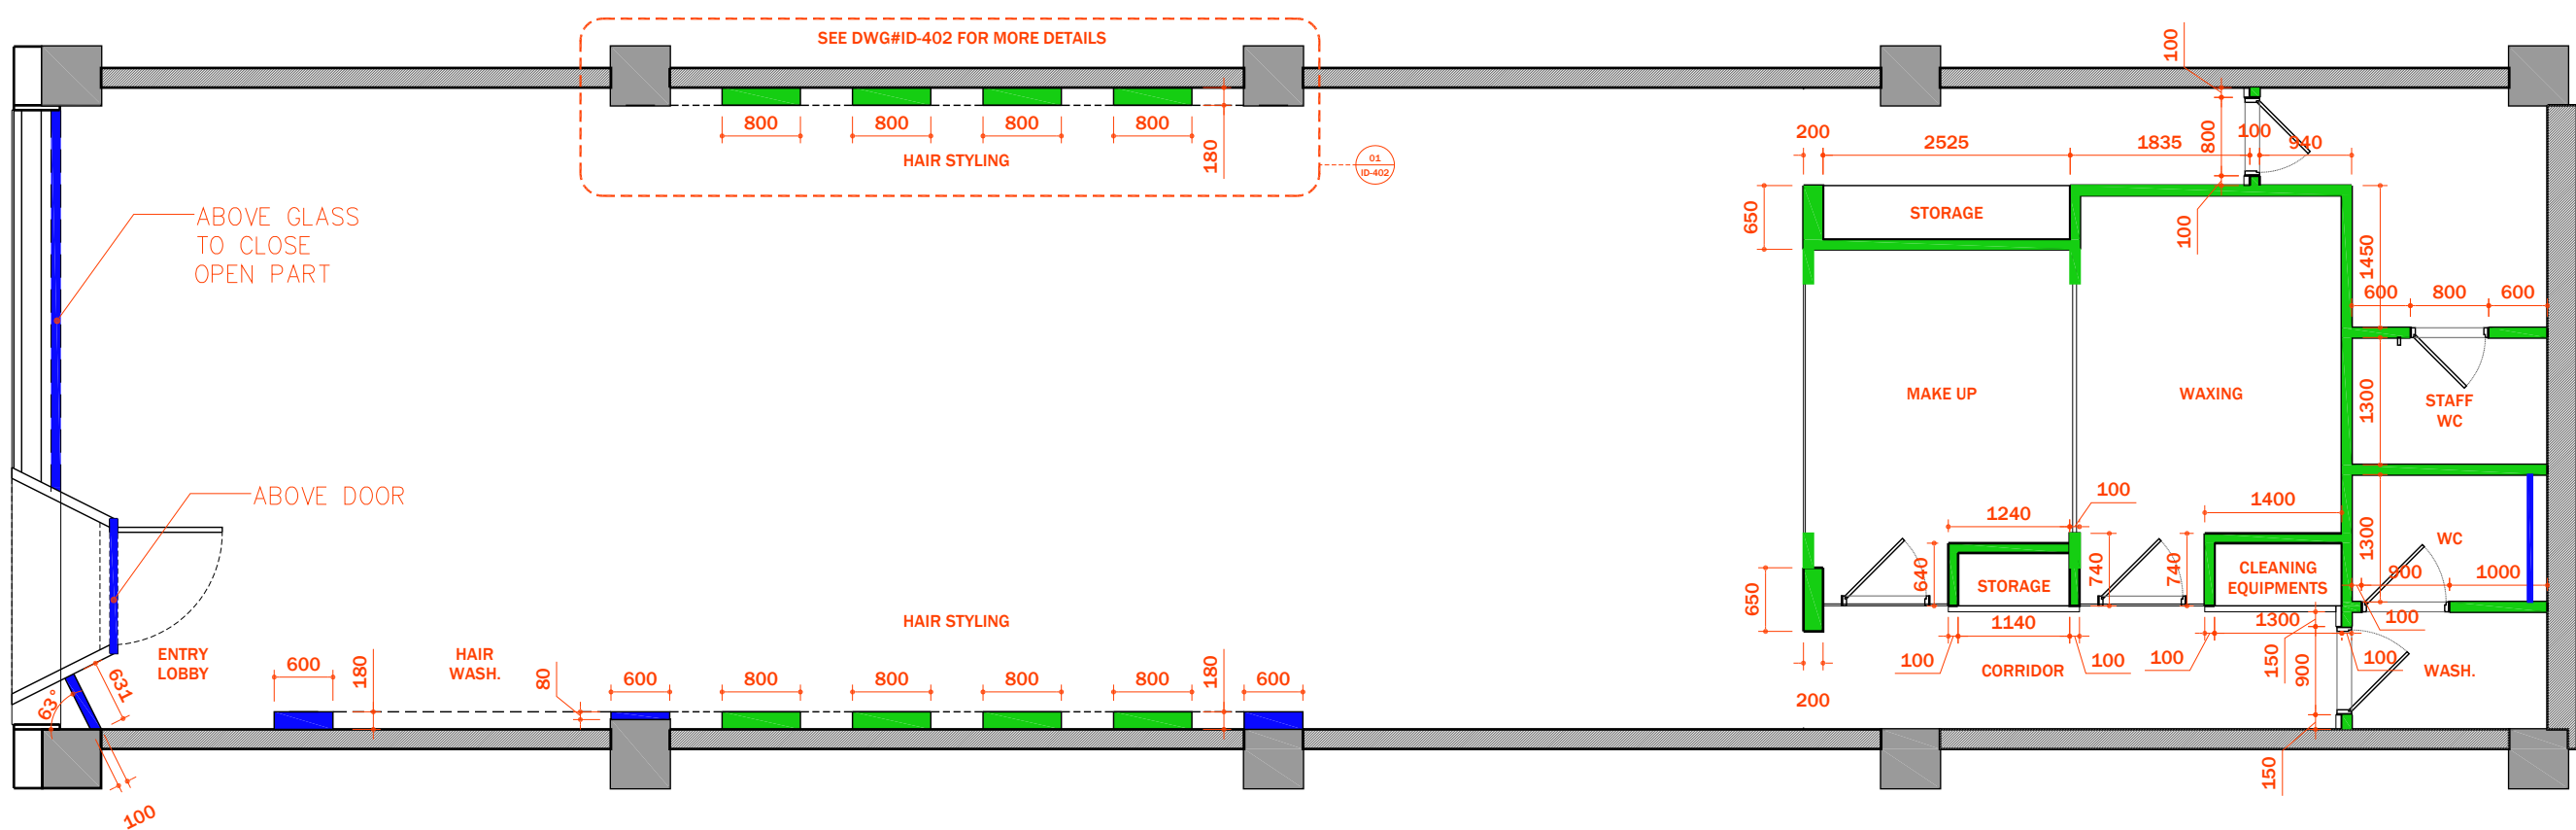

- DRY WALL LAYOUT
SCALE 1:75

LEGEND:

- CEMENT WALLS
- GYPSUM WALLS

PROJECT NAME
the

PROJECT NUMBER 01. 2021

DATE ISSUED
28.09.2025

Revisions Issue Date
REV DATE

Notes
1.
2.
3.

NOT FOR CONSTRUCTION





PHASE
PROJECT PHASE
TRADE
INTERIOR

Scale 1:75

CALLOUTS AND
DOOR TAGS


A-104

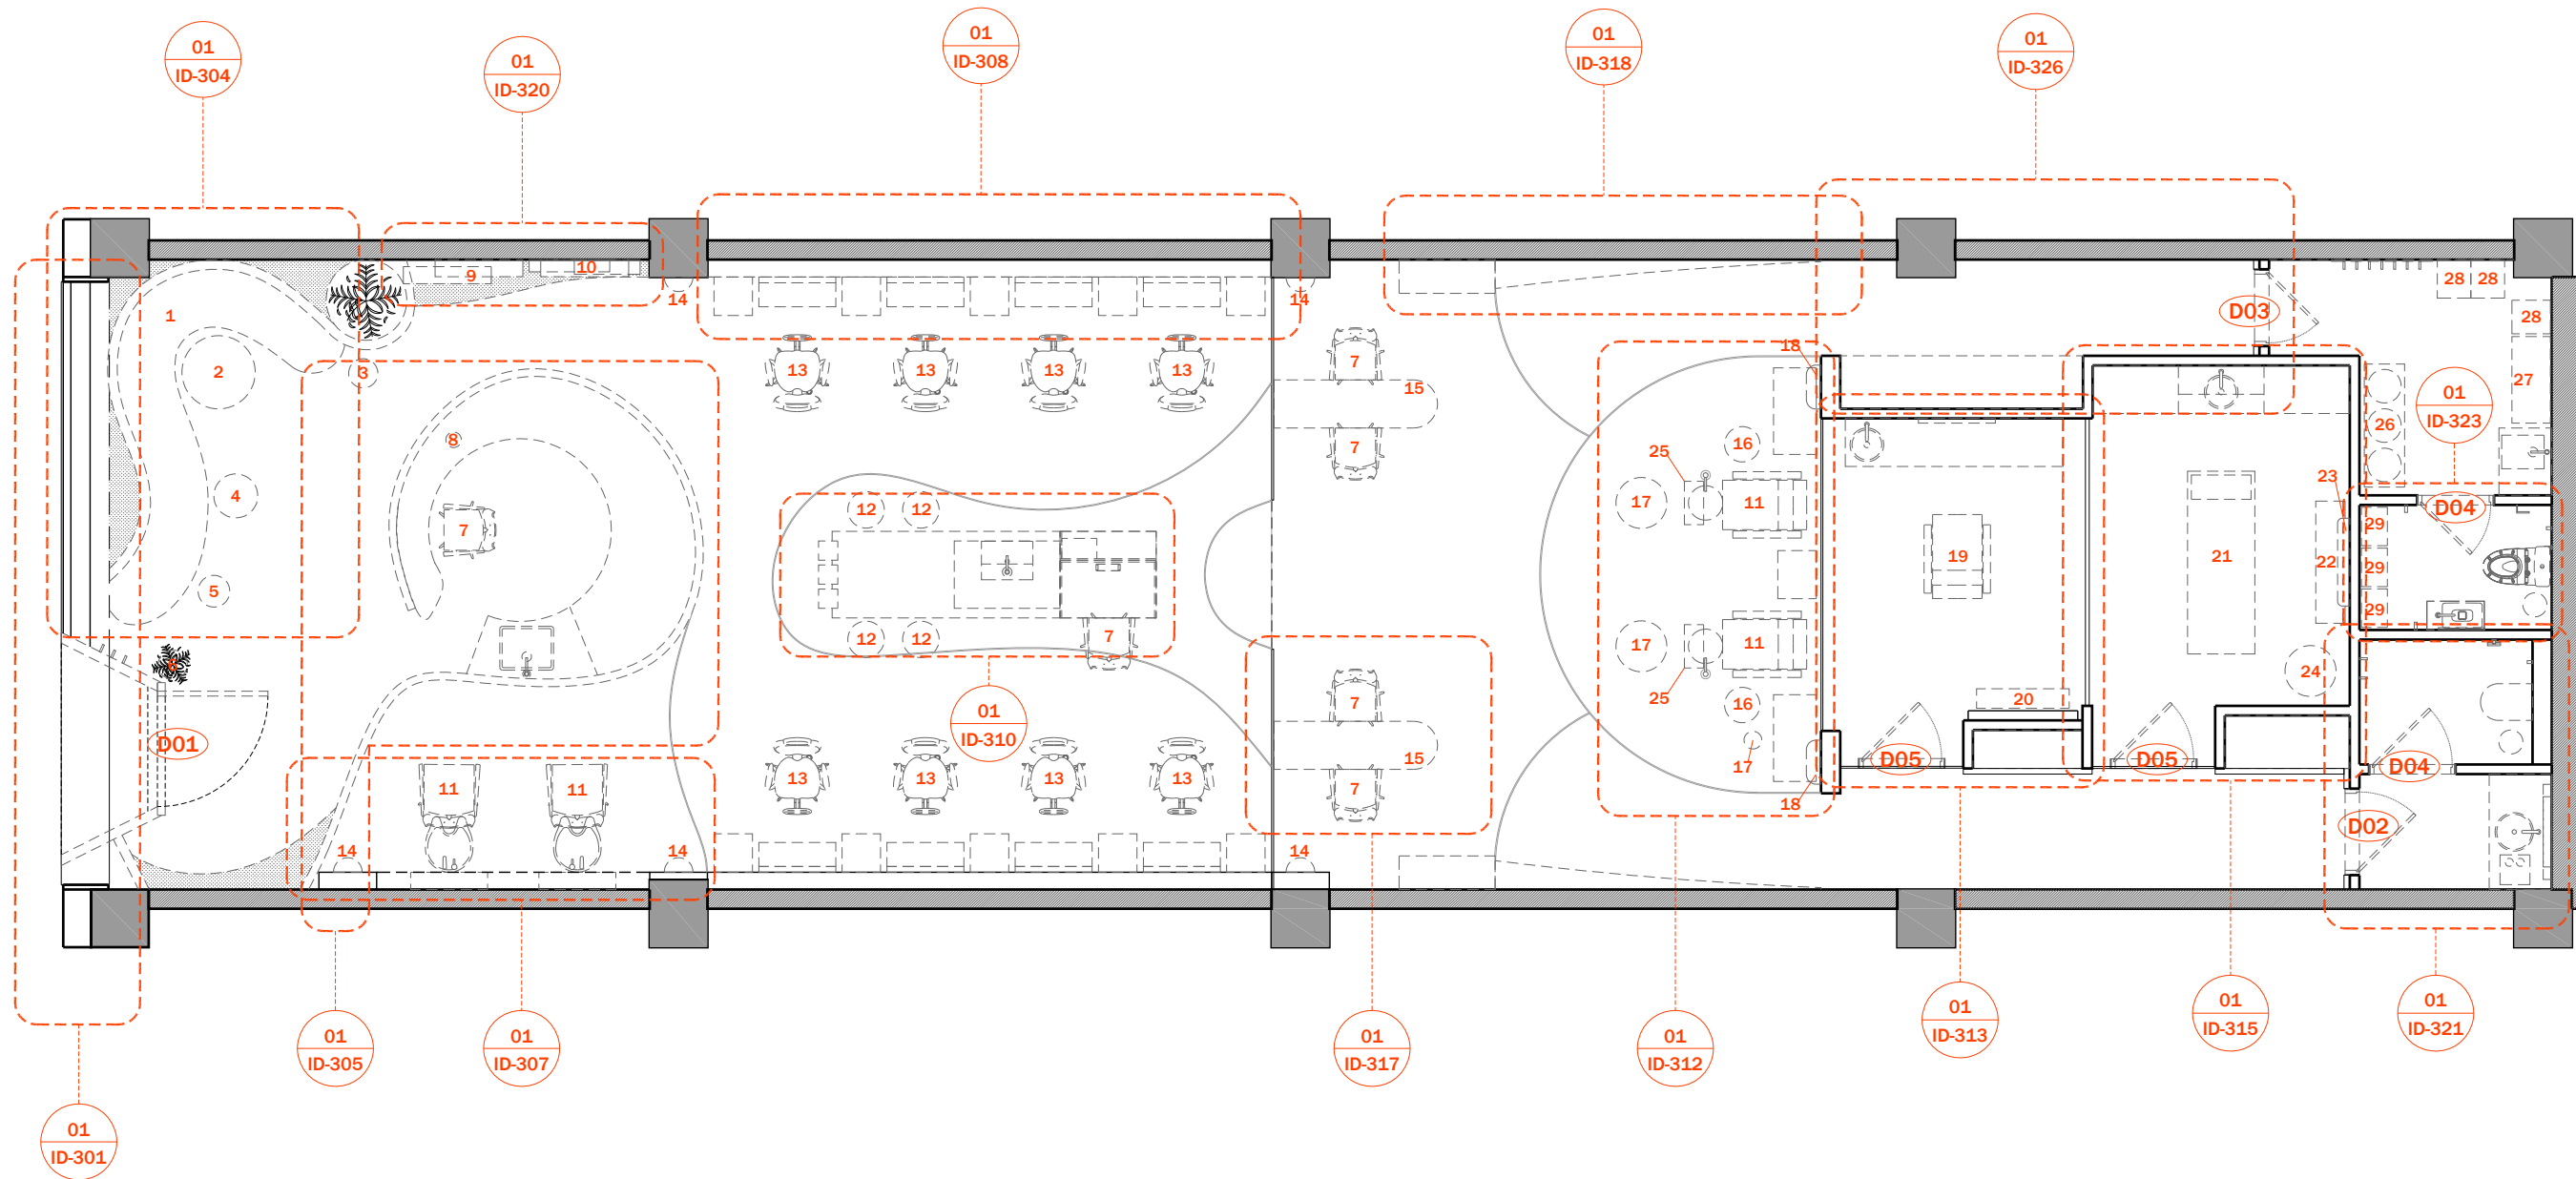

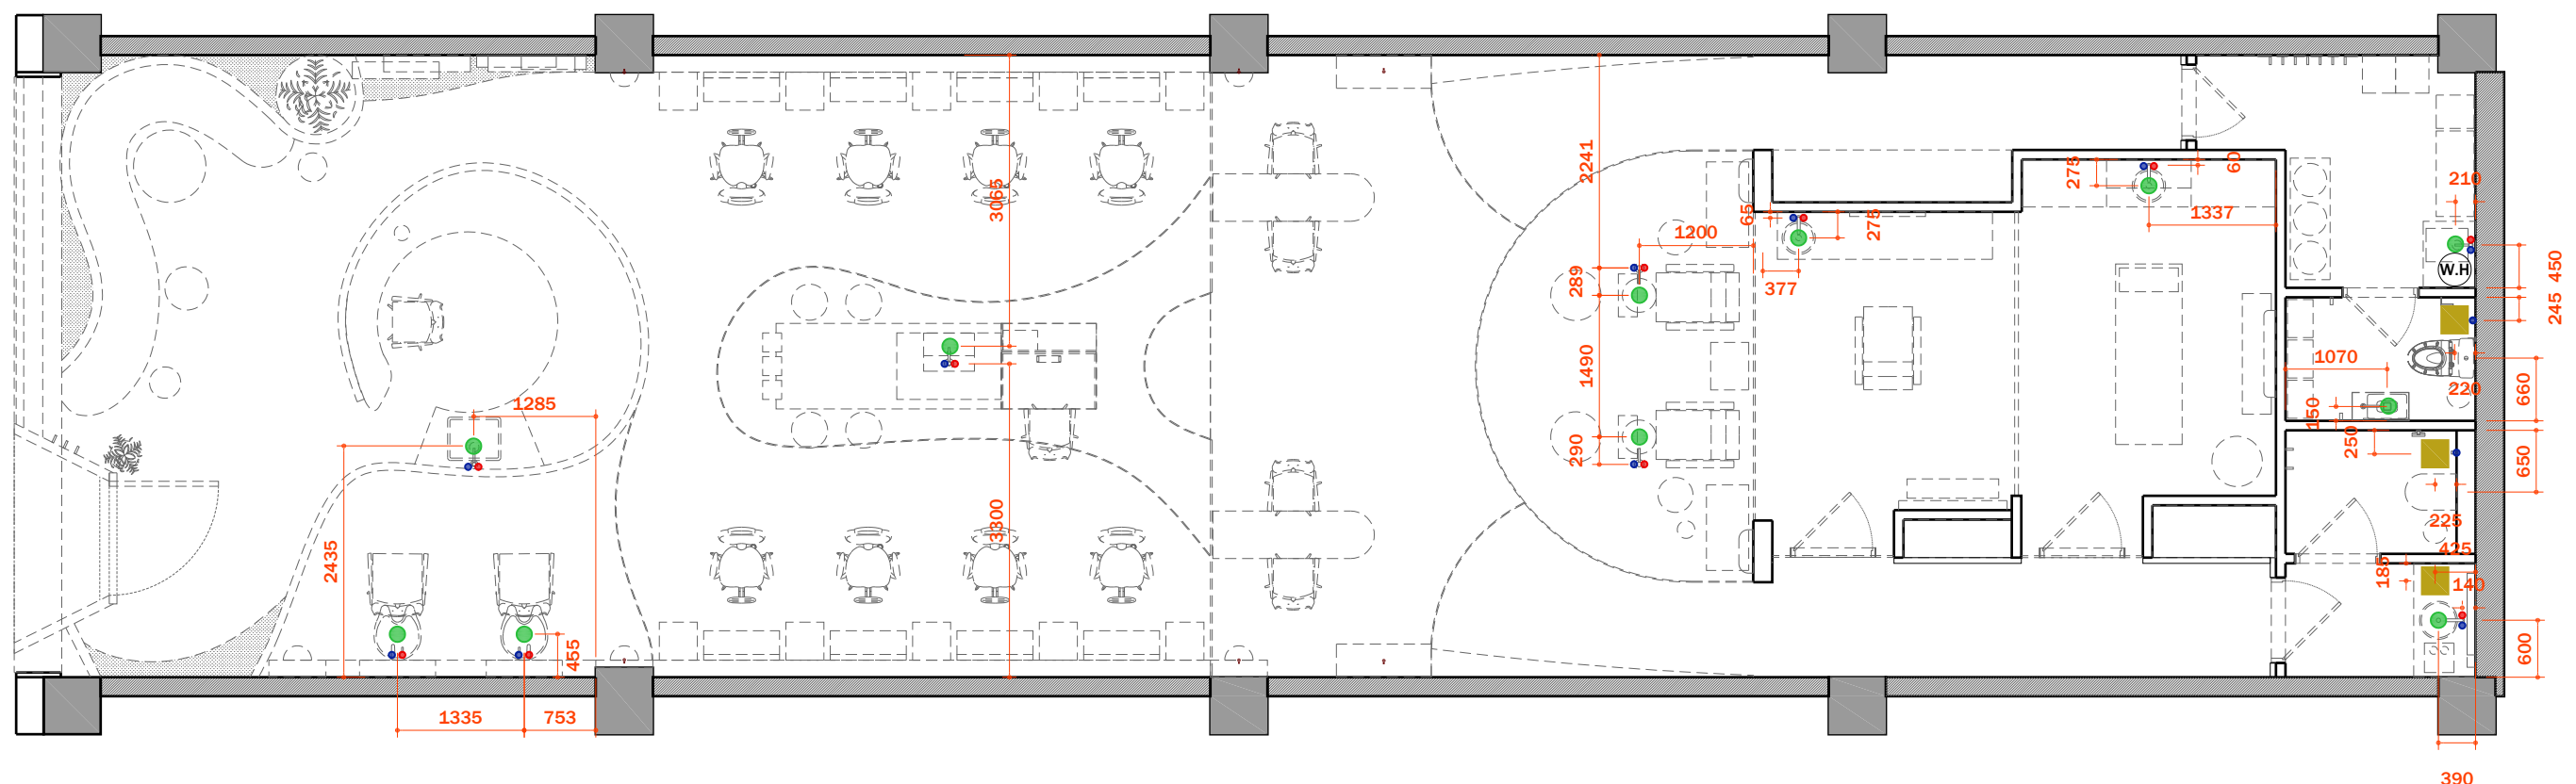


LEGEND :

-  DRAINAGE SYSTEM FOR SINKS
-  HOT AND COLD WATER SUPPLY
-  FLOOR DRAINS
-  WATER HEATER

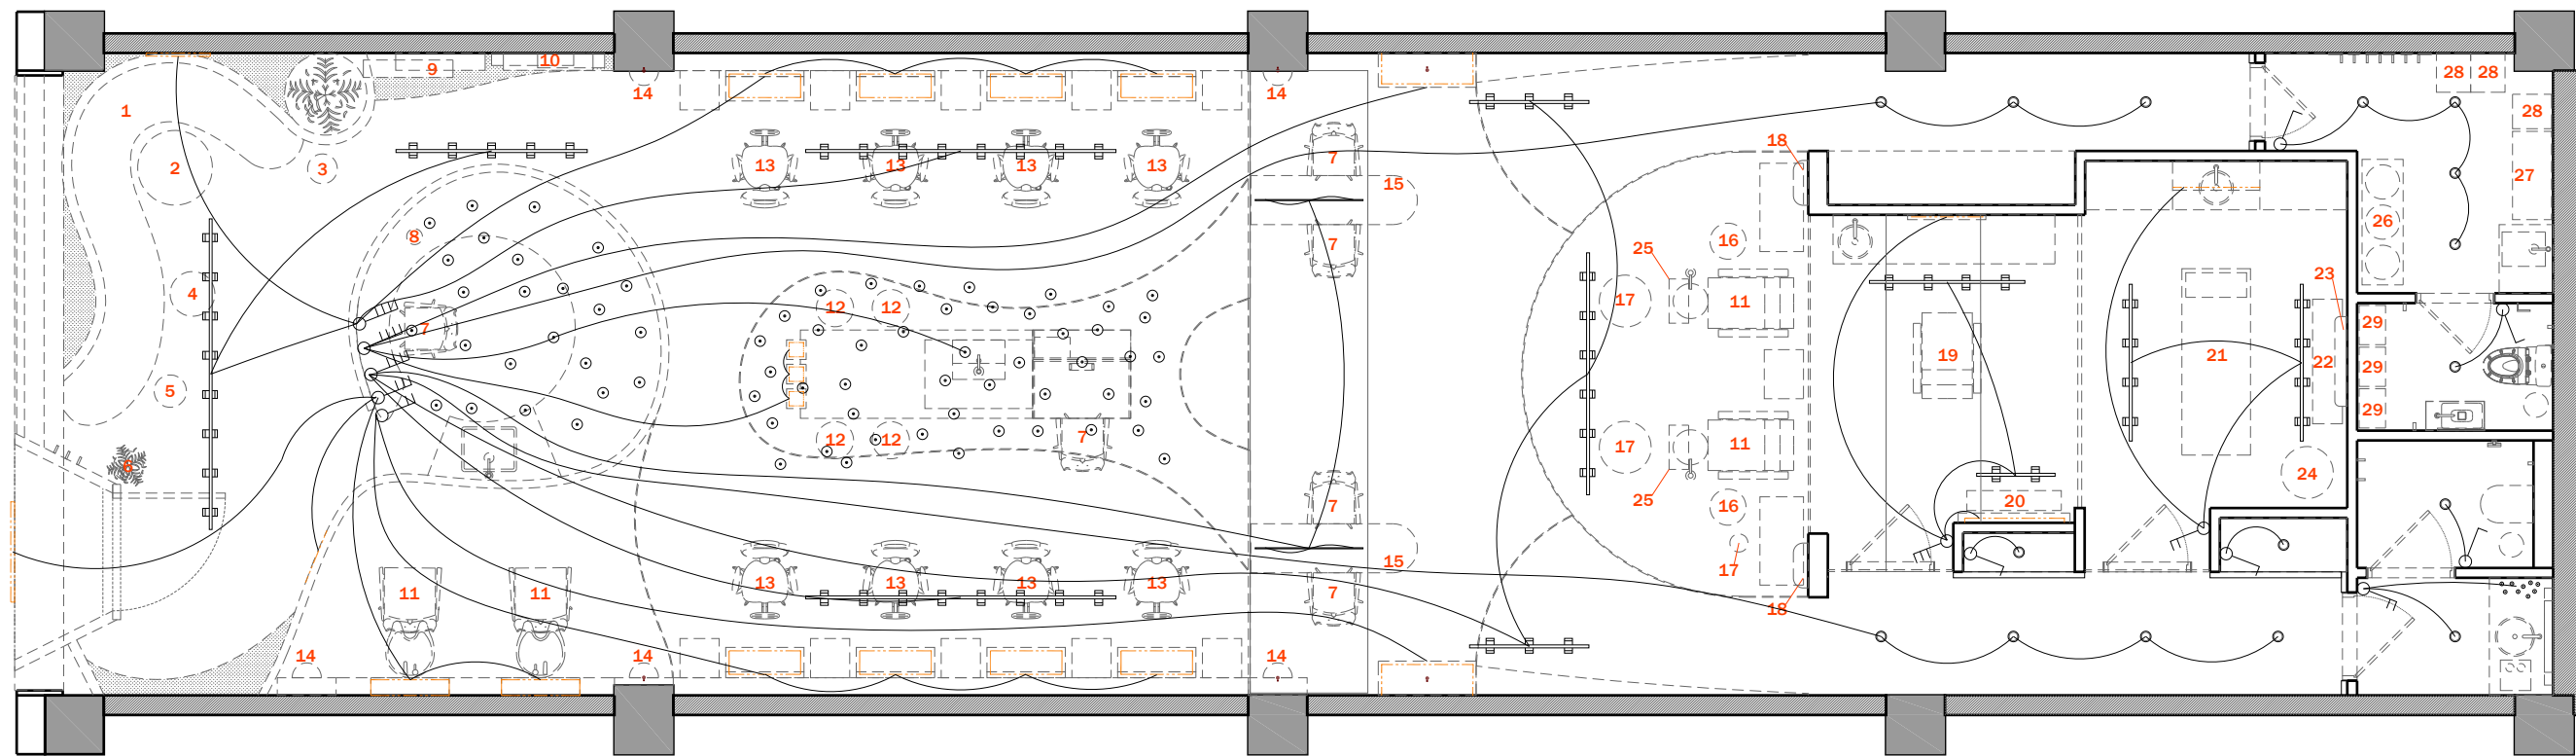

LEGEND :

- TRACK LIGHTS
- DOWN LIGHTS
- CONCEALED LIGHT
- PENDANT LIGHTS
- DECORATIVE PENDANT LIGHTS
- SQUARE CEILING DIFFUSER
- 1 GANG SWITCH
- 2 GANG SWITCH
- 3 GANG SWITCH
- 4 GANG SWITCH

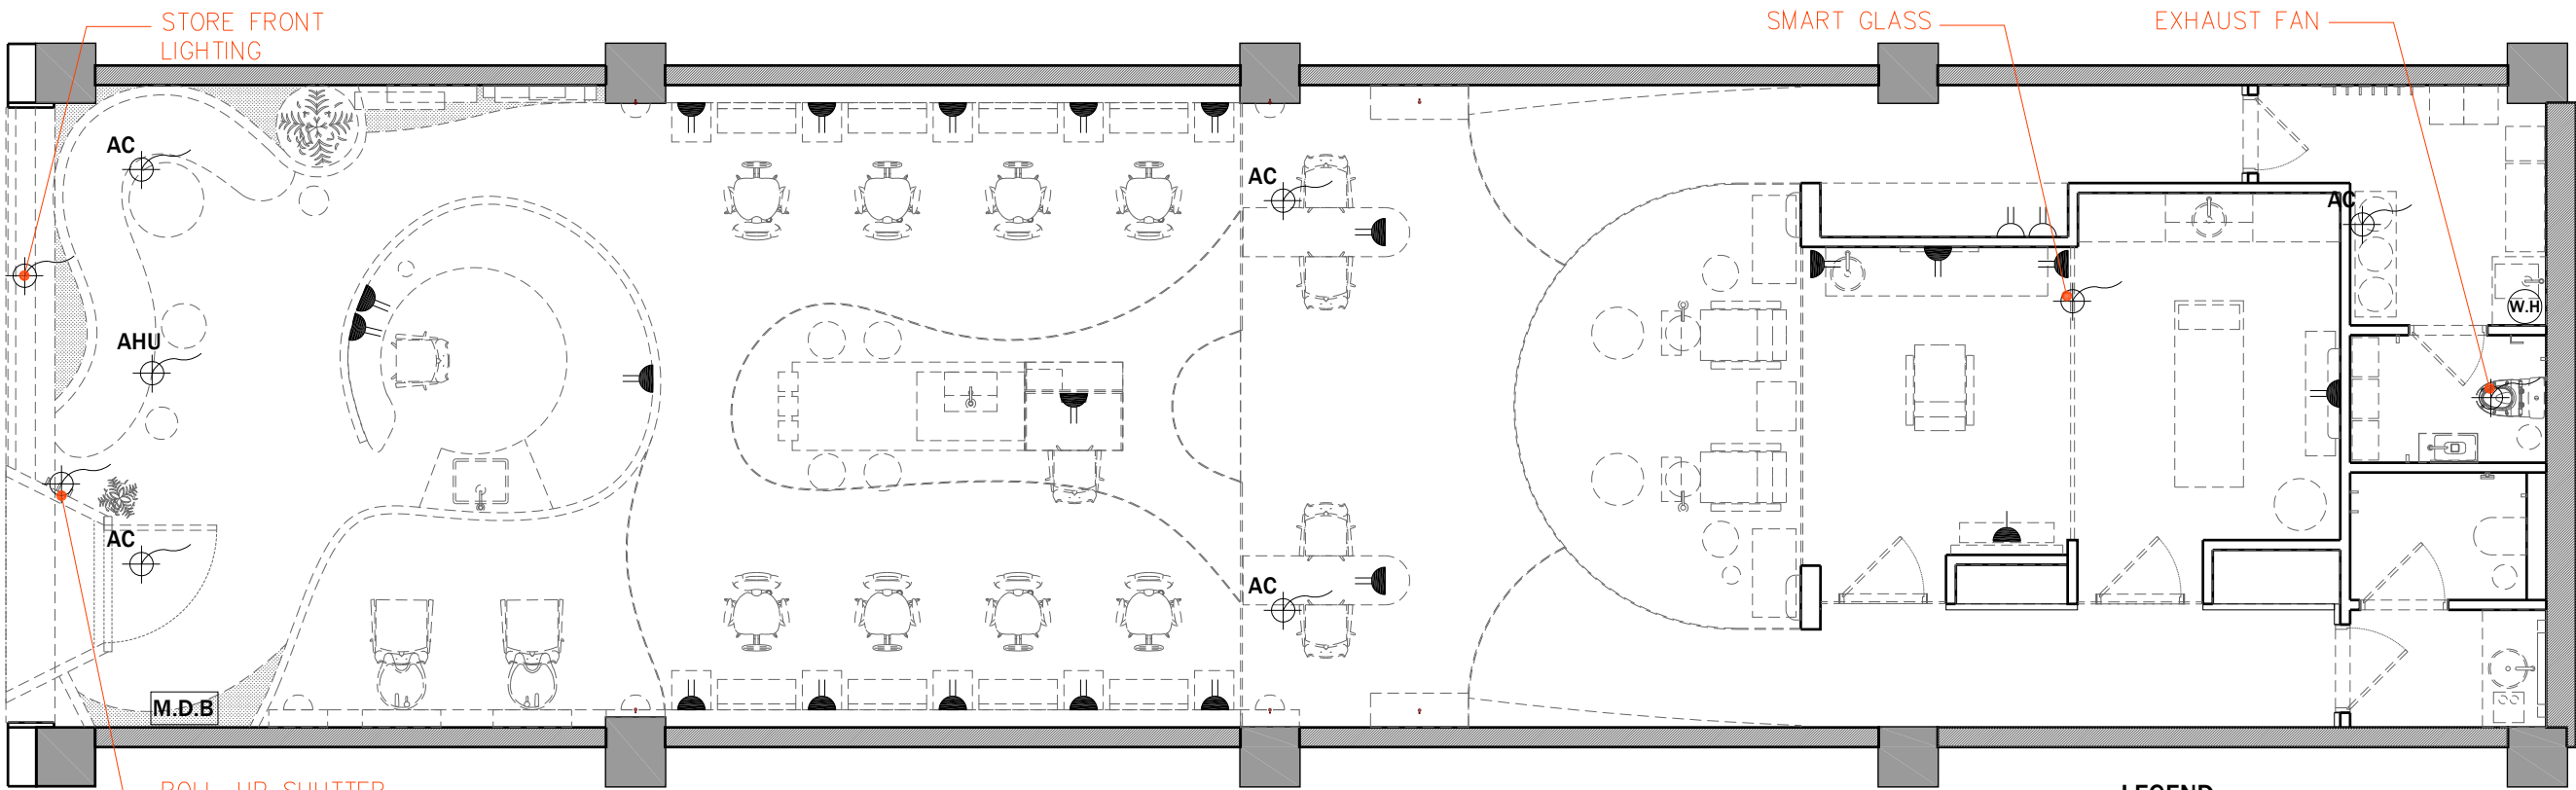

LEGEND :

220V SINGLE POWER SOCKET
ABOVE COUNTER

220V DOUBLE POWER SOCKET
ABOVE COUNTER

220V SINGLE POWER SOCKET
UNDER COUNTER

220V DOUBLE POWER SOCKET
UNDER COUNTER


W.H WATER HEATER

AC PROVISION FOR AC

PROVISION FOR FIXTURES AND
EQUIPMENTS

AHU PROVISION FOR AHU

M.D.B ELECTRICAL M.D.B

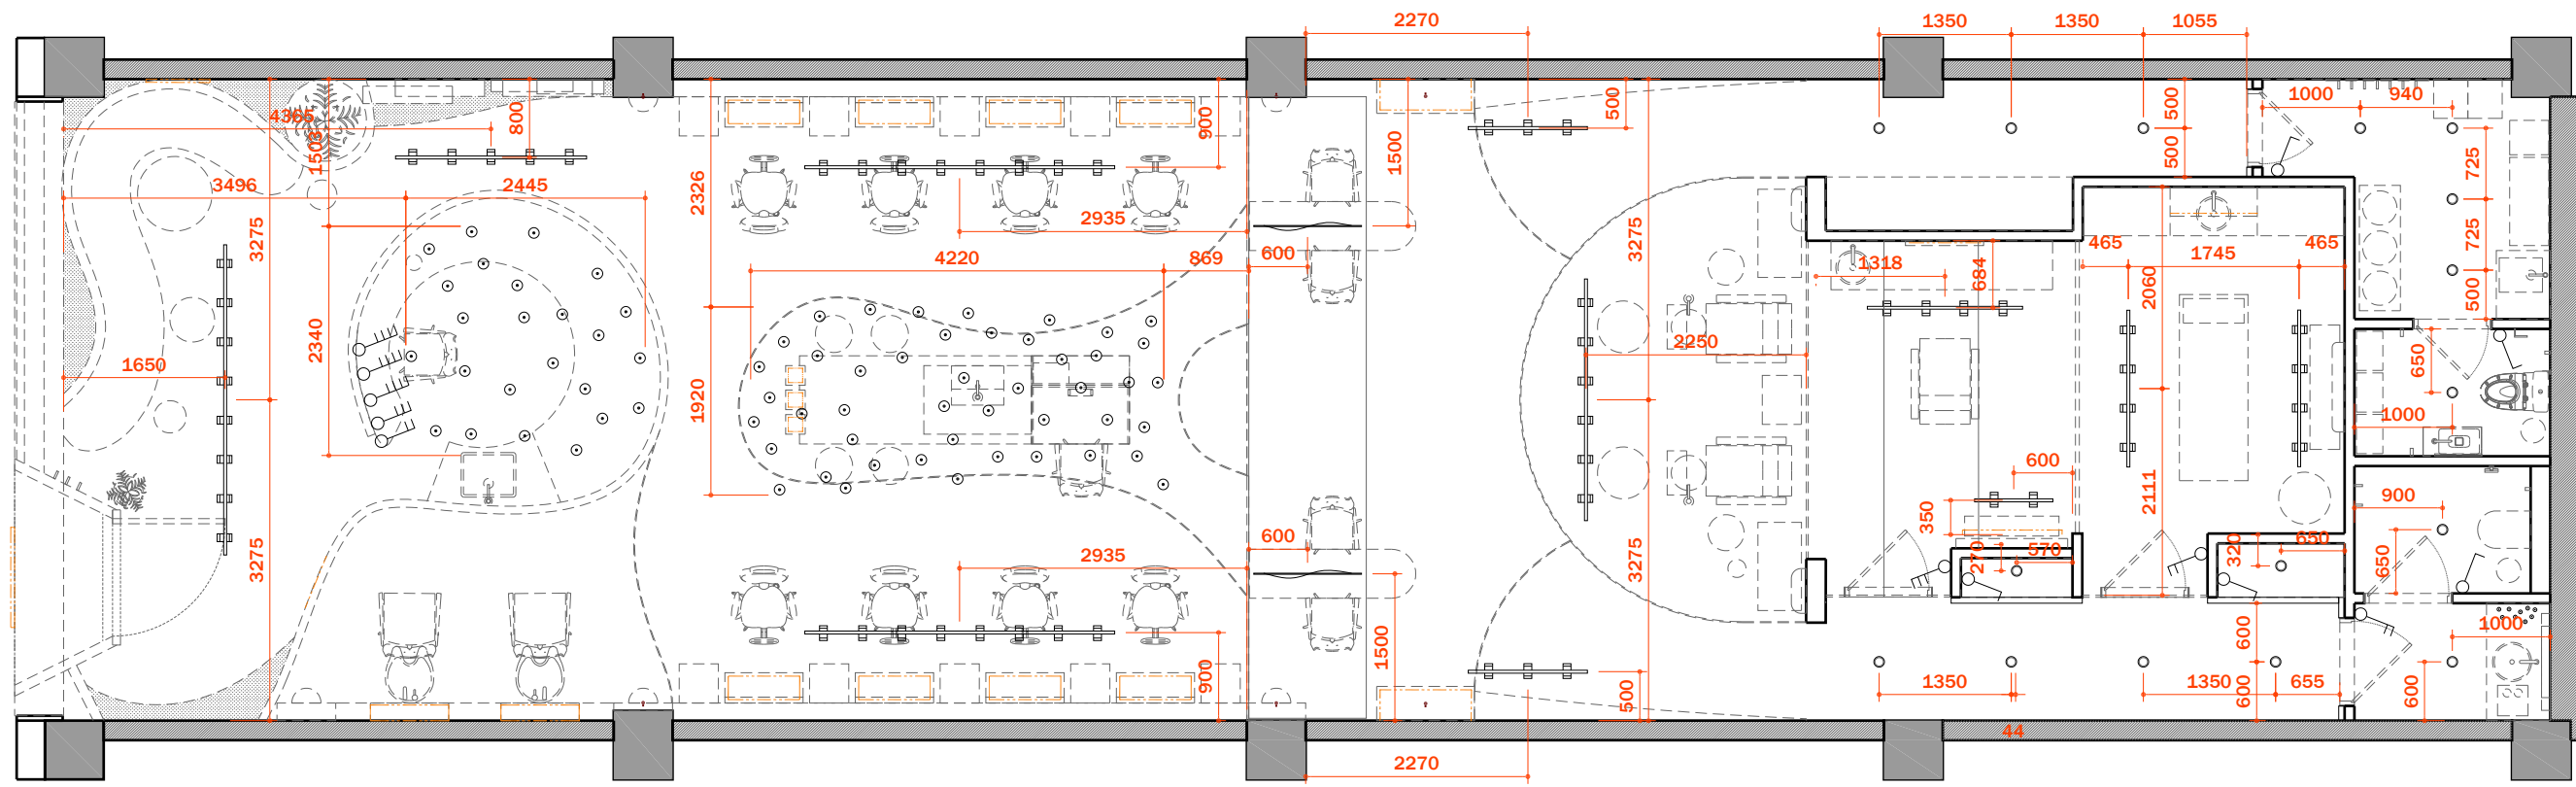



LEGEND :

- TRACK LIGHTS
- DOWN LIGHTS
- CONCEALED LIGHT
- PENDANT LIGHTS
- DECORATIVE PENDANT LIGHTS
- SQUARE CEILING DIFFUSER
- 1 GANG SWITCH
- 2 GANG SWITCH
- 3 GANG SWITCH
- 4 GANG SWITCH




PRINT ON A3 ©2021

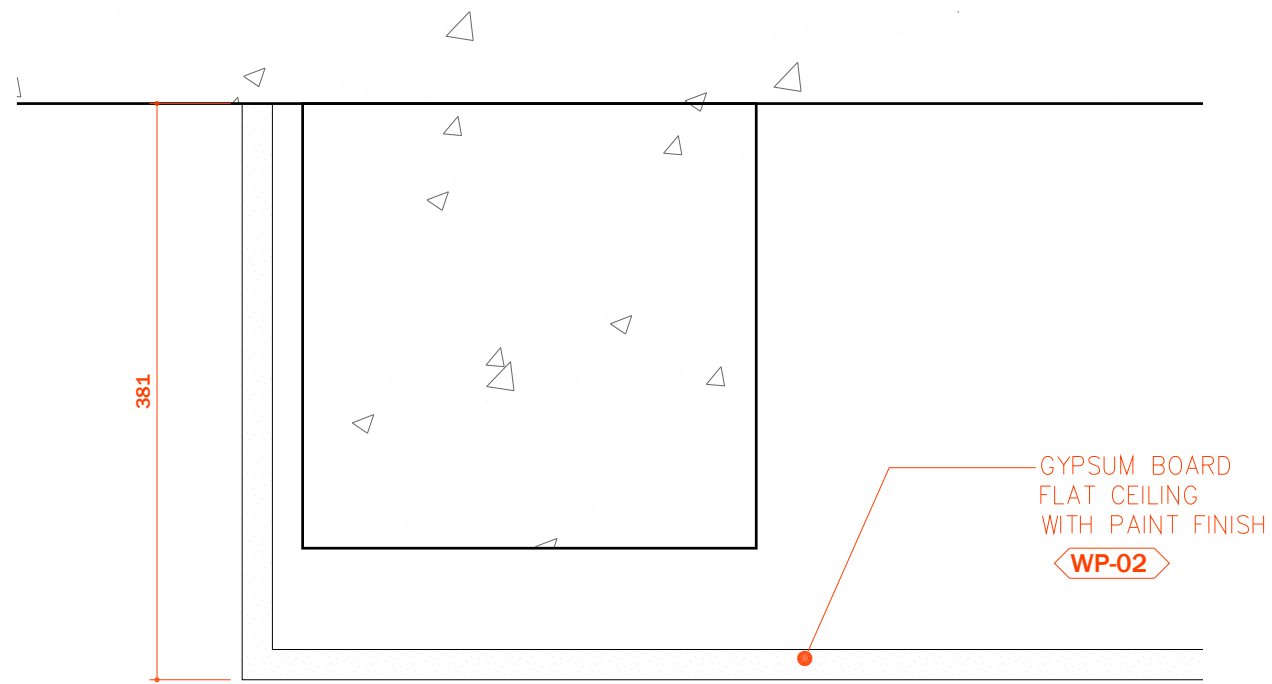

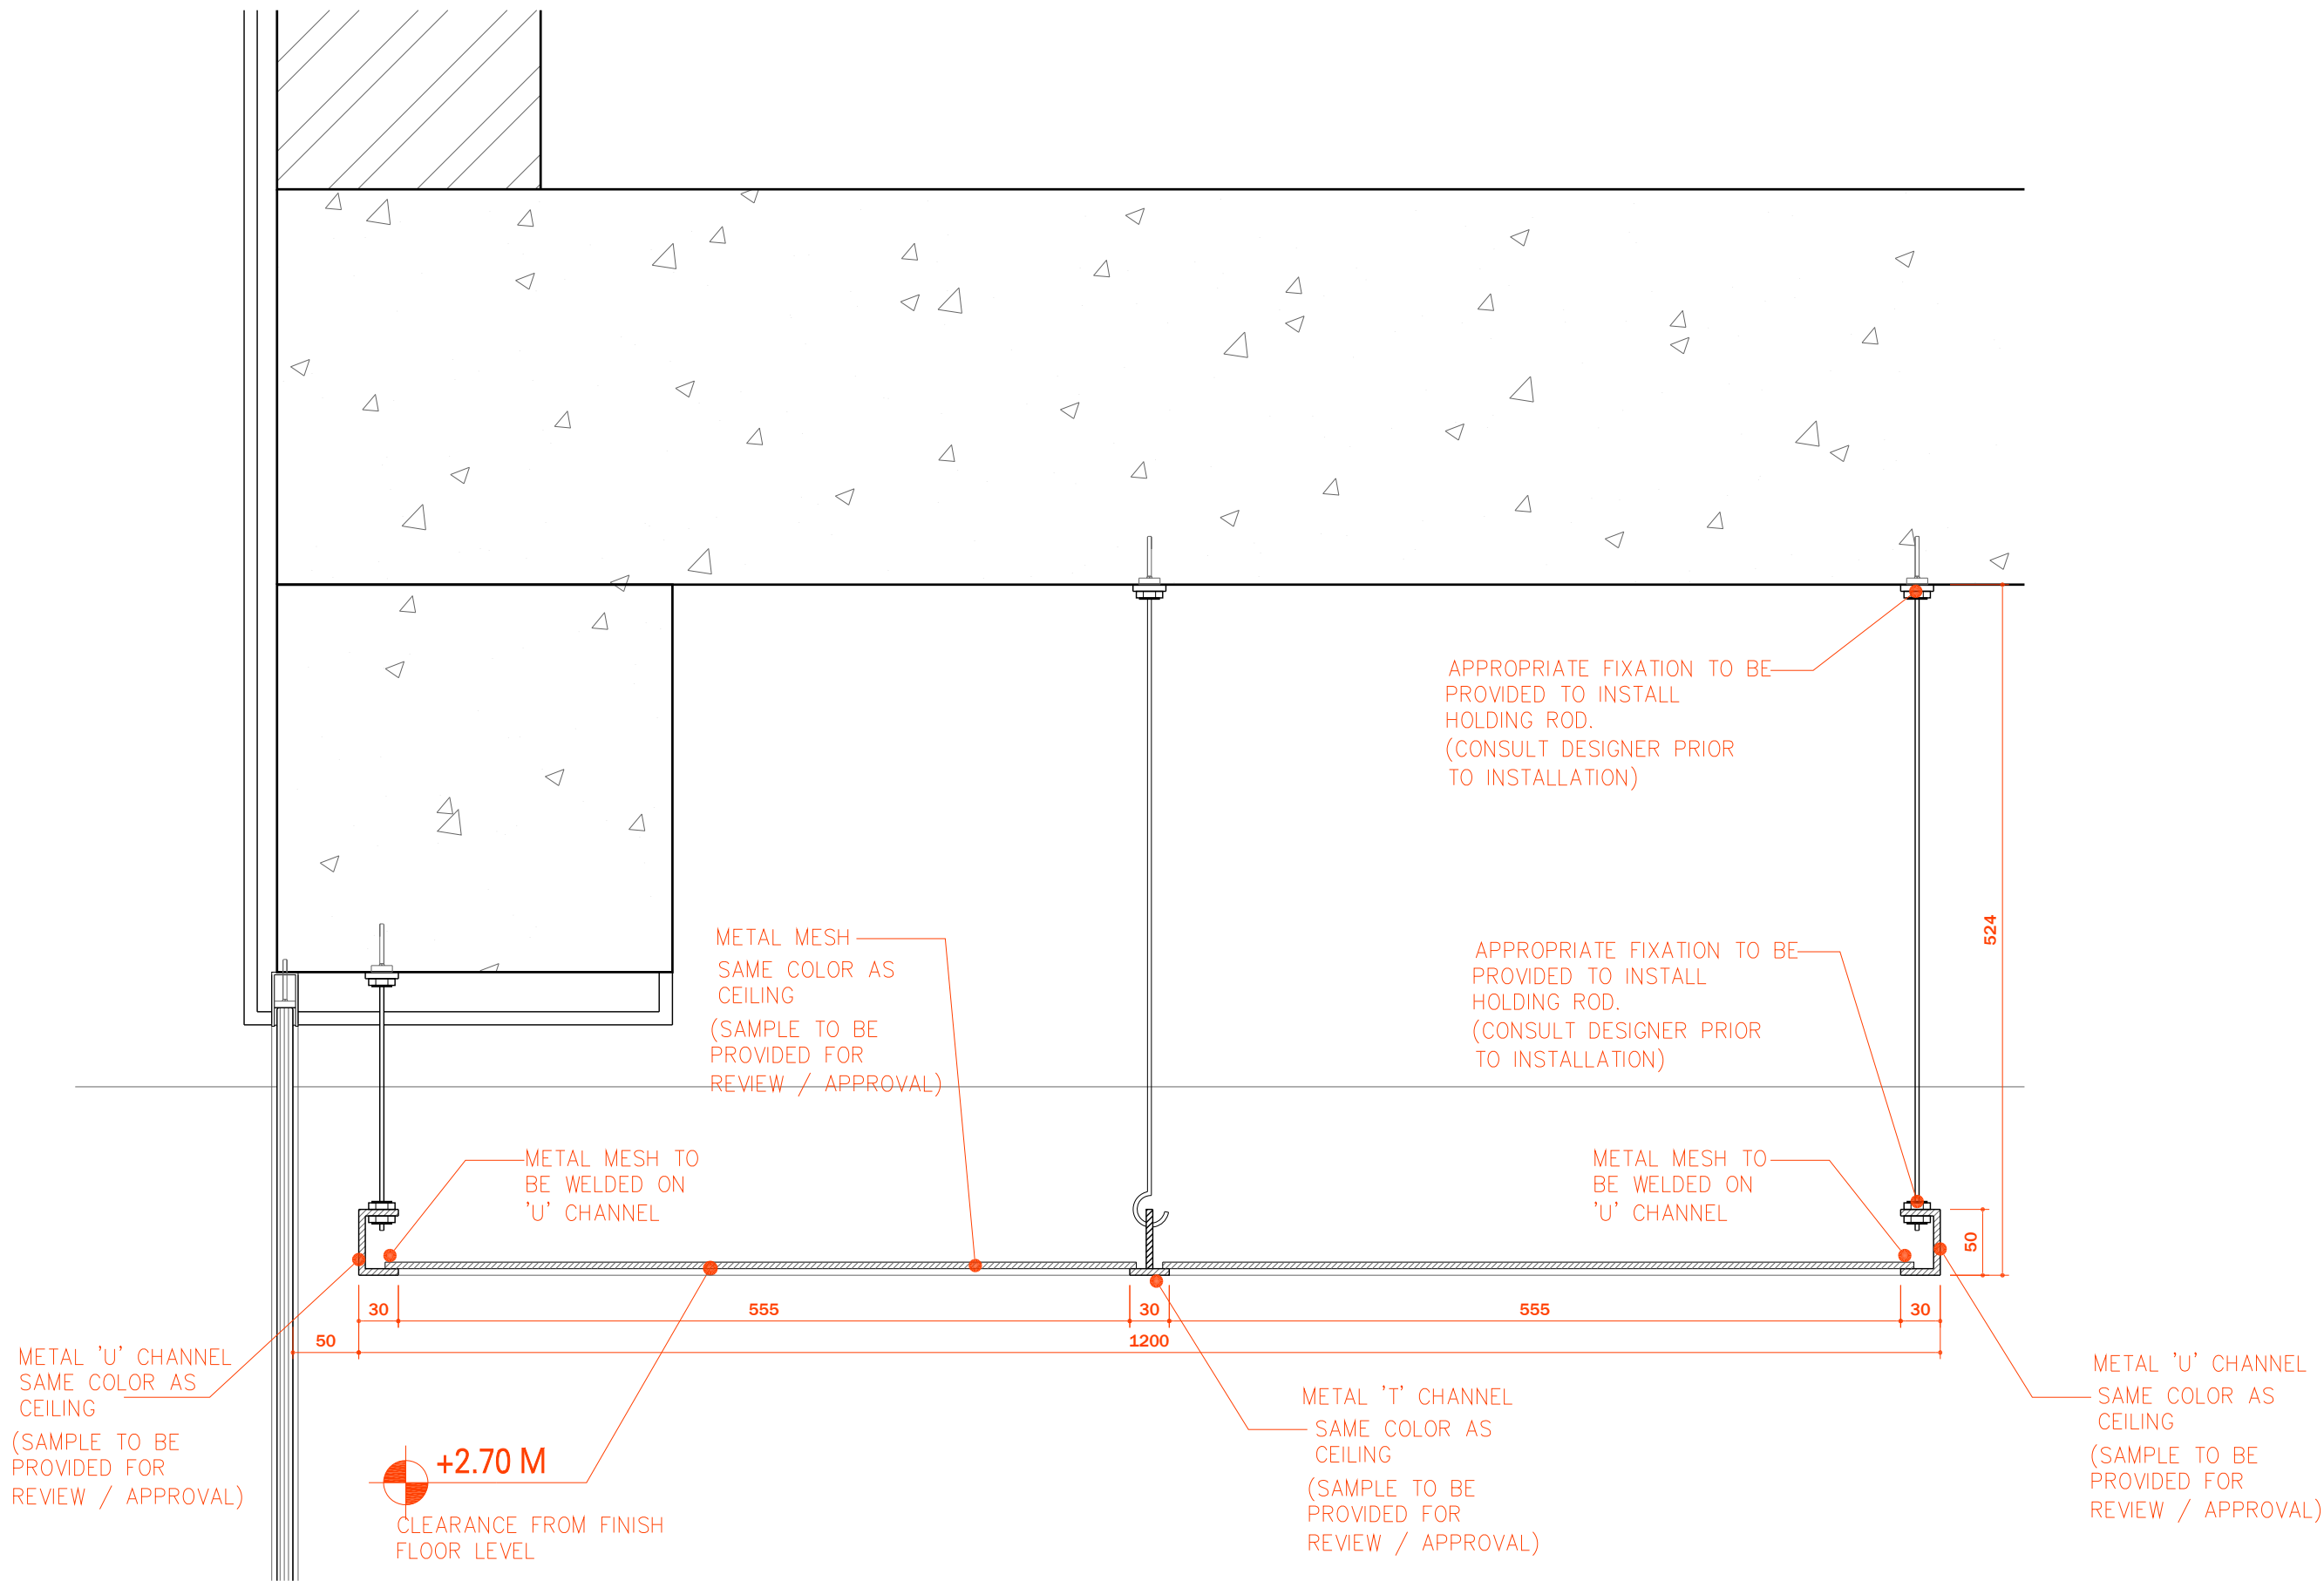

01 METAL MESH CEILING SECTION DETAIL
SCALE 1:5

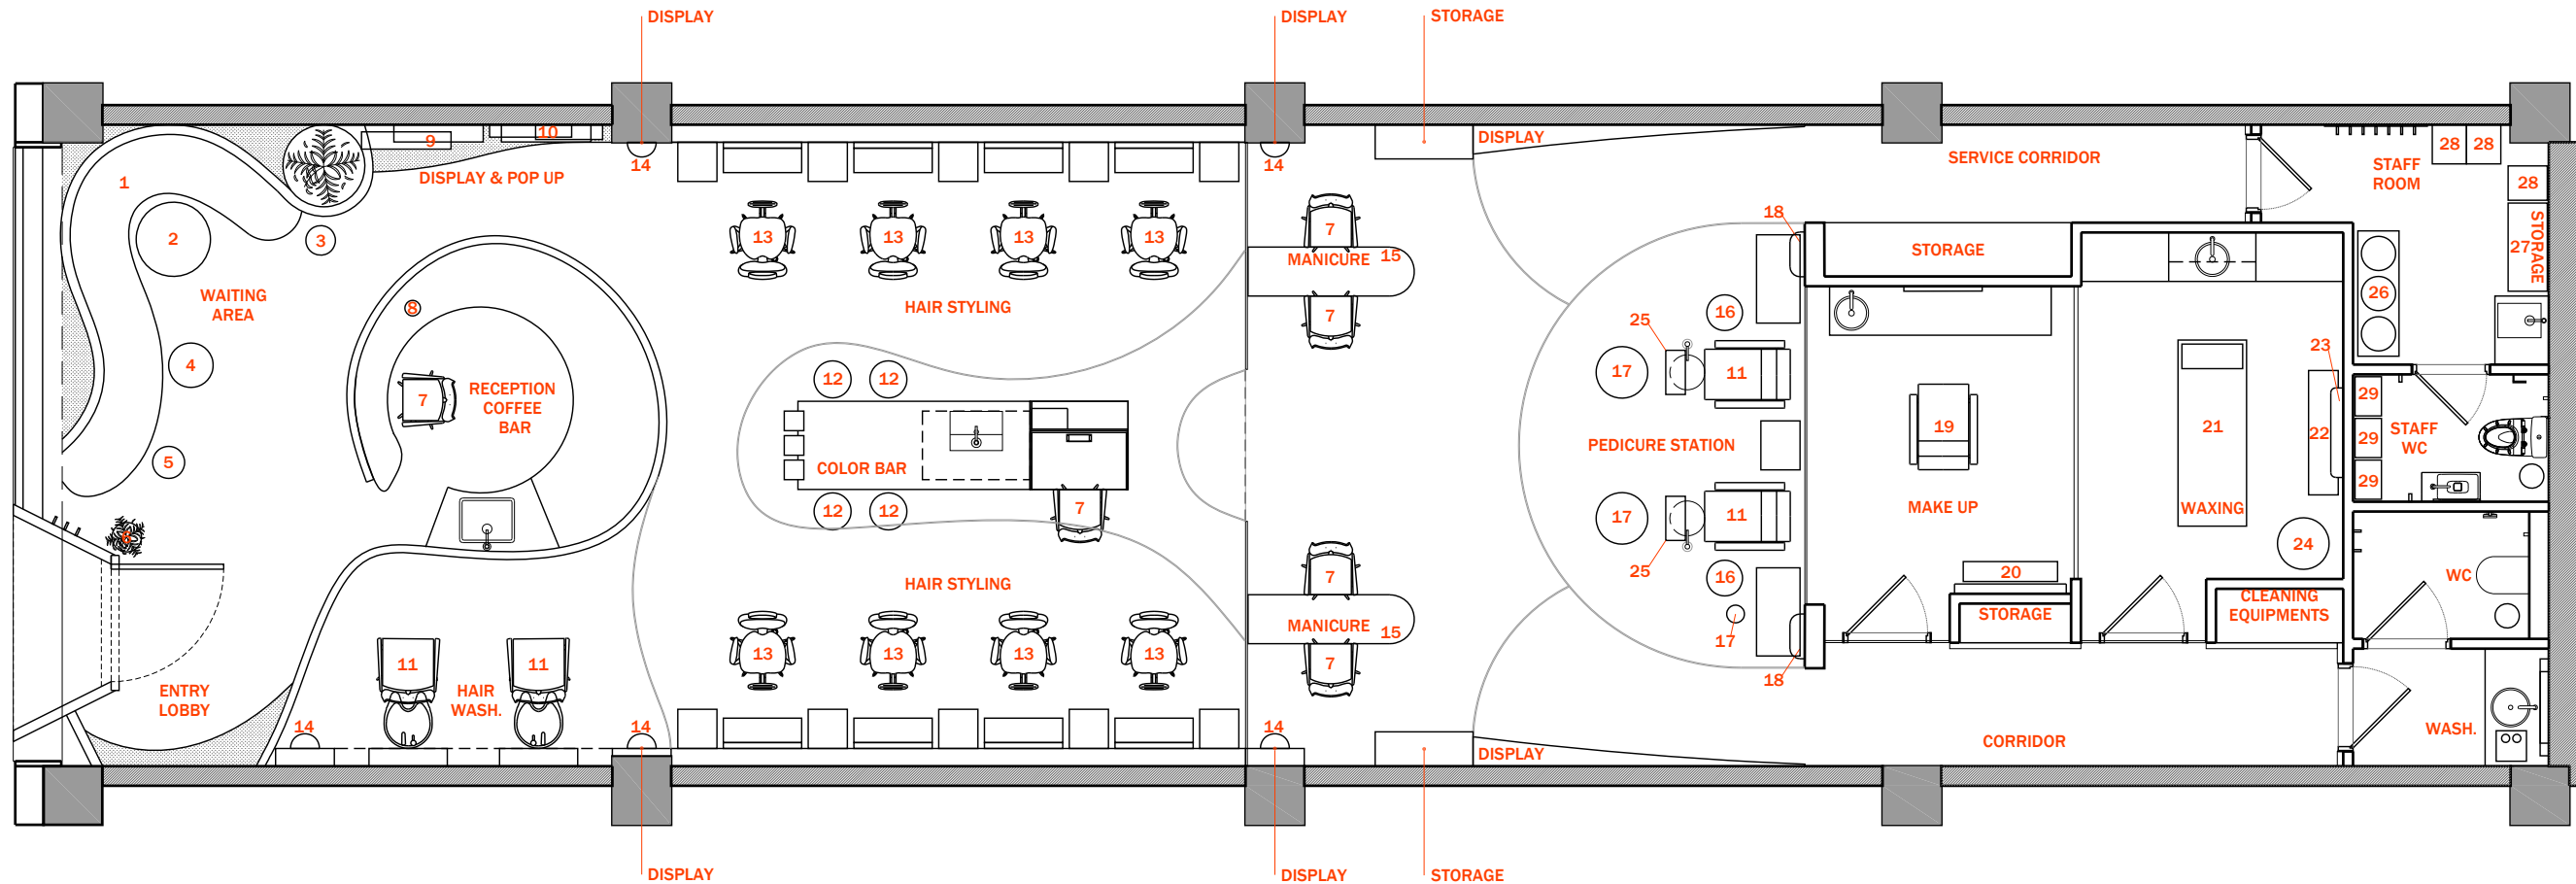

FURNITURE LAYOUT
SCALE 1:75



the
ORJWANI

210305

01. 2021

DATE ISSUED

28.09.2025

Revisions

Issue Date

Notes

- 1.
- 2.
- 3.

Project North

PHASE

EXEC DRAWINGS

TRADE

INTERIOR DRAWING

Scale





1:75

GROUND FLOOR FLOORING + FINISHING LAYOUT

ID-202

PRINT ON A3

©2021

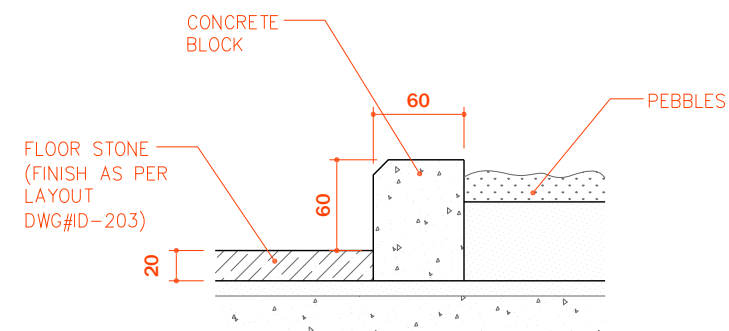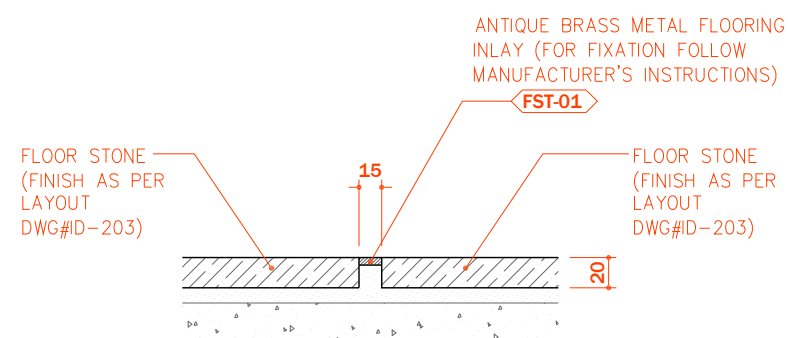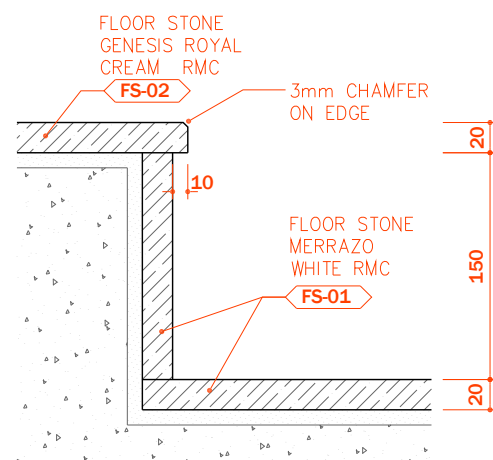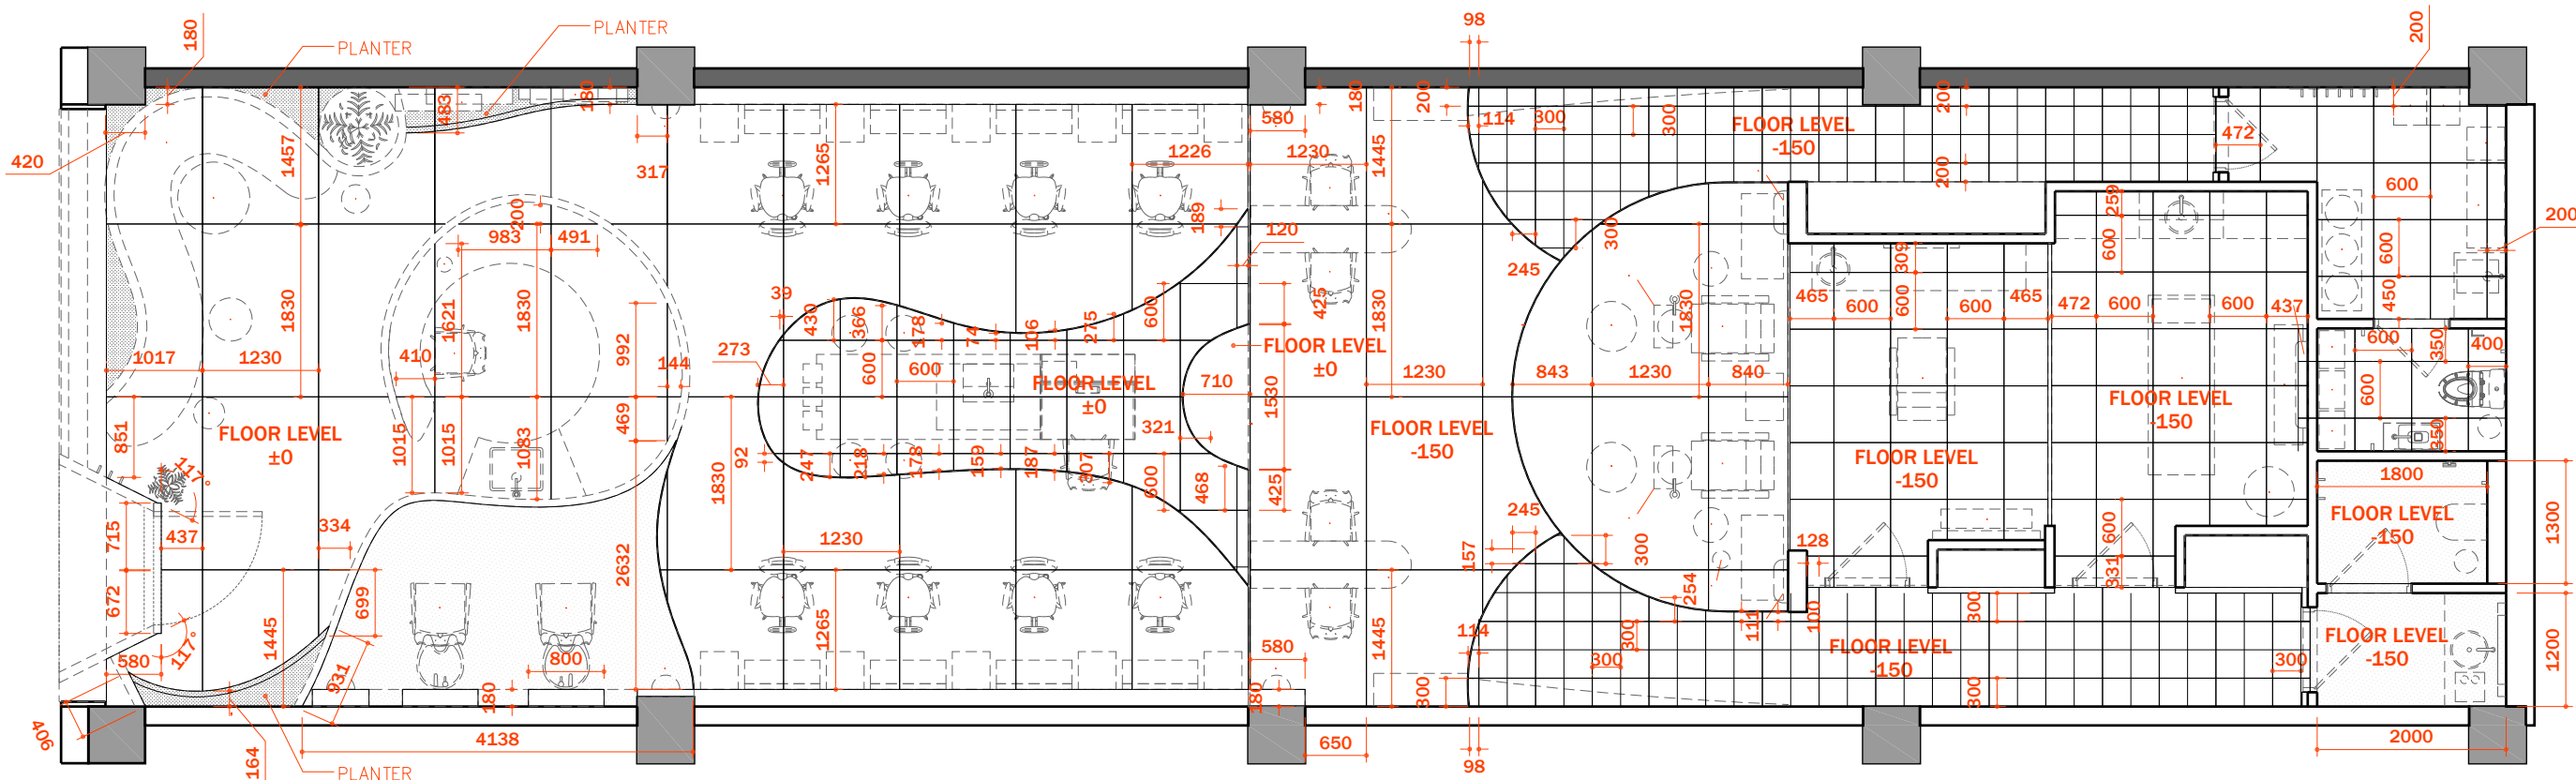


GENERAL NOTES

1. This drawing shall be read in conjunction with all other relevant architectural, structural & electrical drawings including those of other consultants.
2. It is the responsibility of contractors & manufacturers to check all relevant site dimensions prior to the start of construction or manufacture.
3. All materials and components must be installed on site in accordance with manufacturer's instructions, shop drawings and standard details.
4. All dimensions are in millimeters unless noted otherwise.

NOTES FOR MANUFACTURER:

- * Construction methods shown on drawings are suggested methods only.
* Full shop drawings and samples are to be provided by contractor for approval prior to manufacture.


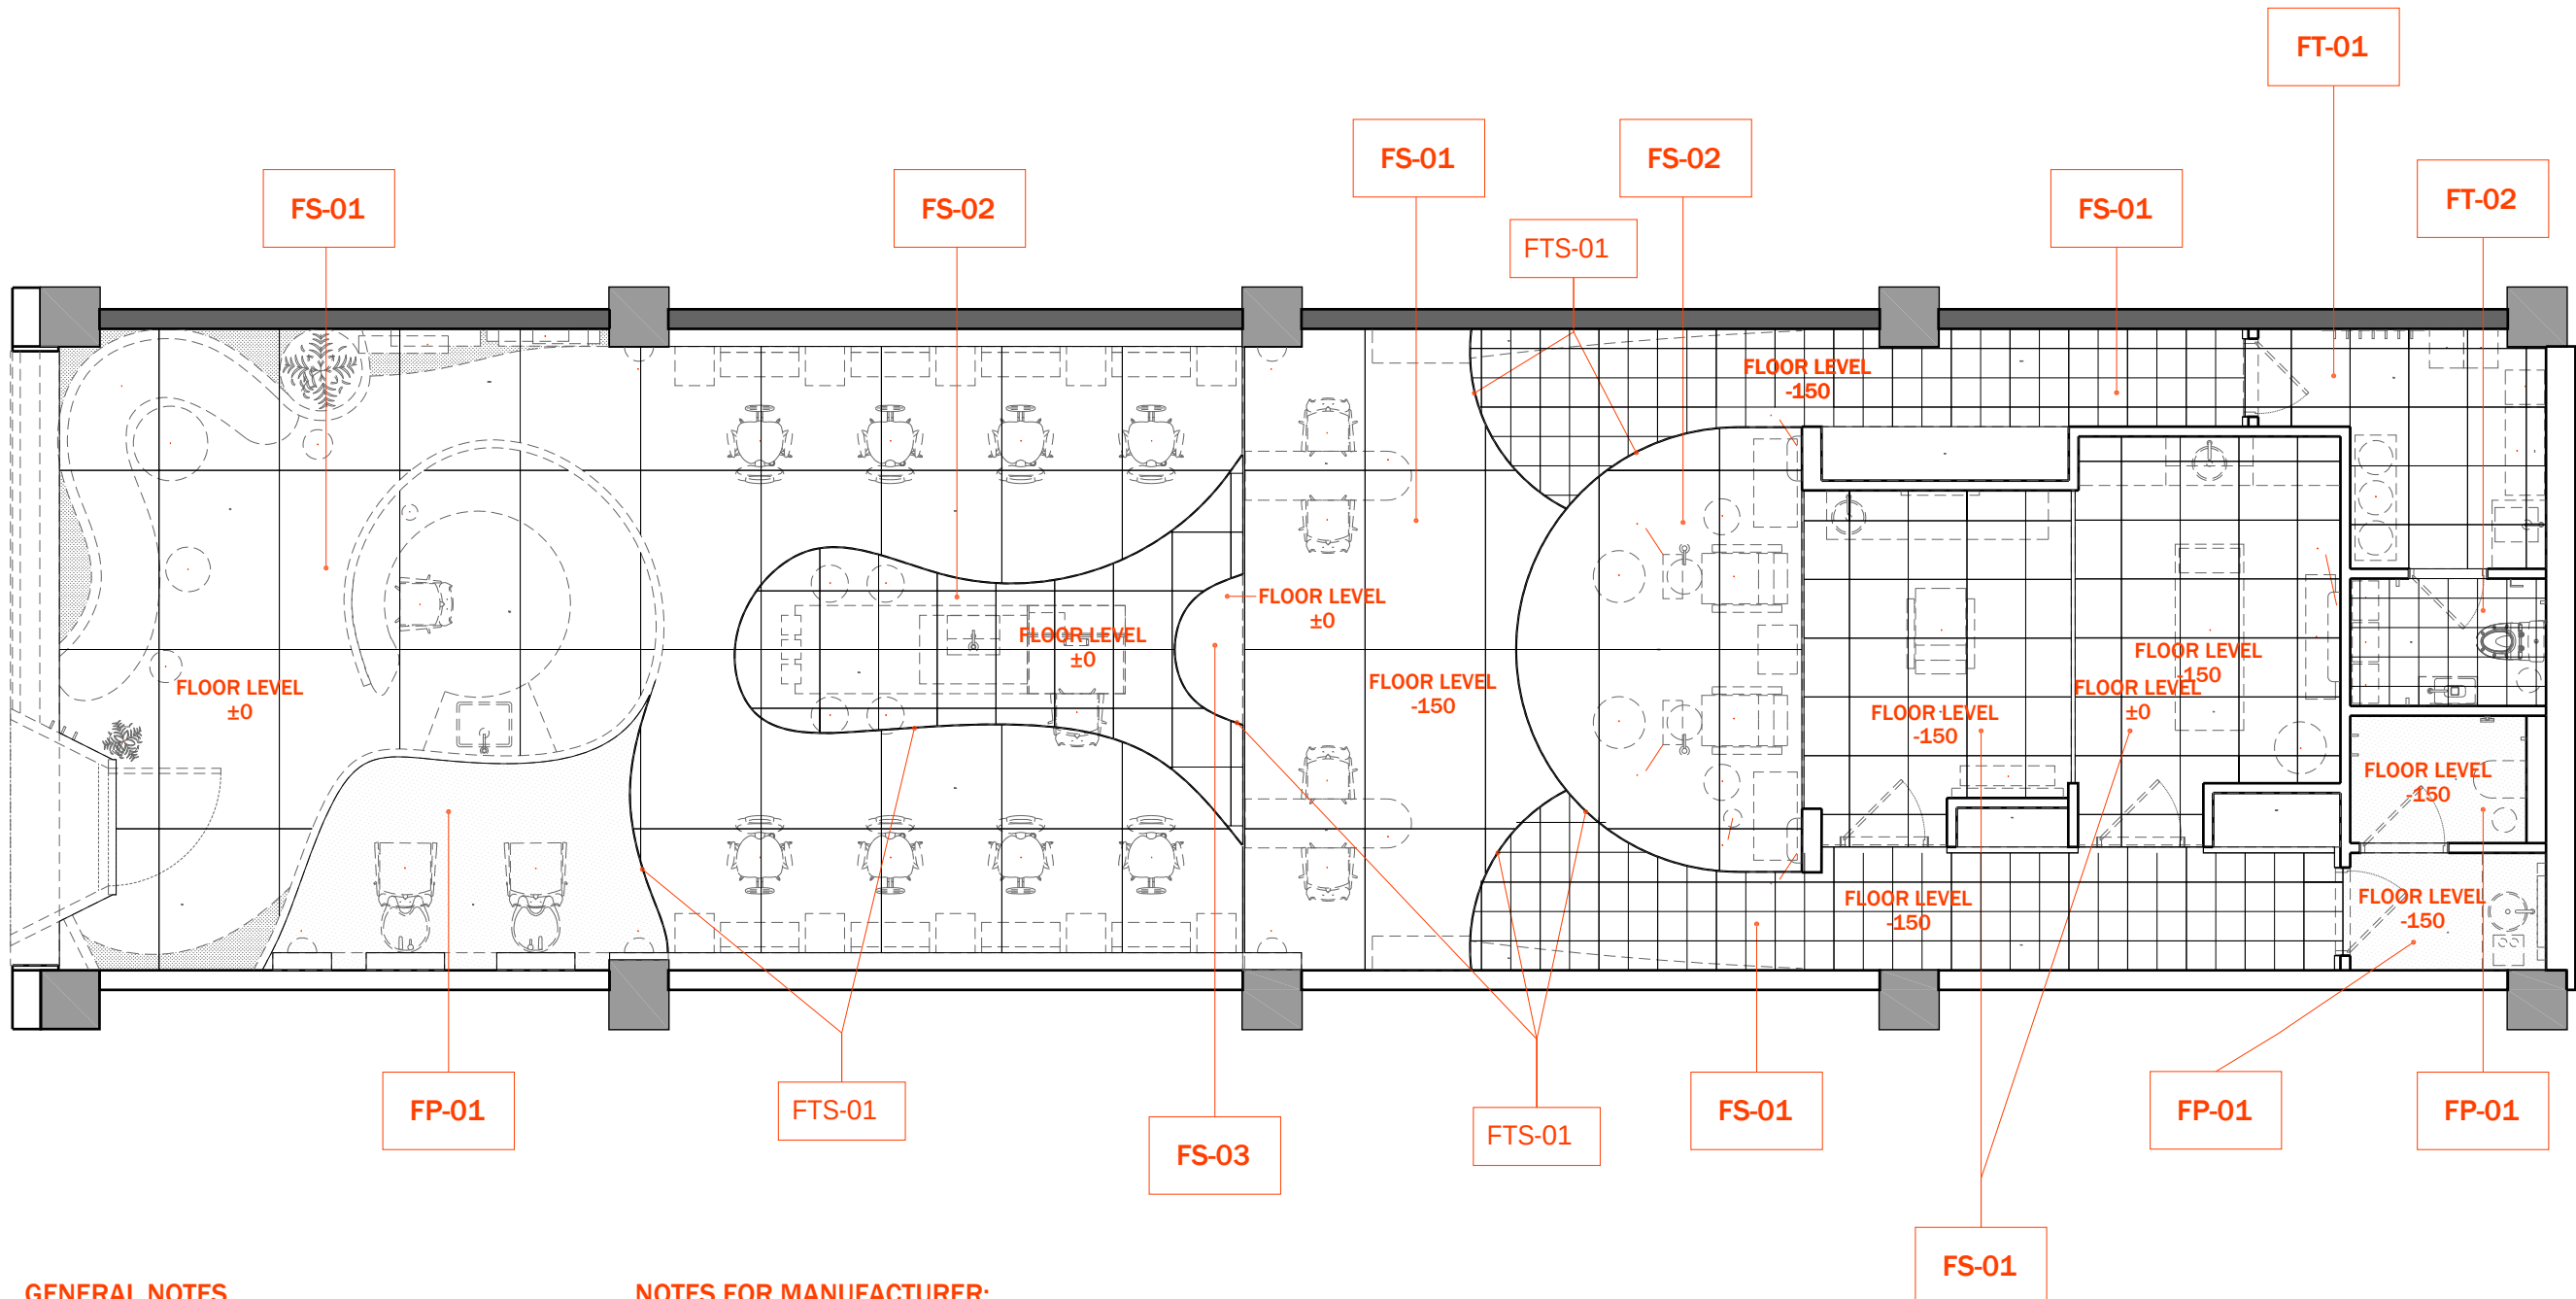






GENERAL NOTES

1. This drawing shall be read in conjunction with all other relevant architectural, structural & electrical drawings including those of other consultants.
2. It is the responsibility of contractors & manufacturers to check all relevant site dimensions prior to the start of construction or manufacture.
3. All materials and components must be installed on site in accordance with manufacturer's instructions, shop drawings and standard details.
4. All dimensions are in millimeters unless noted otherwise.

NOTES FOR MANUFACTURER:

- * Construction methods shown on drawings are suggested methods only.
- * Full shop drawings and samples are to be provided by contractor for approval prior to manufacture.

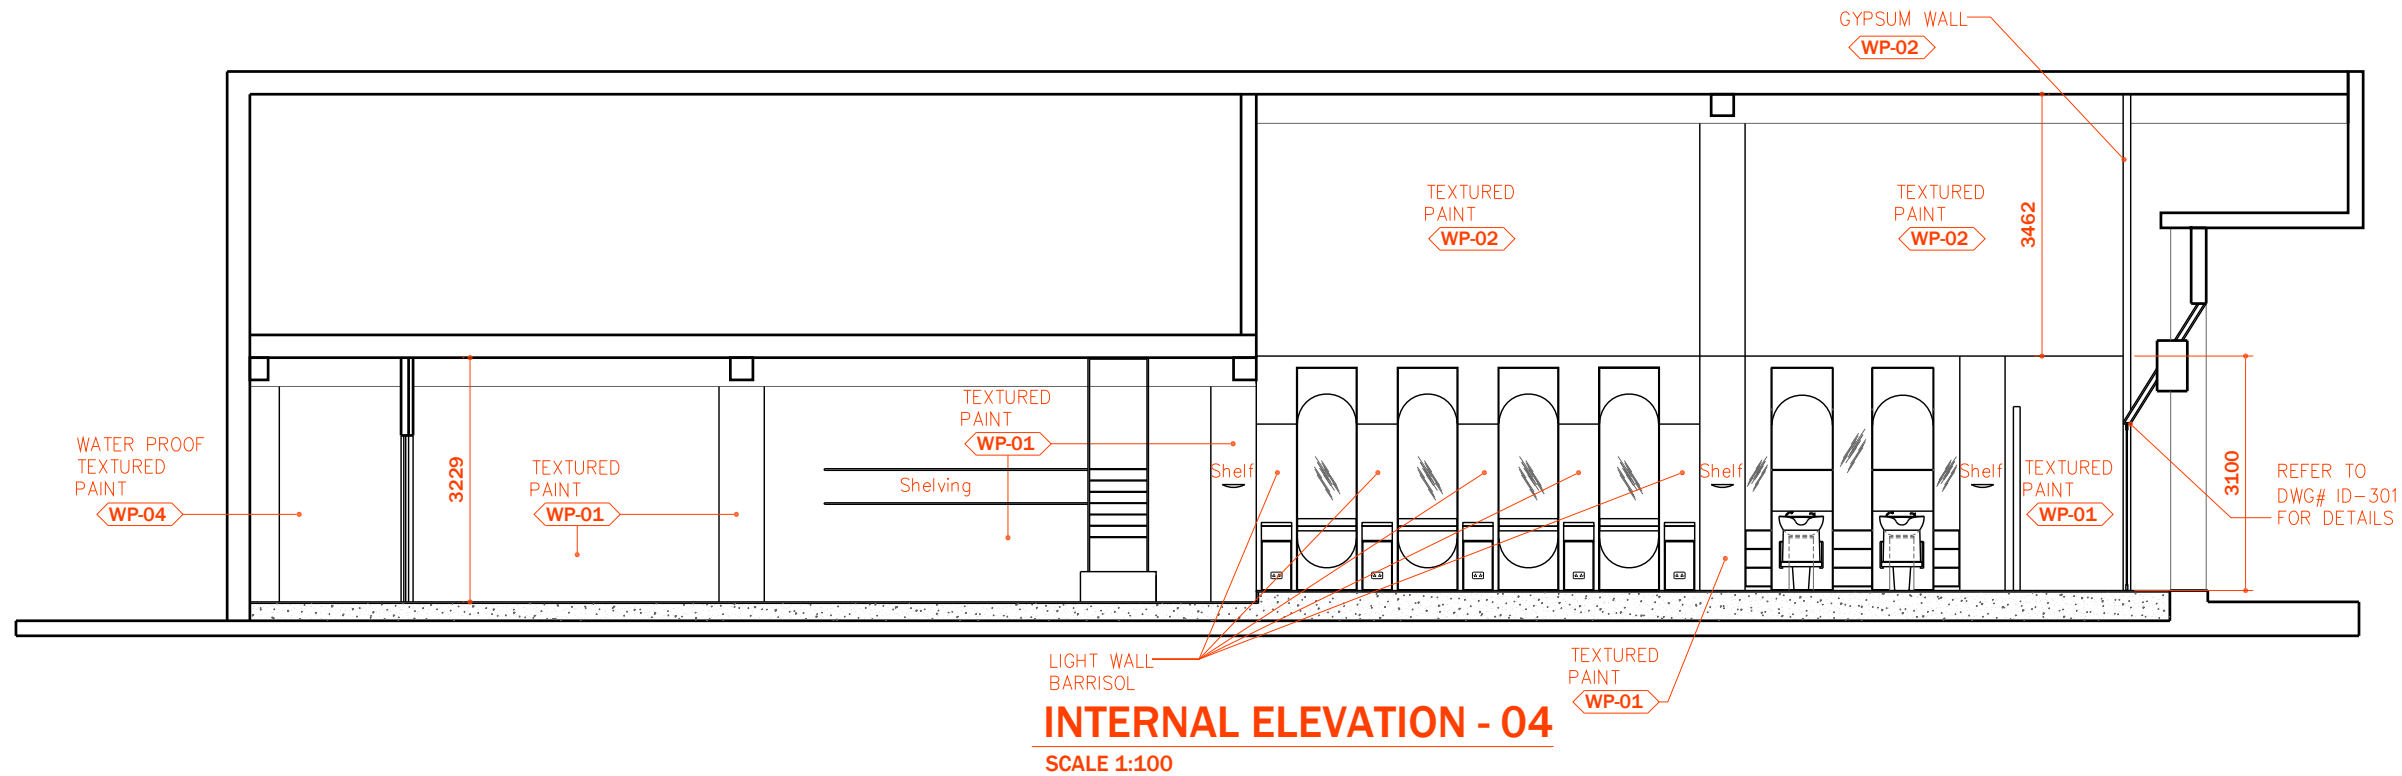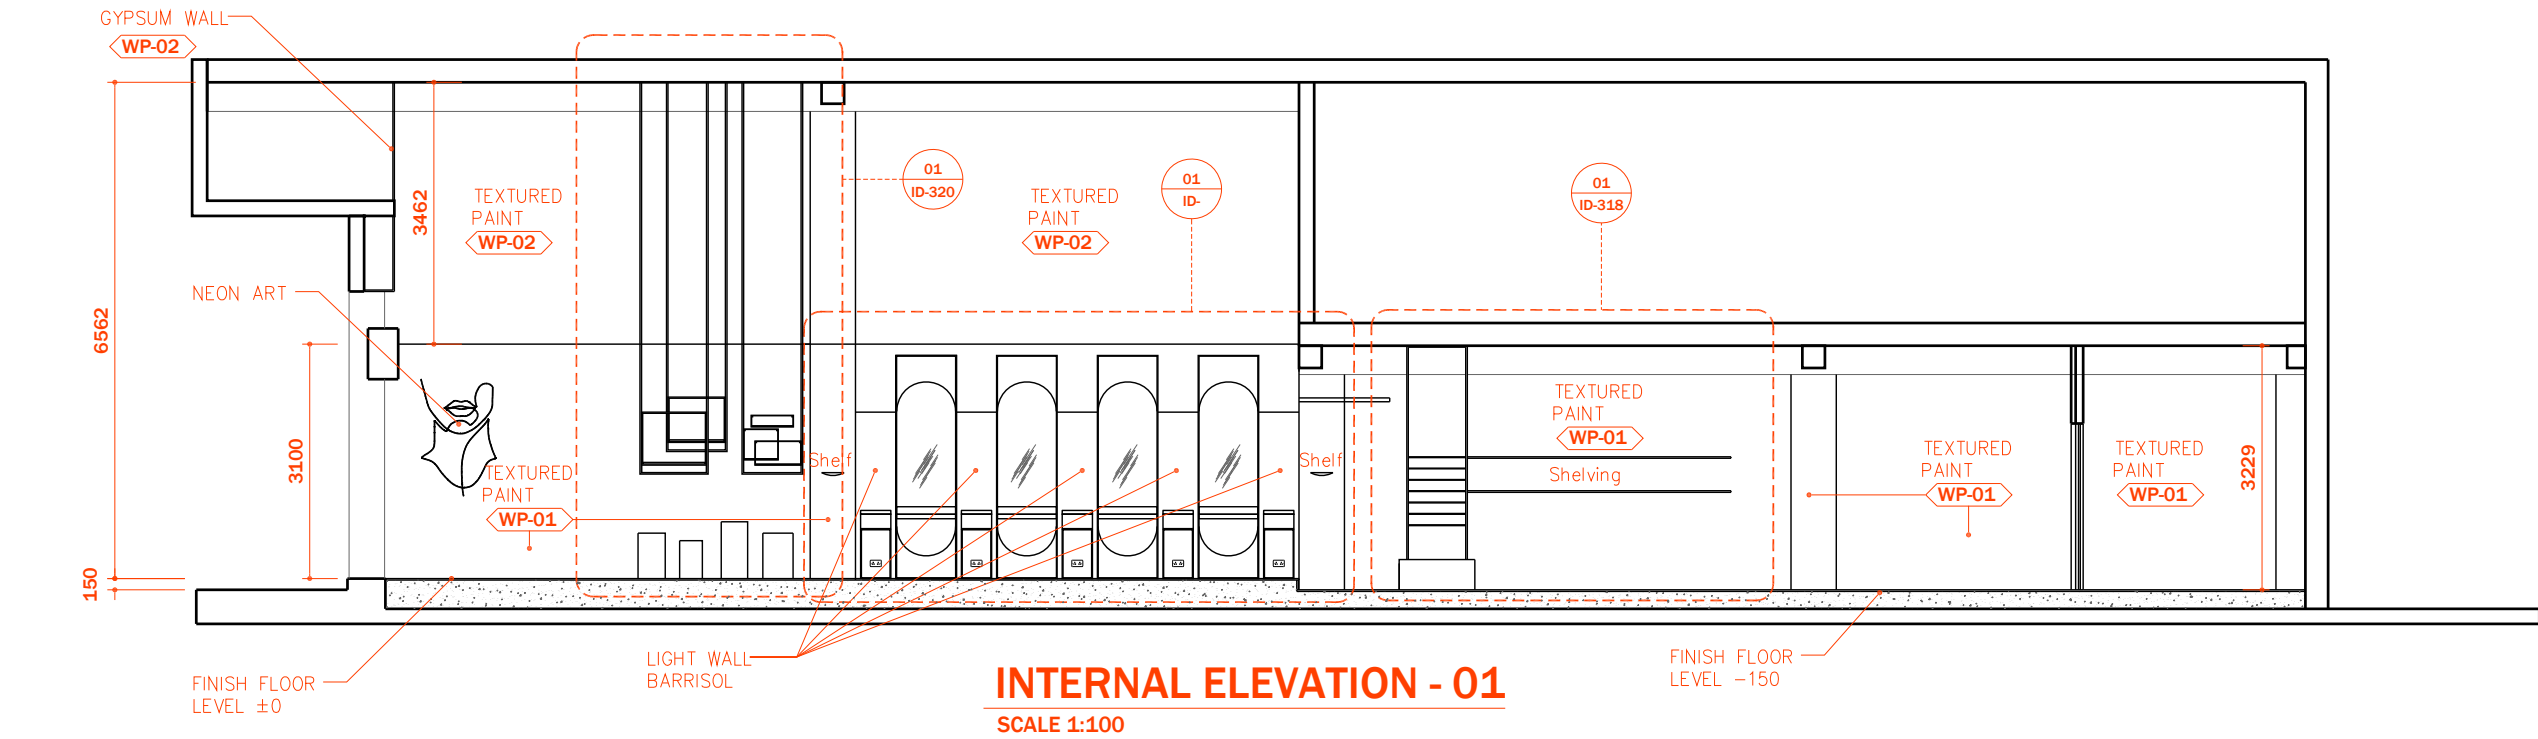

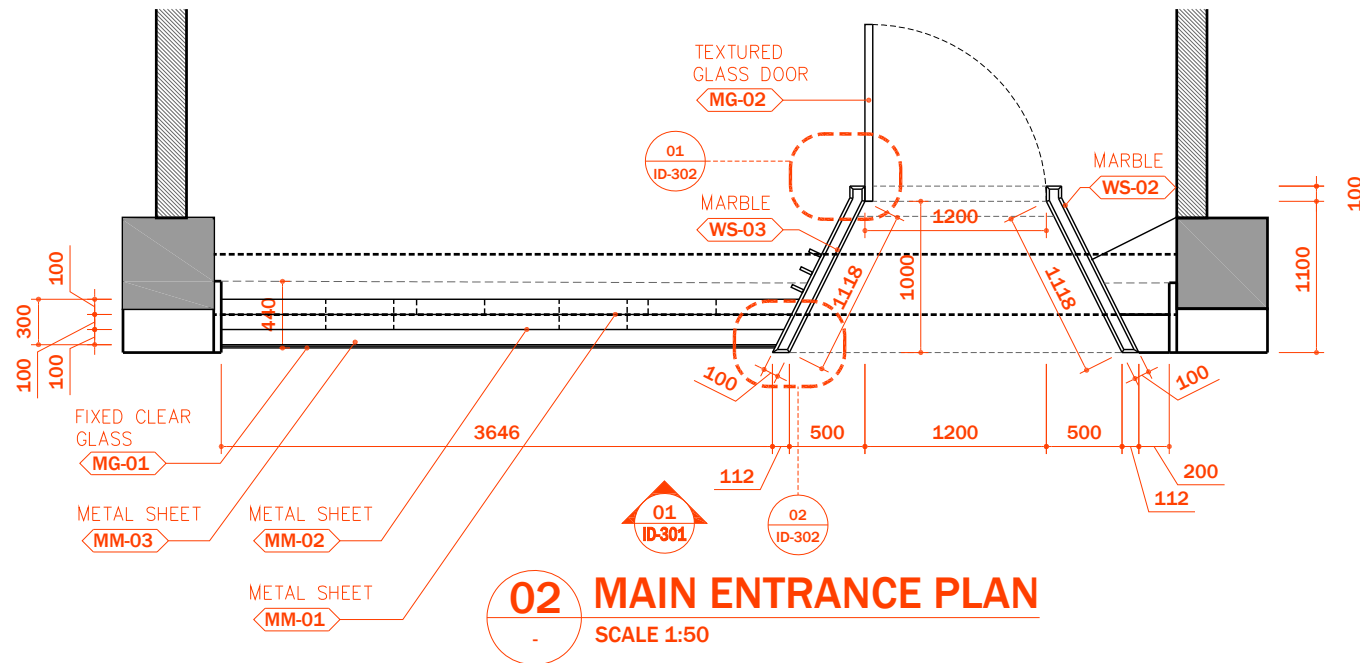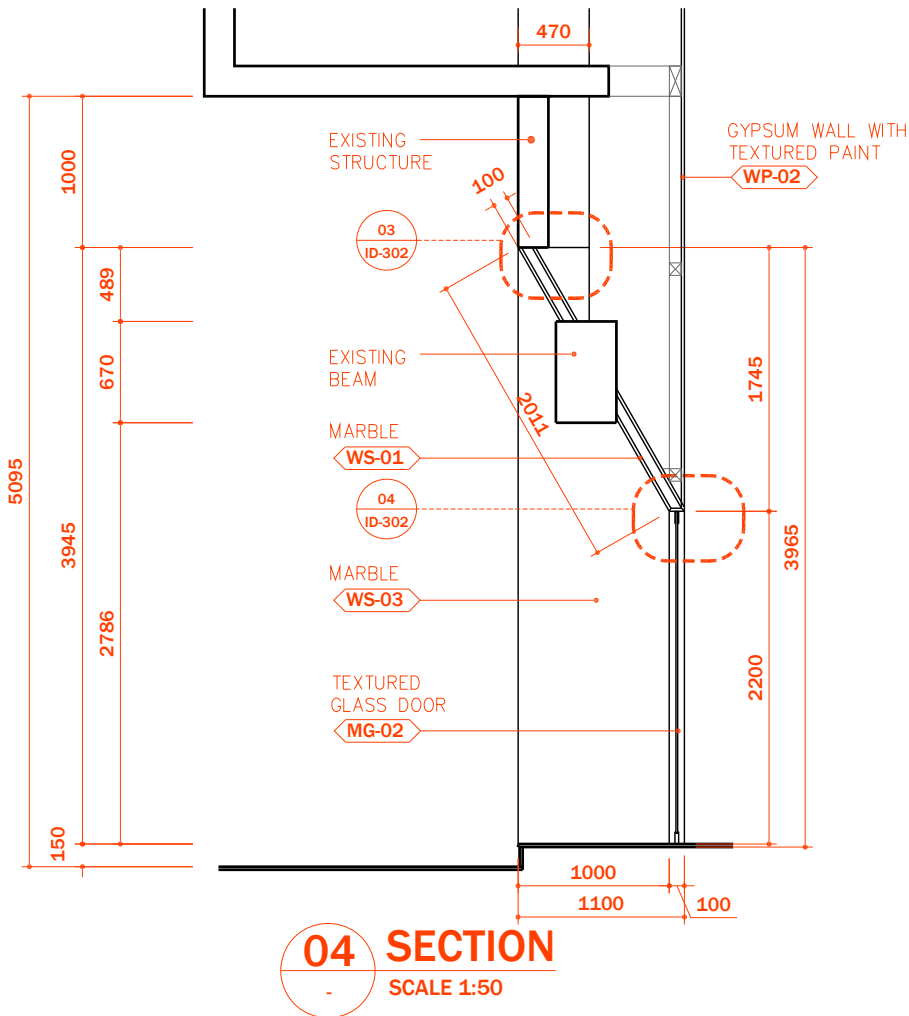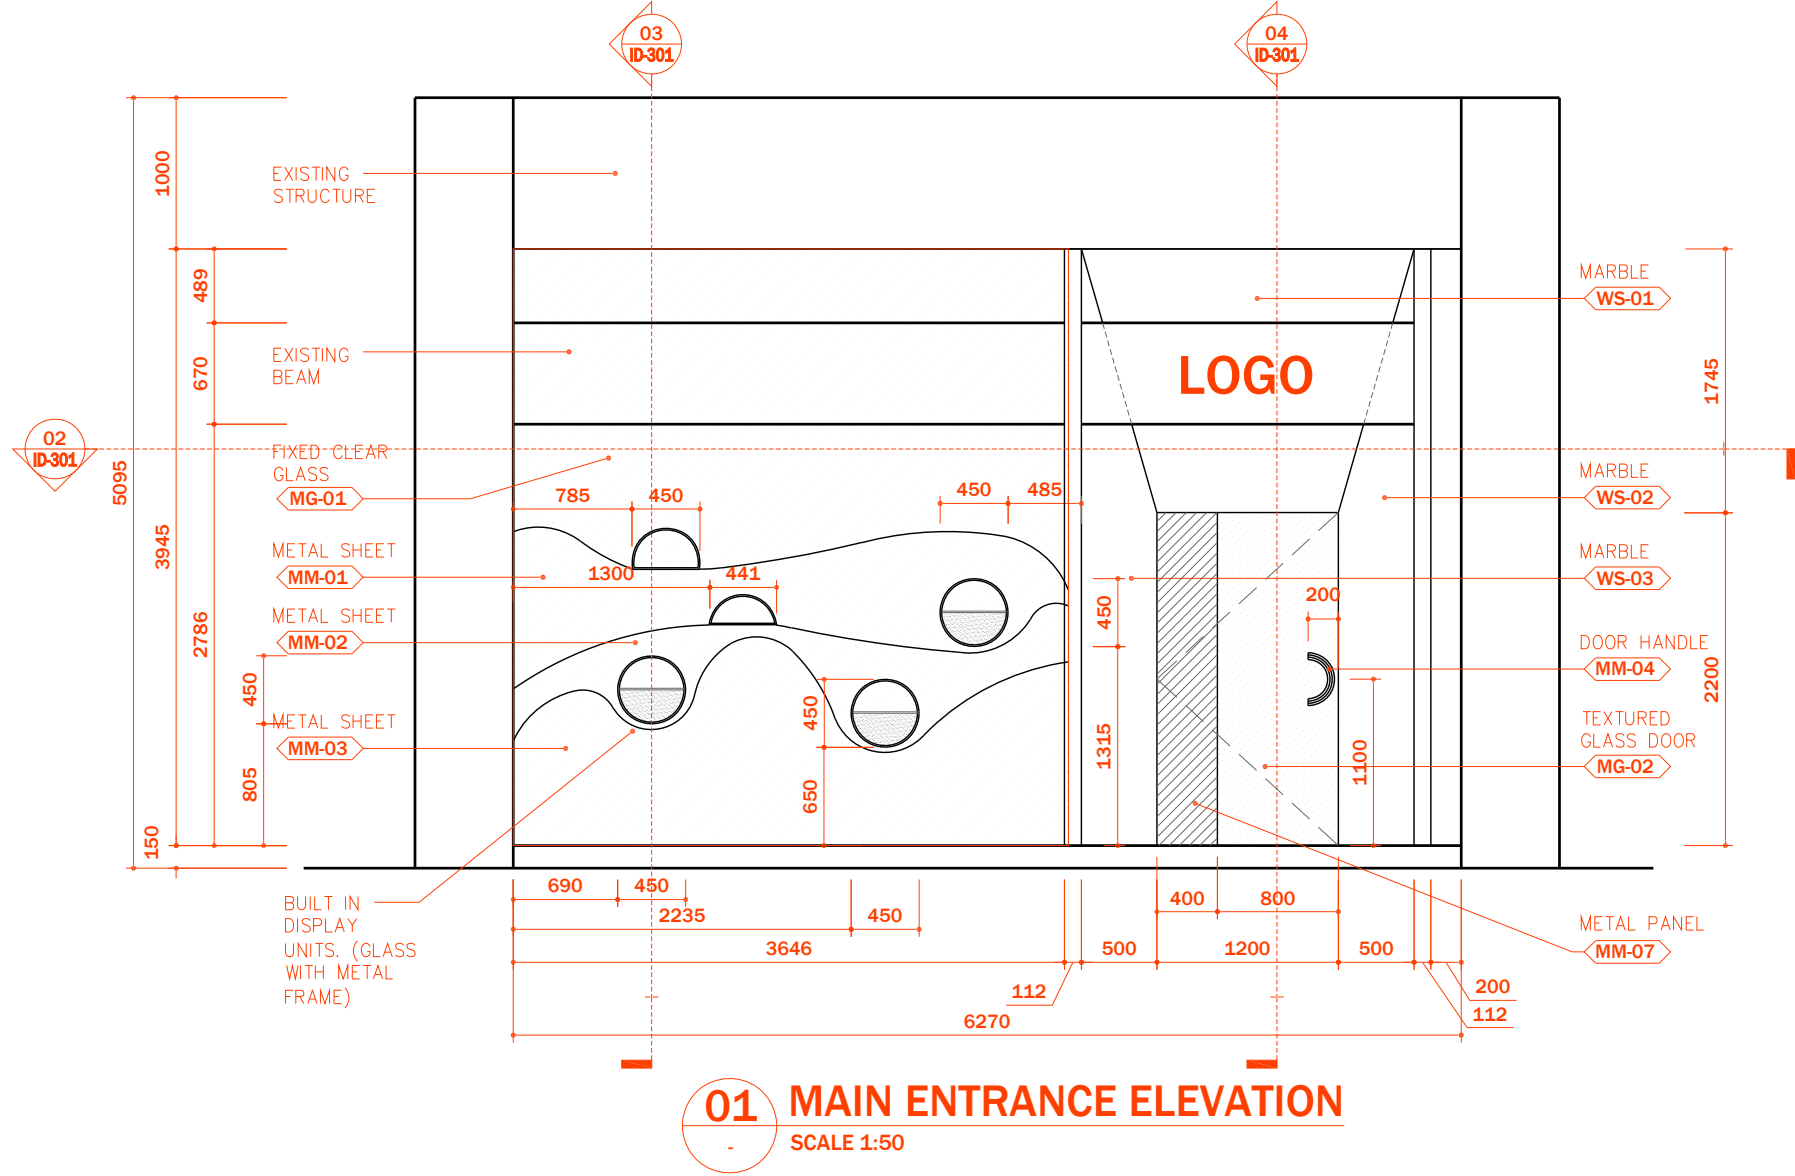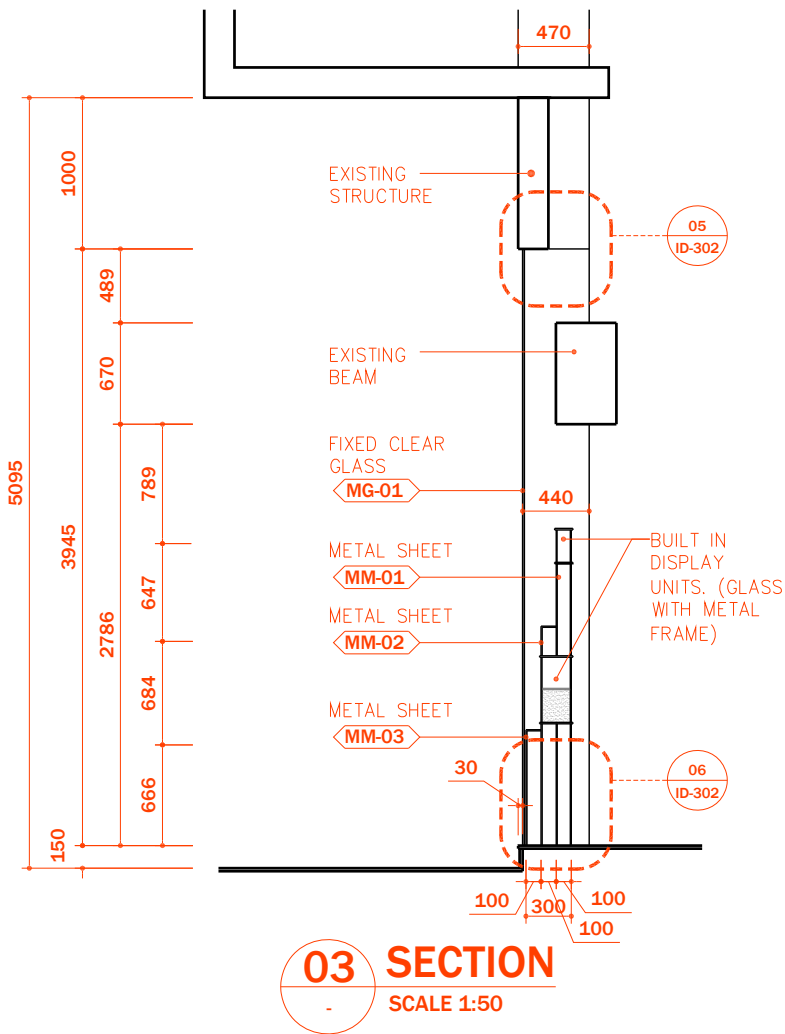



the

01. 2021

28.09.2025

Issue Date

REV DATE

- 1.
- 2.
- 3.

Figure 1



PROJECT PHASE


INTERIOR DRAWING

1:75


GROUND FLOOR

ID-302


© 2021

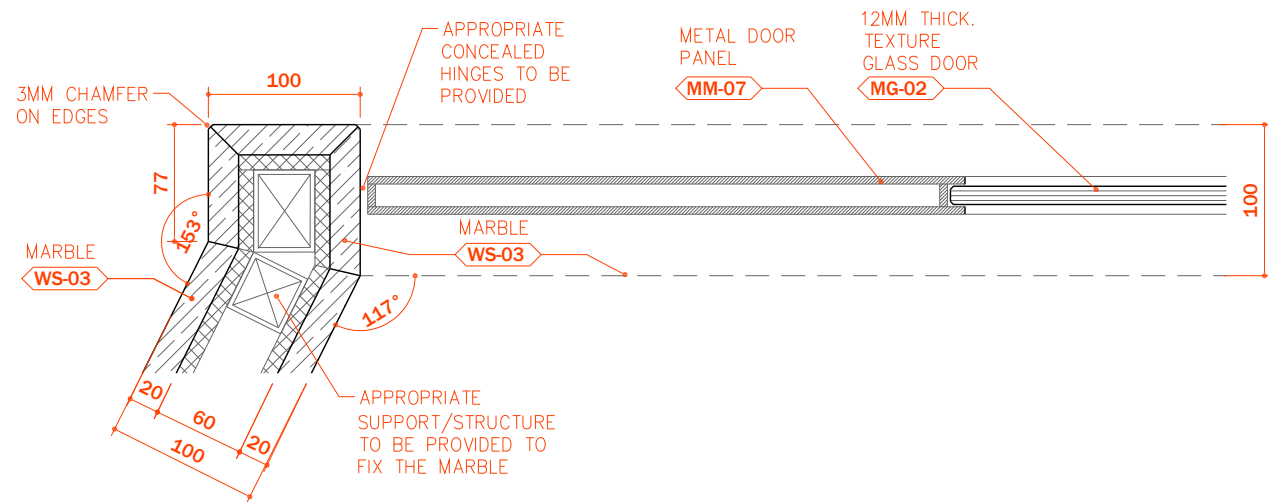


SCALE 1:5

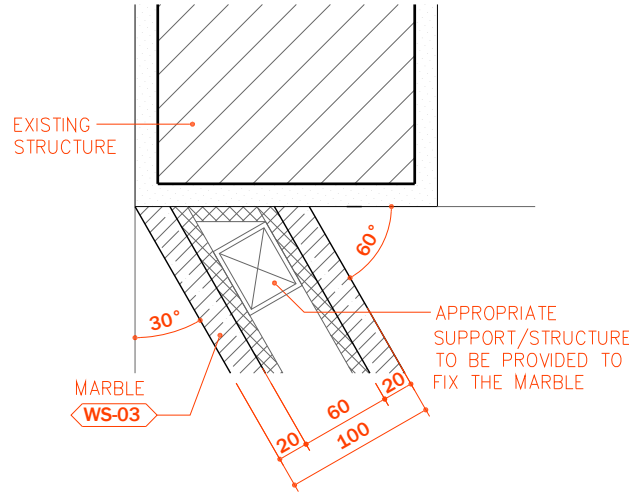


SCALE 1:5

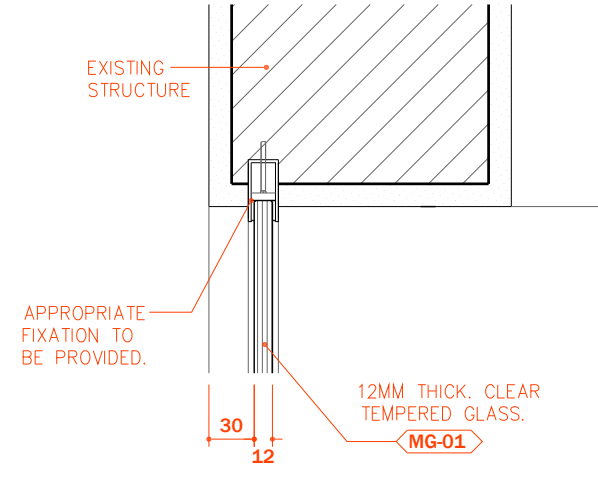


SCALE 1:5

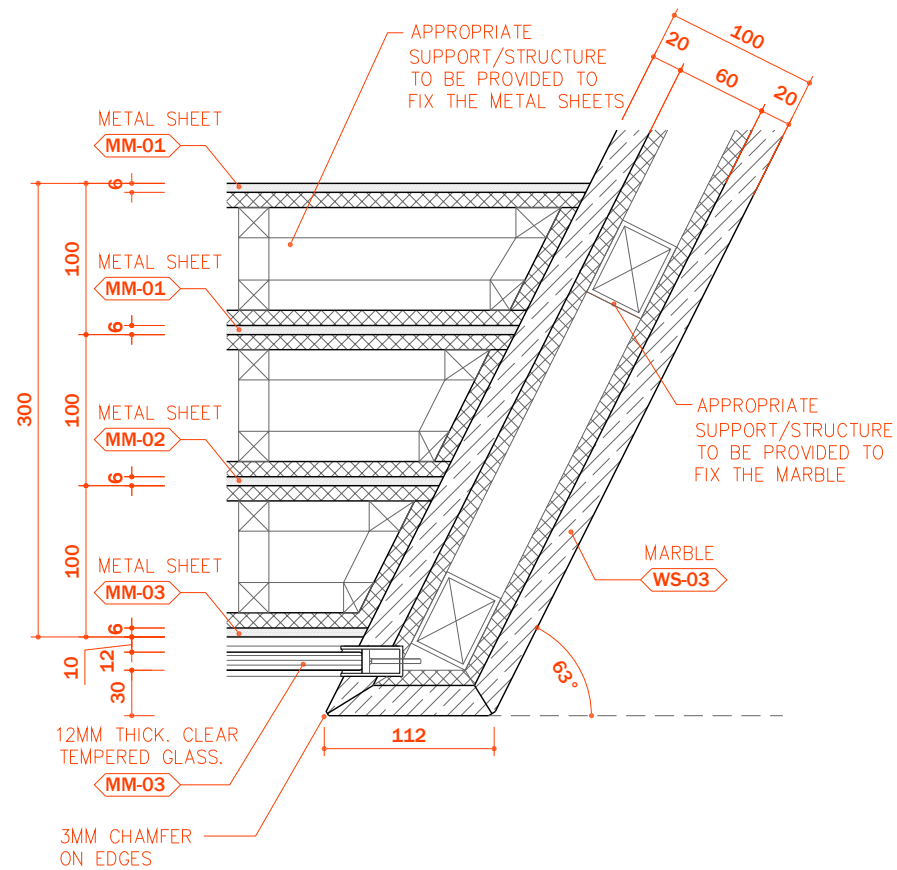



SCALE 1:5

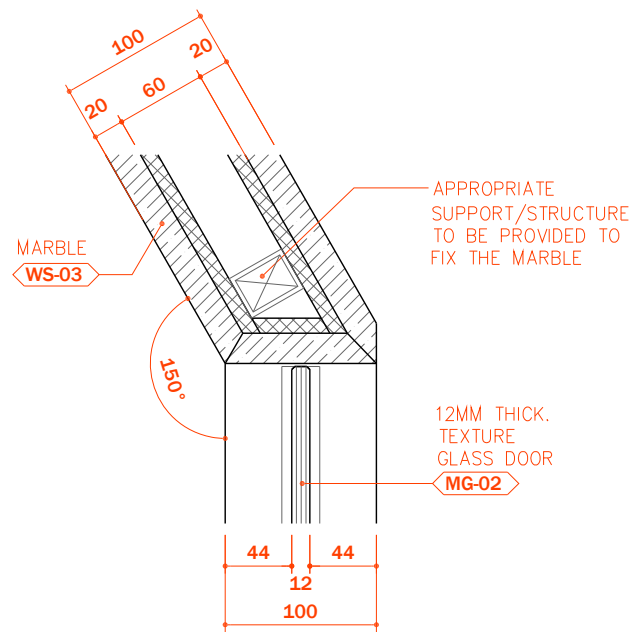


SCALE 1:5

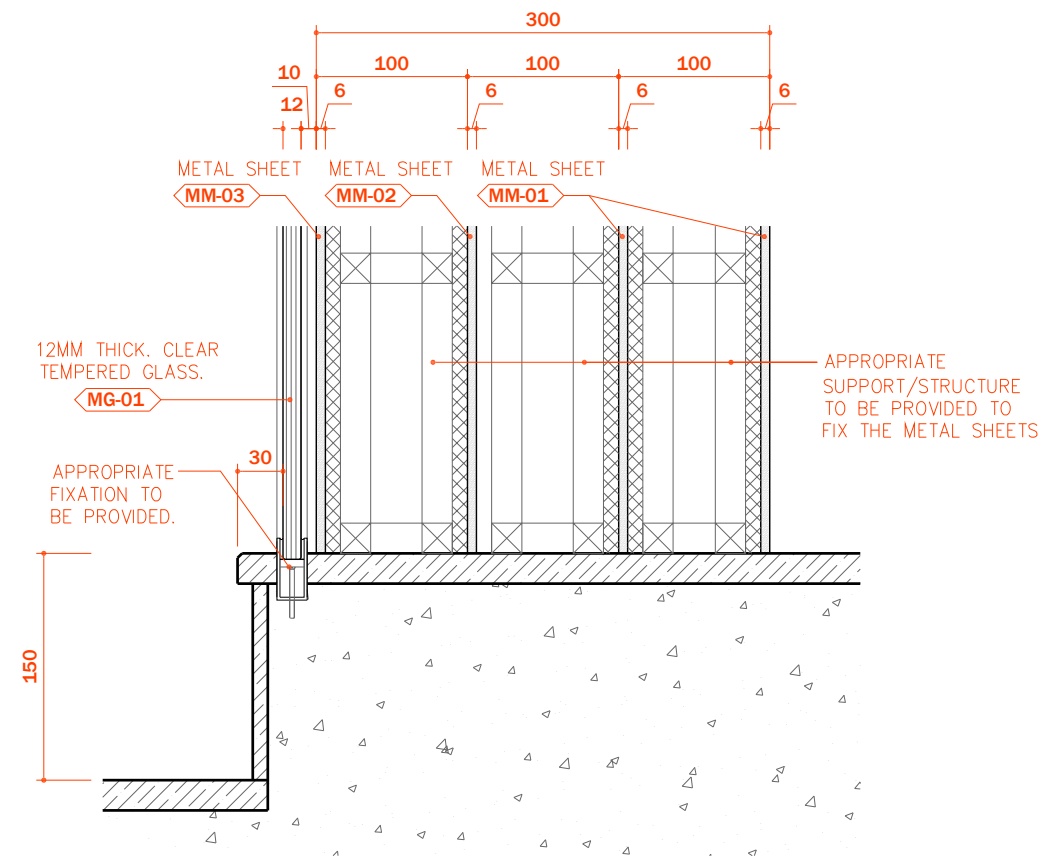


SCALE 1:5

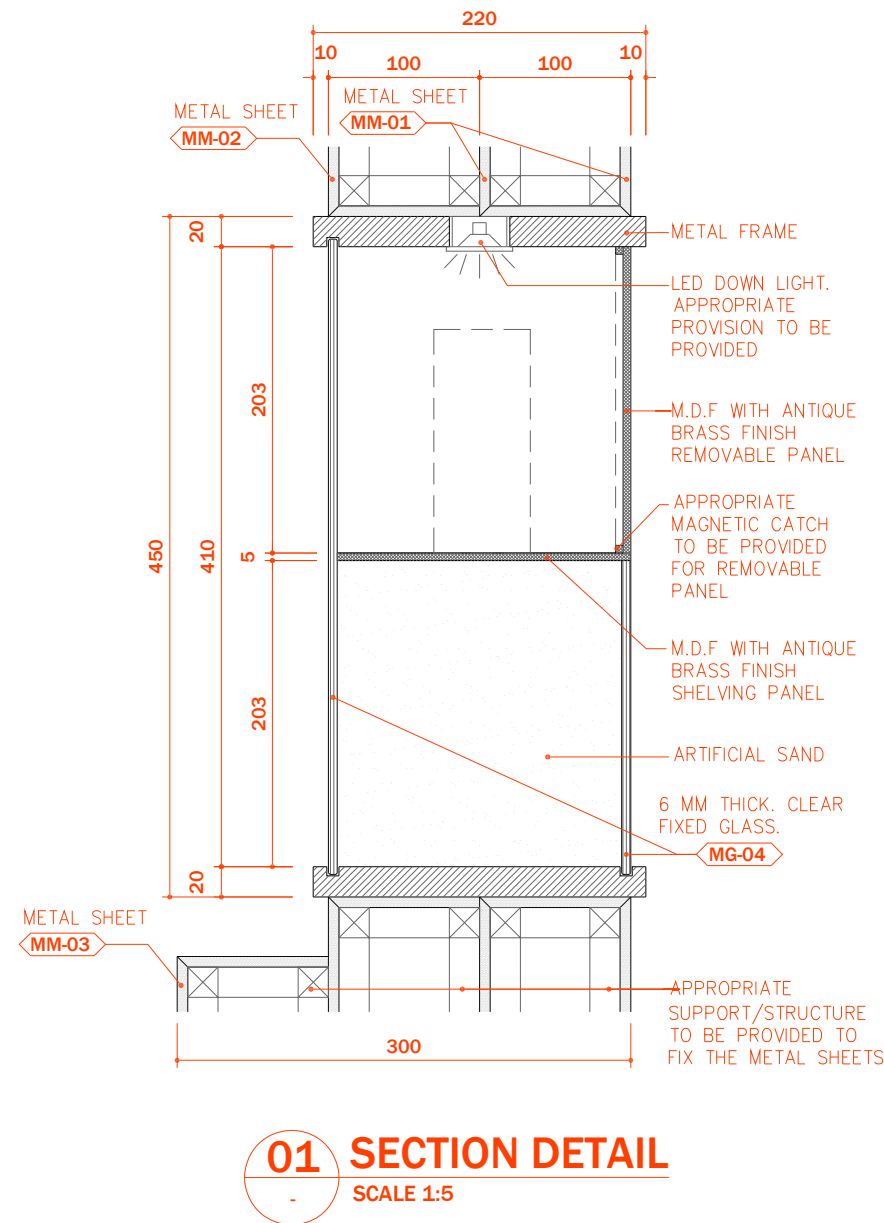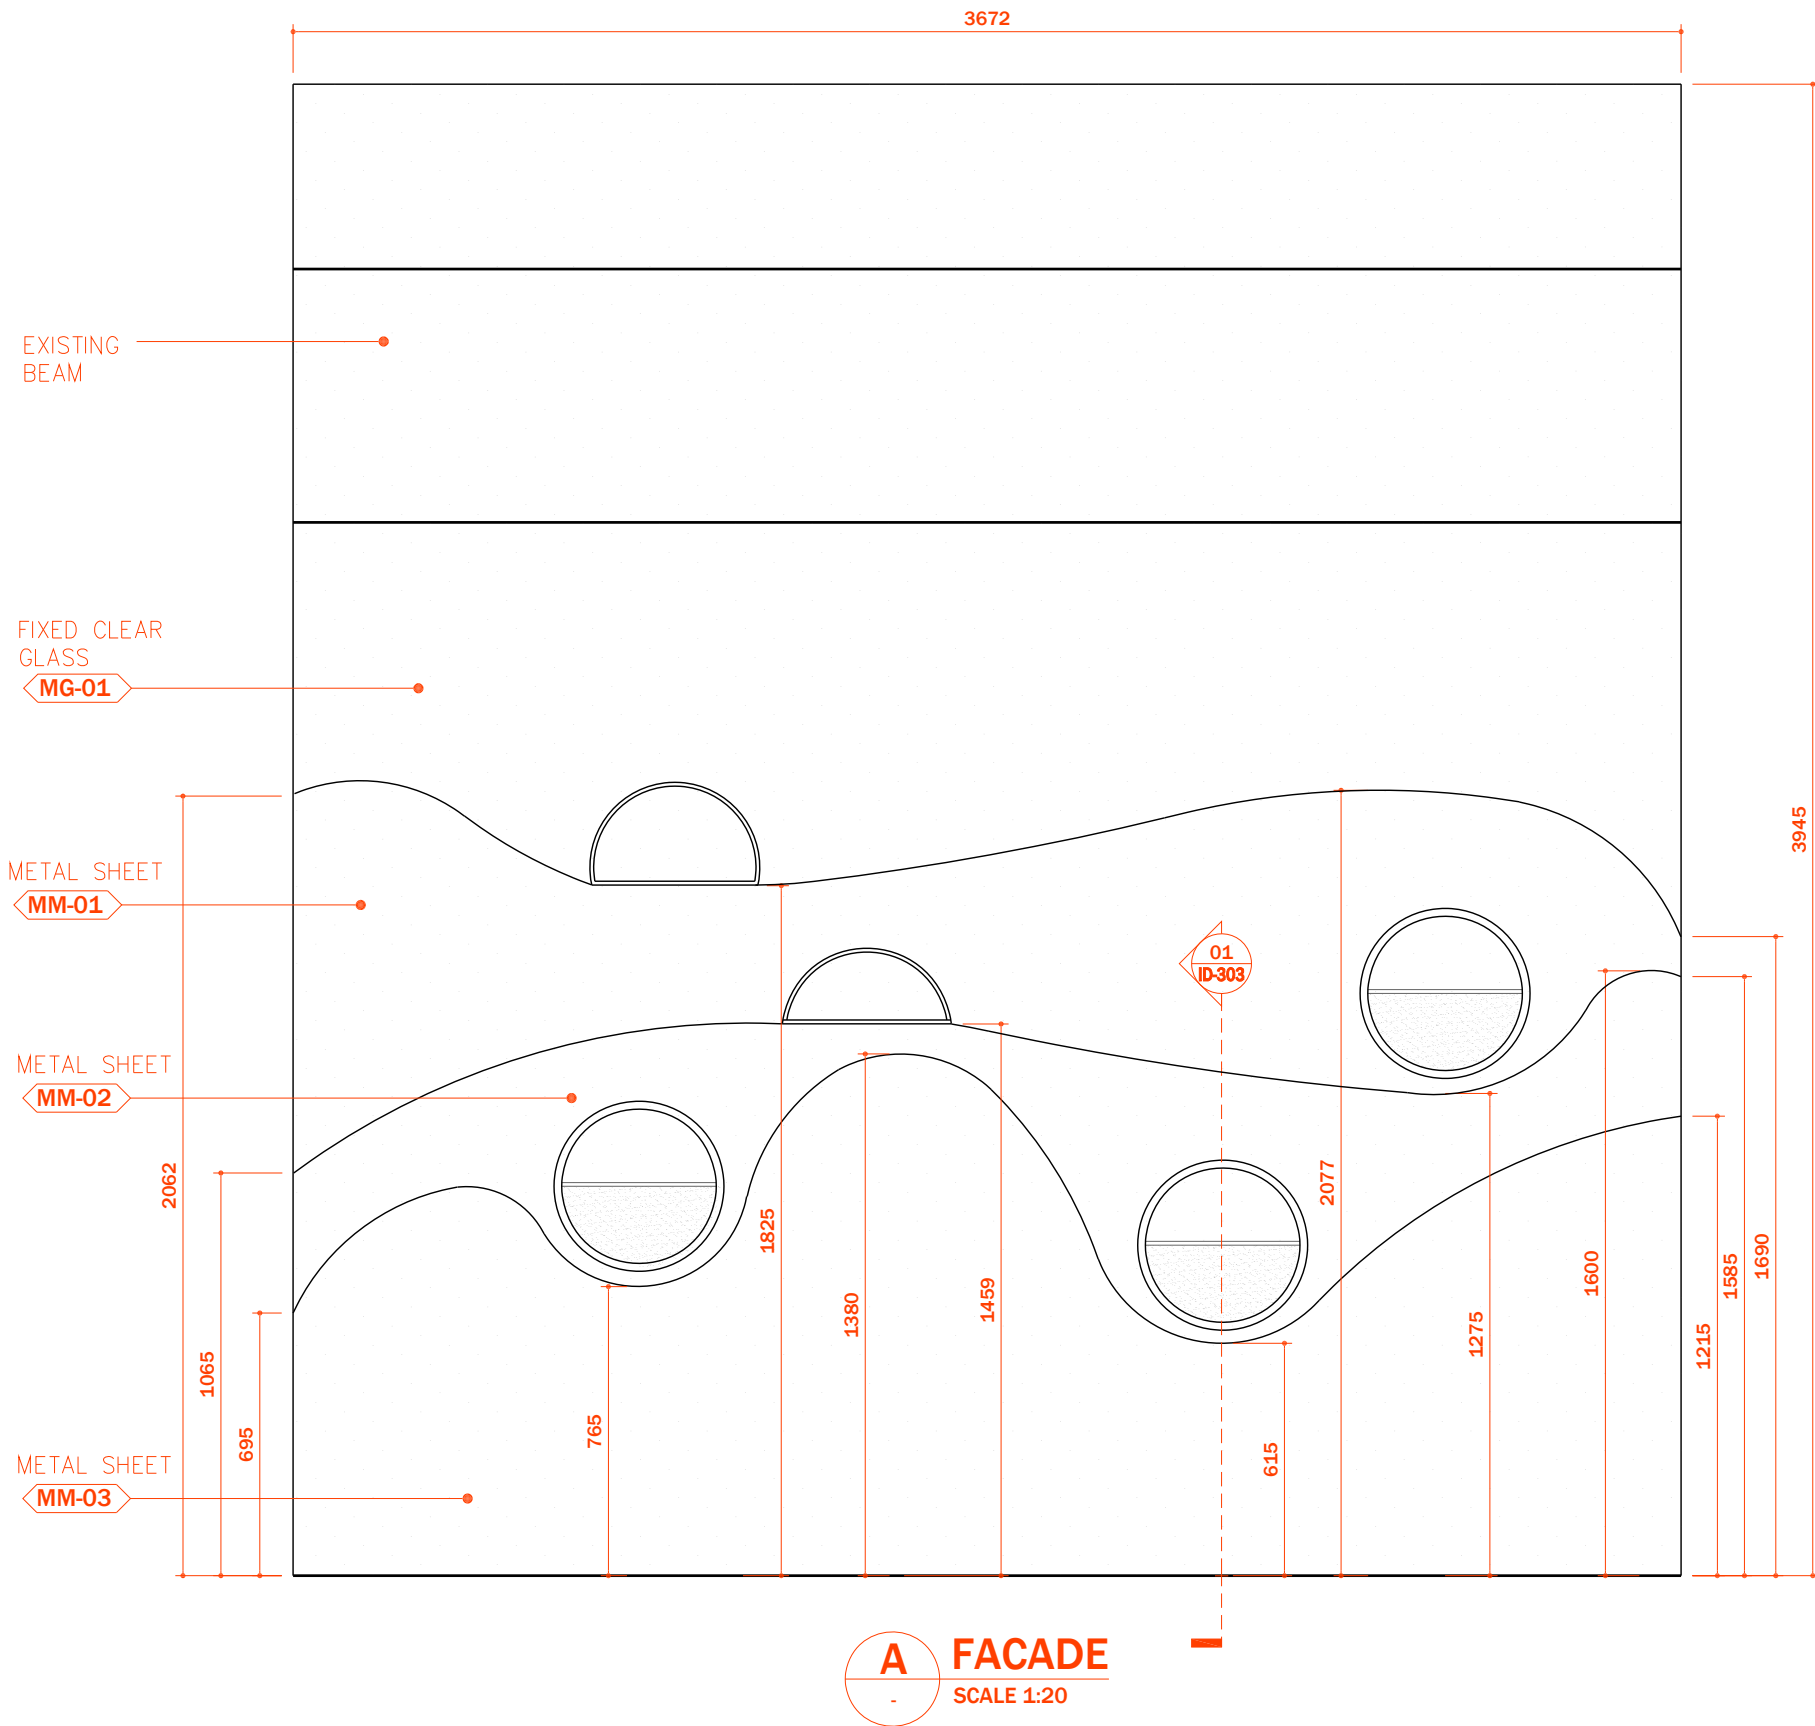


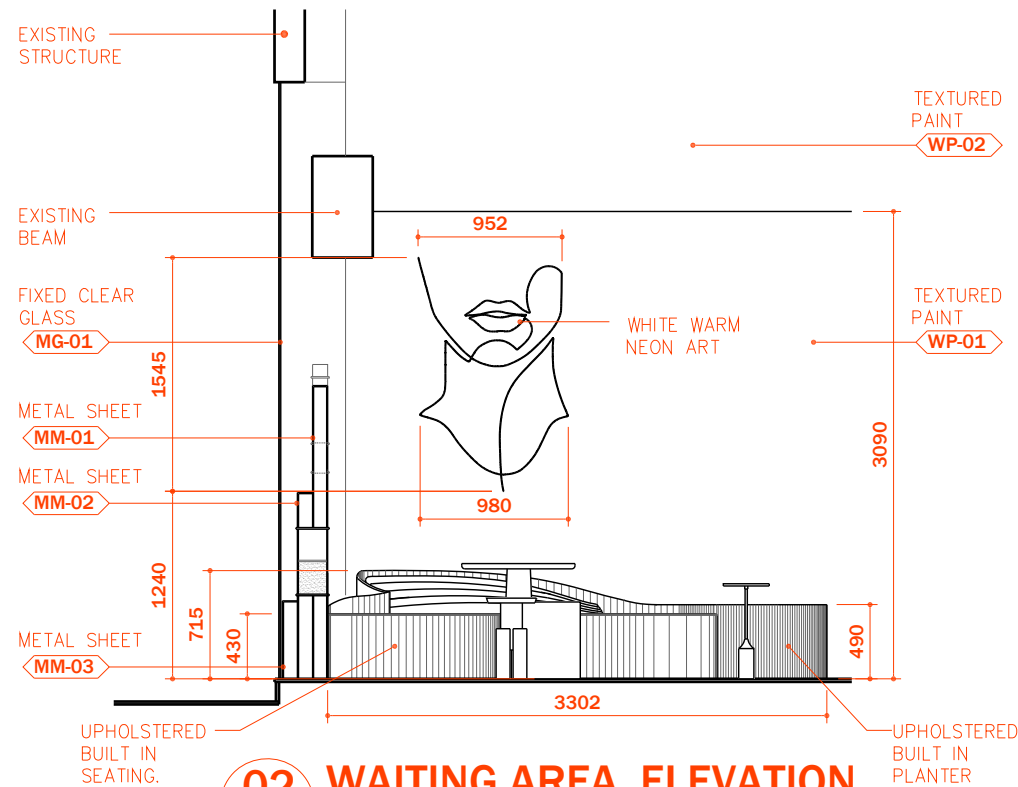


02 WAITING AREA ELEVATION
SCALE 1:50

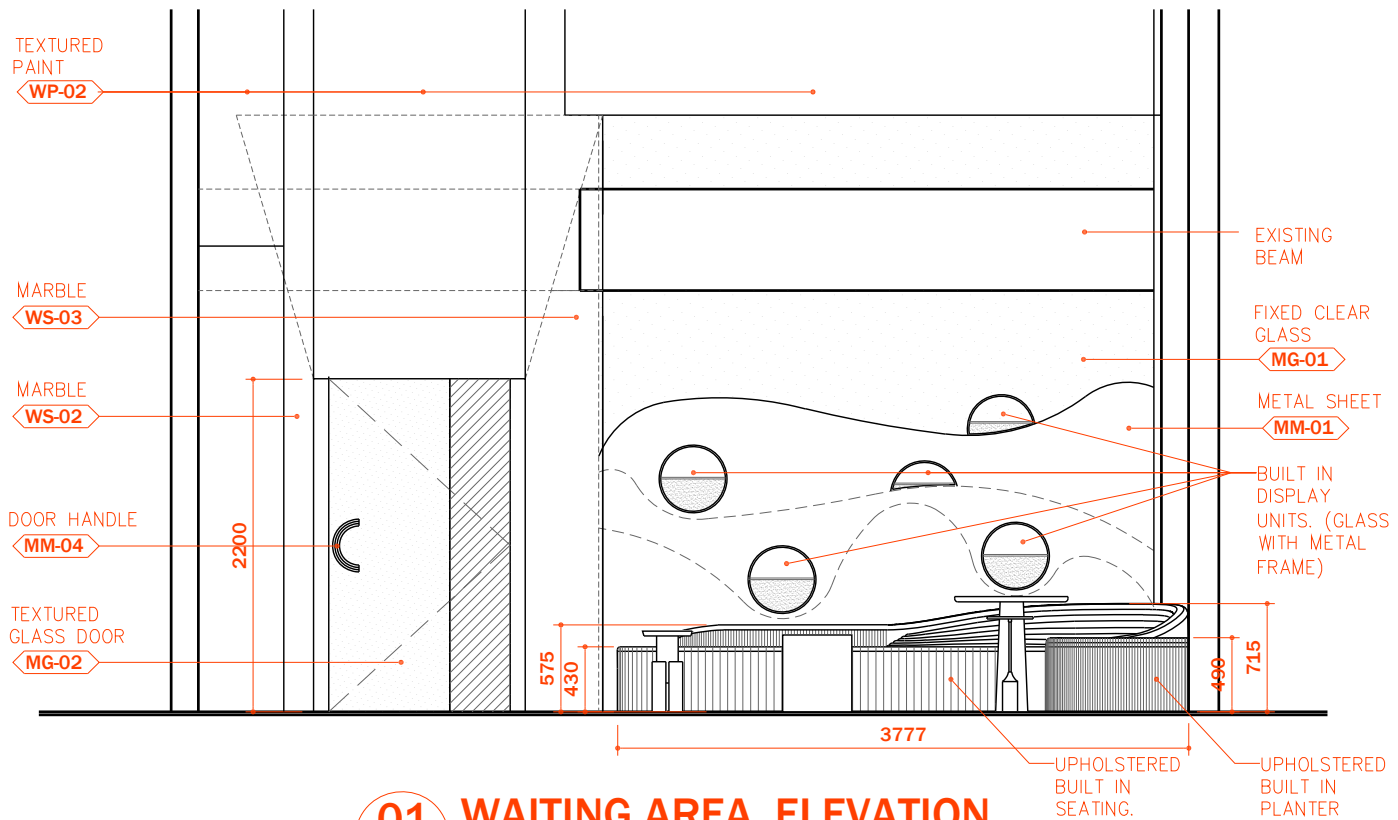





01 WAITING AREA ELEVATION
SCALE 1:50

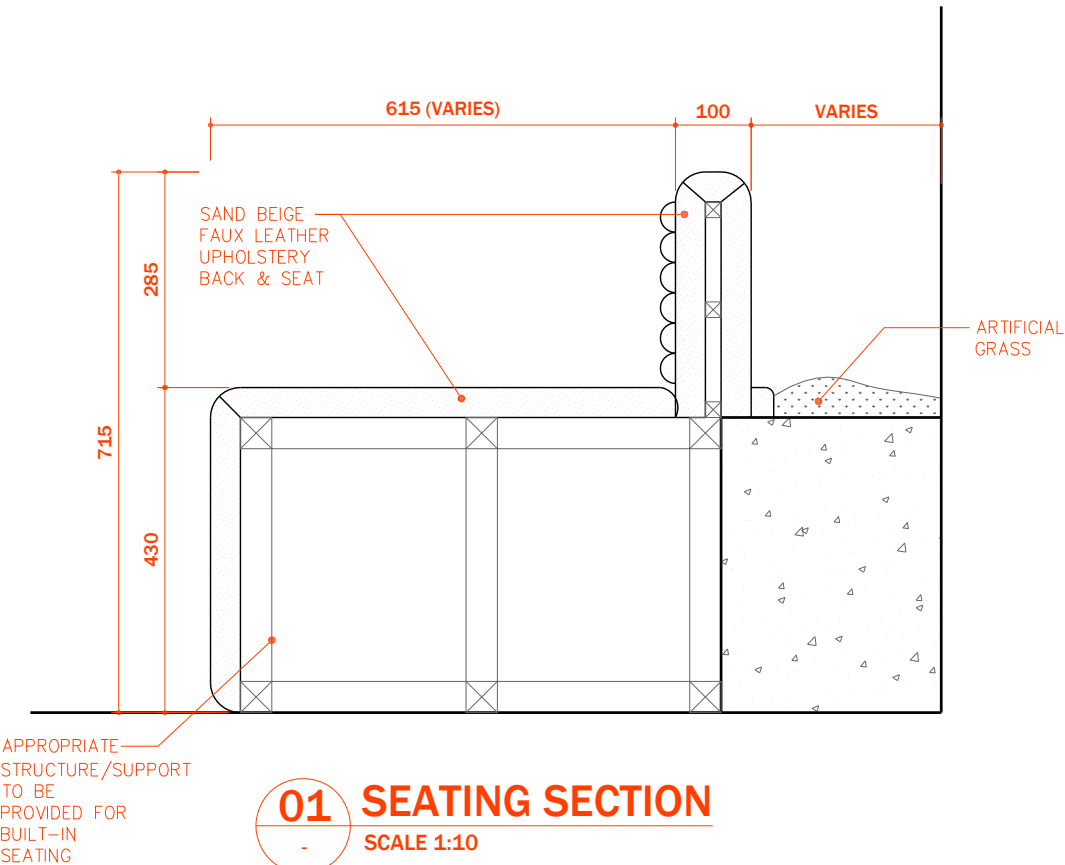


01 SEATING SECTION
SCALE 1:10

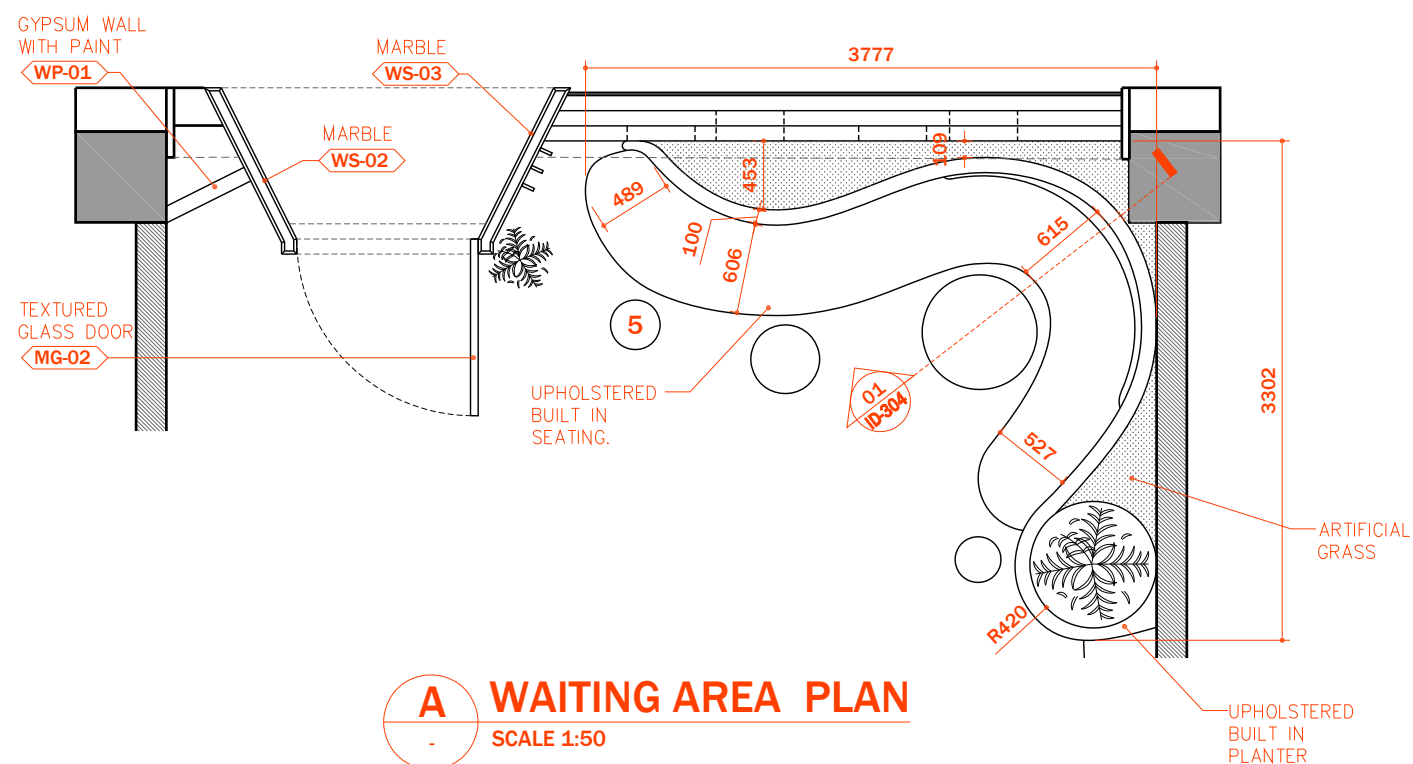


A WAITING AREA PLAN
SCALE 1:50

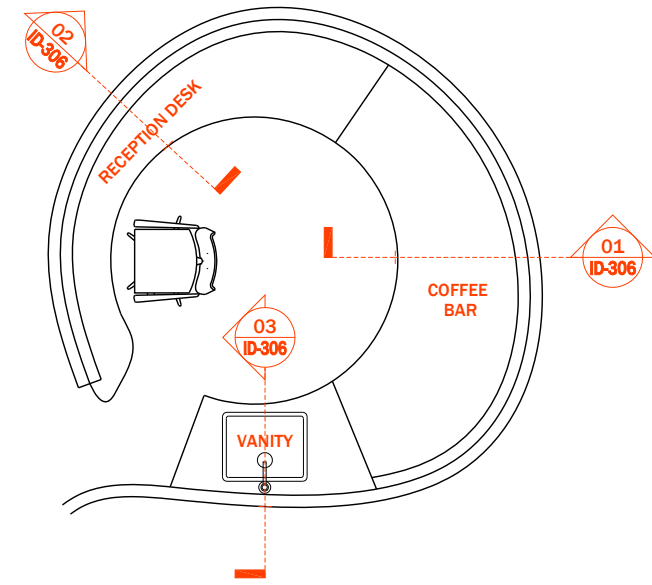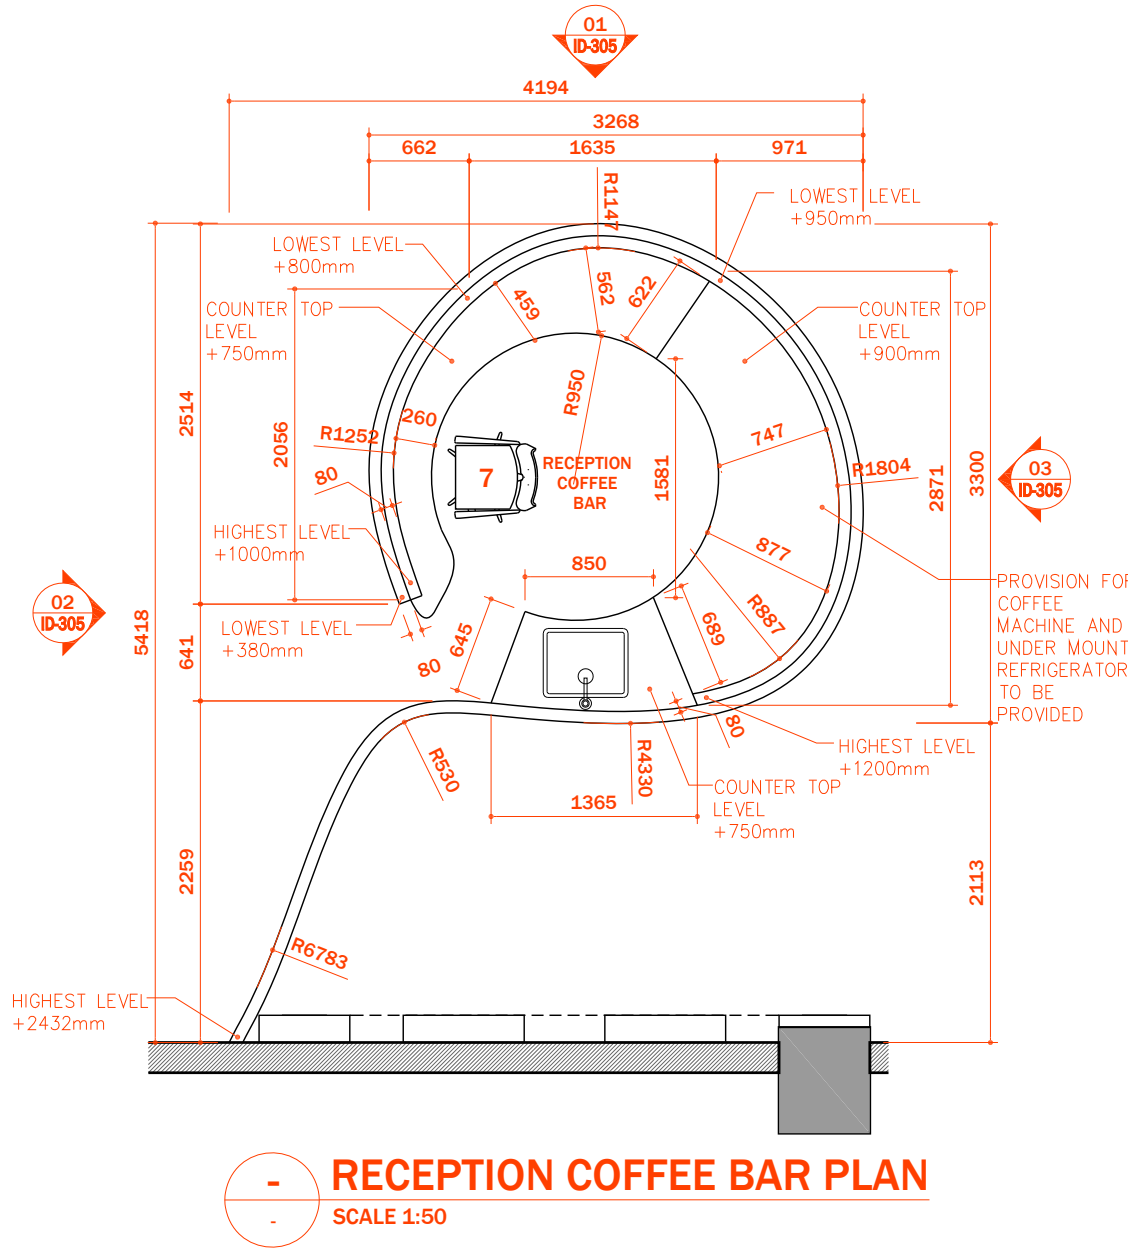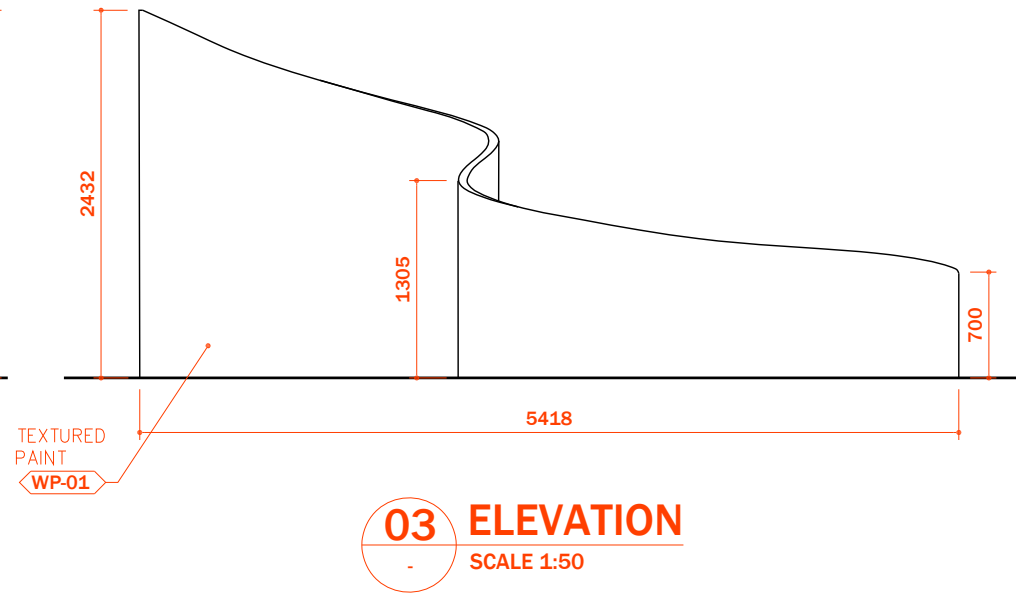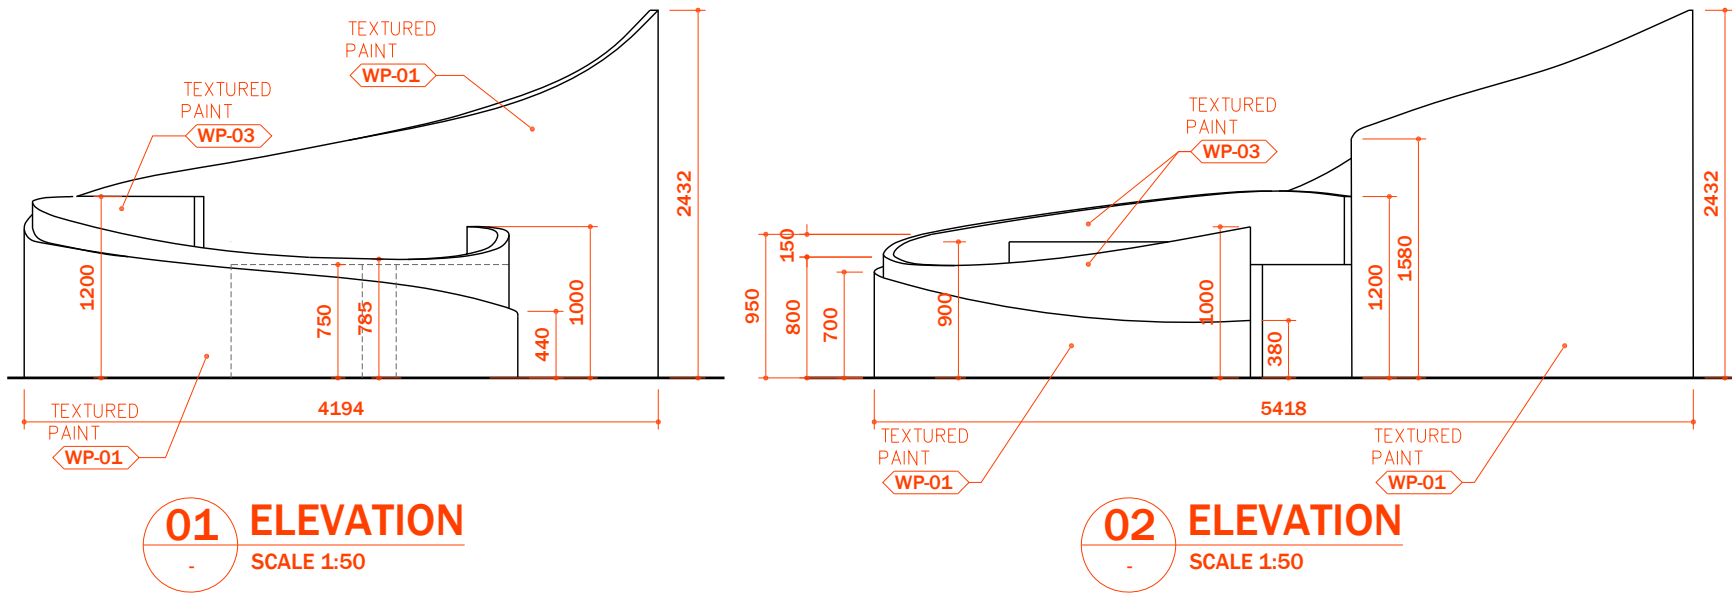

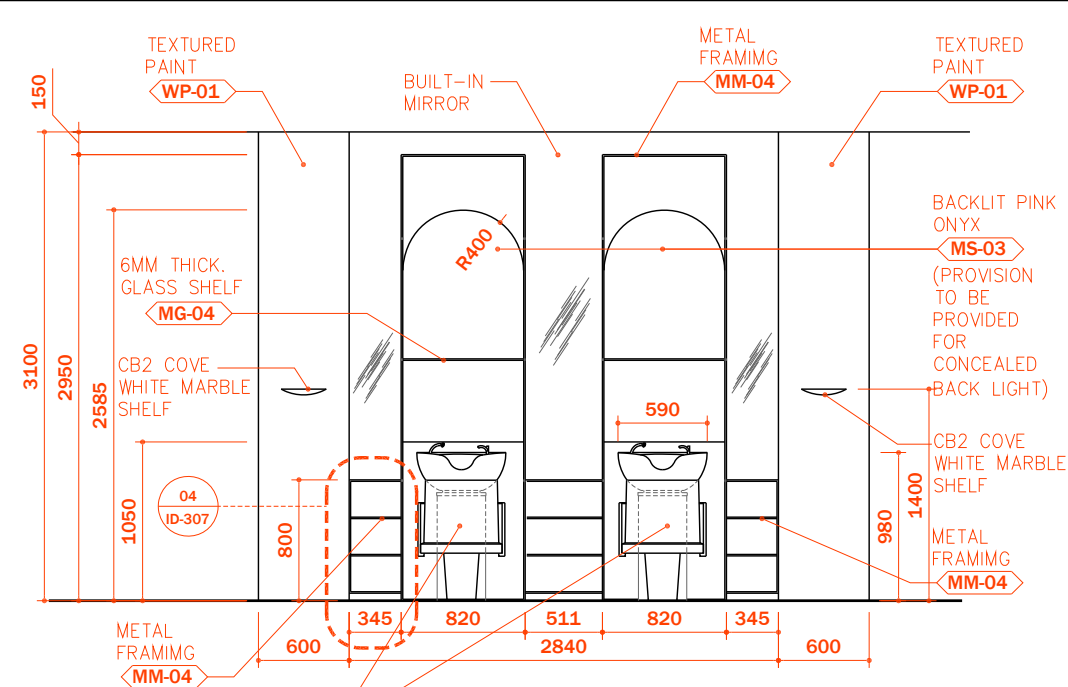


SHAMPOO BOWLS WASH INN ALUOTIS MEDIUM GCW003BZ GAMMA & BROSS CHAIR UPHOLSTERY IN SAND BEIGE FAUX LEATHER.

(PROVISION FOR WATER SUPPLY AND DRAINAGE TO BE PROVIDED AS PER MANUFACTURER'S REQUIREMENTS)

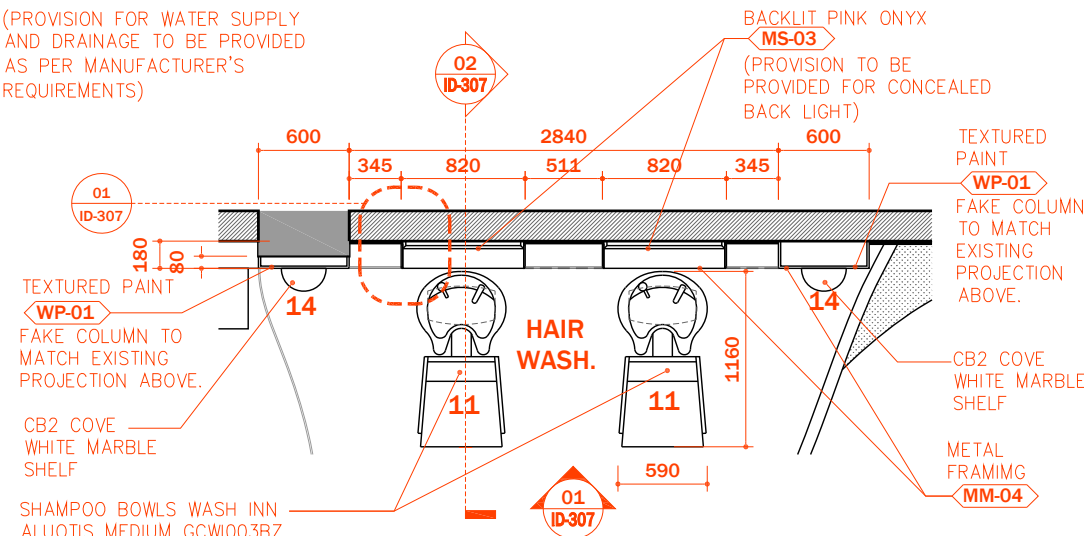


HAIR WASH AREA PLAN
SCALE 1:50


(PROVISION FOR WATER SUPPLY AND DRAINAGE TO BE PROVIDED AS PER MANUFACTURER'S REQUIREMENTS)

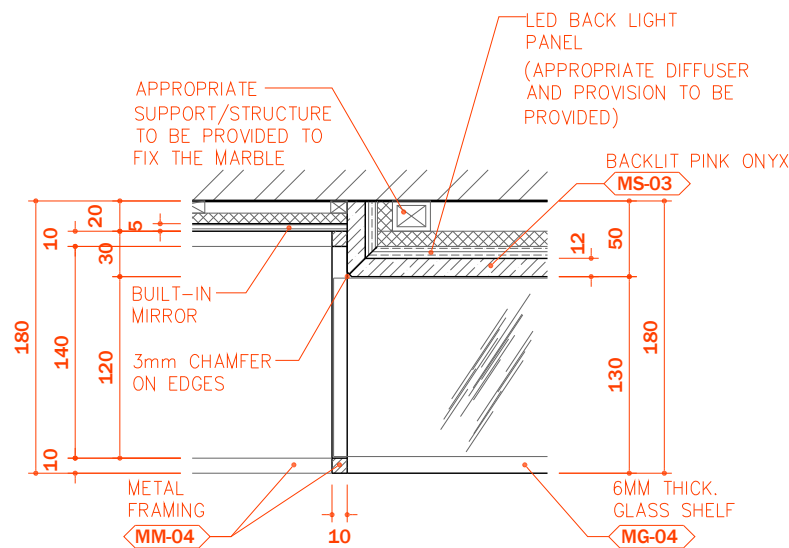


01 SPOT DETAIL
SCALE 1:5

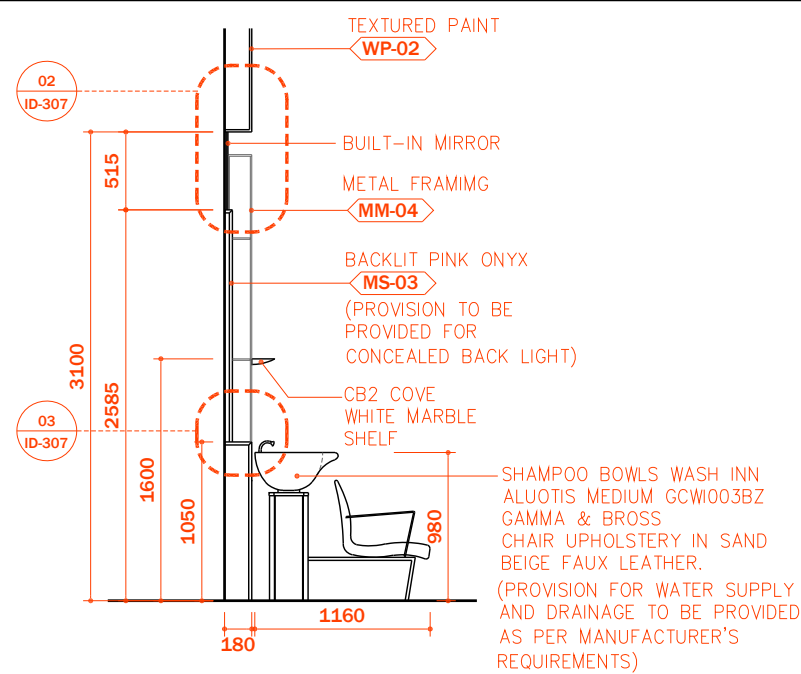


02 SECTION
SCALE 1:50

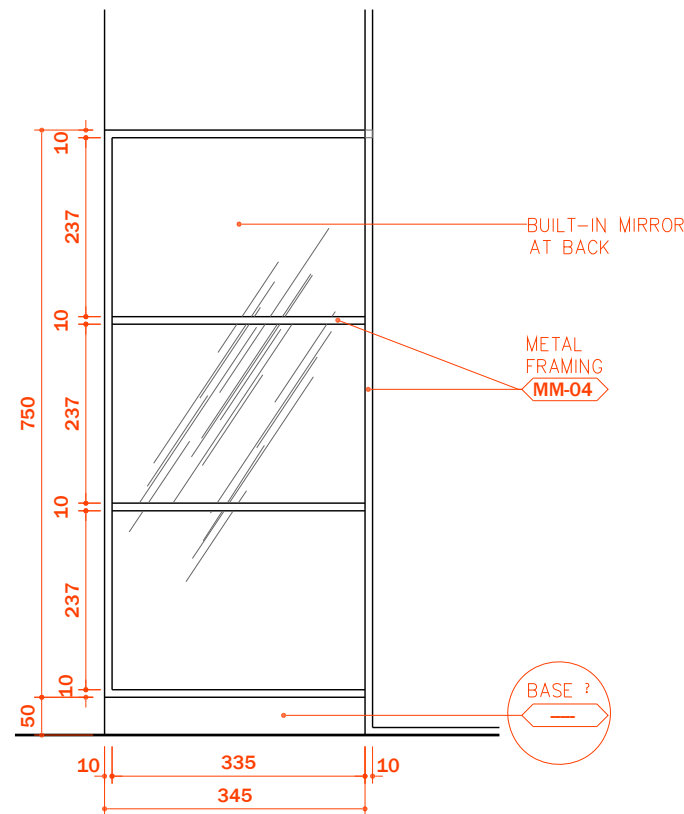







04 SPOT DETAIL
SCALE 1:10

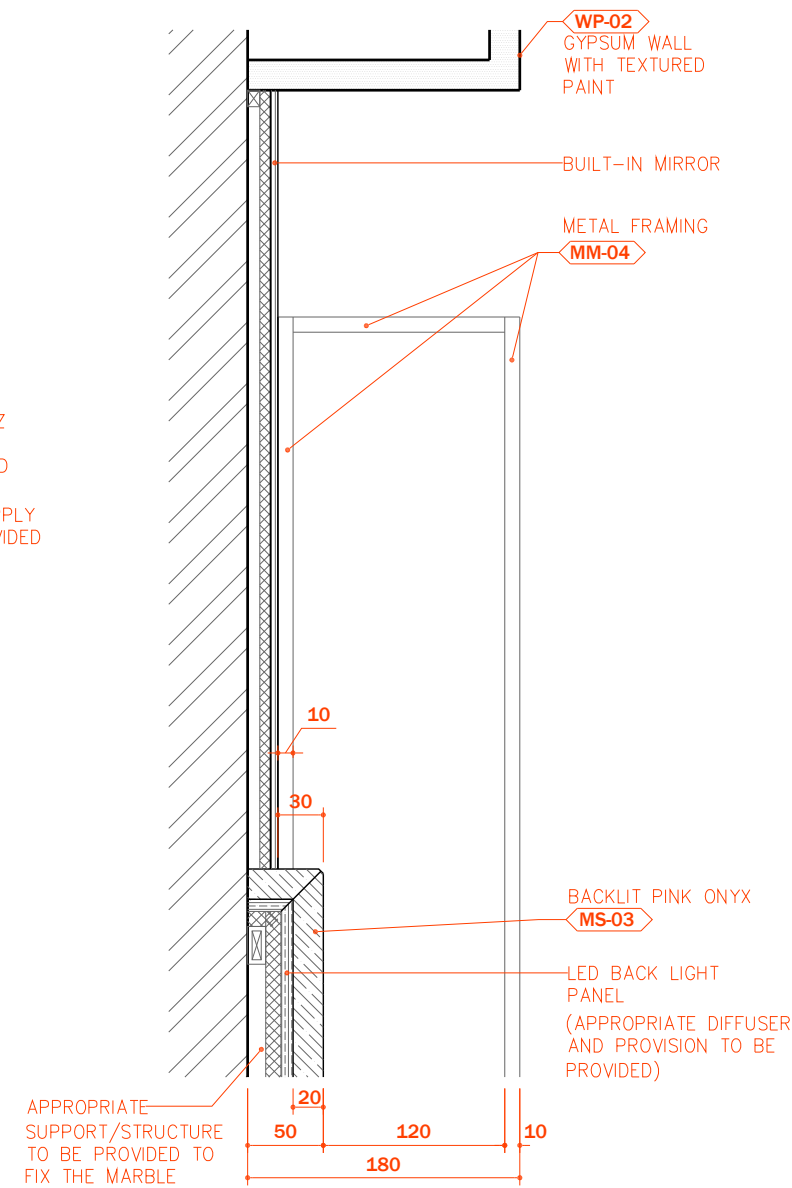


02 SPOT DETAIL
SCALE 1:5

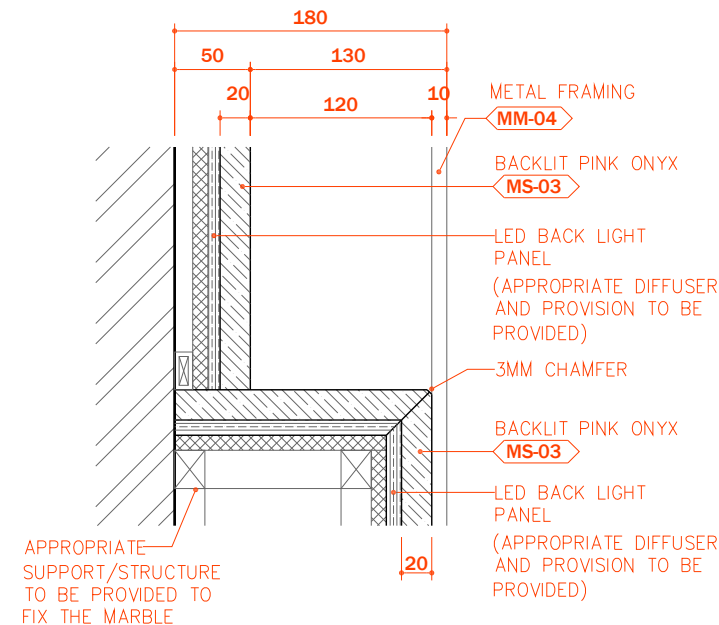


03 SPOT DETAIL
SCALE 1:5

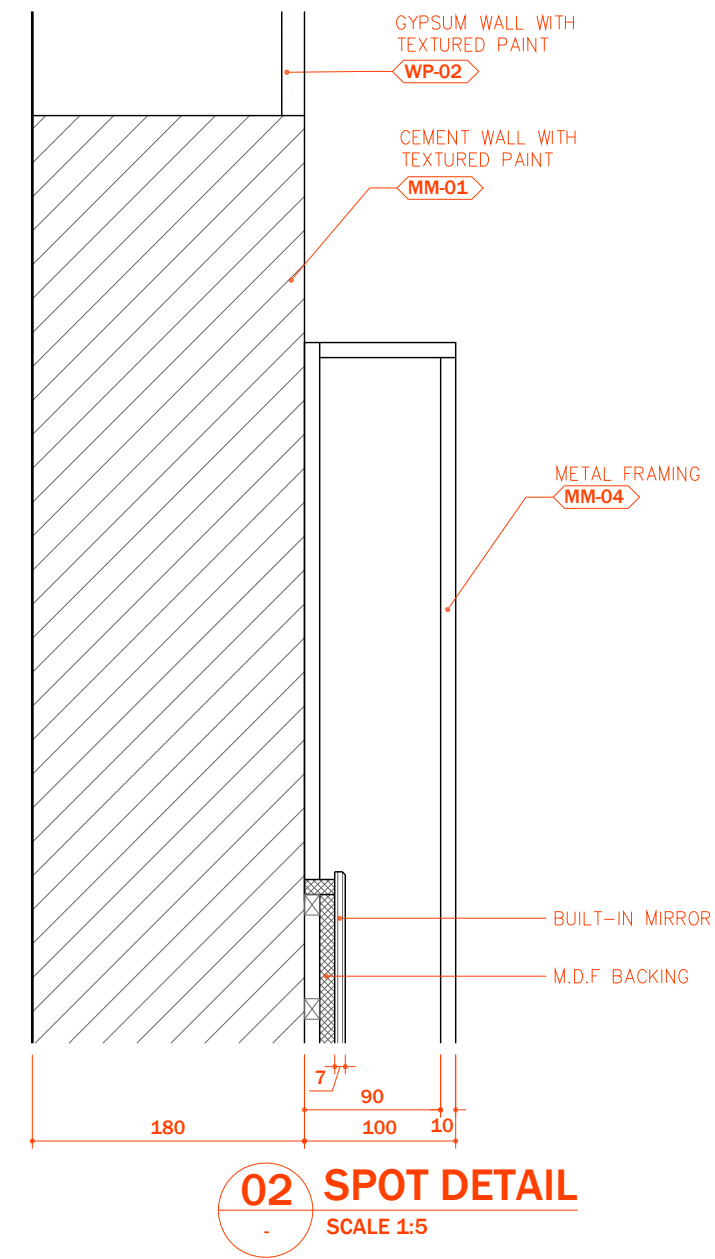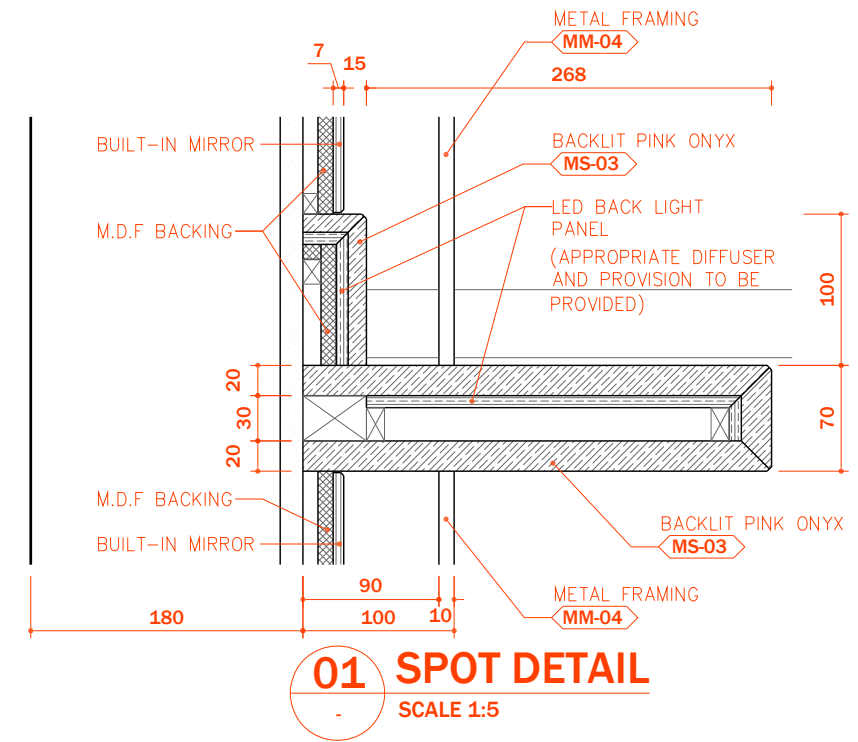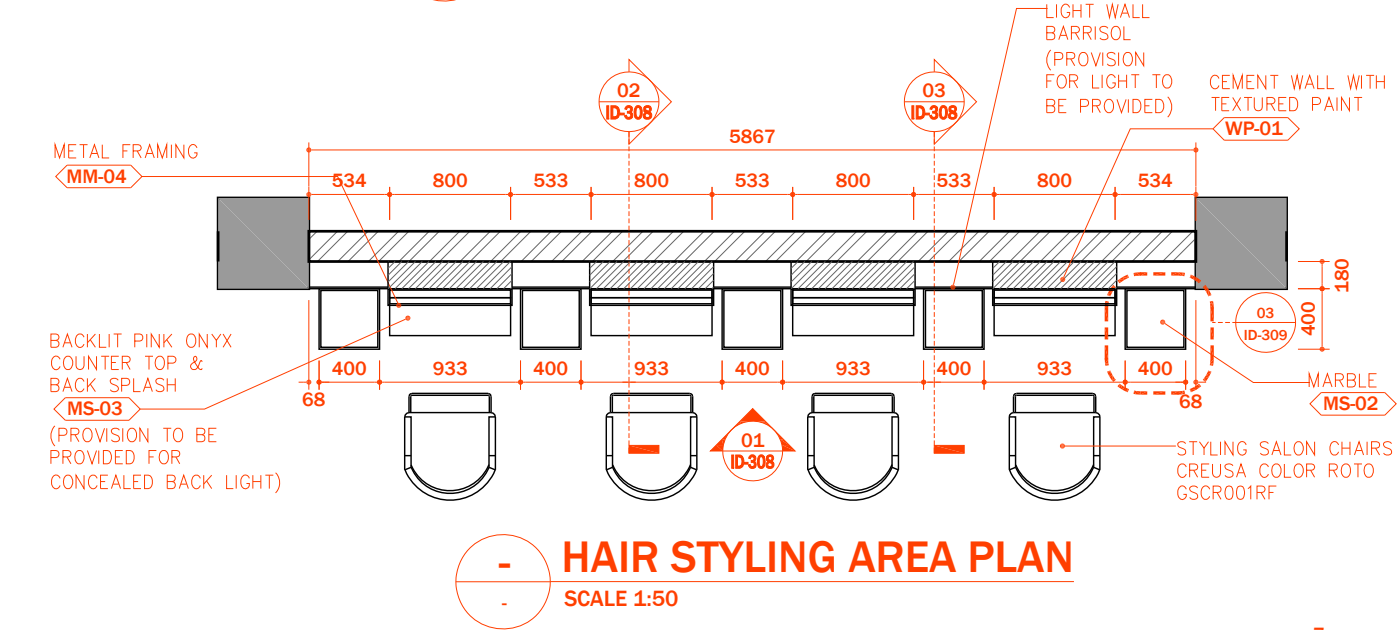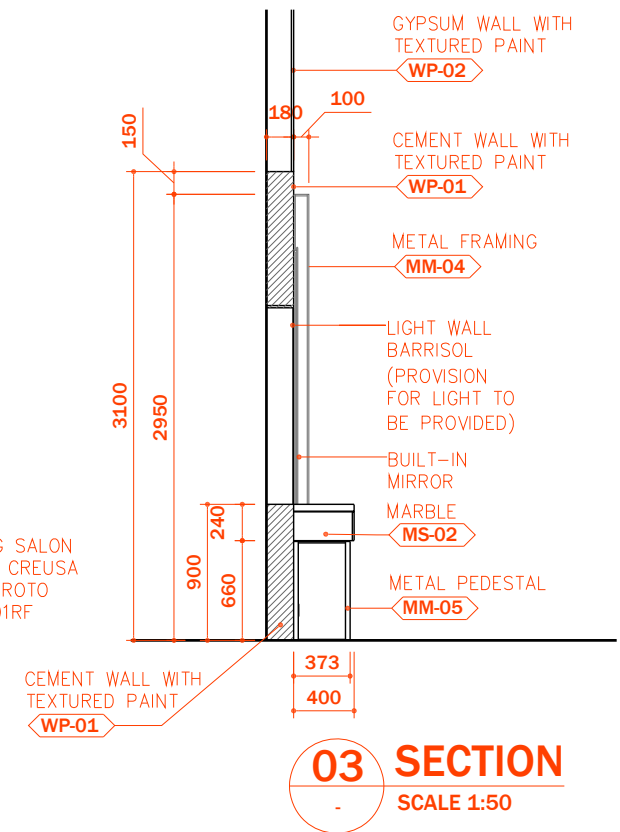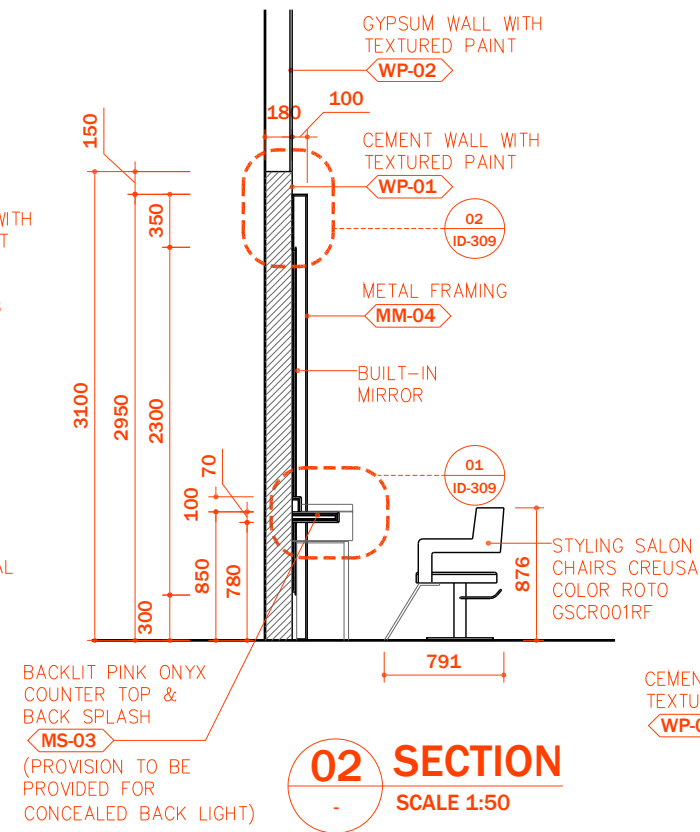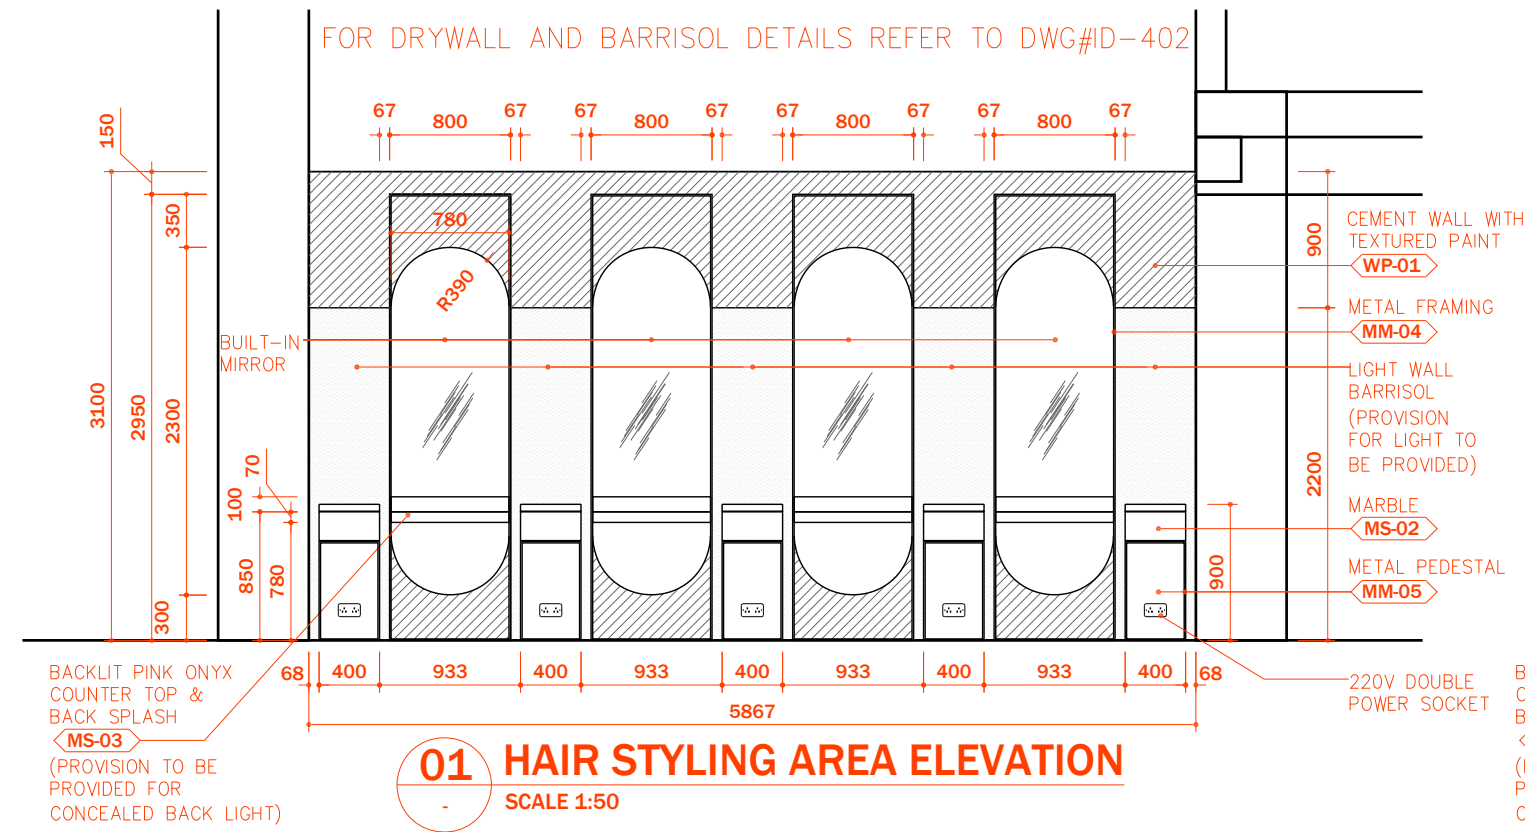


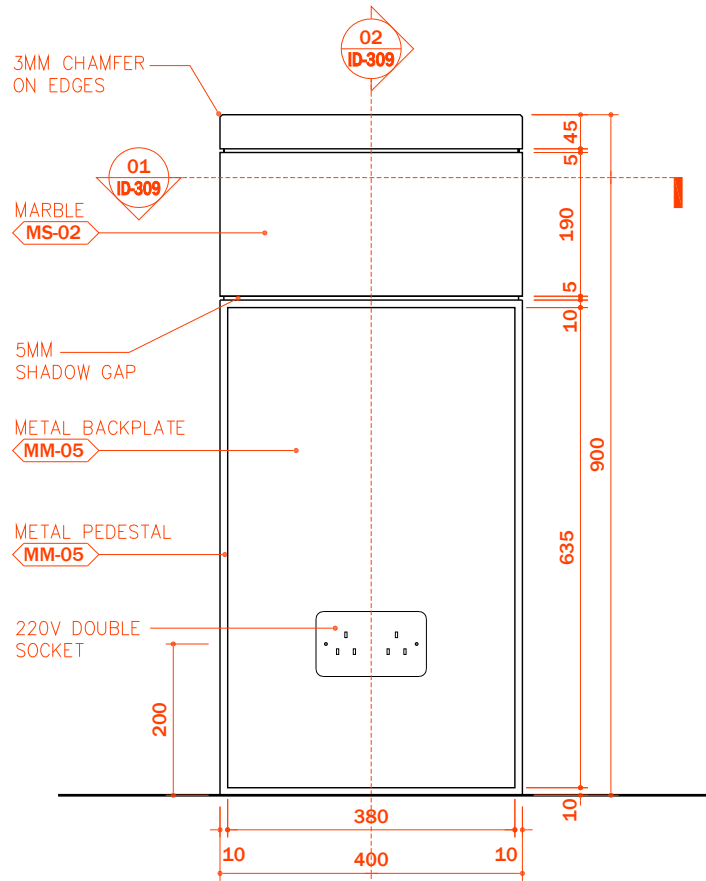


A DRAWER UNIT ELEVATION
SCALE 1:10

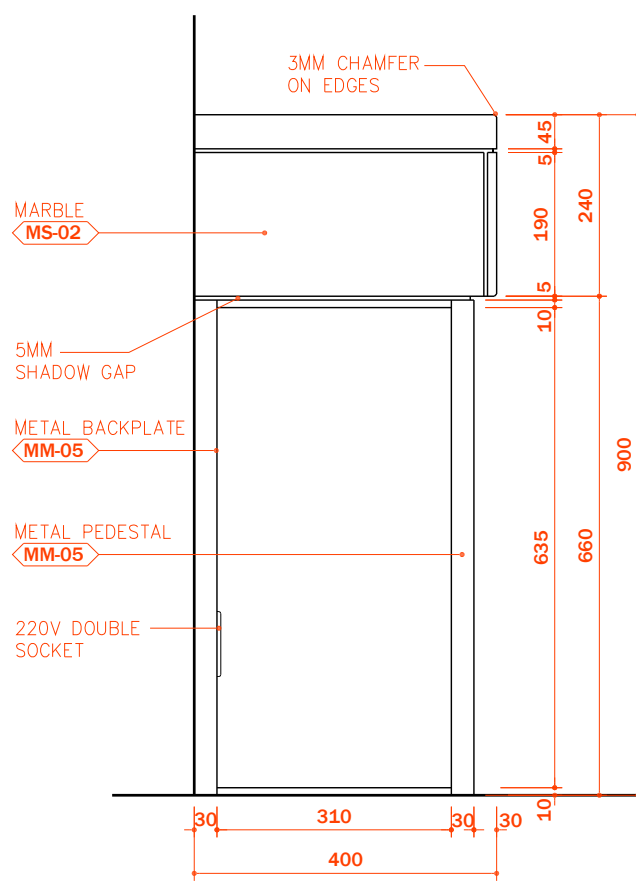


B DRAWER UNIT ELEVATION
SCALE 1:10

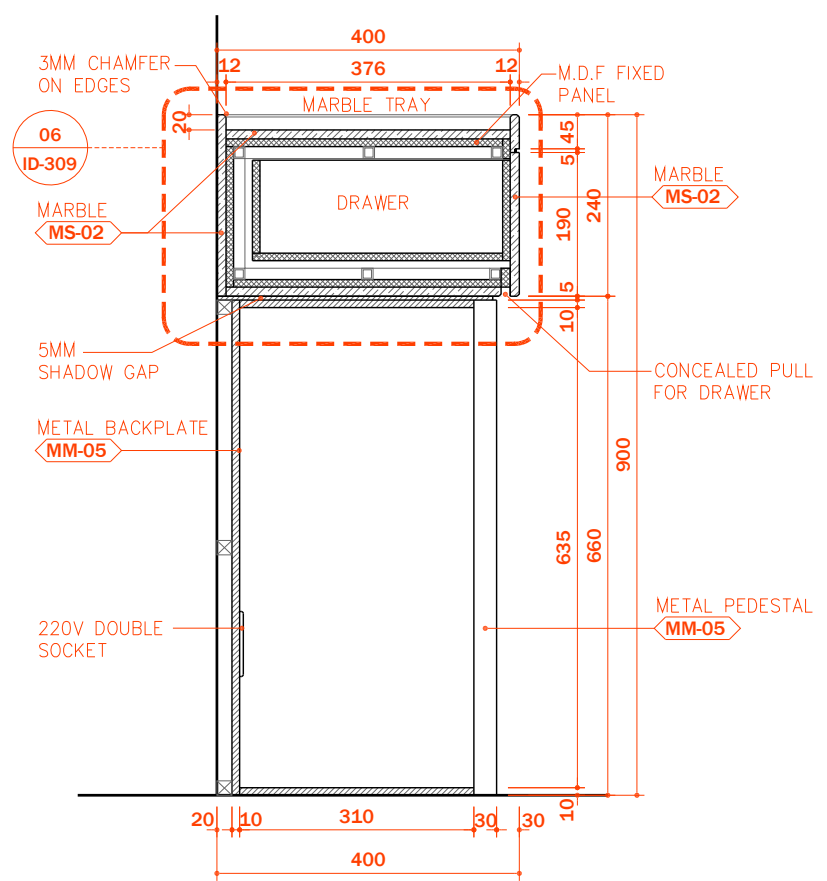


02 SECTION
SCALE 1:10

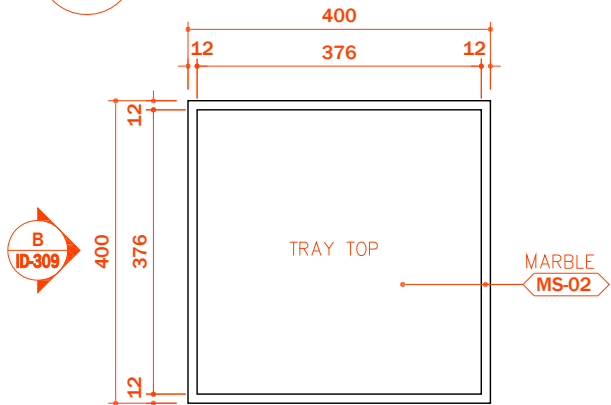


03 DRAWER UNIT PLAN
SCALE 1:10

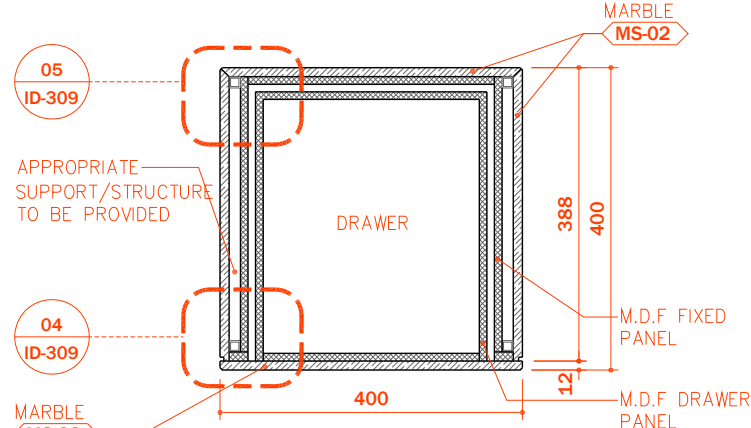


01 SECTION DETAIL
SCALE 1:10

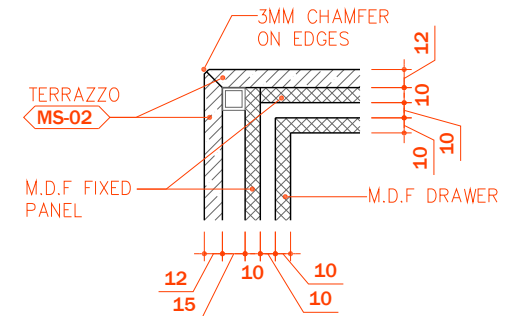








05 SPOT DETAIL
SCALE 1:5

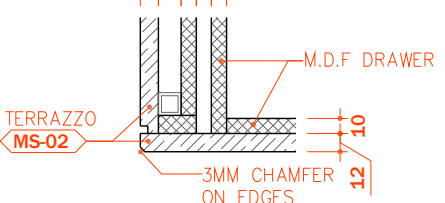


04 SPOT DETAIL
SCALE 1:5

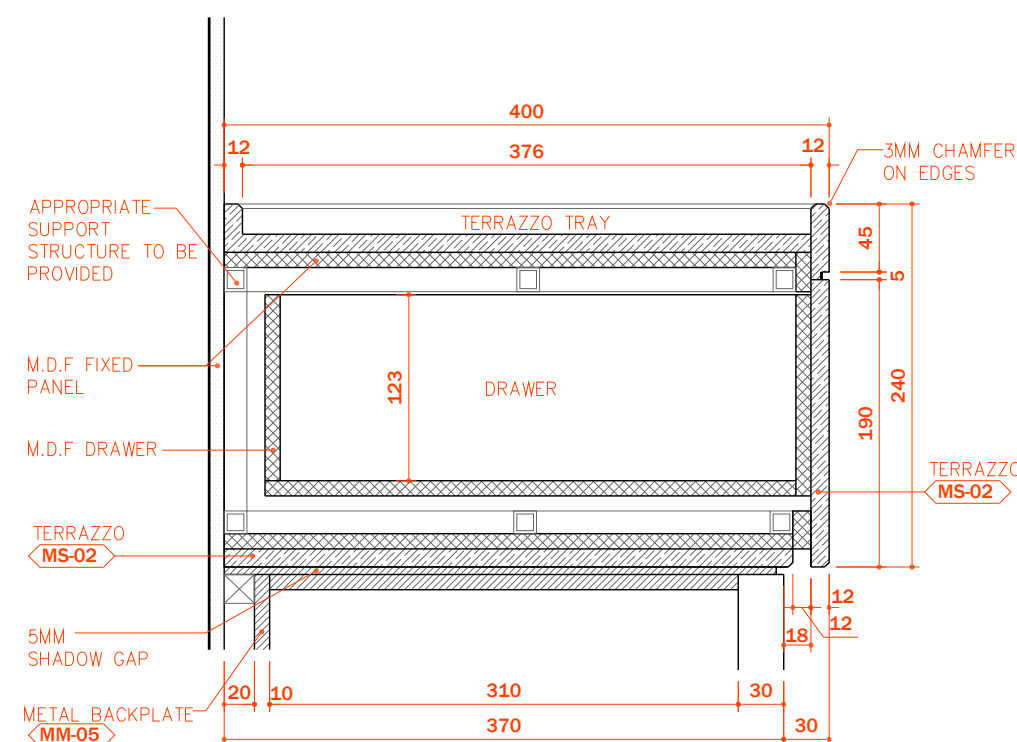


06 SPOT DETAIL
SCALE 1:5

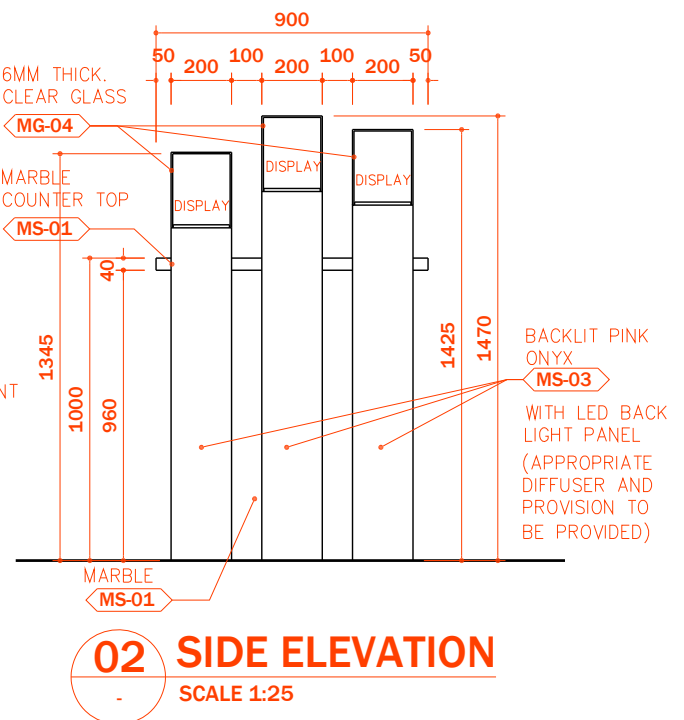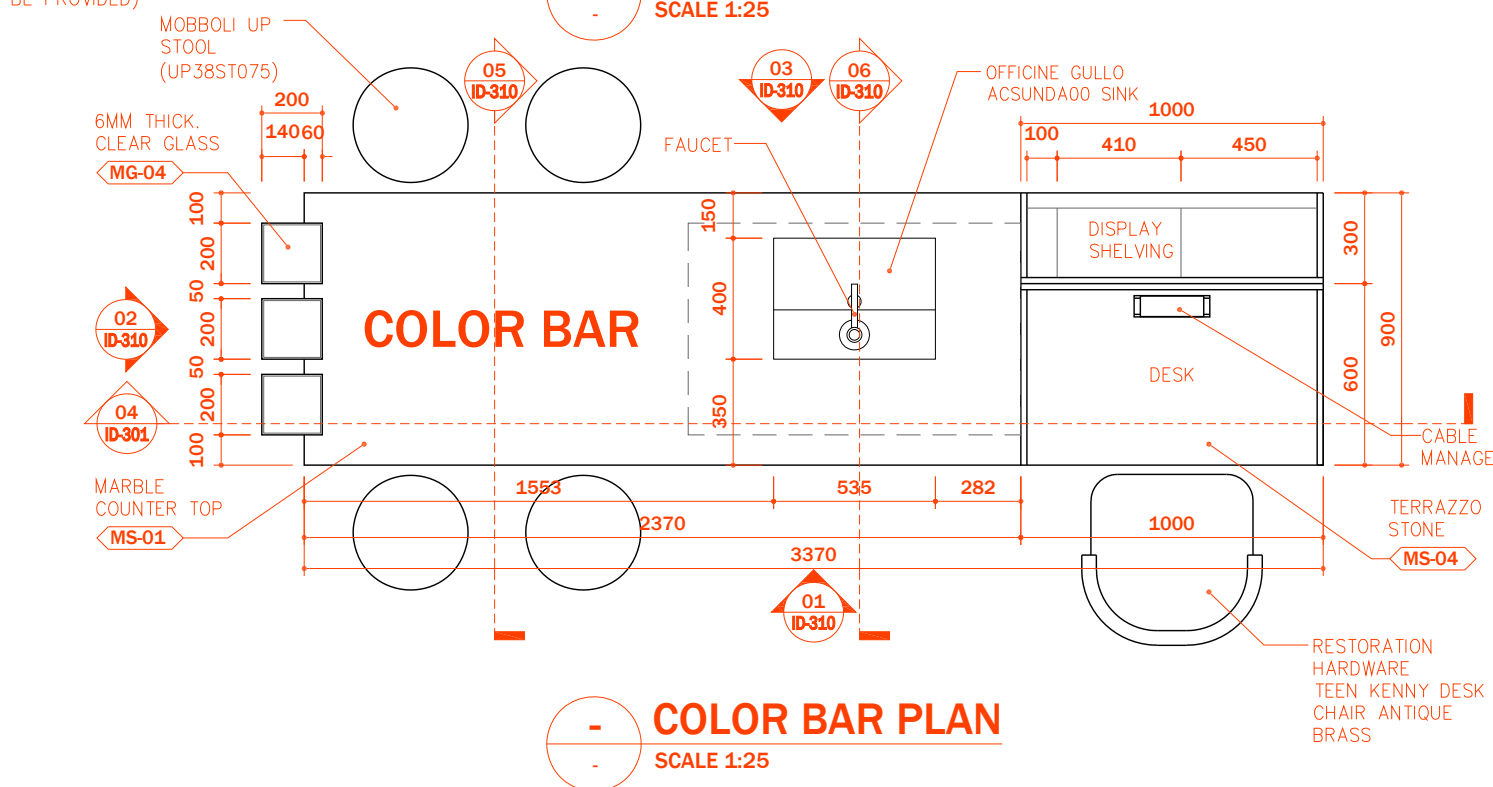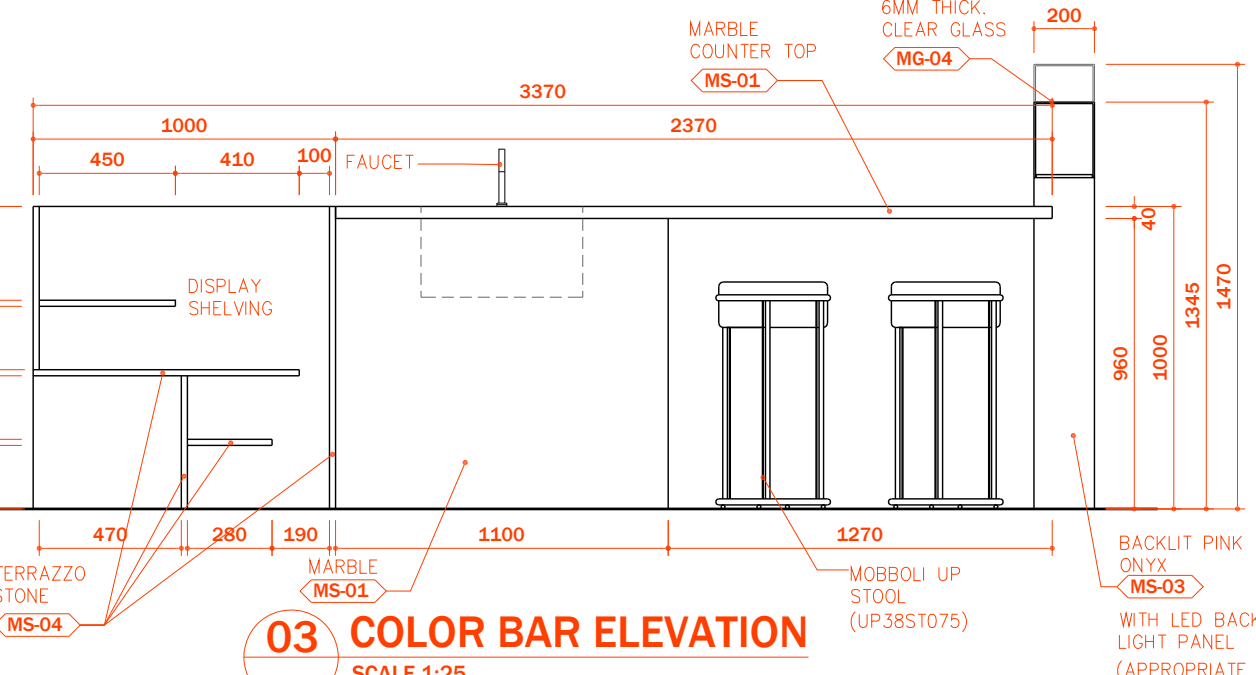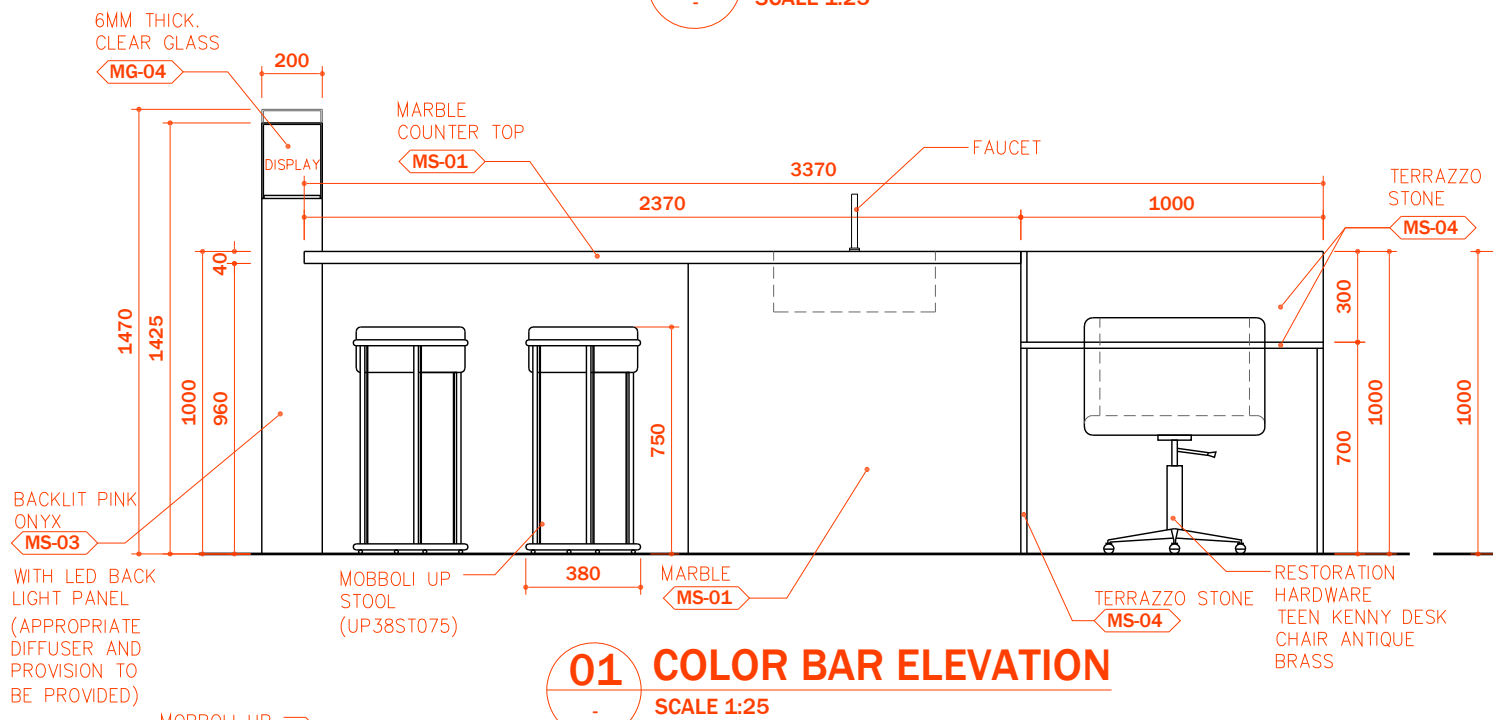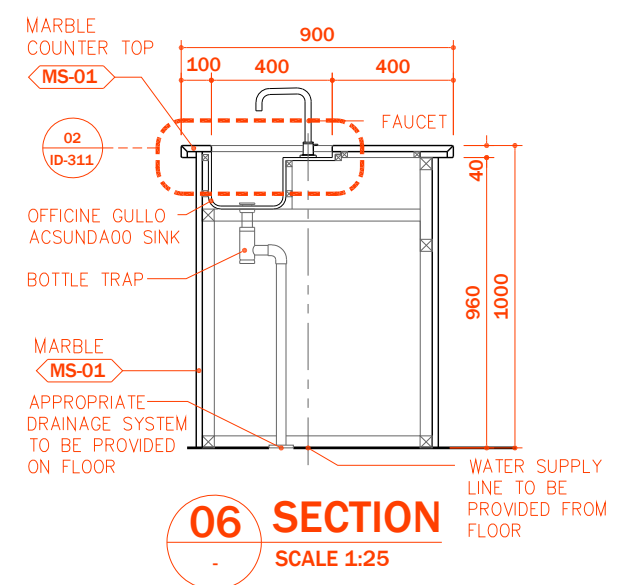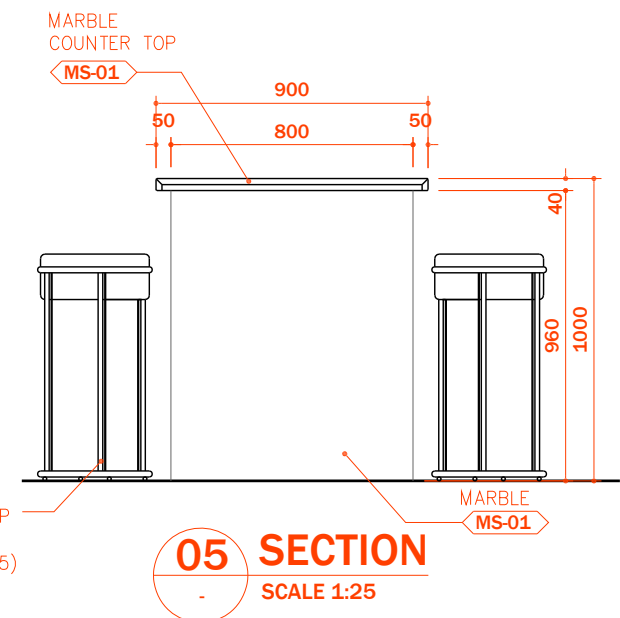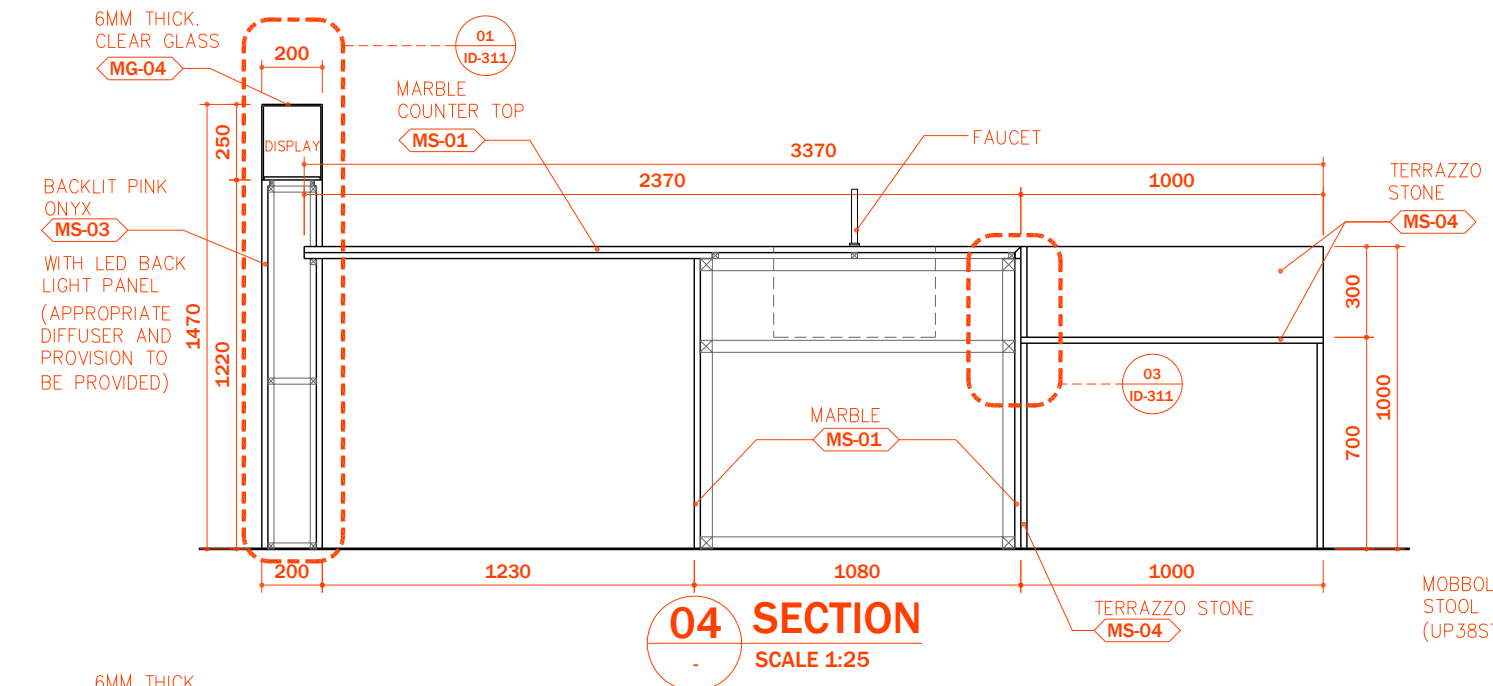


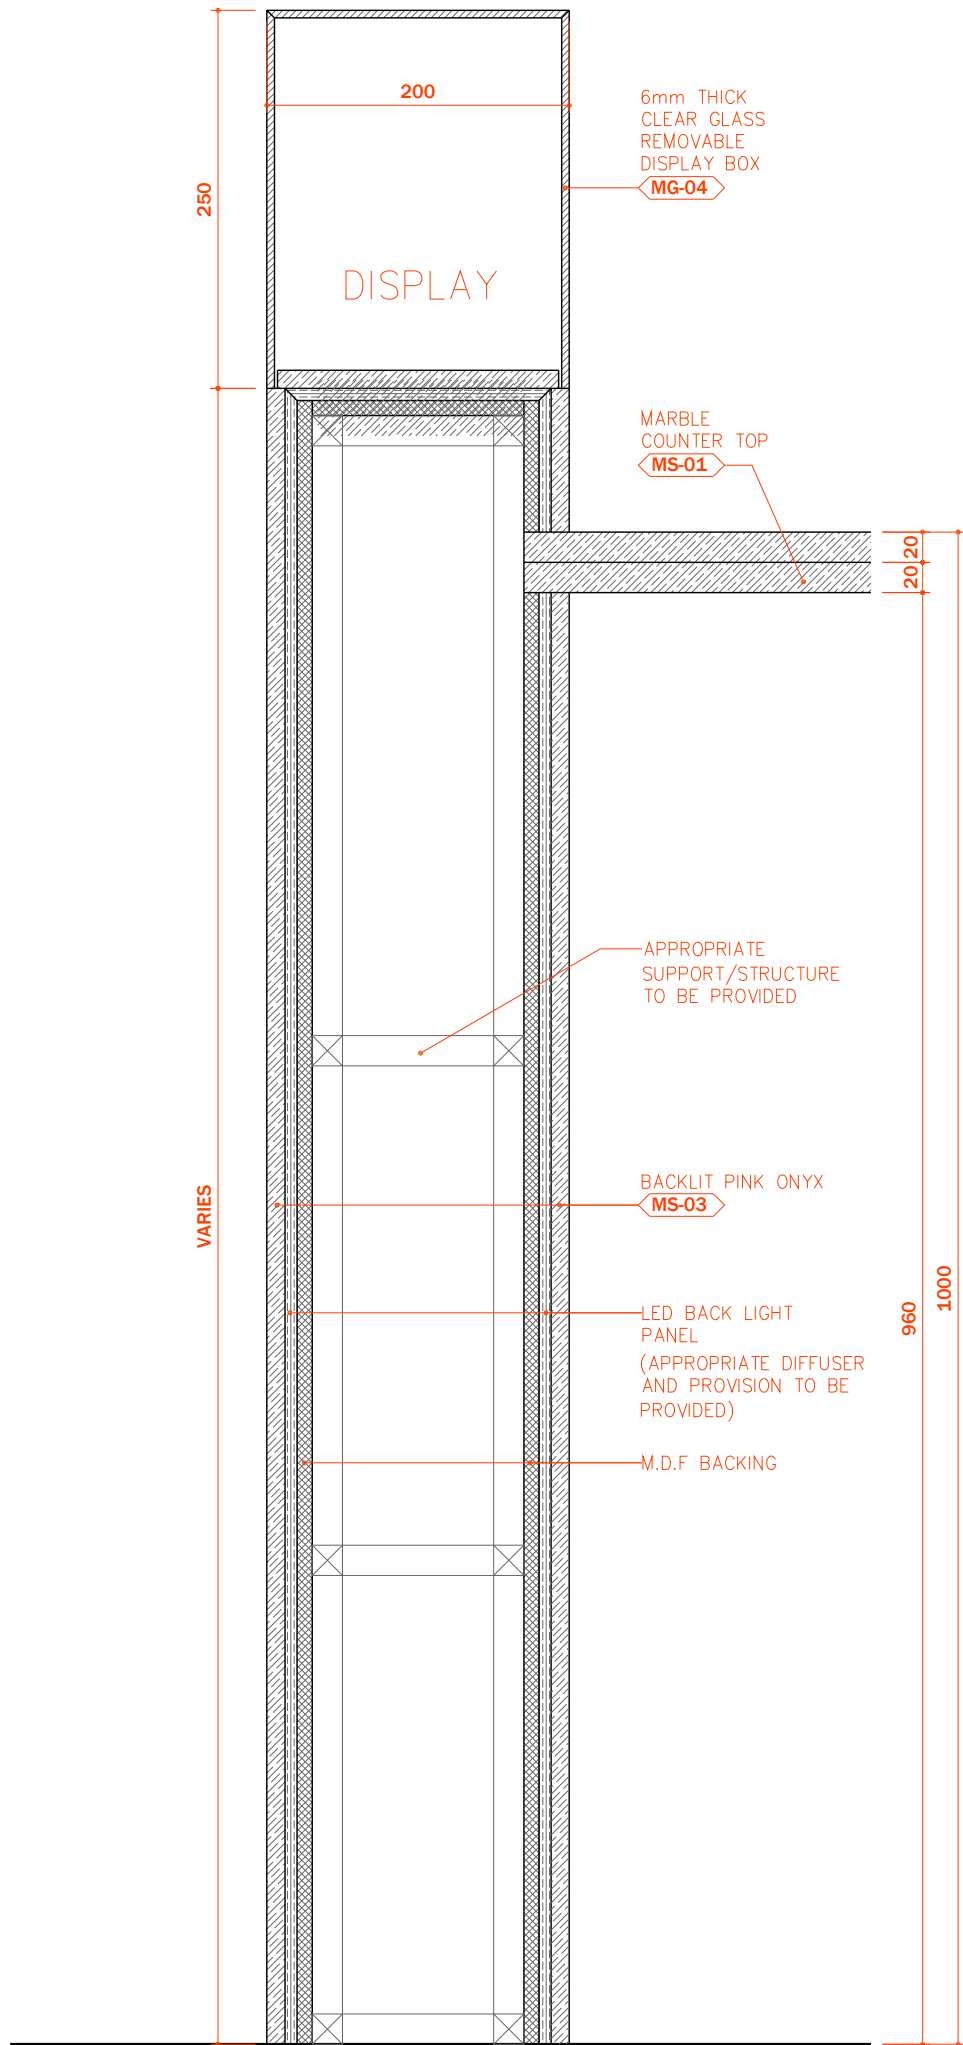


01 DISPLAY BOX DETAIL
SCALE 1:5

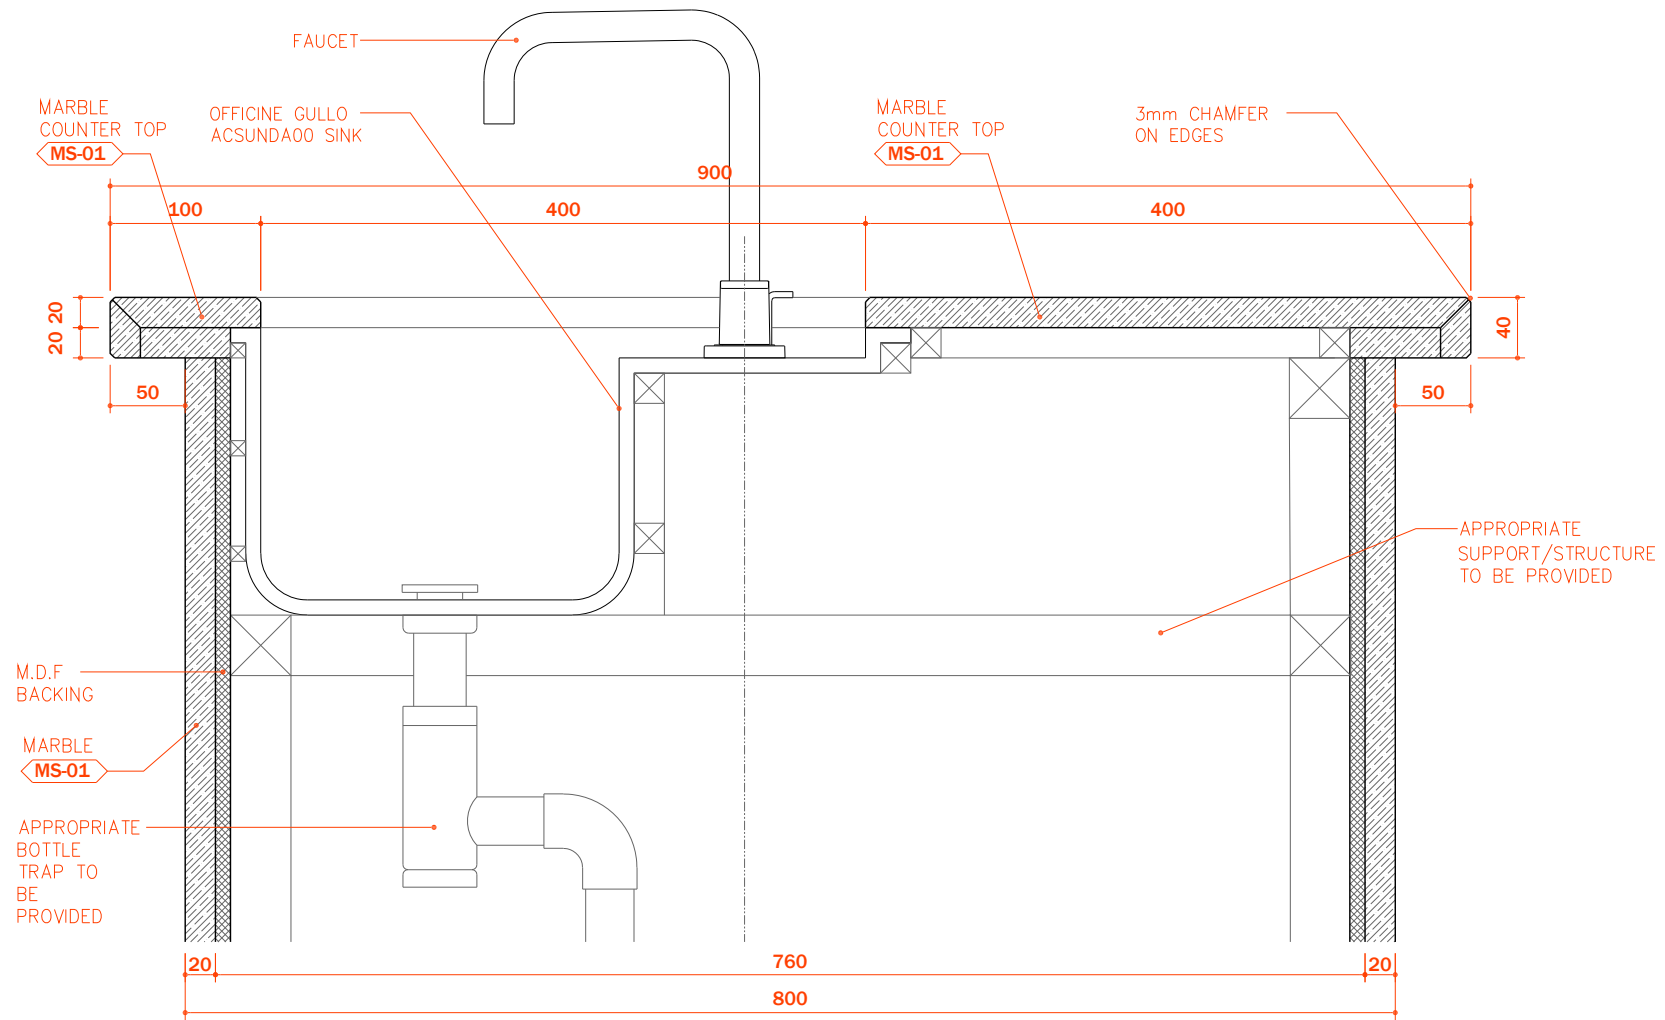


02 COLOR BAR DETAIL
SCALE 1:5

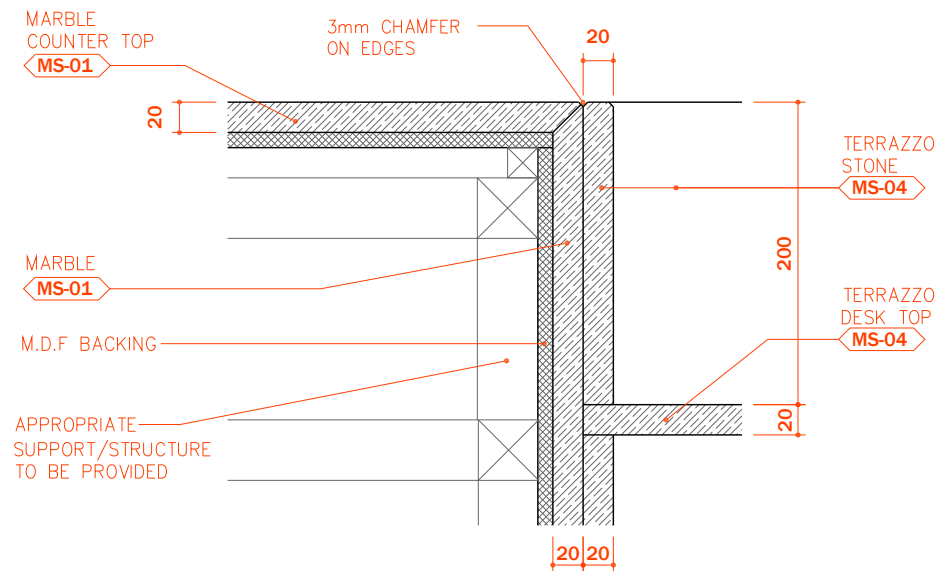


03 COLOR BAR DETAIL
SCALE 1:5

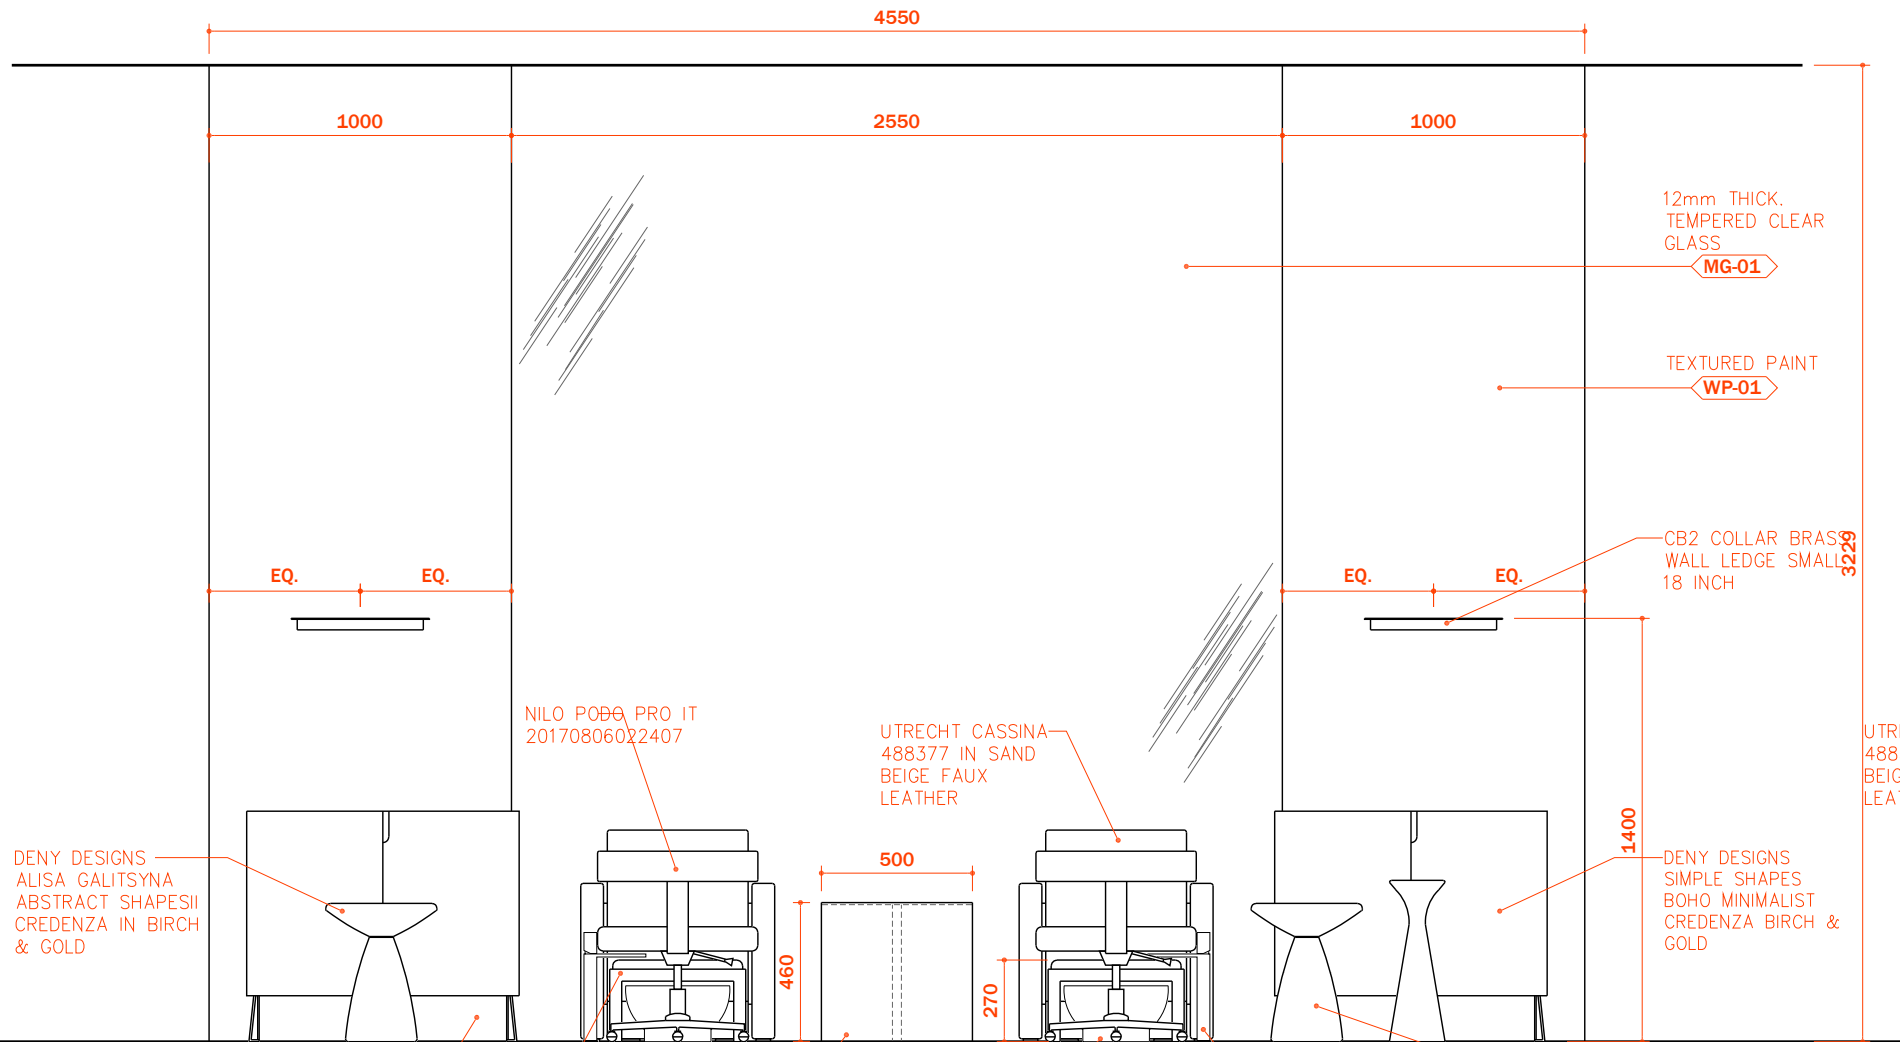

01 PEDICURE STATION ELEVATION
SCALE 1:25

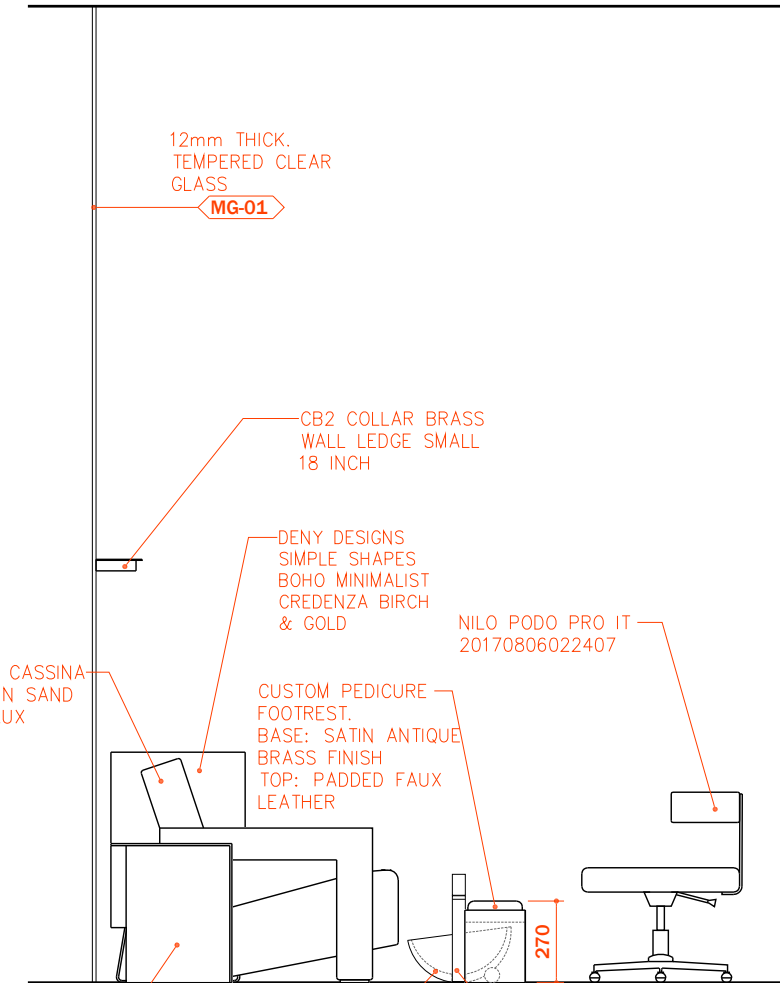


02 PEDICURE STATION SIDE ELEVATION
SCALE 1:25

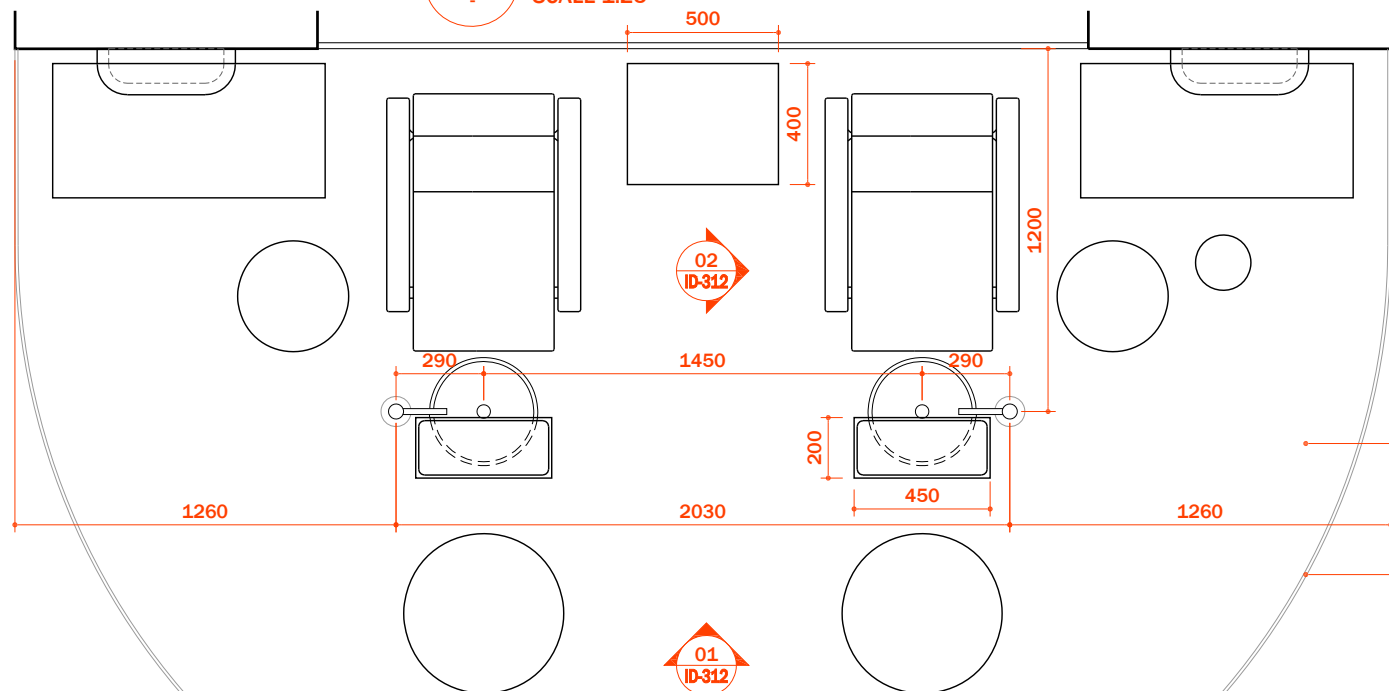

01 PEDICURE STATION PLAN
SCALE 1:25


GENESIS ROYAL
CREAM RMC.
FLOOR MARBLE
FS-02

ANTIQUE BRASS
METAL FLOORING
INLAY
FTS-01

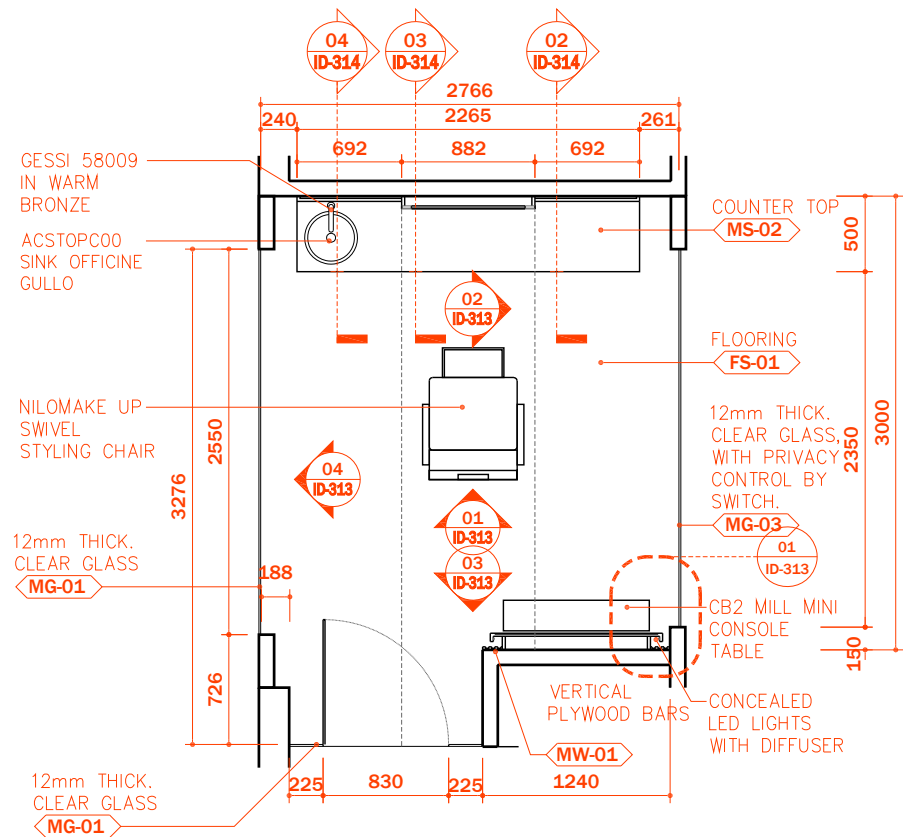


MAKE UP ROOM PLAN

SCALE 1:50

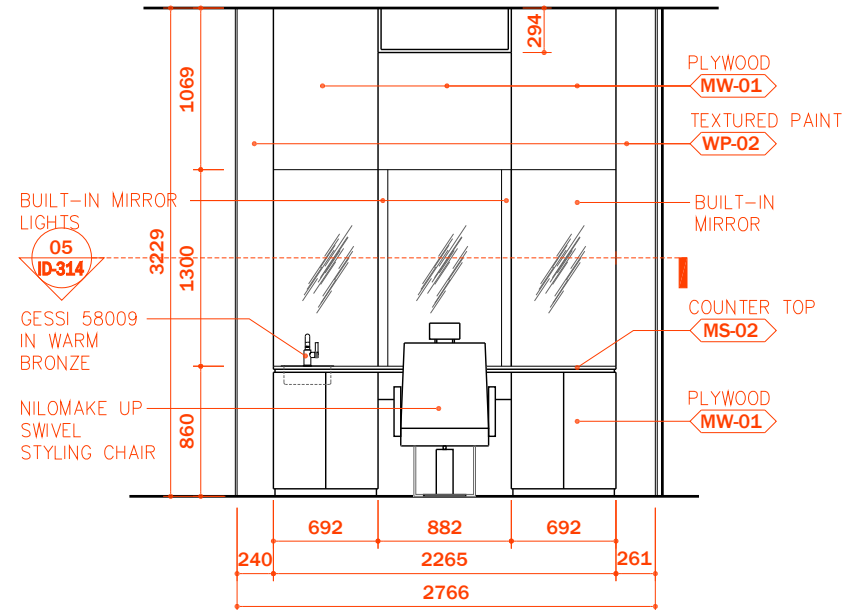


01 ELEVATION

SCALE 1:50

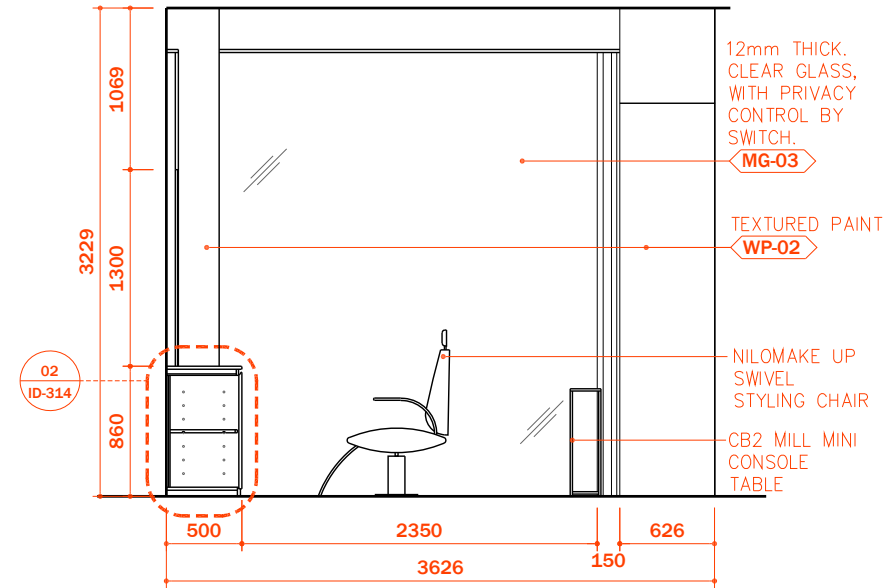


02 ELEVATION

SCALE 1:50

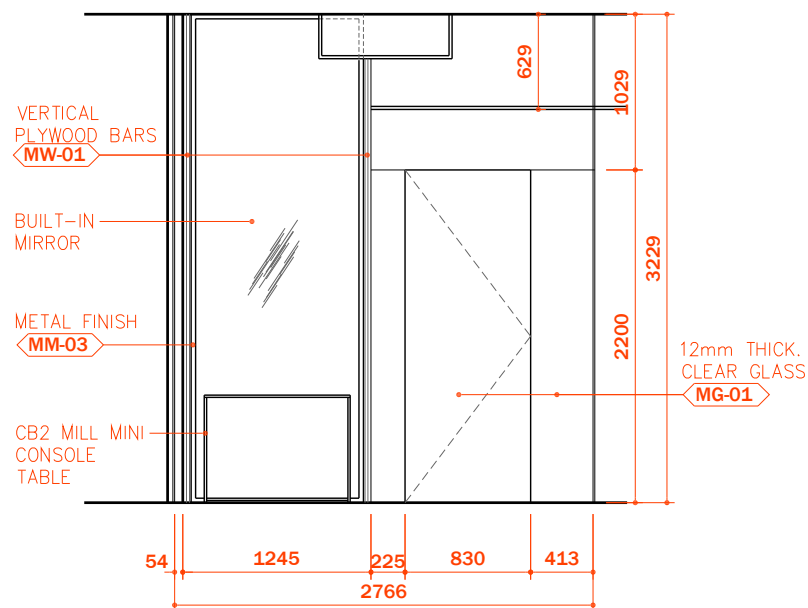


03 ELEVATION

SCALE 1:50

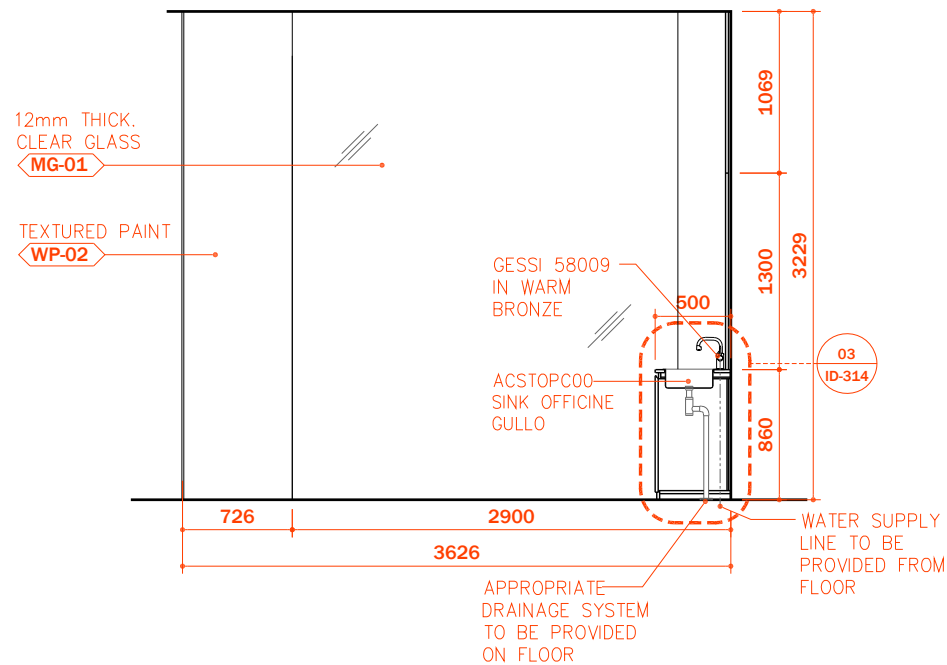





04 ELEVATION


SCALE 1:50

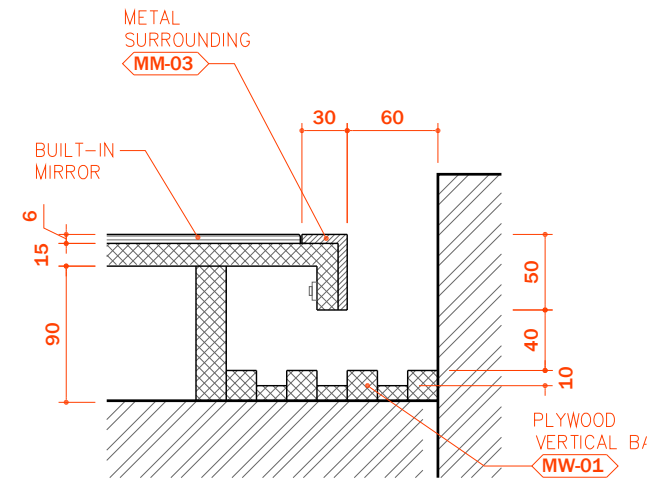

01 SPOT DETAIL


SCALE 1:5

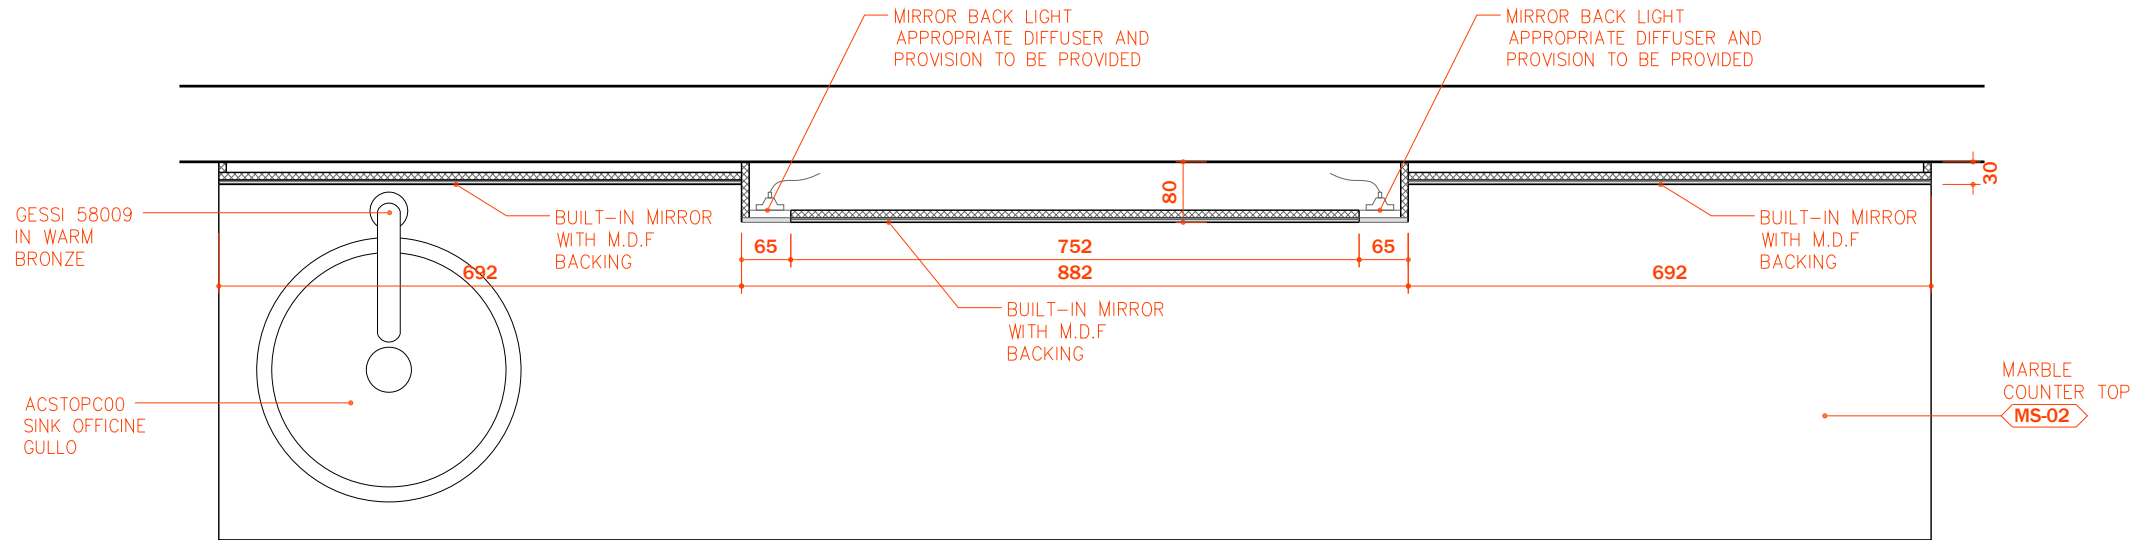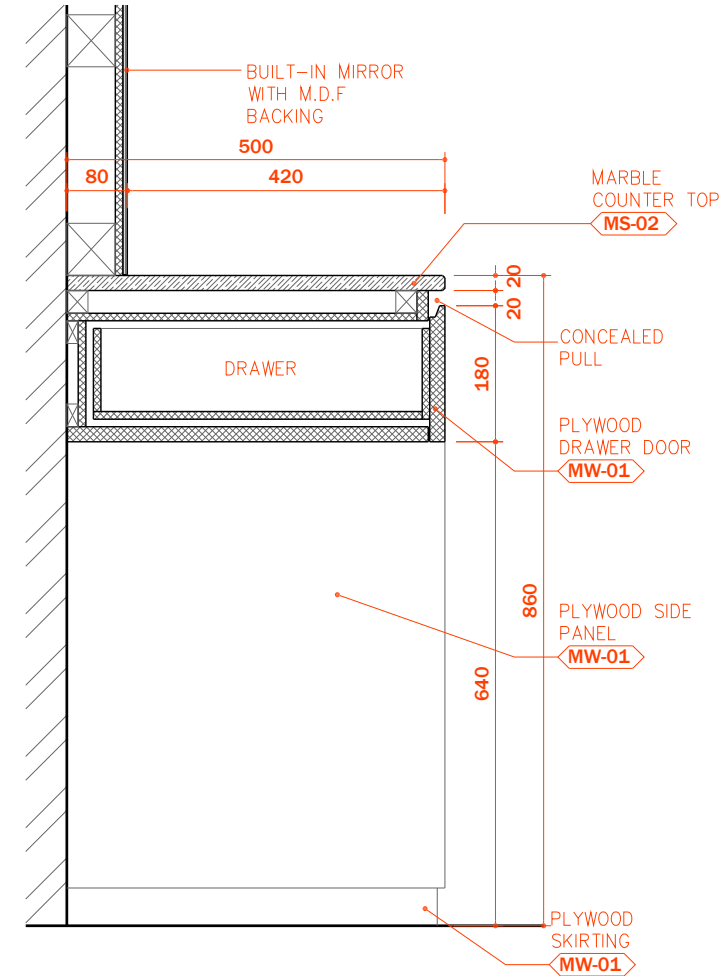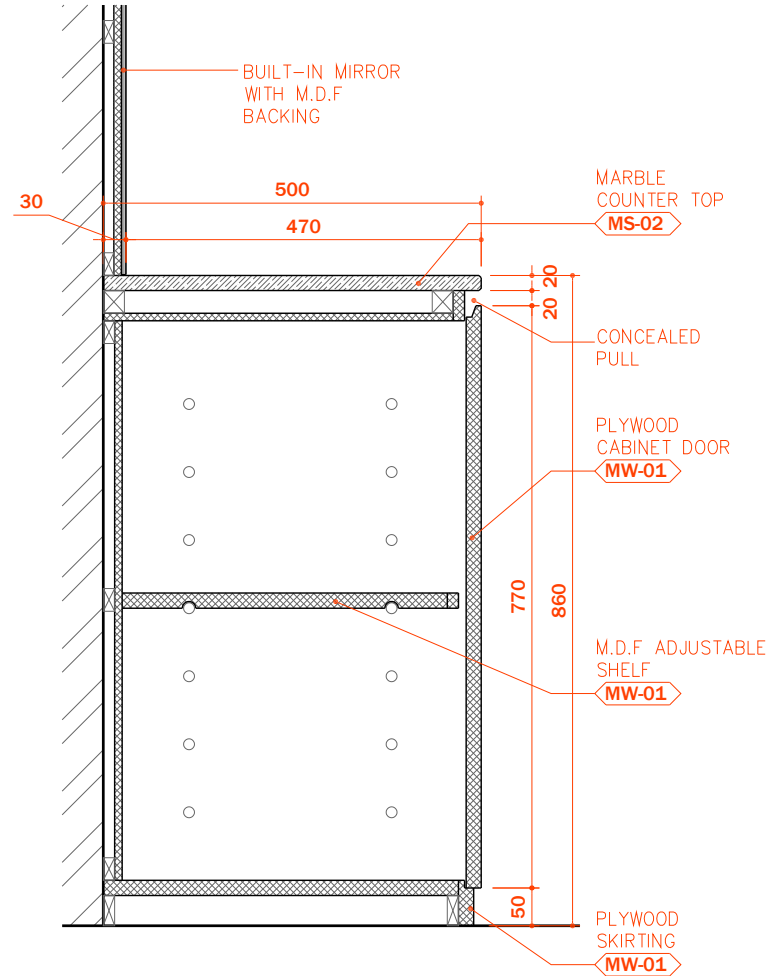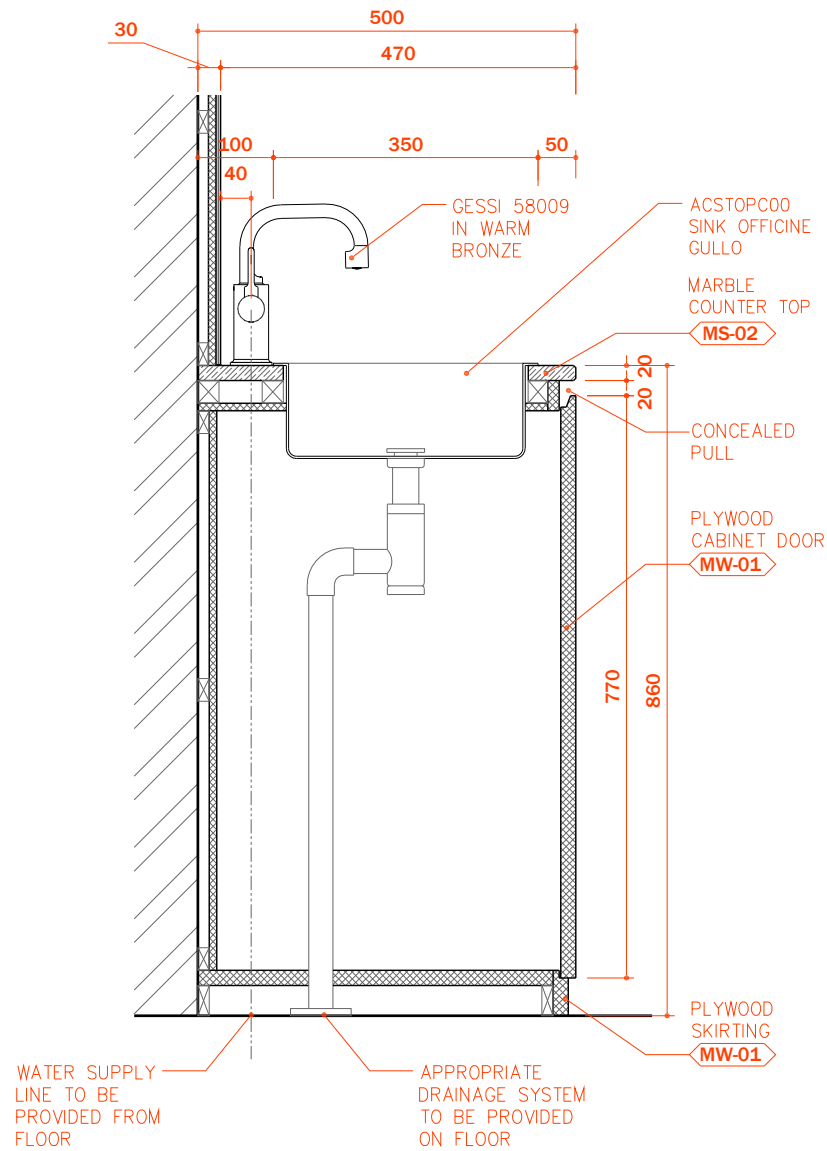

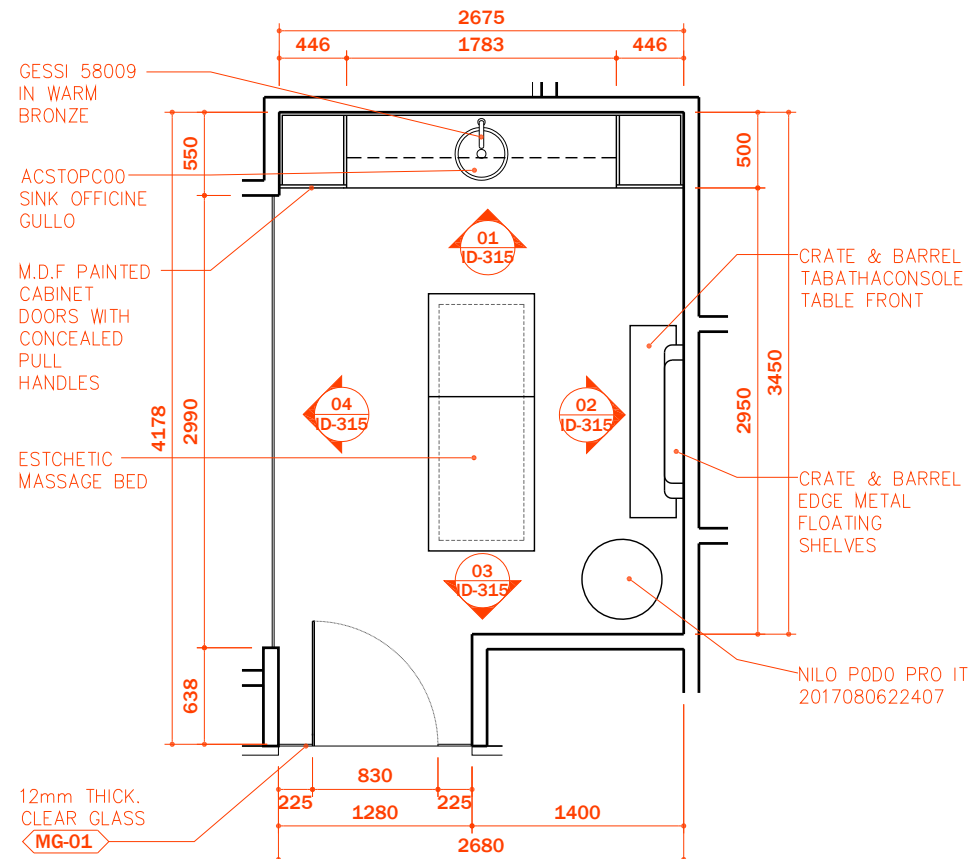


WAXING ROOM PLAN

SCALE 1:50

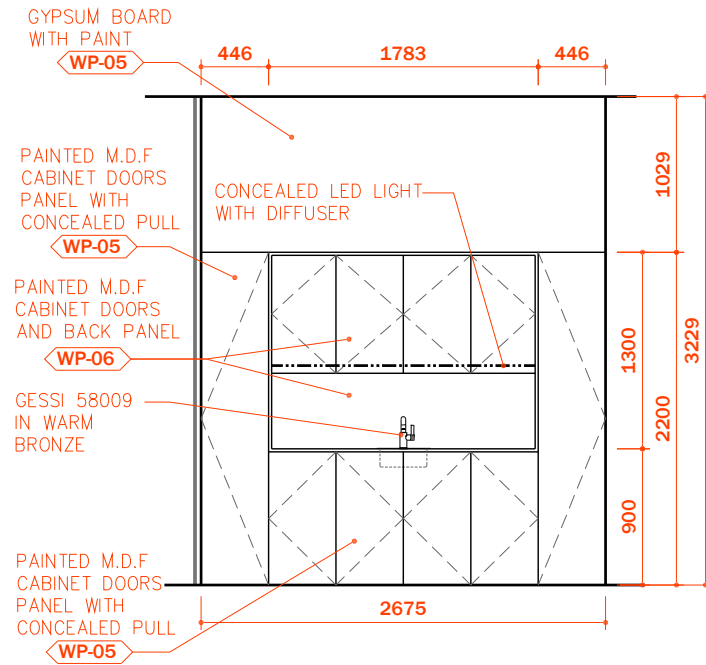


01 ELEVATION

SCALE 1:50

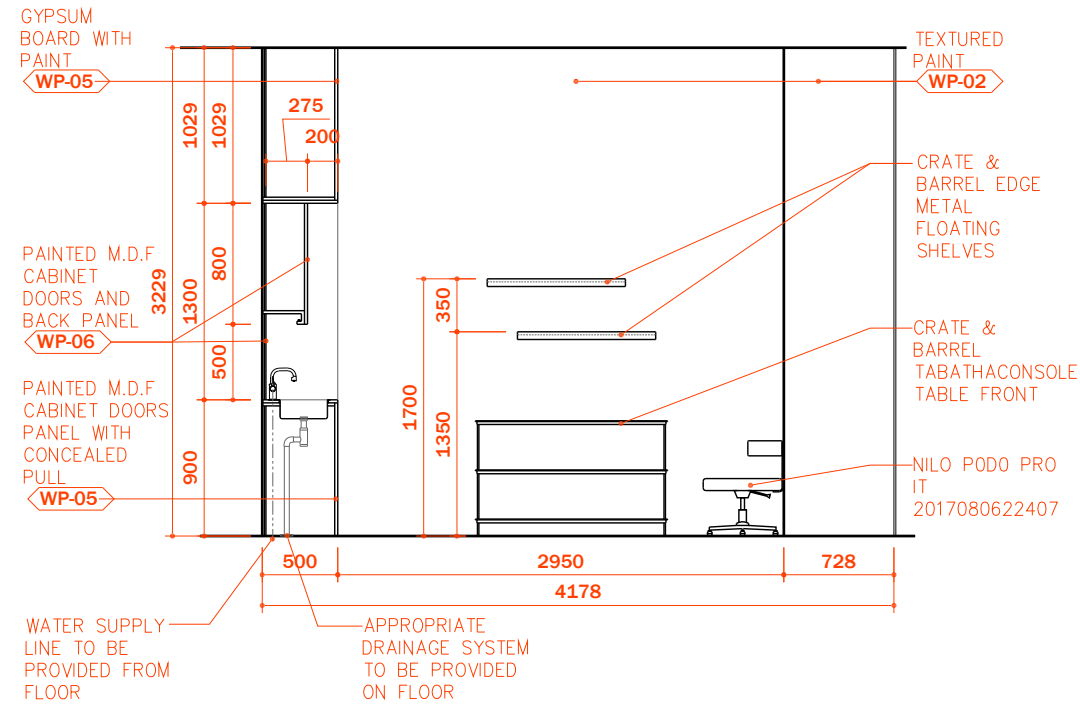


02 ELEVATION

SCALE 1:50

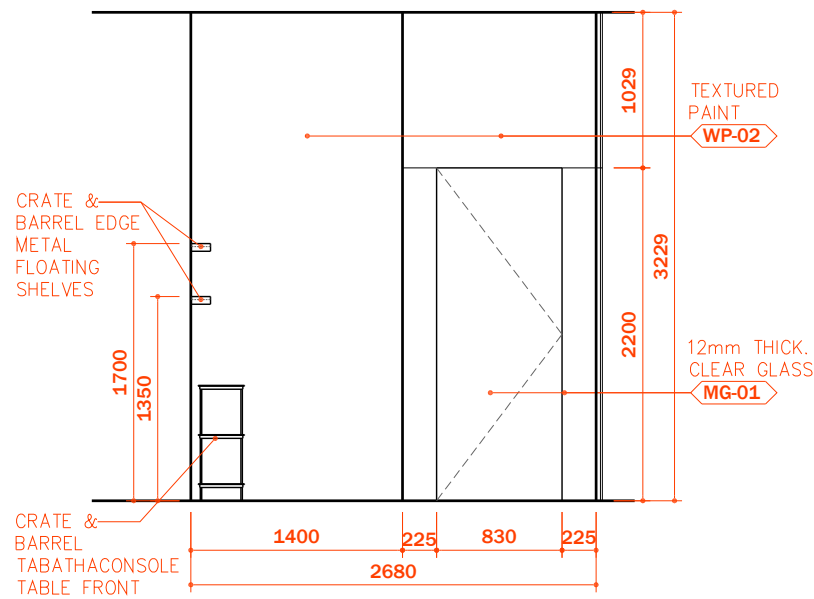


03 ELEVATION

SCALE 1:50

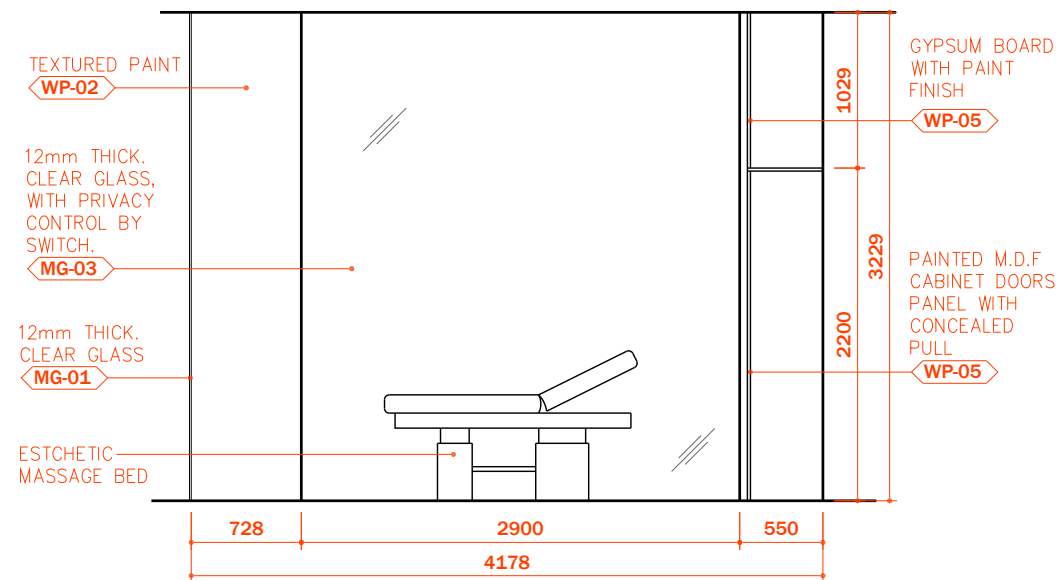


04 ELEVATION


SCALE 1:50

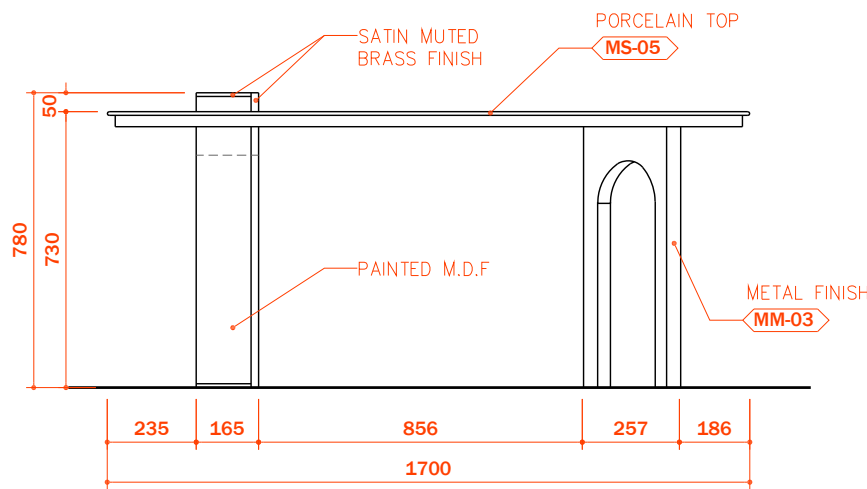


A MANICURE DESK ELEVATION
SCALE 1:20

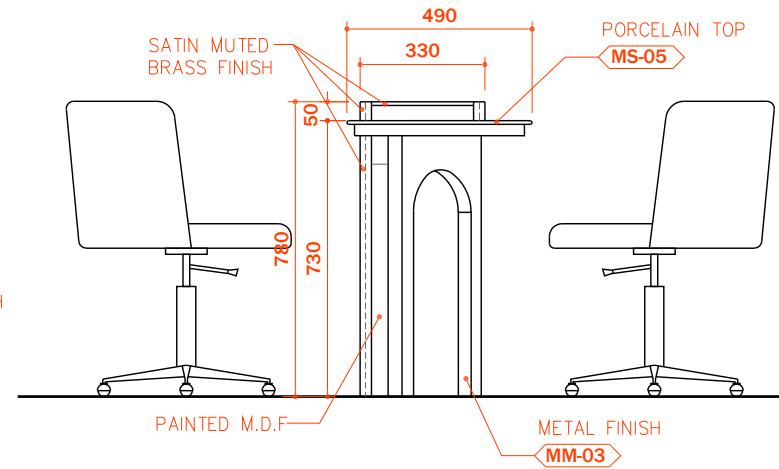


B SIDE ELEVATION
SCALE 1:20

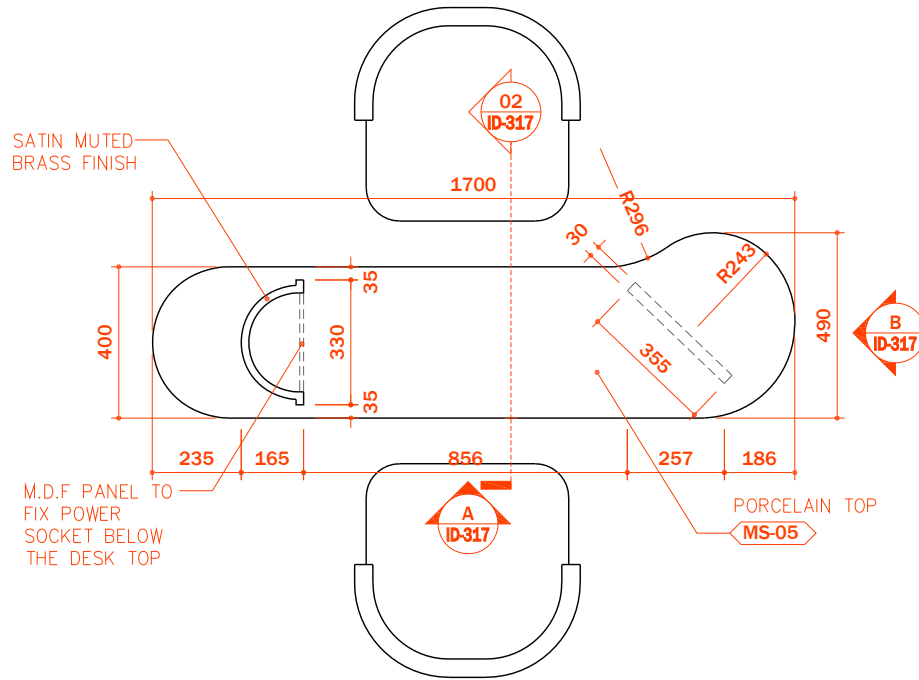


01 MANICURE DESK PLAN
SCALE 1:20

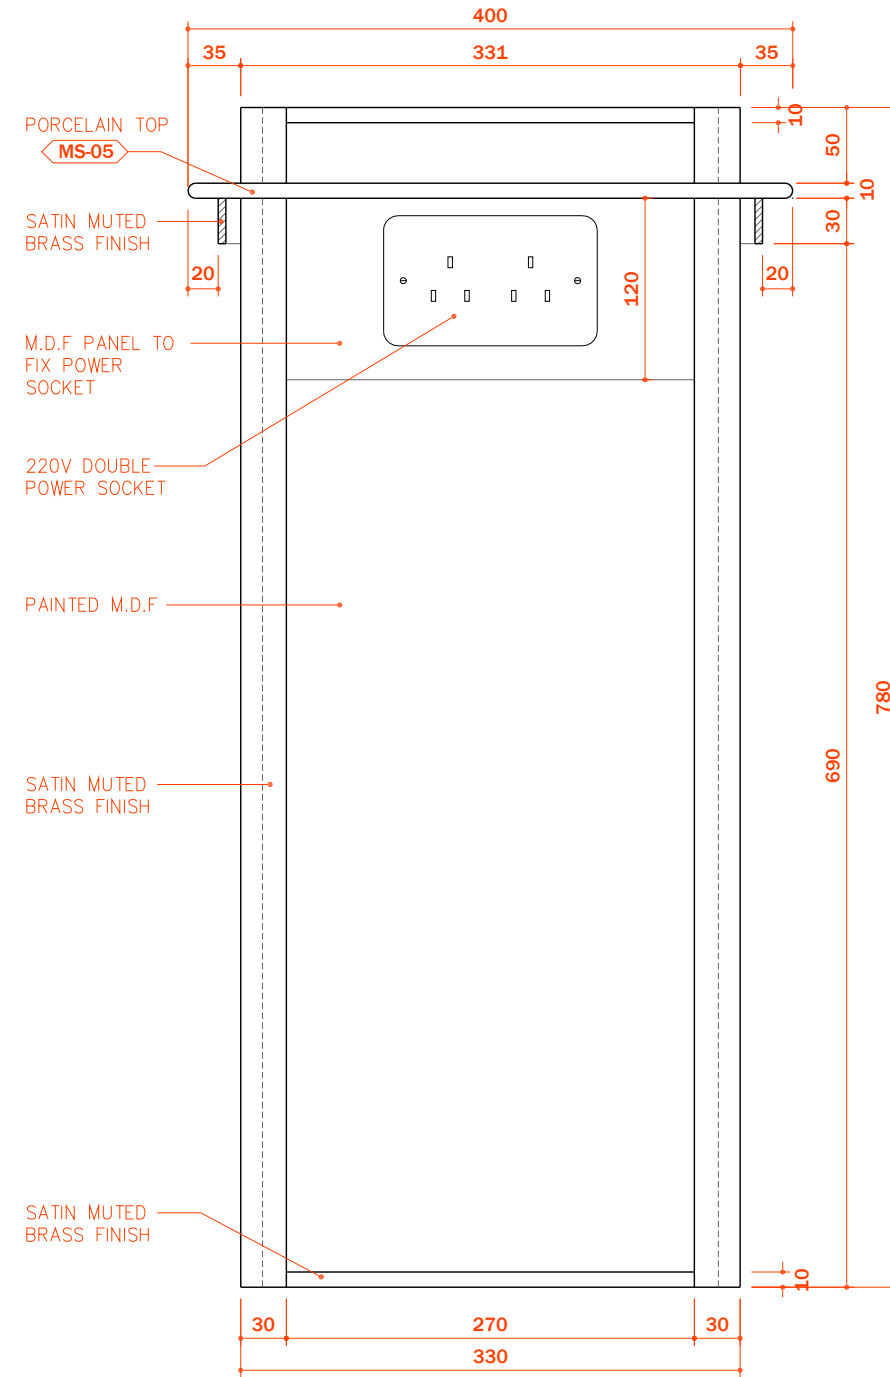


02 SECTION
SCALE 1:20

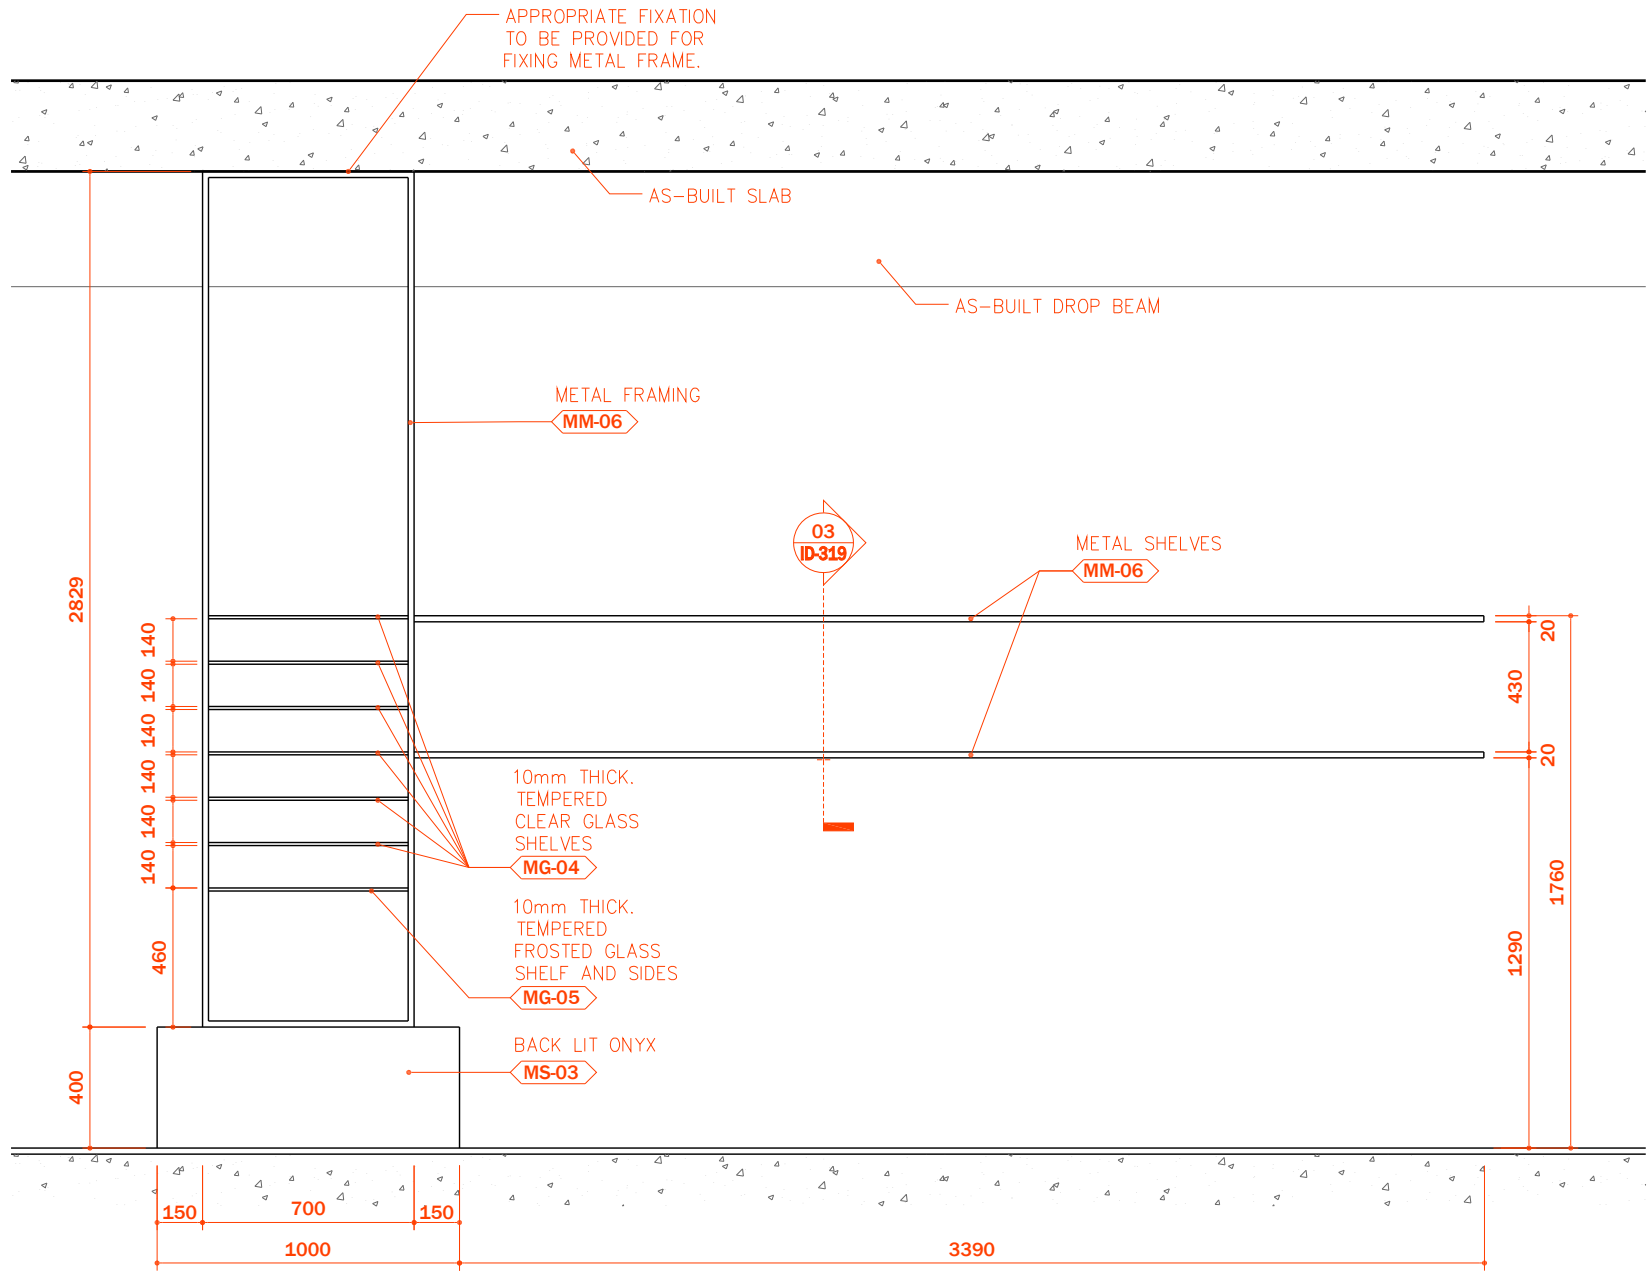


A DISPLAY / SHELVING ELEVATION
SCALE 1:25

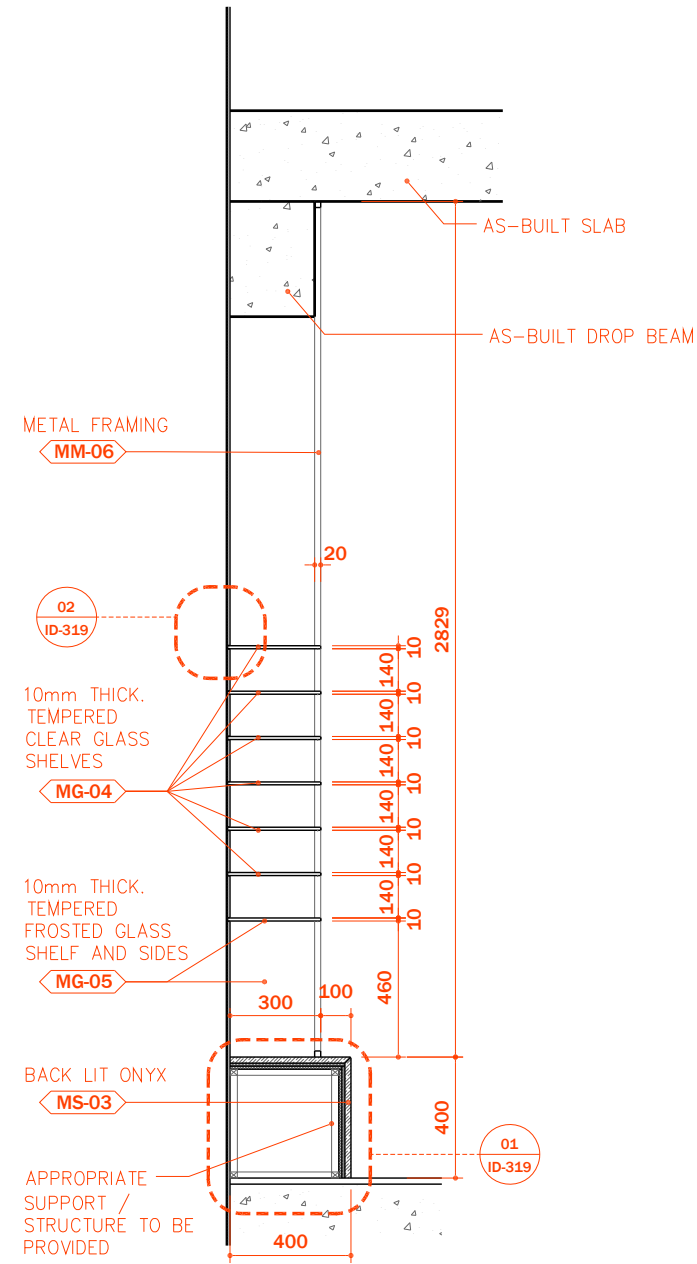


02 SECTION
SCALE 1:25

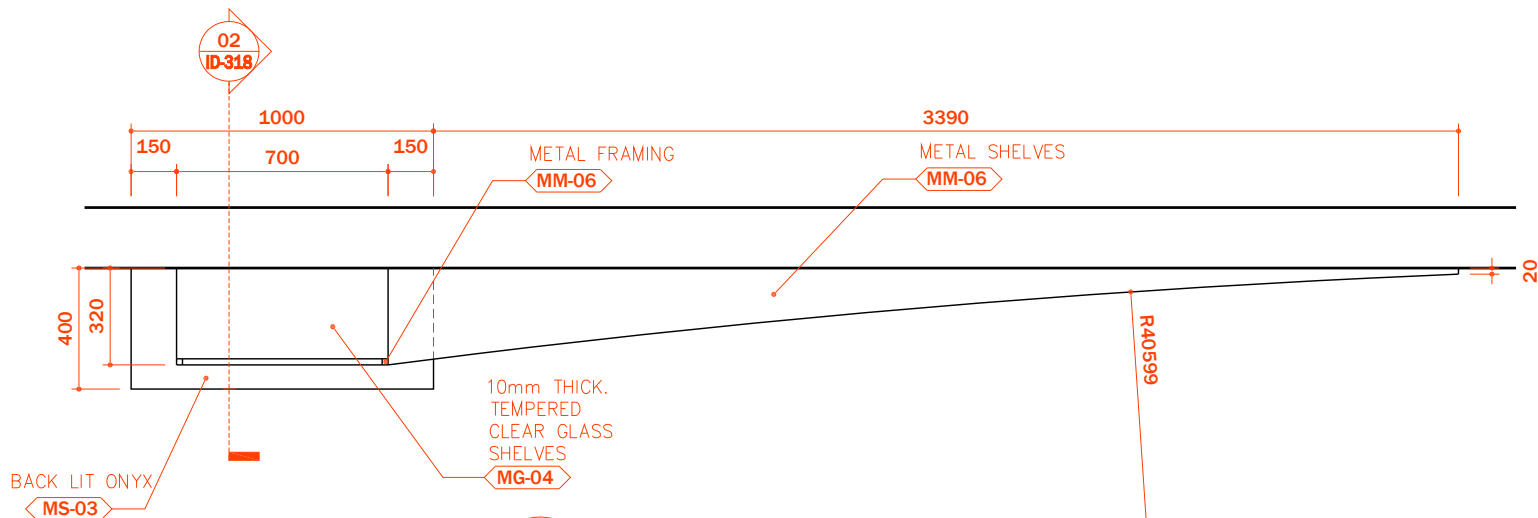


01 DISPLAY / SHELVING PLAN
SCALE 1:25

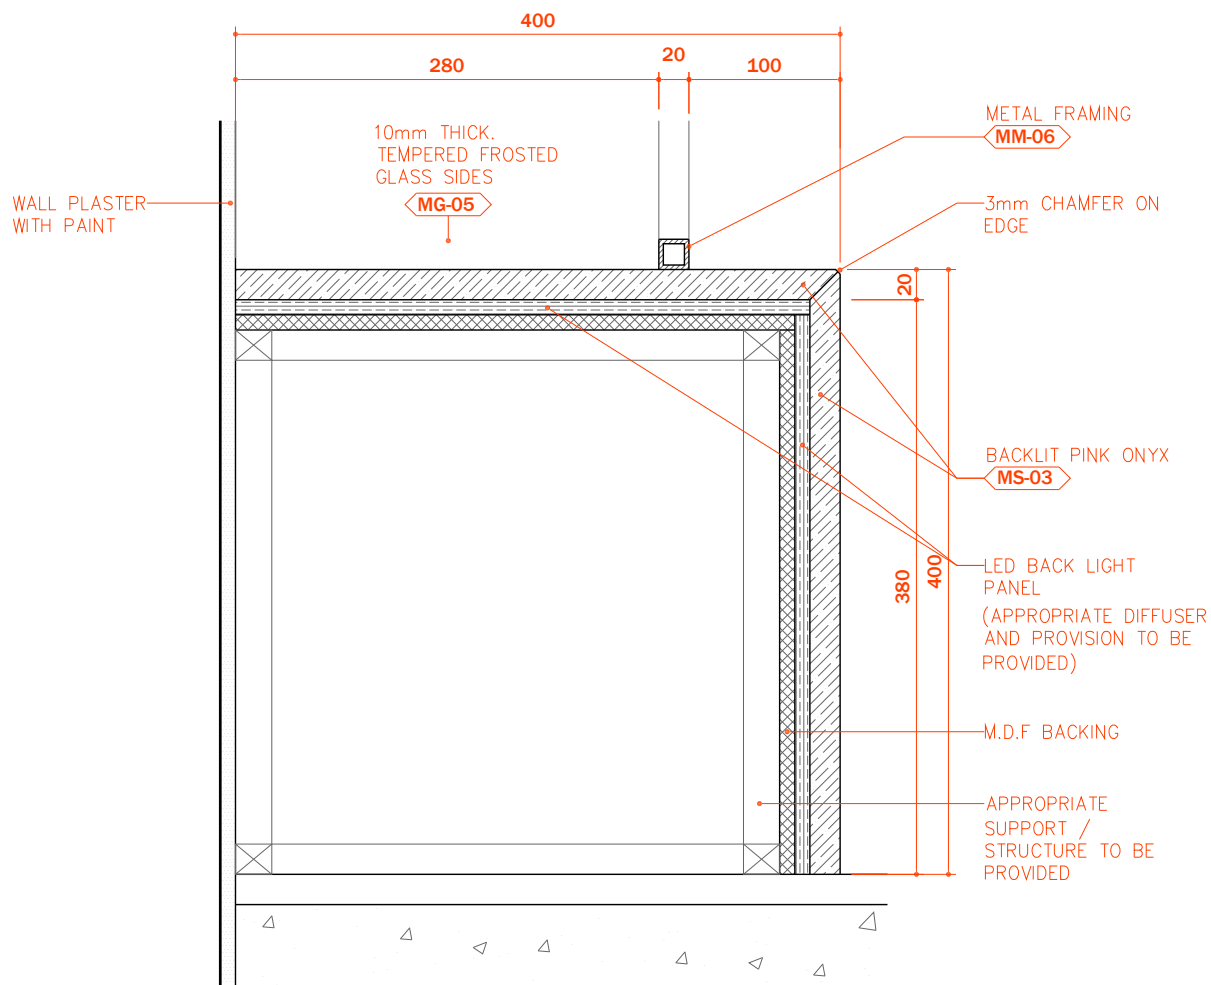


01 SPOT DETAIL
SCALE 1:5

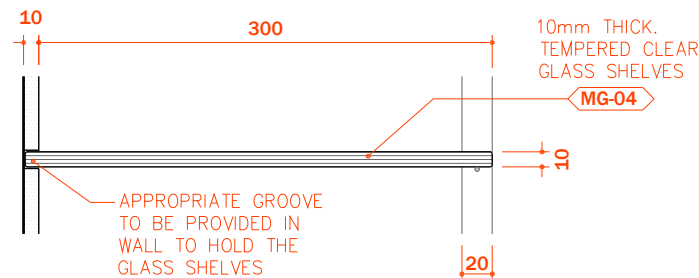


02 SPOT DETAIL
SCALE 1:5

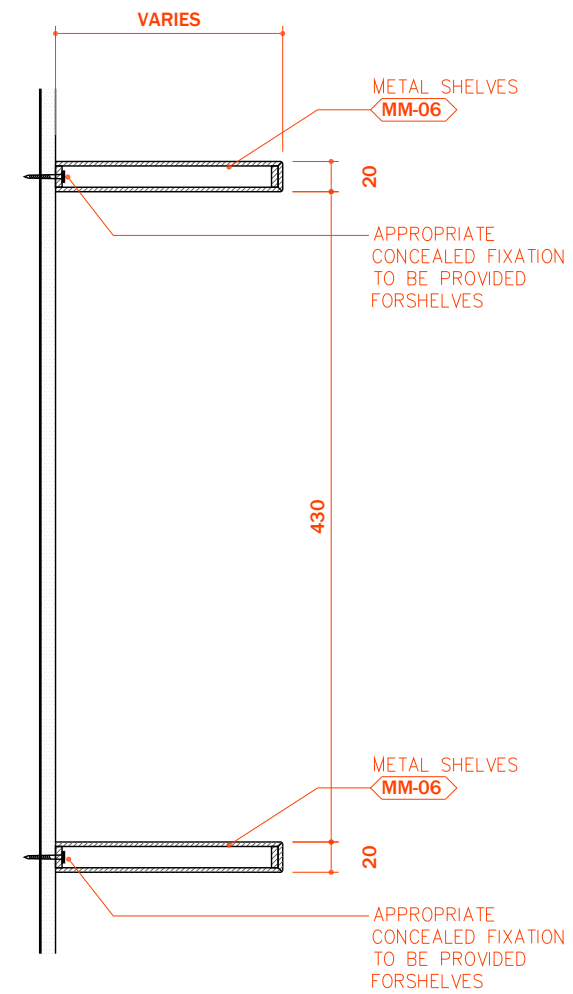


03 SPOT DETAIL
SCALE 1:5

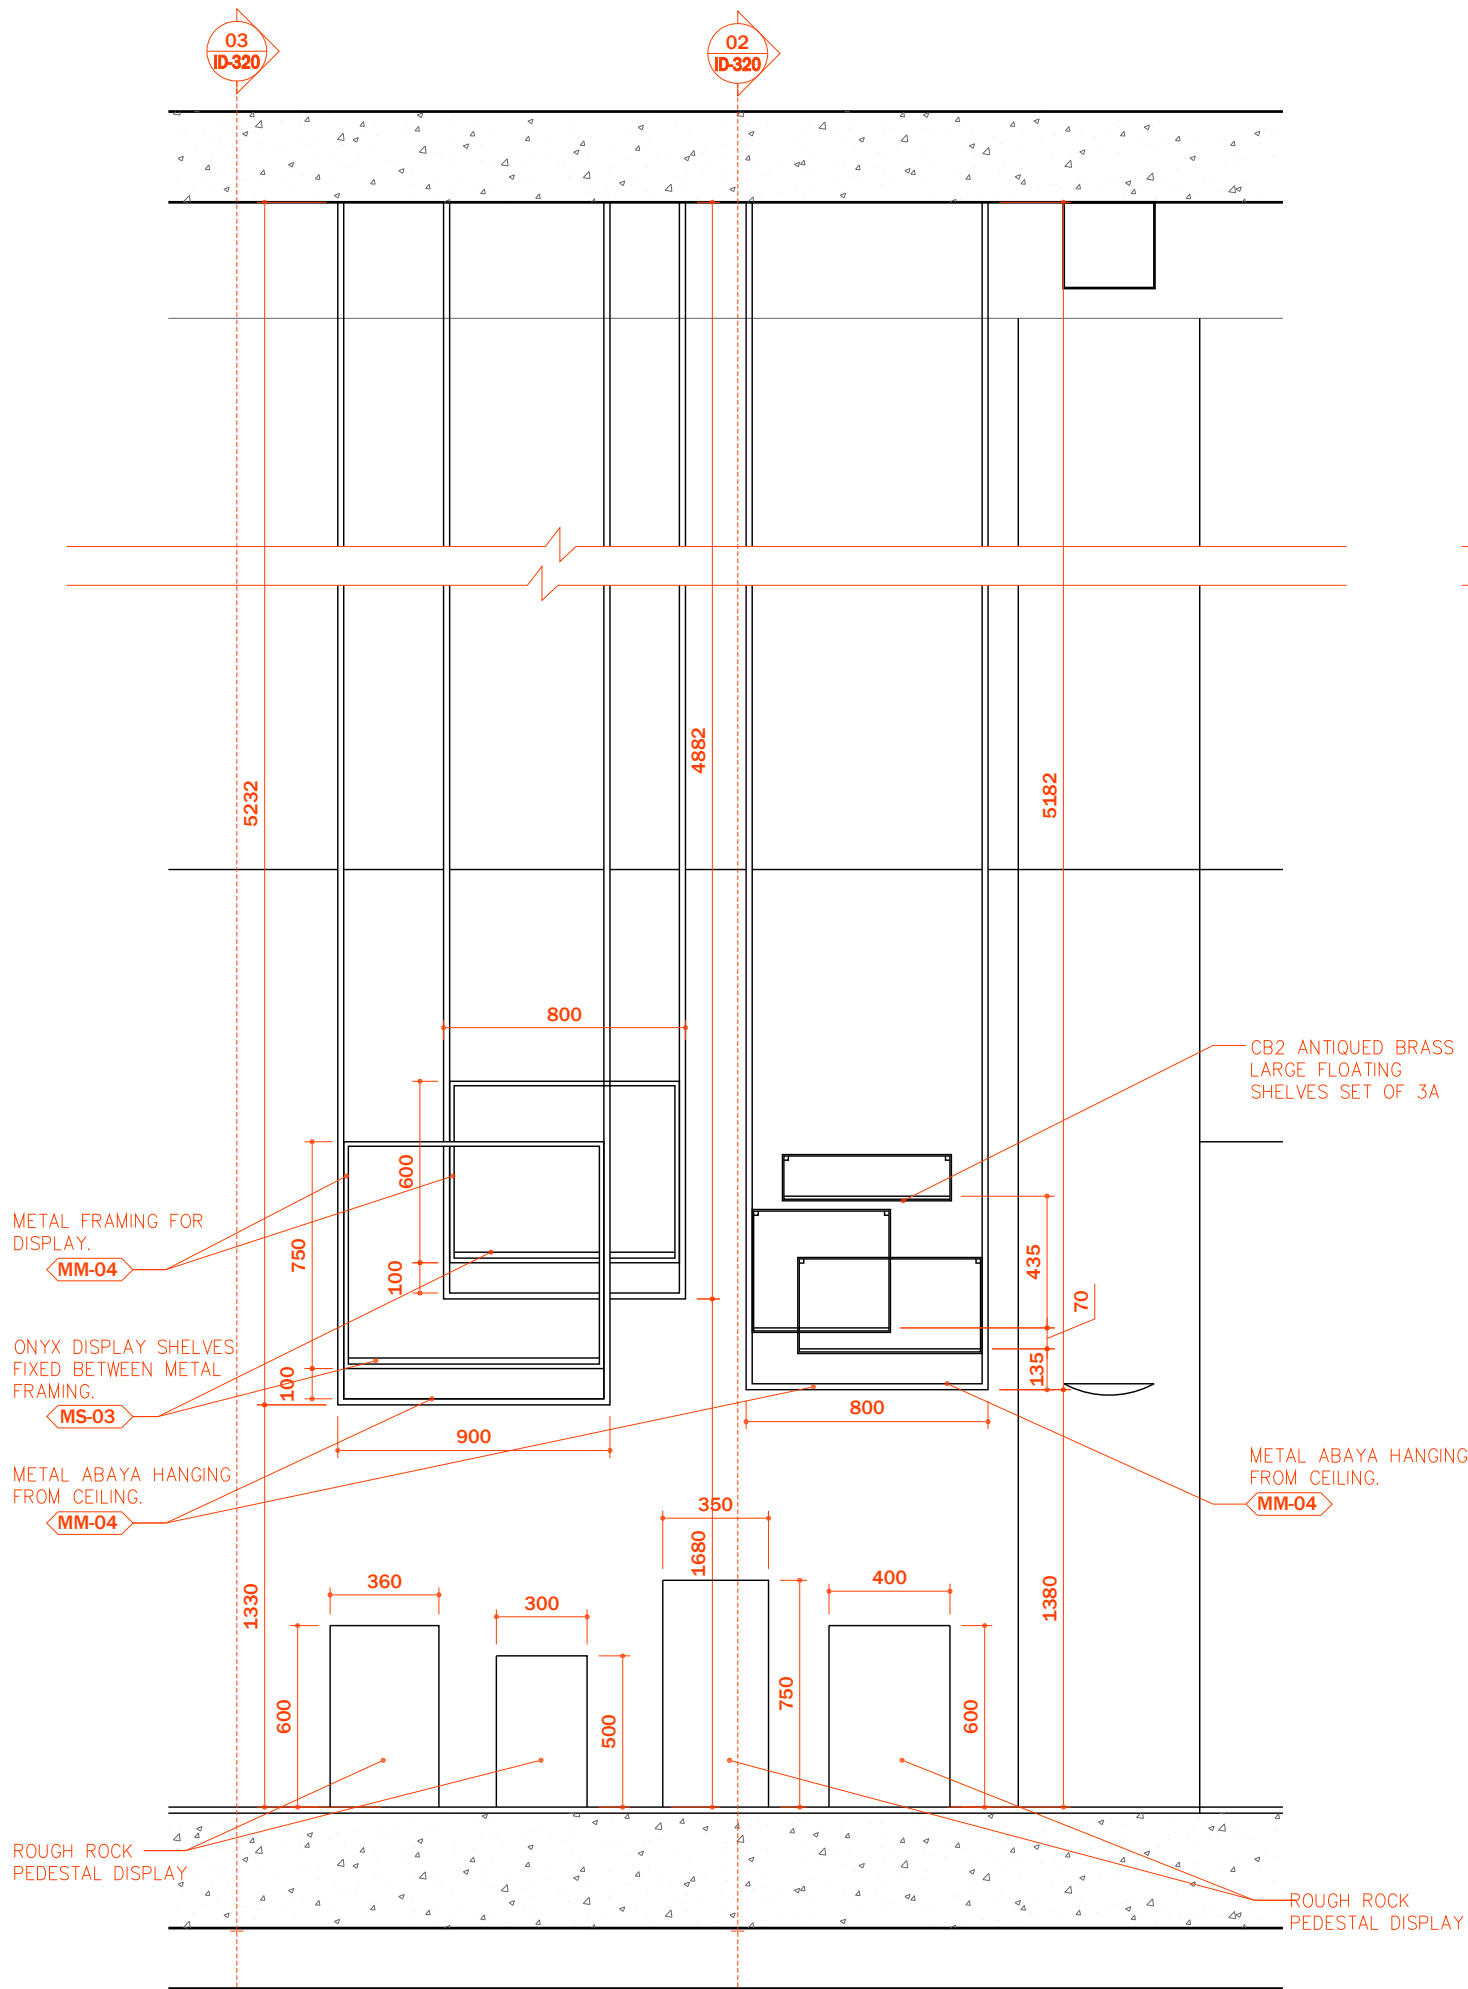


01 CEILING HUNGED DISPLAY + ABAYA HANGING ELEVATION
SCALE 1:25

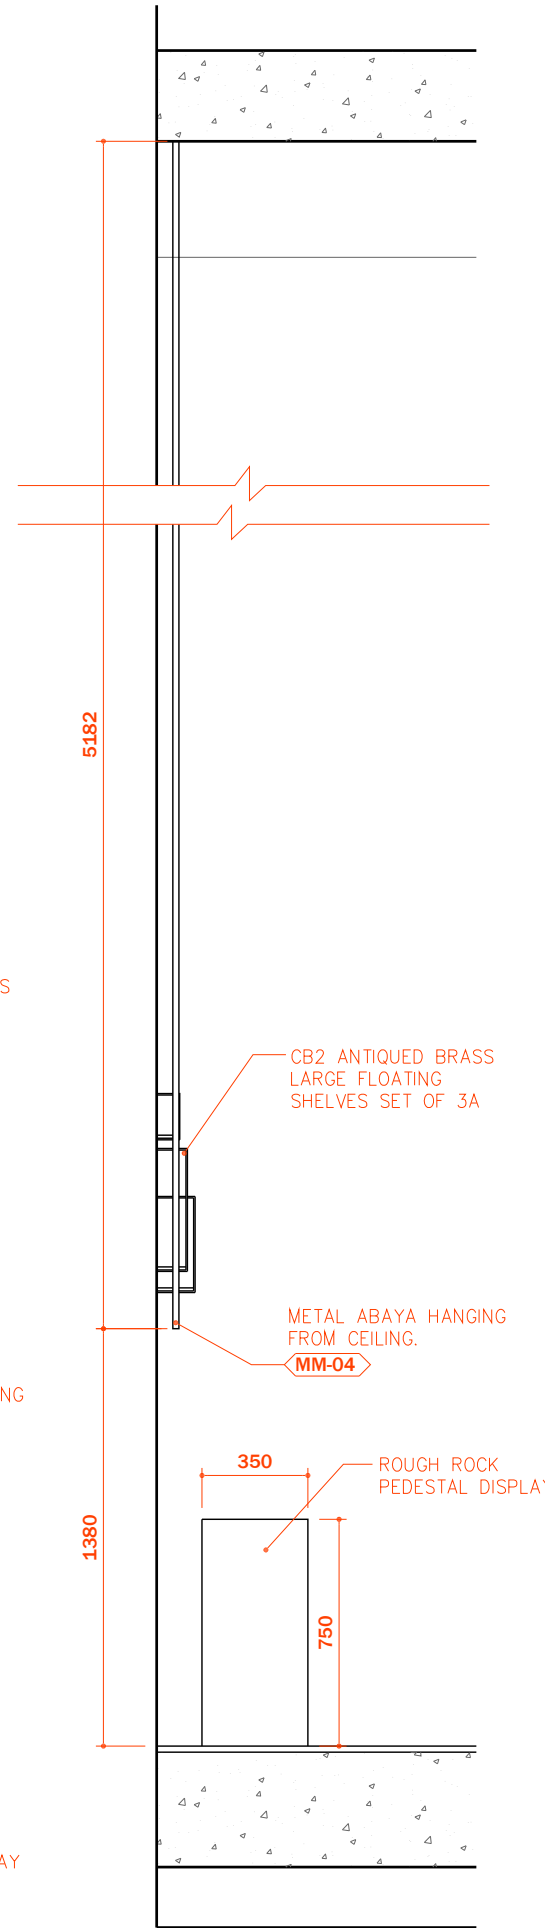

02 SECTION
SCALE 1:25

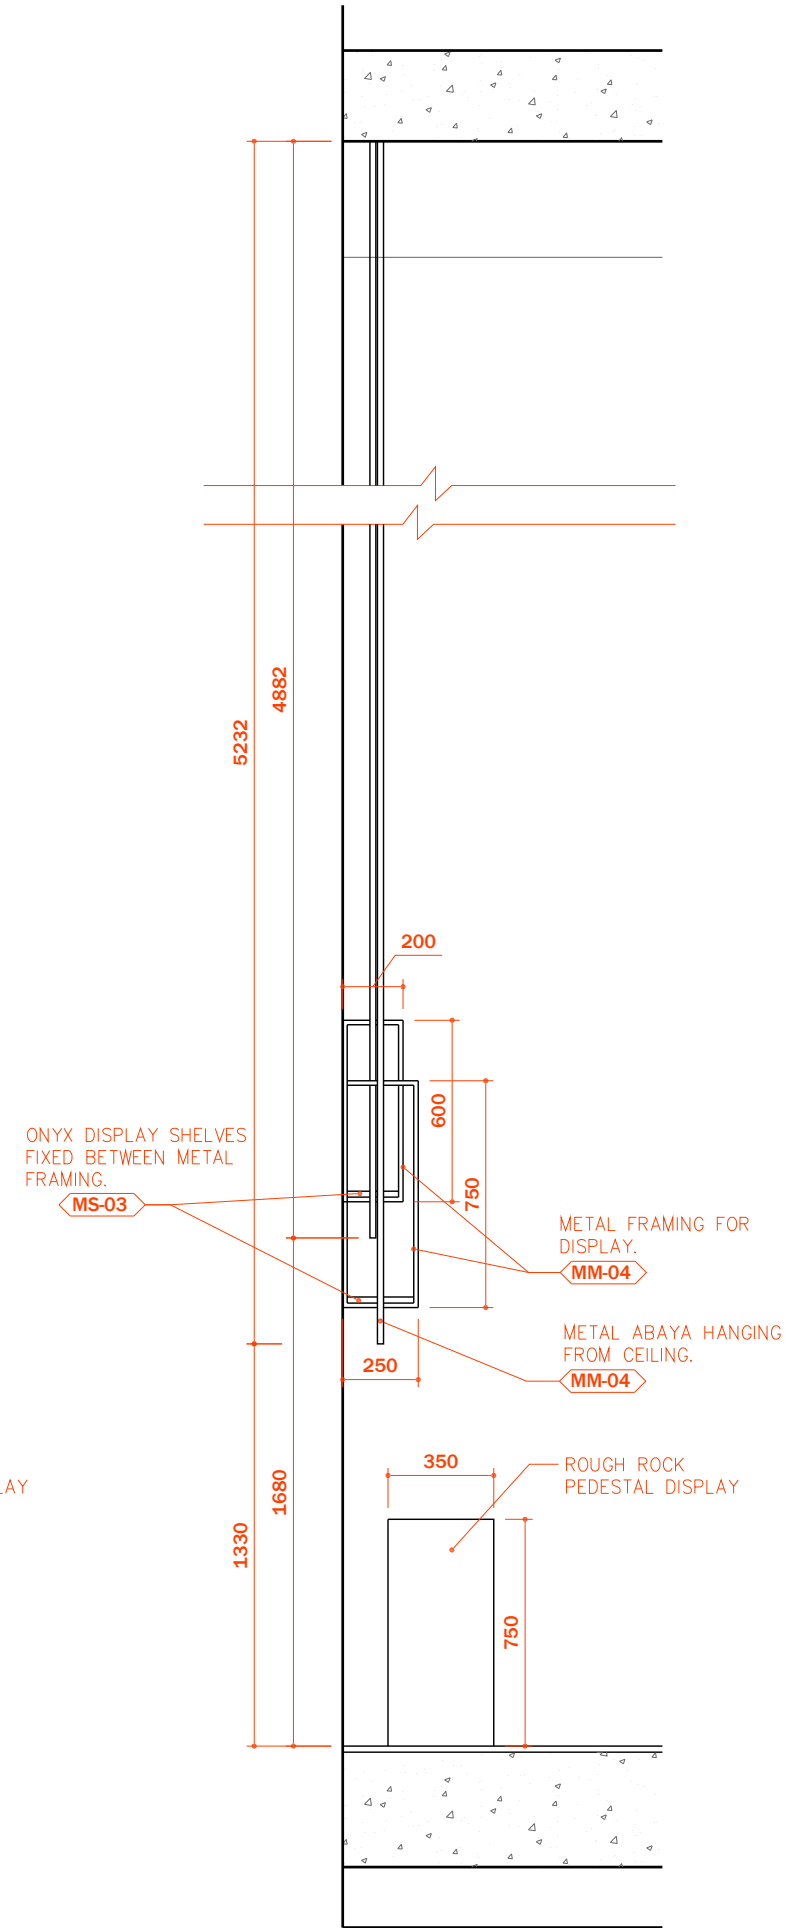


03 SECTION
SCALE 1:25

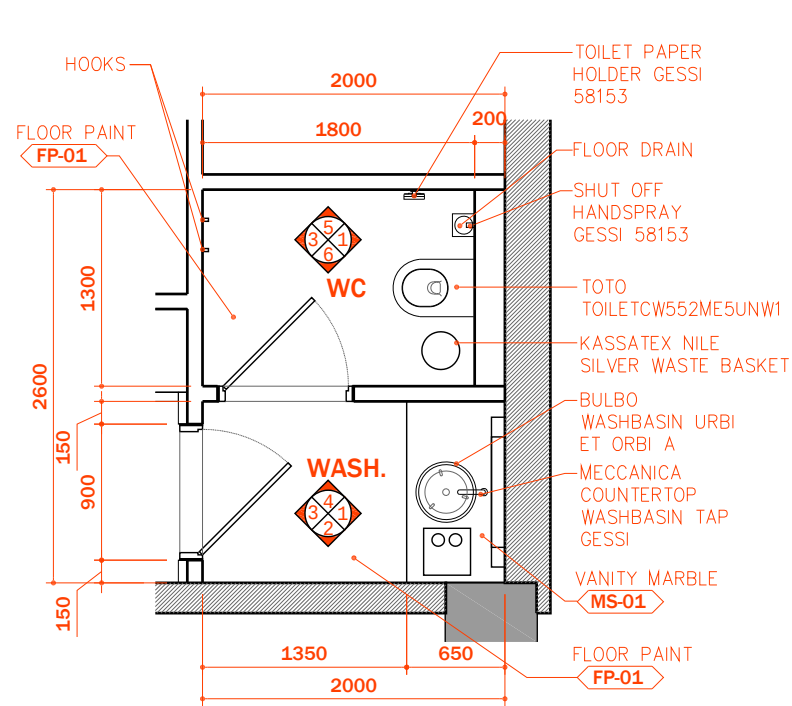


RESTROOM PLAN

SCALE 1:50

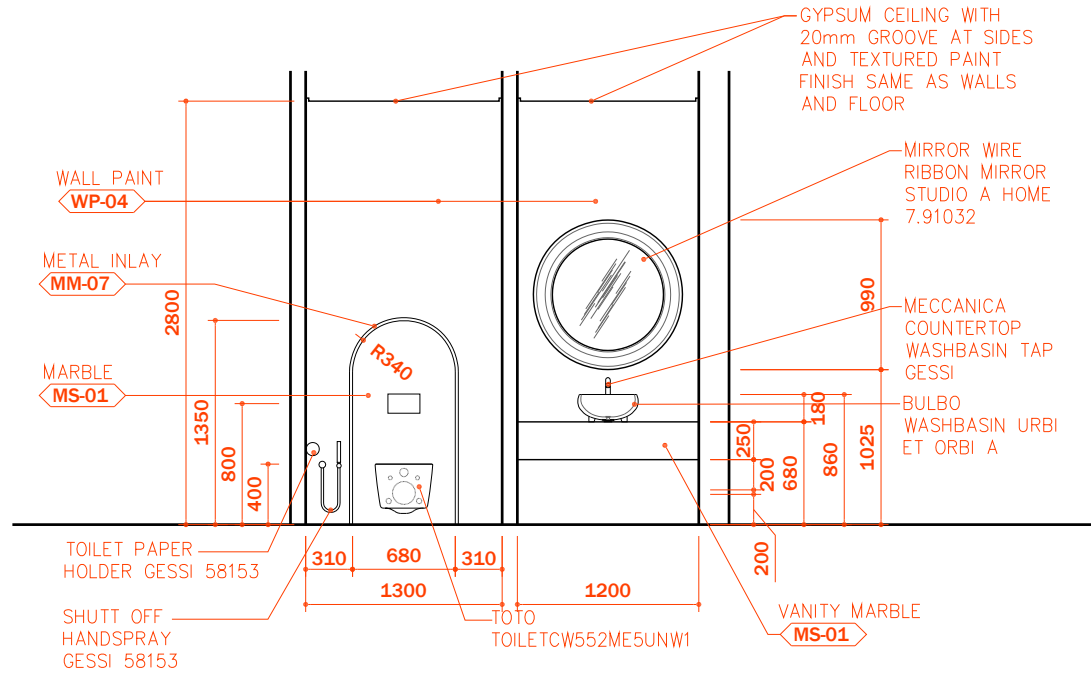


01 ELEVATION

SCALE 1:50

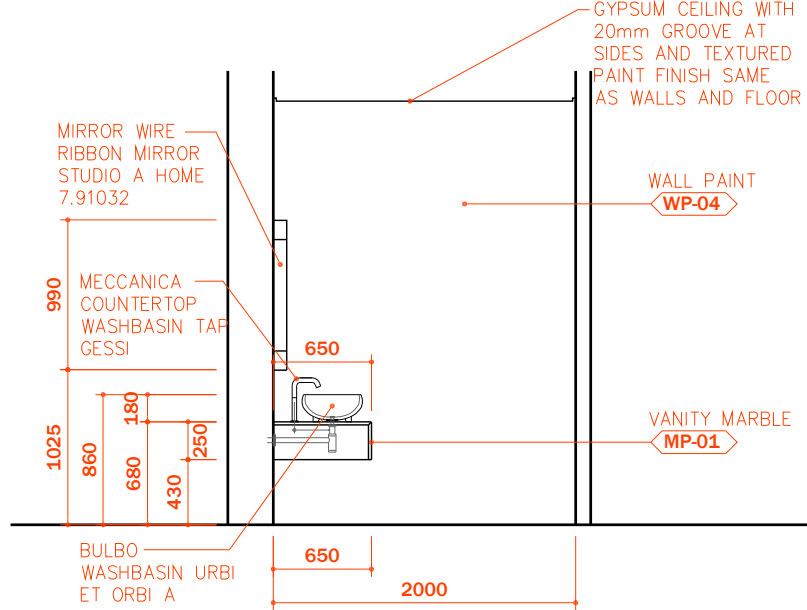


02 ELEVATION

SCALE 1:50

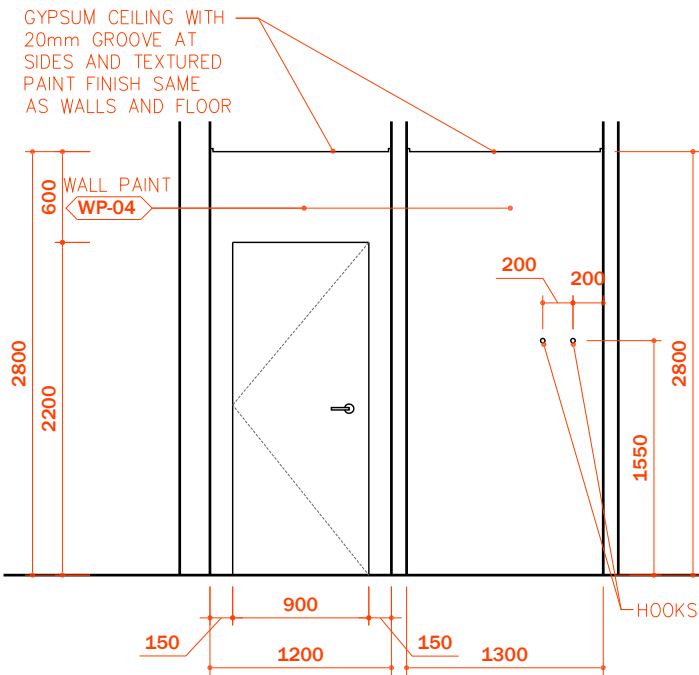


03 ELEVATION

SCALE 1:50

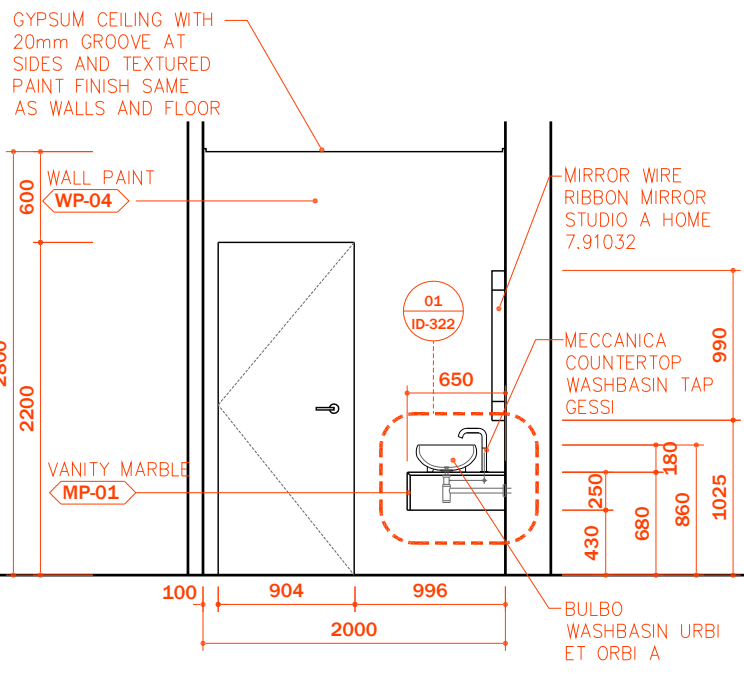


04 ELEVATION

SCALE 1:50

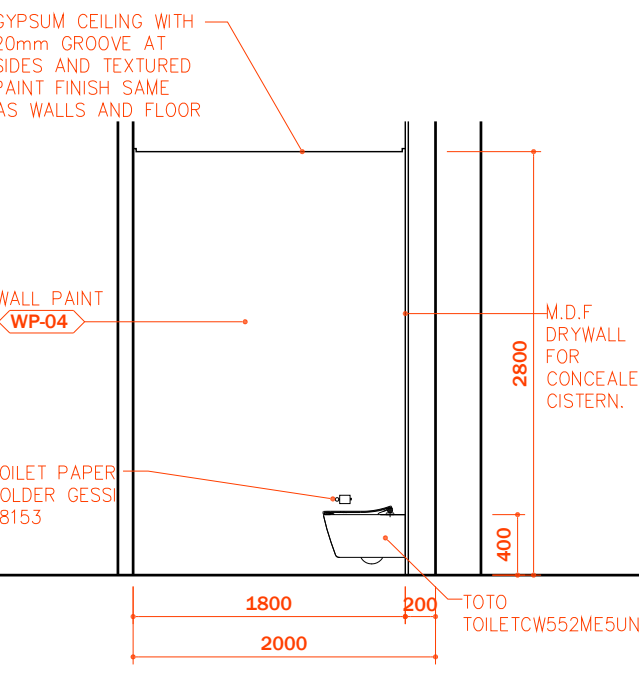


05 ELEVATION

SCALE 1:50





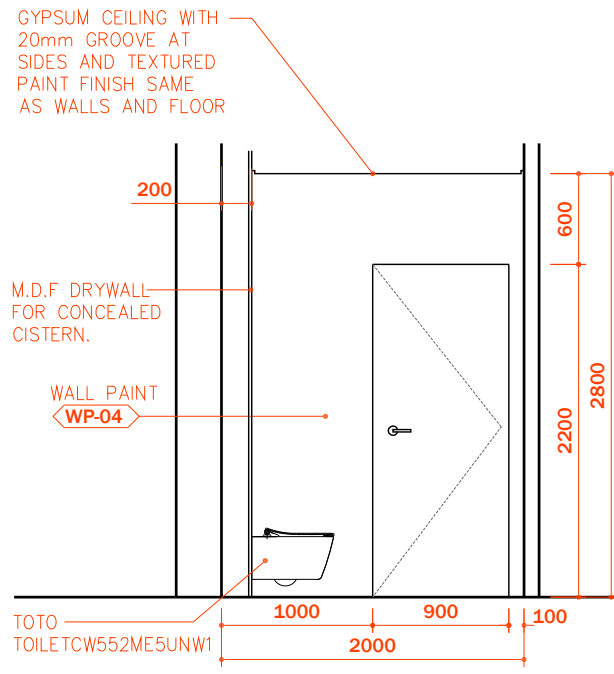





06 ELEVATION

SCALE 1:50

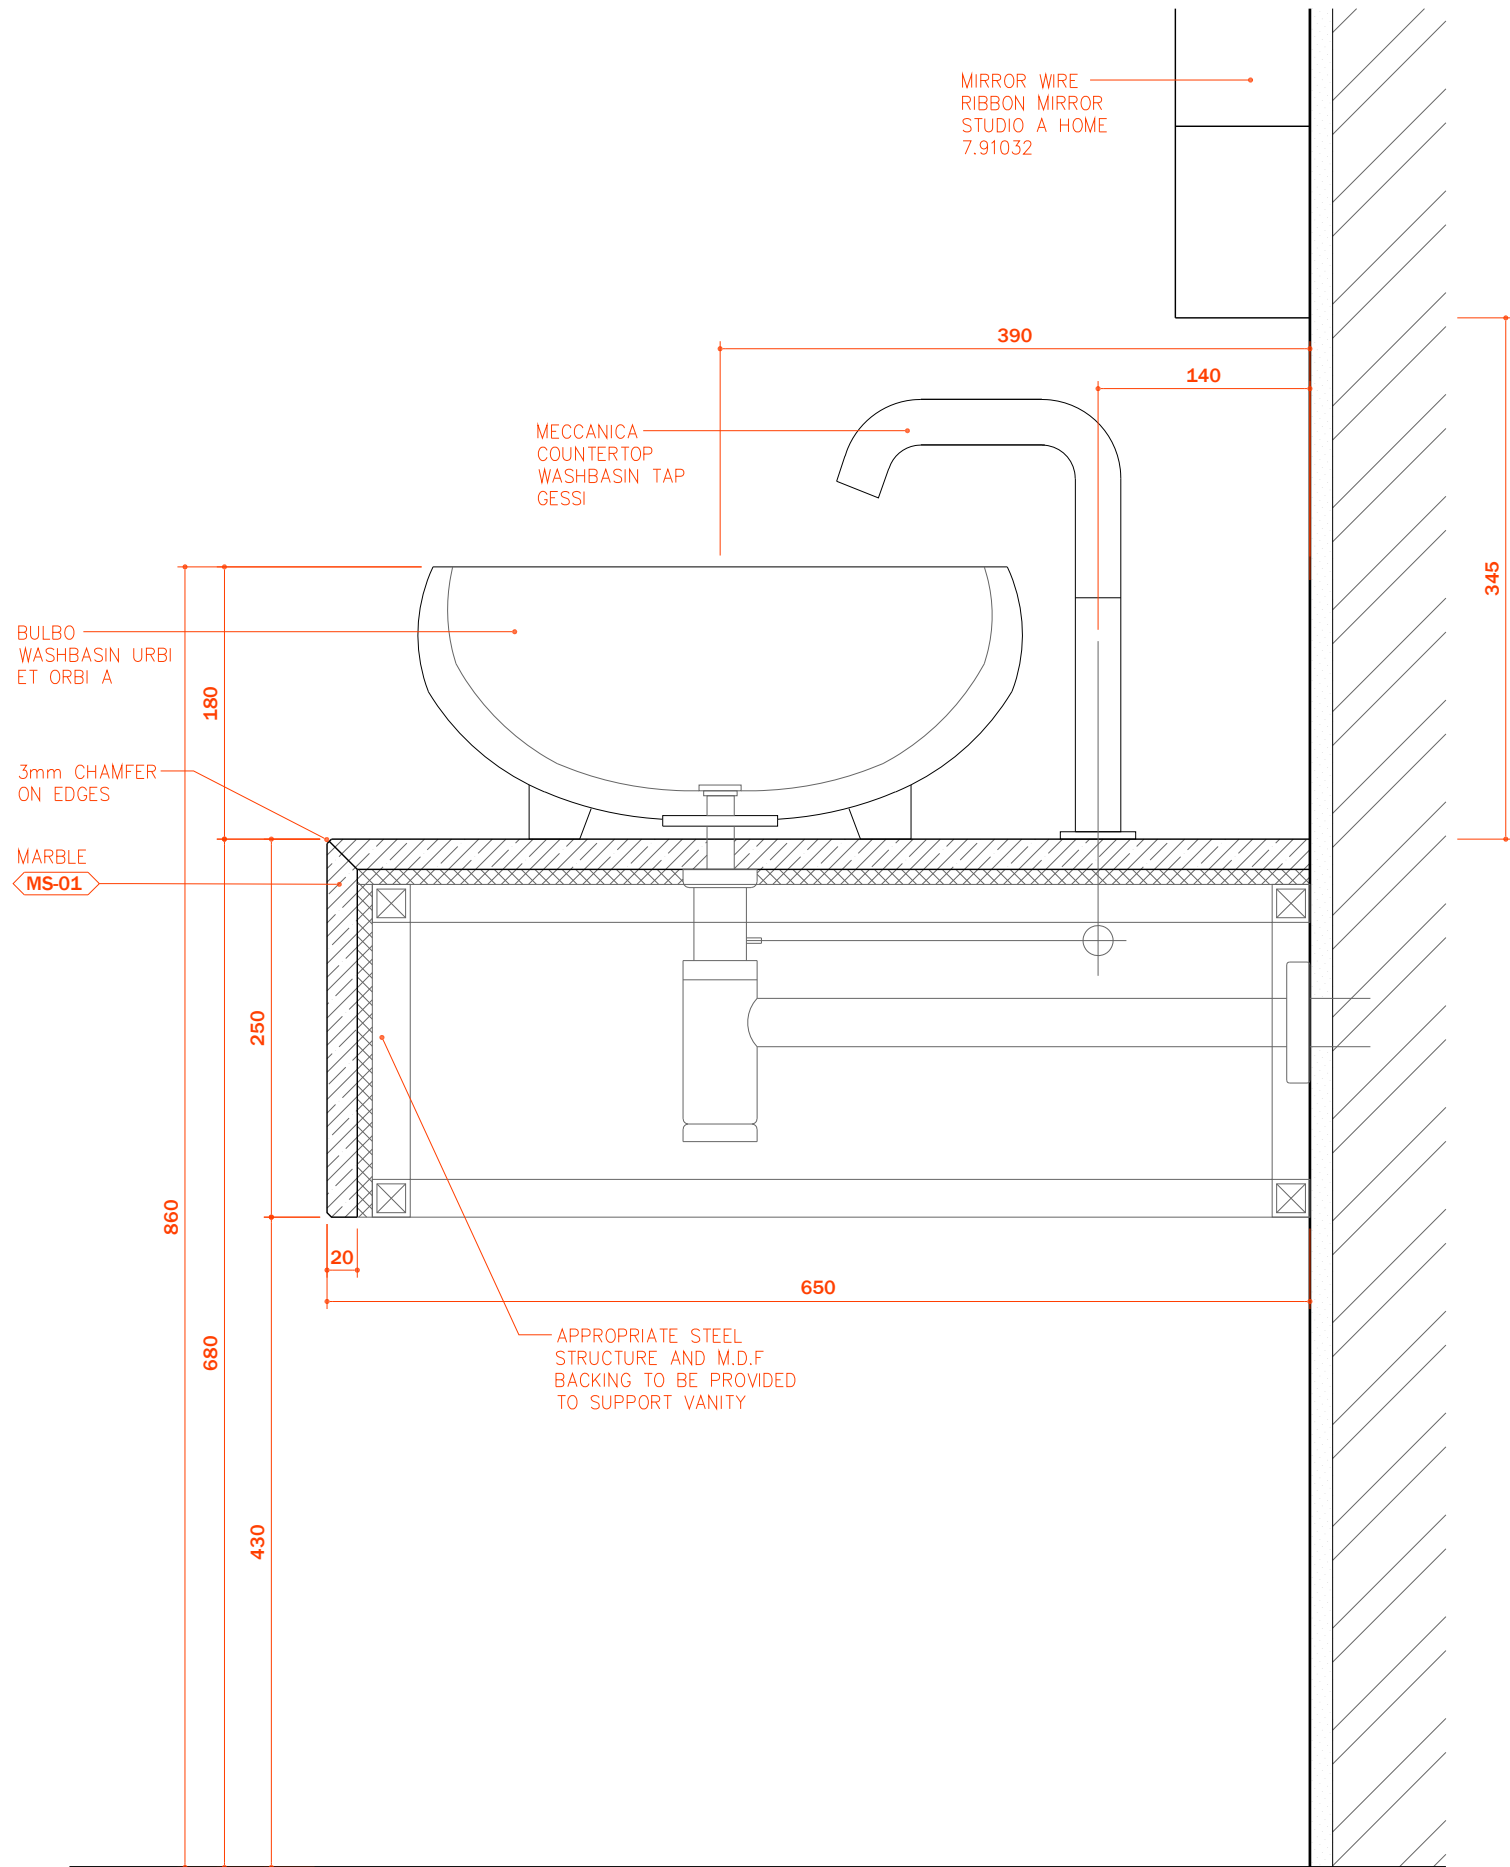

01 VANITY DETAIL
SCALE 1:5

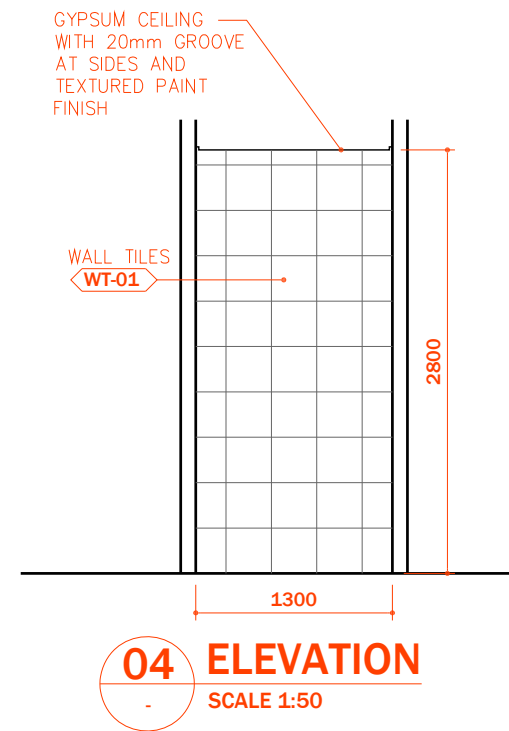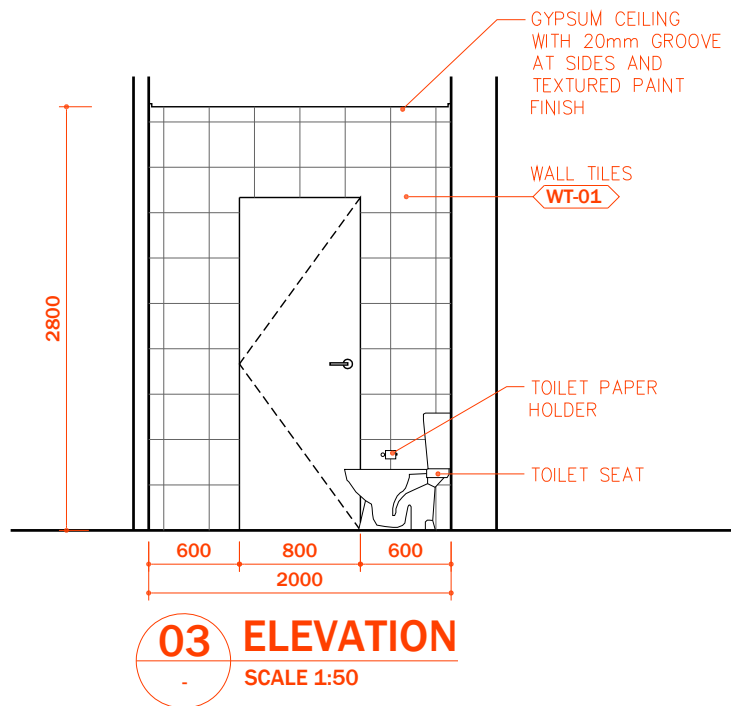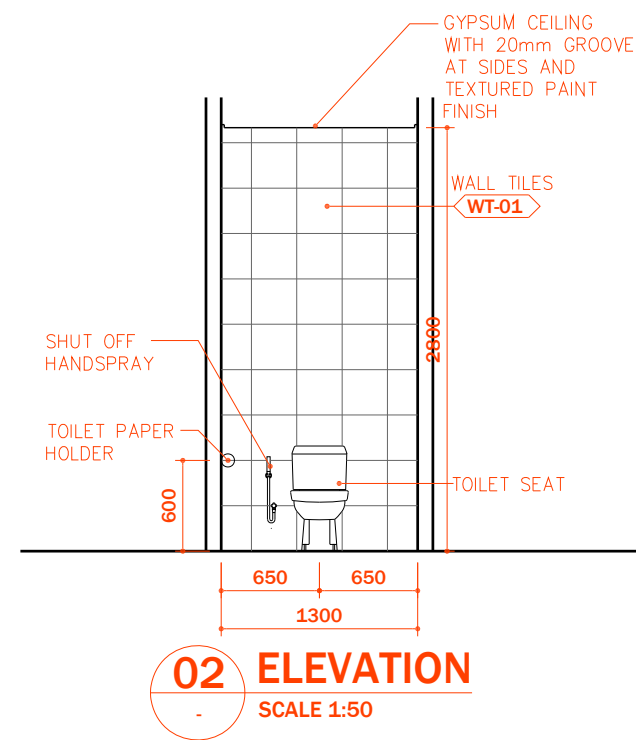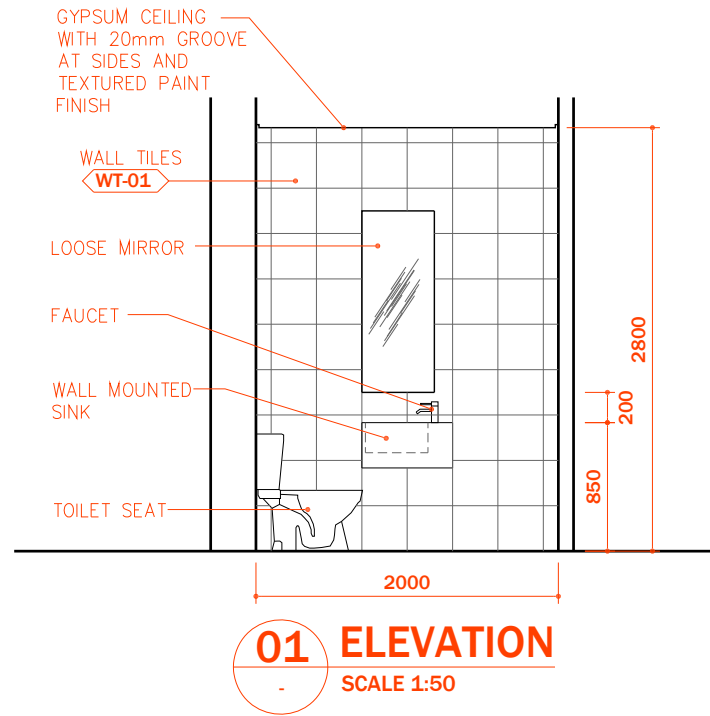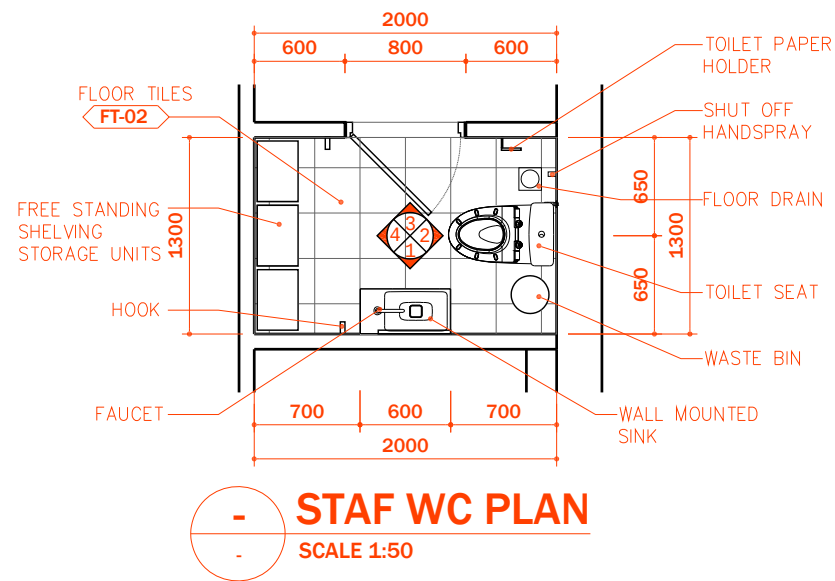

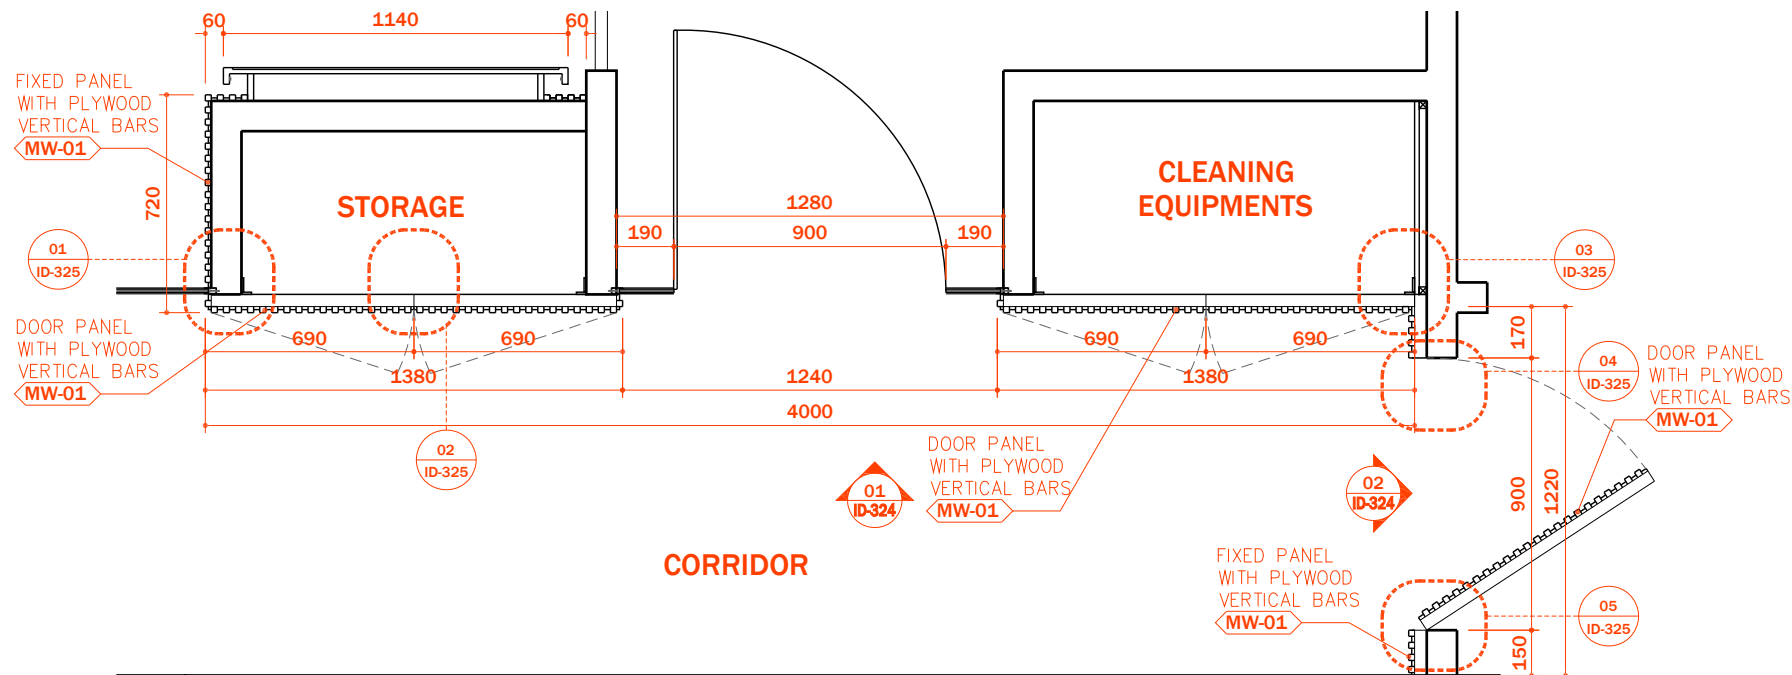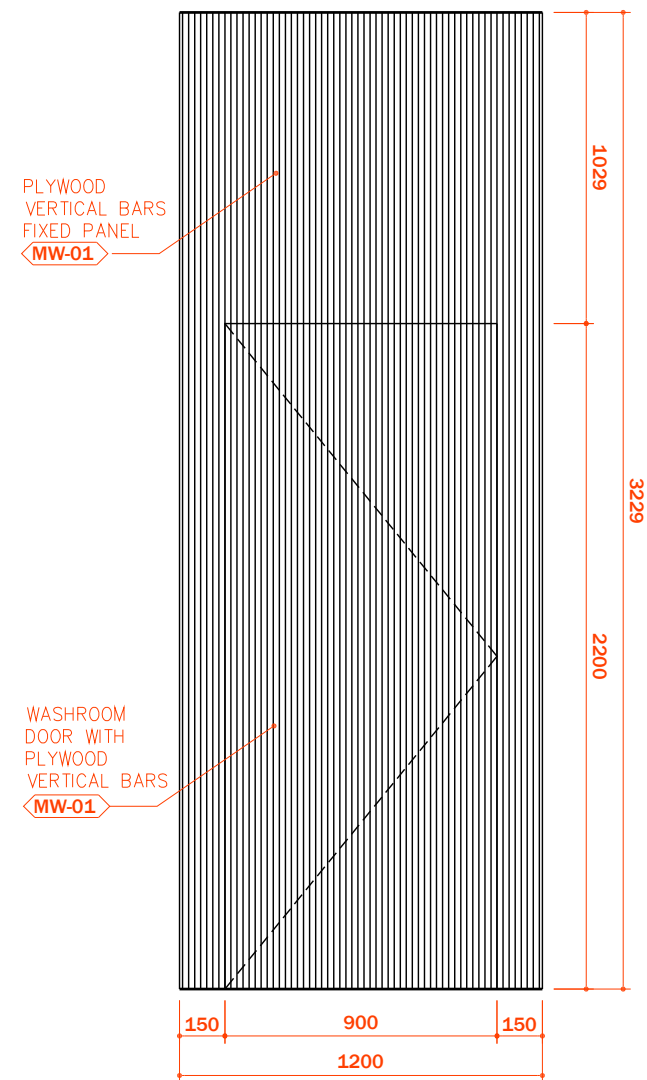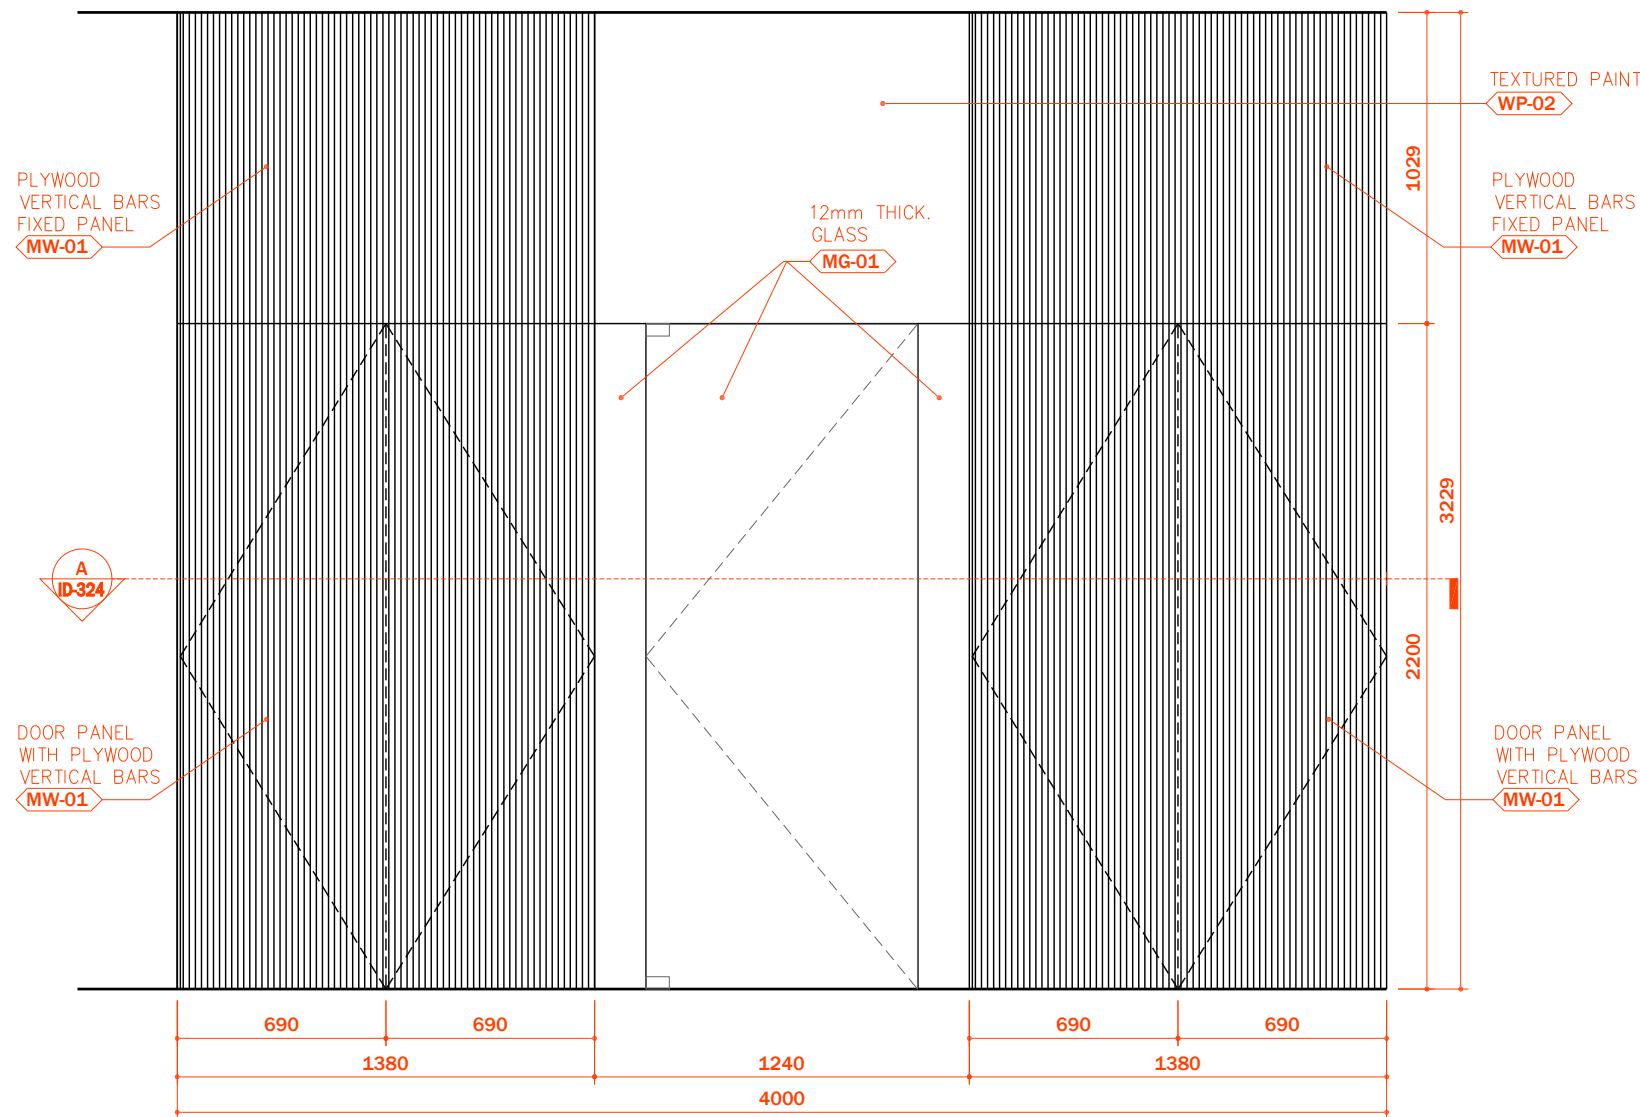

A CORRIDOR STORAGE AND WASHROOM DOOR PLAN
SCALE 1:25



the **PROJECT NAME**

# PROJECT NUMBER	01. 2021
------------------	----------

DATE ISSUED

28.09.2025

Revisions	Issue Date
-----------	------------

	REV DATE
---	----------

NOT FOR CONSTRUCTION

Notes

- 1.
- 2.
- 3.



PHASE

PROJECT PHASE

TRADE

INTERIOR DRAWING


Scale	1:5
-------	-----

CORRIDOR STORAGE AND WASHROOM DOOR PANELS DETAILS


ID-325

PRINT ON A3


© 2021

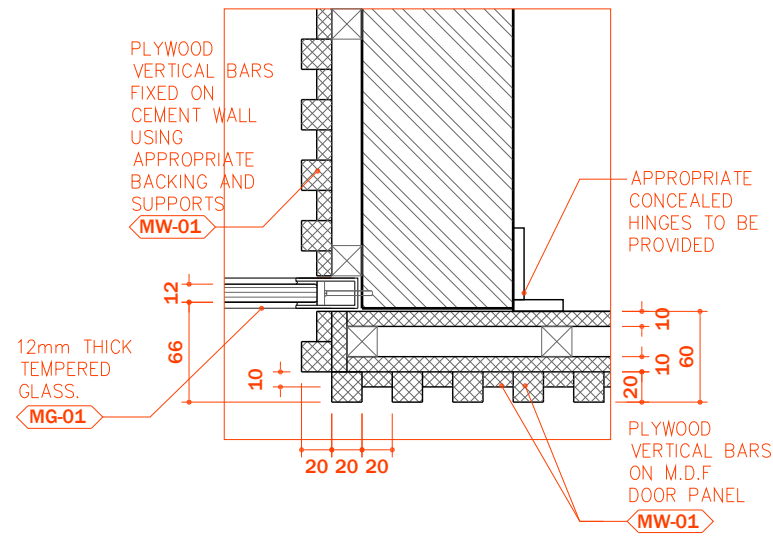


01 SPOT DETAIL
SCALE 1:5

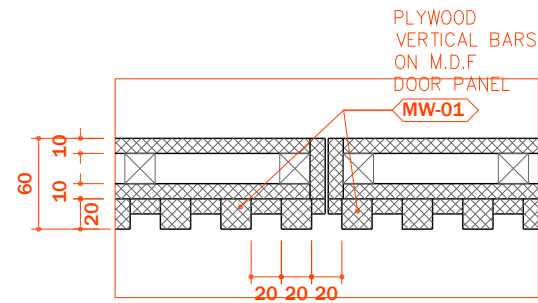


02 SPOT DETAIL

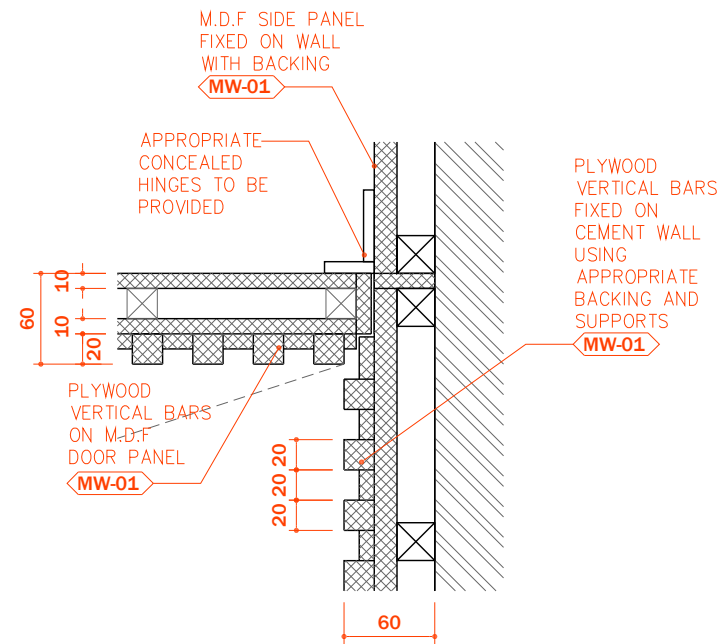

03 SPOT DETAIL
SCALE 1:5

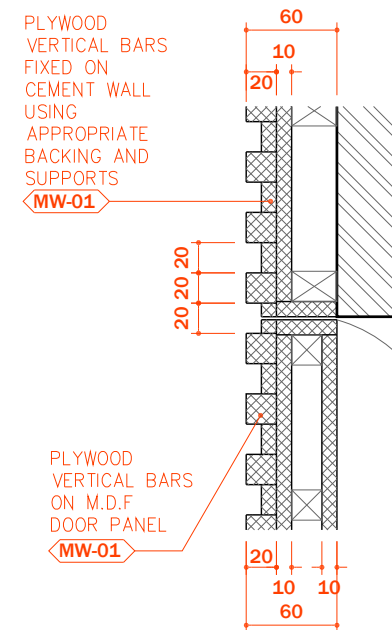

04 SPOT DETAIL
SCALE 1:5

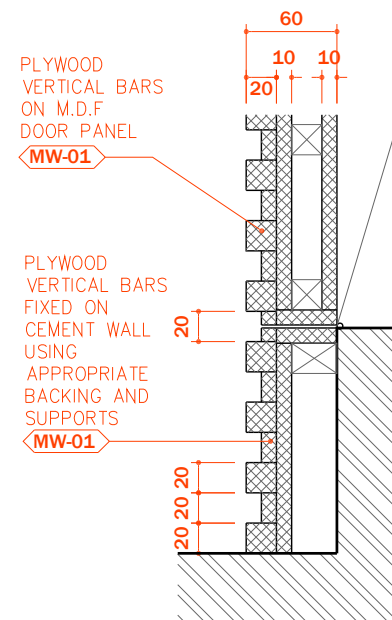

05 SPOT DETAIL
SCALE 1:5

the

01. 2021

28.09.2025

1 REV DATE

- 1.
- 2.
- 3.

NOT FOR CONSTRUCTION



PHASE
PROJECT PHASE
TRADE
INTERIOR DRAWING

1:25

CORRIDOR CABINET AND STAFF ROOM DOOR PANELS DETAILS

ID-326

© 2021




SCALE 1:25




SCALE 1:25




SCALE 1:25

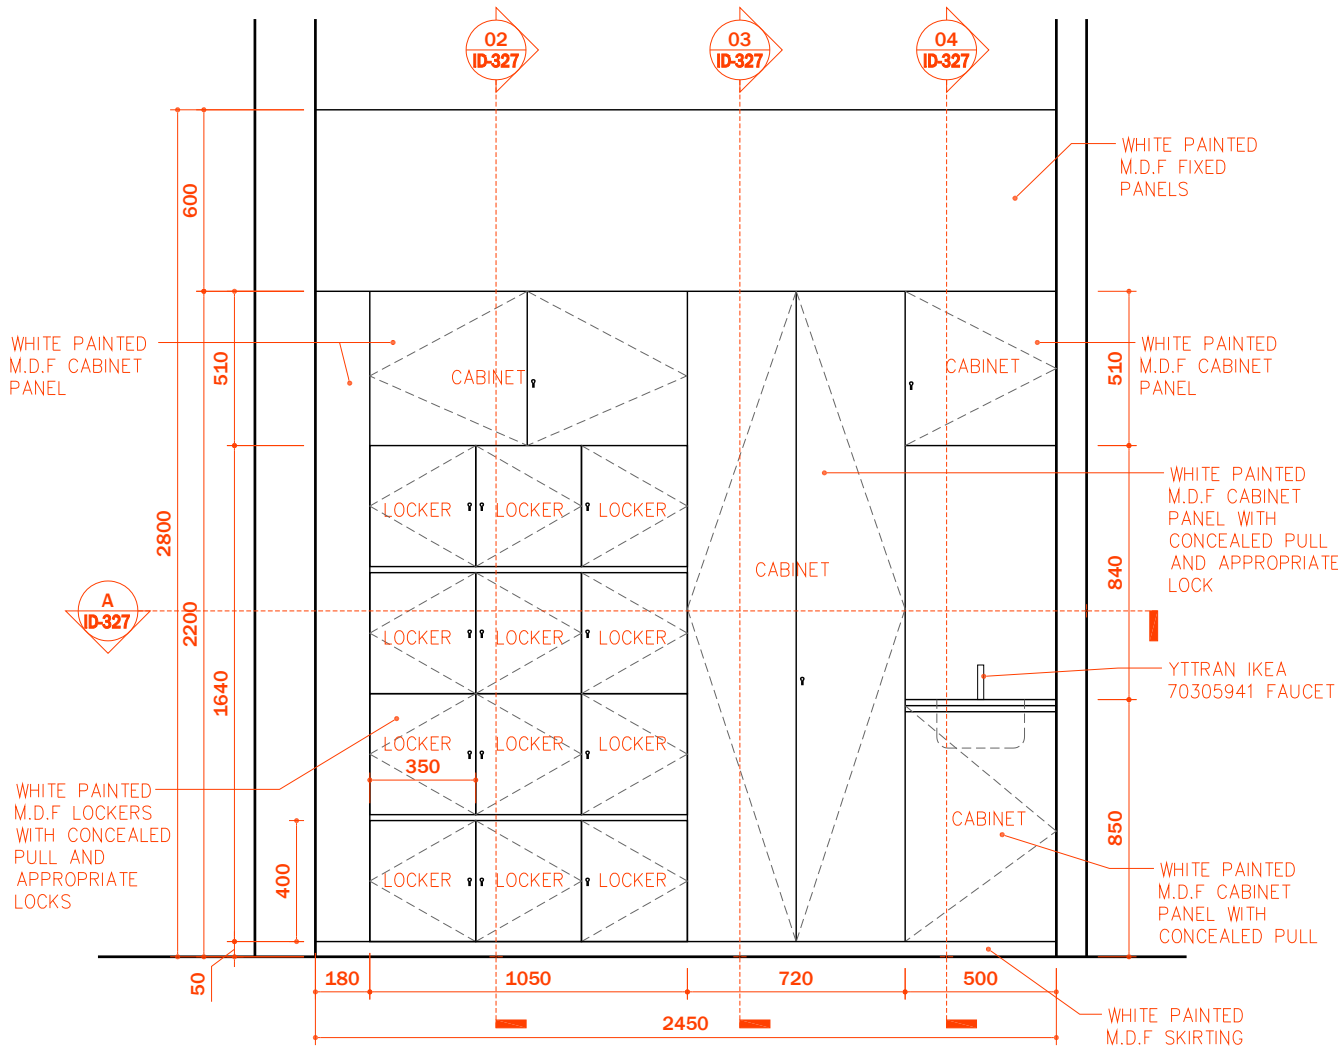


01 STAF ROOM BUILT-IN CABINET ELEVATION
SCALE 1:25

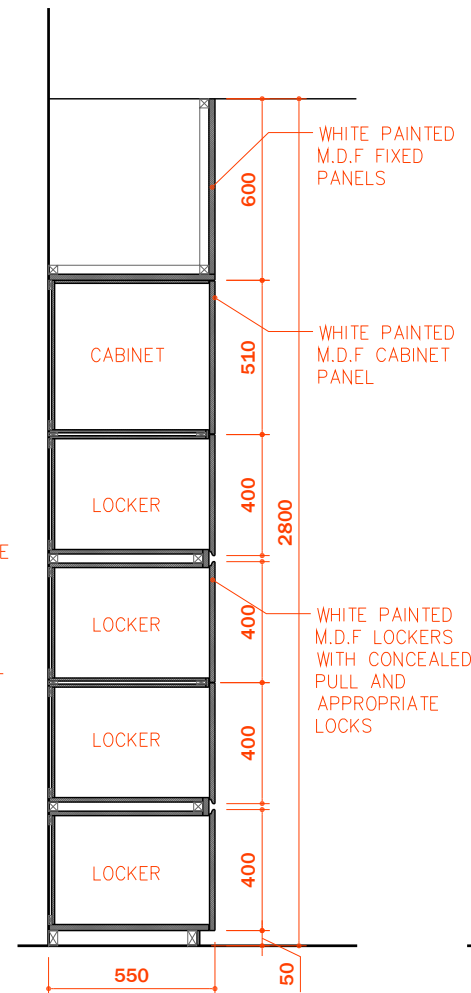


02 SECTION
SCALE 1:25

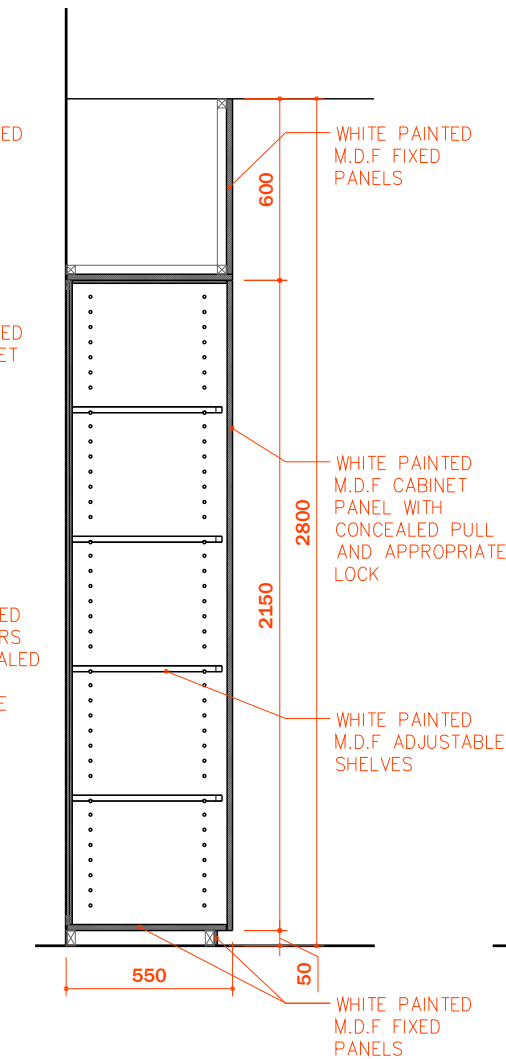


03 SECTION
SCALE 1:25

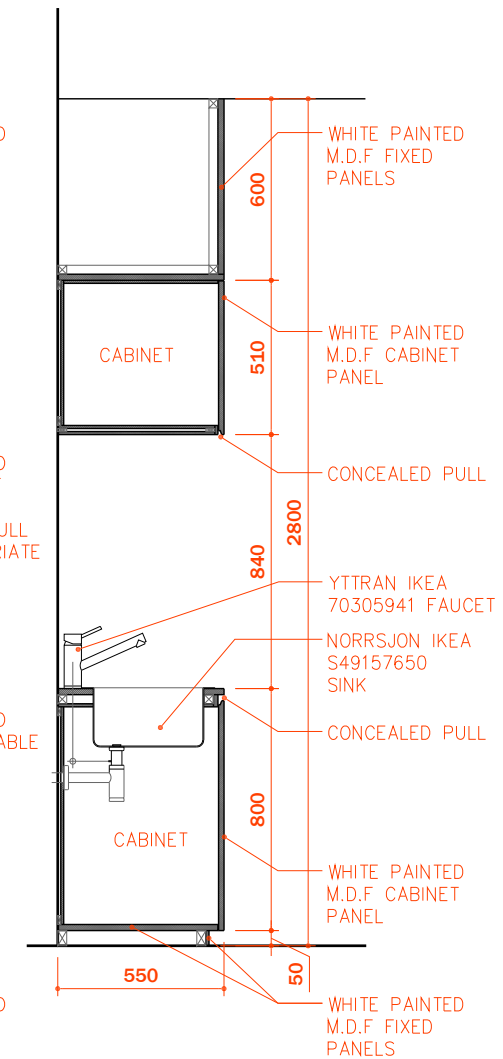

04 SECTION
SCALE 1:25

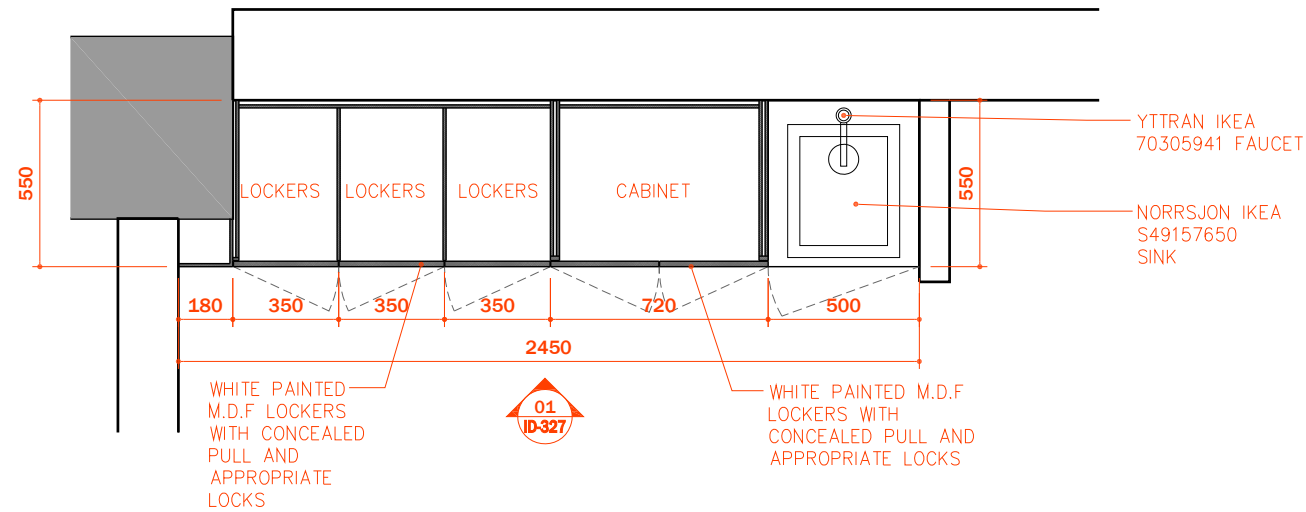


A STAF ROOM BUILT-IN CABINET PLAN
SCALE 1:25

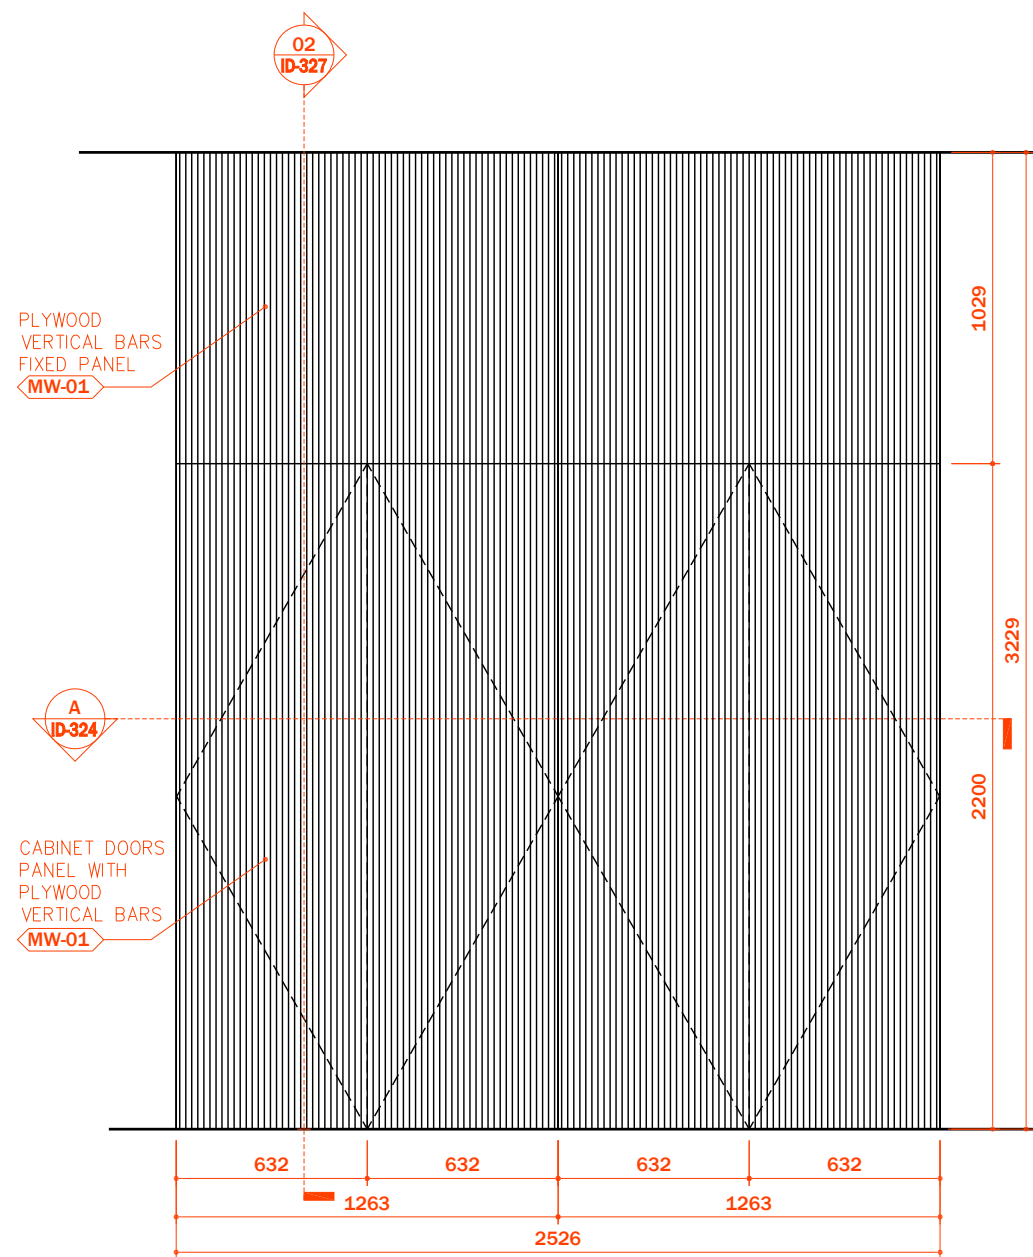


01 ELEVATION


SCALE 1:25

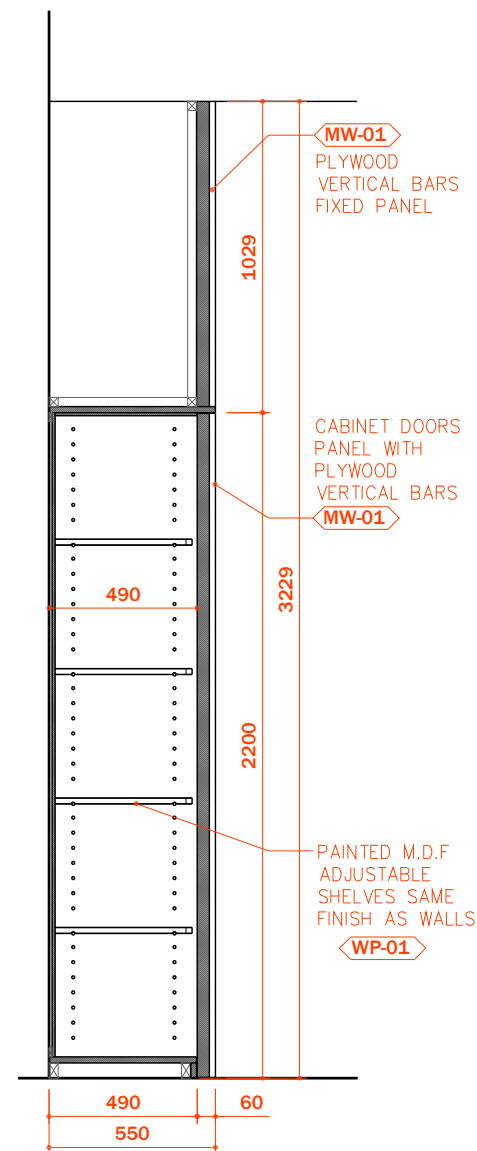


02 SECTION
- **SCALE 1:25**

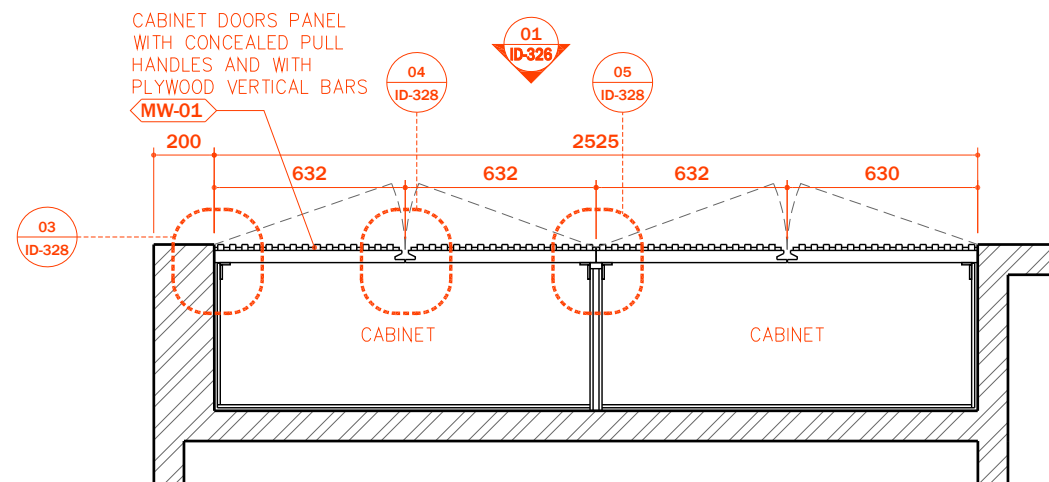


A CORRIDOR CABINET PLAN
SCALE 1:25

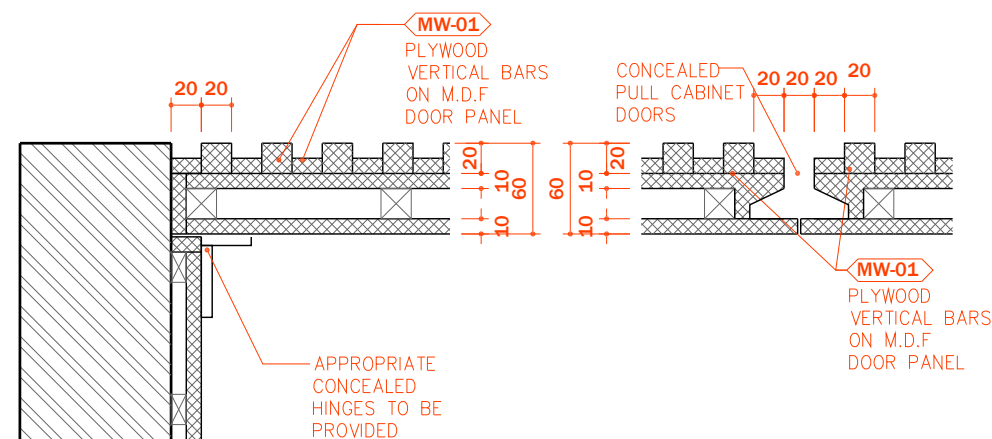

03 SPOT DETAIL
SCALE 1:5

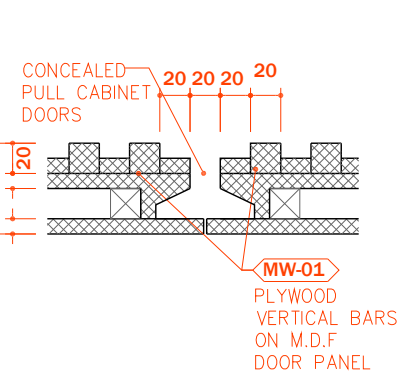

04 SPOT DETAIL
SCALE 1:5

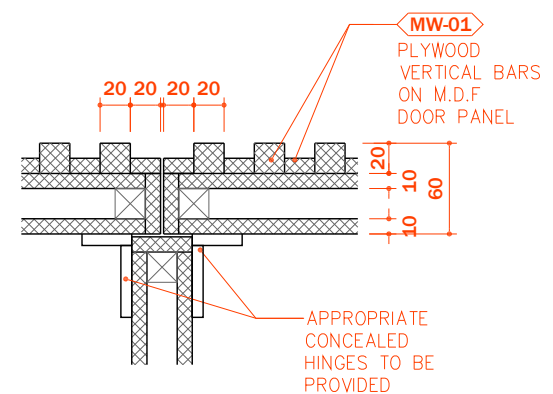

05 SPOT DETAIL
SCALE 1:5



the **PROJECT NAME**

# PROJECT NUMBER	01. 2021
------------------	----------

TE ISSUED

28.09.2025

Revisions	Issue Date
-----------	------------

1 REV DATE

Notes

- 1.
- 2.
- 3.

NOT FOR CONSTRUCTION



PHASE
PROJECT PHASE



TRADE
INTERIOR DRAWING

Scale	1:25 , 1:5
-------	------------

CORRIDOR CABINET DETAILS

ID-328

PRINT ON A3 © 2021

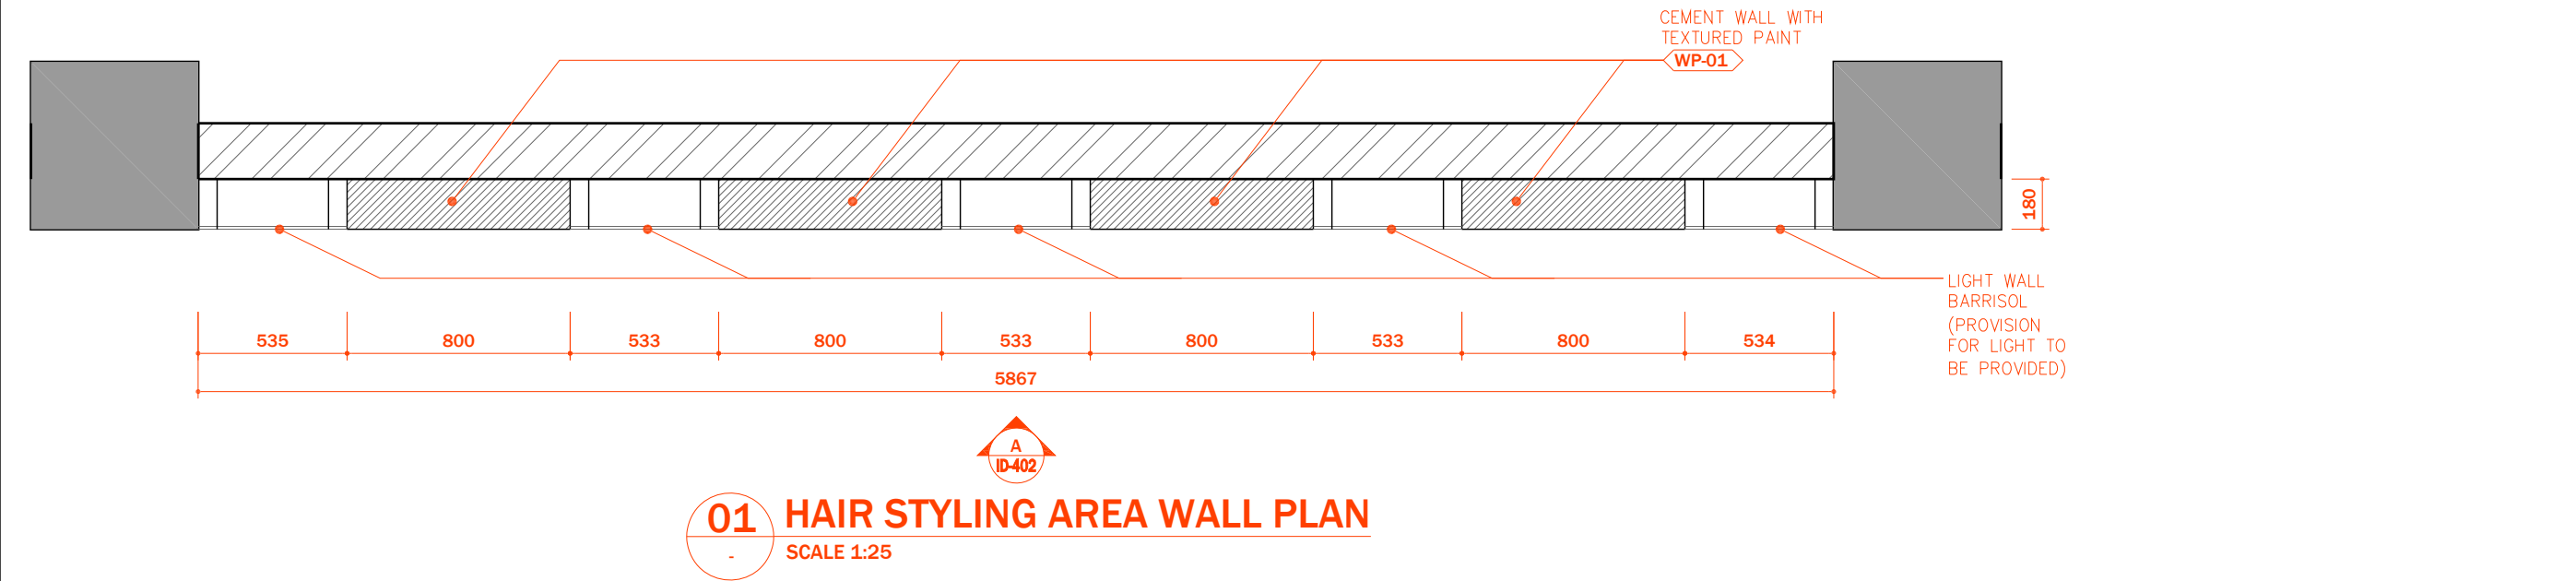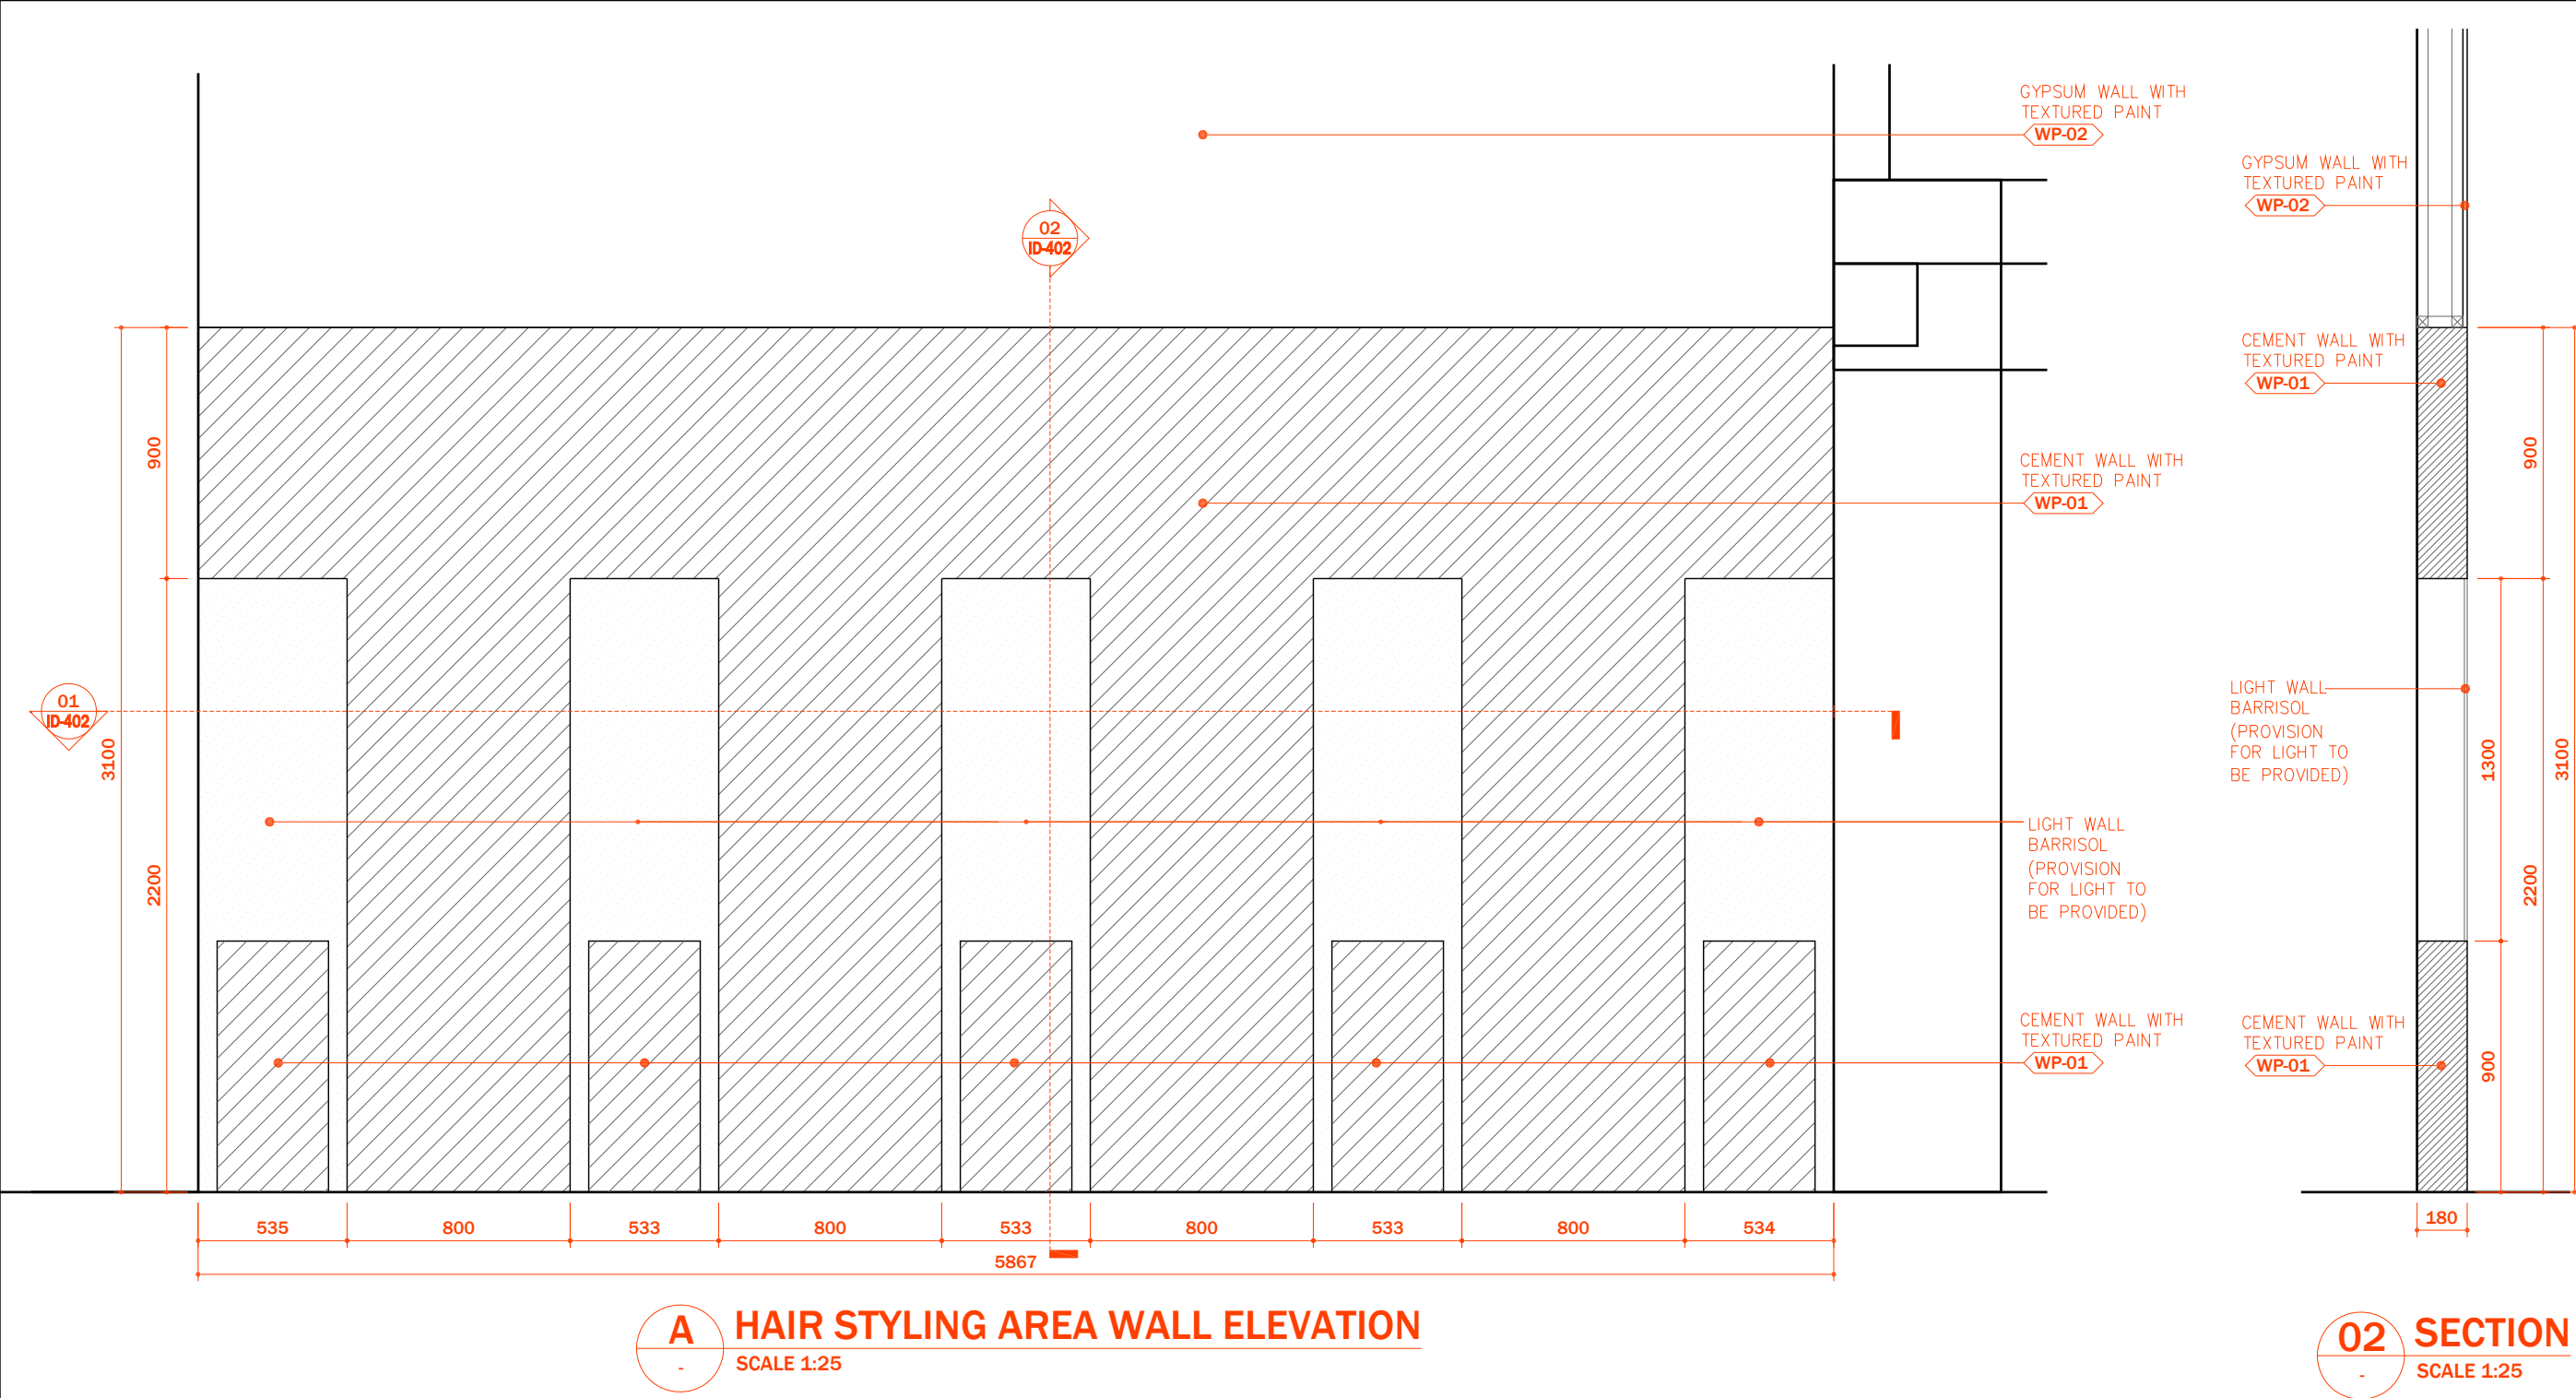

D01	D02	D03	D04	D05
ELEVATION Scale 1:25 PLAN Scale 1:25	ELEVATION Scale 1:25 PLAN Scale 1:25	ELEVATION Scale 1:25 PLAN Scale 1:25	ELEVATION Scale 1:25 PLAN Scale 1:25	ELEVATION Scale 1:25 PLAN Scale 1:25
DESCRIPTION : SINGLE HINGED METAL AND TEXTURED GLASS DOOR.	DESCRIPTION : SINGLE HINGED WOODEN DOOR WITH PLYWOOD BARS FIXED VERTICALLY ON M.D.F.	DESCRIPTION : SINGLE HINGED WOODEN DOOR WITH PLYWOOD BARS FIXED VERTICALLY ON M.D.F.	DESCRIPTION : SINGLE HINGED WOODEN DOOR WITHOUT ARCHITRAVE SPECIAL CONCEALED HINGES TO BE FIXED DIRECTLY ON WALL.	DESCRIPTION : SINGLE HINGED GLASS DOORS WITH APPROPRIATE HINGES AND DOOR HANDLES IN CHROME FINISH
QUANTITY : 01	QUANTITY : 01	QUANTITY : 01	QUANTITY : 02	QUANTITY : 02

PROJECT NAME

the

PROJECT NUMBER

01. 2021

DATE ISSUED

28.09.2025

Revisions

Issue Date

REV DATE

NOT FOR CONSTRUCTION

Notes

1.

2.

3.

Project North

PHASE

PROJECT PHASE

TRADE

INTERIOR DRAWING

Scale

1:25

DOORS SCHEDULE

ID-403

PRINT ON A3

© 2021

NOT FOR CONSTRUCTION

Notes
1.
2.
3.




PHASE
PROJECT PHASE
TRADE
INTERIOR DRAWING


Scale 1:75


GROUND FLOOR
ELECTRICAL
LIGHTING LAYOUT


E-201

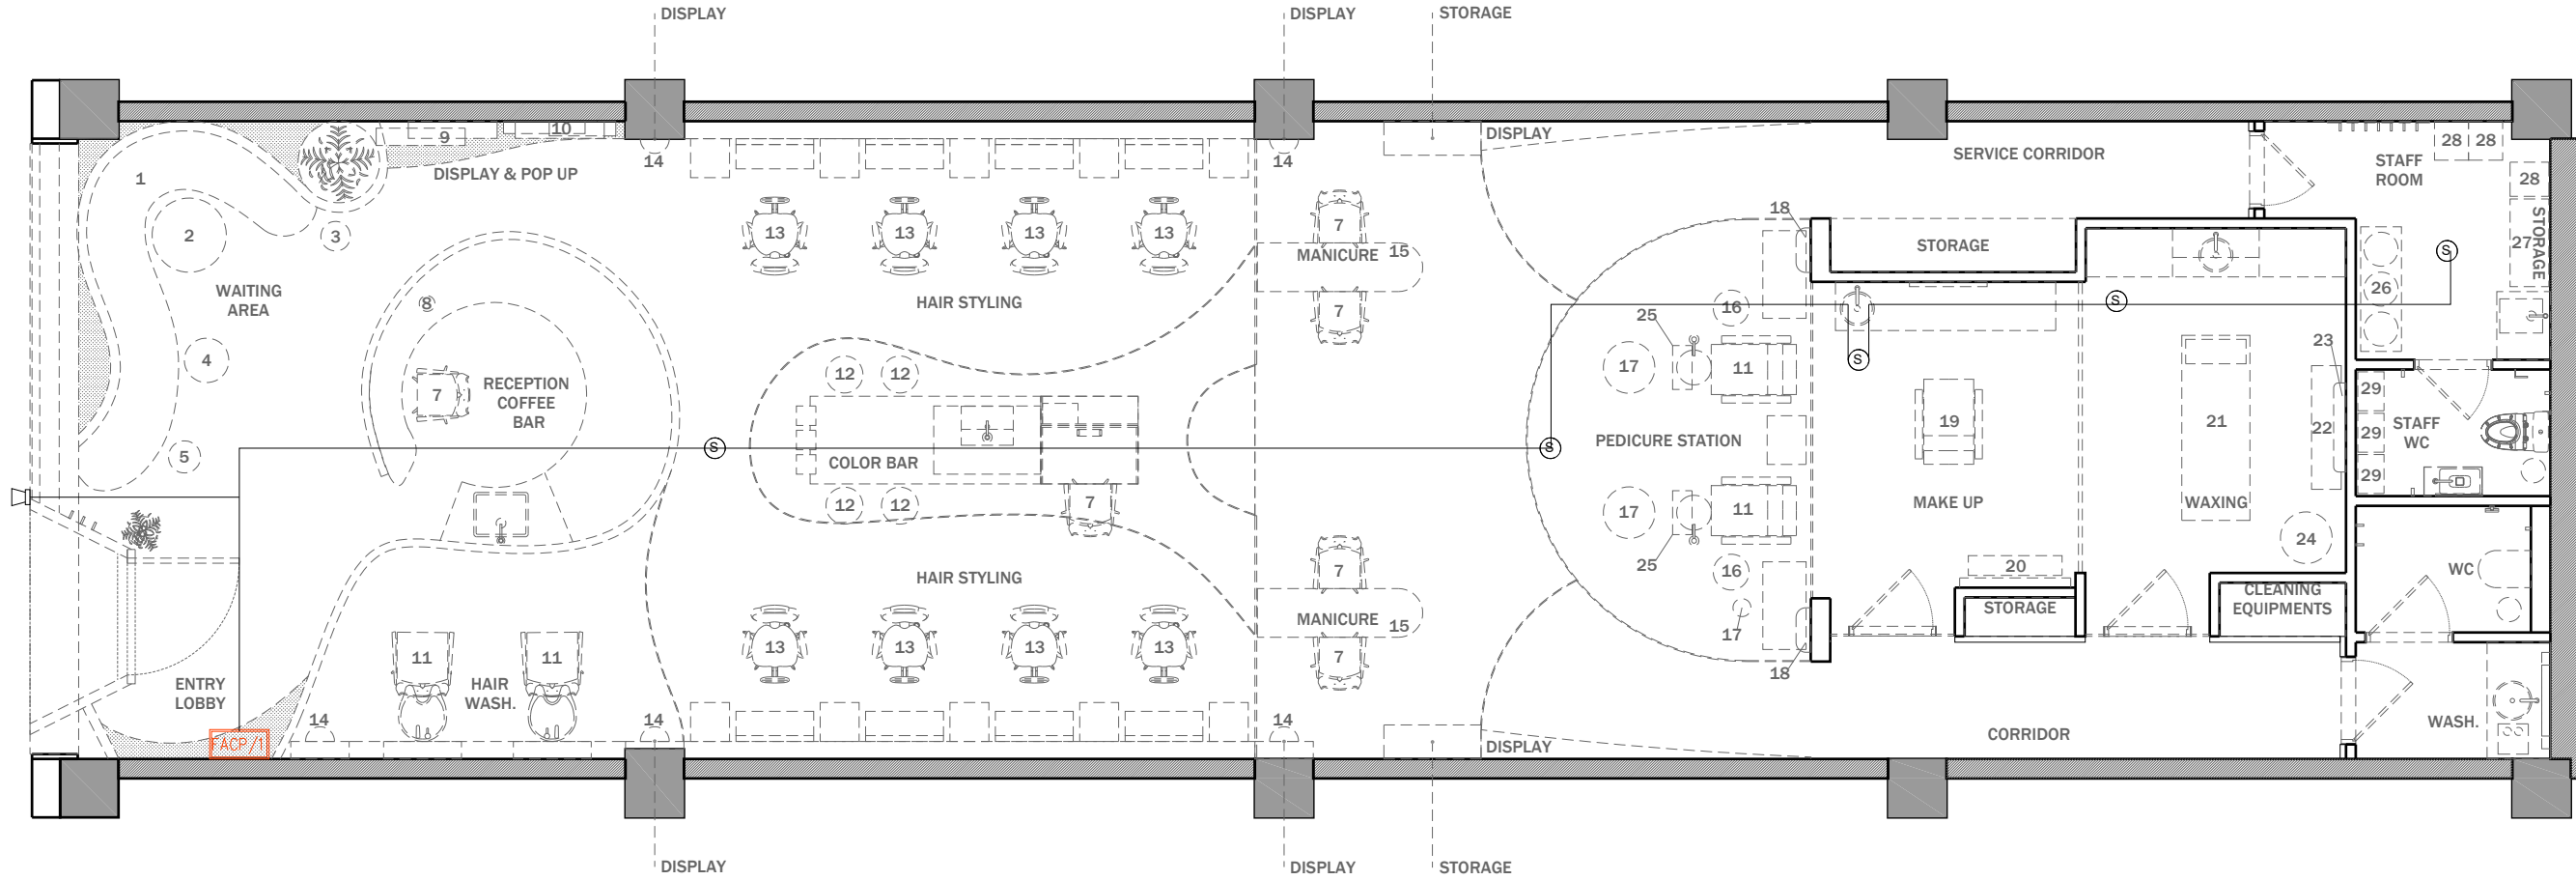


	ADDRESSABLE ELECTRONIC SOUNDER
	ADDRESSABLE ELECTRIC SMOKE DETECTOR
	FIRE ALARM PANEL
	WIRING

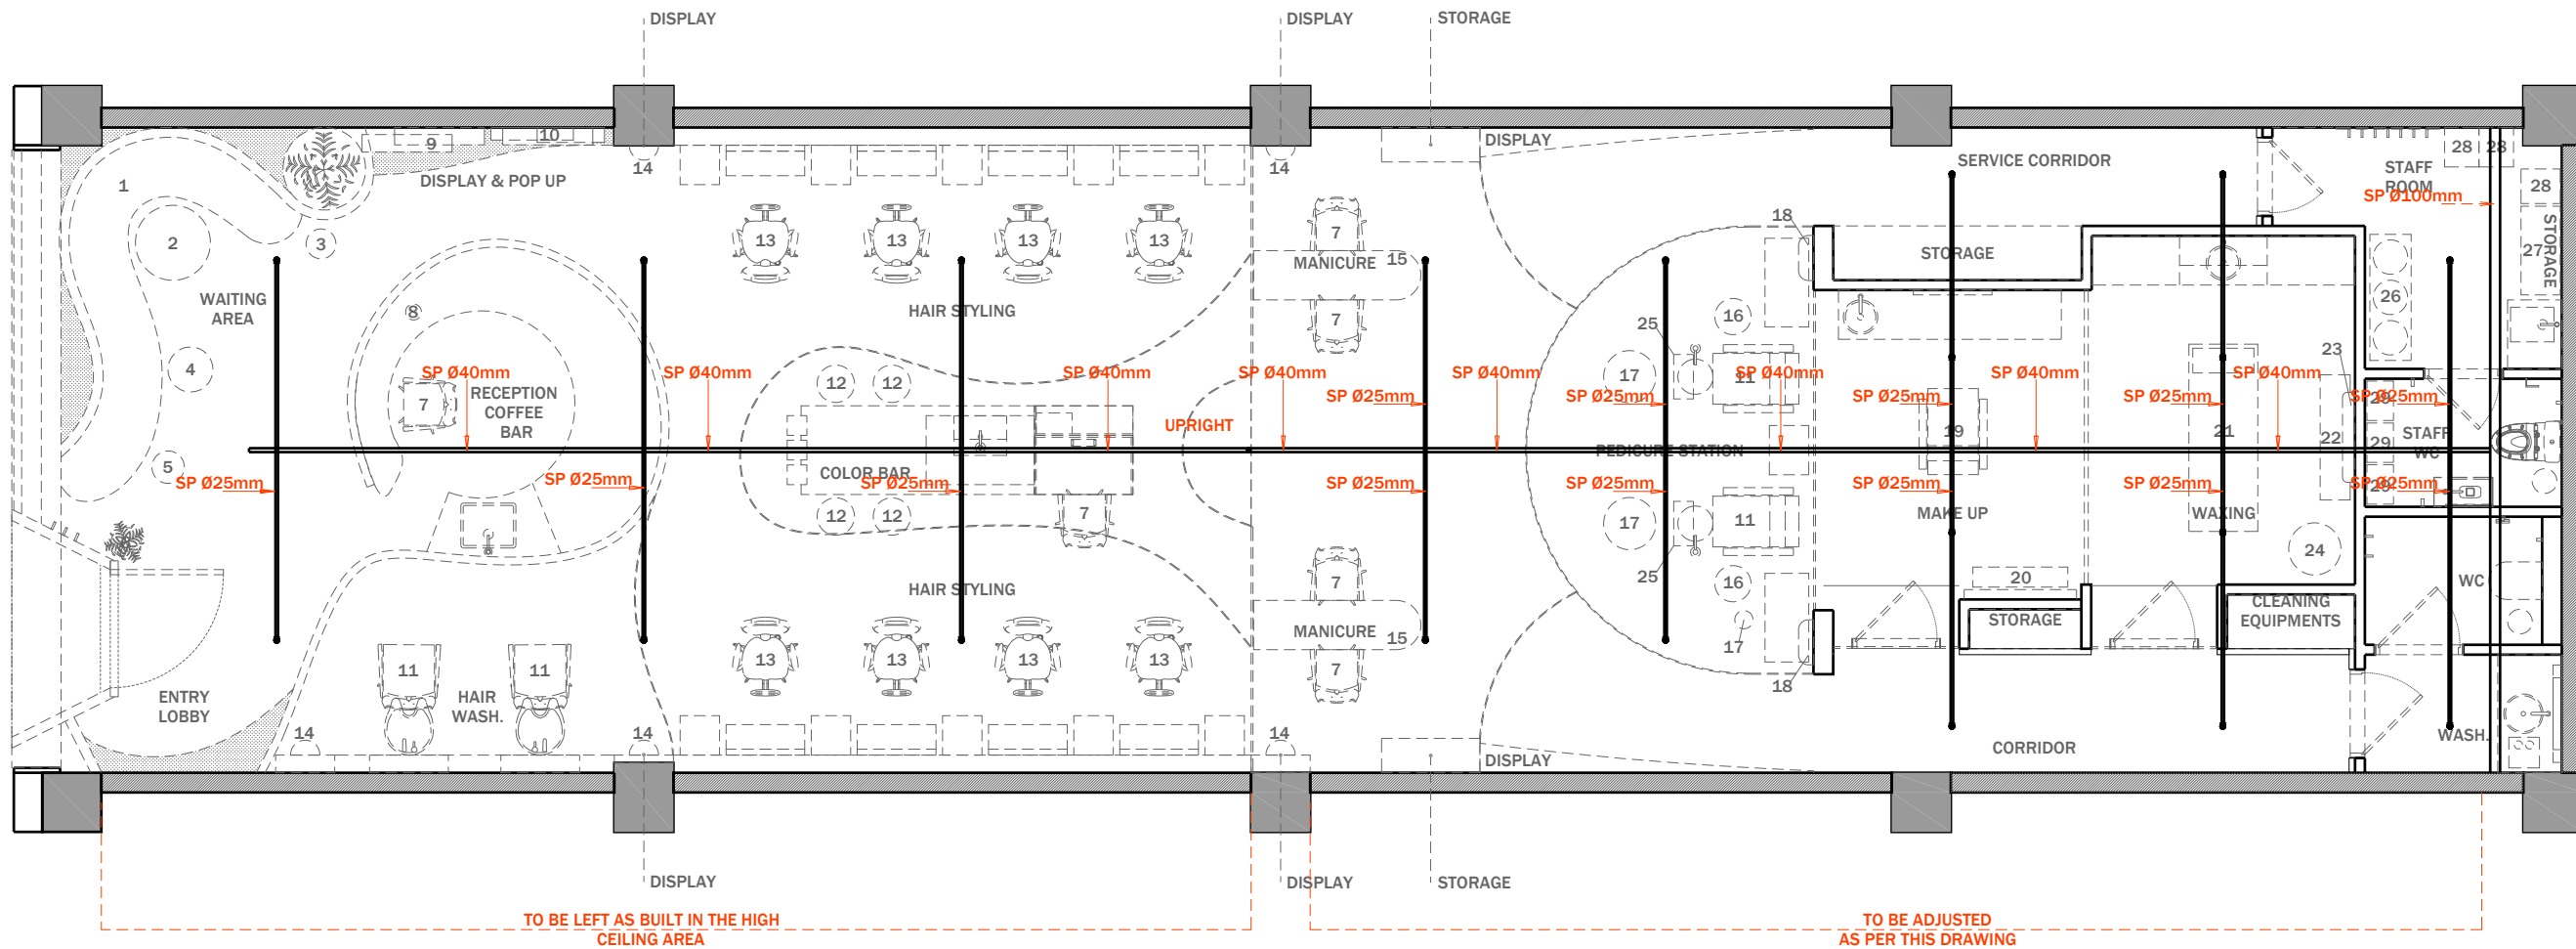

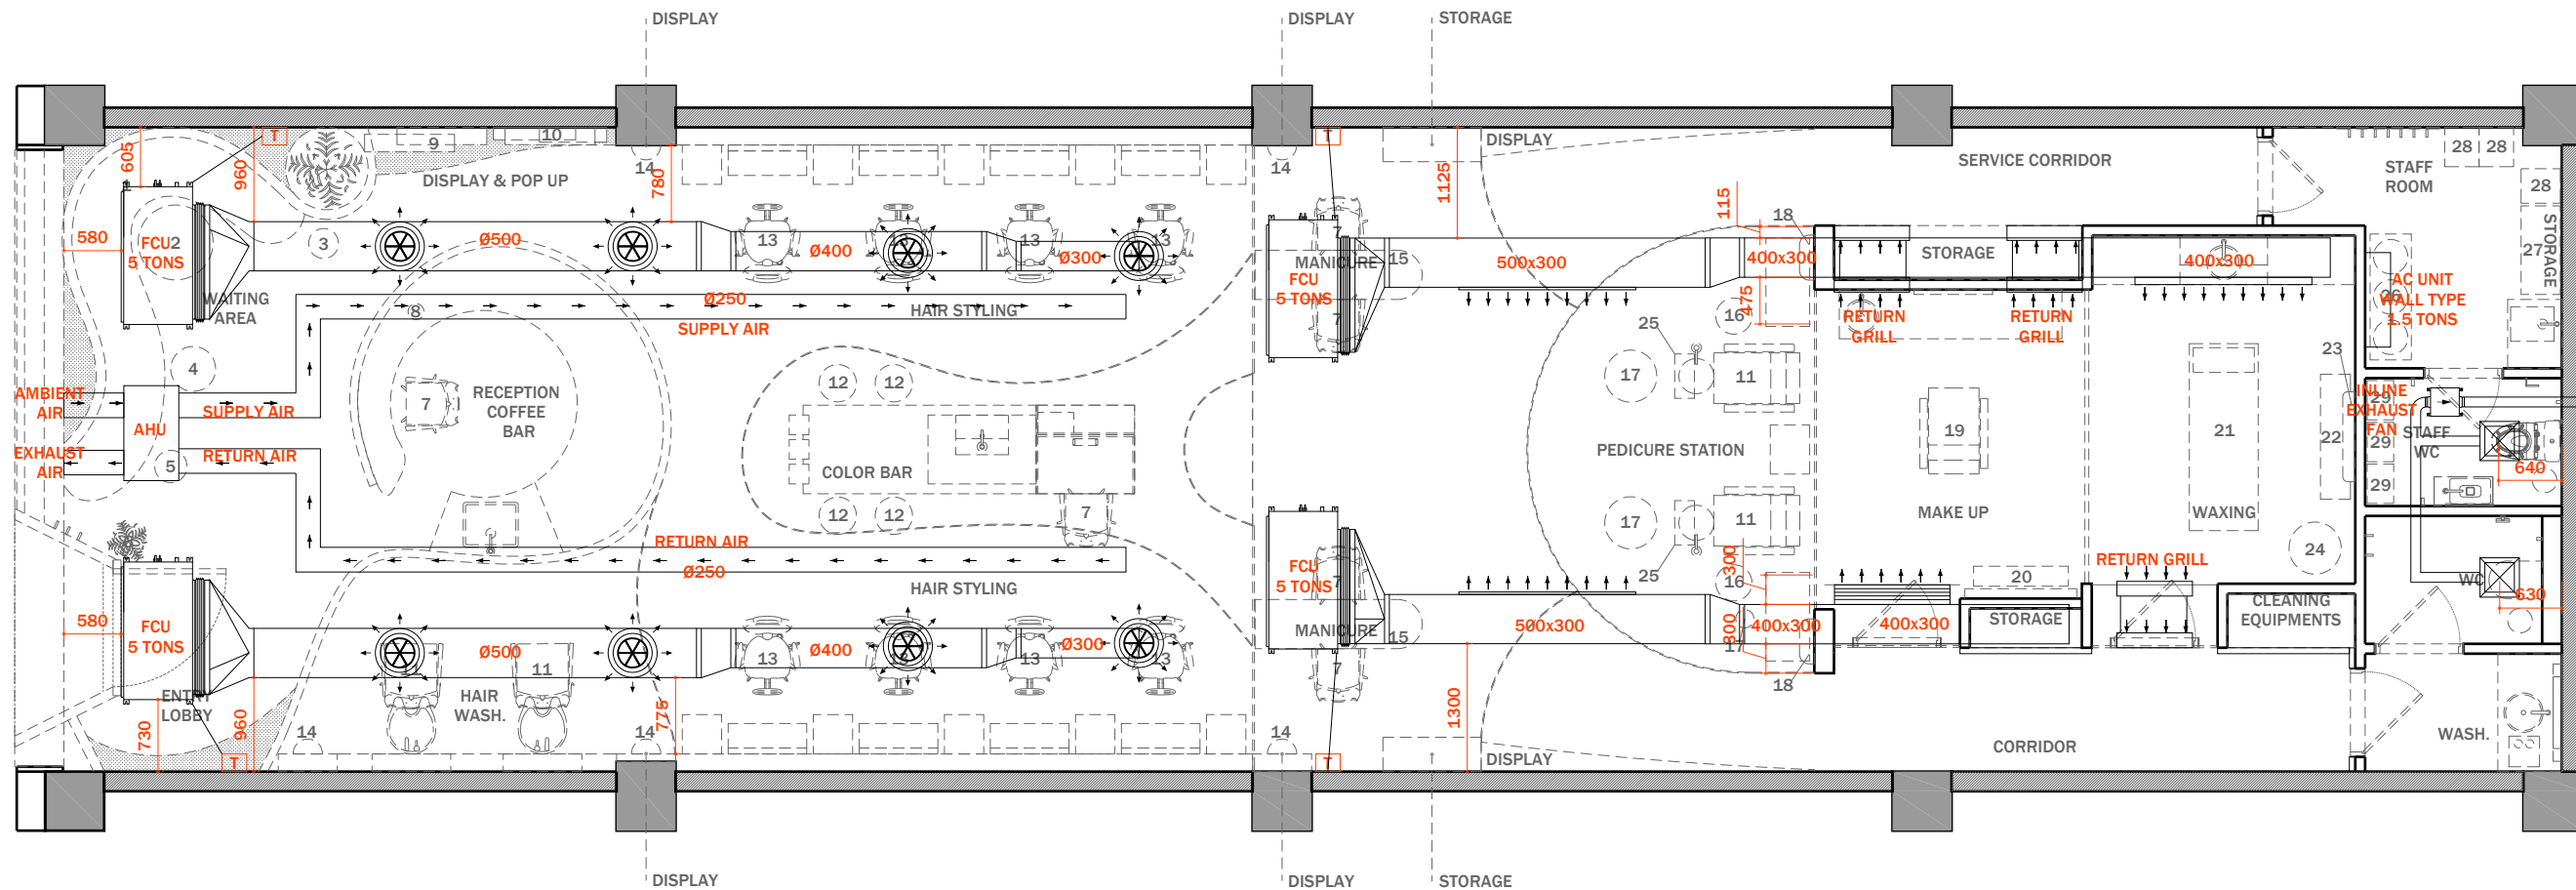

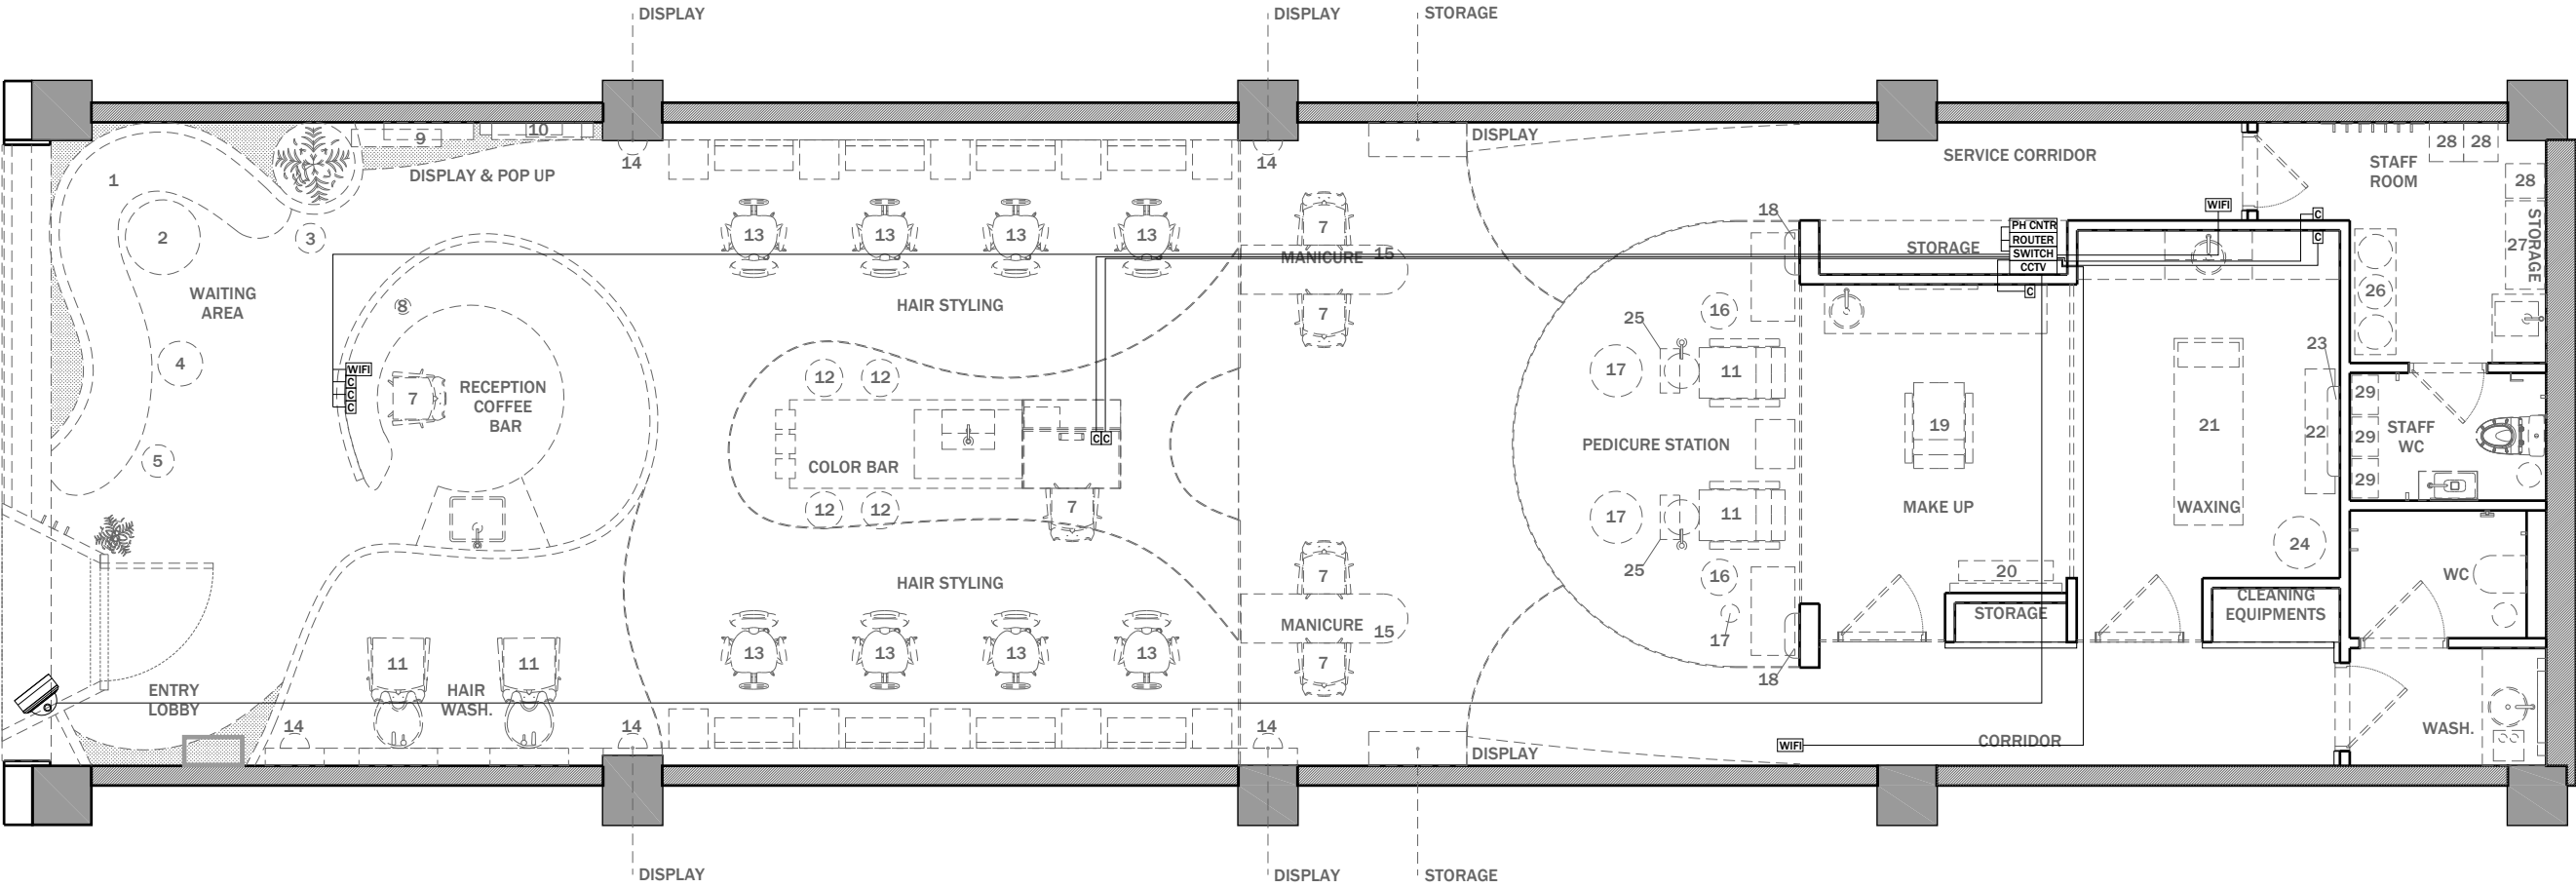

CCTV	CCTV NVR	WIFI	WI-FI HOTSPOT
SWITCH	NETWORK SWITCH	CCTV CAMERA	CCTV CAMERA
ROUTER	INTERNET/PHONE ROUTER	C	CAT6 SOCKET TERMINATED
PH CNTR	IP PHONE CENTRAL UNIT		CAT6 WIRING

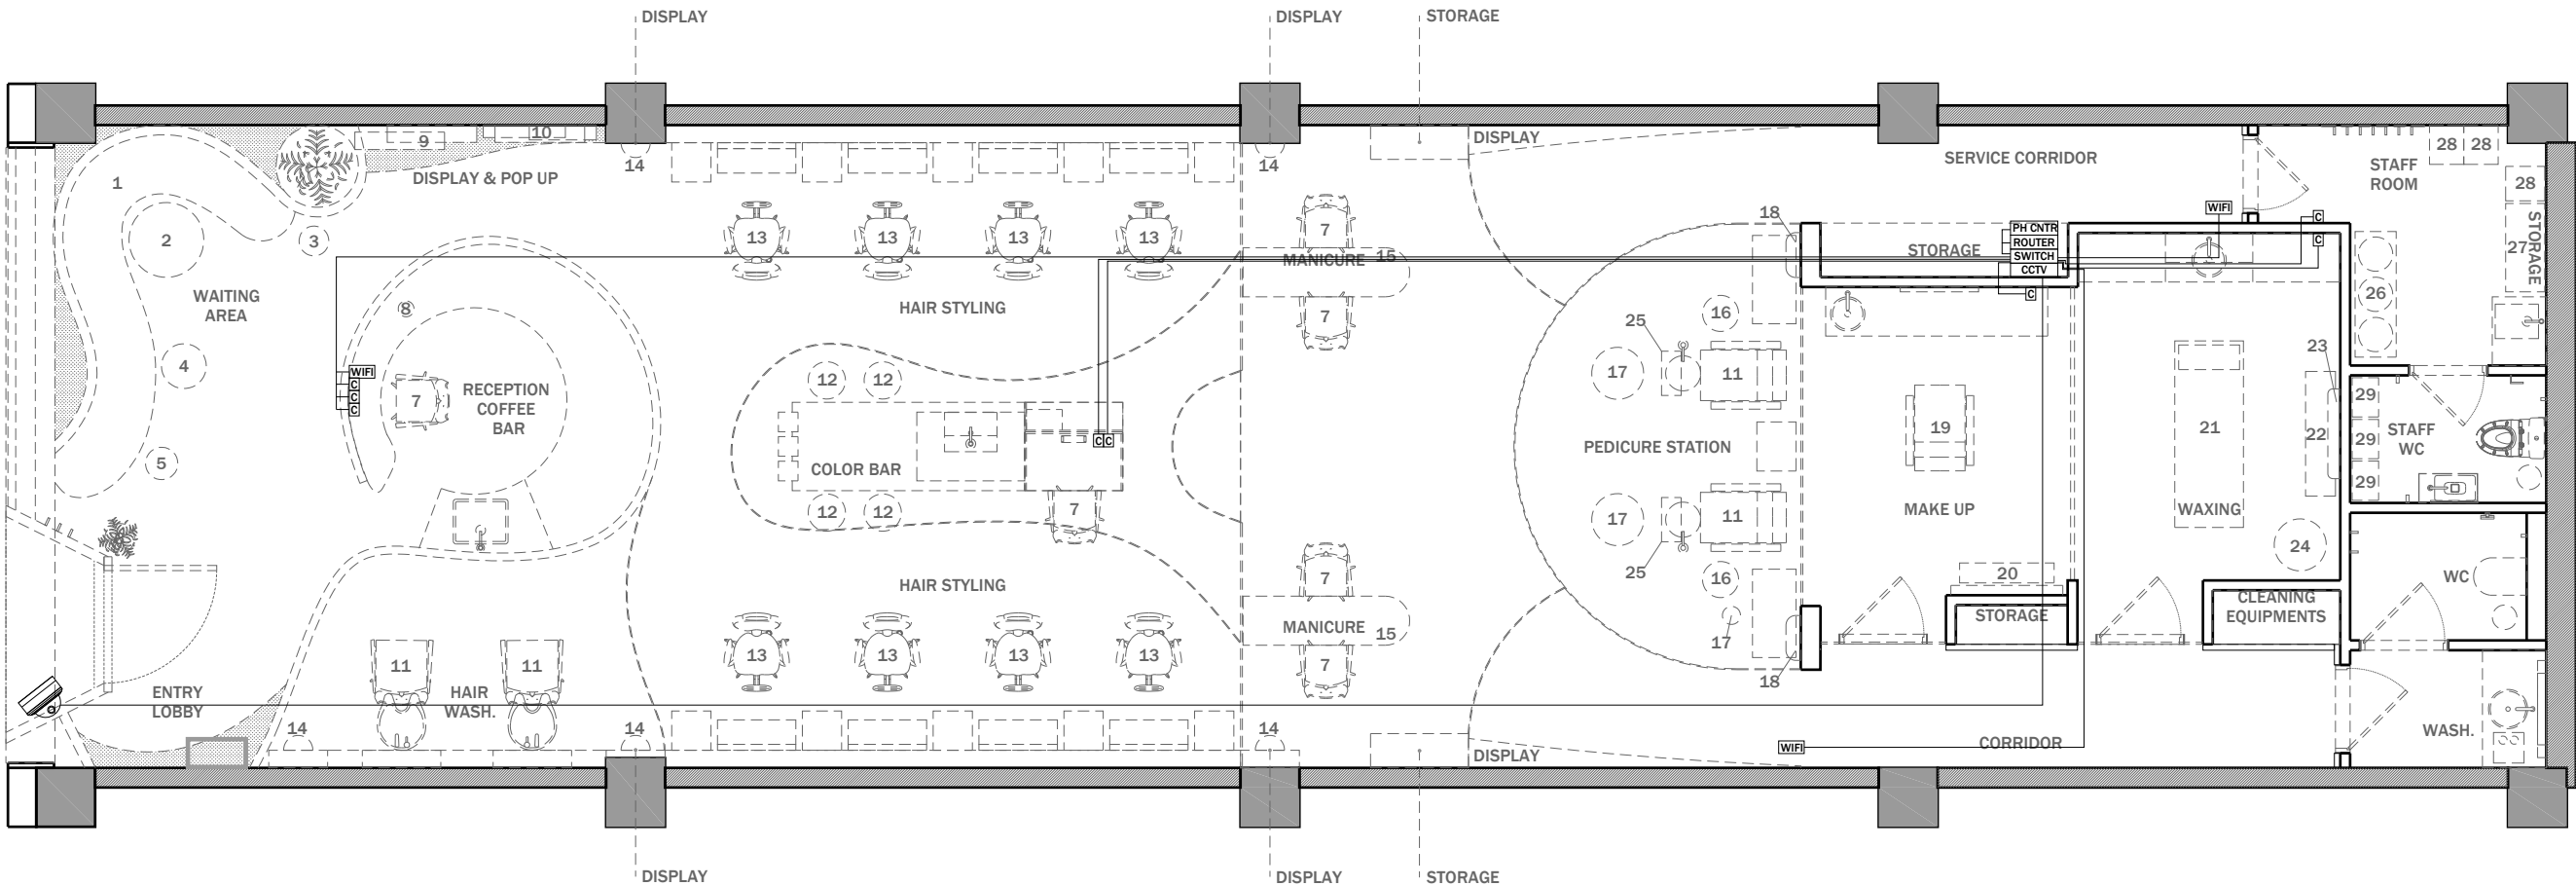

CCTV	CCTV NVR	WIFI	WI-FI HOTSPOT
SWITCH	NETWORK SWITCH	CCTV CAMERA	CCTV CAMERA
ROUTER	INTERNET/PHONE ROUTER	C	CAT6 SOCKET TERMINATED
PH CNTR	IP PHONE CENTRAL UNIT		CAT6 WIRING