



FURNITURE LAYOUT
SCALE 1:75

GENERAL NOTES

1. This drawing shall be read in conjunction with all other relevant architectural, structural & electrical drawings including those of other consultants.
2. It is the responsibility of contractors & manufacturers to check all relevant site dimensions prior to the start of construction or manufacture.
3. All materials and components must be installed on site in accordance with manufacturer's instructions, shop drawings and standard details.
4. All dimensions are in millimeters unless noted otherwise.
5. Full working drawings, specifications and samples are to be provided by Contractor/Supplier for approval prior to manufacture.

KEY PLAN

J	REV. WITH CLOUD	AC	AM	SM	2023.01.16
I	REV. WITH CLOUD	MP	AM	SM	2022.11.16
H	GEN. REV.	MP	AM	SM	2022.10.27
G	REV. WITH CLOUD	MP	AM	SM	2022.08.31
F	REV. WITH CLOUD	MP	AM	SM	2022.08.30
E	REV. WITH CLOUD	AC	AM	SM	2022.06.26
D	GEN. REV.	AC	AM	SM	2022.06.14
C	GEN. REV.	AC	AM	SM	2022.06.09
B	GEN. REV.	AC	AM	SM	2022.05.11
A	GEN. REV.	AC	AM	SM	2022.05.08
X	INITIAL ISSUE	AC	AM	SM	2022.04.26

REV.#	GENERAL NOTES	DRAWN BY	CHECKED BY	APPROVED BY	DATE
PROJECT TITLE	REFERENCE				

ARCAPITA - ATLANTA	ARC08
DRAWING TITLE	G


FURNITURE LAYOUT

DRAWING NUMBER	REVISION
ID-101	J

SCALE	FORMAT	ADDITIONAL NOTES	DESIGN DEVELOPMENT
1:75	A1		

SIMA MALAK + ALSSAMOURE
DESIGN ASSOCIATES
P.O. Box 15707 - Riyadh 11454 KSA
Tel. 01 441 4963 - Fax. 01 441 3867
simals@simals.com

©SIMA MALAK + ALSSAMOURE DESIGN ASSOCIATES (شركة) 2003
This document including all drawing and text is the property and copyright of SIMA MALAK + ALSSAMOURE DESIGN ASSOCIATES for use solely with respect to this Project and shall not be copied or reproduced by any means except by agreement in writing from SIMA MALAK + ALSSAMOURE DESIGN ASSOCIATES.

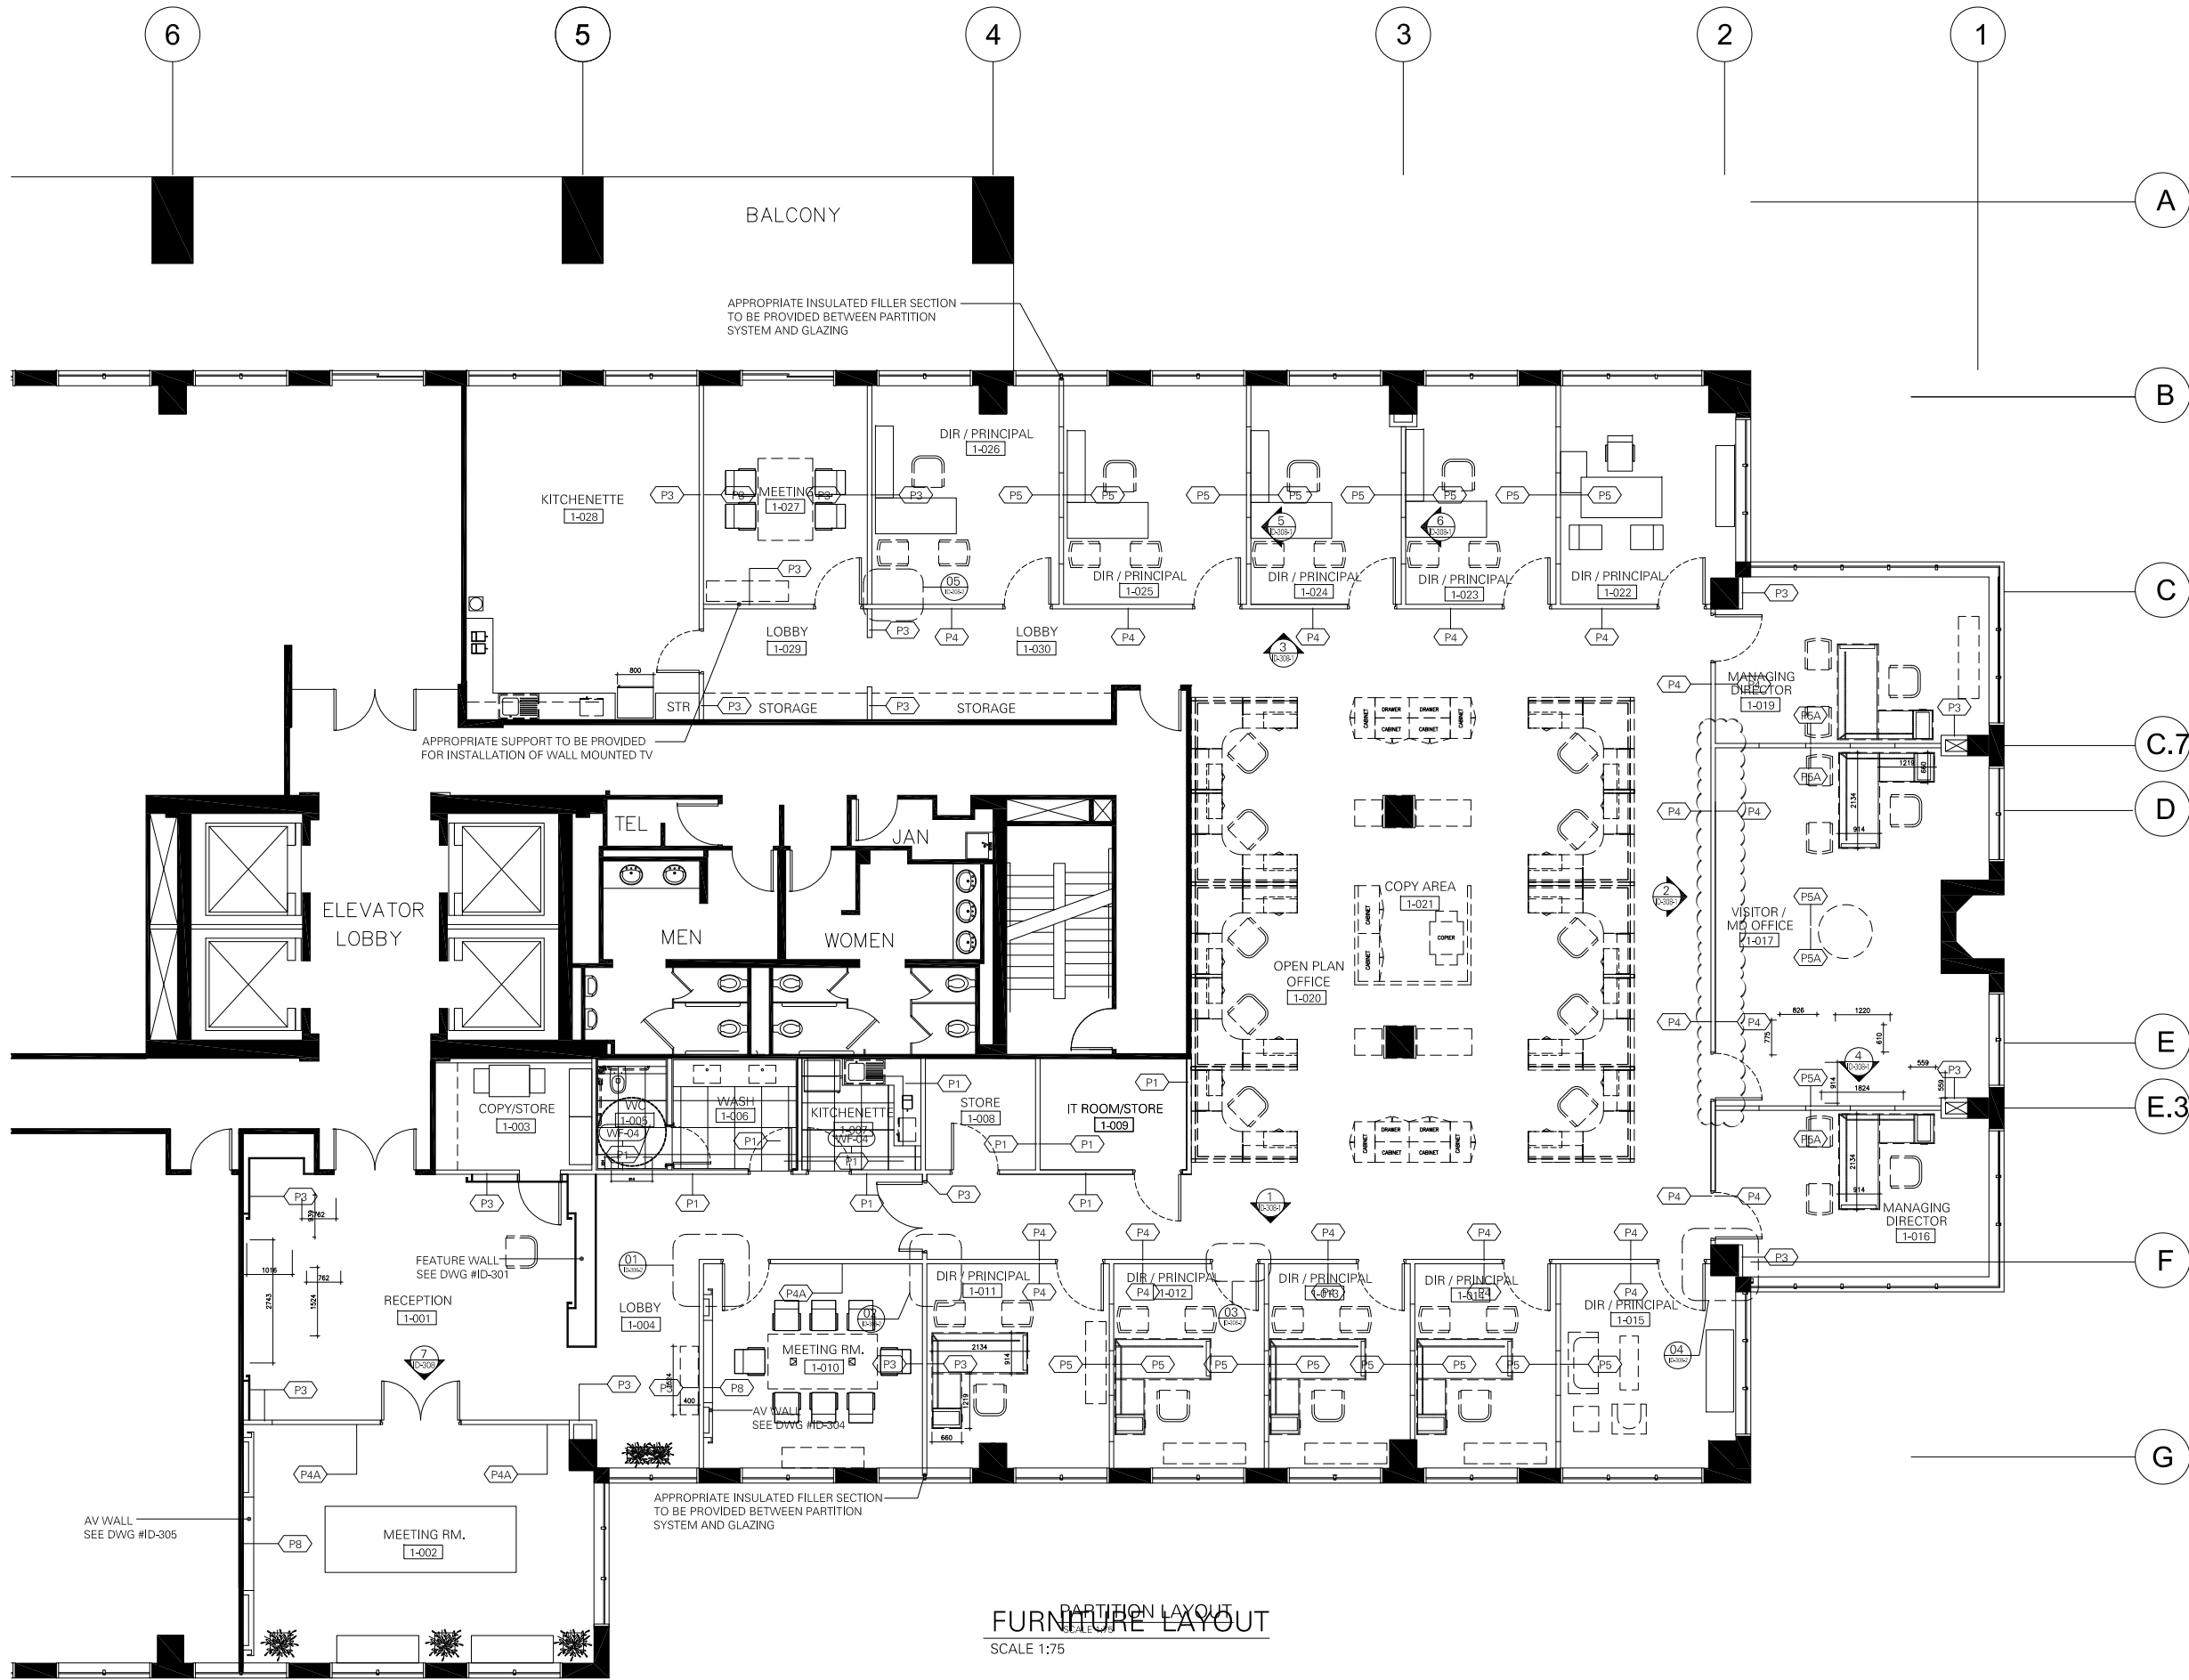

PARTITION LAYOUT
FURNITURE LAYOUT
SCALE 1:75

GENERAL NOTES

1. This drawing shall be read in conjunction with all other relevant architectural, structural & electrical drawings including those of other consultants.
2. It is the responsibility of contractors & manufacturers to check all relevant site dimensions prior to the start of construction or manufacture.
3. All materials and components must be installed on site in accordance with manufacturer's instructions, shop drawings and standard details.
4. All dimensions are in millimeters unless noted otherwise.
5. Full working drawings, specifications and samples are to be provided by Contractor/Supplier for approval prior to manufacture.

PARTITION TYPE:

P1 - 100mm thick Blockwork.

P3 - Metal stud gypsum wall.

P4 - FULLY GLAZED PARTITION SYSTEM: Double glazed office partition wall system with Aluminum profiles. Fully glazed module. Frame in anodized aluminum silver finish as per approved sample. Equipment panel with back painted glass (MG-02).

P4A - FULLY GLAZED PARTITION SYSTEM: Double glazed office partition wall system with Aluminum profiles. Fully glazed module. Frame in anodized aluminum silver finish as per approved sample. Equipment panel with back painted glass (MG-02) glazing to have sandblasting /manifestation applied to faces inside of both layers of glazing.

P5 - PARTIALLY GLAZED PARTITION SYSTEM: Double glazed office partition wall system with Aluminum profiles. Partially glazed module consisting of double glazed upper panels and wood veneered lower panels (MW-02) with insulation, frame in anodized aluminum silver finish as per approved sample.

P8 - Metal stud Gypsum partition with fitted A/V wall consisting of wood paneling / Cabinetry.

NOTES:

*. All doors are to be solid plain leaf with wood veneered.

*. Partition supplier to conduct their own site survey to obtain asbuilt dimensions and submit plans, elevations and details for approval.

KEY PLAN

D	REV. WITH CLOUD	MP	AM	SM	2022.11.16
C	REV. WITH CLOUD	MP	AM	SM	2022.10.27
B	REV. WITH CLOUD	MP	AM	SM	2022.08.17
A	GENERAL REV.	AC	AM	SM	2022.08.11
X	INITIAL ISSUE	AC	AM	SM	2022.06.02
REV.#	GENERAL NOTES	DRAWN BY	CHECKED BY	APPROVED BY	DATE

PROJECT TITLE	REFERENCE
ARCAPITA - ATLANTA	ARC08 G

DRAWING TITLE

PARTITION LAYOUT

DRAWING NUMBER

ID-102

REVISION

SCALE 1:75

FORMAT AT

ADDITIONAL NOTES

DESIGN DEVELOPMENT


**SIMA MALAK + ALSSAMOURE
DESIGN ASSOCIATES**

P.O. Box 15707 - Riyadh 11454 KSA

Tel. 01 441 4963 - Fax. 01 441 3867

simal@simas.com

©SIMA MALAK + ALSSAMOURE DESIGN ASSOCIATES () 2003
This document including all drawing and text is the property and copyright of SIMA MALAK + ALSSAMOURE DESIGN ASSOCIATES for use solely with respect to this Project and shall not be copied or reproduced by any means except by agreement in writing from SIMA MALAK + ALSSAMOURE DESIGN ASSOCIATES.

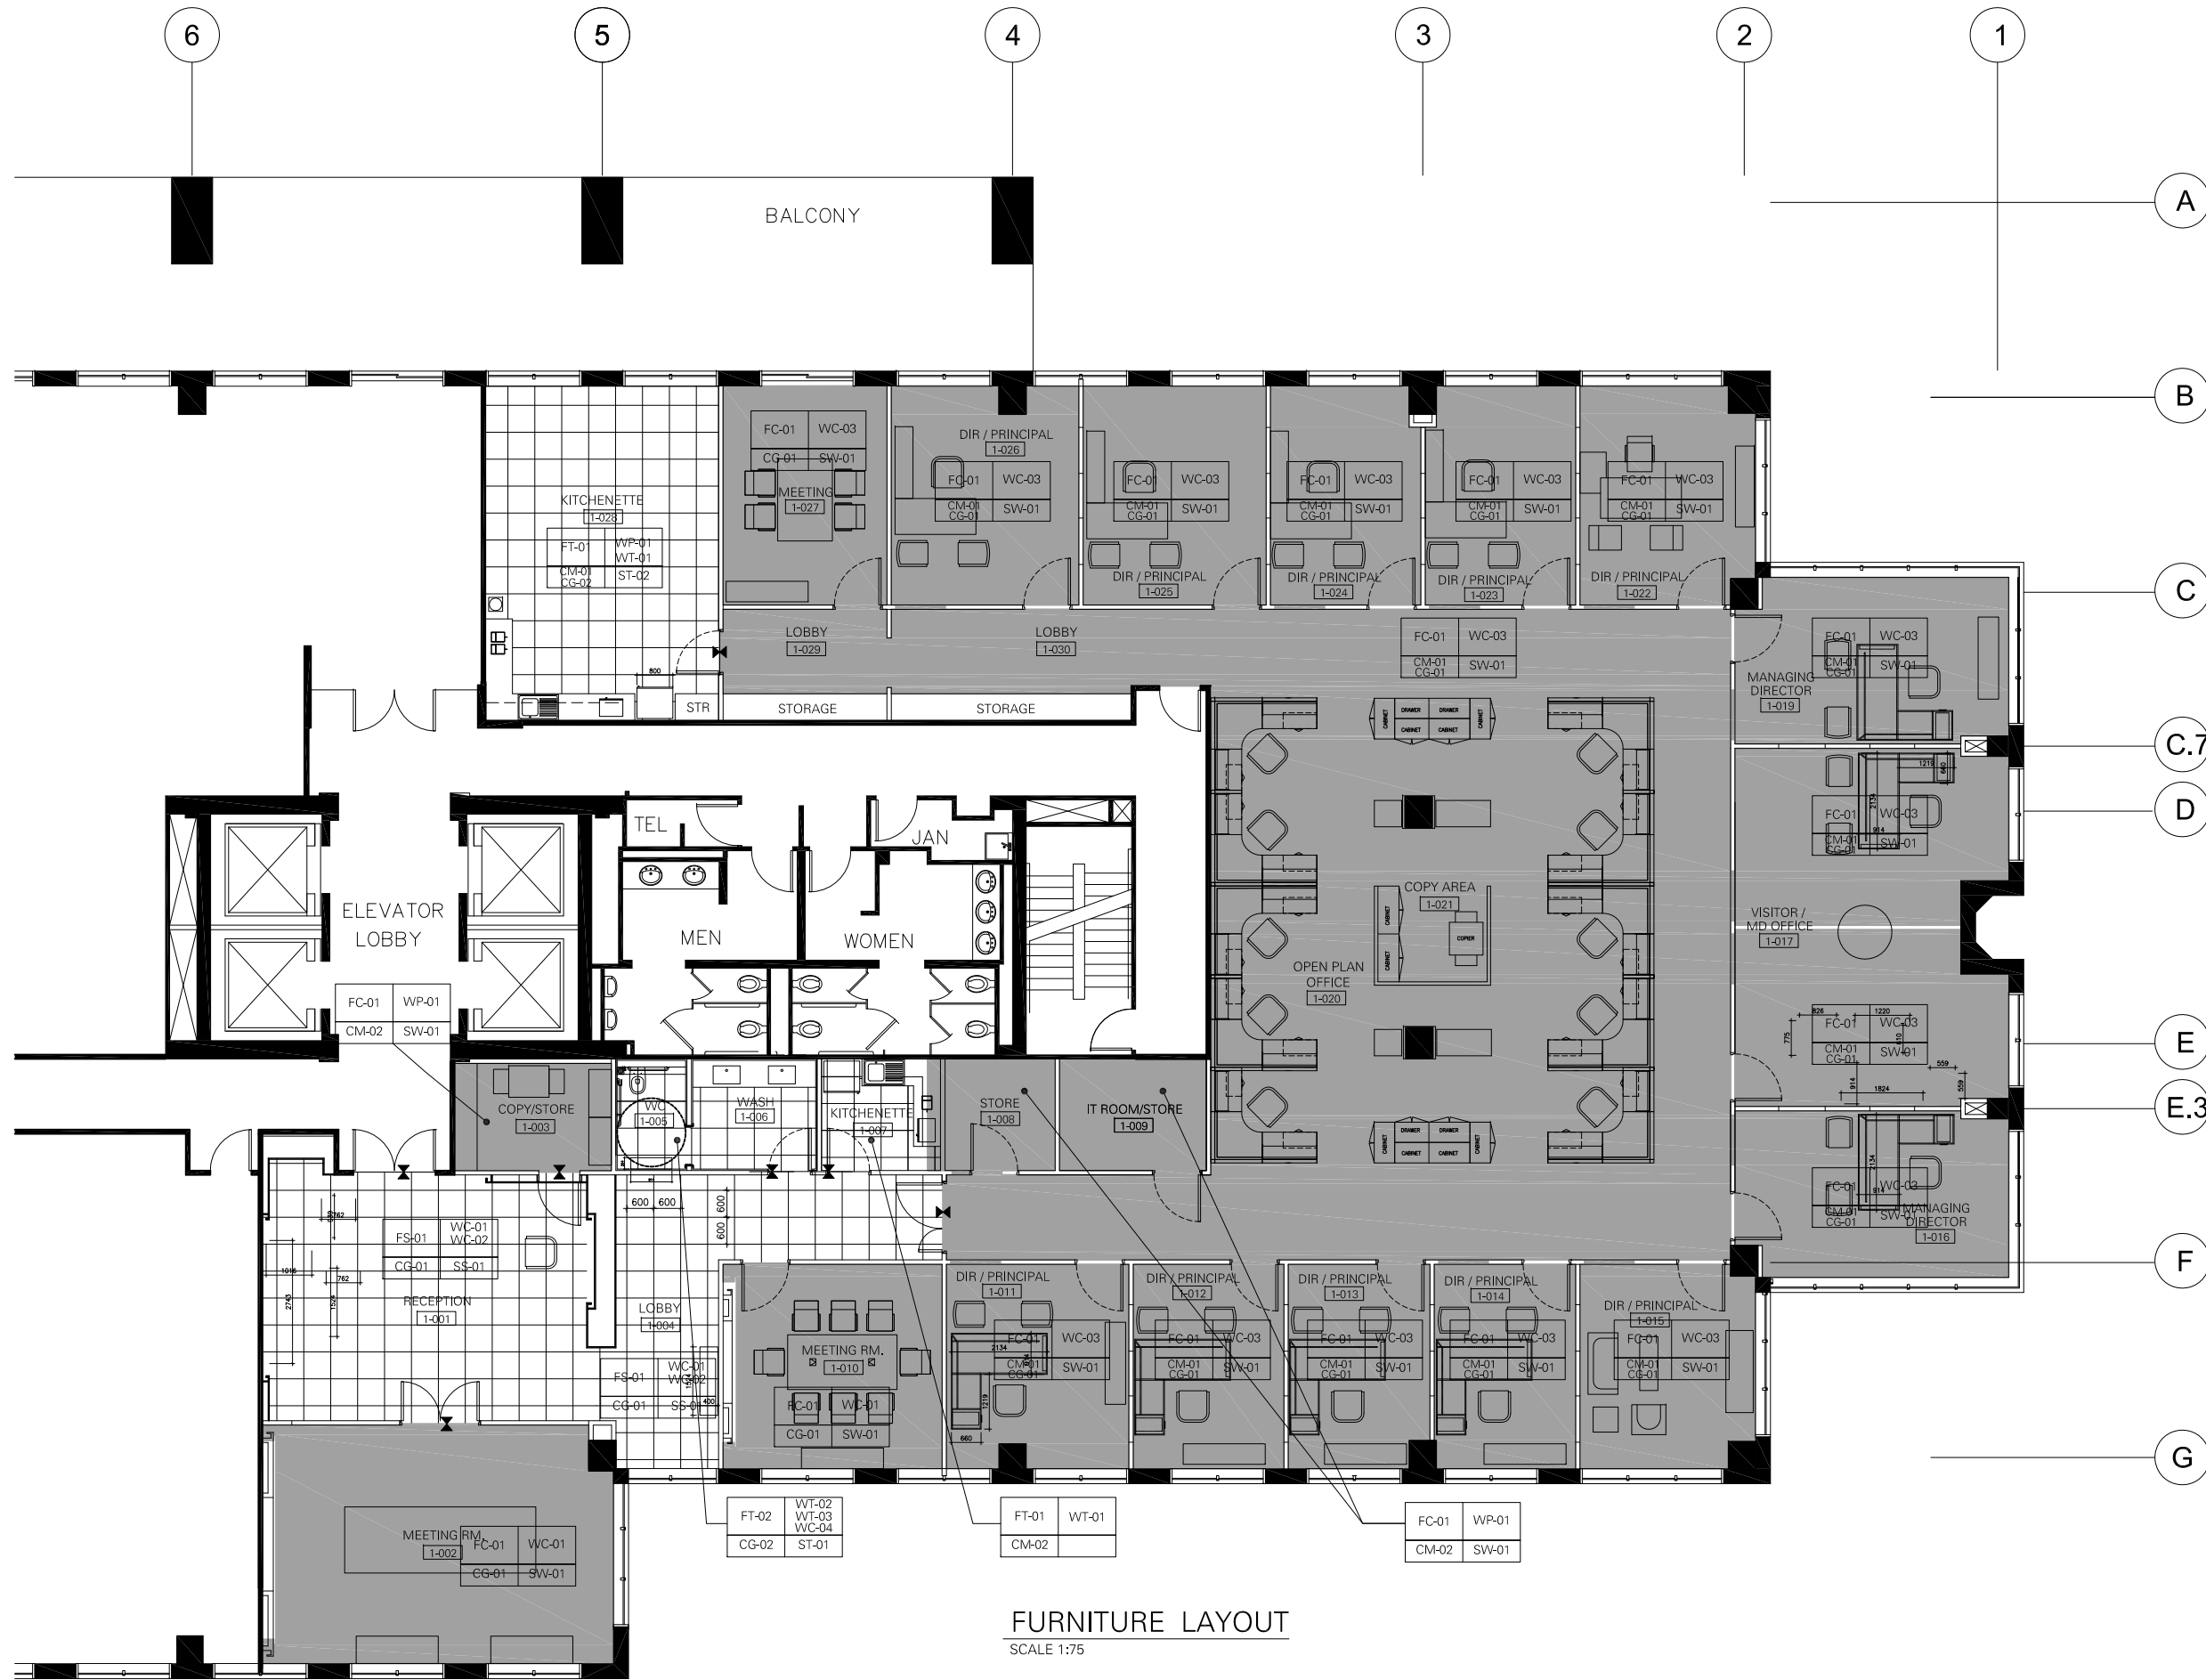

FURNITURE LAYOUT
SCALE 1:75

GENERAL NOTES


1. This drawing shall be read in conjunction with all other relevant architectural, structural & electrical drawings including those of other consultants.
2. It is the responsibility of contractors & manufacturers to check all relevant site dimensions prior to the start of construction or manufacture.
3. All materials and components must be installed on site in accordance with manufacturer's instructions, shop drawings and standard details.
4. All dimensions are in millimeters unless noted otherwise.
5. Full working drawings, specifications and samples are to be provided by Contractor/Supplier for approval prior to manufacture.

KEY PLAN

REV.	DESCRIPTION	DATE	BY	CHECKED	APPROVED
A	GENERAL REV.	2022.08.18	MP	AM	SM
X	INITIAL ISSUE	2022.08.11	AC	AM	SM
REV.#	GENERAL NOTES	DRAWN BY	CHECKED BY	APPROVED BY	DATE
PROJECT TITLE					REFERENCE
ARCAPITA - ATLANTA					ARC08 G
DRAWING TITLE					
FINISHING LAYOUT					
DRAWING NUMBER					REVISION
ID-103					
SCALE	FORMAT	ADDITIONAL NOTES	DESIGN DEVELOPMENT		
1:75	AT				

SIMA MALAK + ALSSAMOURE
DESIGN ASSOCIATES
P.O. Box 15707 - Riyadh 11454 KSA
Tel. 01 441 4963 - Fax. 01 441 3867
simas@simal.com

©SIMA MALAK + ALSSAMOURE DESIGN ASSOCIATES (شركة) 2003
This document including all drawing and text is the property and copyright of SIMA MALAK + ALSSAMOURE DESIGN ASSOCIATES for use solely with respect to this Project and shall not be copied or reproduced by any means except by agreement in writing from SIMA MALAK + ALSSAMOURE DESIGN ASSOCIATES.

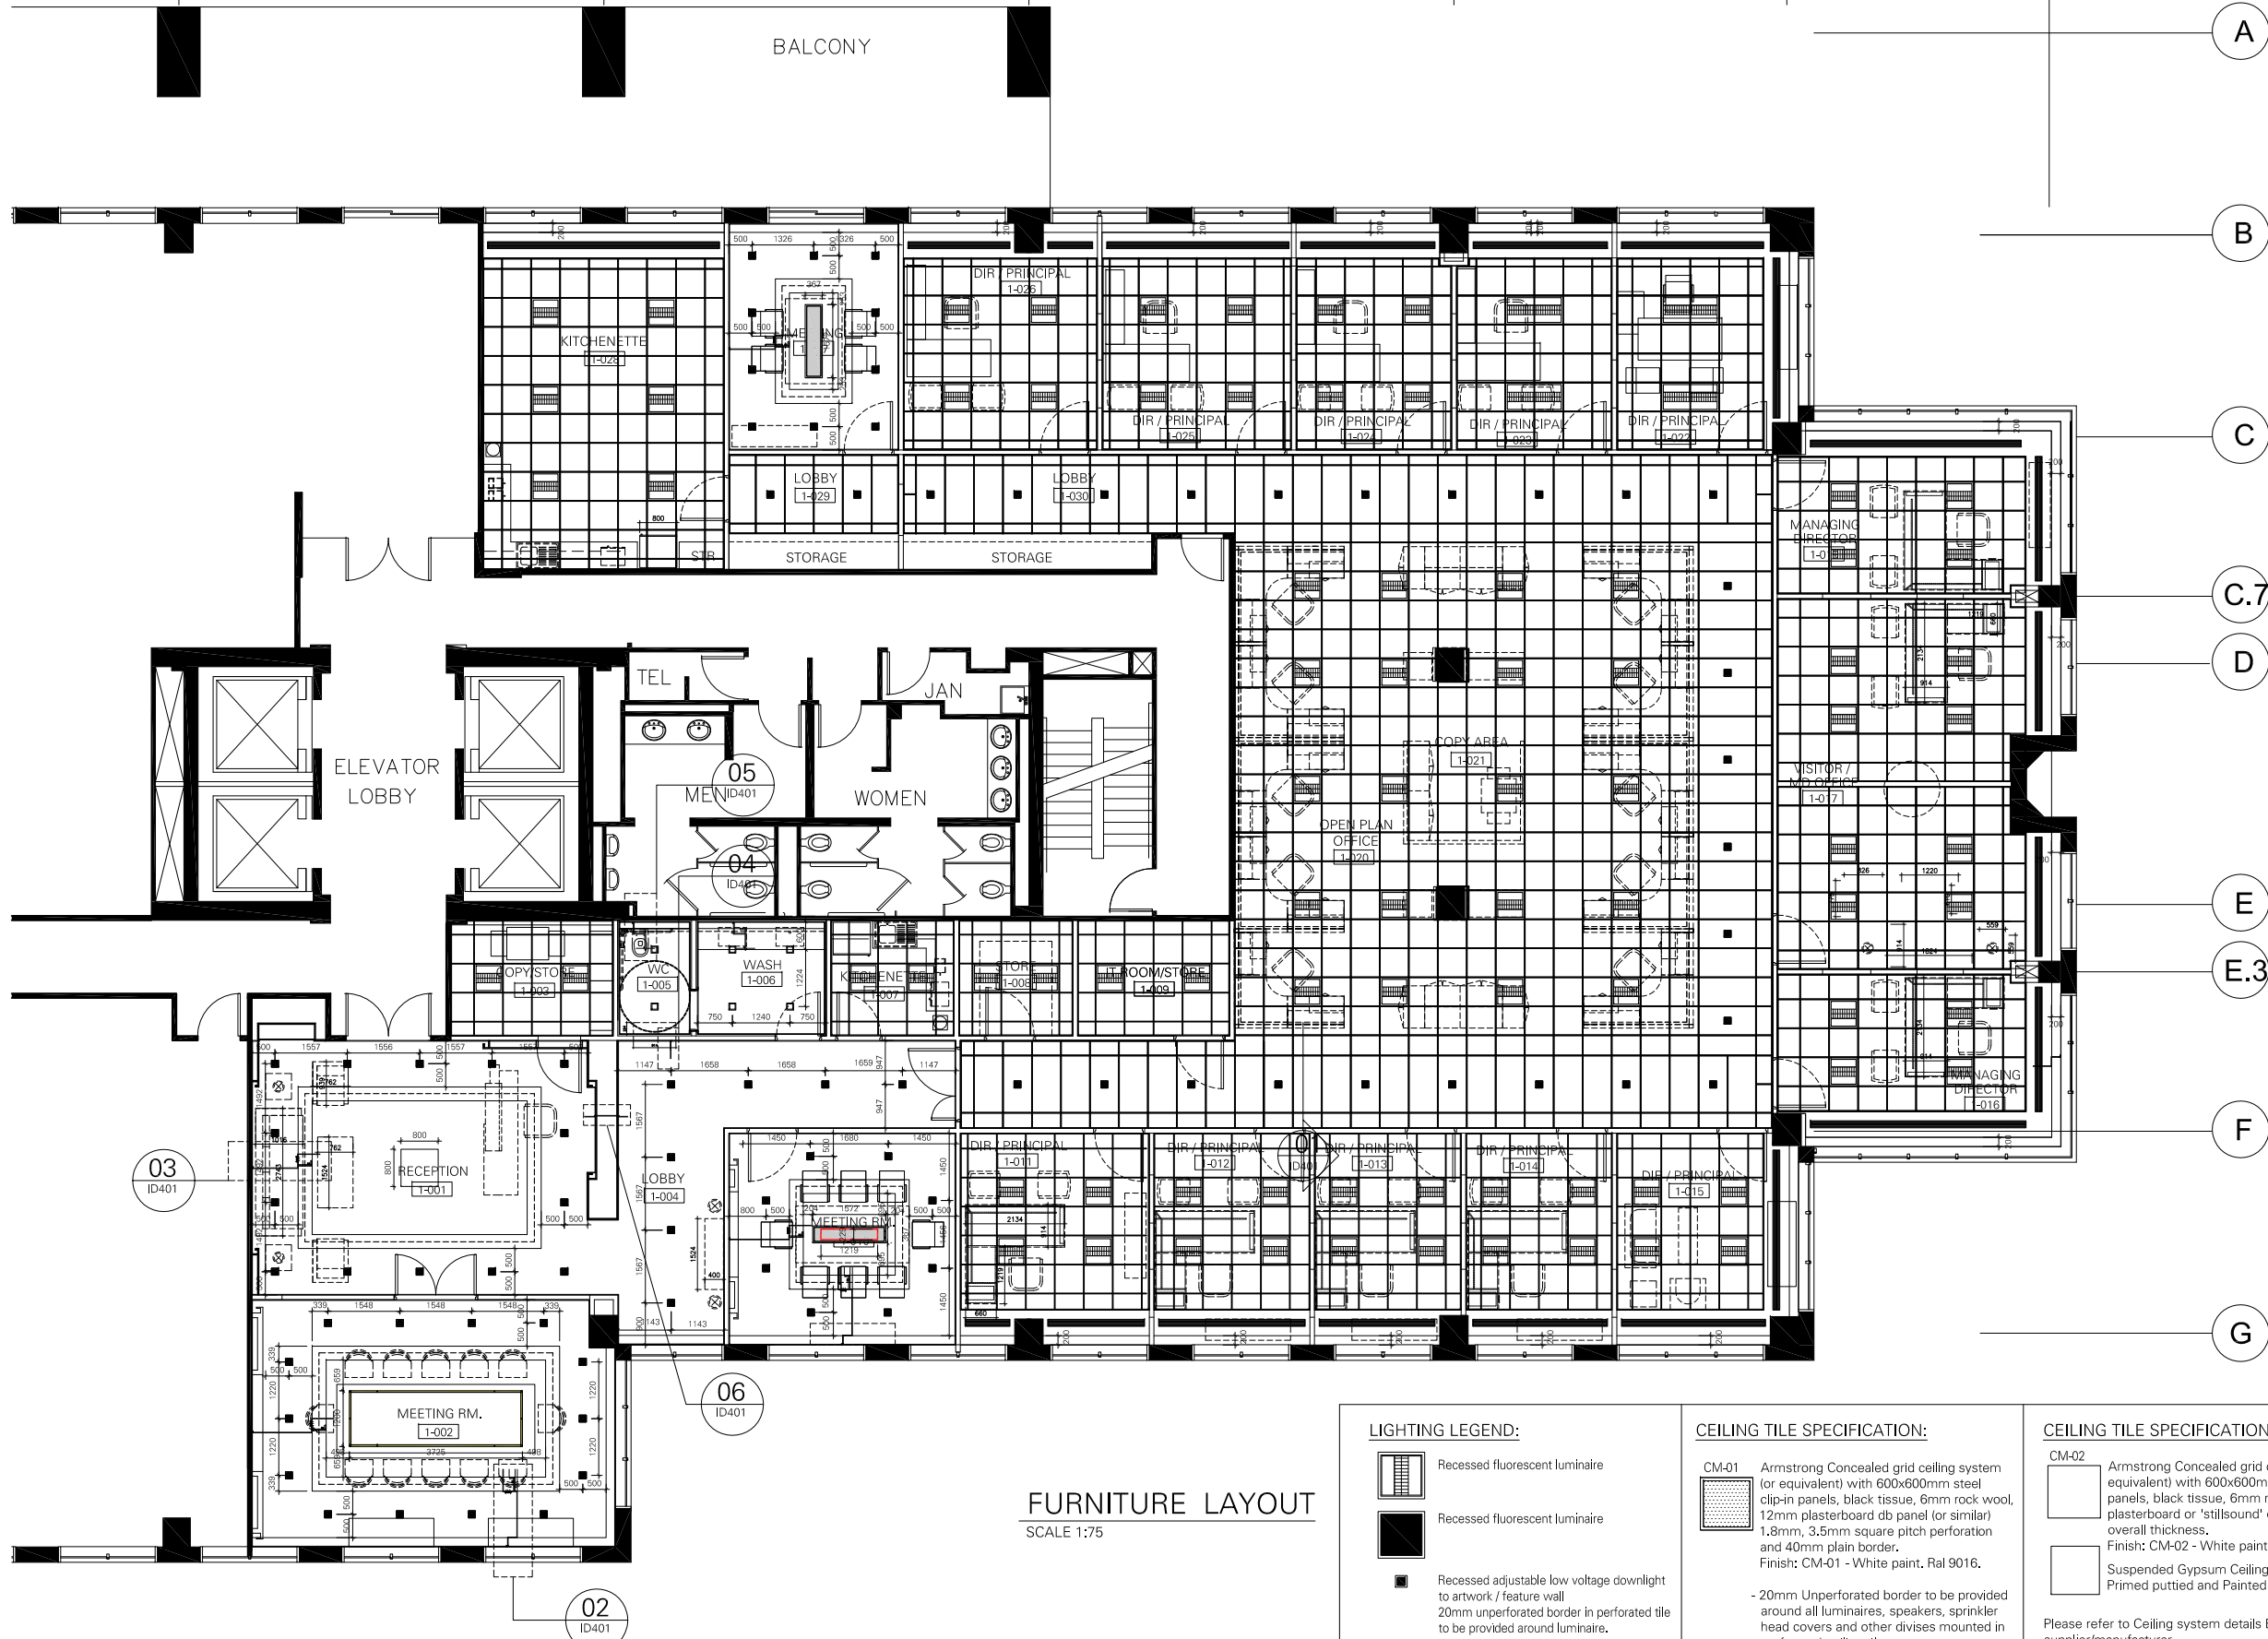

FURNITURE LAYOUT
SCALE 1:75

LIGHTING LEGEND:



Recessed fluorescent luminaire



Recessed adjustable low voltage downlight to artwork / feature wall
20mm unperforated border in perforated tile to be provided around luminaire.

All Luminaires to be Ral 9016 to co-ordinate with ceiling system.

Continuous liner lighting (Corridor)



Decorative light fittings



Concealed LED Strip Light

CEILING TILE SPECIFICATION:



CM-01 Armstrong Concealed grid ceiling system (or equivalent) with 600x600mm steel clip-in panels, black tissue, 6mm rock wool, 12mm plasterboard db panel (or similar) 1.8mm, 3.5mm square pitch perforation and 40mm plain border.
Finish: CM-01 - White paint, Ral 9016.

- 20mm Unperforated border to be provided around all luminaires, speakers, sprinkler head covers and other divises mounted in perforated ceiling tiles.

- If integrated luminaires are not used a suitable recess should be provided so that the fitting is installed flush with the ceiling

- Speakers and Sprinkler head covers should also be mounted in a corresponding recess so that they are flush with the ceiling.

Full Shop drawings and details to be provided by Contractor / Manufacturer.

CEILING TILE SPECIFICATION:



CM-02 Armstrong Concealed grid ceiling system (or equivalent) with 600x600mm steel clip-in panels, black tissue, 6mm rock wool, 12mm plasterboard or 'stillsound' db panel, 16mm overall thickness.
Finish: CM-02 - White paint, RAL. 9016.

Suspended Gypsum Ceiling
Primed puttied and Painted white, RAL. 9016.

Please refer to Ceiling system details By Ceiling supplier/manufacturer.

NOTES

- All ceiling levels taken from FFL.
- Unless noted otherwise all ceiling levels are +2.70m, from FFL.

GENERAL NOTES

1. This drawing shall be read in conjunction with all other relevant architectural, structural & electrical drawings including those of other consultants.
2. It is the responsibility of contractors & manufacturers to check all relevant site dimensions prior to the start of construction or manufacture.
3. All materials and components must be installed on site in accordance with manufacturer's instructions , shop drawings and standard details.
4. All dimensions are in millimeters unless noted otherwise.
5. Full working drawings, specifications and samples are to be provided by Contractor/Supplier for approval prior to manufacture.

NOTES FOR MANUFACTURE:

- * Construction methods shown on drawings are suggested methods only.
- * Full working drawings and samples are to be provided by contractor for approval prior to manufacture.
- * Please refer to relevant sub consultants drawings for Audio visual, security and I.T. requirements.

FINISHES

- * All Elements of the ceiling including AC Grill and ceiling mounted devices should be Ral 9016.
- * Samples of all finishes are to be provided by the contractor to be approved by the designer prior to manufacture / construction.

Full Shop drawings and details to be provided by Contractor / Manufacturer.

KEY PLAN

D	GENERAL REV.	MP	AM	SM	2022.09.01
C	REV. CALLOUTS	MP	AM	SM	2022.08.17
B	REV. WITH CLOUD	AC	AM	SM	2022.06.27
A	TOILET REV.	AC	AM	SM	2022.06.15
X	INITIAL ISSUE	AC	AM	SM	2022.06.08
REV.#	GENERAL NOTES	DRAWN BY	CHECKED BY	APPROVED BY	DATE
PROJECT TITLE					REFERENCE

ARCAPITA - ATLANTA

ARC08
G

DRAWING TITLE

REFLECTED CEILING PLAN

DRAWING NUMBER

ID-201

REVISION

B

SCALE

1:75

FORMAT

AT

ADDITIONAL


NOTES

DESIGN DEVELOPMENT


SIMA MALAK + ALSSAMOURE DESIGN ASSOCIATES

P.O. Box 15707 - Riyadh 11454 KSA
Tel. 01 441 4963 - Fax. 01 441 3867
simals@simals.com


©SIMA MALAK + ALSSAMOURE DESIGN ASSOCIATES () 2003
This document including all drawing and text is the property and copyright of SIMA MALAK + ALSSAMOURE DESIGN ASSOCIATES for use solely with respect to this Project and shall not be copied or reproduced by any means except by agreement in writing from SIMA MALAK + ALSSAMOURE DESIGN ASSOCIATES.

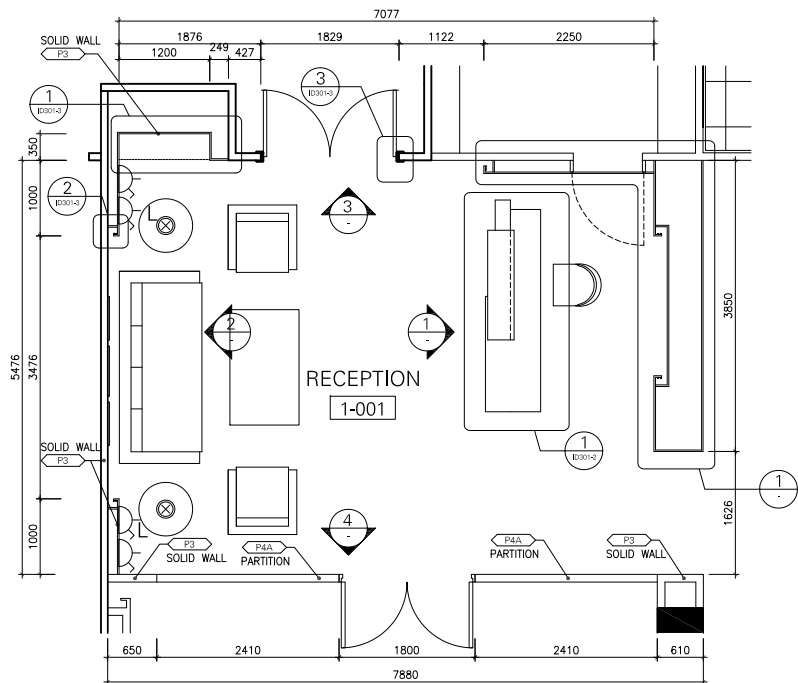


1 RECEPTION PLAN
SCALE 1:50

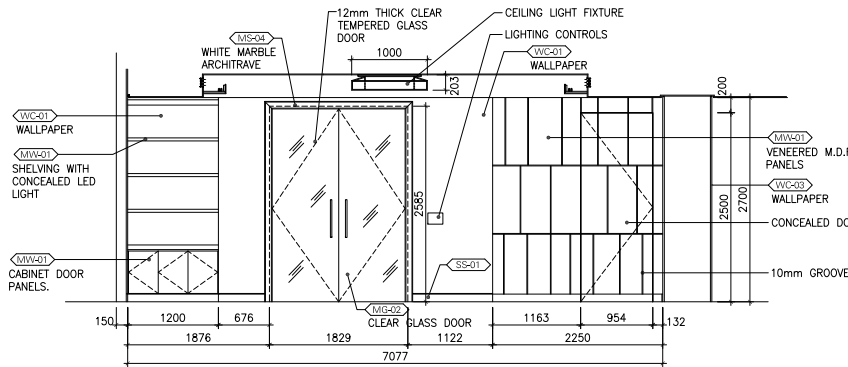


3 ELEVATION
SCALE 1:50

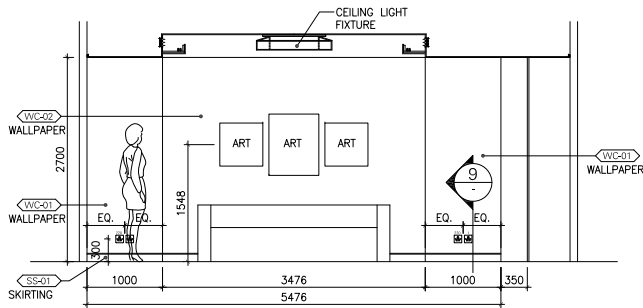


2 ELEVATION
SCALE 1:50

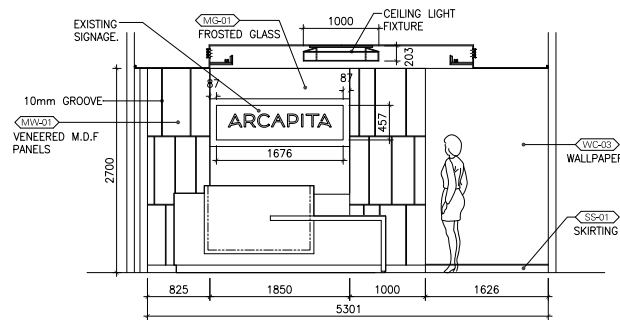


1 ELEVATION
SCALE 1:50

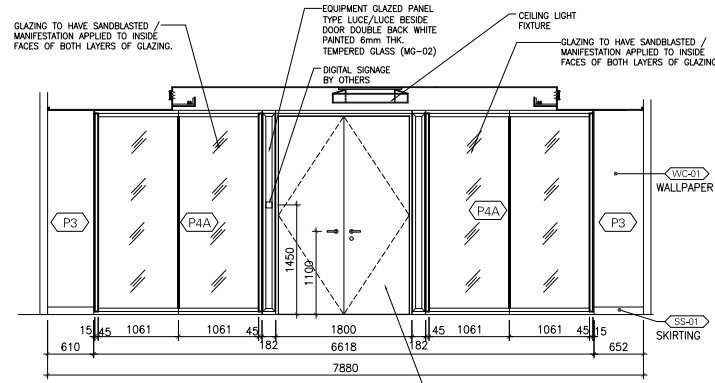


4 ELEVATION
SCALE 1:50

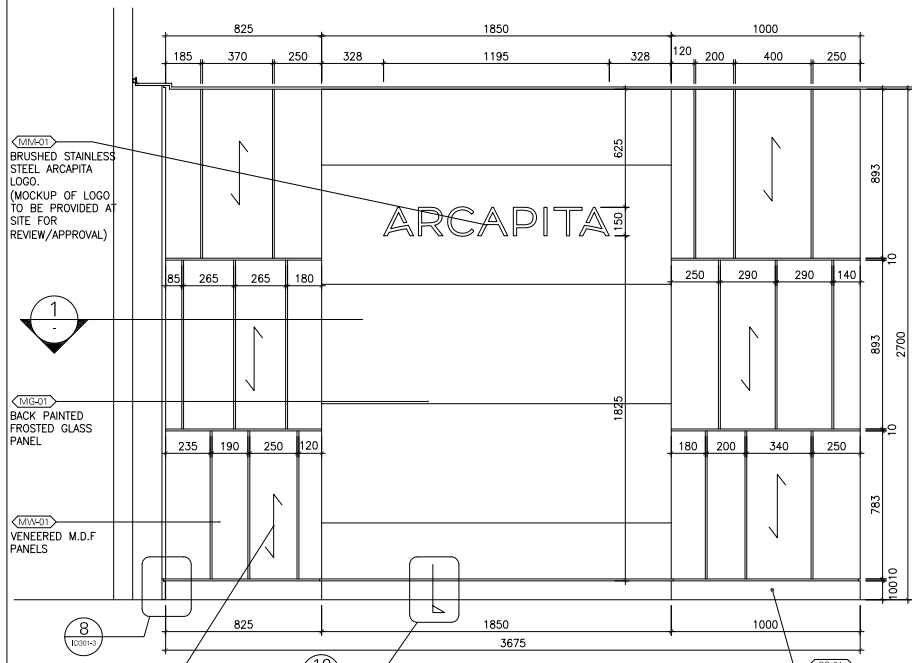

2 ELEVATION
SCALE 1:20

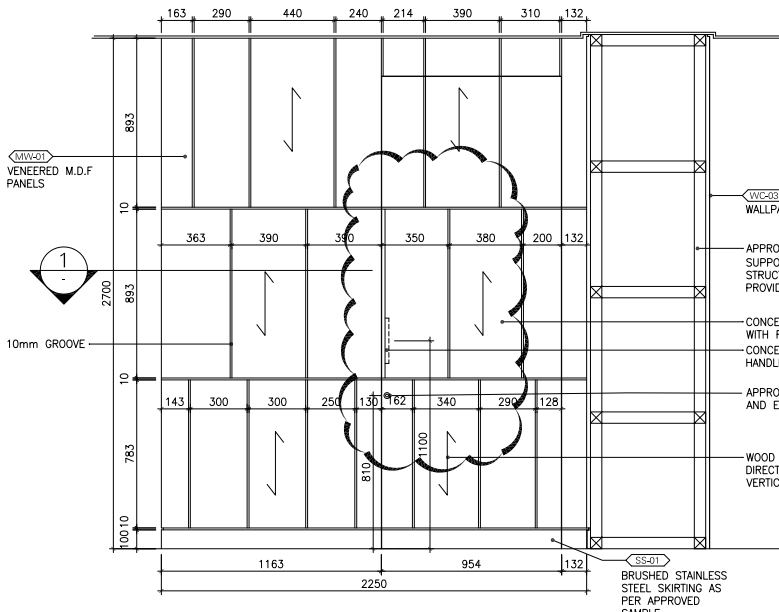

3 ELEVATION
SCALE 1:20

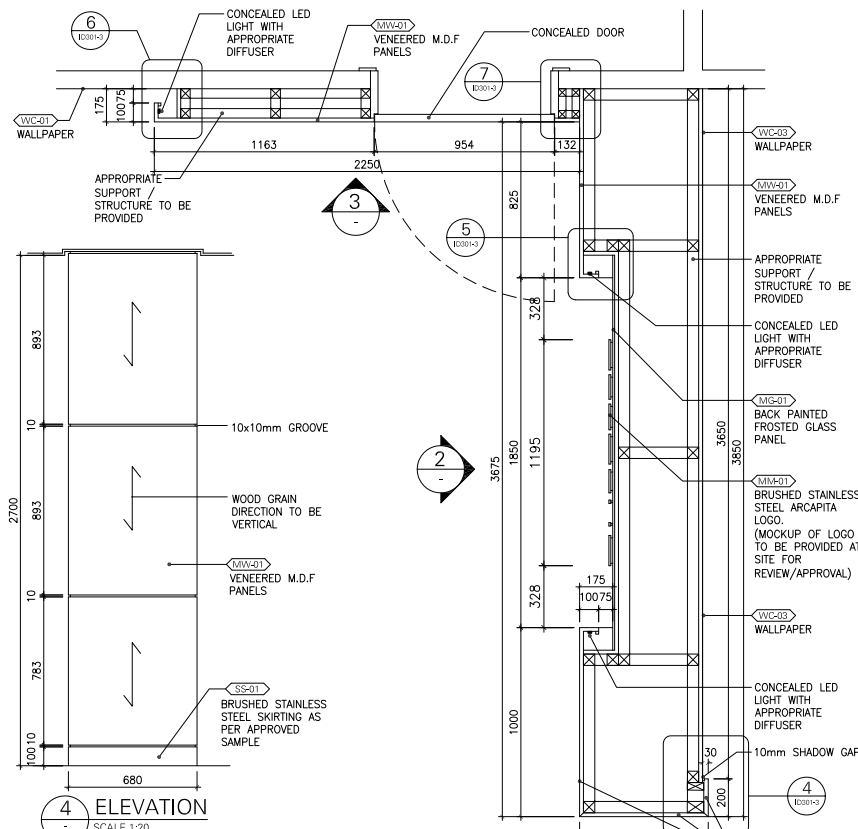

1 FEATURE WALL SECTION PLAN
SCALE 1:20

GENERAL NOTES

1. This drawing shall be read in conjunction with all other relevant architectural, structural & electrical drawings including those of other consultants.
2. It is the responsibility of contractors & manufacturers to check all relevant site dimensions prior to the start of construction or manufacture.
3. All materials and components must be installed on site in accordance with manufacturer's instructions, shop drawings and standard details.
4. All dimensions are in millimeters unless noted otherwise.
5. Full working drawings, specifications and samples are to be provided by Contractor/Supplier for approval prior to manufacture.








FINISHES

* Please Refer to Finishing Schedule for full specifications:
ARC08-1-3 FIN


KEY PLAN




A	REV. WITH CLOUD	AC	AM	SM	2022.10.28
X	INITIAL ISSUE	MP	AM	SM	2022.08.11
REV.#	GENERAL NOTES	DRAWN BY	CHECKED BY	APPROVED BY	DATE
PROJECT TITLE					REFERENCE
ARC - ATLANTA					ARC08
					G
DRAWING TITLE					
RECEPTION (1-001) PLAN AND ELEVATIONS AND BACK WALL DETAILS					
DRAWING NUMBER					REVISION
ID-301-1					A
SCALE	FORMAT	ADDITIONAL NOTES		DESIGN DEVELOPMENT	
1:50 / 1:20	A1				
					
SIMA MALAK + ALSSAMOURE DESIGN ASSOCIATES					
P.O. Box 15707 - Riyadh 11454 KSA Tel. 01 441 4963 - Fax. 01 441 3867 simals@simals.com					

©SIMA MALAK + ALSSAMOURE DESIGN ASSOCIATES () 2003
This document including all drawing and text is the property and copyright of SIMA MALAK + ALSSAMOURE DESIGN ASSOCIATES for use solely with respect to this Project and shall not be copied or reproduced by any means except by agreement in writing from SIMA MALAK + ALSSAMOURE DESIGN ASSOCIATES.

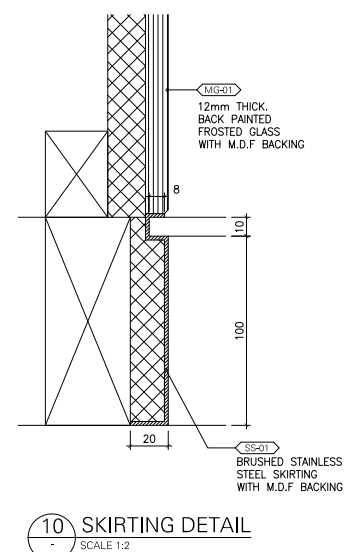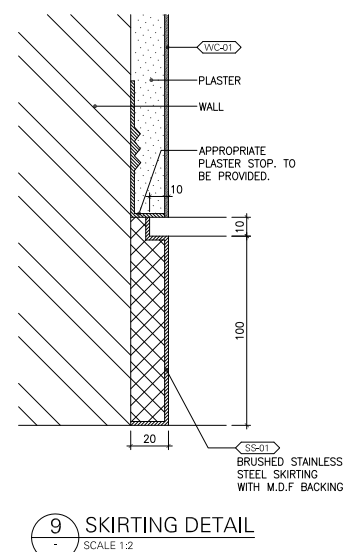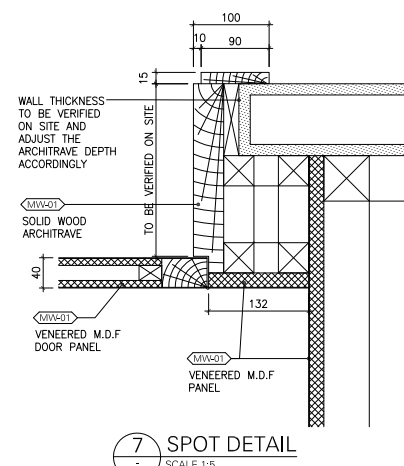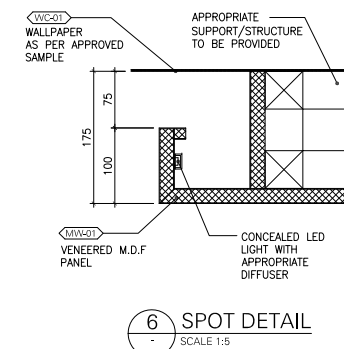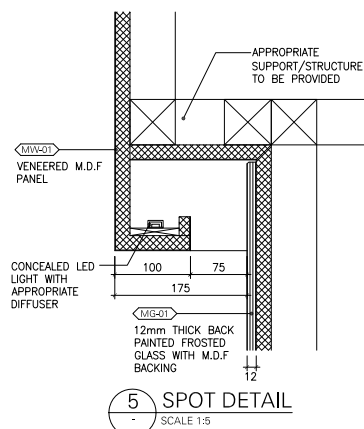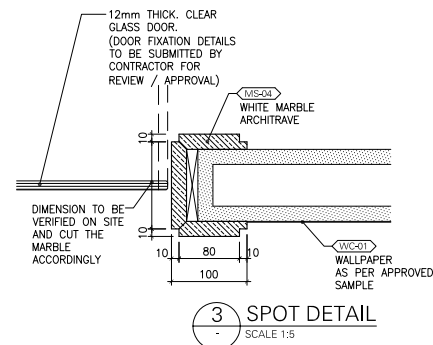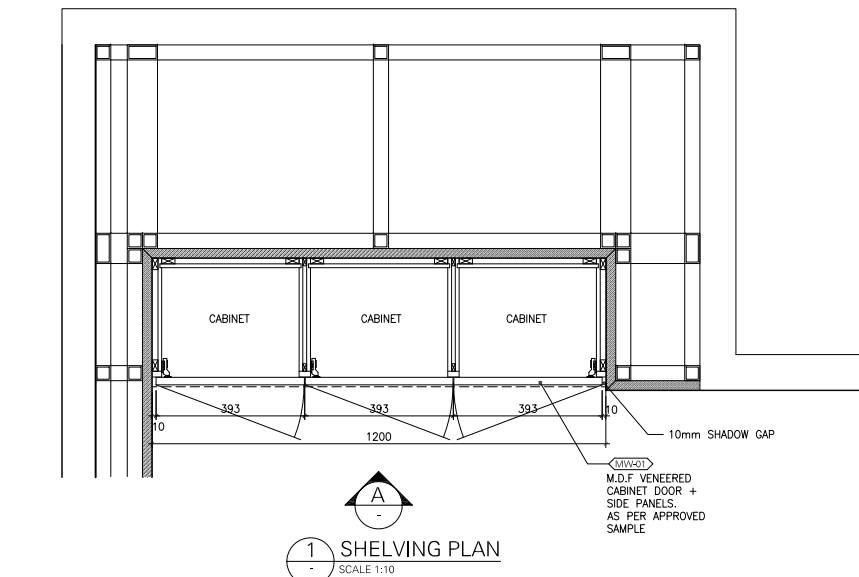

- * REQUIREMENTS FOR ALL DEVICES AND CABLE MANAGEMENT TO BE VERIFIED WITH IT DEPARTMENT/CONSULTANT.

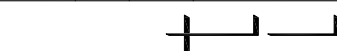KEY PLAN							
X	INITIAL ISSUE	MP	AM	SM	2022.08.		
REV.#	GENERAL NOTES	DRAWN BY	CHECKED BY	APPROVED BY		DATE	
PROJECT TITLE						REFERENCE	
ARC - ATLANTA						ARCO G	
DRAWING TITLE							
RECEPTION (1-001) DETAILS							
DRAWING NUMBER						REVISION	
ID-301-3						-	
SCALE	FORMAT	ADDITIONAL NOTES		DESIGN DEVELOPMENT			
1:10	A1						
							
SIMA MALAK + ALSSAMOURE DESIGN ASSOCIATES							
P.O. Box 15707 - Riyadh 11454 KSA Tel. 01 441 4963 - Fax. 01 441 3867 simal@simals.com							

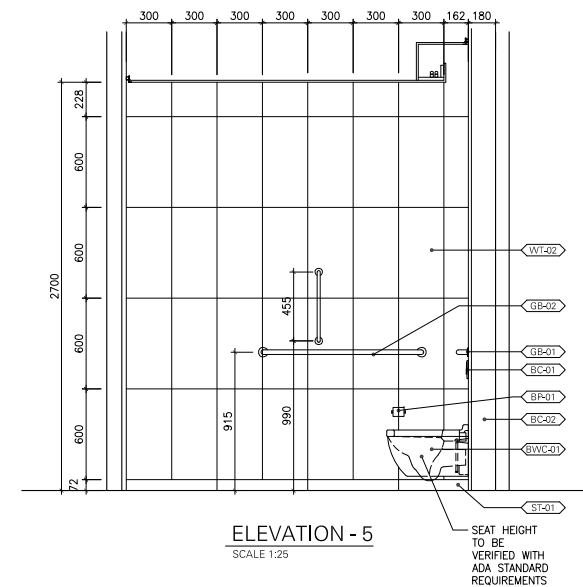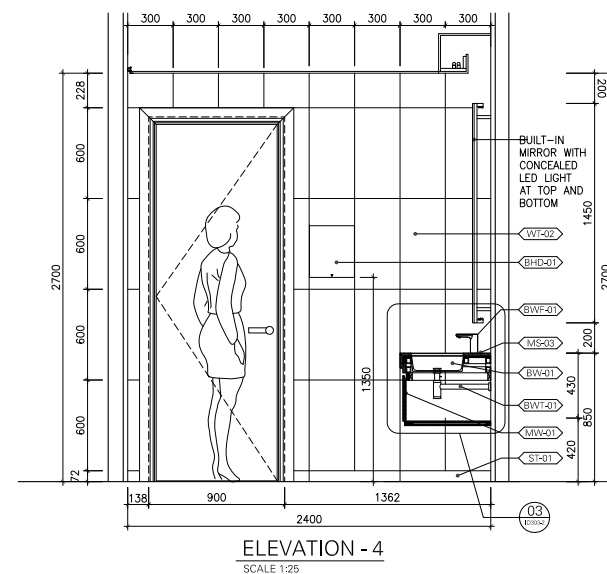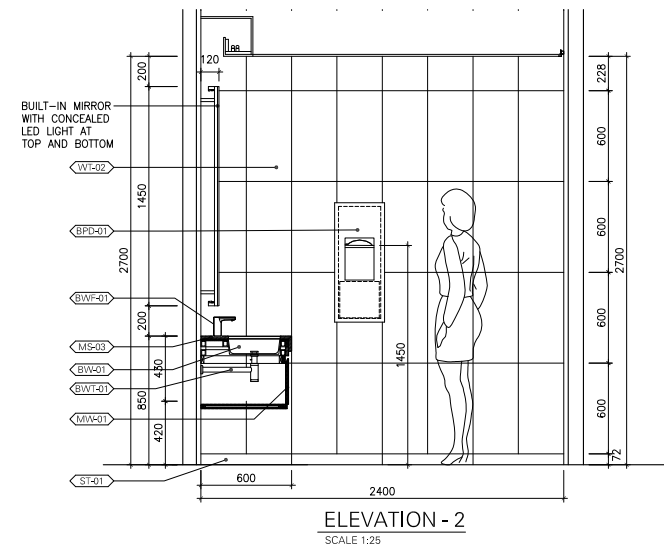


- ## GENERAL NOTES
1. This drawing shall be read in conjunction with all other relevant architectural, structural & electrical drawings including those of other consultants.
 2. It is the responsibility of contractors & manufacturer to check all relevant site dimensions prior to the start of construction or manufacture.
 3. All materials and components must be installed on site in accordance with manufacturer's instructions , shop drawings and standard details.
 4. All dimensions are in millimeters unless noted otherwise.
 5. Full working drawings, specifications and samples are to be provided by Contractor/Supplier for approval prior to manufacture.
 6. Appropriate slope for the flooring to the drain to be provided by Contractor.
- ### NOTES FOR MANUFACTURER:
- * Construction methods shown on drawings are suggested methods only.
 - * All Fixing & Screws to be concealed. If not possible manufacturer to consult with designers before manufacture.
 - * All site dimensions to be confirmed by contractor prior to the manufacture of items.
 - * All materials used in bathrooms to be water resistant, moisture, rust and mould treated such as marine ply , stainless steel, aluminum or equivalent.
 - * All joints to be water sealed and water proof membrane to be provided as required.
 - * All glass and mirrors to have polished smooth edges all round.
 - * All Bathrooms, washrooms floors and steps to be in Hond non slip finish.

1. Full working drawings, specifications and samples are to be provided by Contractor/Supplier for approval prior to manufacture.
2. Please Refer to Finishing Schedule and Sanitary Schedule for full specifications:
ARC08.1.3.FIN
ARC08.1.3.WC-01

1. All positions of sanitary accessories including towel rails, mirrors & artwork etc. to be confirmed on site and fixed after final approval.
2. Finishes will continue behind loose furniture fixtures, ie. mirrors and art works etc.

TYPICAL SOCKET POSITIONS:

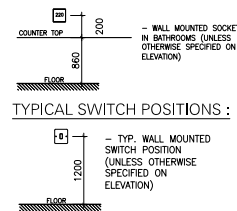

X	INITIAL ISSUE	MP	AM	SM	2022.07.18	
REV.#	GENERAL NOTES	DRAWN BY	CHECKED BY	APPROVED BY	DATE	
PROJECT TITLE					REFERENCE	
ARCAPITA - ATLANTA					ARC08 G	


DRAWING NUMBER	REVISION
ID-303-1	-

SCALE	FORMAT	ADDITIONAL NOTES	DESIGN DEVELOPMENT
1:25	A1		




SIMA MALAK + ALSSAMOURÉ
DESIGN ASSOCIATES
P.O. Box 15707 - Riyadh 11454 KSA
Tel. 01 441 4963 - Fax. 01 441 3867
simals@simals.com


©SIMA MALAK + ALSSAMOURE DESIGN ASSOCIATES (مسور) 2003
This document including all drawing and text is the property and
copyright of SIMA MALAK + ALSSAMOURE DESIGN ASSOCIATES for
use solely with respect to this Project and shall not be copied or
reproduced by any means except by agreement in writing from
SIMA MALAK + ALSSAMOURE DESIGN ASSOCIATES.

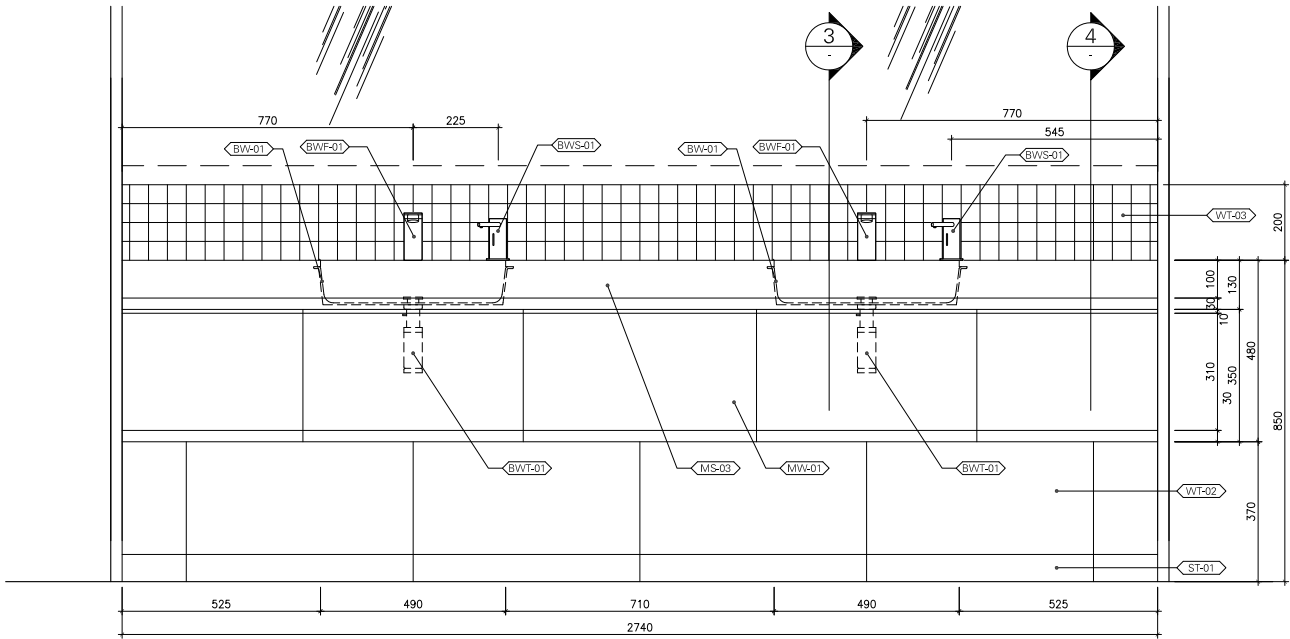


2 VANITY ELEVATION
SCALE 1:10

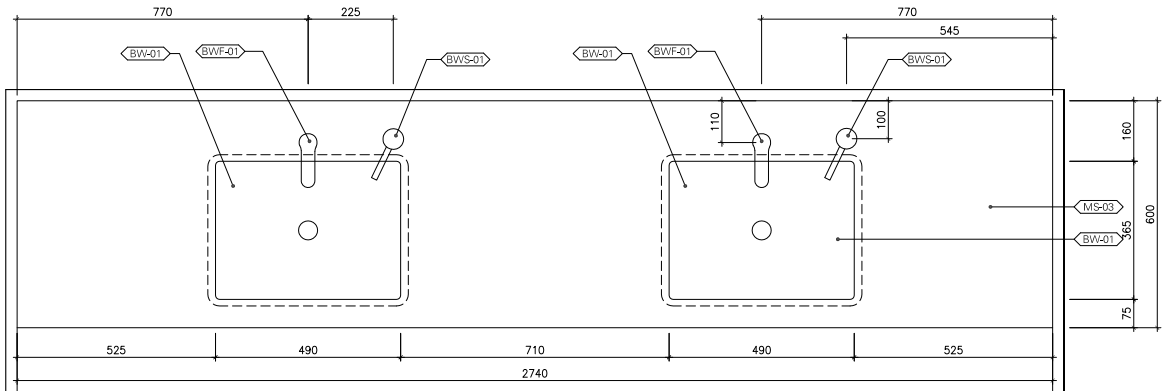

1 VANITY PLAN
SCALE 1:10

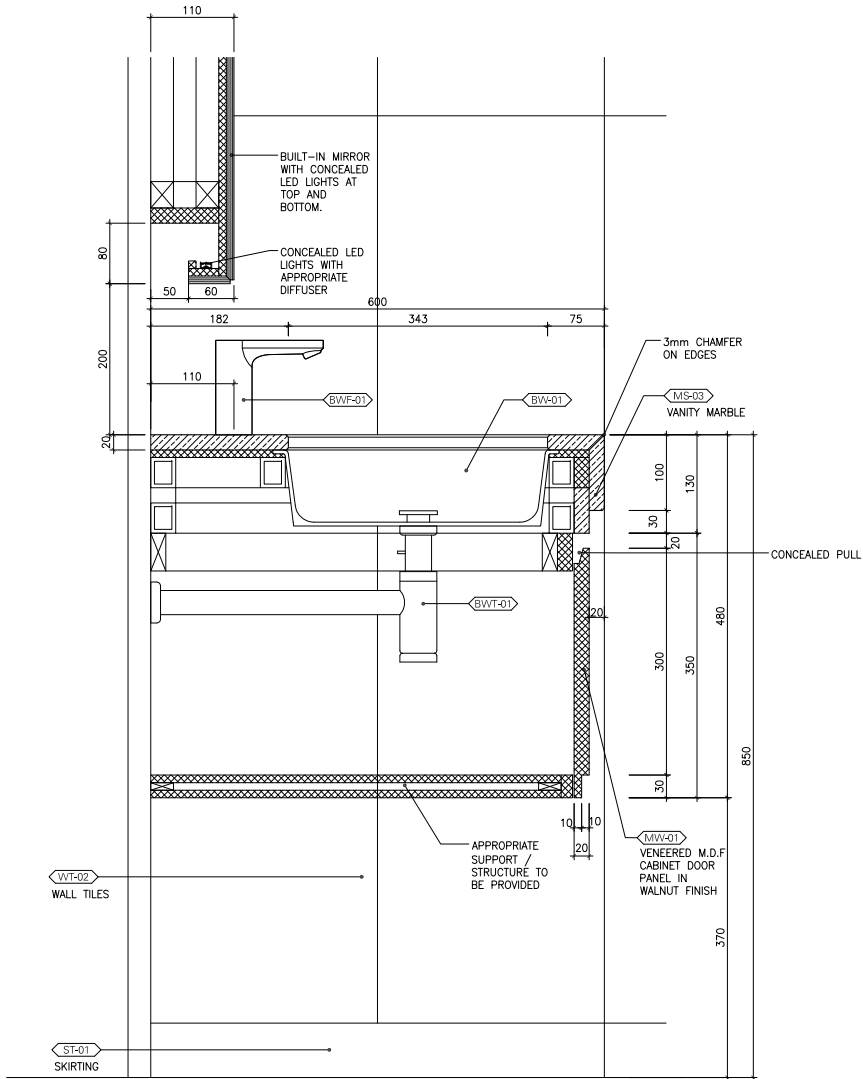

3 VANITY SECTION
SCALE 1:5

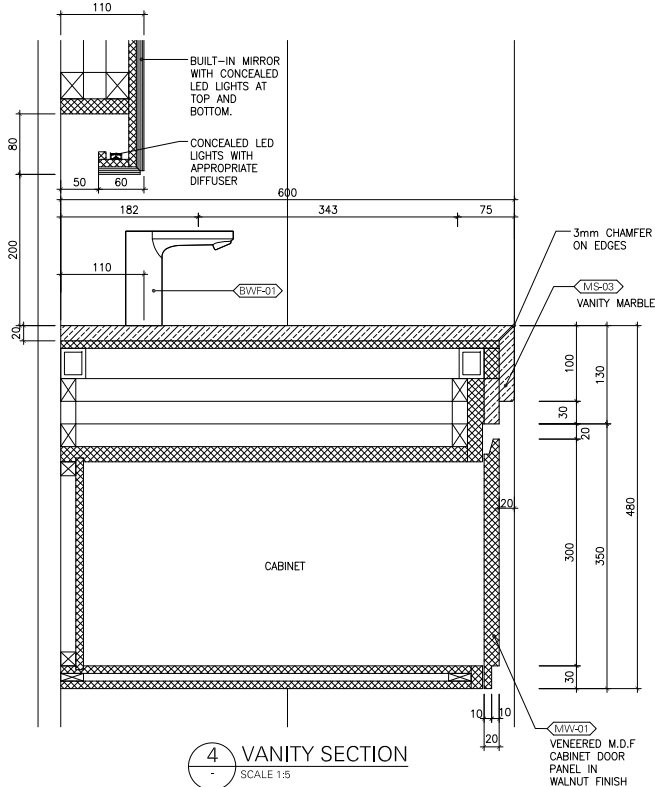

4 VANITY SECTION
SCALE 1:5

GENERAL NOTES

1. This drawing shall be read in conjunction with all other relevant architectural, structural & electrical drawings including those of other consultants.
2. It is the responsibility of contractors & manufacturers to check all relevant site dimensions prior to the start of construction or manufacture.
3. All materials and components must be installed on site in accordance with manufacturer's instructions, shop drawings and standard details.
4. All dimensions are in millimeters unless noted otherwise.
5. Full working drawings, specifications and samples are to be provided by Contractor/Supplier for approval prior to manufacture.
6. Appropriate slope for the flooring to the drain to be provided by Contractor.

NOTES FOR MANUFACTURER:

- * Construction methods shown on drawings are suggested methods only.
- * All Fixing & Screws to be concealed. If not possible manufacturer to consult with designers before manufacture.
- * All site dimension to be confirmed by contractor prior to the manufacture of items.
- * All materials used in bathrooms to be water resistant, moisture, rust and mould treated such as marine ply, stainless steel, aluminum or equivalent.
- * All joints to be water sealed and water proof membrane to be provided as required.
- * All glass and mirrors to have polished smooth edges all round.
- * All Bathrooms, washrooms floors and steps to be in Hard non slip finish.

FINISHES

1. Full working drawings, specifications and samples are to be provided by Contractor/Supplier for approval prior to manufacture.
2. Please Refer to Finishing Schedule and Sanitary Schedule for full specifications:
ARC08.1.3.FIN
ARC08.1.3.WC-01

ACCESSORIES

1. All positions of sanitary accessories including towel rails, mirrors & artwork etc, to be confirmed on site and fixed after final approval.
2. Finishes will continue behind loose furniture fixtures, ie, mirrors and art works etc.

KEY PLAN

INITIAL ISSUE	MP	AM	SM	2022.08.08
REV.#	GENERAL NOTES	DRAWN BY	CHECKED BY	APPROVED BY

PROJECT TITLE

ARCAPITA - ATLANTA

DRAWING TITLE

WASHROOM (1-006)
VANITY DETAILS

DRAWING NUMBER

ID-303-2

SCALE

1:10, 1:5

FORMAT


A1

ADDITIONAL NOTES

DESIGN DEVELOPMENT

**SIMA MALAK + ALSSAMOURE
DESIGN ASSOCIATES**
P.O. Box 15707 - Riyadh 11454 KSA
Tel. 01 441 4963 - Fax. 01 441 3867
simals@simals.com

©SIMA MALAK + ALSSAMOURE DESIGN ASSOCIATES () 2003
This document including all drawing and text is the property and
copyright of SIMA MALAK + ALSSAMOURE DESIGN ASSOCIATES for
use solely with respect to this Project and shall not be copied or
reproduced by any means except by agreement in writing from
SIMA MALAK + ALSSAMOURE DESIGN ASSOCIATES.

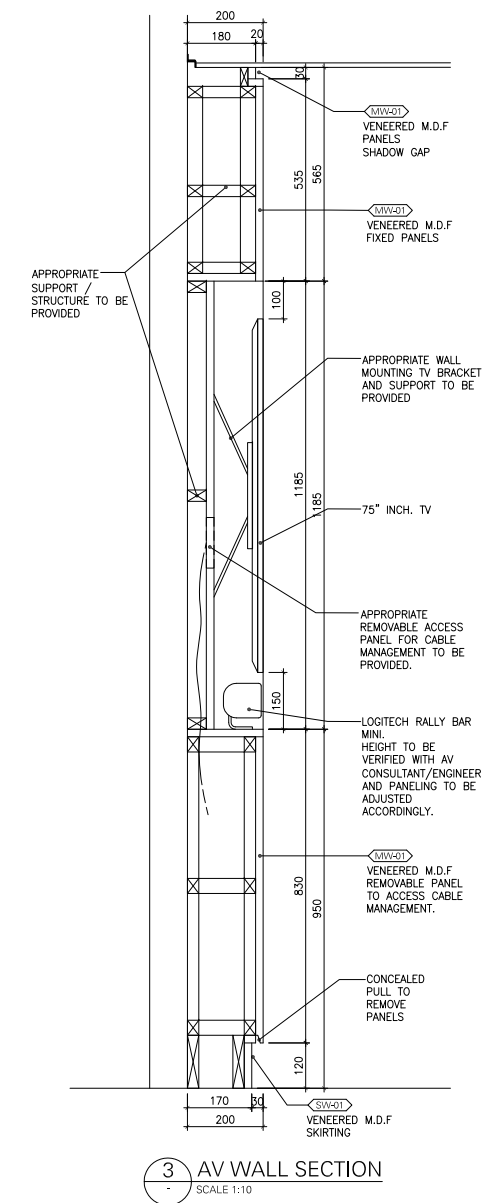

- | <u>GENERAL NOTES</u> | |
|----------------------|---|
| 1. | This drawing shall be read in conjunction with all other relevant architectural, structural & electrical drawings including those of other consultants. |
| 2. | It is the responsibility of contractors & manufacturers to check all relevant site dimensions prior to the start of construction or manufacture. |
| 3. | All materials and components must be installed on site in accordance with manufacturer's instructions, shop drawings and standard details. |
| 4. | All dimensions are in millimeters unless noted otherwise. |
| 5. | Full working drawings, specifications and samples are to be provided by Contractor/Supplier for approval prior to manufacture. |

NOTES FOR MANUFACTURER:

- * FULL REQUIREMENTS FOR AV EQUIPMENT TO BE CO-ORDINATED WITH AV CONSULTANT / ENGINEER.
- * HEIGHT OF THE TV AND CAMERA TO BE VERIFIED WITH AV CONSULTANT AND PANELING TO BE ADJUSTED ACCORDINGLY.

NOTES :

- * Construction methods shown on drawings are suggested methods only.
- * All Fixing & Screws to be concealed. If not possible manufacturer to consult with designers before manufacture.
- * All site dimension to be confirmed by contractor prior to the manufacture of items.

FINISHES

1. Full working drawings, specifications and samples are to be provided by Contractor/Supplier for approval prior to manufacture.
 2. Please Refer to Finishing Schedule for full specifications:
- ARC08-1-3 FIN

KEY PLAN

	INITIAL ISSUE	MP	AM	SM	2022.08.09
---	---------------	----	----	----	------------

REV.#	GENERAL NOTES	DRAWN BY	CHECKED BY	APPROVED BY	DATE
PROJECT TITLE					REFERENCE

ARC - ATLANTA	ARC08
	G

DRAWING TITLE

MEETING ROOM (1-010)

AV WALL PLAN ELEVATION AND SECTIONS

DRAWING NUMBER	REVISION


ID-304			
SCALE	FORMAT	ADDITIONAL NOTES	DESIGN DEVELOPMENT
1:10	A1		



SIMA MALAK + ALSSAMOURE
DESIGN ASSOCIATES



P.O. Box 15707 - Riyadh 11454 KSA
Tel. 01 441 4963 - Fax. 01 441 3867
simals@simals.com

©SIMA MALAK + ALSSAMOURI DESIGN ASSOCIATES (مسور) 2003
This document including all drawing and text is the property and
copyright of SIMA MALAK + ALSSAMOURI DESIGN ASSOCIATES for
use solely with respect to this Project and shall not be copied or
reproduced by any means except by agreement in writing from
SIMA MALAK + ALSSAMOURI DESIGN ASSOCIATES.

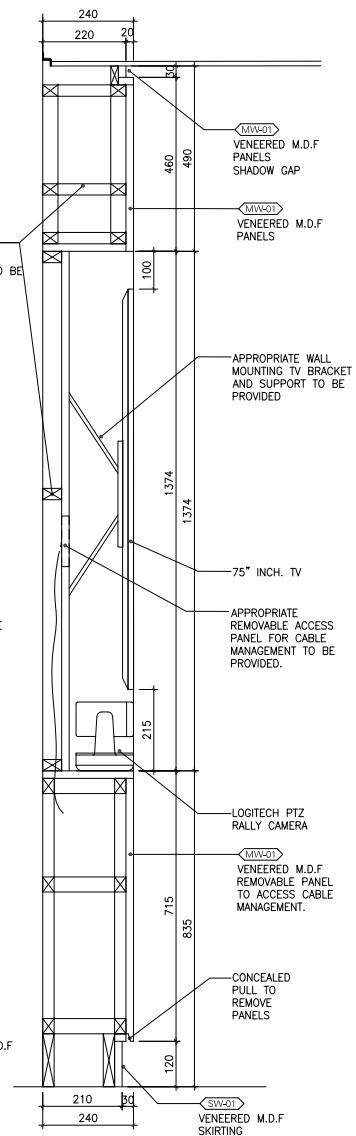

©SIMA MALAK + ALSSAMOUR DESIGN ASSOCIATES (—) 2003
This document including all drawing and text is the property and
copyright of SIMA MALAK + ALSSAMOUR DESIGN ASSOCIATES for
use solely with respect to this Project and shall not be copied or
reproduced by any means except by agreement in writing from
SIMA MALAK + ALSSAMOUR DESIGN ASSOCIATES.

PLAN (KITCHENETTE 1-028)

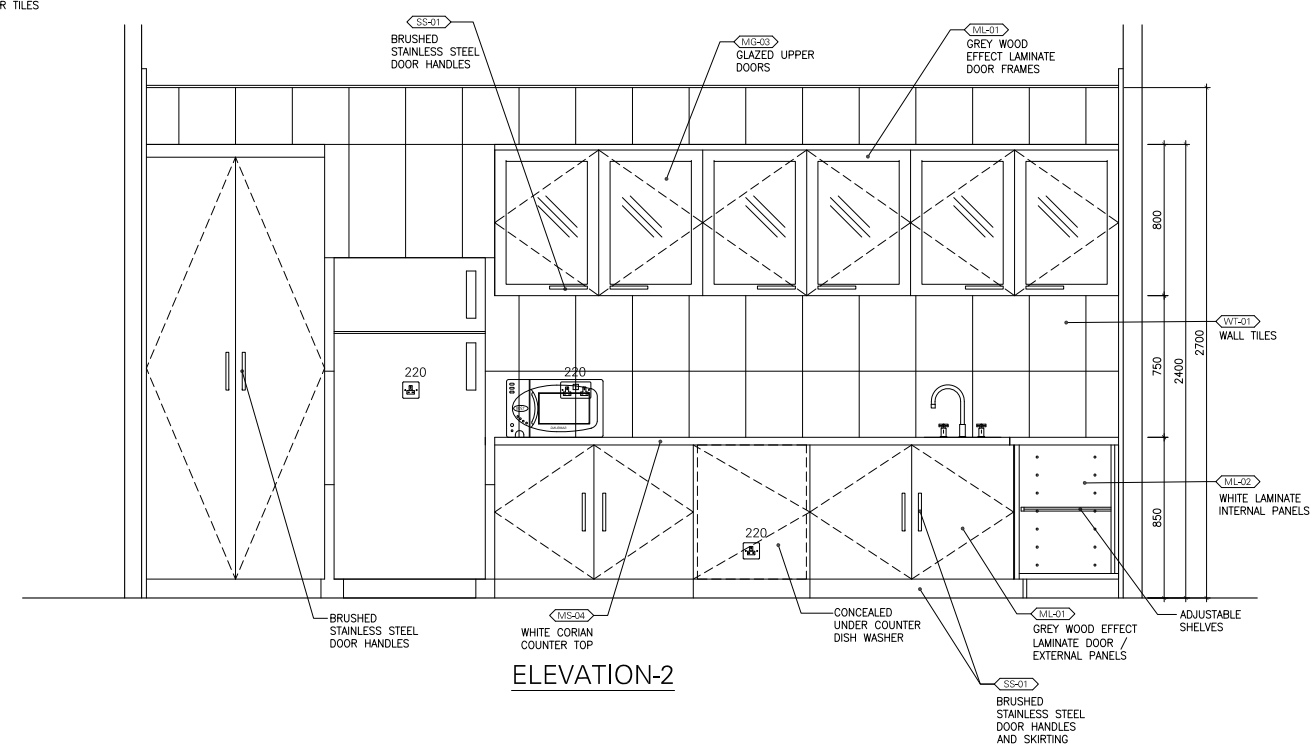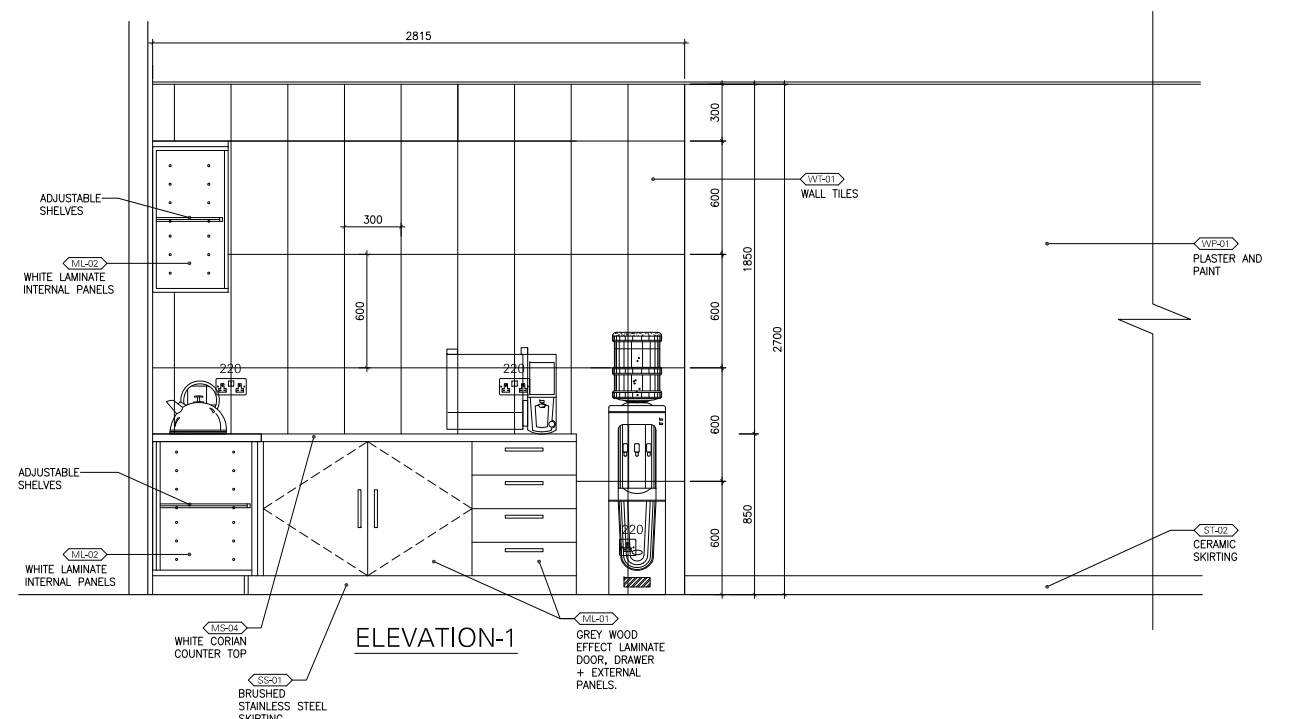



GENERAL NOTES

1. This drawing shall be read in conjunction with all other relevant architectural, structural & electrical drawings including those of other consultants.
2. It is the responsibility of contractors & manufacturers to check all relevant site dimensions prior to the start of construction or manufacture.
3. All materials and components must be installed on site in accordance with manufacturer's instructions, shop drawings and standard details.
4. All dimensions are in millimeters unless noted otherwise.
5. Full working drawings, specifications and samples are to be provided by Contractor/Supplier for approval prior to manufacture.

NOTES FOR MANUFACTURER:

1. Full working drawings, specifications and samples are to be provided by Contractor/Supplier for approval prior to manufacture.

TYPICAL SOCKET POSITIONS:

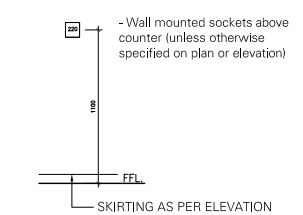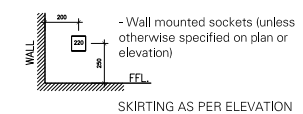

KEY PLAN

X	INITIAL ISSUE	AC	AM	SM	2022.08.09	
REV.#	GENERAL NOTES	DRAWN BY	CHECKED BY	APPROVED BY	DATE	
PROJECT TITLE				REFERENCE		
ARCAPITA - ATLANTA				ARC08 G		

KITCHENETTE (1-028) PLAN AND ELEVATIONS

DRAWING NUMBER			REVISION	
ID-306				
SCALE	FORMAT	ADDITIONAL NOTES	DESIGN DEVELOPMENT	
1:20	A1			



SIMA MALAK + ALSSAMOURÉ
DESIGN ASSOCIATES
P.O. Box 15707 - Riyadh 11454 KSA
Tel. 01 441 4963 - Fax. 01 441 3867
simals@simals.com

©SIMA MALAK + ALSSAMOURÉ DESIGN ASSOCIATES (شركة) 2003
This document including all drawing and text is the property and
copyright of SIMA MALAK + ALSSAMOURÉ DESIGN ASSOCIATES for
use solely with respect to this Project and shall not be copied or
reproduced by any means except by agreement in writing from
SIMA MALAK + ALSSAMOURÉ DESIGN ASSOCIATES.

This drawing shall be read in conjunction with all other relevant architectural, structural & electrical drawings including those of other consultants.

It is the responsibility of contractors & manufacturers to check all relevant site dimensions prior to the start of construction or manufacture.

All materials and components must be installed on site in accordance with manufacturer's instructions , shop drawings and standard details.


All dimensions are in millimeters unless noted otherwise.


Full working drawings, specifications and samples are to be provided by Contractor/Supplier for approval prior to manufacture.

1. Full working drawings, specifications and samples are to be provided by Contractor/Supplier for approval prior to manufacture.


- Wall mounted sockets (unless otherwise specified on plan or elevation)

SKIRTING AS PER ELEVATION

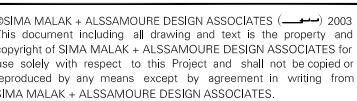


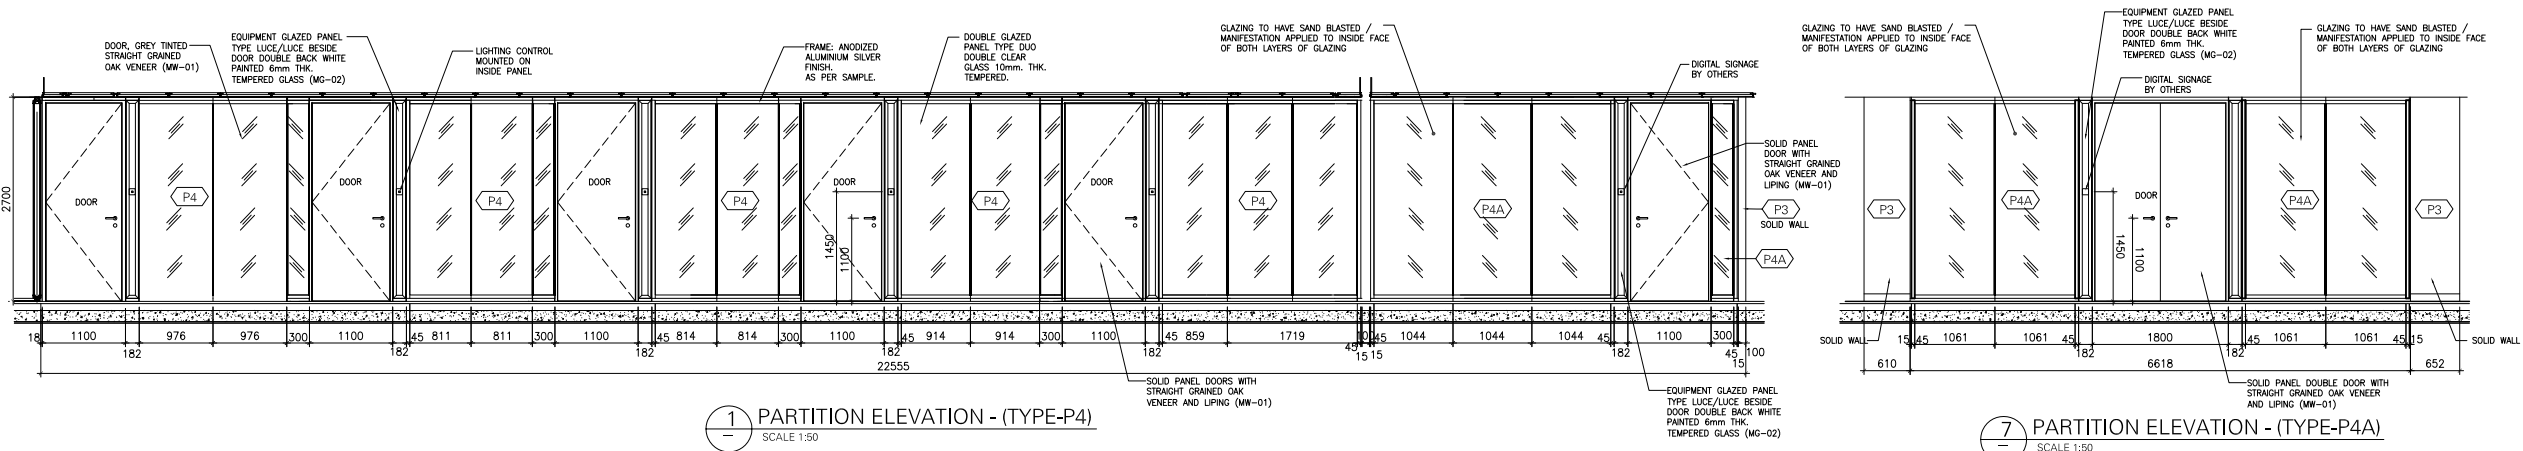


1 PARTITION ELEVATION - (TYPE-P4)
SCALE 1:50

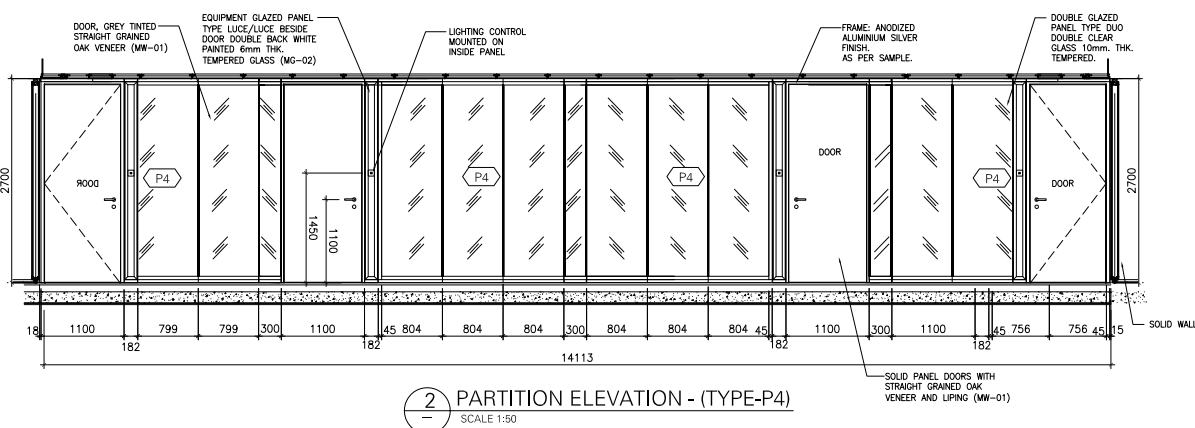


2 PARTITION ELEVATION - (TYPE-P4)
SCALE 1:50

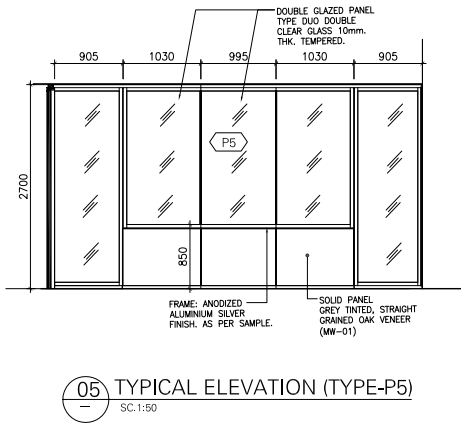


05 TYPICAL ELEVATION (TYPE-P5)
SC.1:50

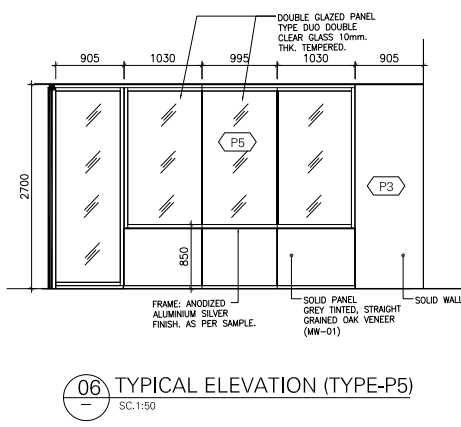

06 TYPICAL ELEVATION (TYPE-P5)
SC.1:50

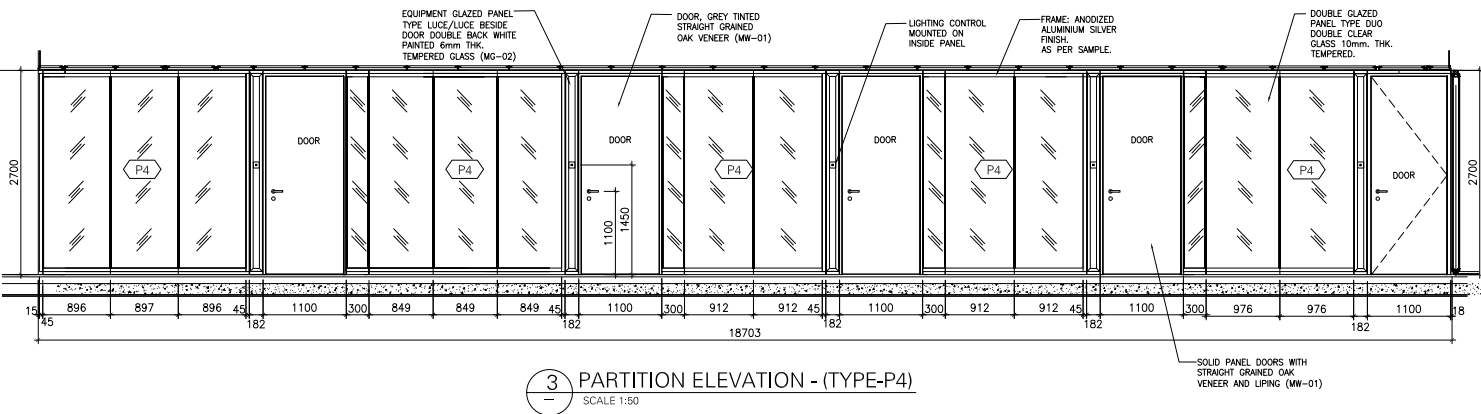

3 PARTITION ELEVATION - (TYPE-P4)
SCALE 1:50

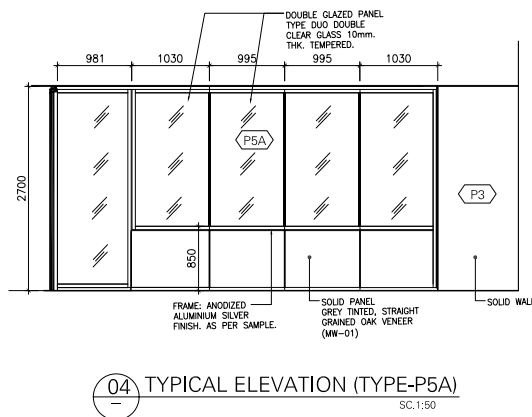

04 TYPICAL ELEVATION (TYPE-P5A)
SC.1:50

GENERAL NOTES

1. This drawing shall be read in conjunction with all other relevant architectural, structural & electrical drawings including those of other consultants.
2. It is the responsibility of contractors & manufacturers to check all relevant site dimensions prior to the start of construction or manufacture.
3. All materials and components must be installed on site in accordance with manufacturer's instructions, shop drawings and standard details.
4. All dimensions are in millimeters unless noted otherwise.
5. Full working drawings, specifications and samples are to be provided by Contractor/Supplier for approval prior to manufacture.

PARTITION TYPE:

P1 - 100mm thick Blockwork.

P3 - Metal stud gypsum wall.

P4 - FULLY GLAZED PARTITION SYSTEM: Double glazed office partition wall system with Aluminum profiles. Fully glazed module. Frame in anodized aluminum silver finish as per approved sample. Equipment panel with back painted glass (MG-02).

P4A - DUO DOUBLE FULLY GLAZED PARTITION SYSTEM: Double glazed office partition wall system with Aluminum profiles. Fully glazed module. Frame in anodized aluminum silver finish as per approved sample. Equipment panel with back painted glass (MG-02) glazing to have sandblasting /manifestation applied with clear horizontal staggered banding as per detail.

P5 - PARTIALLY GLAZED PARTITION SYSTEM: Double glazed office partition wall system with Aluminum profiles. Partially glazed module consisting of double glazed upper panels and wood veneered lower panels (MW-01) with insulation, frame in anodized aluminum silver finish as per approved sample.

P5A - PARTIALLY GLAZED PARTITION SYSTEM: Double glazed office partition wall system with Aluminum profiles. Partially glazed module consisting of double glazed upper panels and wood veneered lower panels (MW-01) with insulation, frame in anodized aluminum silver finish as per approved sample.

P8 - Metal stud Gypsum partition with fitted A/V wall consisting of wood paneling / Cabinetry.

NOTES:

- *. All doors are to be solid plain leaf with wood veneered.
- *. Partition supplier to conduct their own site survey to obtain asbuilt dimensions and submit plans, elevations and details for approval.






KEY PLAN

A	GEN. REV.	MP	AM	SM	2022.10.27
X	INITIAL ISSUE	AC/MP	AM	SM	2022.08.17
REV.#	GENERAL NOTES	DRAWN BY	CHECKED BY	APPROVED BY	DATE
PROJECT TITLE					REFERENCE
ARC - ATLANTA					ARC08 G

DRAWING TITLE	
PARTITION ELEVATIONS	
DRAWING NUMBER	REVISION
ID-308	A
SCALE	FORMAT
1:50	A1
ADDITIONAL NOTES	DESIGN DEVELOPMENT

SIMA MALAK + ALSSAMOURE
DESIGN ASSOCIATES
P.O. Box 15707 - Riyadh 11454 KSA
Tel. 01 441 4963 - Fax. 01 441 3867
simas@simal.com

©SIMA MALAK + ALSSAMOURE DESIGN ASSOCIATES (شركة) 2003
This document including all drawing and text is the property and copyright of SIMA MALAK + ALSSAMOURE DESIGN ASSOCIATES for use solely with respect to this Project and shall not be copied or reproduced by any means except by agreement in writing from SIMA MALAK + ALSSAMOURE DESIGN ASSOCIATES.

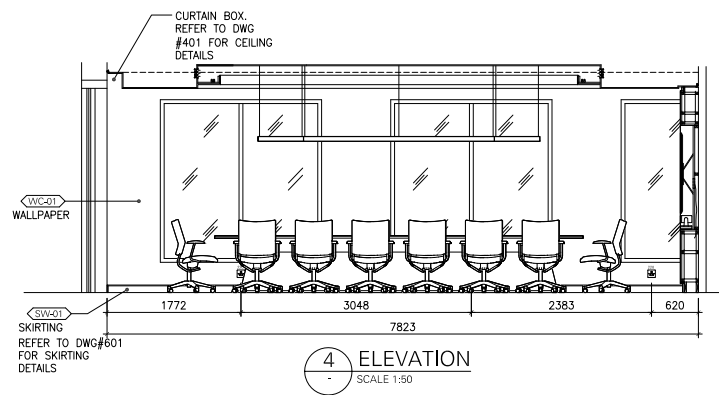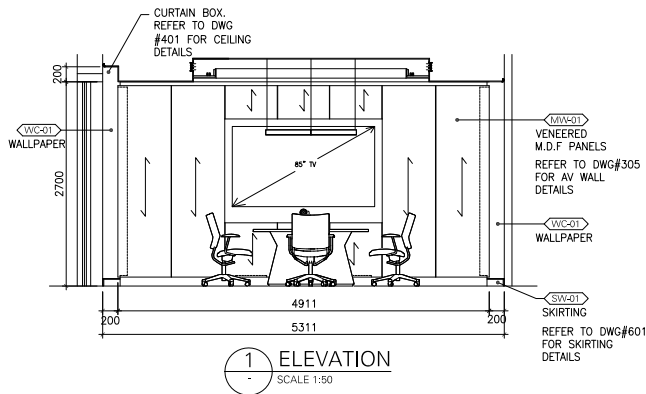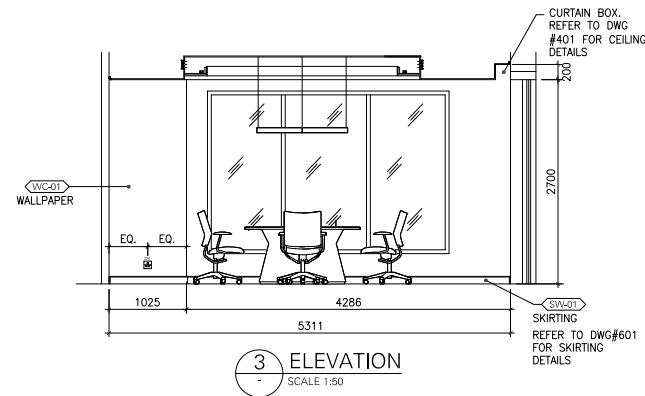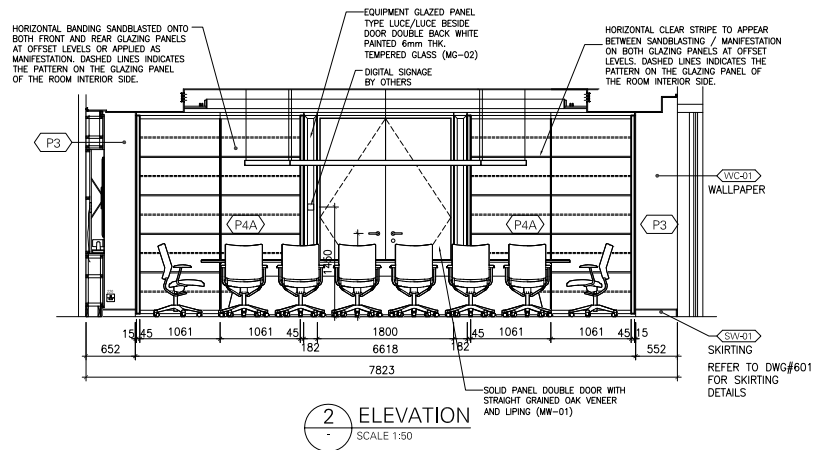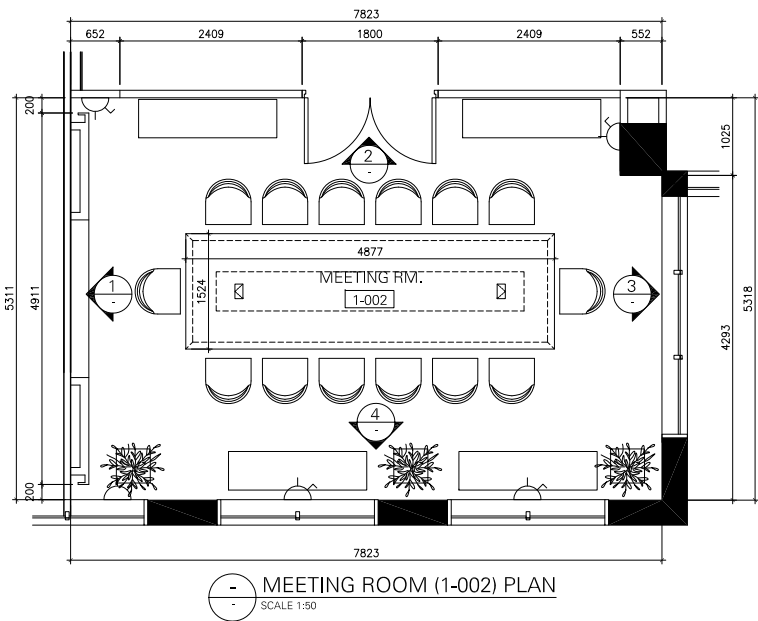

GENERAL NOTES

1. This drawing shall be read in conjunction with all other relevant architectural, structural & electrical drawings including those of other consultants.
2. It is the responsibility of contractors & manufacturers to check all relevant site dimensions prior to the start of construction or manufacture.
3. All materials and components must be installed on site in accordance with manufacturer's instructions, shop drawings and standard details.
4. All dimensions are in millimeters unless noted otherwise.
5. Full working drawings, specifications and samples are to be provided by Contractor/Supplier for approval prior to manufacture.

FINISHES

* Please Refer to Finishing Schedule for full specifications:
ARC08-1-3 FIN


KEY PLAN

REV.#	GENERAL NOTES	DRAWN BY	CHECKED BY	APPROVED BY	DATE
1	INITIAL ISSUE	MP	AM	SM	2022.08.22
PROJECT TITLE					REFERENCE
ARC - ATLANTA					ARC08 G


DRAWING TITLE	
MEETING ROOM (1-002) PLAN AND ELEVATIONS	
DRAWING NUMBER	
ID-309	
REVISION	
-	
SCALE	FORMAT
1:50	A1
ADDITIONAL NOTES	DESIGN DEVELOPMENT

**SIMA MALAK + ALSSAMOURE
DESIGN ASSOCIATES**
P.O. Box 15707 - Riyadh 11454 KSA
Tel. 01 441 4963 - Fax. 01 441 3867
simals@simals.com


©SIMA MALAK + ALSSAMOURE DESIGN ASSOCIATES (شركة) 2003
This document including all drawing and text is the property and
copyright of SIMA MALAK + ALSSAMOURE DESIGN ASSOCIATES for
use solely with respect to this Project and shall not be copied or
reproduced by any means except by agreement in writing from
SIMA MALAK + ALSSAMOURE DESIGN ASSOCIATES.

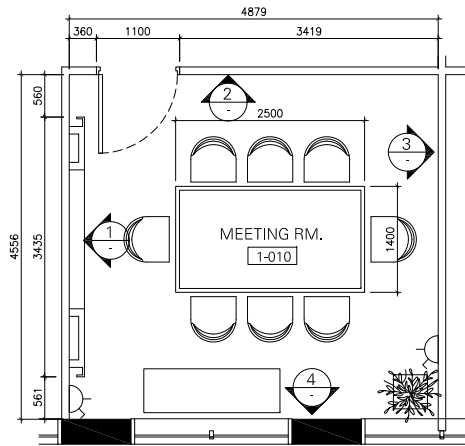


MEETING ROOM (1-010) PLAN
SCALE 1:50

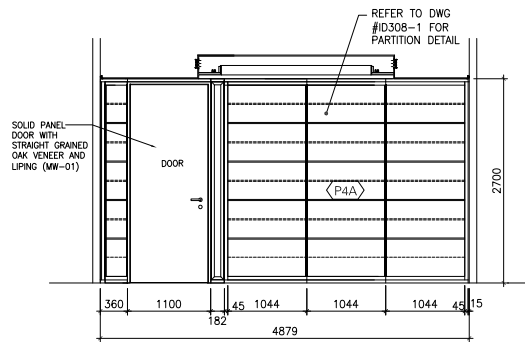


2 ELEVATION
SCALE 1:50

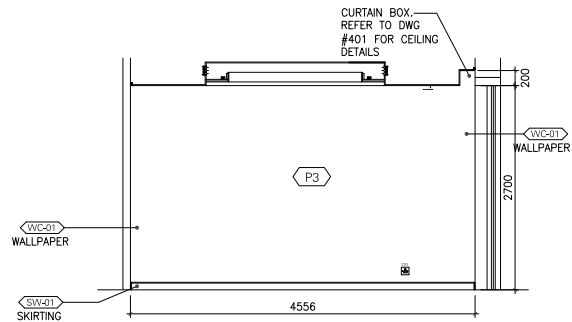

3 ELEVATION
SCALE 1:50

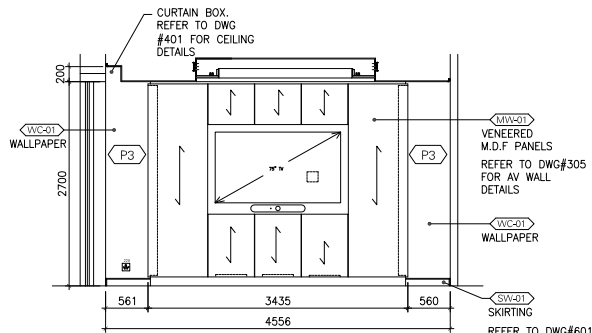

1 ELEVATION
SCALE 1:50

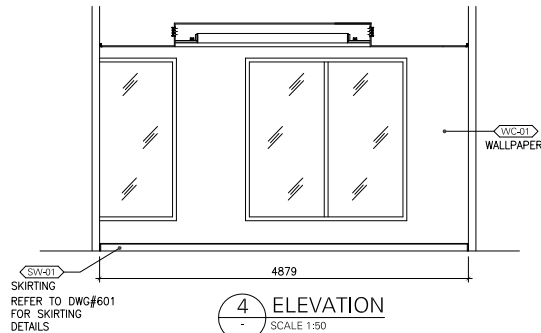

4 ELEVATION
SCALE 1:50

GENERAL NOTES

1. This drawing shall be read in conjunction with all other relevant architectural, structural & electrical drawings including those of other consultants.
2. It is the responsibility of contractors & manufacturers to check all relevant site dimensions prior to the start of construction or manufacture.
3. All materials and components must be installed on site in accordance with manufacturer's instructions, shop drawings and standard details.
4. All dimensions are in millimeters unless noted otherwise.
5. Full working drawings, specifications and samples are to be provided by Contractor/Supplier for approval prior to manufacture.

FINISHES

* Please Refer to Finishing Schedule for full specifications:
ARC08-1-3 FIN

KEY PLAN

INITIAL ISSUE	MP	AM	SM	2022.08.22
REV.#	GENERAL NOTES	DRAWN BY	CHECKED BY	APPROVED BY

PROJECT TITLE	REFERENCE
---------------	-----------

ARC - ATLANTA	ARC08 G
---------------	------------


DRAWING TITLE
MEETING ROOM (1-010) PLAN AND ELEVATIONS

DRAWING NUMBER	REVISION
ID-310	-


SCALE	FORMAT	ADDITIONAL NOTES	DESIGN DEVELOPMENT
1:50	A1		

**SIMA MALAK + ALSSAMOURE
DESIGN ASSOCIATES**
P.O. Box 15707 - Riyadh 11454 KSA
Tel. 01 441 4963 - Fax. 01 441 3867
simals@simals.com


©SIMA MALAK + ALSSAMOURE DESIGN ASSOCIATES (شركة) 2003
This document including all drawing and text is the property and
copyright of SIMA MALAK + ALSSAMOURE DESIGN ASSOCIATES for
use solely with respect to this Project and shall not be copied or
reproduced by any means except by agreement in writing from
SIMA MALAK + ALSSAMOURE DESIGN ASSOCIATES.

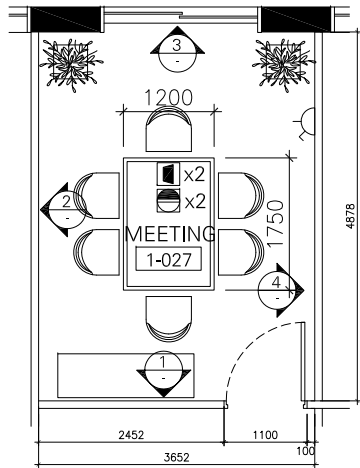


MEETING ROOM (1-027) PLAN
SCALE 1:50

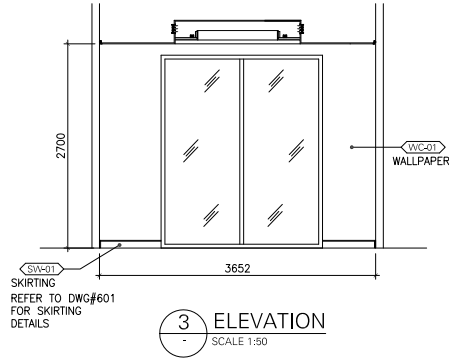


3 ELEVATION
SCALE 1:50

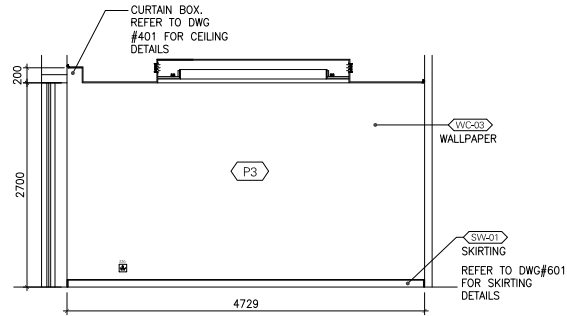

4 ELEVATION
SCALE 1:50

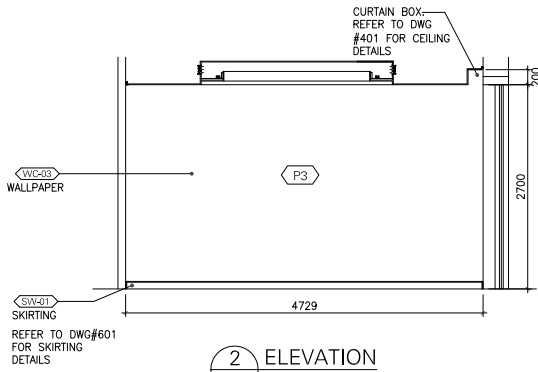

2 ELEVATION
SCALE 1:50

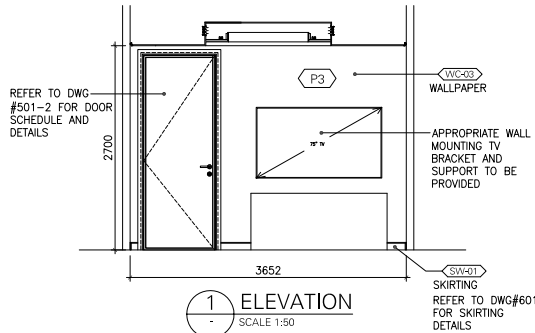

1 ELEVATION
SCALE 1:50

GENERAL NOTES

1. This drawing shall be read in conjunction with all other relevant architectural, structural & electrical drawings including those of other consultants.
2. It is the responsibility of contractors & manufacturers to check all relevant site dimensions prior to the start of construction or manufacture.
3. All materials and components must be installed on site in accordance with manufacturer's instructions, shop drawings and standard details.
4. All dimensions are in millimeters unless noted otherwise.
5. Full working drawings, specifications and samples are to be provided by Contractor/Supplier for approval prior to manufacture.

FINISHES

* Please Refer to Finishing Schedule for full specifications:
ARC08-1-3 FIN

KEY PLAN

INITIAL ISSUE	MP	AM	SM	2022.08.22
REV.#	GENERAL NOTES	DRAWN BY	CHECKED BY	APPROVED BY

PROJECT TITLE	REFERENCE
ARC - ATLANTA	ARC08 G


DRAWING TITLE
MEETING ROOM (1-027) PLAN AND ELEVATIONS

DRAWING NUMBER	REVISION
ID-311	-


SCALE	FORMAT	ADDITIONAL NOTES	DESIGN DEVELOPMENT
1:50	A1		

SIMA MALAK + ALSSAMOURE
DESIGN ASSOCIATES
P.O. Box 15707 - Riyadh 11454 KSA
Tel. 01 441 4963 - Fax. 01 441 3867
simals@simals.com


©SIMA MALAK + ALSSAMOURE DESIGN ASSOCIATES (شركة) 2003
This document including all drawing and text is the property and copyright of SIMA MALAK + ALSSAMOURE DESIGN ASSOCIATES for use solely with respect to this Project and shall not be copied or reproduced by any means except by agreement in writing from SIMA MALAK + ALSSAMOURE DESIGN ASSOCIATES.

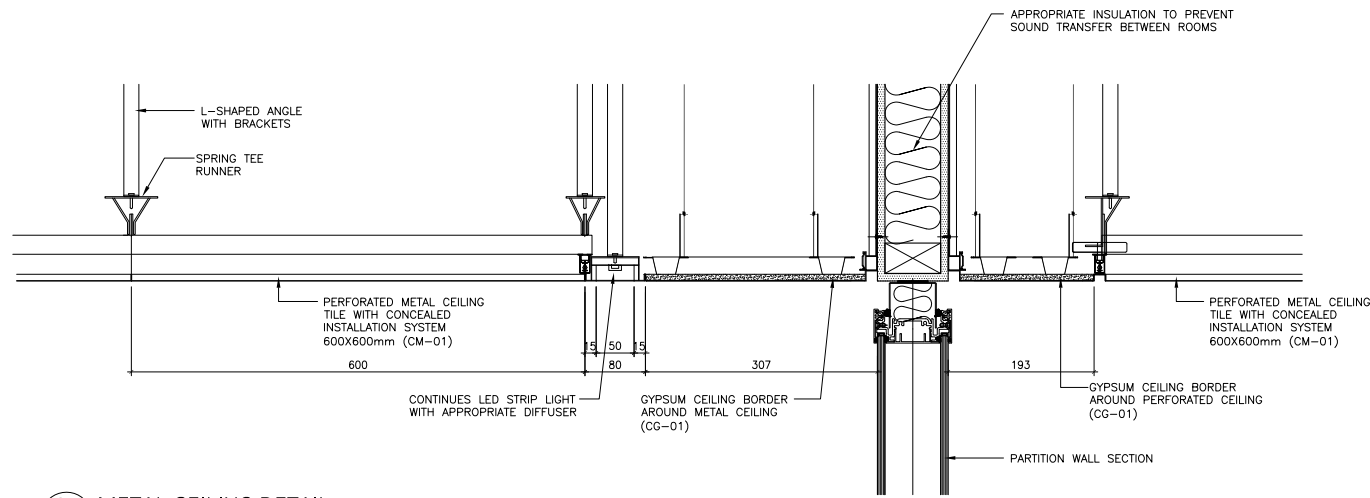


01 METAL CEILING DETAIL
SC. 1:5

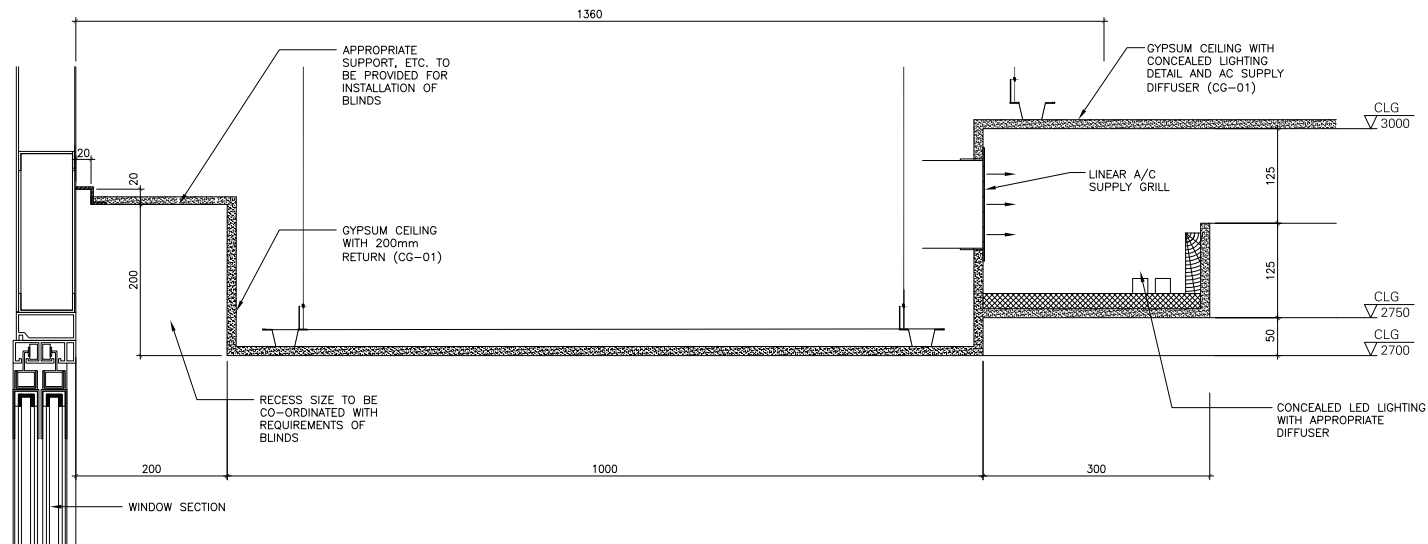


02 TYPICAL GYPSUM CEILING DETAIL WITH CONCEALED LED LIGHT AND CURTAIN BOX @ MEETING ROOMS
SC. 1:5

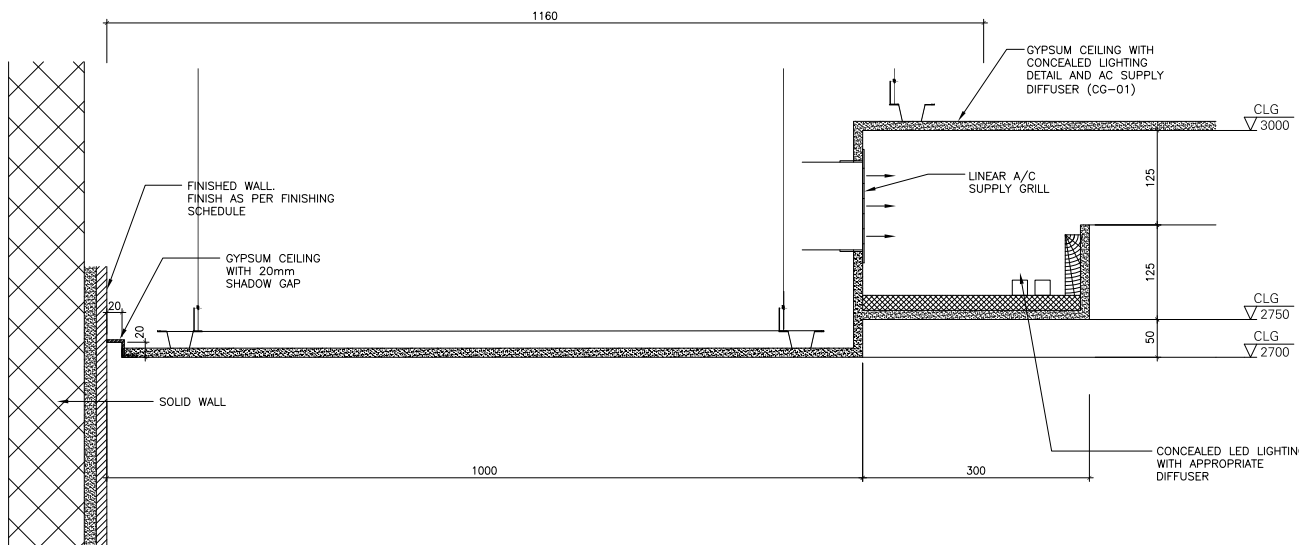


03 TYPICAL GYPSUM CEILING DETAIL WITH CONCEALED LED LIGHT @ RECEPTION
SC. 1:5

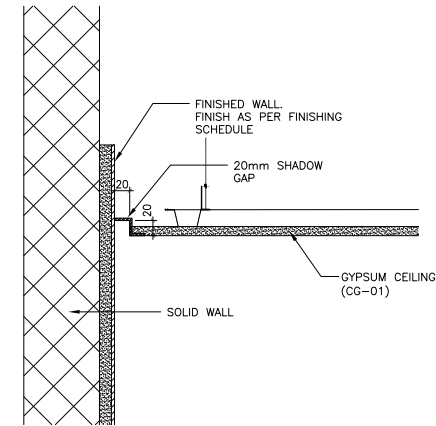

04 TYPICAL GYPSUM FLAT CEILING DETAIL
SC. 1:5

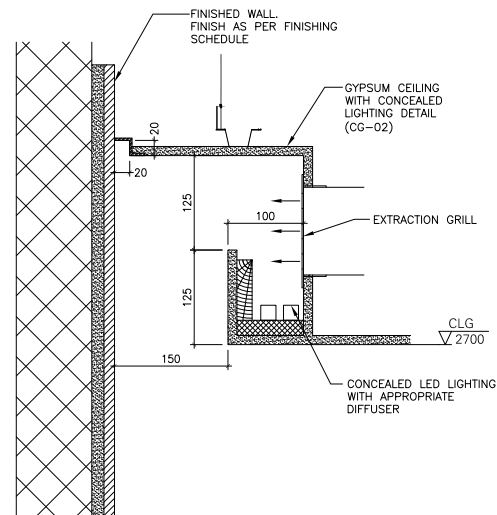

05 CEILING DETAIL WITH CONCEALED LED LIGHTS @ RESTROOM
SC. 1:5

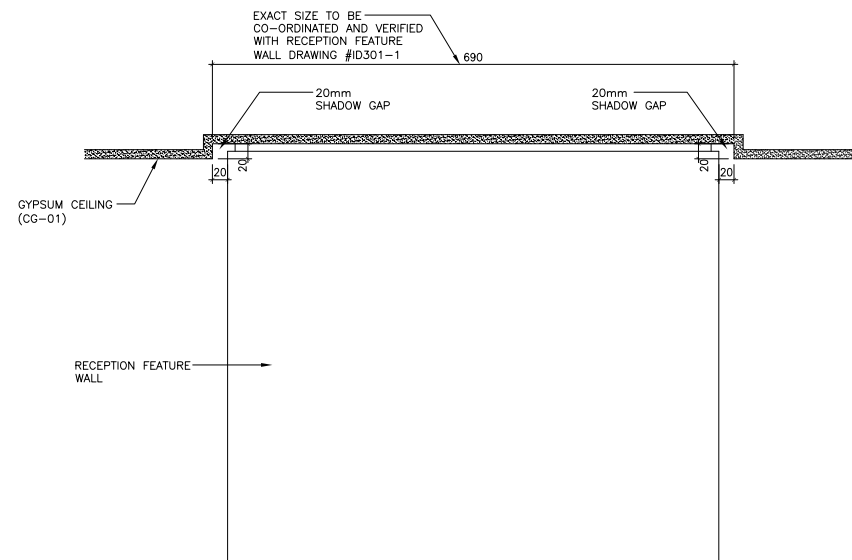

06 DETAIL AT RECEPTION FEATURE WALL
SC. 1:5

GENERAL NOTES

1. This drawing shall be read in conjunction with all other relevant architectural, structural & electrical drawings including those of other consultants.
2. It is the responsibility of contractors & manufacturers to check all relevant site dimensions prior to the start of construction or manufacture.
3. All materials and components must be installed on site in accordance with manufacturer's instructions, shop drawings and standard details.
4. All dimensions are in millimeters unless noted otherwise.
5. Full working drawings, specifications and samples are to be provided by Contractor/Supplier for approval prior to manufacture.

NOTES FOR MANUFACTURE:

- * Construction methods shown on drawings are suggested methods only.
- * Full working drawings and samples are to be provided by contractor for approval prior to manufacture.
- * Please refer to relevant sub consultants drawings for Audio visual, security and I.T. requirements.

FINISHES

- * All Elements of the ceiling including AC Grill and ceiling mounted devices should be Ral 9016.
- * Samples of all finishes are to be provided by the contractor to be approved by the designer prior to manufacture / construction.

Full Shop drawings and details to be provided by Contractor / Manufacturer.


KEY PLAN

INITIAL ISSUE	MP	AM	SM	2022.08.17
REV.#	GENERAL NOTES	DRAWN BY	CHECKED BY	APPROVED BY
PROJECT TITLE	REFERENCE			
ARC - ATLANTA				ARC08 G

DRAWING TITLE	
TYPICAL CEILING DETAILS	
DRAWING NUMBER	REVISION
ID-401	-
SCALE	FORMAT
1:5	A1
ADDITIONAL NOTES	DESIGN DEVELOPMENT

SIMA MALAK + ALSSAMOURE DESIGN ASSOCIATES
P.O. Box 15707 - Riyadh 11454 KSA
Tel. 01 441 4963 - Fax. 01 441 3867
simas@simal.com


©SIMA MALAK + ALSSAMOURE DESIGN ASSOCIATES (شركة) 2003
This document including all drawing and text is the property and copyright of SIMA MALAK + ALSSAMOURE DESIGN ASSOCIATES for use solely with respect to this Project and shall not be copied or reproduced by any means except by agreement in writing from SIMA MALAK + ALSSAMOURE DESIGN ASSOCIATES.

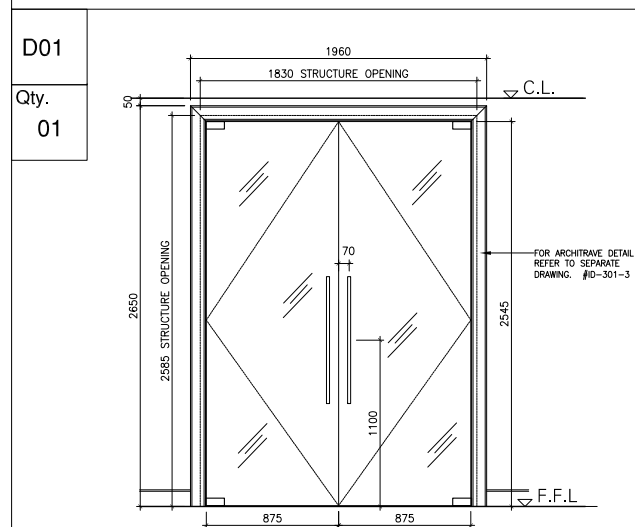

DOOR DESCRIPTION : 12mm THICK TOUGHENED CLEAR GLASS DOUBLE
DOOR. WITH STAINLESS STEEL PATCH FITTINGS AND PULL HANDLES.
GLASS SIZE: H875 x W2460mm EACH PANEL (EXACT DIMENSIONS TO BE
CONFIRMED ON SITE.)
CLEAR PLASTIC SEAL TO BE PROVIDED ALL ROUND.

REQUIREMENTS FOR ACCESS CONTROL AND OTHER HARDWARE TO BE CO-ORDINATED WITH SECURITY/IT CONSULTANT.


DOOR HARDWARE: REFER TO SEPARATE SCHEDULE - ARC08-1-3 DH01

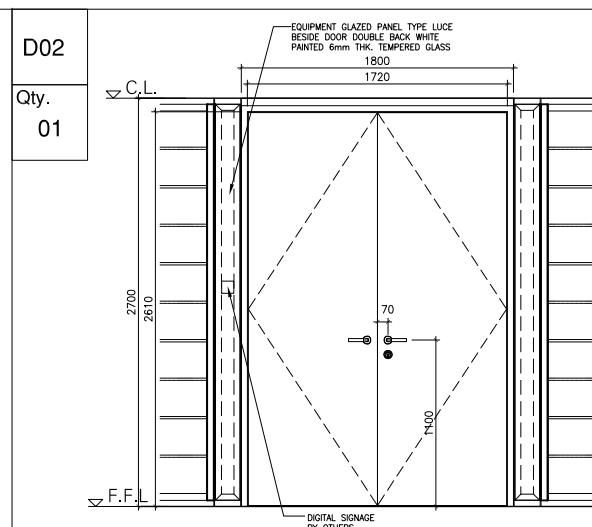

OFFICE PARTITION SYSTEM FLAT LEAF DOUBLE DOOR WITH EQUIPMENT
 PANEL ON ONE SIDE. DOOR PANELS WITH REAL STRAIGHT GRAINED
 OAK WOOD VENEER WITH TINTED SATIN FINISH. FRAME AS PER SELECTED
 PARTITION SYSTEM SUPPLIER TO PROVIDE FULL DETAILS

REQUIREMENTS FOR DIGITAL SIGNAGE TO BE CO-ORDINATED WITH IT/AV CONSULTANT.


DOOR HARDWARE: REFER TO SEPARATE SCHEDULE - ARC08-1-3 DH01

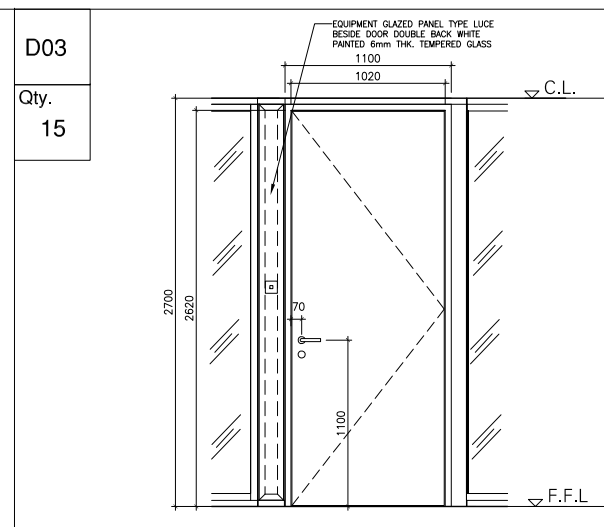

OFFICE PARTITION SYSTEM FLAT LEAF SINGLE DOOR WITH EQUIPMENT
 PANEL ON ONE SIDE. DOOR PANEL WITH REAL STRAIGHT GRAINED
 OAK WOOD VENEER WITH TINTED SATIN FINISH. FRAME AS PER SELECTED
 PARTITION SYSTEM SUPPLIER TO PROVIDE FULL DETAILS

REQUIREMENTS FOR DIGITAL SIGNAGE TO BE CO-ORDINATED WITH IT/AV CONSULTANT.


DOOR HARDWARE: REFER TO SEPARATE SCHEDULE - ARC08-1-3 DH01

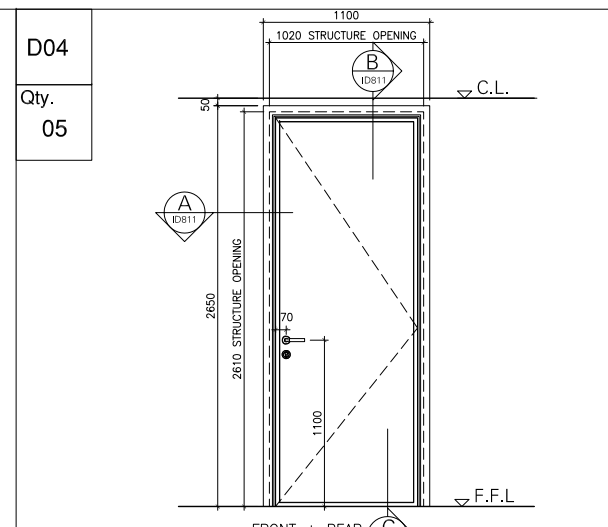

DOOR DESCRIPTION : FLAT LEAF SOLID WOOD SINGLE DOOR WITH REAL STRAIGHT GRAINED OAK WOOD VENEER AND GREY TINTED SATIN FINISH. SOLID WOOD FRAME AND ARCHITRAVE TO MATCH DOOR LEAF.

DOOR FRAME DETAIL : REFER TO SEPARATE DRAWING - ID811


DOOR HARDWARE: REFER TO SEPARATE SCHEDULE - ARC08-1-3 DH01

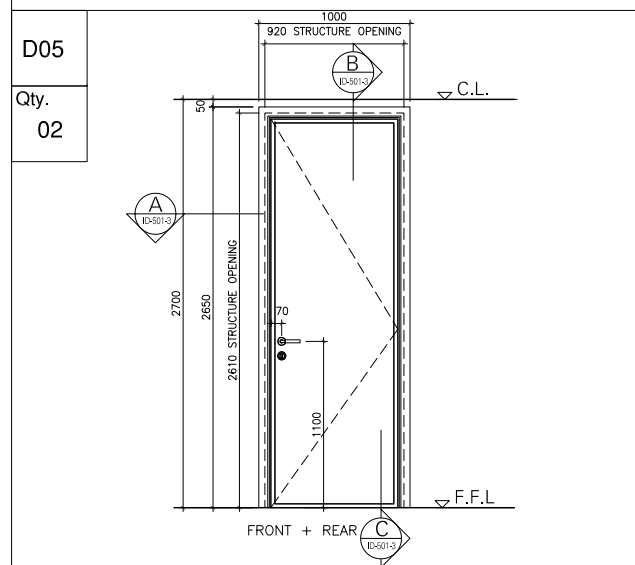

DOOR DESCRIPTION : WATER RESISTANT FLAT LEAF SOLID WOOD SINGLE DOOR WITH REAL STRAIGHT GRAINED LIGHT OAK WOOD VENEER AND GREY TINTED SATIN FINISH. SOLID WOOD FRAME AND ARCHITRAVE TO MATCH DOOR LEAF.

DOOR FRAME DETAIL : REFER TO SEPARATE DRAWING - ID811



DOOR HARDWARE: REFER TO SEPARATE SCHEDULE - ARC08-1-3 DH01

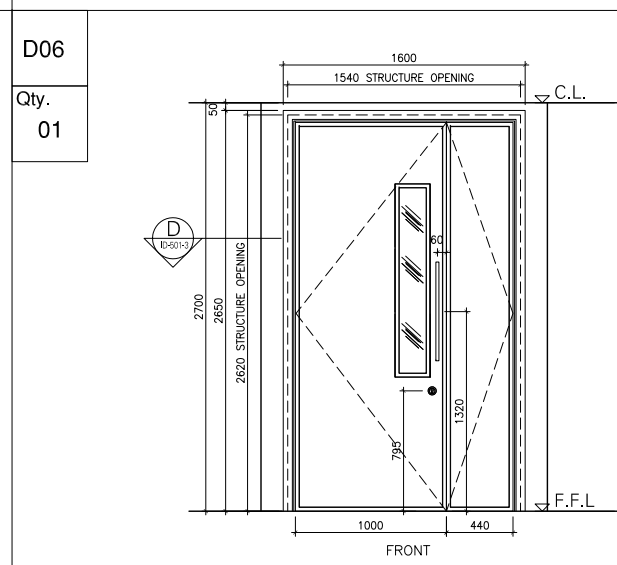

DOOR DESCRIPTION : FLAT LEAF SOLID WOOD DOUBLE DOOR SET WITH REAL STRAIGHT GRAINED LIGHT OAK WOOD VENEER AND GREY TINTED SATIN FINISH. SOLID WOOD FRAME AND ARCHITRAVE TO MATCH DOOR LEAF. WITH VISION PANEL. VISION PANEL WITH CLEAR GLASS.

DOOR AND FRAME DETAIL : REFER TO SEPARATE DRAWING - ID811

DOOR HARDWARE: REFER TO SEPARATE SCHEDULE - ARC08-1-3 DH01

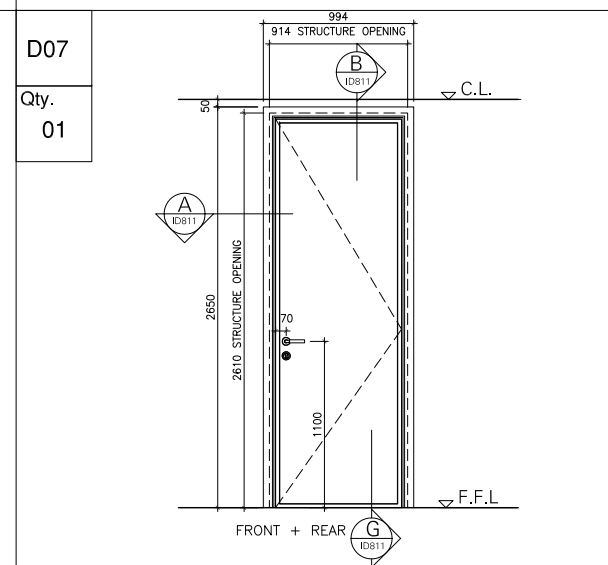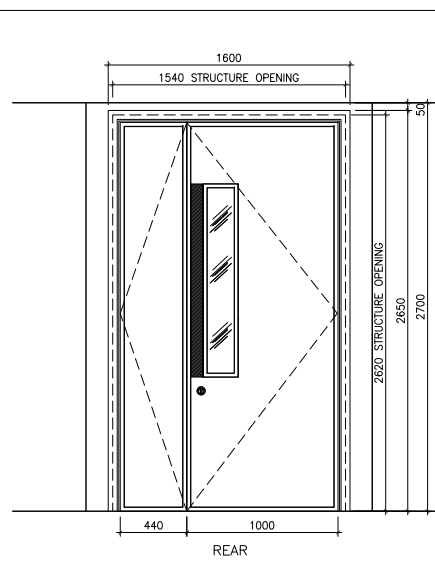

DOOR DESCRIPTION : FLAT LEAF SOLID WOOD SINGLE DOOR WITH REAL STRAIGHT GRAINED OAK WOOD VENEER AND GREY TINTED SATIN FINISH. SOLID WOOD FRAME AND ARCHITRAVE TO MATCH DOOR LEAF.

REQUIREMENTS FOR ACCESS CONTROL AND OTHER HARDWARE TO BE
CO-ORDINATED WIT SECURITY/IT CONSULTANT.

DOOR DETAIL : REFER TO SEPARATE DRAWING - ID-301-3

DOOR HARDWARE: REFER TO SEPARATE SCHEDULE - ARC08-1-3 DH01

GENERAL NOTES

1. This drawing shall be read in conjunction with all other relevant architectural, structural & electrical drawings including those of other consultants.
2. It is the responsibility of contractors & manufacturers to check all relevant site dimensions prior to the start of construction or manufacture.
3. All materials and components must be installed on site in accordance with manufacturer's instructions, shop drawings and standard details.
4. All dimensions are in millimeters unless noted otherwise.
5. Full working drawings, specifications and samples are to be provided by Contractor/Supplier for approval prior to manufacture.

NOTES:

- All dimensions are structural opening sizes.
- All office doors to be rated at 30dB R_w
Acoustic door seals to jamb and head and threshold drop seals are required.
- All woodwork finishes should be as per approved samples. Contractor to submit samples for approval prior to manufacturing commences.

* Requirements for Access Control and other Hardware to be Co-Ordinated with Security/IT Consultant.

* Requirements for Digital Signage to be Co-Ordinated with IT/AV Consultant.

FINISHES

* Please Refer to Finishing Schedule for full specifications:
ARC08-1-3 FIN

KEY PLAN

X	INITIAL ISSUE	MP	AM	SM	2022.06.18	
REV.#	GENERAL NOTES	DRAWN BY	CHECKED BY	APPROVED BY	DATE	
PROJECT TITLE					REFERENCE	
ARCAPITA - ATLANTA					ARC08 G	

DOORS KEY PLAN





DRAWING NUMBER			REVISION
ID-501-3			-
SCALE	FORMAT	ADDITIONAL NOTES	DESIGN DEVELOPMENT
1:75	A1		




SIMA MALAK + ALSSAMOURÉ
DESIGN ASSOCIATES

P.O. Box 15707 - Riyadh 11454 KSA
Tel. 01 441 4963 - Fax. 01 441 3867
simals@simals.com


©SIMA MALAK + ALSSAMOURÉ DESIGN ASSOCIATES (موسم) 2003
This document including all drawing and text is the property and
copyright of SIMA MALAK + ALSSAMOURÉ DESIGN ASSOCIATES for
use solely with respect to this Project and shall not be copied or
reproduced by any means except by agreement in writing from
SIMA MALAK + ALSSAMOURÉ DESIGN ASSOCIATES.

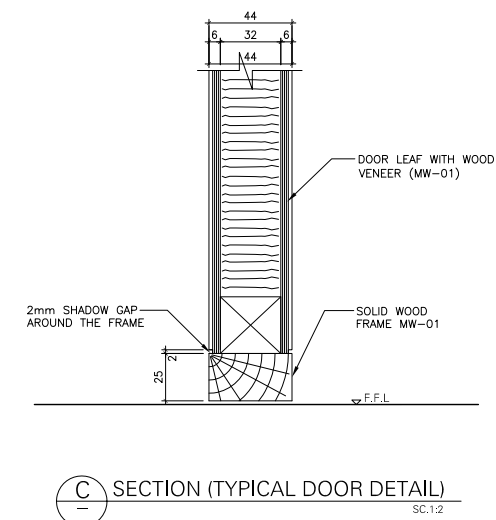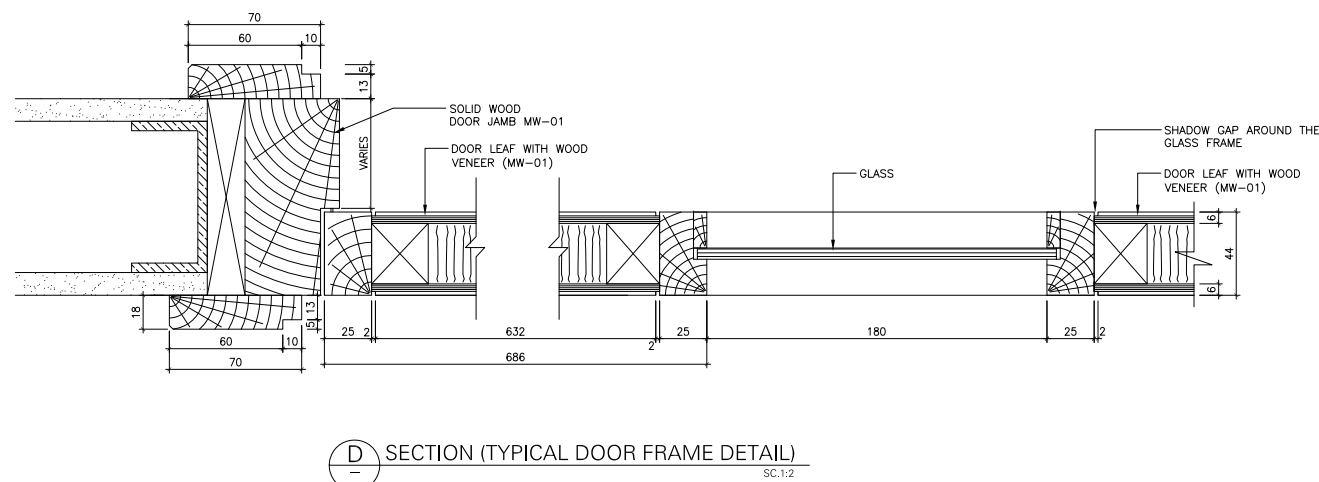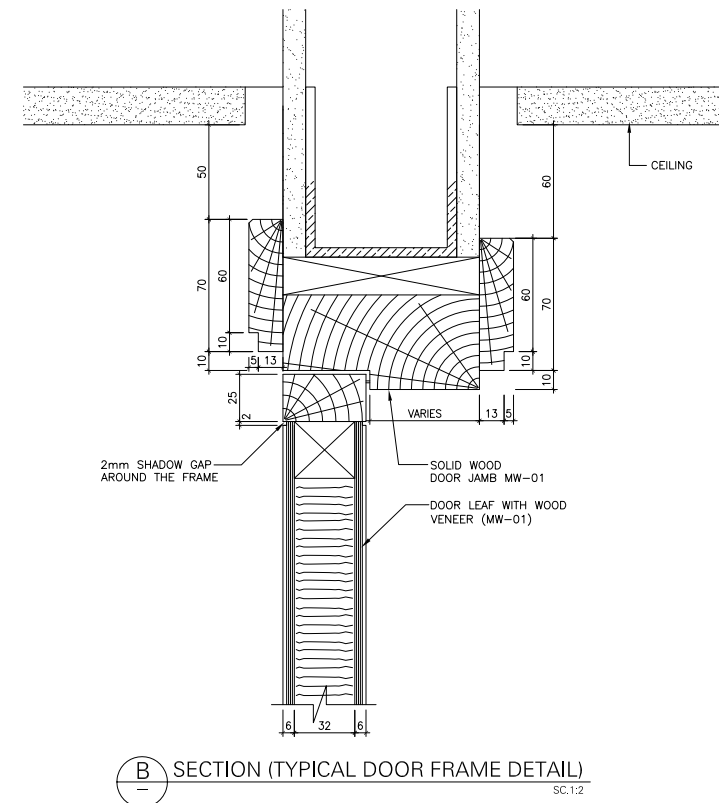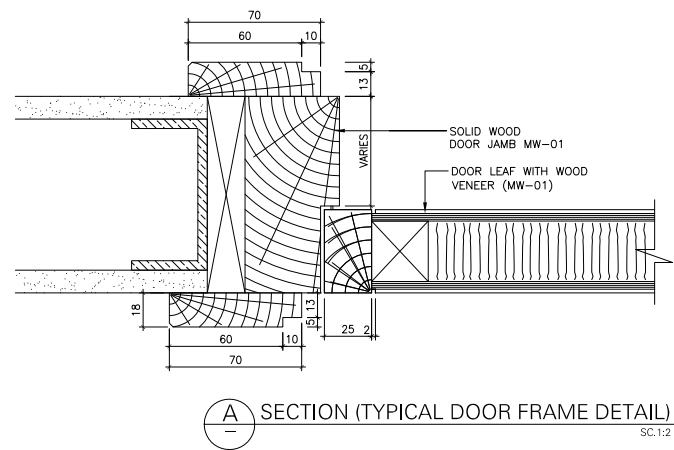


©SIMA MALAK + ALSSAMOURÉ DESIGN ASSOCIATES (سـمـوـر) 2003
This document including all drawing and text is the property and
copyright of SIMA MALAK + ALSSAMOURÉ DESIGN ASSOCIATES for
use solely with respect to this Project and shall not be copied or
reproduced by any means except by agreement in writing from
SIMA MALAK + ALSSAMOURÉ DESIGN ASSOCIATES.

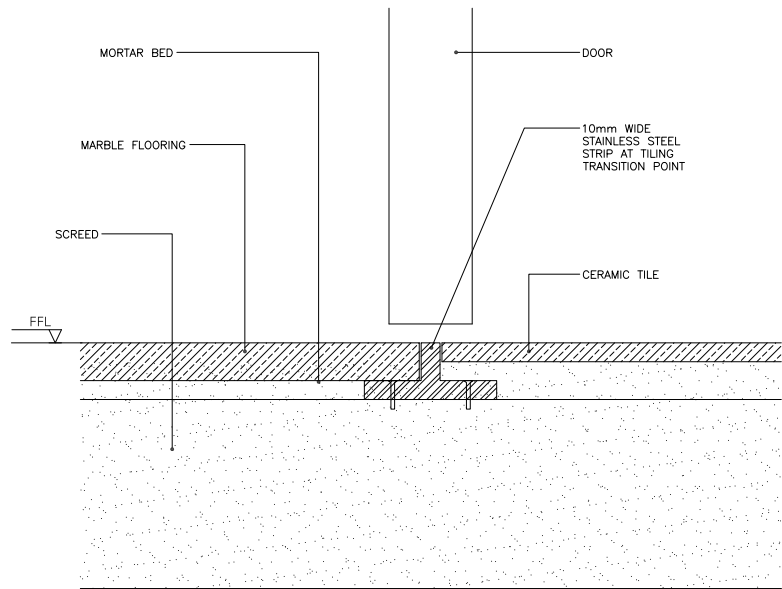


01 FLOOR TRANSITION DETAIL (MARBLE + CERAMIC TILE DETAIL)
SC: 1:2

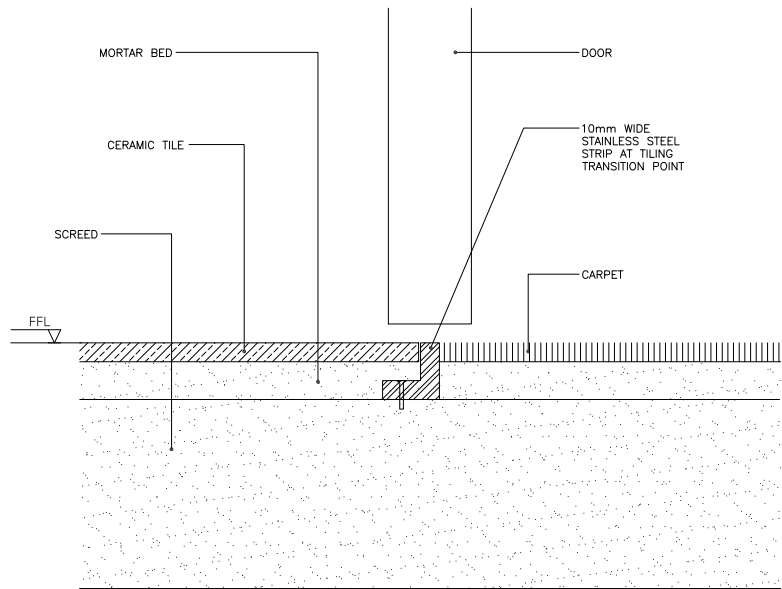


02 FLOOR TRANSITION DETAIL (CERAMIC TILE DETAIL)
SC: 1:2

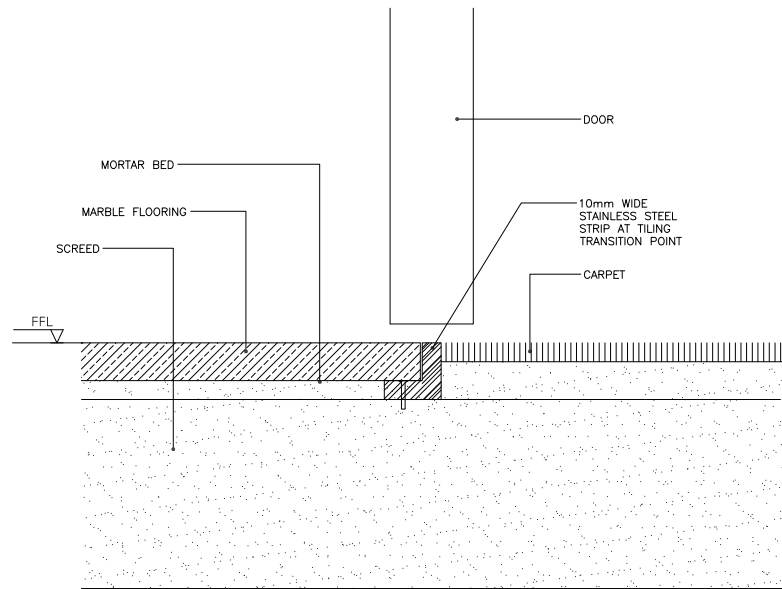

03 FLOOR TRANSITION DETAIL (MARBLE & CARPET DETAIL)
SC: 1:2

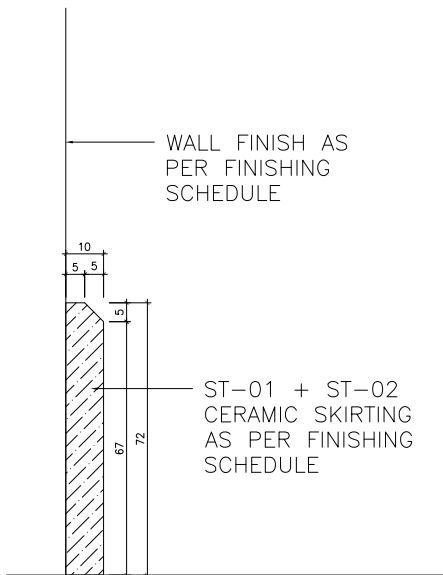

04 TYPICAL CERAMIC SKIRTING DETAIL (ST-01 + ST-02)
SC: 1:1
KITCHENETTE (1-028) AND RESTROOM (1-05,1-006)

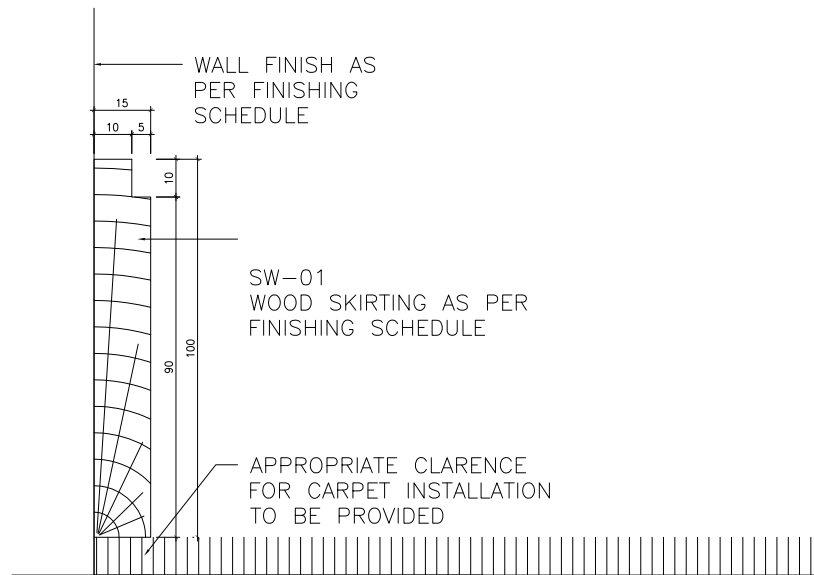

05 TYPICAL WOOD SKIRTING DETAIL (SW-01)
SC: 1:1
ALL AREAS (EXCEPT RECEPTION, KITCHENETTE AND RESTROOM)

GENERAL NOTES

1. This drawing shall be read in conjunction with all other relevant architectural, structural & electrical drawings including those of other consultants.
2. It is the responsibility of contractors & manufacturers to check all relevant site dimensions prior to the start of construction or manufacture.
3. All materials and components must be installed on site in accordance with manufacturer's instructions, shop drawings and standard details.
4. All dimensions are in millimeters unless noted otherwise.
5. Full working drawings, specifications and samples are to be provided by Contractor/Supplier for approval prior to manufacture.

NOTES FOR MANUFACTURER:

- * Construction methods shown on drawings are suggested methods only.
- * Construction methods must be discussed between designer and manufacturer prior to Fabrication.
- * All details must be adhered to any deviation must be discussed with the designer prior to manufacture.
- * Structure to be specified by manufacturer considering practicalities and the aesthetics of the design.

FINISHES

- * Please Refer to Finishing Schedule for full specifications:
ARC08-1-3 FIN

KEY PLAN

☒	INITIAL ISSUE	MP	AM	SM	2022.08.18
REV.#	GENERAL NOTES	DRAWN BY	CHECKED BY	APPROVED BY	DATE
PROJECT TITLE				REFERENCE	
ARCAPITA - ATLANTA				ARC08 G	

DRAWING TITLE

TYPICAL DETAILS

DRAWING NUMBER				REVISION
ID-601				-
SCALE	FORMAT	ADDITIONAL NOTES	DESIGN DEVELOPMENT	
1:75	A1			




**SIMA MALAK + ALSSAMOURE
DESIGN ASSOCIATES**
P.O. Box 15707 - Riyadh 11454 KSA
Tel. 01 441 4963 - Fax. 01 441 3867
simals@simals.com

©SIMA MALAK + ALSSAMOURE DESIGN ASSOCIATES (شركة) 2003
This document including all drawing and text is the property and copyright of SIMA MALAK + ALSSAMOURE DESIGN ASSOCIATES for use solely with respect to this Project and shall not be copied or reproduced by any means except by agreement in writing from SIMA MALAK + ALSSAMOURE DESIGN ASSOCIATES.

ARC08 - ARCAPITA - ATLANTA

INTERIOR DESIGN PROPOSAL

5 JULY 2022

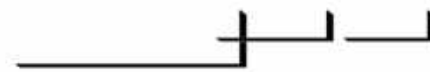

**SIMA MALAK + ALSSAMDOURE
DESIGN ASSOCIATES**

P.O. Box 15707 - Riyadh 11454 KSA
Tel. 01 441 4963 - Fax. 01 441 3867
simals@simals.com



WOOD PANELING
(WITH LIGHTER FINISH)



RECEPTION DESK
(WITH LIGHTER FINISH)



REAR WALL (WITH GLASS CENTRAL PANEL)



FINISH FOR RECEPTION DESK



SOFA



TABLE LAMP



CEILING LIGHT



ARM CHAIR



SIDE TABLE



COFFEE TABLE



RECEPTION CHAIR



ARC08 – ARCAPITA – ATLANTA

PROPOSED MATERIAL SELECTION - RECEPTION (1-001)

P201A – 27 JUNE 2022



SIMA MALAK + ALSSAMOURE
DESIGN ASSOCIATES
 P.O. Box 15707 - Riyadh 11454 KSA
 Tel. 01 441 4863 - Fax. 01 441 3867
 SIMA@SIMALS.COM



SOFA


CHAIR

UPHOLSTERY FOR SOFA AND CHAIRS IN RECEPTION AREA

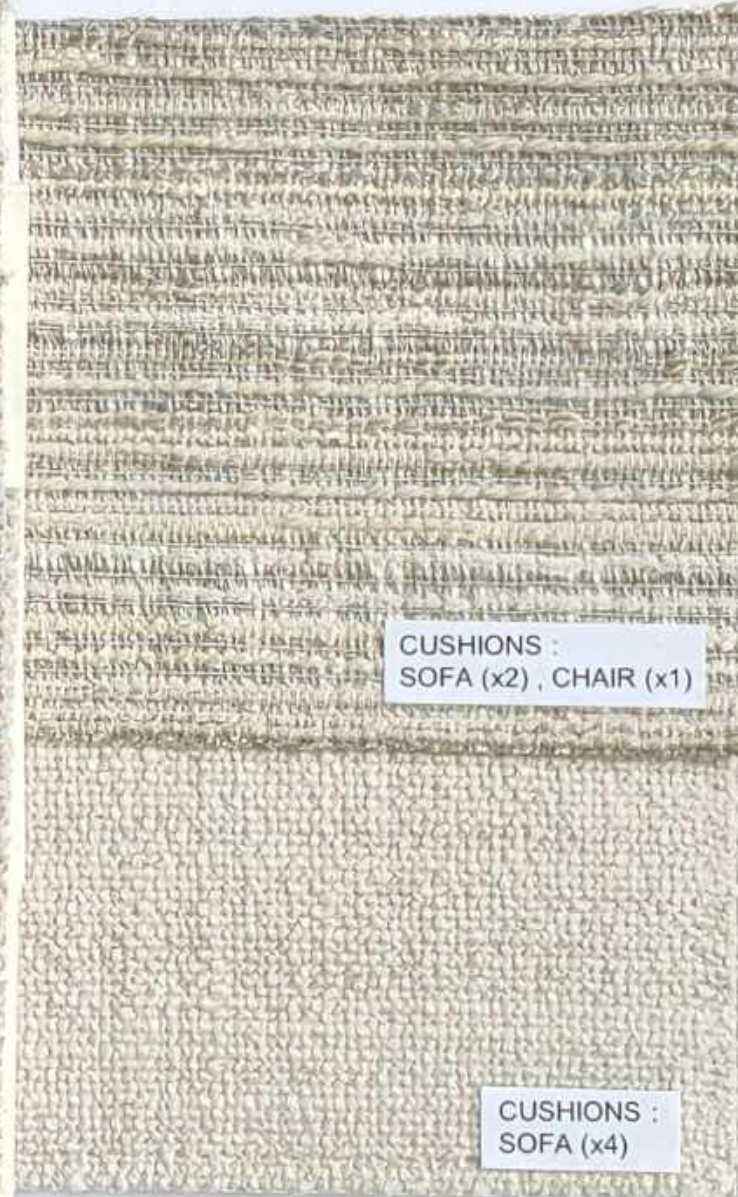

CUSHIONS :
SOFA (x2) , CHAIR (x1)

CUSHIONS :
SOFA (x4)

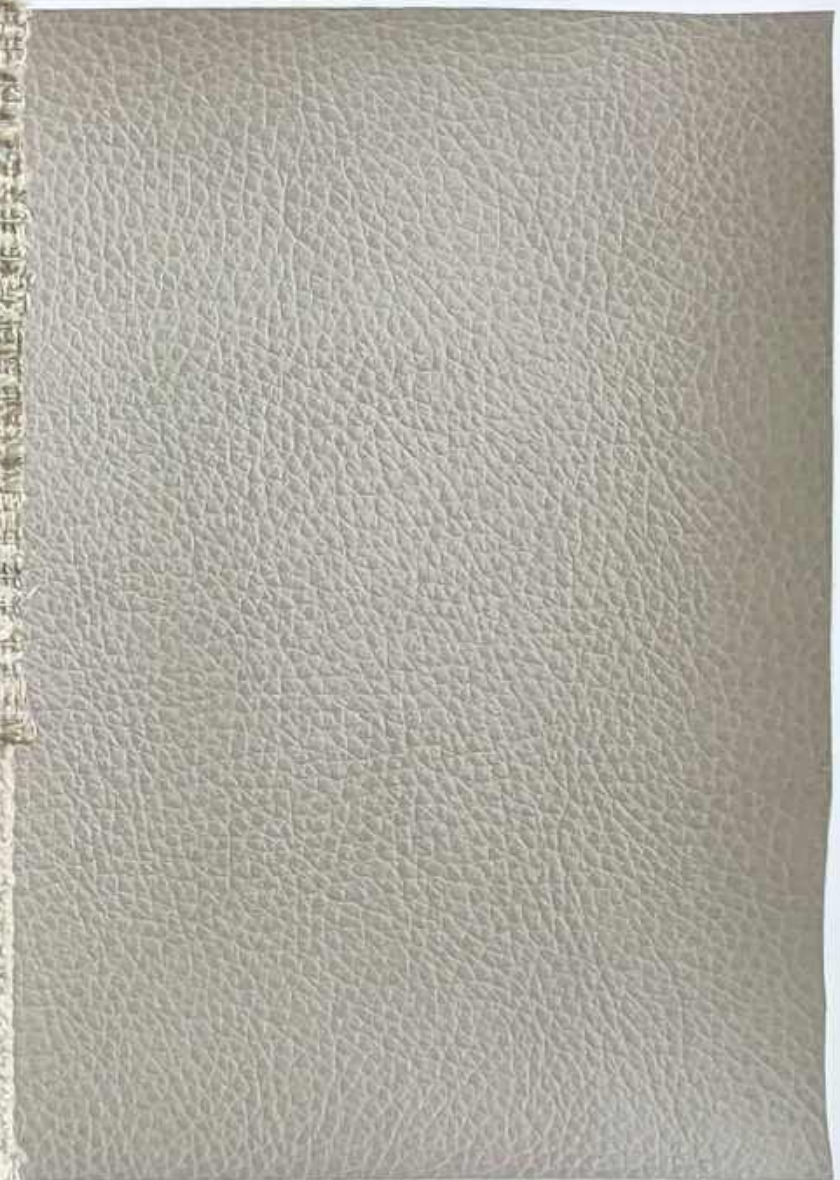

UPHOLSTERY FOR BENCH IN LOBBY (1-004)

ARC08 – ARCAPITA – ATLANTA

PROPOSED FABRIC SELECTION - AREA (1-001) + LOBBY (1-004)

P201B – 5 JUNLY 2022



CONSOLE



FLOOR STANDING LAMP



BENCH




AV WALL (WITH LIGHTER FINISH)



AV WALL (WITH LIGHTER FINISH)



CEILING

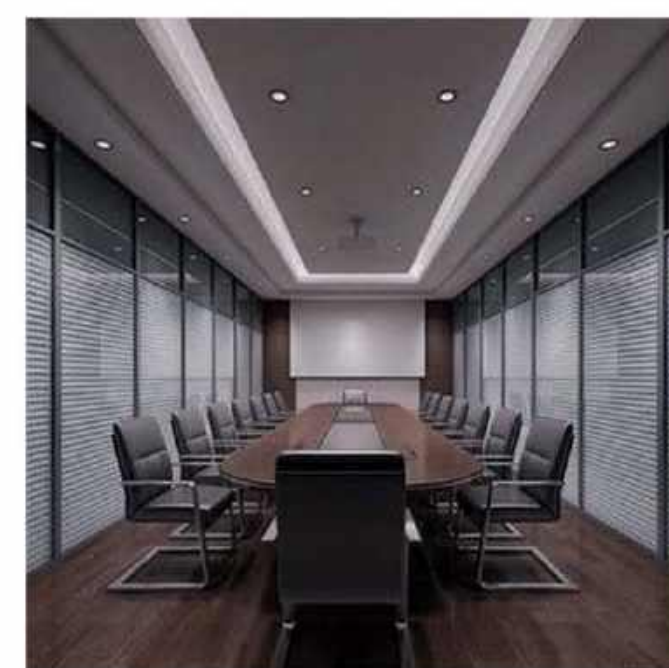

CEILING



AV WALL



CEILING / LIGHTING



AV WALL



PARTITION WITH FROSTED FINISH

ARC08 - ARCAPITA - ATLANTA

INTERIOR PROPOSAL - MEETING / CONFERENCE ROOM CONCEPTS
P102A - 27 JUNE 2022



MEETING TABLE



CREDENZA



MEETING CHAIR



THICKET ! M75, PALDAO, MATTE
WOOD FINISHES



BRUSHED STAINLESS STEEL



MEETING TABLE



CREDENZA



MEETING CHAIR




THICKET | M75, PALDAO, MATTE
WOOD FINISHES



BRUSHED STAINLESS STEEL



ROMAN BLINDS

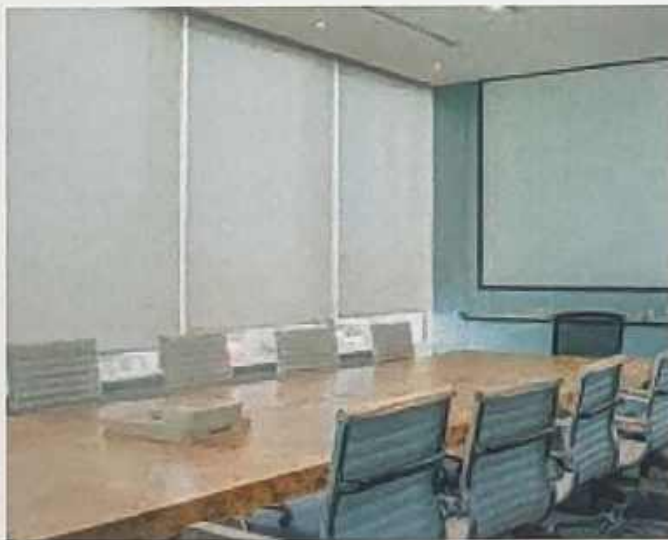

ROLLER BLINDS



ROMAN BLINDS FABRIC

FOR ALL AREAS



ROLLER BLINDS MATERIAL
(OPTION - 01)

FOR MEETING ROOMS

ROLLER BLINDS MATERIAL
(OPTION - 02)



DESK



CREDENZA



DESK CHAIR




MEETING TABLE CHAIR



VISITOR CHAIR OPTIO - 01




MEETING TABLE - OPTION 02

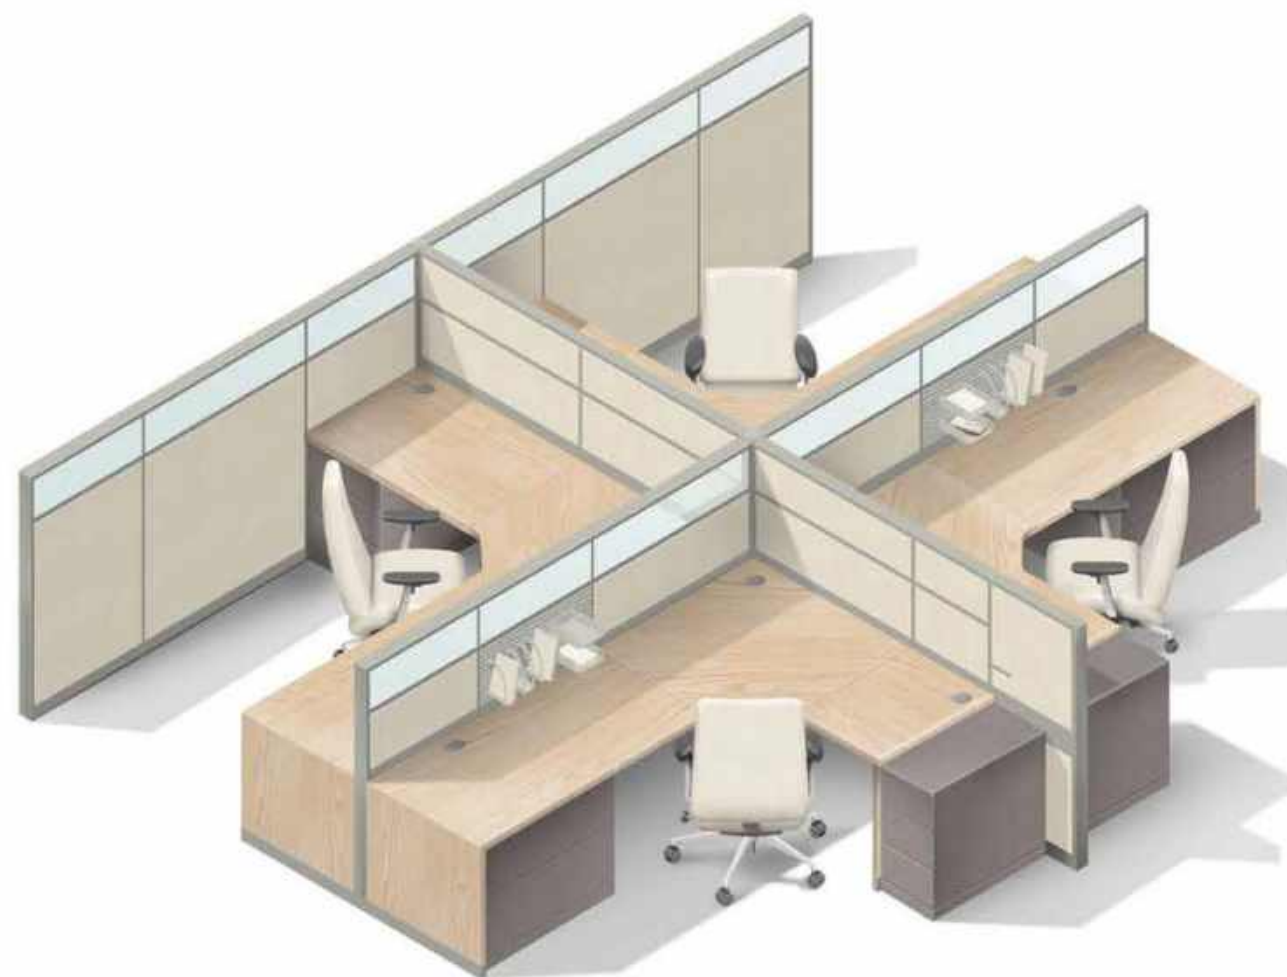

ARC08 - ARCAPITA - ATLANTA

INTERIOR PROPOSAL - FURNITURE SELECTION - OPEN PLAN OFFICE (1-020)
P360B - 5 JULY 2022

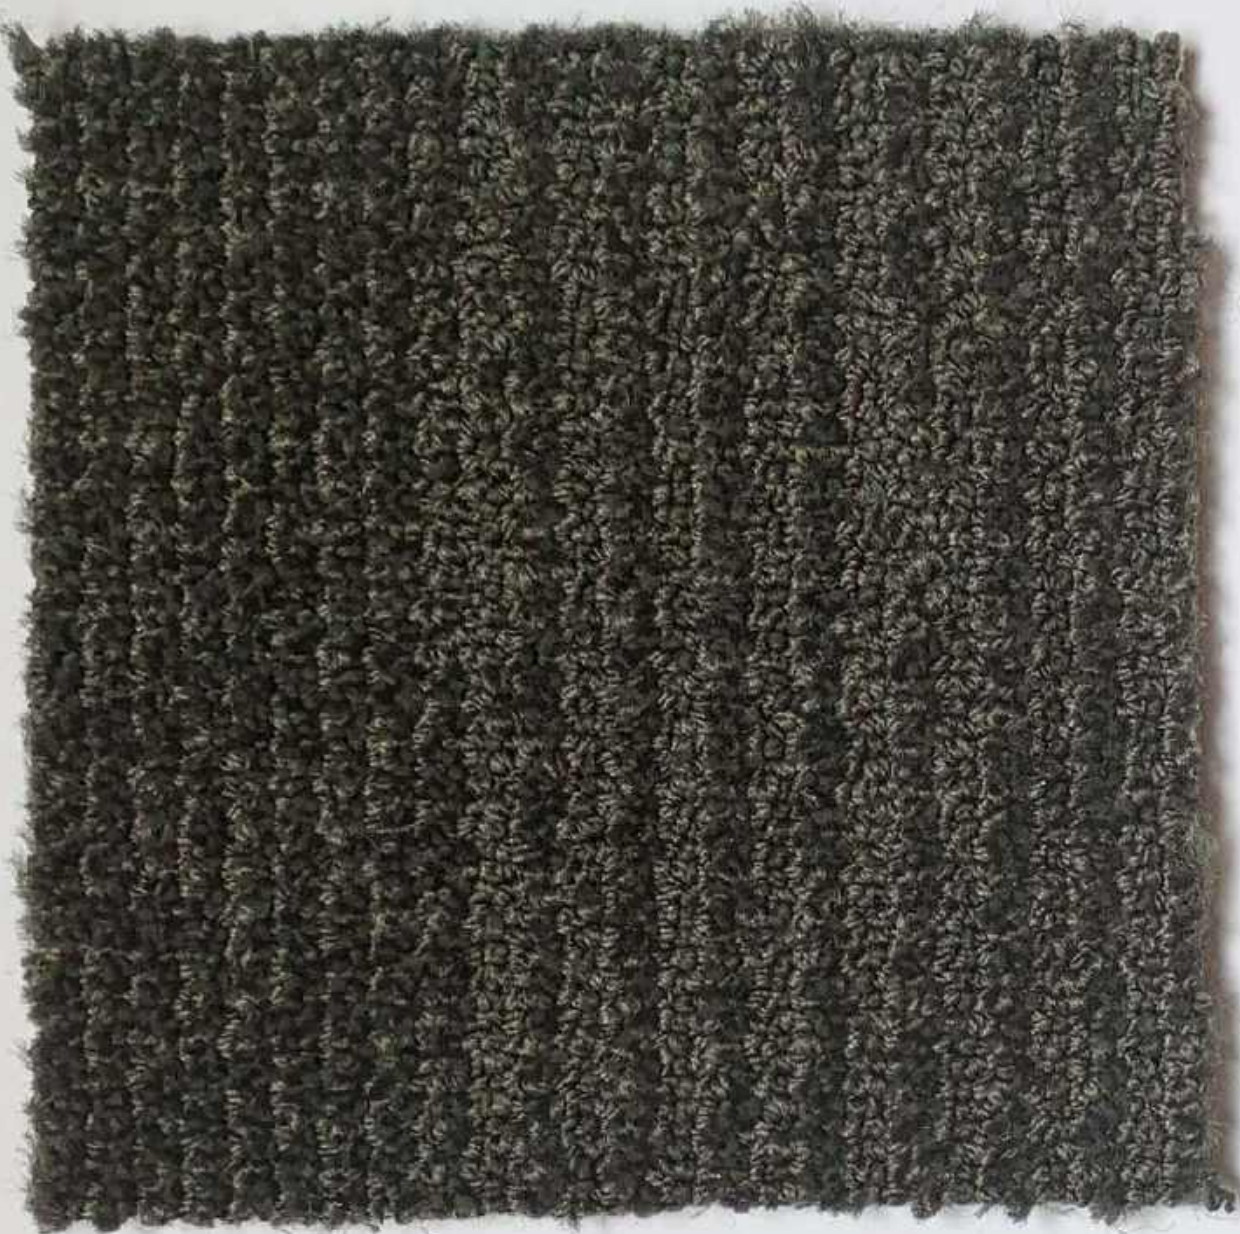

CARPET TILES



DOORS, SKIRTING + PANELLING



PARTITION FRAMING




WALL PAPER

ARC08 – ARCAPITA – ATLANTA

PROPOSED MATERIAL SELECTION - GENERAL OFFICE AREA

P203 – 15 JUN 2022

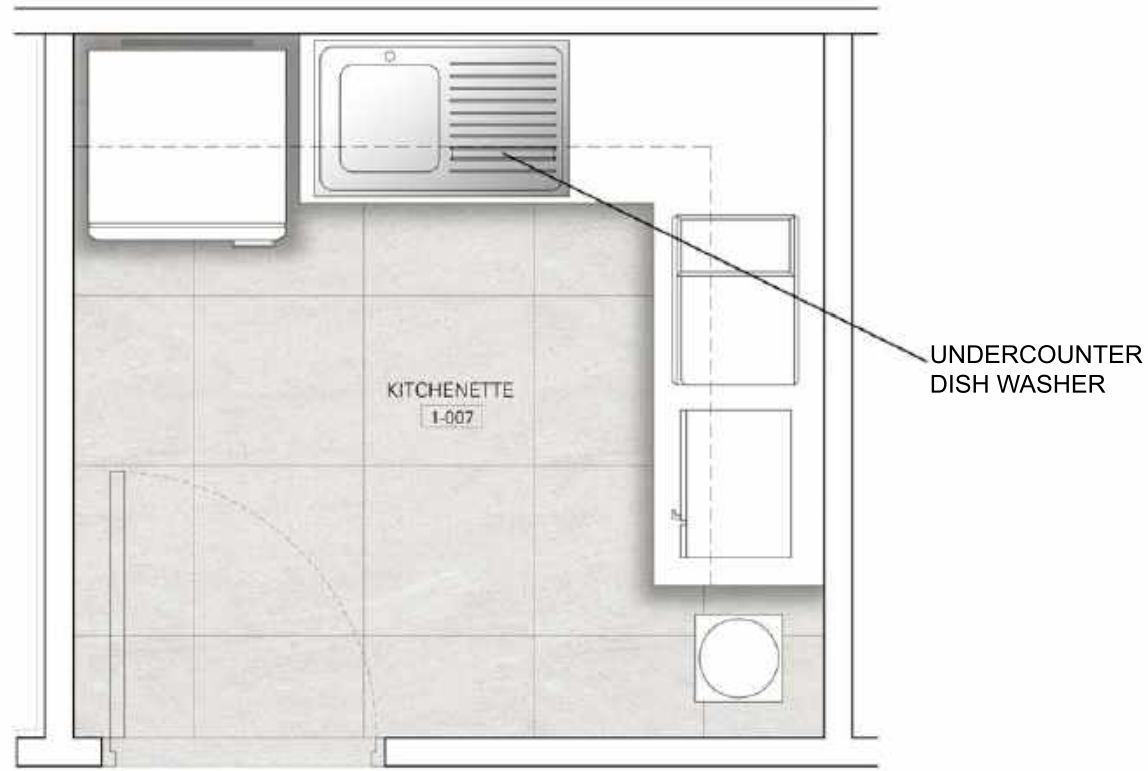

KITCHENETTE PLAN



ELEVATION-1



ELEVATION-2



CHAIR



TABLE



FLOOR TILES (60x60 cm)
+
WALL TILES (30x60 cm)



DRAWERS AND DOOR PANELS



COUNTER



DOOR HANDLES
SKIRTING

ARC08 – ARCAPITA – ATLANTA

PROPOSED MATERIAL SELECTION – KITCHENETTE (1-007)

P206 – 15 JUN 2022





ARC08

INTERIOR PROPOSAL - PROPOSED WC(1-005) + WASH(1-006) PLAN AND ELEVATIONS
P115B - 5 JULY 2022



UNDER-MOUNTED SINK



FAUCET



SOAP DISPENSER



PAPER TOWEL DISPENSER
AND WASTE RECEPTACLE



ACTUATOR



HANDSPRAY



HOOK



TOILET PAPER HOLDER



CONCEALED CISTERN




TOILET SEAT



BRUSH HOLDER



HAND DRYER

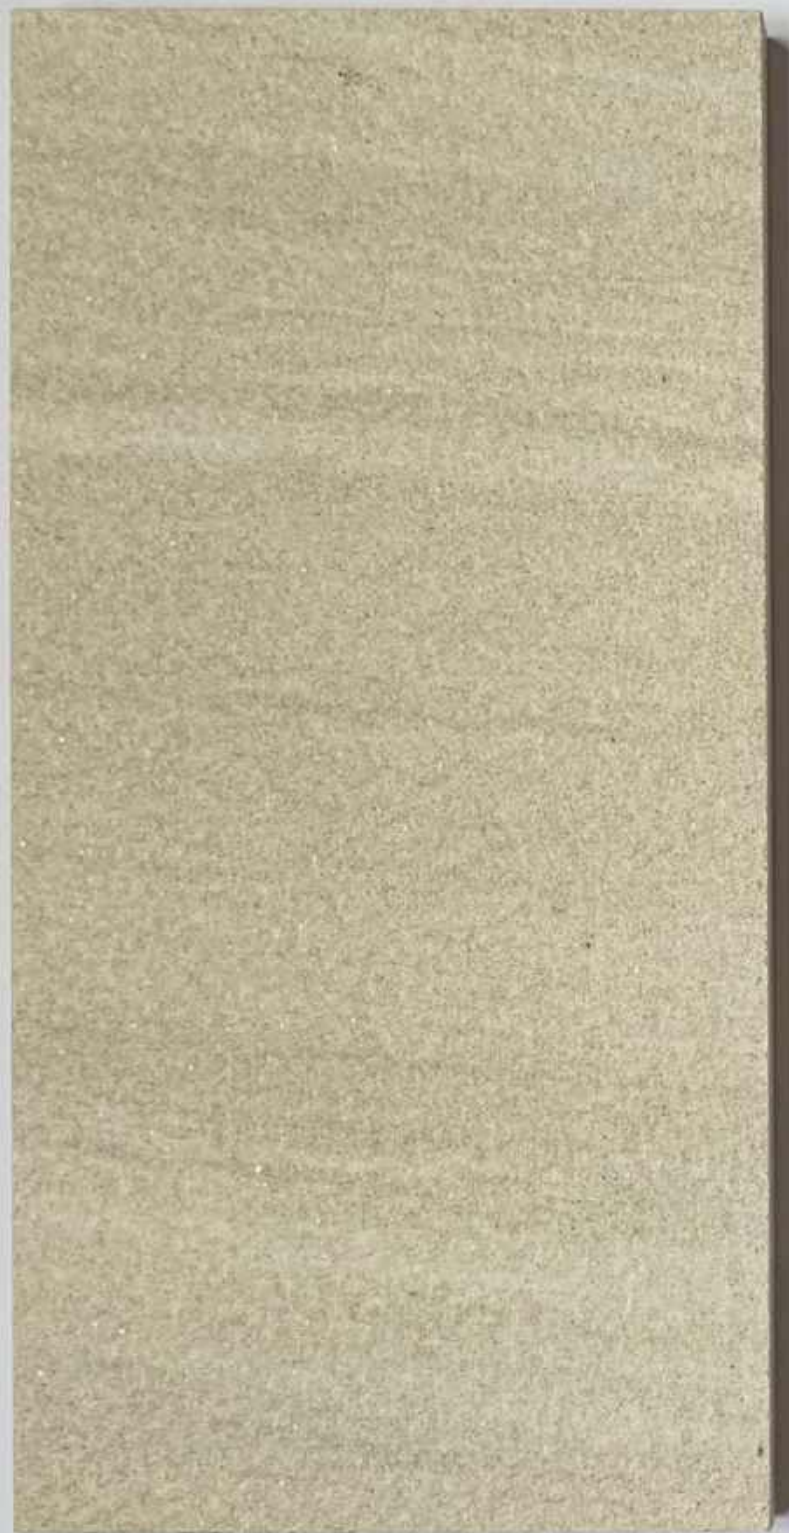

WALLS AND FLOORS



VANITY COUNTER



VANITY WOODWORK



WASHROOM WALL



ARC08 - ARCAPITA - ATLANTA

INTERIOR PROPOSAL - STORAGE UNIT LOBBY(1-029+1-030) CONCEPTS
P105 - 27 JUNE 2022



STORAGE UNITS ELEVATION



WOOD FINISH



WALLPAPER