


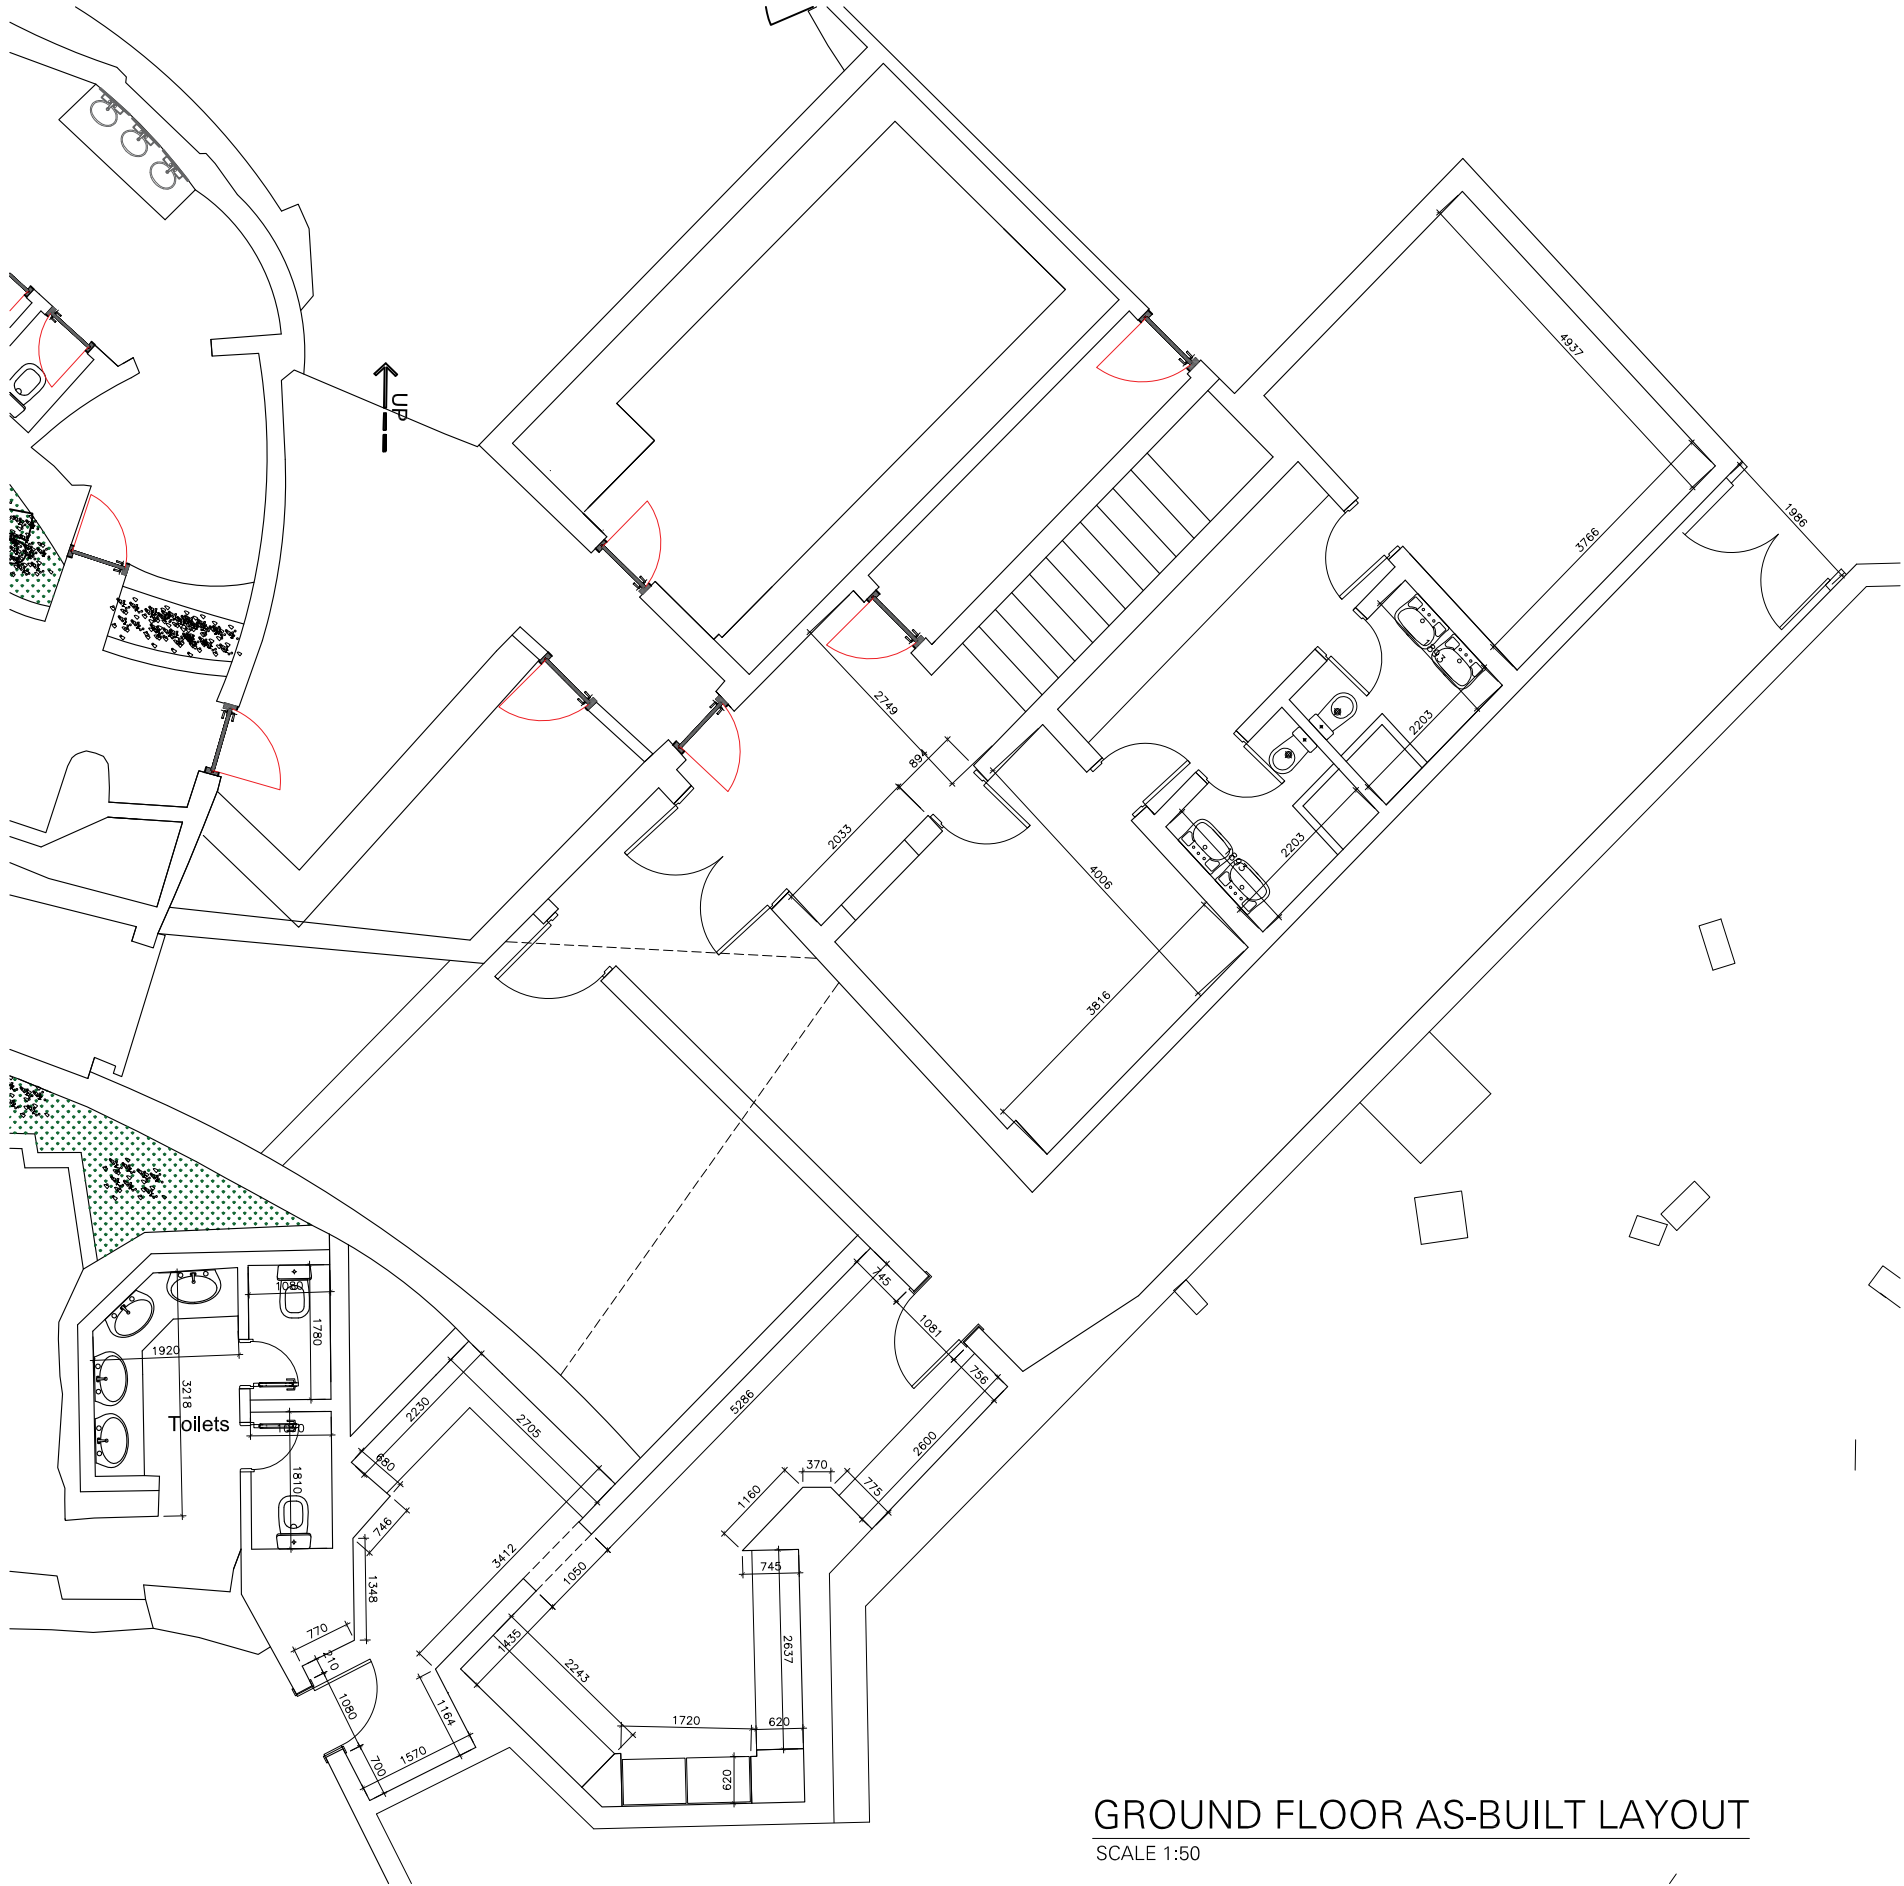

GROUND FLOOR AS-BUILT LAYOUT
SCALE 1:50

GENERAL NOTES

1. This drawing shall be read in conjunction with all other relevant architectural, structural & electrical drawings including those of other consultants.
2. It is the responsibility of contractors & manufacturers to check all relevant site dimensions prior to the start of construction or manufacture.
3. All materials and components must be installed on site in accordance with manufacturer's instructions, shop drawings and standard details.
4. All dimensions are in millimeters unless noted otherwise.
5. Full working drawings, specifications and samples are to be provided by Contractor/Supplier for approval prior to manufacture.

KEY PLAN

INITIAL ISSUE	MP	AM	SM	2025.02.10
REV.#	GENERAL NOTES	DRAWN BY	CHECKED BY	APPROVED BY

PROJECT TITLE	REFERENCE
KRR01-RIYADH	KRR01 G

DRAWING TITLE
AS-BUILT GROUND FLOOR LAYOUT


DRAWING NUMBER	REVISION
A-002	-

SCALE	FORMAT	ADDITIONAL NOTES	DESIGN DEVELOPMENT
1:125	A1		

SIMA MALAK + ALSSAMOURE
DESIGN ASSOCIATES

P.O. Box 15707 - Riyadh 11454 KSA
Tel. 01 441 4963 - Fax. 01 441 3867
simals@simals.com

©SIMA MALAK + ALSSAMOURE DESIGN ASSOCIATES (شركة) 2003
This document including all drawing and text is the property and copyright of SIMA MALAK + ALSSAMOURE DESIGN ASSOCIATES for use solely with respect to this Project and shall not be copied or reproduced by any means except by agreement in writing from SIMA MALAK + ALSSAMOURE DESIGN ASSOCIATES.

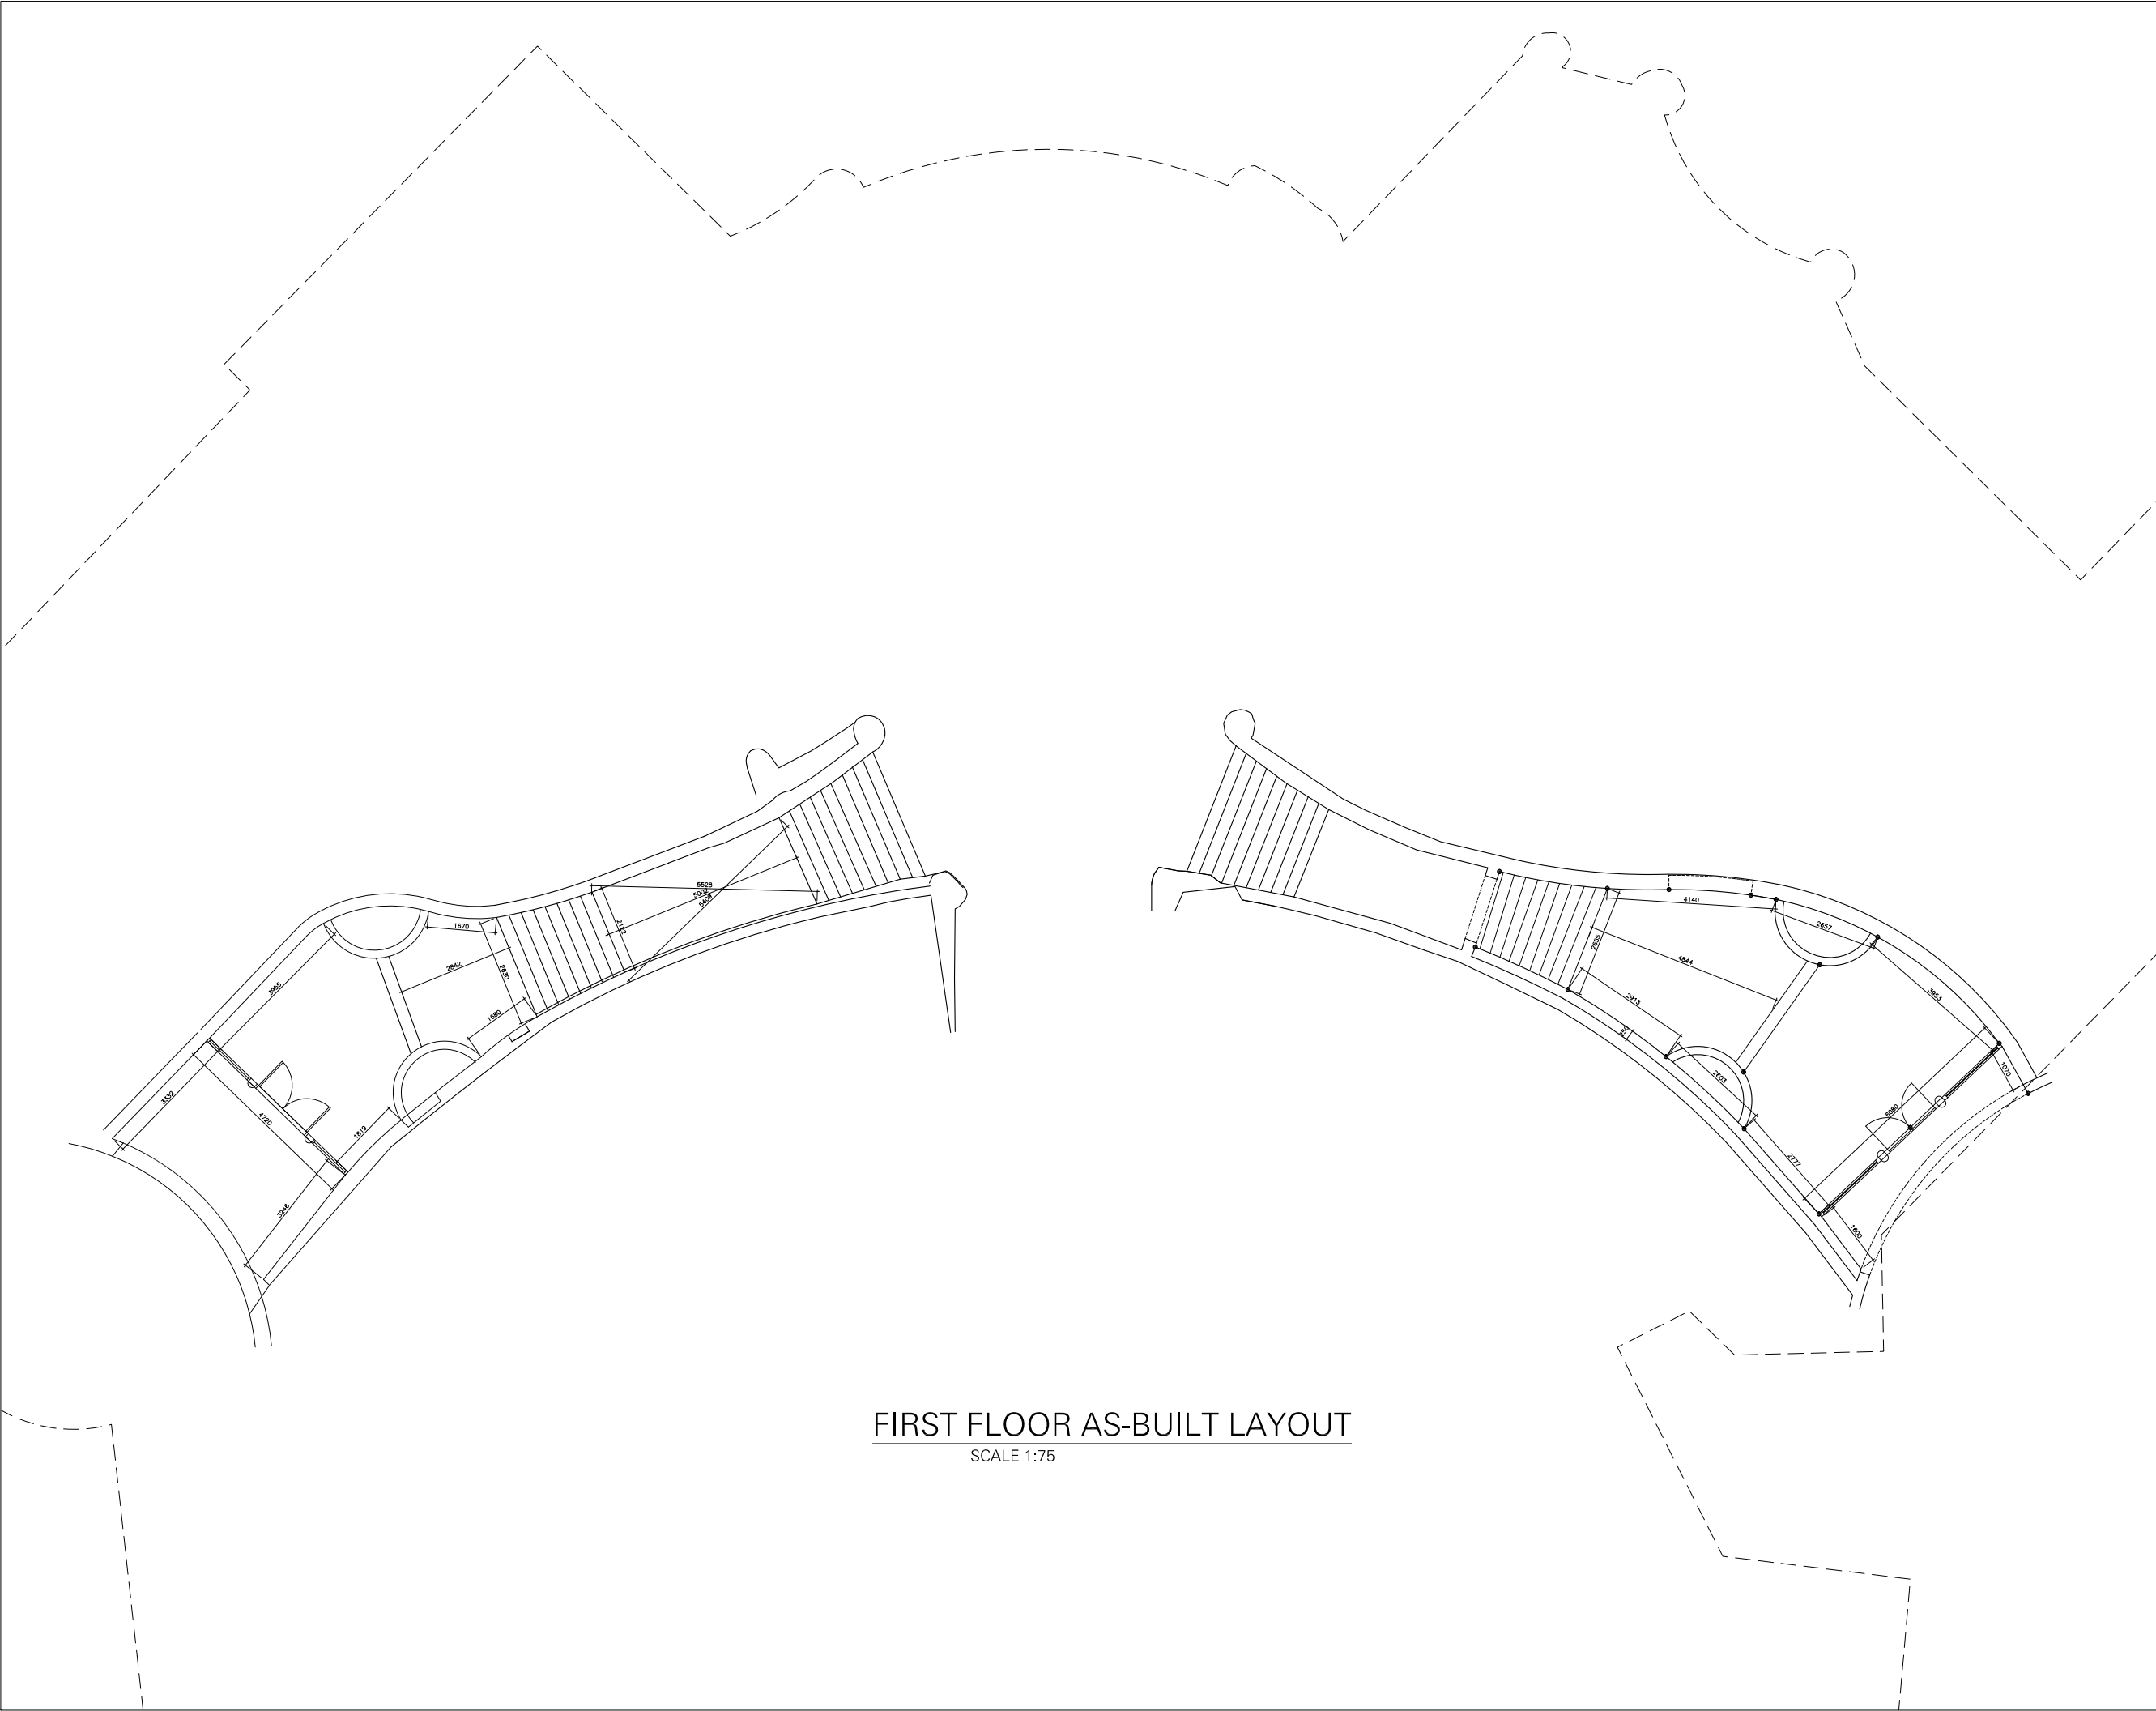

FIRST FLOOR AS-BUILT LAYOUT
SCALE 1:75

GENERAL NOTES

1. This drawing shall be read in conjunction with all other relevant architectural, structural & electrical drawings including those of other consultants.
2. It is the responsibility of contractors & manufacturers to check all relevant site dimensions prior to the start of construction or manufacture.
3. All materials and components must be installed on site in accordance with manufacturer's instructions, shop drawings and standard details.
4. All dimensions are in millimeters unless noted otherwise.
5. Full working drawings, specifications and samples are to be provided by Contractor/Supplier for approval prior to manufacture.

KEY PLAN

☒	INITIAL ISSUE	MP	AM	SM	2025.02.10
-------------------------------------	---------------	----	----	----	------------

REV.#	GENERAL NOTES	DRAWN BY	CHECKED BY	APPROVED BY	DATE
-------	---------------	----------	------------	-------------	------

PROJECT TITLE				REFERENCE
KRR01-RIYADH				KRR01 G

DRAWING TITLE

AS-BUILT
FIRST FLOOR LAYOUT

DRAWING NUMBER	REVISION
A-003	-

SCALE	FORMAT	ADDITIONAL NOTES	DESIGN DEVELOPMENT
1:125	A1		



**SIMA MALAK + ALSSAMOURE
DESIGN ASSOCIATES**
P.O. Box 15707 - Riyadh 11454 KSA
Tel. 01 441 4963 - Fax. 01 441 3867
simals@simals.com

©SIMA MALAK + ALSSAMOURE DESIGN ASSOCIATES (شركة) 2003
This document including all drawing and text is the property and
copyright of SIMA MALAK + ALSSAMOURE DESIGN ASSOCIATES for
use solely with respect to this Project and shall not be copied or
reproduced by any means except by agreement in writing from
SIMA MALAK + ALSSAMOURE DESIGN ASSOCIATES.

FOR CABINET
DETAILS SEE
DRAWING No.
ID-407

FOR TV CABINET —
DETAILS SEE DRAWING
No. ID-405

GENERAL NOTES

1. This drawing shall be read in conjunction with all other relevant architectural, structural & electrical drawings including those of other consultants.
2. It is the responsibility of contractors & manufacturers to check all relevant site dimensions prior to the start of construction or manufacture.
3. All materials and components must be installed on site in accordance with manufacturer's instructions, shop drawings and standard details.
4. All dimensions are in millimeters unless noted otherwise.
5. Full working drawings, specifications and samples are to be provided by Contractor/Supplier for approval prior to manufacture.

KEY PLAN

X	INITIAL ISSUE	MP/AC	AM	SM	2025.02.	
REV.#	GENERAL NOTES	DRAWN BY	CHECKED BY	APPROVED BY	DATE	
PROJECT TITLE					REFERENCE	
KRR01-RIYADH					KRR01	G

DRAWING TITLE

FIRST FLOOR (LEFT SIDE)
GUEST BEDROOM-1
GENERAL LAYOUT


DRAWING NUMBER	REVISION
A-101	

SCALE	FORMAT	ADDITIONAL NOTES	DESIGN DEVELOPMENT
1:20	A1		

SIMA MALAK + ALSSAMOURE
DESIGN ASSOCIATES

P.O. Box 15707 - Riyadh 11454 KSA
Tel. 01 441 4963 - Fax. 01 441 3867
simals@simals.com

SJMS MALAK + ALSSAMOUR DESIGN ASSOCIATES (شركة) 200
This document including all drawing and text is the property and
copyright of SJMS MALAK + ALSSAMOUR DESIGN ASSOCIATES for
use solely with respect to this Project and shall not be copied or
reproduced by any means except by agreement in writing from
SJMS MALAK + ALSSAMOUR DESIGN ASSOCIATES.

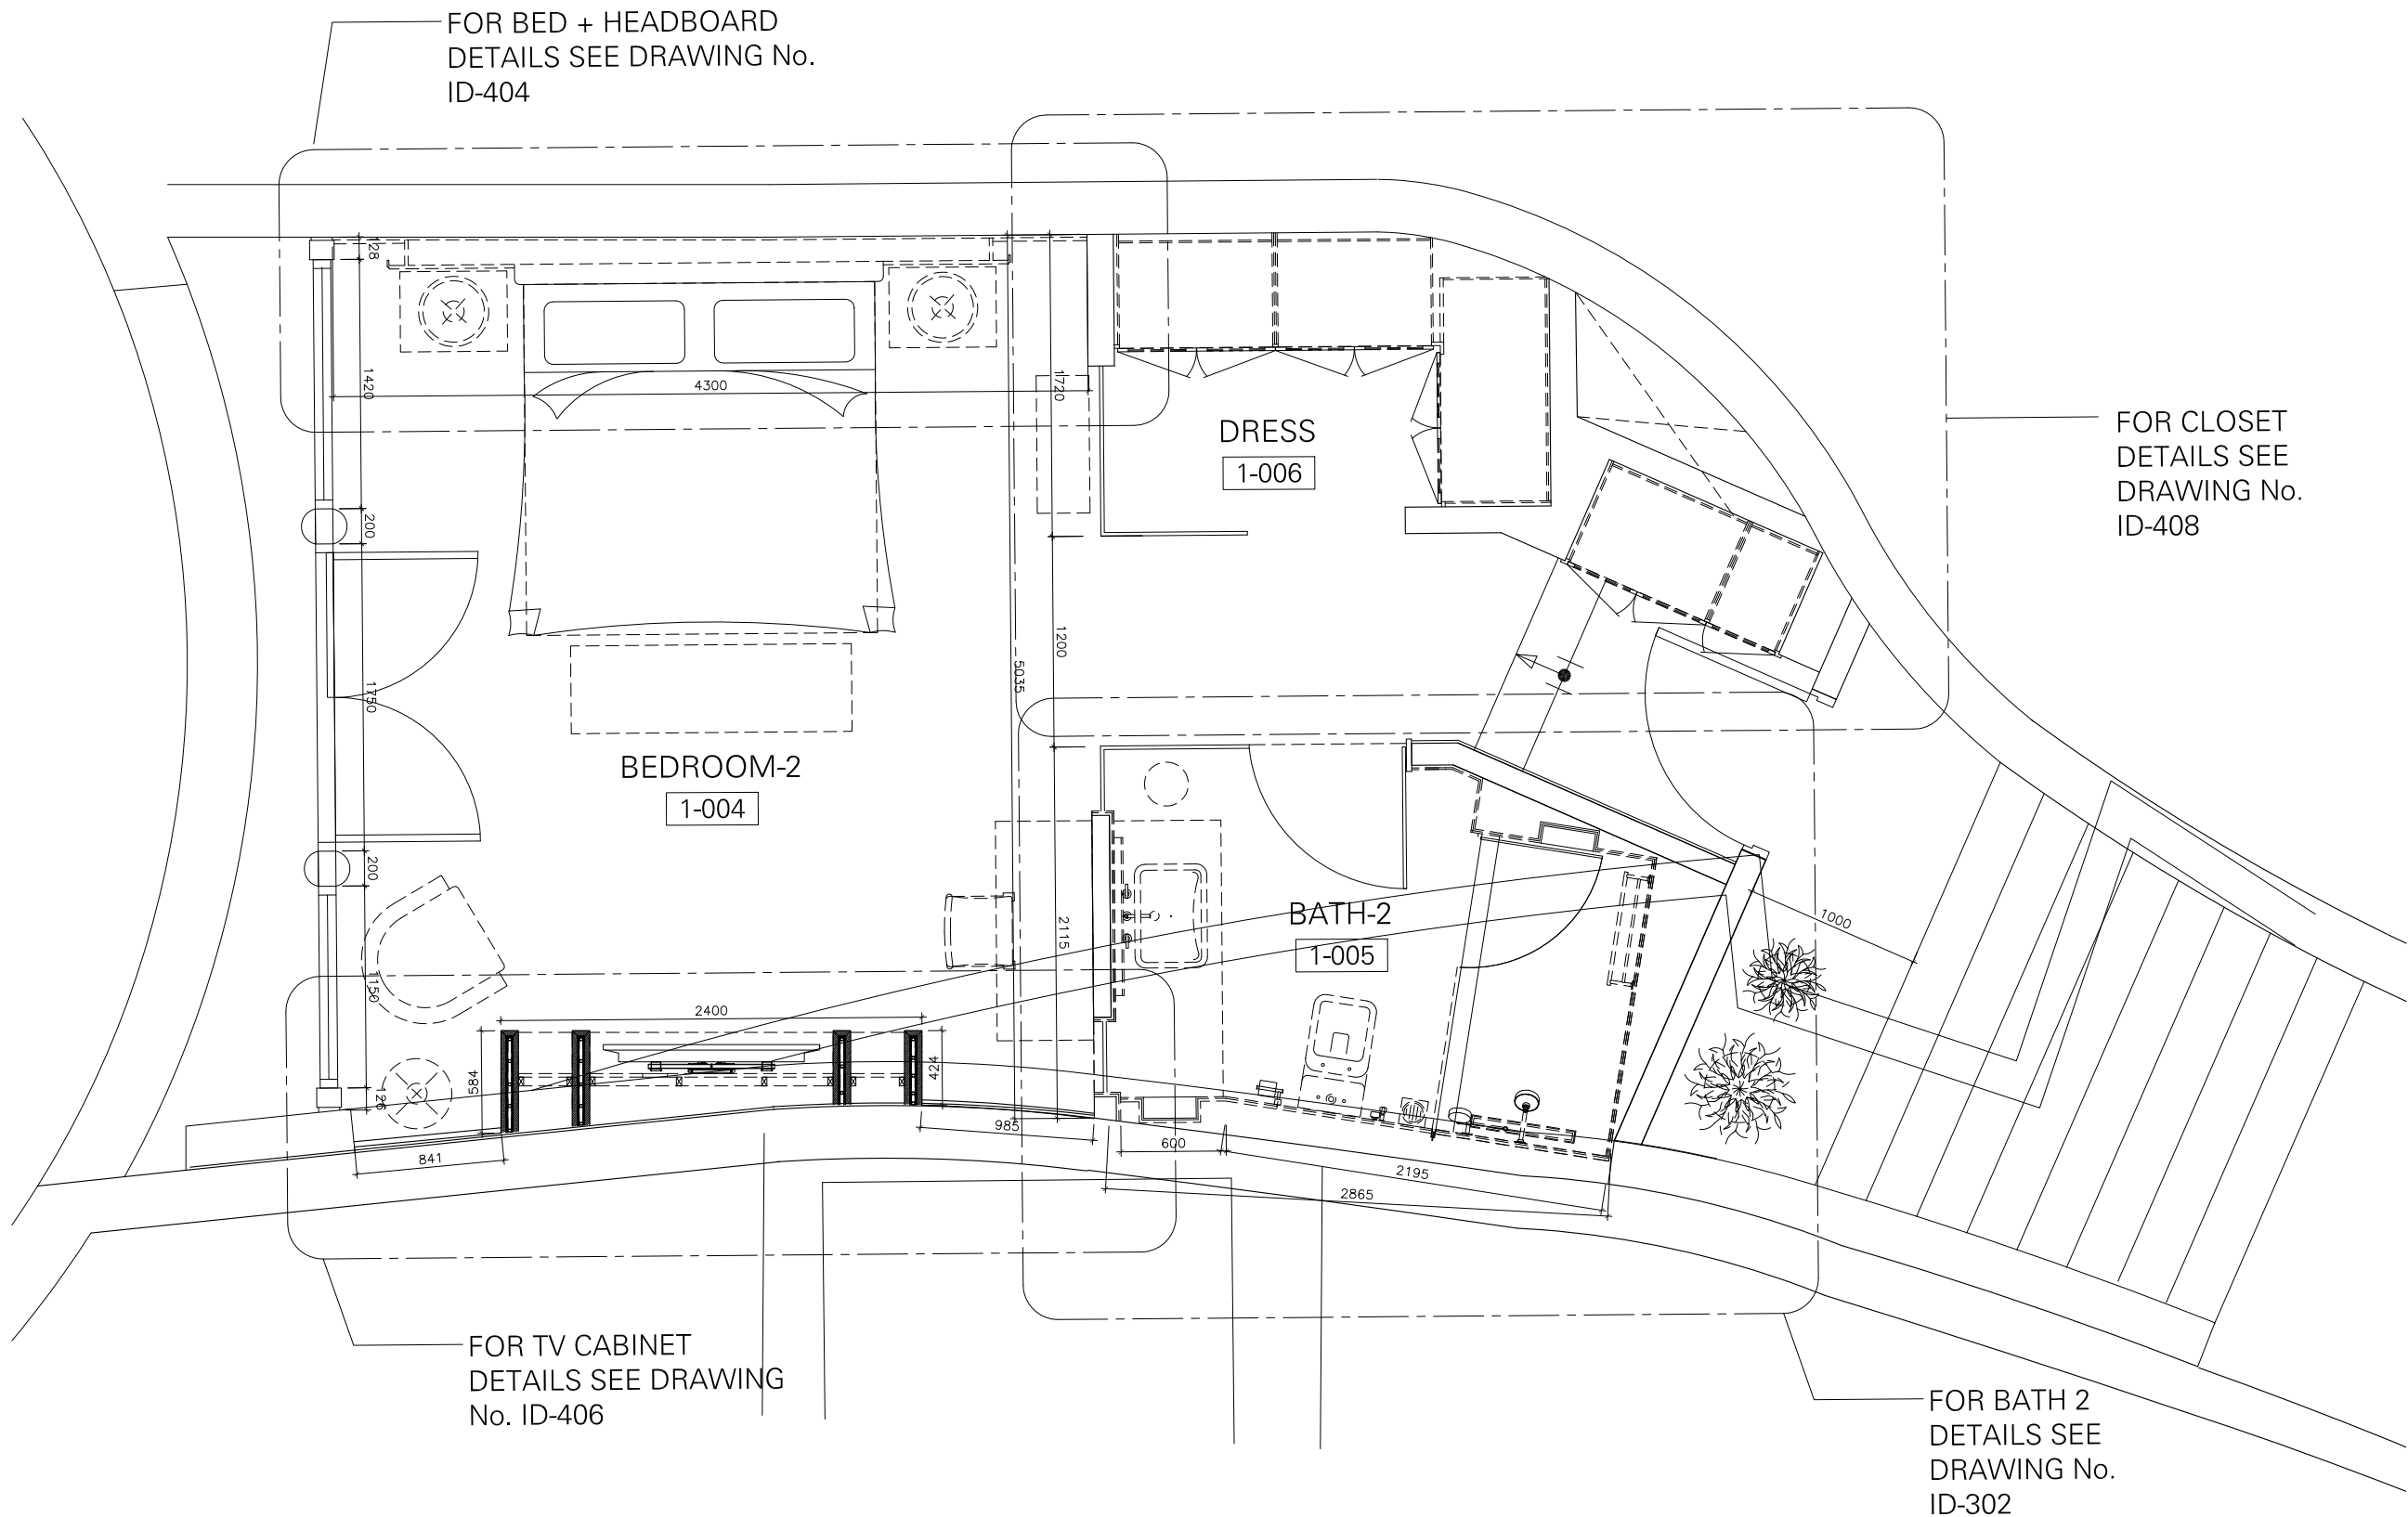


FIRST FLOOR - BEDROOM - 2 (1-004) PLAN
SCALE 1:25

- GENERAL NOTES**
1. This drawing shall be read in conjunction with all other relevant architectural, structural & electrical drawings including those of other consultants.
 2. It is the responsibility of contractors & manufacturers to check all relevant site dimensions prior to the start of construction or manufacture.
 3. All materials and components must be installed on site in accordance with manufacturer's instructions, shop drawings and standard details.
 4. All dimensions are in millimeters unless noted otherwise.
 5. Full working drawings, specifications and samples are to be provided by Contractor/Supplier for approval prior to manufacture.


KEY PLAN

INITIAL ISSUE	MP/AC	AM	SM	2025.02.11
REV.#	GENERAL NOTES	DRAWN BY	CHECKED BY	APPROVED BY
PROJECT TITLE				REFERENCE
KRR01-RIYADH				KRR01 G
DRAWING TITLE				
FIRST FLOOR (RIGHT SIDE) GUEST BEDROOM-2 GENERAL LAYOUT				
DRAWING NUMBER				REVISION
A-102				
SCALE	FORMAT	ADDITIONAL NOTES	DESIGN DEVELOPMENT	
1:20	A1			
SIMA MALAK + ALSSAMOURE DESIGN ASSOCIATES				
P.O. Box 15707 - Riyadh 11454 KSA Tel. 01 441 4963 - Fax. 01 441 3867 simals@simals.com				
©SIMA MALAK + ALSSAMOURE DESIGN ASSOCIATES (شركة) 2003 This document including all drawing and text is the property and copyright of SIMA MALAK + ALSSAMOURE DESIGN ASSOCIATES for use solely with respect to this Project and shall not be copied or reproduced by any means except by agreement in writing from SIMA MALAK + ALSSAMOURE DESIGN ASSOCIATES.				

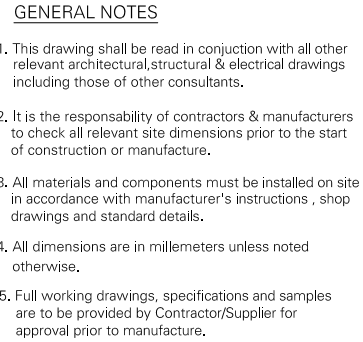

X	INITIAL ISSUE	MP/AC	AM	SM	2025.02.11	
REV#	GENERAL NOTES	DRAWN BY	CHECKED BY	APPROVED BY	DATE	
PROJECT TITLE						REFERENCE
KRR01-RIYADH						KRR01
						G

DRAWING TITLE			
GROUND FLOOR STAFF BEDROOM-5 & 6 GENERAL LAYOUT			
DRAWING NUMBER			REVISION
A-104			
SCALE	FORMAT	ADDITIONAL NOTES	DESIGN DEVELOPMENT
1:20	A1		

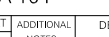


SIMA MALAK + ALSSAMDOURE
DESIGN ASSOCIATES

P.O. Box 15707 - Riyadh 11454 KSA
Tel. 01 441 4963 - Fax. 01 441 3867
simala@simala.com

SIMA MALAK + ALSSAMOURÉ DESIGN ASSOCIATES (مسامورة) 2003
This document including all drawing and text is the property and
copyright of SIMA MALAK + ALSSAMOURÉ DESIGN ASSOCIATES for
use solely with respect to this Project and shall not be copied or
reproduced by any means except by agreement in writing from
SIMA MALAK + ALSSAMOURÉ DESIGN ASSOCIATES.

STAFF BEDROOM - 5 & 6 PLAN

SCALE 1:25

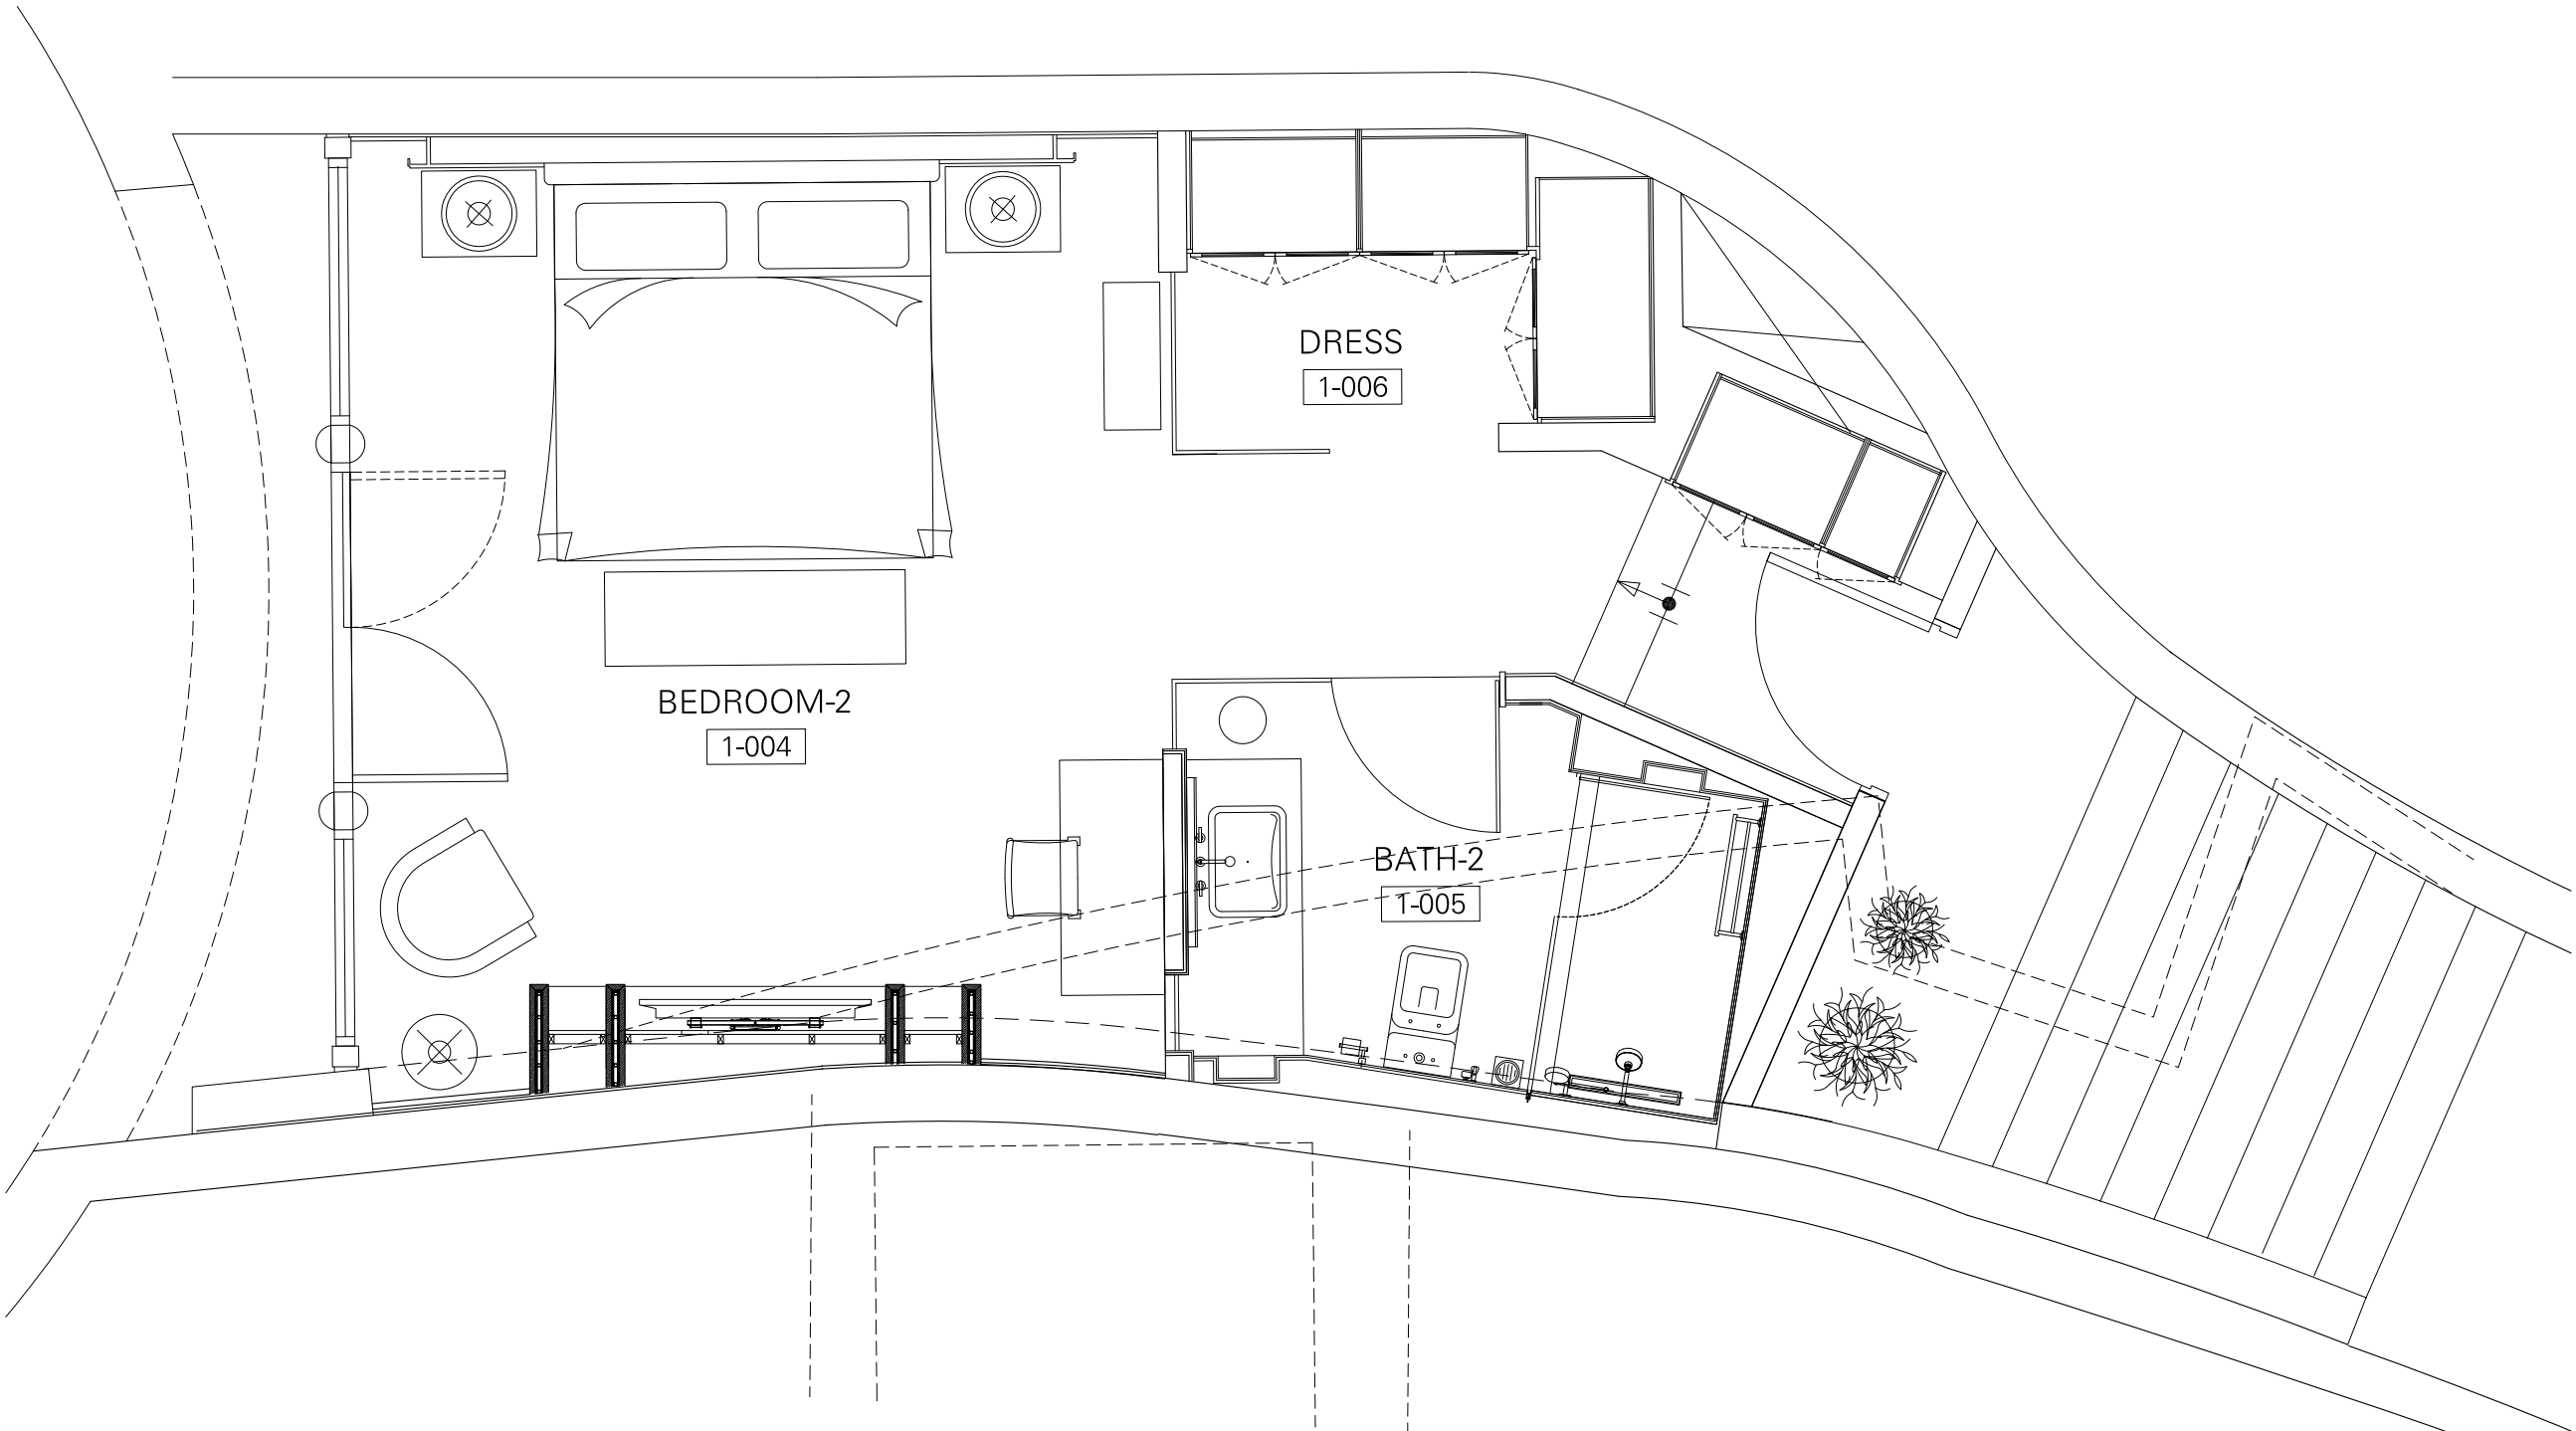

FIRST FLOOR - GUEST BEDROOM - 2 FURNITURE LAYOUT
SCALE 1:25

GENERAL NOTES

1. This drawing shall be read in conjunction with all other relevant architectural, structural & electrical drawings including those of other consultants.
2. It is the responsibility of contractors & manufacturers to check all relevant site dimensions prior to the start of construction or manufacture.
3. All materials and components must be installed on site in accordance with manufacturer's instructions, shop drawings and standard details.
4. All dimensions are in millimeters unless noted otherwise.
5. Full working drawings, specifications and samples are to be provided by Contractor/Supplier for approval prior to manufacture.


KEY PLAN

☒	INITIAL ISSUE	MP/AC	AM	SM	2025.02.11
REV.#	GENERAL NOTES	DRAWN BY	CHECKED BY	APPROVED BY	DATE
PROJECT TITLE				REFERENCE	
KRR01-RIYADH				KRR01 G	

DRAWING TITLE					
FIRST FLOOR (RIGHT SIDE) GUEST BEDROOM-2 FURNITURE LAYOUT					
DRAWING NUMBER					REVISION
ID-102					
SCALE	FORMAT	ADDITIONAL NOTES	DESIGN DEVELOPMENT		
1:20	A1				

**SIMA MALAK + ALSSAMOURE
DESIGN ASSOCIATES**
P.O. Box 15707 - Riyadh 11454 KSA
Tel. 01 441 4963 - Fax. 01 441 3867
simals@simals.com


©SIMA MALAK + ALSSAMOURE DESIGN ASSOCIATES (شركة) 2003
This document including all drawing and text is the property and
copyright of SIMA MALAK + ALSSAMOURE DESIGN ASSOCIATES for
use solely with respect to this Project and shall not be copied or
reproduced by any means except by agreement in writing from
SIMA MALAK + ALSSAMOURE DESIGN ASSOCIATES.

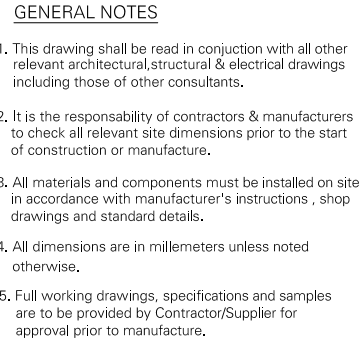

PROJECT TITLE	REFERENCE
KRR01-RIYADH	KRR01
	G

DRAWING NUMBER	REVISION
ID-104	

©SIMA MALAK + ALSSAMOURÉ DESIGN ASSOCIATES (سمير) 2003
This document including all drawing and text is the property and
copyright of SIMA MALAK + ALSSAMOURÉ DESIGN ASSOCIATES for
use solely with respect to this Project and shall not be copied or
reproduced by any means except by agreement in writing from
SIMA MALAK + ALSSAMOURÉ DESIGN ASSOCIATES.

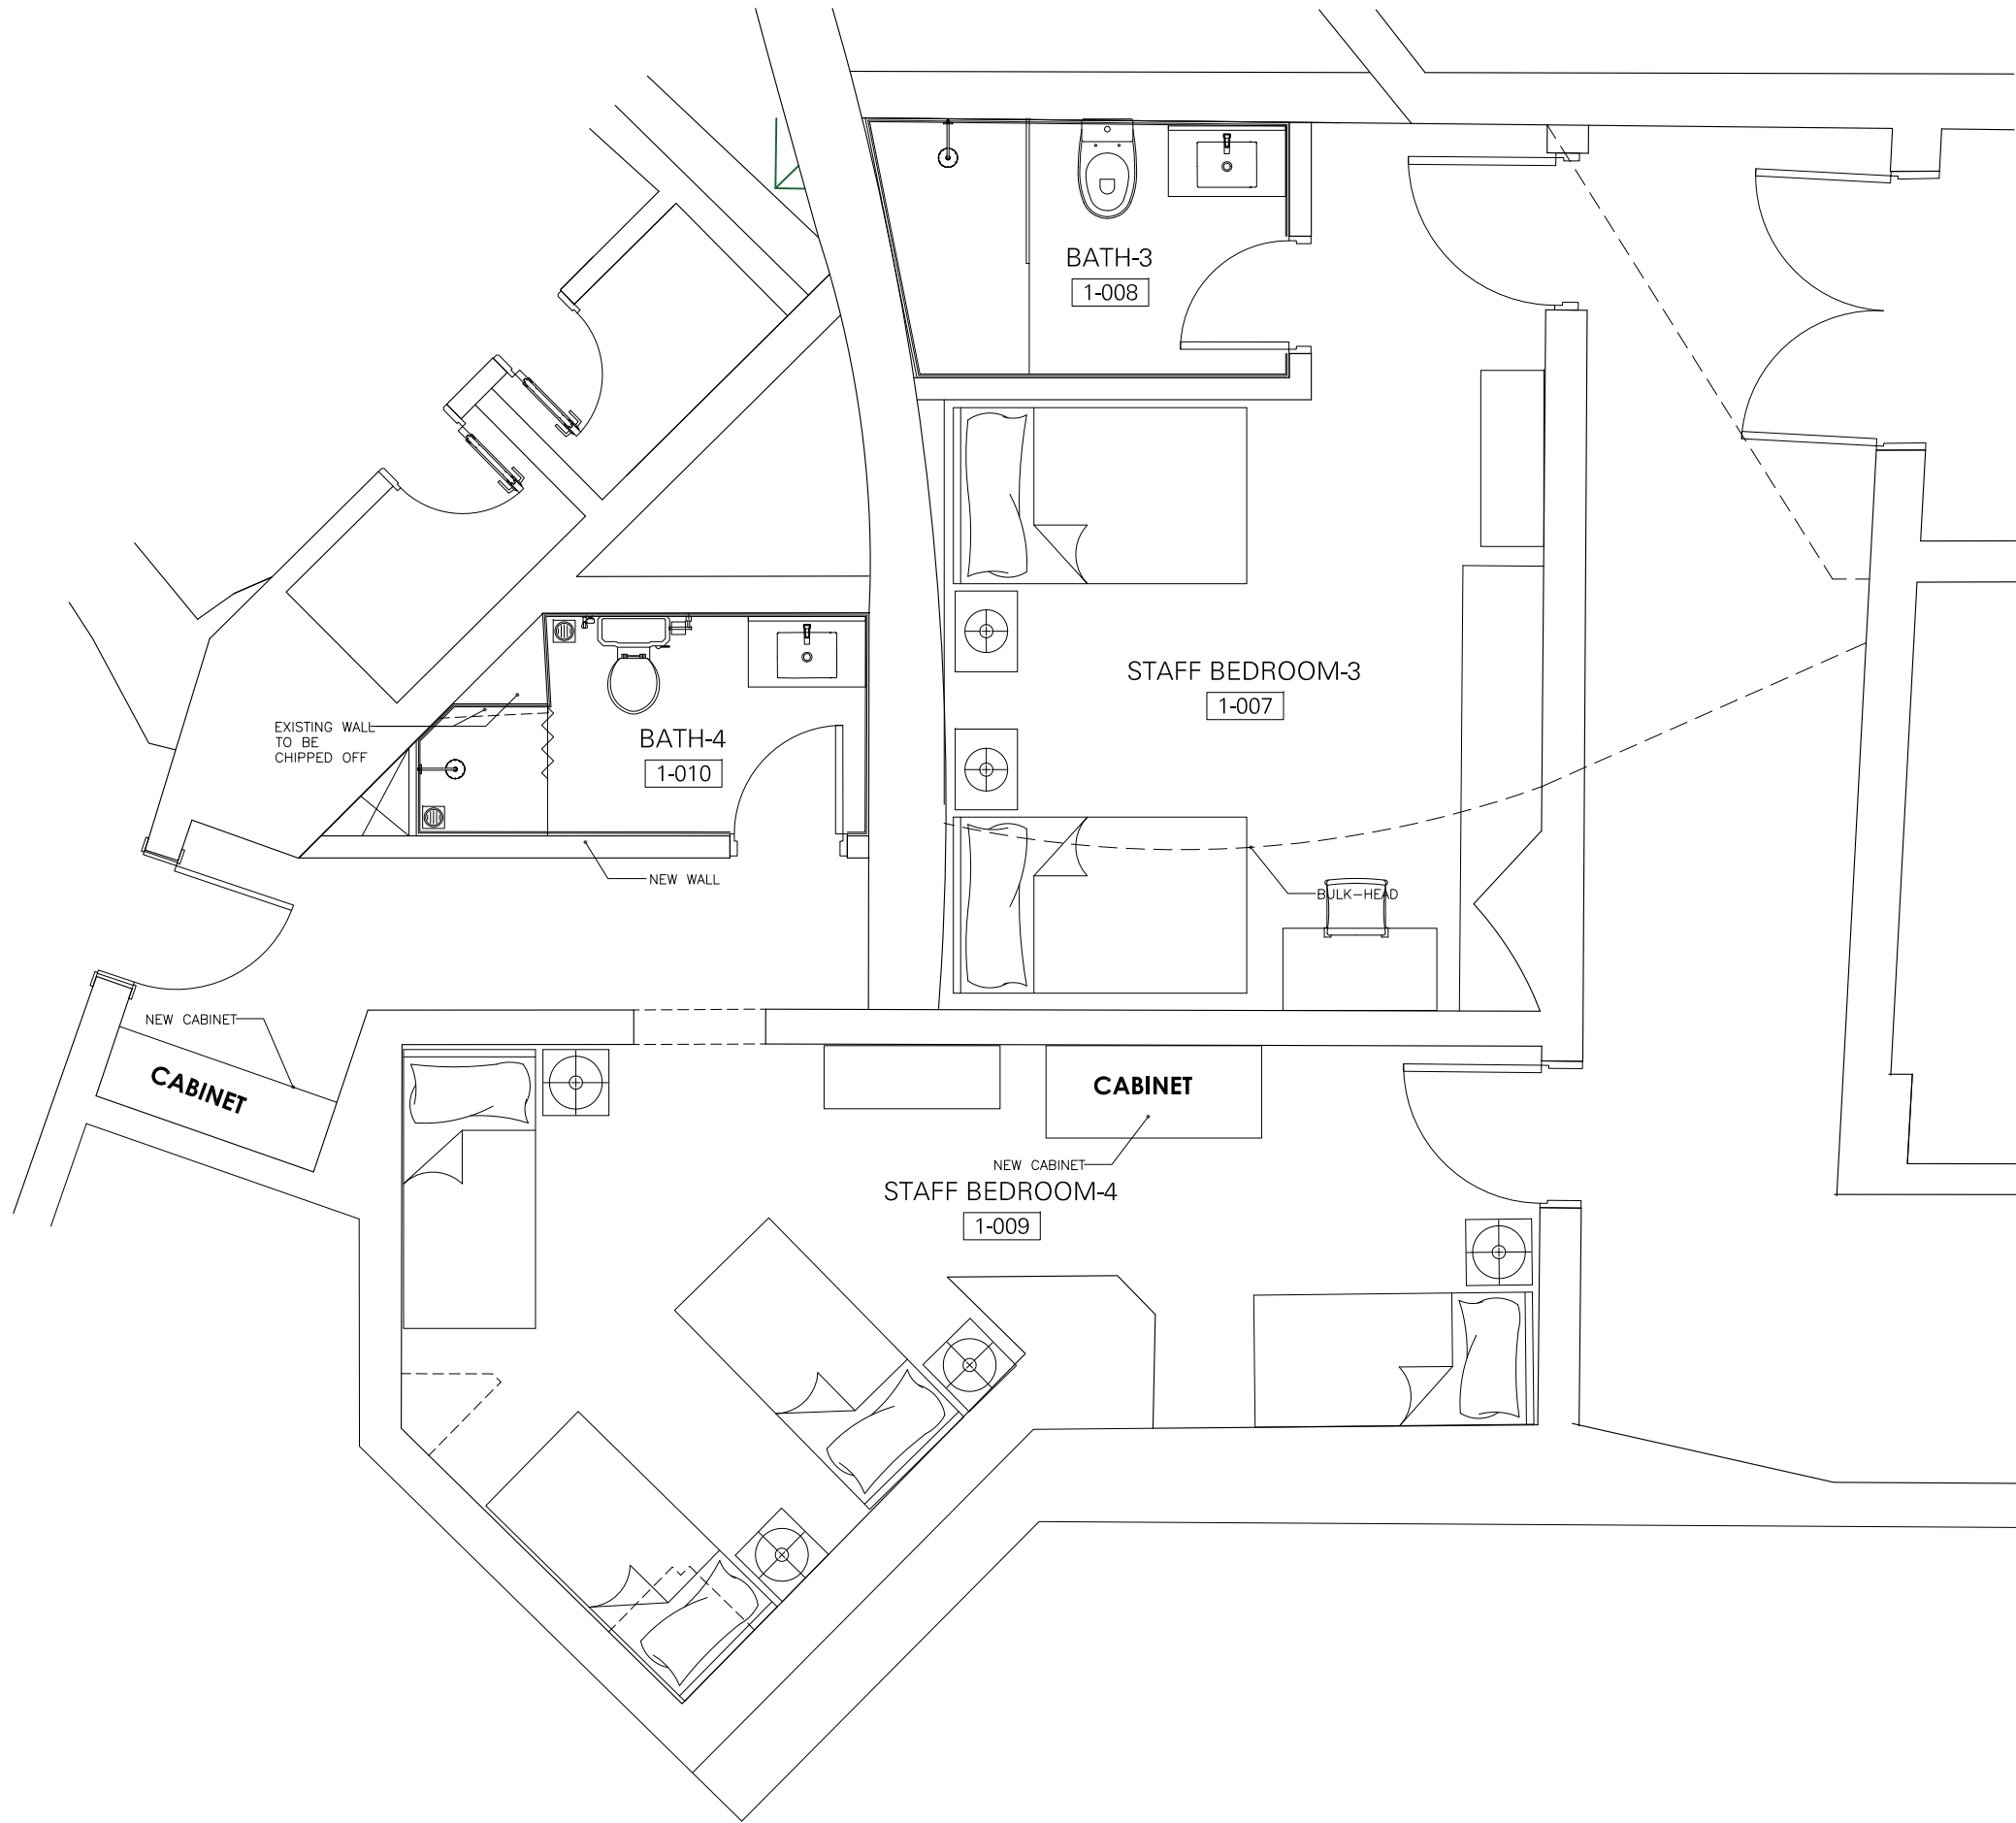

STAFF BEDROOM - 3 & 4 FURNITURE LAYOUT

SCALE 1:25

GENERAL NOTES

1. This drawing shall be read in conjunction with all other relevant architectural, structural & electrical drawings including those of other consultants.
2. It is the responsibility of contractors & manufacturers to check all relevant site dimensions prior to the start of construction or manufacture.
3. All materials and components must be installed on site in accordance with manufacturer's instructions, shop drawings and standard details.
4. All dimensions are in millimeters unless noted otherwise.
5. Full working drawings, specifications and samples are to be provided by Contractor/Supplier for approval prior to manufacture.


KEY PLAN

☒	INITIAL ISSUE	MP/AC	AM	SM	2025.02.11
REV.#	GENERAL NOTES	DRAWN BY	CHECKED BY	APPROVED BY	DATE
PROJECT TITLE				REFERENCE	
KRR01-RIYADH				KRR01 G	

DRAWING TITLE		REVISION	
GROUND FLOOR STAFF BEDROOM-3 & 4 FURNITURE LAYOUT			
DRAWING NUMBER			
ID-103			
SCALE	FORMAT	ADDITIONAL NOTES	DESIGN DEVELOPMENT
1:20	A1		

**SIMA MALAK + ALSSAMOURE
DESIGN ASSOCIATES**
P.O. Box 15707 - Riyadh 11454 KSA
Tel. 01 441 4963 - Fax. 01 441 3867
simals@simals.com

©SIMA MALAK + ALSSAMOURE DESIGN ASSOCIATES (شركة) 2003
This document including all drawing and text is the property and
copyright of SIMA MALAK + ALSSAMOURE DESIGN ASSOCIATES for
use solely with respect to this Project and shall not be copied or
reproduced by any means except by agreement in writing from
SIMA MALAK + ALSSAMOURE DESIGN ASSOCIATES.

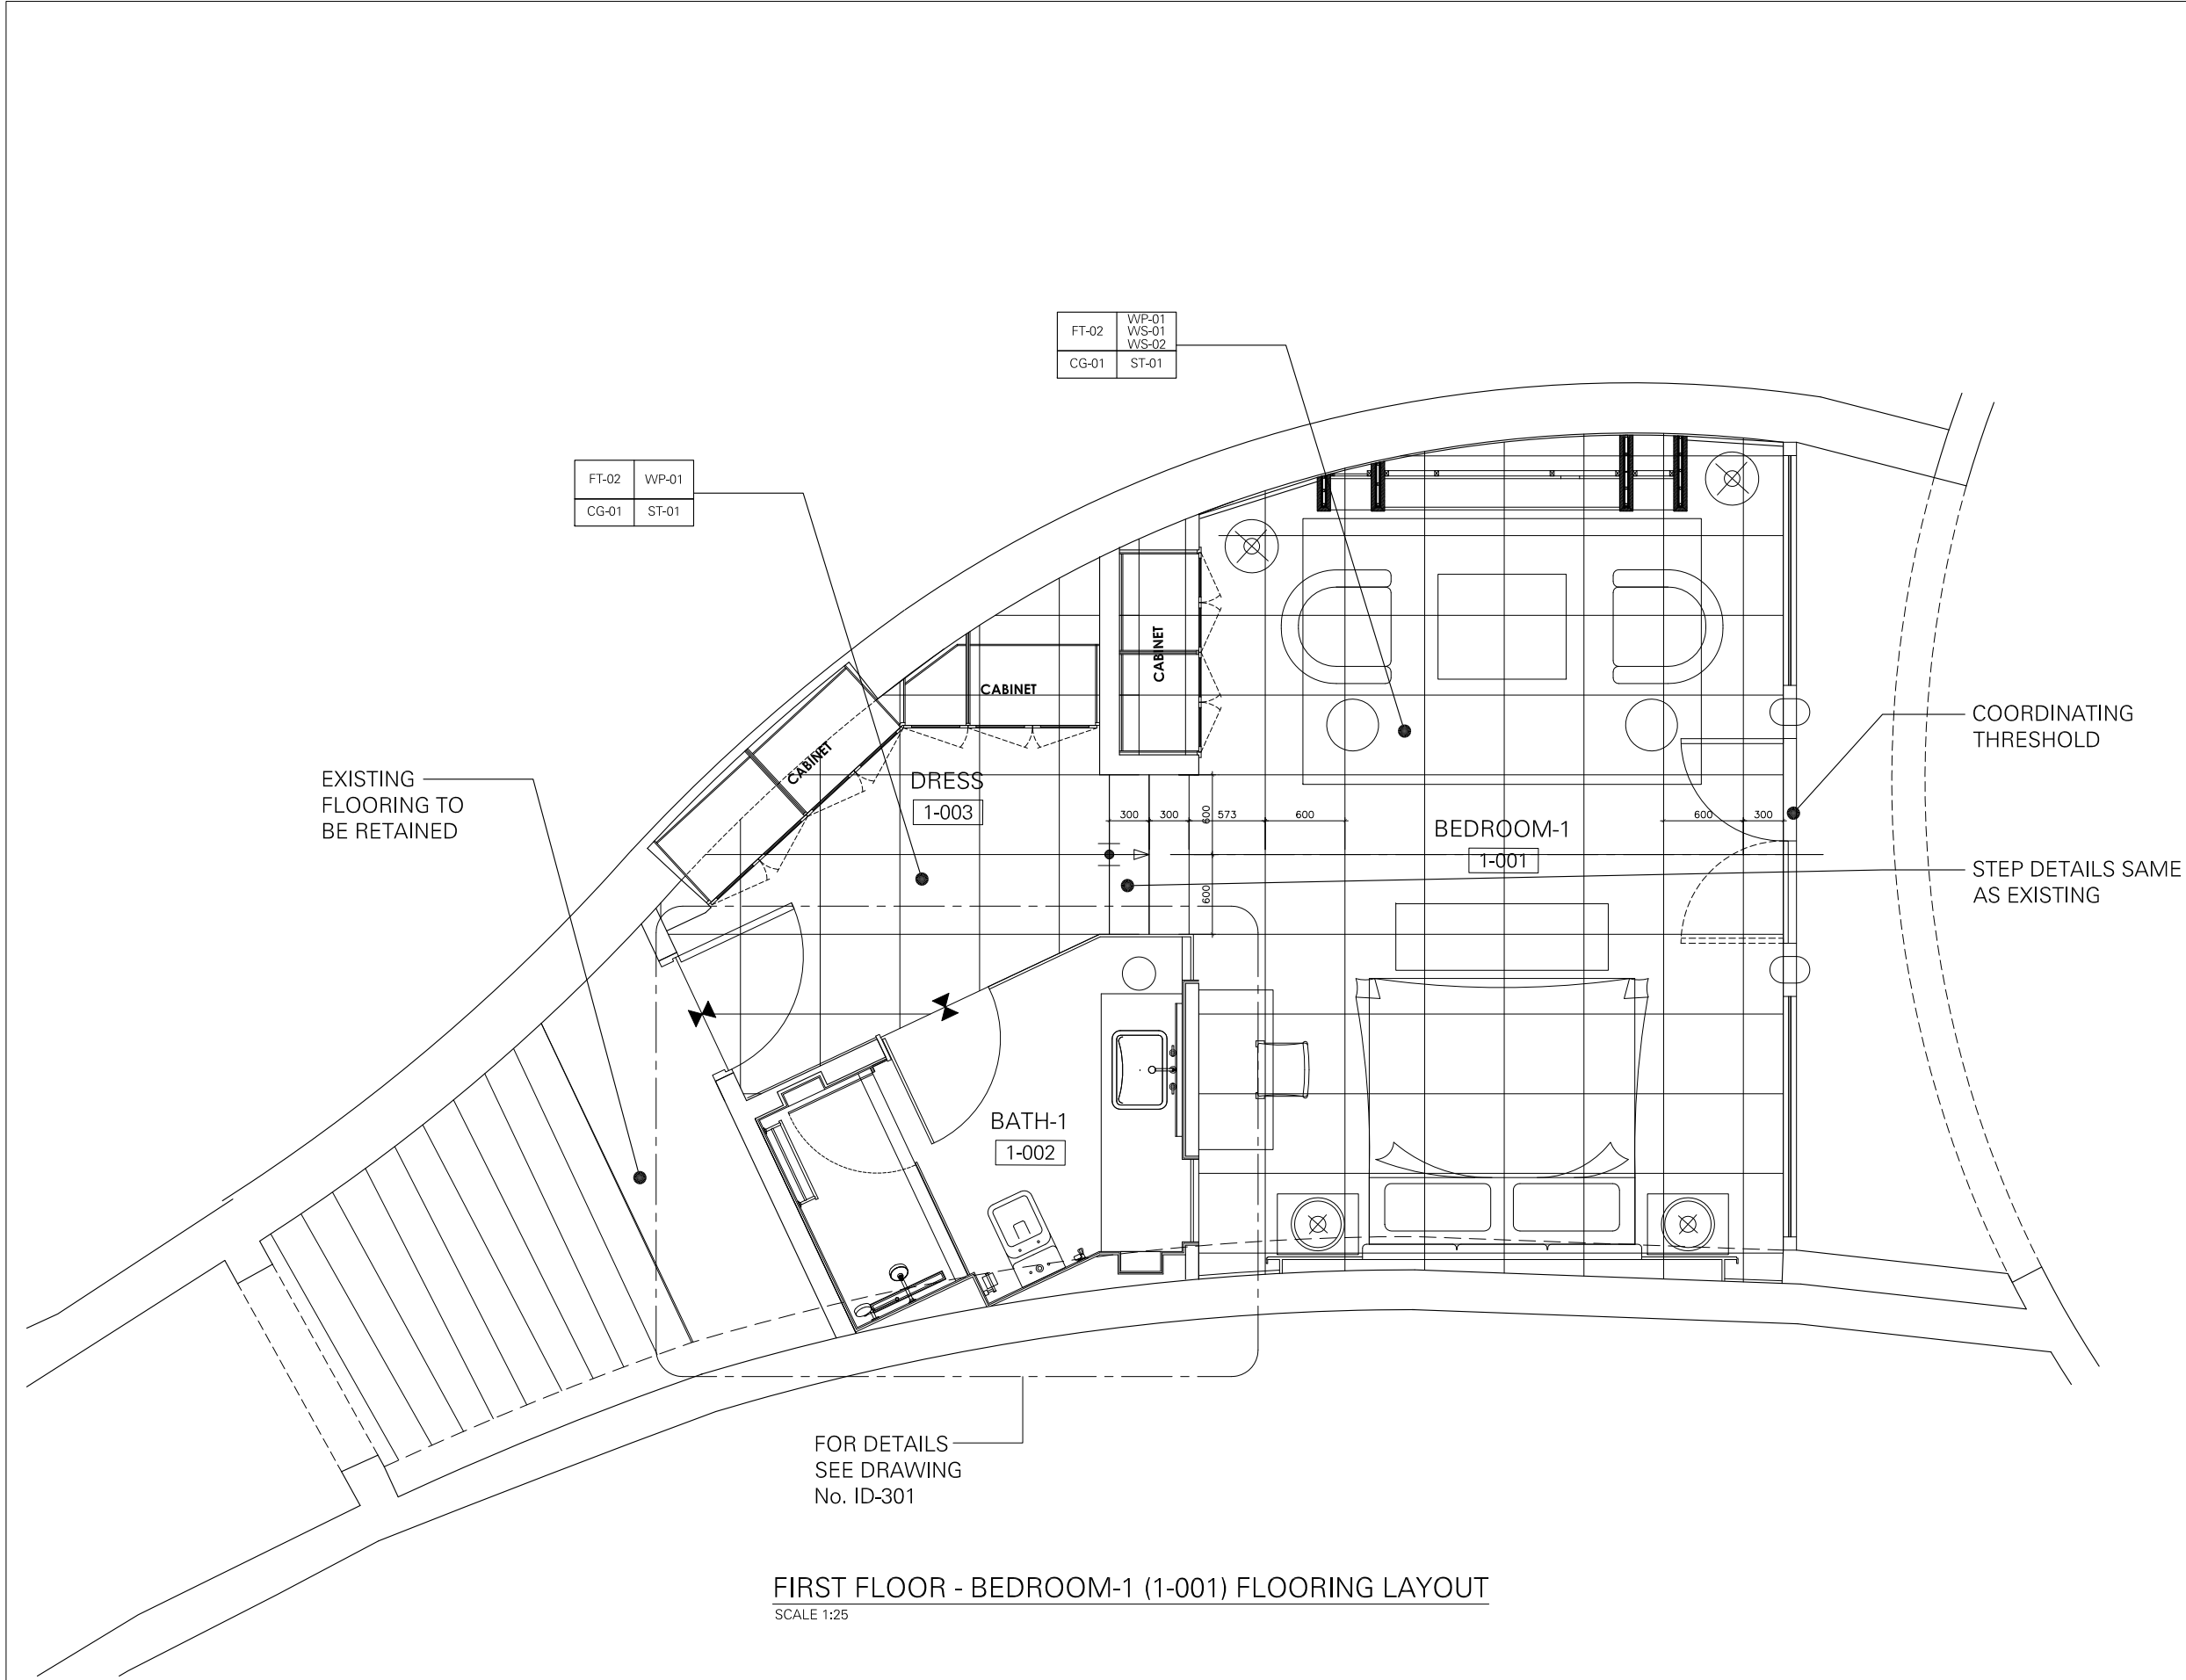

FIRST FLOOR - BEDROOM-1 (1-001) FLOORING LAYOUT
SCALE 1:25

GENERAL NOTES

1. This drawing shall be read in conjunction with all other relevant architectural, structural & electrical drawings including those of other consultants.
2. It is the responsibility of contractors & manufacturers to check all relevant site dimensions prior to the start of construction or manufacture.
3. All materials and components must be installed on site in accordance with manufacturer's instructions, shop drawings and standard details.
4. All dimensions are in millimeters unless noted otherwise.
5. Full working drawings, specifications and samples are to be provided by Contractor/Supplier for approval prior to manufacture.

LEGEND

—X— - Finish Transition / Change in Material

WS-01 - Finish Type

Floor Finish Reference
Wall Finish Reference
Ceiling Finish Reference
Skirting Finish Reference

FINISHES

1. Full working drawings, specifications and samples are to be provided by Contractor/Supplier for approval prior to manufacture.
2. Please Refer to Finishing Schedule for full specifications: KRR01.2.4.1-FIN

KEY PLAN


X	INITIAL ISSUE	MP/AC	AM	SM	2025.02.11
REV.#	GENERAL NOTES	DRAWN BY	CHECKED BY	APPROVED BY	DATE
PROJECT TITLE					REFERENCE
KRR01-RIYADH					KRR01 G

DRAWING TITLE	
FIRST FLOOR (LEFT SIDE) GUEST BEDROOM-1 FLOORING LAYOUT	
DRAWING NUMBER	REVISION
ID-105	

SCALE	FORMAT	ADDITIONAL NOTES	DESIGN DEVELOPMENT
1:20	A1		

**SIMA MALAK + ALSSAMOURE
DESIGN ASSOCIATES**
P.O. Box 15707 - Riyadh 11454 KSA
Tel. 01 441 4963 - Fax. 01 441 3867
simals@simals.com

©SIMA MALAK + ALSSAMOURE DESIGN ASSOCIATES (شركة) 2003
This document including all drawing and text is the property and
copyright of SIMA MALAK + ALSSAMOURE DESIGN ASSOCIATES for
use solely with respect to this Project and shall not be copied or
reproduced by any means except by agreement in writing from
SIMA MALAK + ALSSAMOURE DESIGN ASSOCIATES.

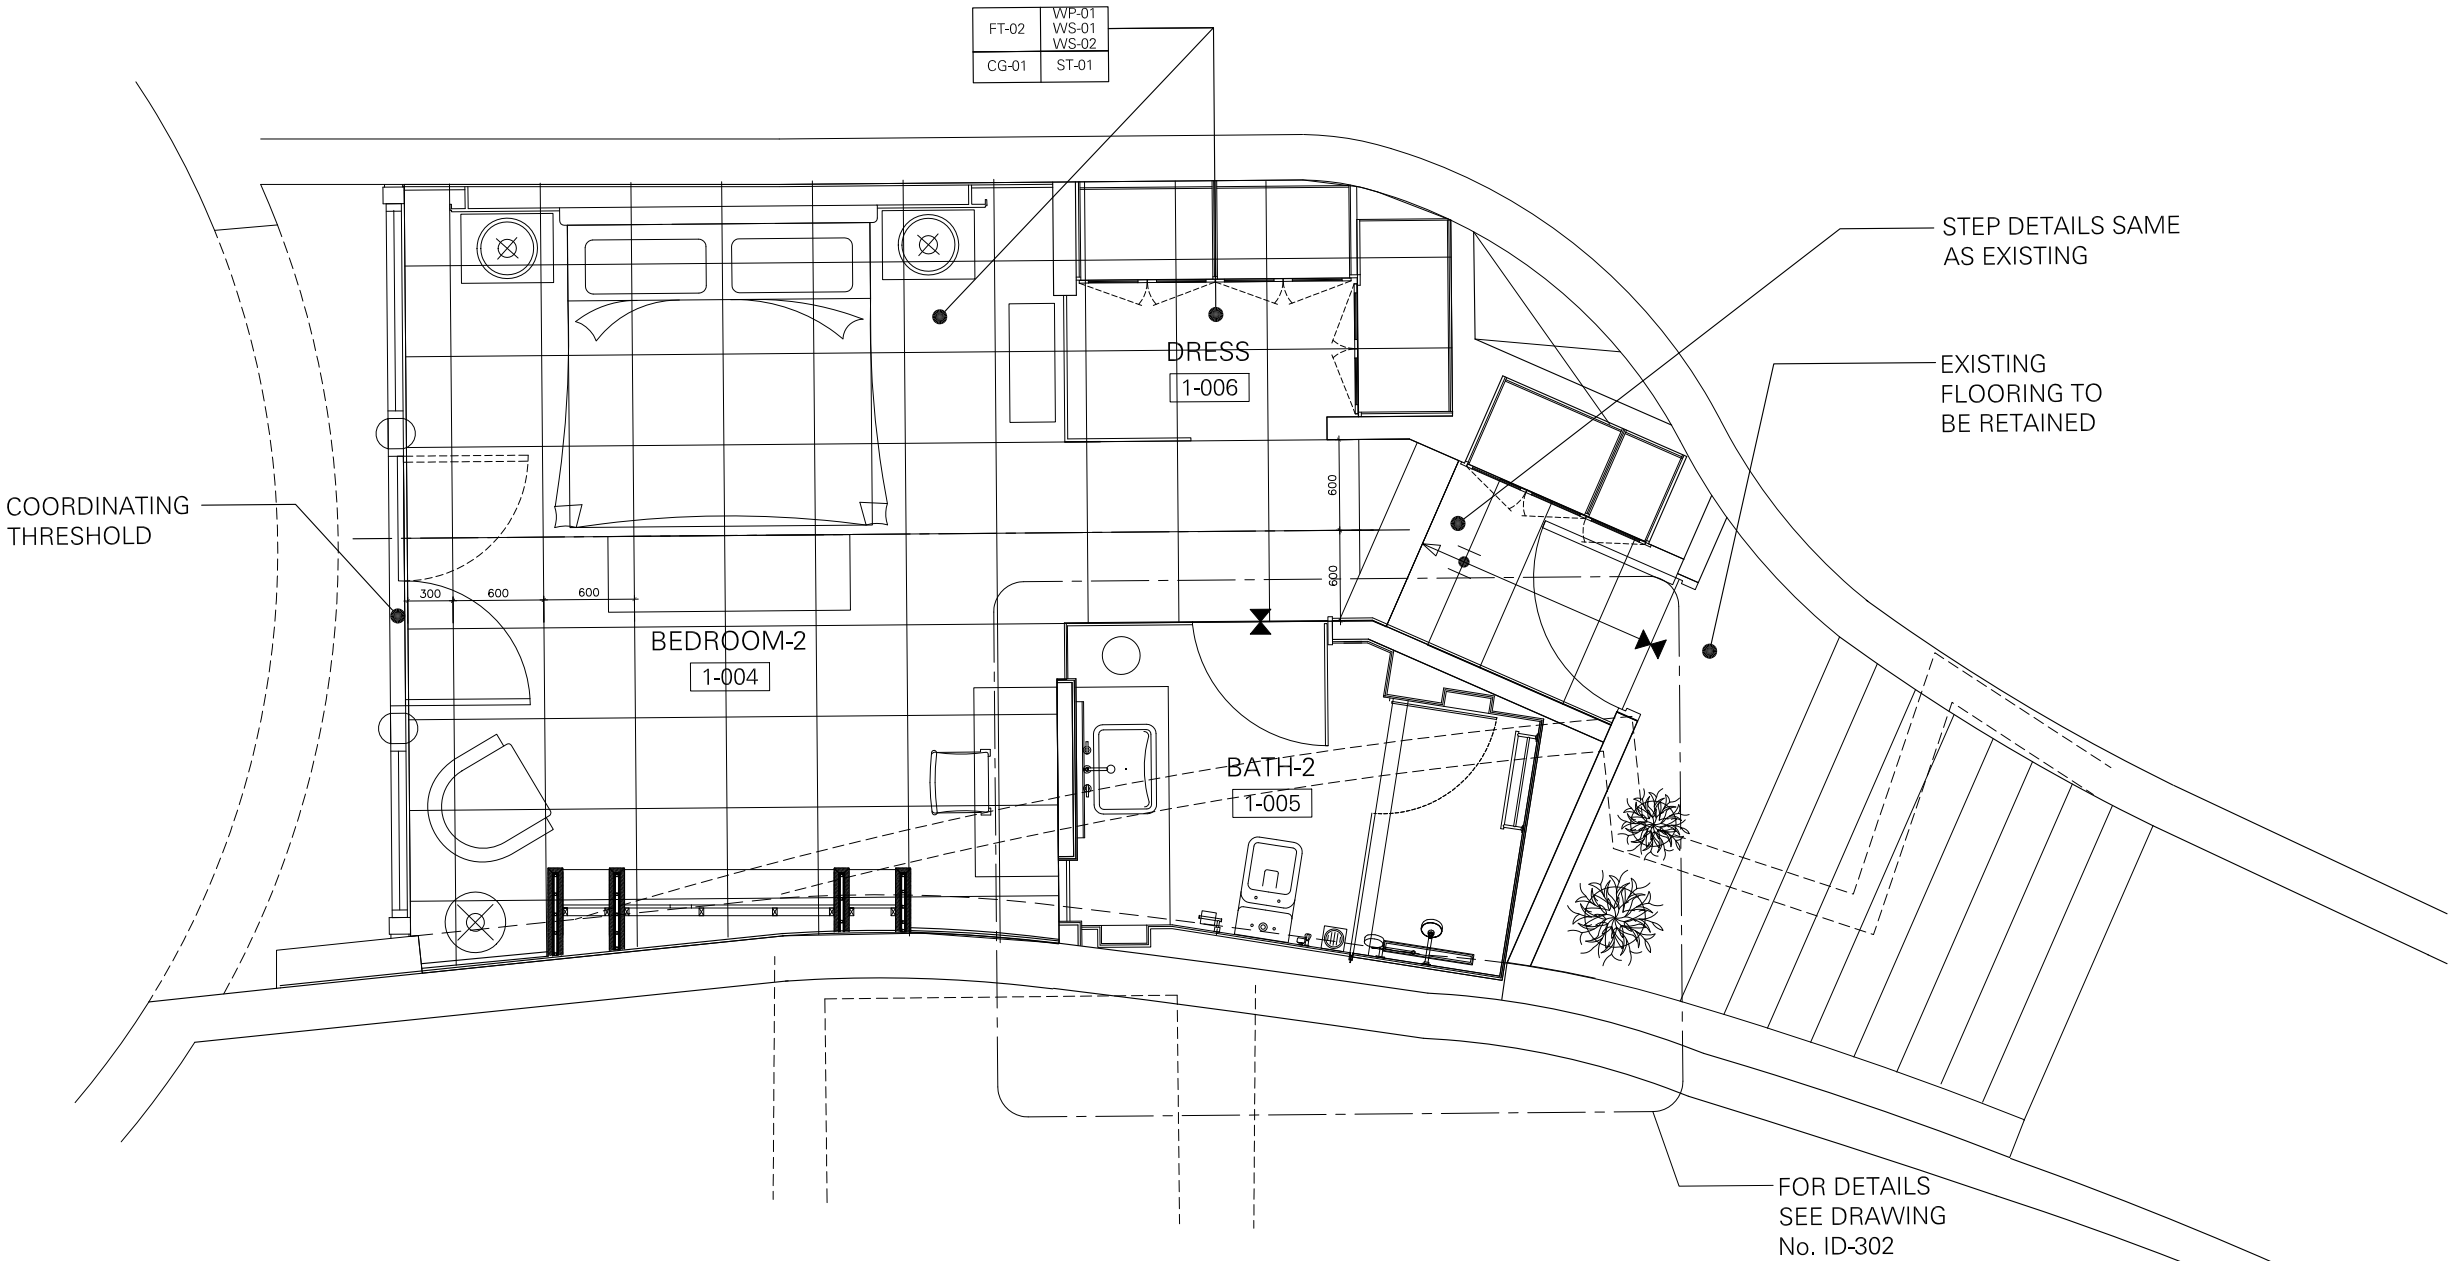


FIRST FLOOR - BEDROOM-2 (1-004) FLOORING LAYOUT
SCALE 1:25

GENERAL NOTES

1. This drawing shall be read in conjunction with all other relevant architectural, structural & electrical drawings including those of other consultants.
2. It is the responsibility of contractors & manufacturers to check all relevant site dimensions prior to the start of construction or manufacture.
3. All materials and components must be installed on site in accordance with manufacturer's instructions, shop drawings and standard details.
4. All dimensions are in millimeters unless noted otherwise.
5. Full working drawings, specifications and samples are to be provided by Contractor/Supplier for approval prior to manufacture.

—X— - Finish Transition / Change in Material

WS-01 - Finish Type

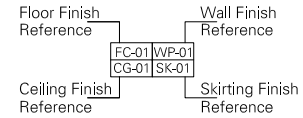

FINISHES

1. Full working drawings, specifications and samples are to be provided by Contractor/Supplier for approval prior to manufacture.
2. Please Refer to Finishing Schedule for full specifications: KRR01.2.4.1-FIN

KEY PLAN

X	INITIAL ISSUE	AC	AM	SM	2025.02.11
REV.#	GENERAL NOTES	DRAWN BY	CHECKED BY	APPROVED BY	DATE

PROJECT TITLE	REFERENCE
---------------	-----------

KRR01-RIYADH	KRR01
	G

DRAWING TITLE

FIRST FLOOR (RIGHT SIDE)
GUEST BEDROOM-2
FLOORING LAYOUT

DRAWING NUMBER	REVISION
----------------	----------


ID-106

SCALE	FORMAT	ADDITIONAL NOTES	DESIGN DEVELOPMENT
1:20	A1		




**SIMA MALAK + ALSSAMOURE
DESIGN ASSOCIATES**
P.O. Box 15707 - Riyadh 11454 KSA
Tel. 01 441 4963 - Fax. 01 441 3867
simals@simals.com

©SIMA MALAK + ALSSAMOURE DESIGN ASSOCIATES (شركة) 2003
This document including all drawing and text is the property and copyright of SIMA MALAK + ALSSAMOURE DESIGN ASSOCIATES for use solely with respect to this Project and shall not be copied or reproduced by any means except by agreement in writing from SIMA MALAK + ALSSAMOURE DESIGN ASSOCIATES.

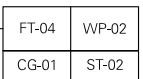

©SIMA MALAK + ALSSAMOURI DESIGN ASSOCIATES (مـ) 2003
This document including all drawing and text is the property and
copyright of SIMA MALAK + ALSSAMOURI DESIGN ASSOCIATES for
use solely with respect to this Project and shall not be copied or
reproduced by any means except by agreement in writing from
SIMA MALAK + ALSSAMOURI DESIGN ASSOCIATES.

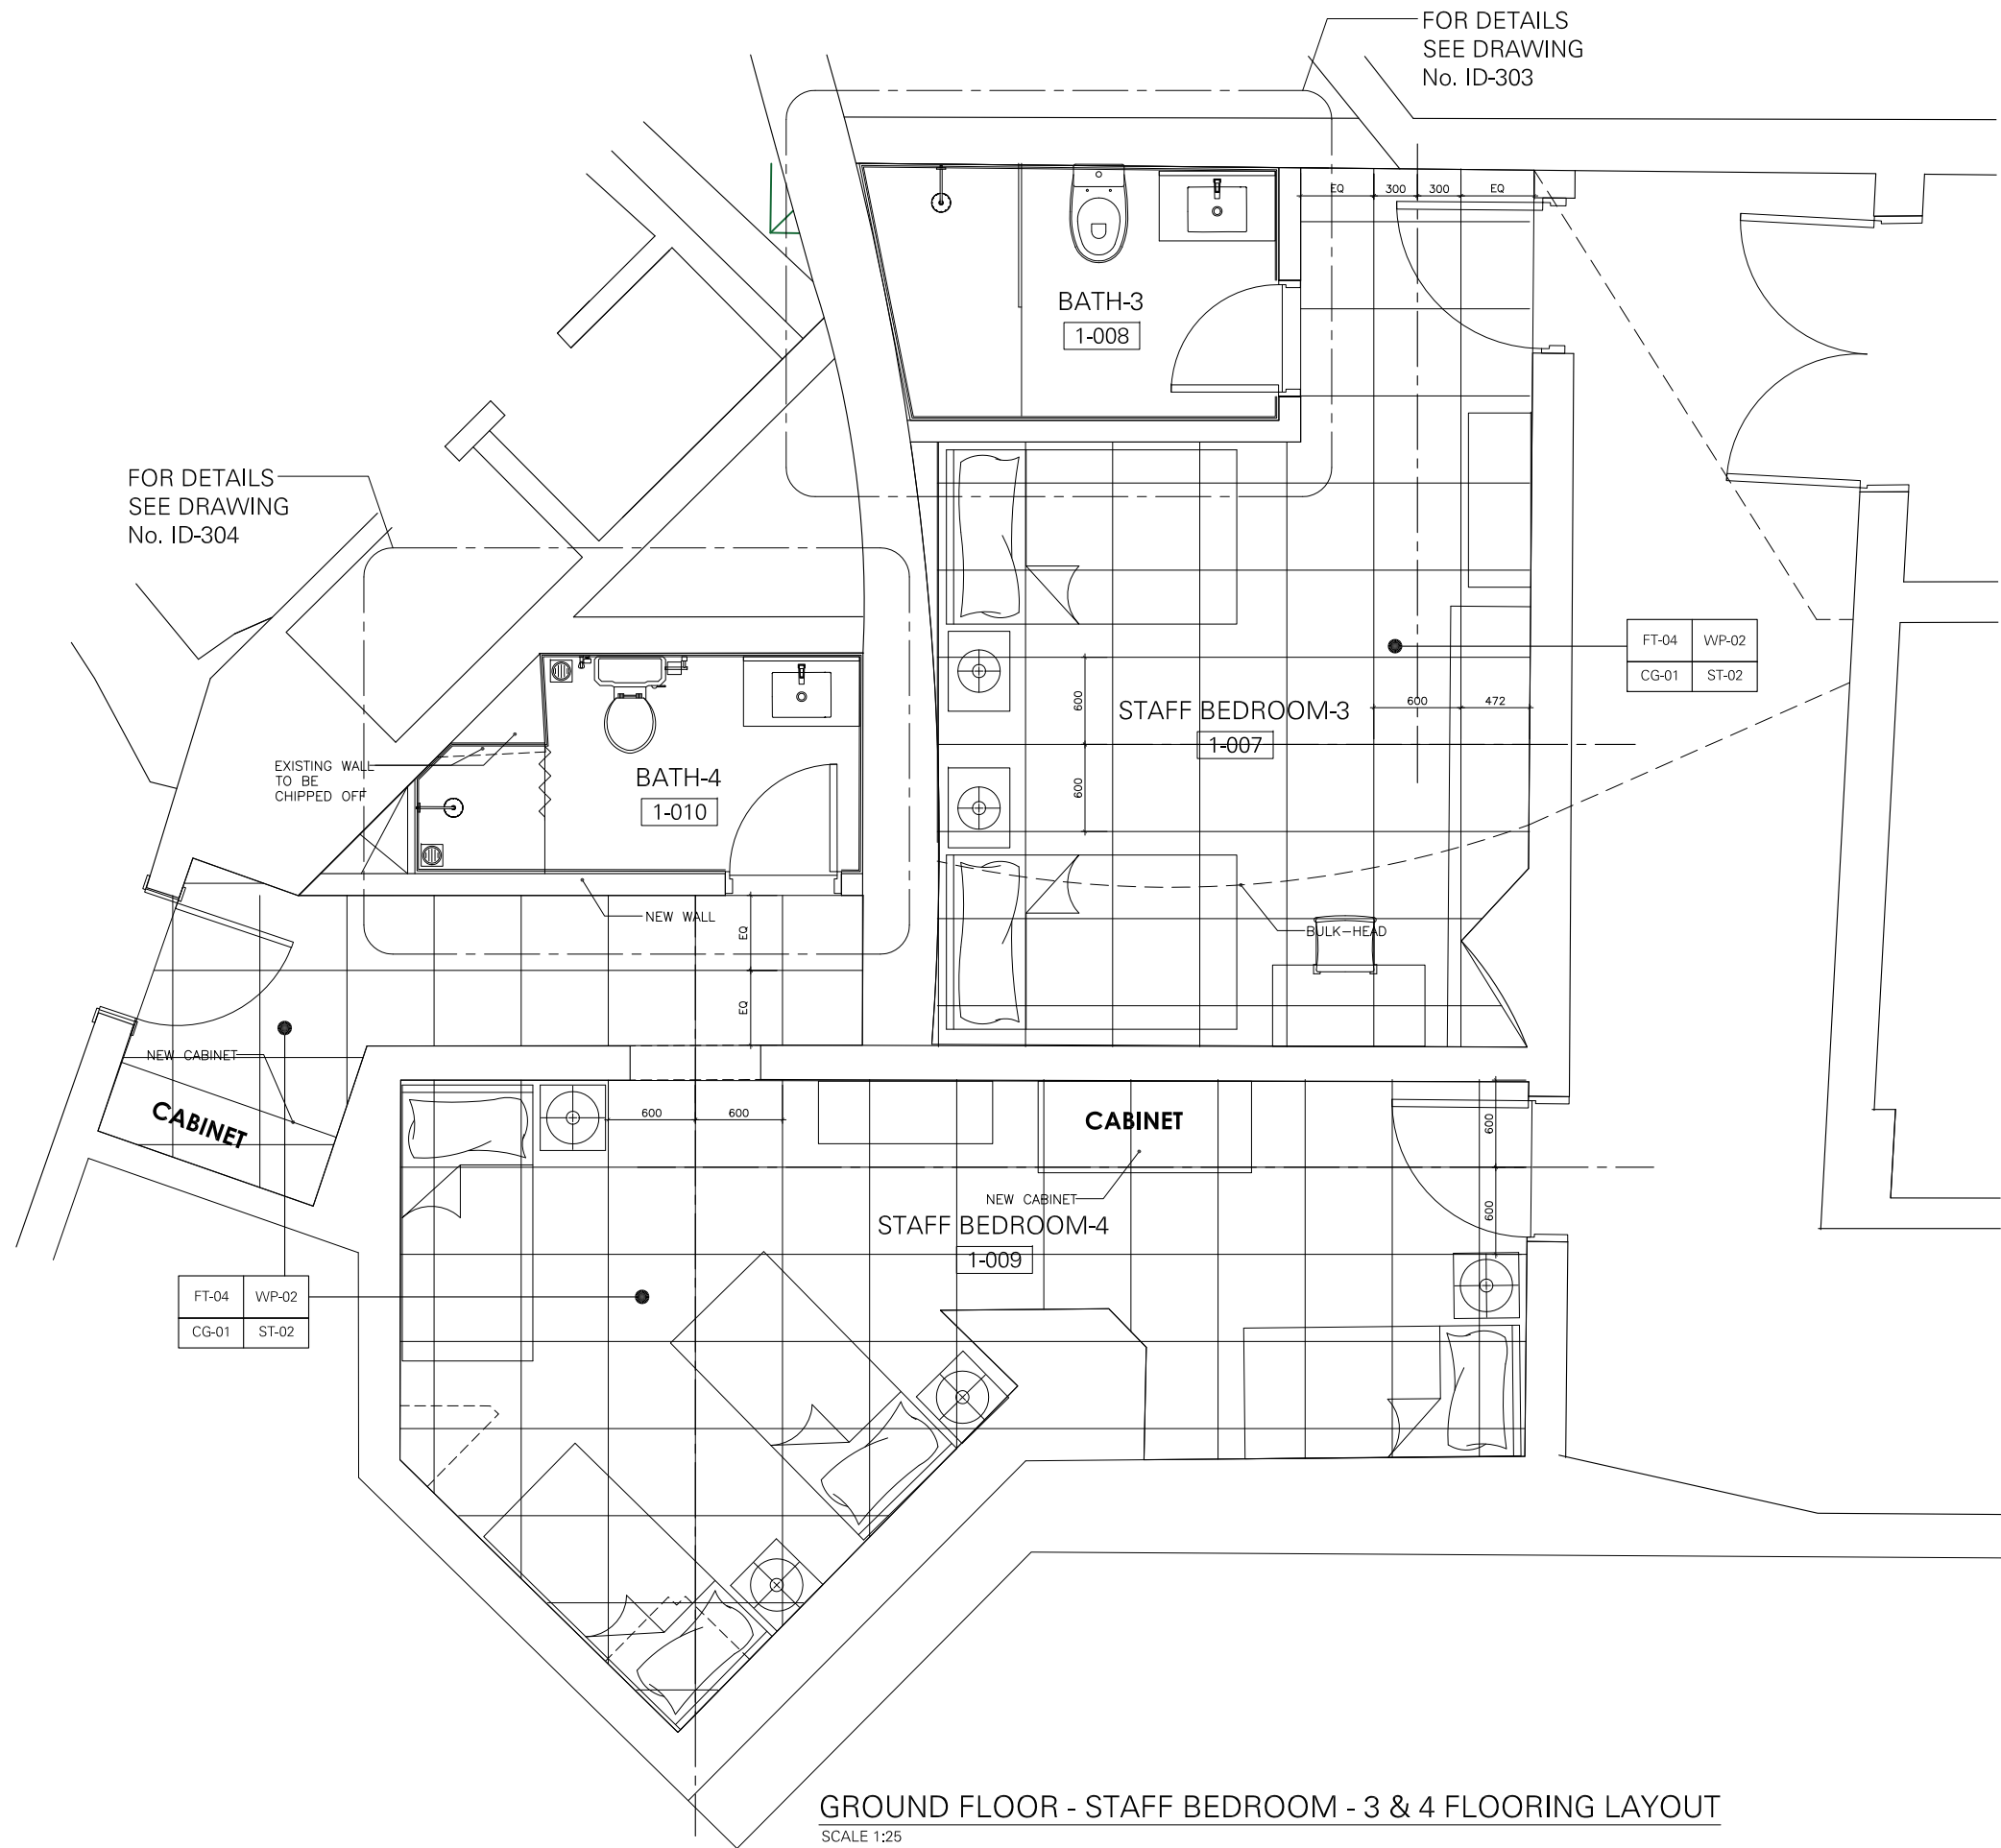

GENERAL NOTES

1. This drawing shall be read in conjunction with all other relevant architectural, structural & electrical drawings including those of other consultants.
2. It is the responsibility of contractors & manufacturers to check all relevant site dimensions prior to the start of construction or manufacture.
3. All materials and components must be installed on site in accordance with manufacturer's instructions, shop drawings and standard details.
4. All dimensions are in millimeters unless noted otherwise.
5. Full working drawings, specifications and samples are to be provided by Contractor/Supplier for approval prior to manufacture.

✂ - Finish Transition / Change in Material

WS-01 - Finish Type

Floor Finish Reference
Wall Finish Reference
Ceiling Finish Reference
Skirting Finish Reference

FC-01 WP-01
CG-01 SK-01

FINISHES

1. Full working drawings, specifications and samples are to be provided by Contractor/Supplier for approval prior to manufacture.
2. Please Refer to Finishing Schedule for full specifications: KRR01.2.4.1-FIN

KEY PLAN


INITIAL ISSUE	AC	AM	SM	2025.02.11
REV.#	GENERAL NOTES	DRAWN BY	CHECKED BY	APPROVED BY
PROJECT TITLE	REFERENCE			
KRR01-RIYADH				KRR01 G

DRAWING TITLE	
GROUND FLOOR STAFF BEDROOM-3 & 4 FLOORING LAYOUT	
DRAWING NUMBER	REVISION
ID-107	
SCALE	FORMAT
1:20	A1
ADDITIONAL NOTES	DESIGN DEVELOPMENT

**SIMA MALAK + ALSSAMOURE
DESIGN ASSOCIATES**

P.O. Box 15707 - Riyadh 11454 KSA
Tel. 01 441 4963 - Fax. 01 441 3867
simals@simals.com

©SIMA MALAK + ALSSAMOURE DESIGN ASSOCIATES (شركة) 2003
This document including all drawing and text is the property and
copyright of SIMA MALAK + ALSSAMOURE DESIGN ASSOCIATES for
use solely with respect to this Project and shall not be copied or
reproduced by any means except by agreement in writing from
SIMA MALAK + ALSSAMOURE DESIGN ASSOCIATES.

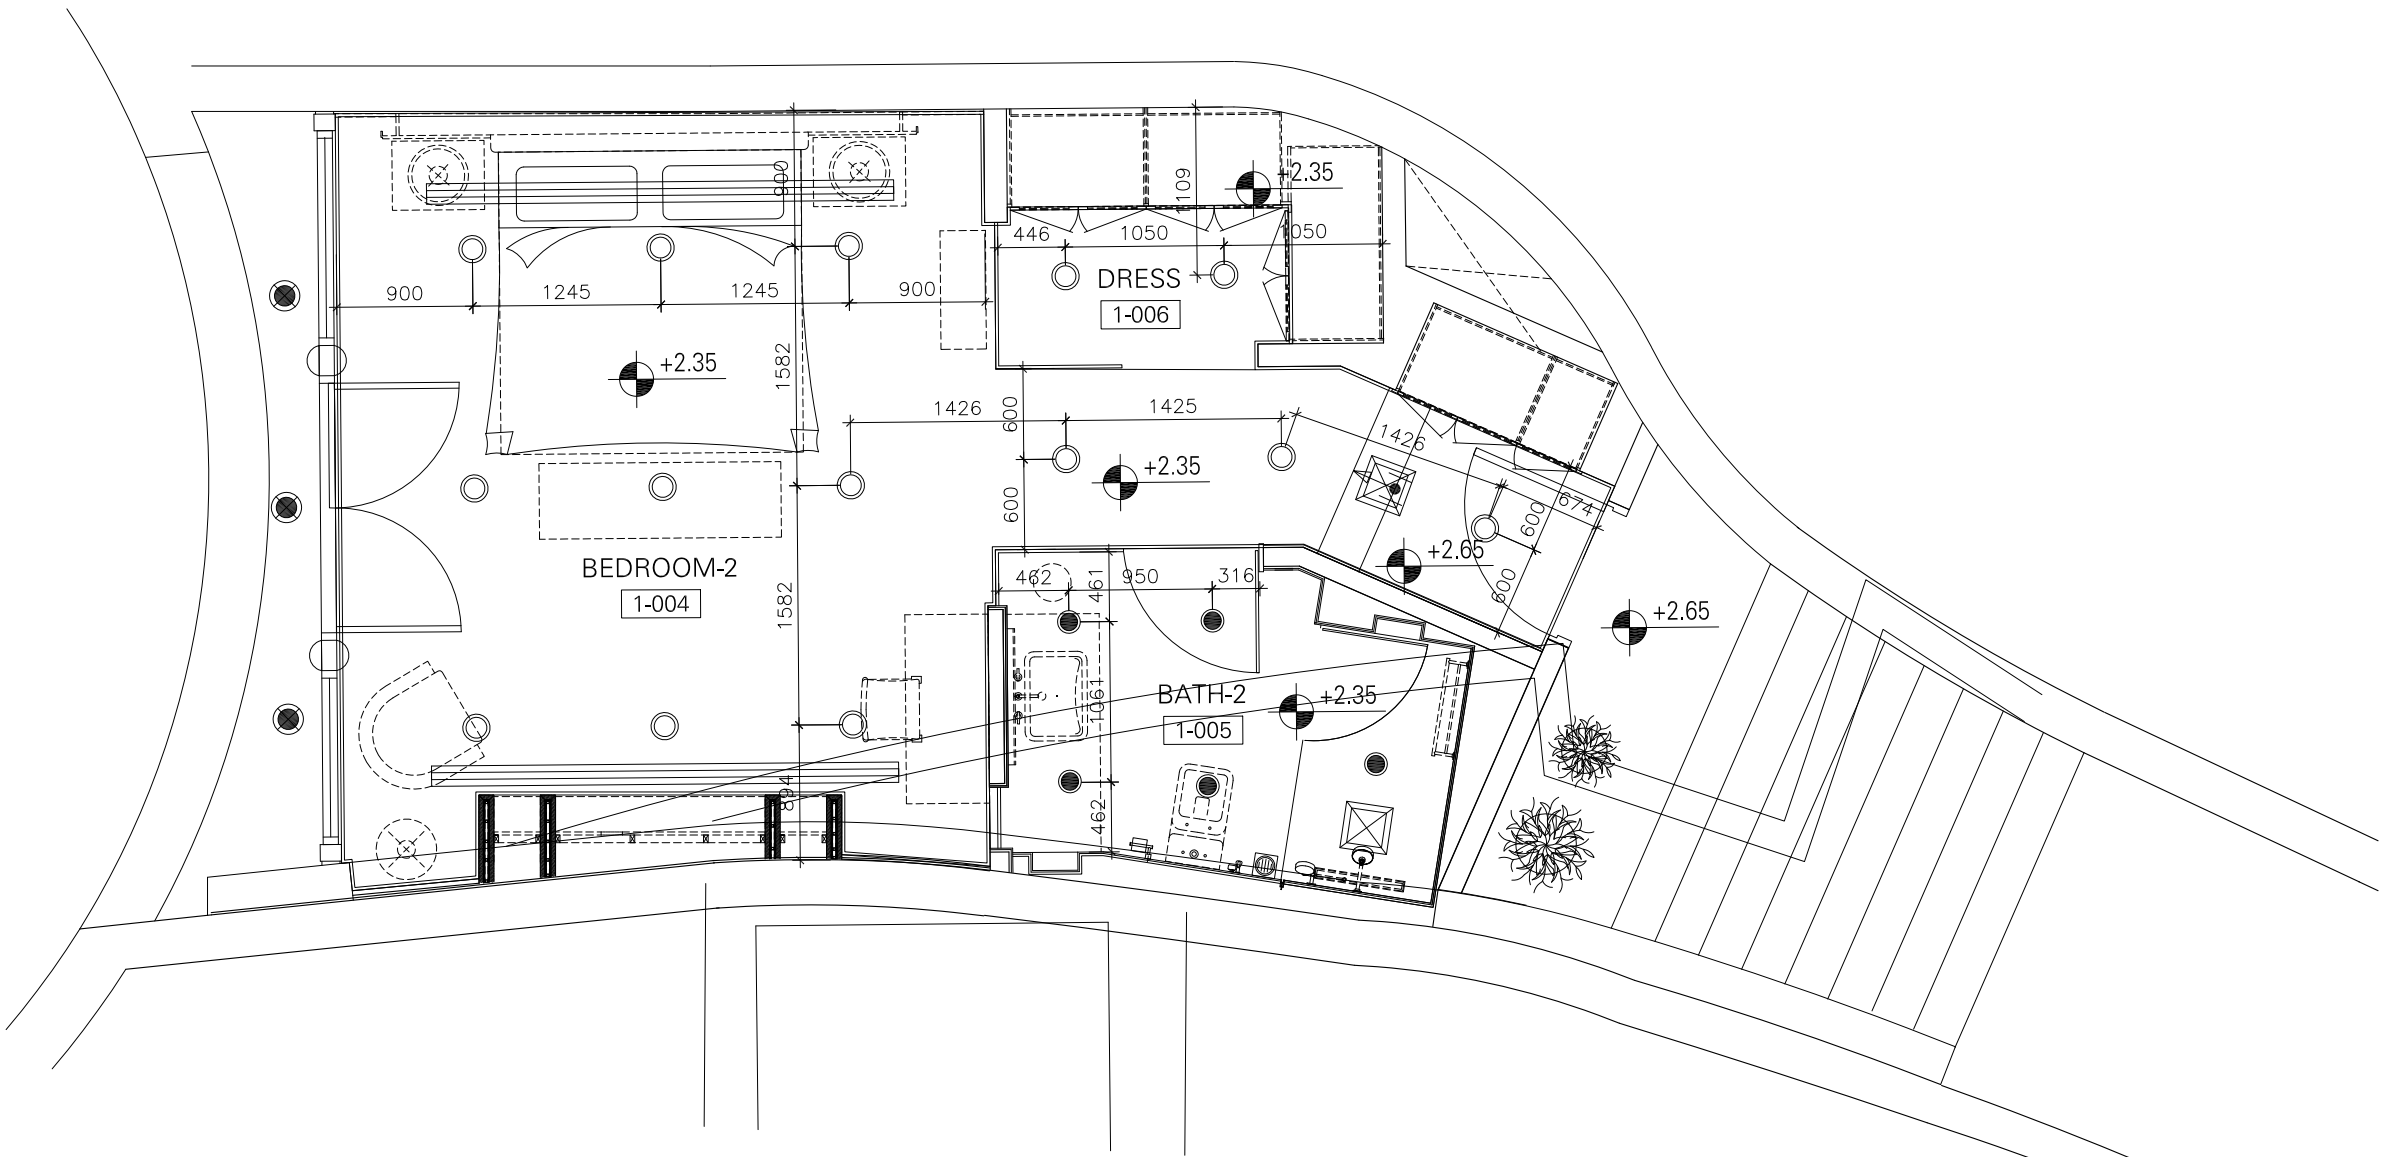

FIRST FLOOR - GUEST BEDROOM - 2 REFLECTED CEILING LAYOUT
SCALE 1:25

GENERAL NOTES

1. This drawing shall be read in conjunction with all other relevant architectural, structural & electrical drawings including those of other consultants.
2. It is the responsibility of contractors & manufacturers to check all relevant site dimensions prior to the start of construction or manufacture.
3. All materials and components must be installed on site in accordance with manufacturer's instructions, shop drawings and standard details.
4. All dimensions are in millimeters unless noted otherwise.
5. Full working drawings, specifications and samples are to be provided by Contractor/Supplier for approval prior to manufacture.

FINISHES

1. Please Refer to Finishing Schedule for full specifications: KRR01.2.4.1-FIN

LEGEND :

- Recessed Downlight (Small)
- Recessed Downlight (Big)
- Recessed Downlight in Bathrooms (IP45 Halogen 60w.)
- ⦿ Exterior Surface mounted Downlight (IP65)
- ☼ Mirror Wall Light
- ⊠ Exhaust Grill

KEY PLAN

INITIAL ISSUE	AC	AM	SM	2025.02.11
---------------	----	----	----	------------

REV.#	GENERAL NOTES	DRAWN BY	CHECKED BY	APPROVED BY	DATE
-------	---------------	----------	------------	-------------	------

PROJECT TITLE	REFERENCE
---------------	-----------

KRR01-RIYADH	KRR01 G
--------------	------------

DRAWING TITLE

FIRST FLOOR (RIGHT SIDE)
GUEST BEDROOM-2
REFLECTED CEILING LAYOUT

DRAWING NUMBER	REVISION
----------------	----------


ID-202	
--------	--

SCALE	FORMAT	ADDITIONAL NOTES	DESIGN DEVELOPMENT
1:25	A1		



**SIMA MALAK + ALSSAMOURE
DESIGN ASSOCIATES**
P.O. Box 15707 - Riyadh 11454 KSA
Tel. 01 441 4963 - Fax. 01 441 3867
simals@simals.com

©SIMA MALAK + ALSSAMOURE DESIGN ASSOCIATES (شركة) 2003
This document including all drawing and text is the property and
copyright of SIMA MALAK + ALSSAMOURE DESIGN ASSOCIATES for
use solely with respect to this Project and shall not be copied or
reproduced by any means except by agreement in writing from
SIMA MALAK + ALSSAMOURE DESIGN ASSOCIATES.

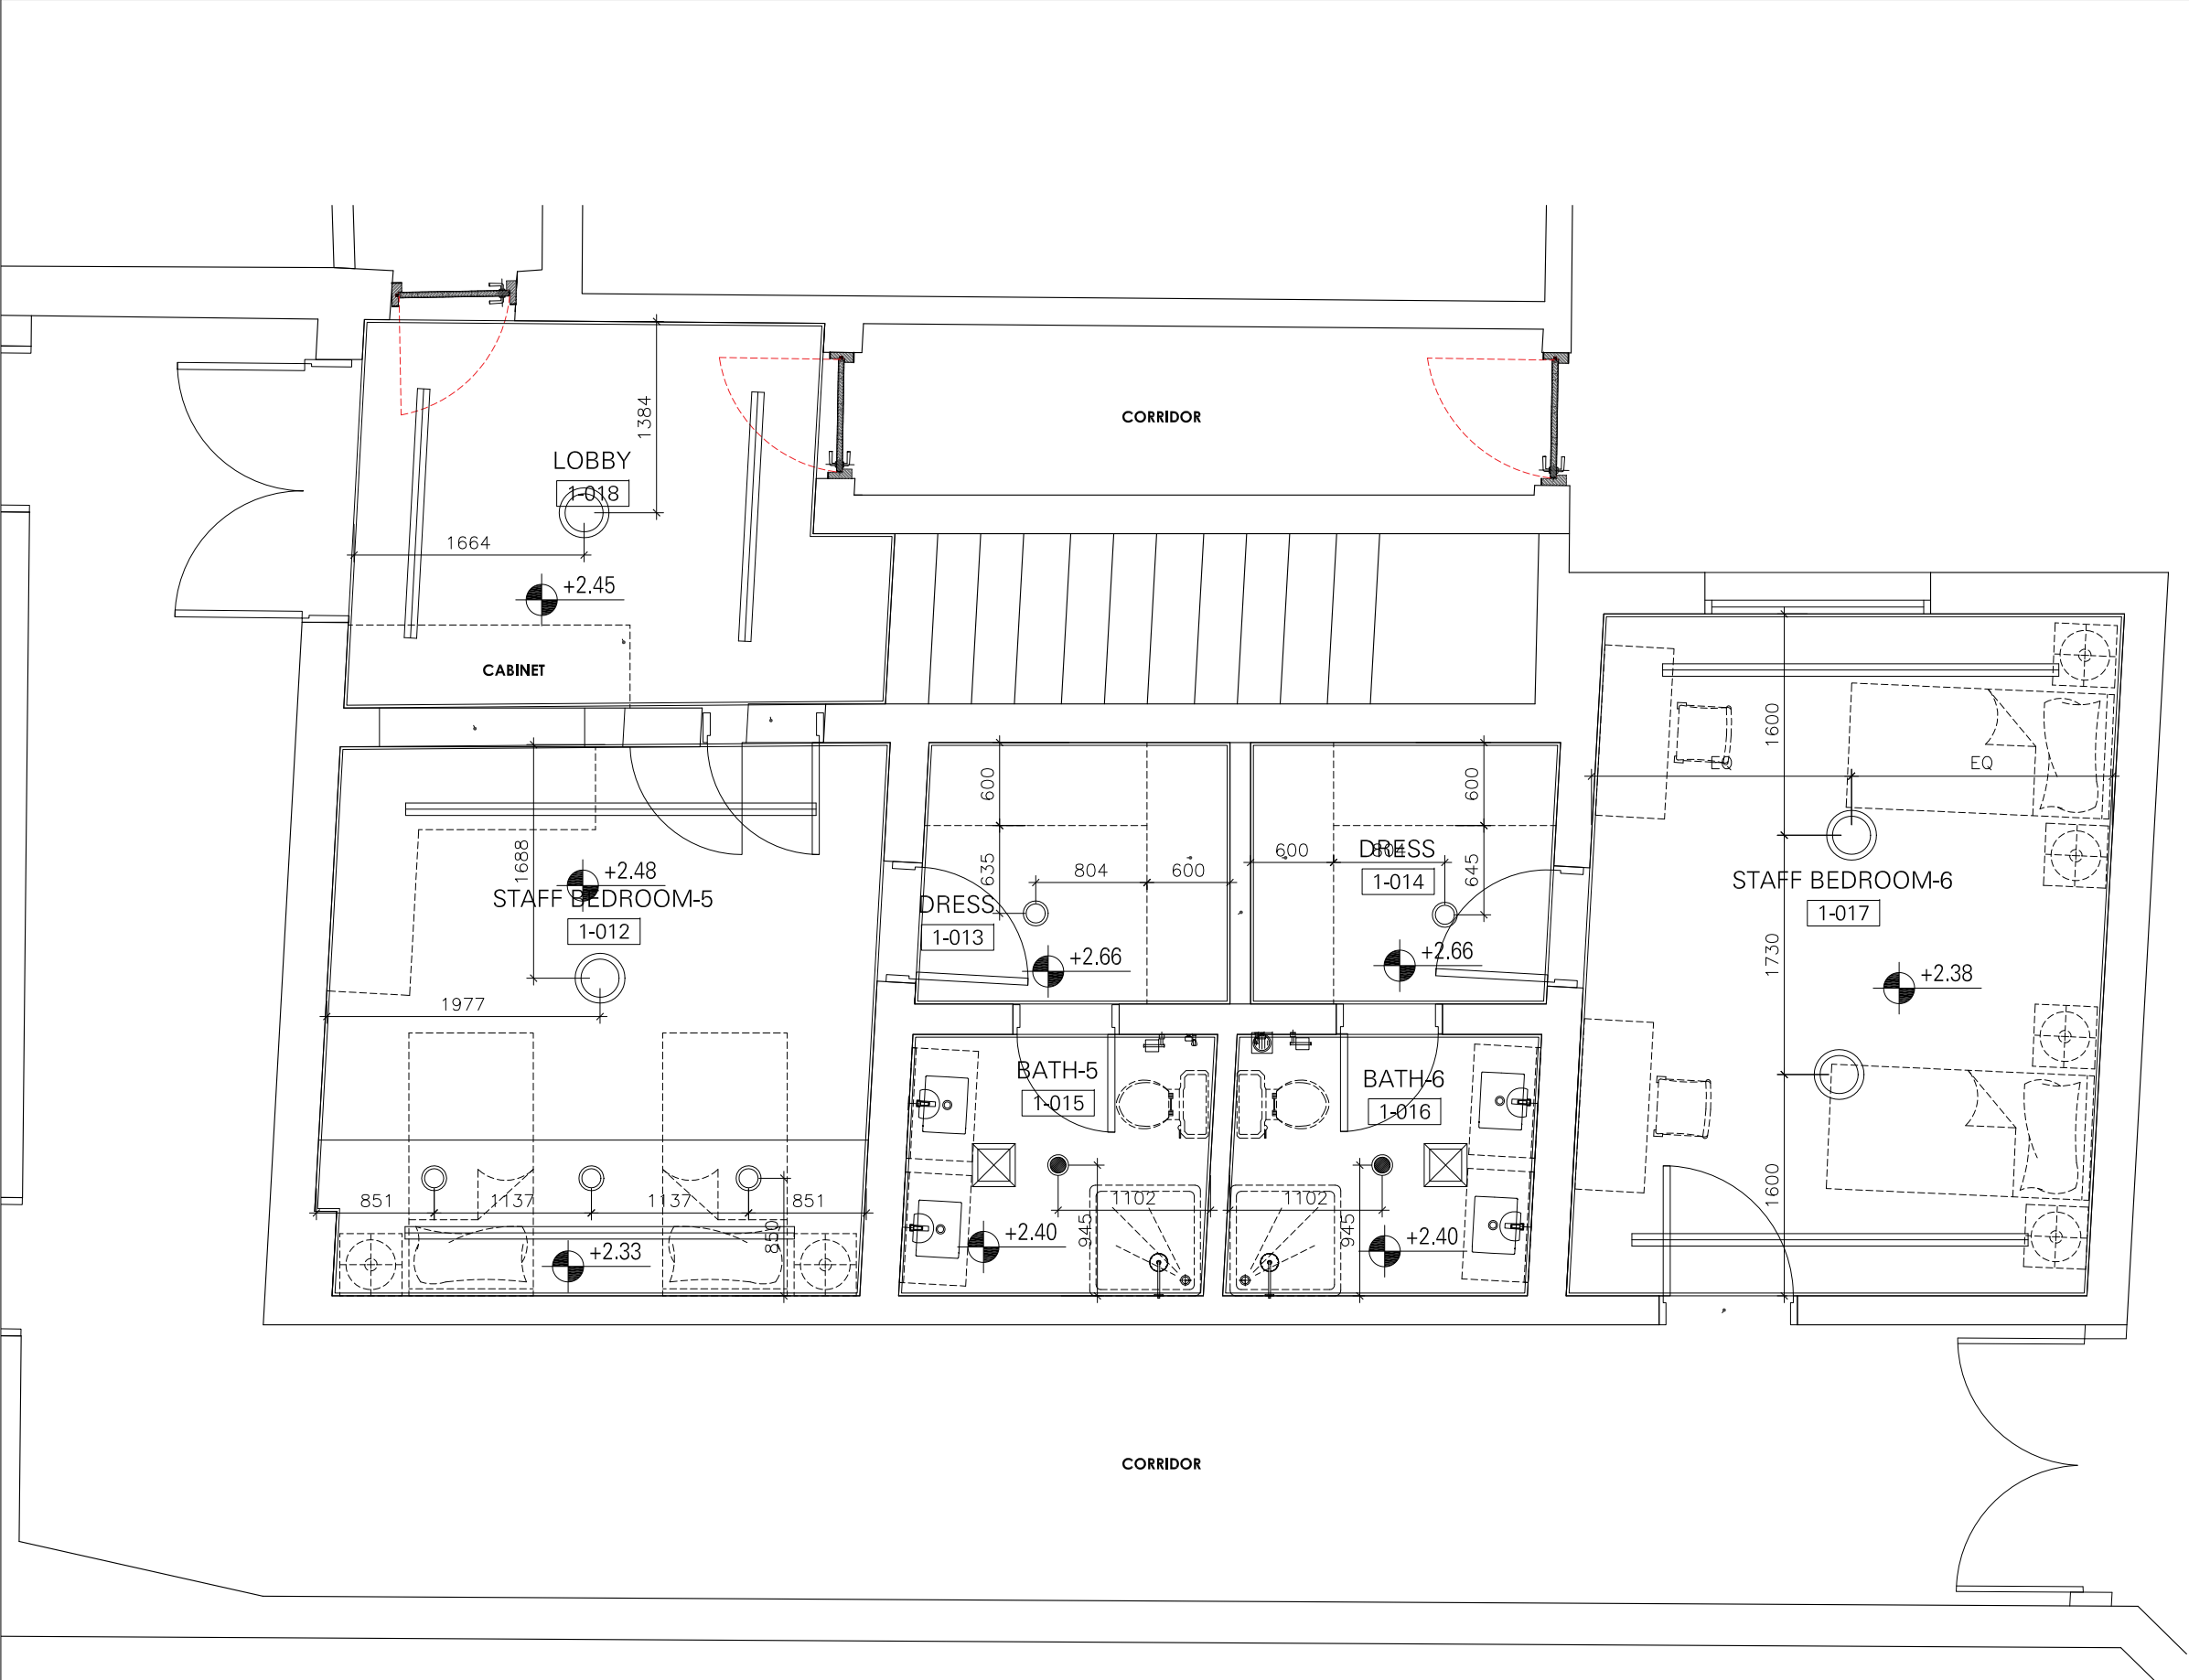

STAFF BEDROOM - 5 & 6 REFLECTED CEILING LAYOUT
SCALE 1:25

GENERAL NOTES

1. This drawing shall be read in conjunction with all other relevant architectural, structural & electrical drawings including those of other consultants.
2. It is the responsibility of contractors & manufacturers to check all relevant site dimensions prior to the start of construction or manufacture.
3. All materials and components must be installed on site in accordance with manufacturer's instructions, shop drawings and standard details.
4. All dimensions are in millimeters unless noted otherwise.
5. Full working drawings, specifications and samples are to be provided by Contractor/Supplier for approval prior to manufacture.

FINISHES

1. Please Refer to Finishing Schedule for full specifications: KRR01.2.4.1-FIN

LEGEND :

- Recessed Downlight (Small)
- Recessed Downlight (Big)
- Recessed Downlight in Bathrooms (IP45 Halogen 60w.)
- ^S Surface Mounted Downlight in Bathroom (IP45 Halogen 60w.)
- ^S Surface Mounted Downlight (Small)
- Exterior Surface mounted Downlight (IP65)
- ☐ Mirror Wall Light
- ☒ Exhaust Grill

KEY PLAN

INITIAL ISSUE	AC	AM	SM	2025.02.11
REV.#	GENERAL NOTES	DRAWN BY	CHECKED BY	APPROVED BY
PROJECT TITLE				REFERENCE
KRR01-RIYADH				KRR01 G


DRAWING TITLE	
GROUND FLOOR STAFF BEDROOM-5 & 6 REFLECTED CEILING LAYOUT	
DRAWING NUMBER	REVISION
ID-204	

SCALE	FORMAT	ADDITIONAL	DESIGN DEVELOPMENT
1:25	A1	NOTES	

SIMA MALAK + ALSSAMOURE
DESIGN ASSOCIATES

P.O. Box 15707 - Riyadh 11454 KSA
Tel. 01 441 4963 - Fax. 01 441 3867
simals@simals.com

©SIMA MALAK + ALSSAMOURE DESIGN ASSOCIATES (شركة) 2003
This document including all drawing and text is the property and copyright of SIMA MALAK + ALSSAMOURE DESIGN ASSOCIATES for use solely with respect to this Project and shall not be copied or reproduced by any means except by agreement in writing from SIMA MALAK + ALSSAMOURE DESIGN ASSOCIATES.

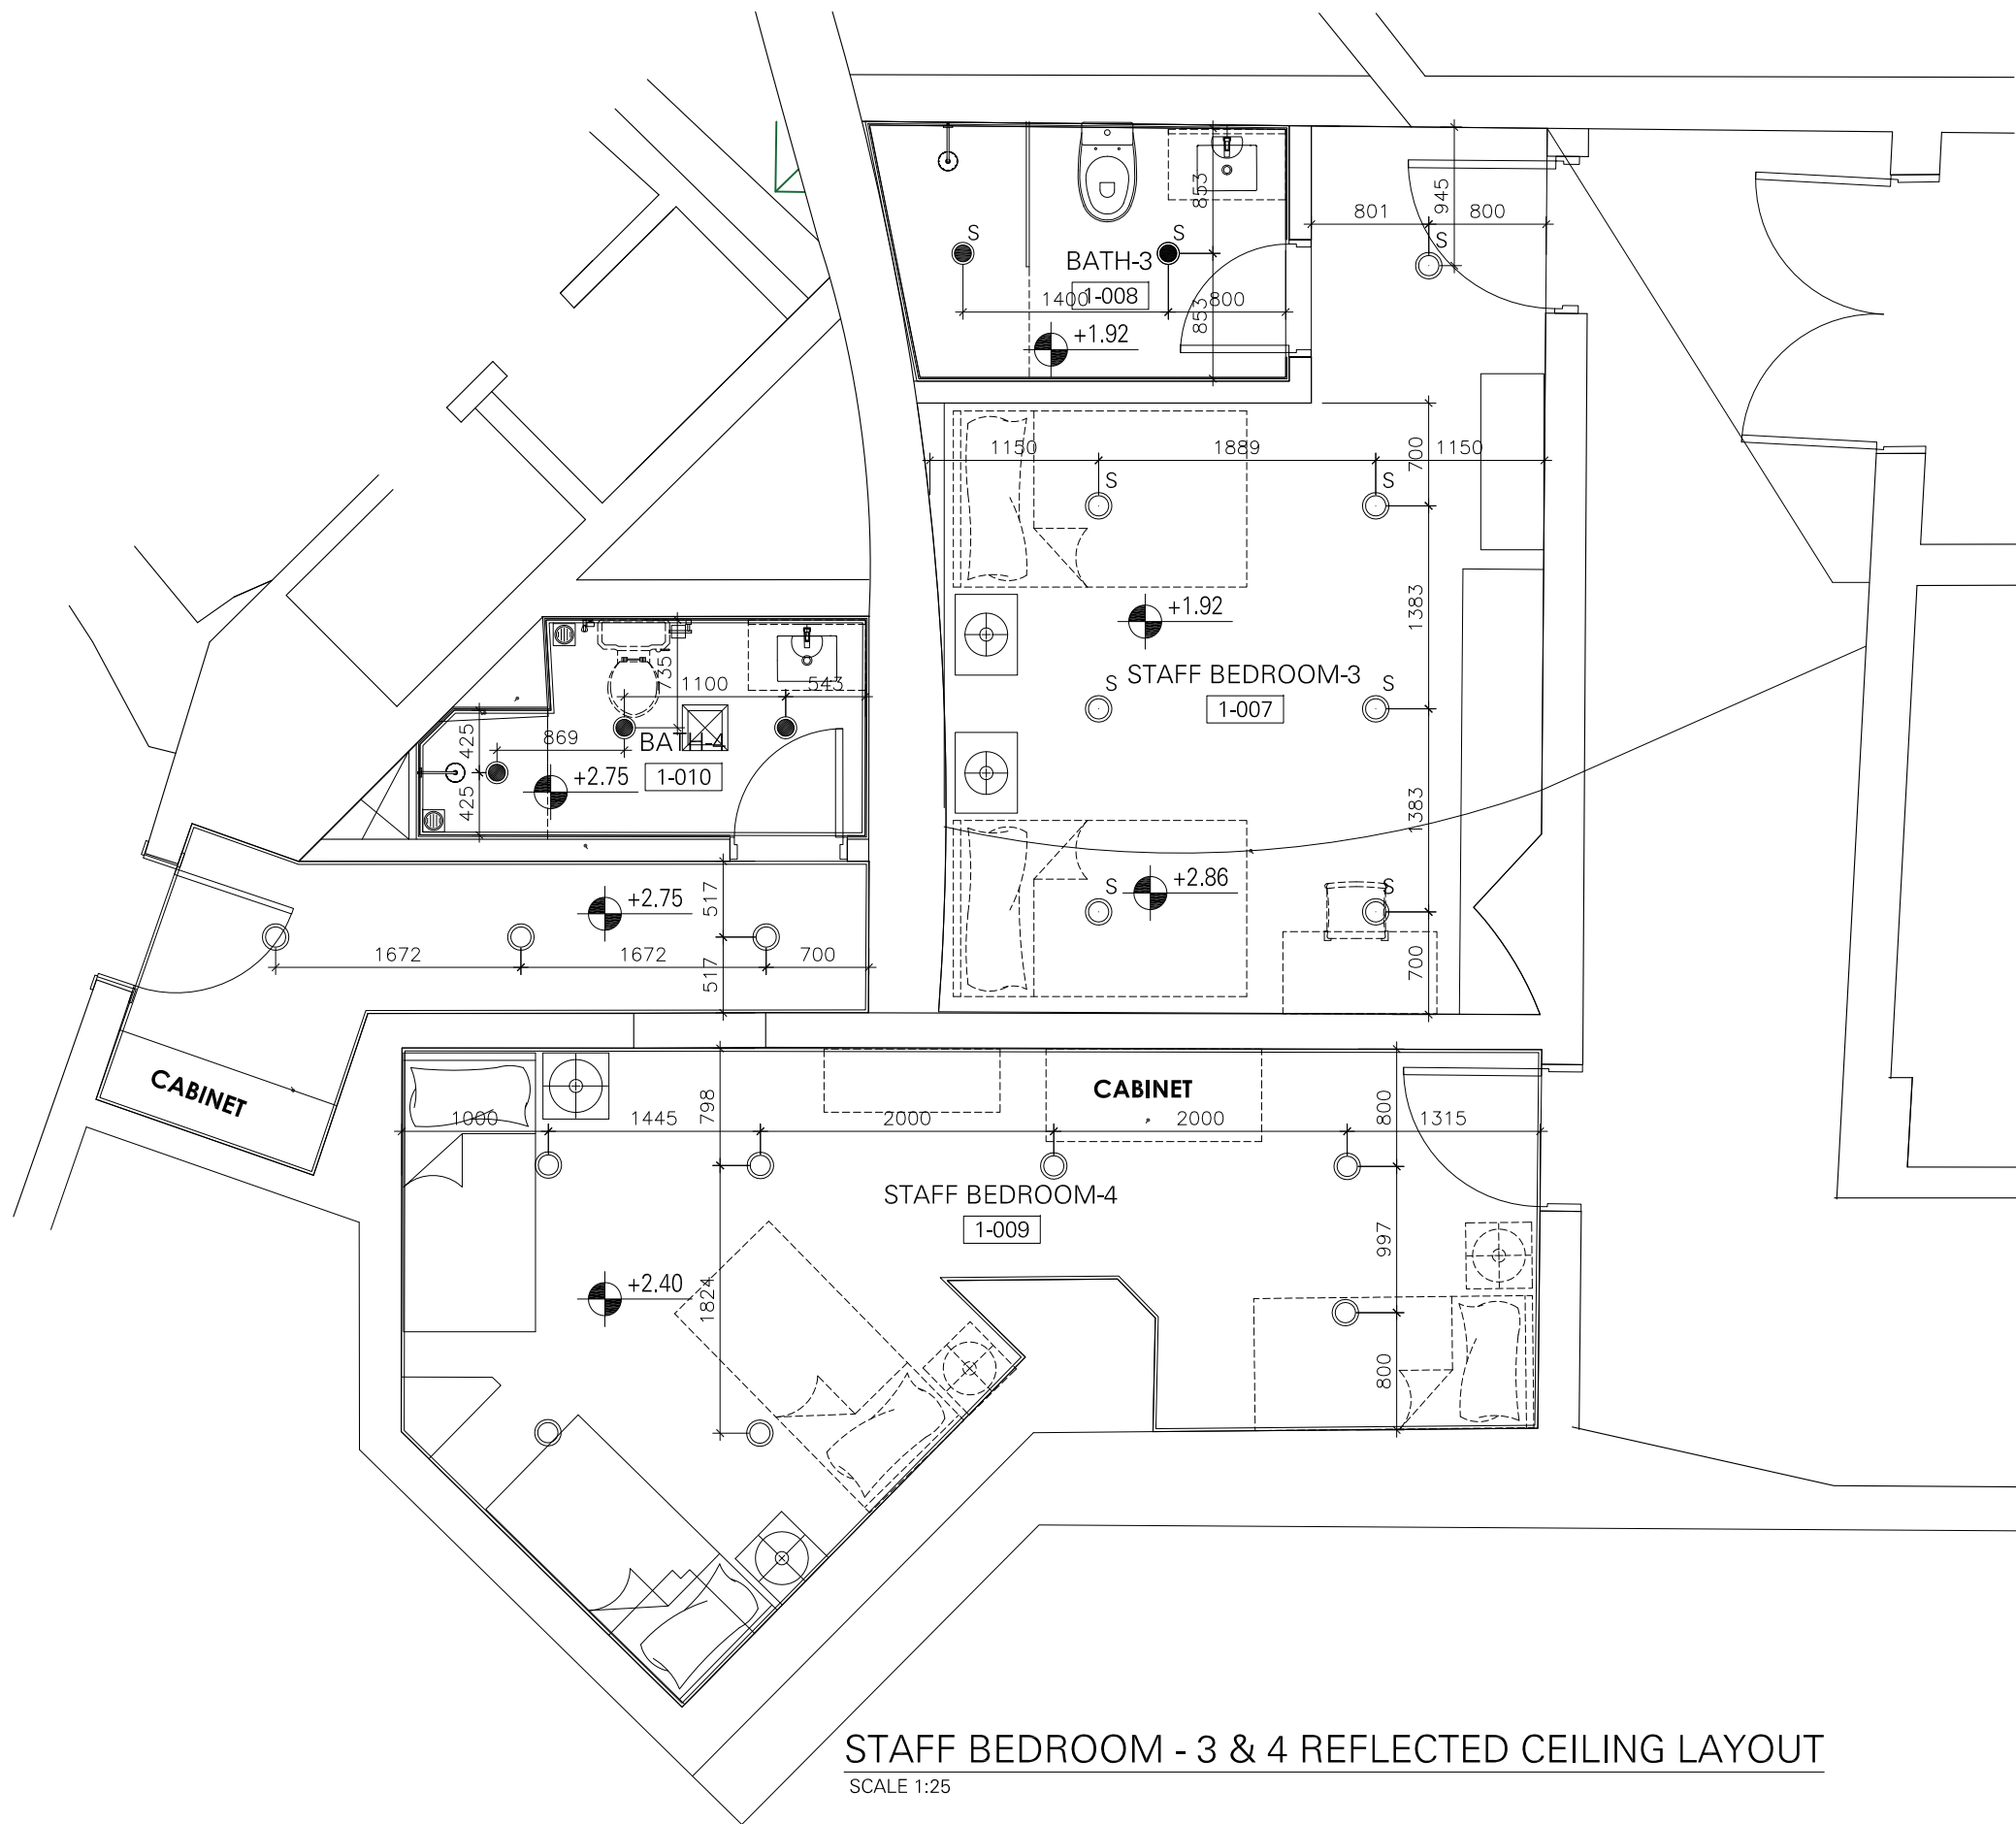

GENERAL NOTES

1. This drawing shall be read in conjunction with all other relevant architectural, structural & electrical drawings including those of other consultants.
2. It is the responsibility of contractors & manufacturers to check all relevant site dimensions prior to the start of construction or manufacture.
3. All materials and components must be installed on site in accordance with manufacturer's instructions, shop drawings and standard details.
4. All dimensions are in millimeters unless noted otherwise.
5. Full working drawings, specifications and samples are to be provided by Contractor/Supplier for approval prior to manufacture.

FINISHES

1. Please Refer to Finishing Schedule for full specifications; KRR01.2.4.1-FIN

LEGEND :

- Recessed Downlight (Small)
- Recessed Downlight (Big)
- Recessed Downlight in Bathrooms (IP45 Halogen 60w.)
- Surface Mounted Downlight in Bathroom (IP45 Halogen 60w.)
- Surface Mounted Downlight (Small)
- Exterior Surface mounted Downlight (IP65)
- ☐ Mirror Wall Light
- ☐ Exhaust Grill




KEY PLAN

INITIAL ISSUE	AC	AM	SM	2025.02.11
REV.#	GENERAL NOTES	DRAWN BY	CHECKED BY	APPROVED BY
PROJECT TITLE	REFERENCE			
KRR01-RIYADH				KRR01 G

DRAWING TITLE			
GROUND FLOOR STAFF BEDROOM-3 & 4 REFLECTED CEILING LAYOUT			
DRAWING NUMBER			
ID-203			
REVISION			
SCALE	FORMAT	ADDITIONAL NOTES	DESIGN DEVELOPMENT
1:25	A1		


SIMA MALAK + ALSSAMOURE
DESIGN ASSOCIATES
P.O. Box 15707 - Riyadh 11454 KSA
Tel. 01 441 4963 - Fax. 01 441 3867
simals@simals.com

©SIMA MALAK + ALSSAMOURE DESIGN ASSOCIATES (شركة) 2003
This document including all drawing and text is the property and copyright of SIMA MALAK + ALSSAMOURE DESIGN ASSOCIATES for use solely with respect to this Project and shall not be copied or reproduced by any means except by agreement in writing from SIMA MALAK + ALSSAMOURE DESIGN ASSOCIATES.

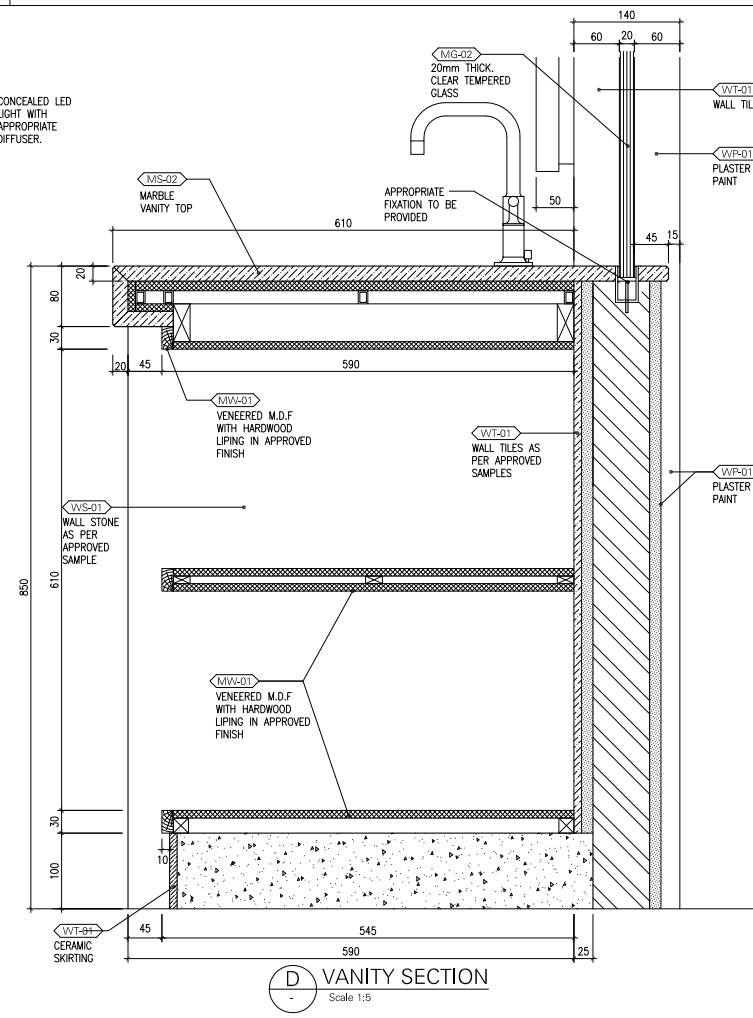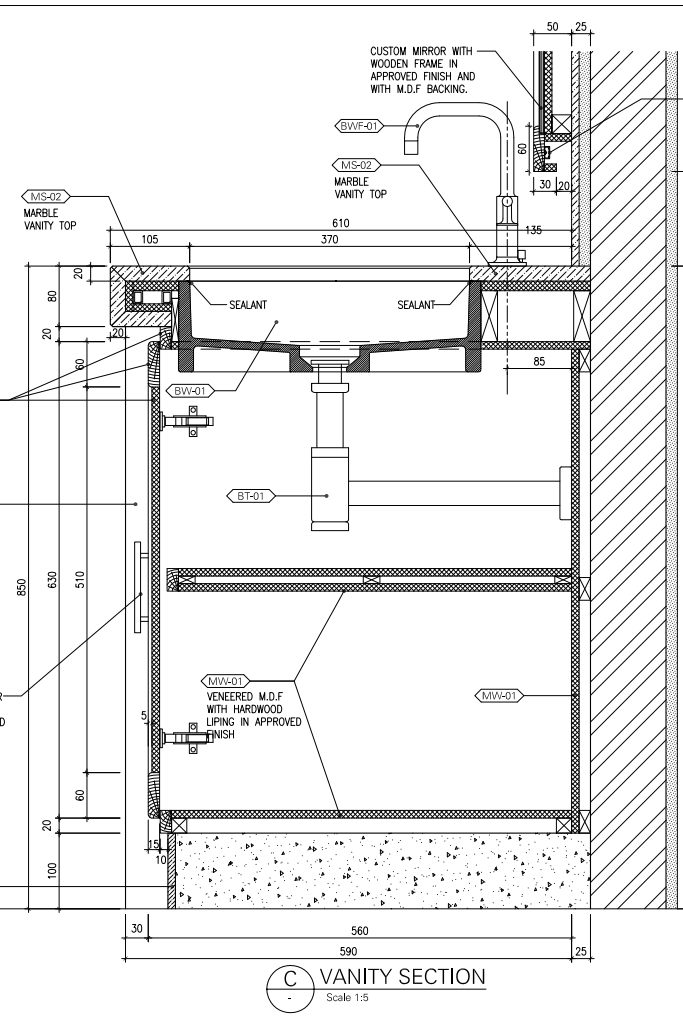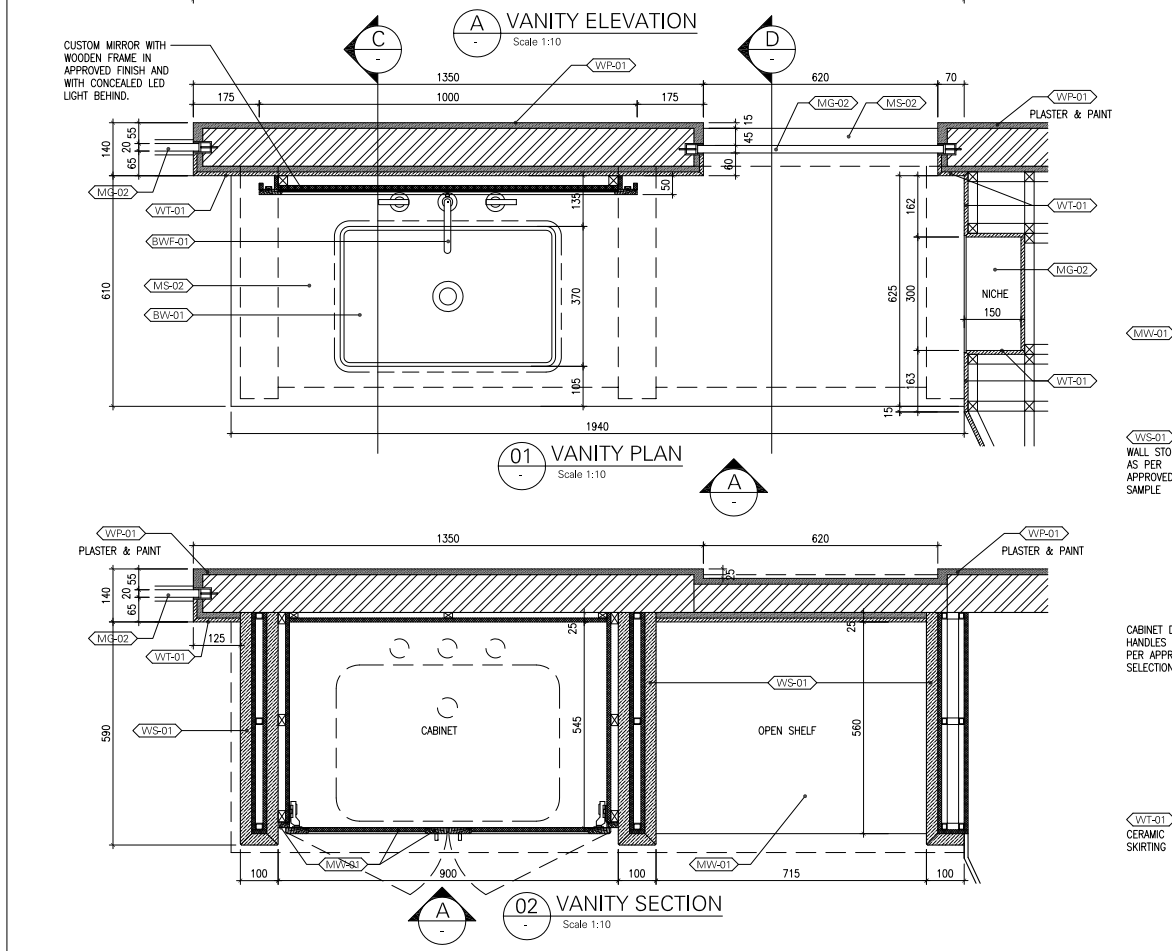


- ### ACCESSORIES
1. All positions of sanitary accessories including towel rails, mirrors & artwork etc. to be confirmed on site and fixed after final approval.
 2. Finishes will continue behind loose furniture fixtures. ie.mirrors and art works etc.


KEY PLAN						
X	INITIAL ISSUE	MP	AM	SM	2026.02.11	
REV.#	GENERAL NOTES	DRAWN BY	CHECKED BY	APPROVED BY	DATE	
PROJECT TITLE					REFERENCE	
KRR01-RIYADH					KRR01	
					G	
DRAWING TITLE						
MAIN VILLA - FIRST FLOOR BATH -1 (1-002) VANITY & OTHER DETAILS						
DRAWING NUMBER					REVISION	
ID-402						
SCALE		FORMAT		DESIGN DEVELOPMENT		
1:20		A1		ADDITIONAL NOTES		
SIMA MALAK + ALLSSAMOURE DESIGN ASSOCIATES						
P.O. Box 15707 - Riyadh 11454 KSA						
Tel. 01 441 4963 - Fax. 01 441 3867						
simas@simals.com						
©SIMA MALAK + ALLSSAMOURE DESIGN ASSOCIATES (شركة) 2003 This document including all drawing and text is the property and copyright of SIMA MALAK + ALLSSAMOURE DESIGN ASSOCIATES for use solely with respect to this Project and shall not be copied or reproduced by any means except by agreement in writing from SIMA MALAK + ALLSSAMOURE DESIGN ASSOCIATES.						

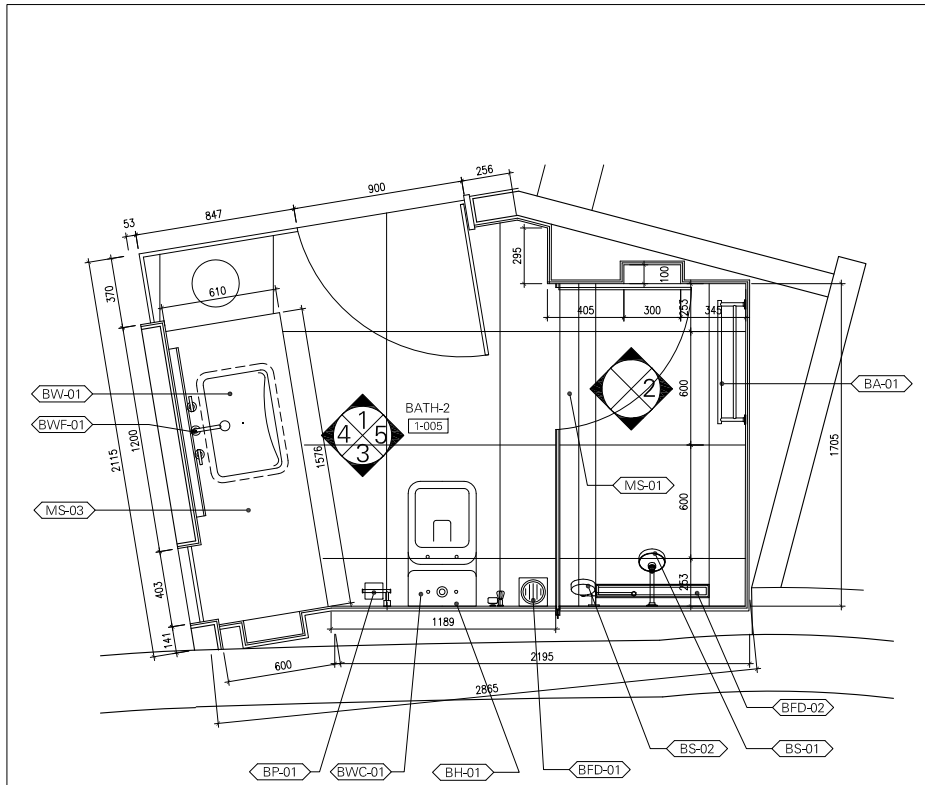


BATHROOM-2 (1-005) PLAN
SCALE 1:20

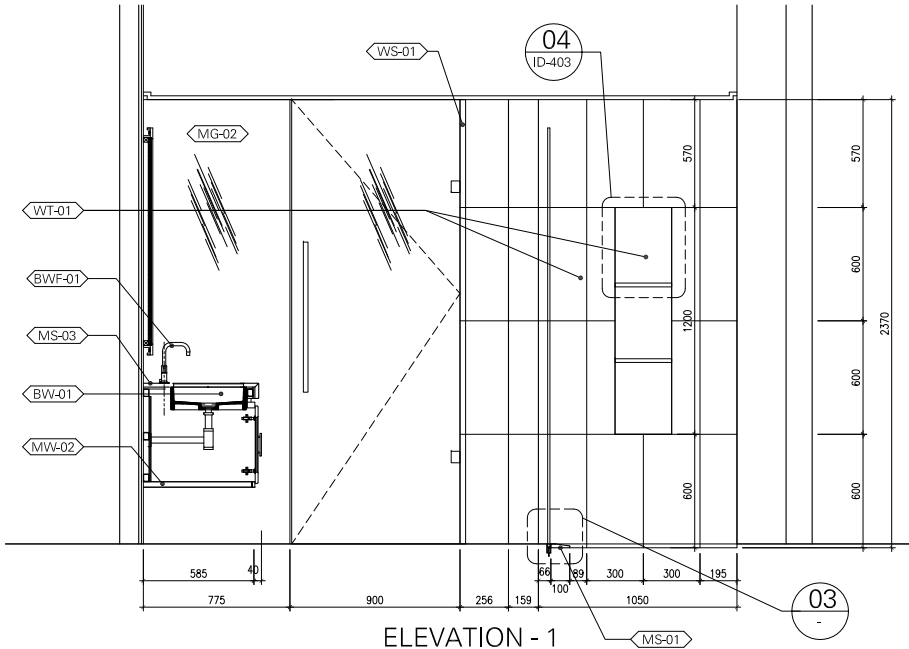


ELEVATION - 1
SCALE 1:20

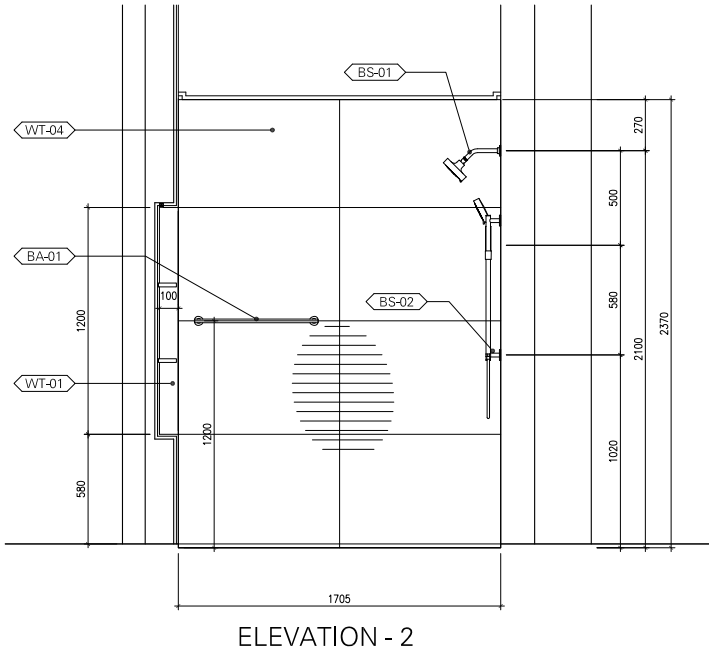


ELEVATION - 2
SCALE 1:20

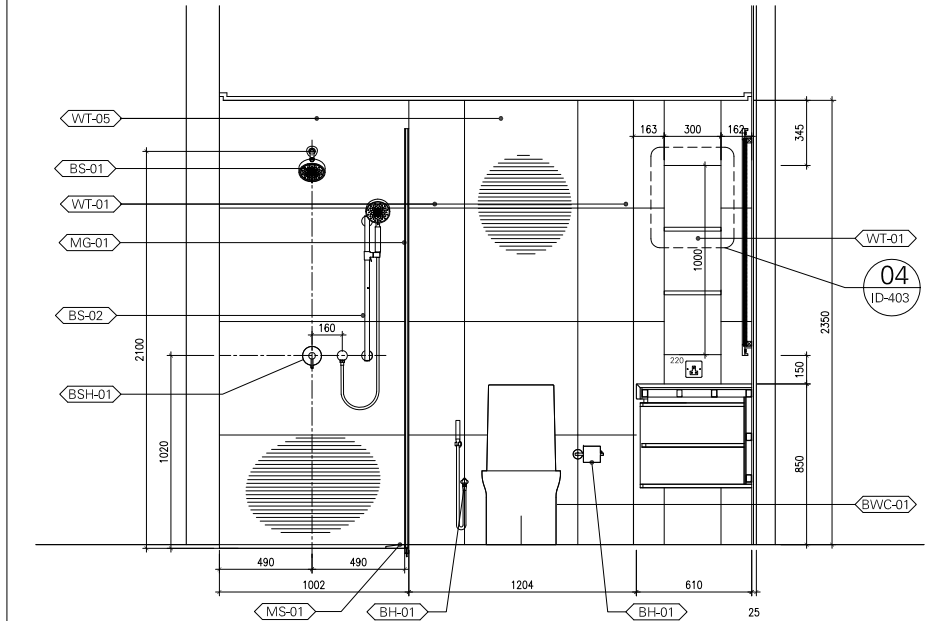

ELEVATION - 3
SCALE 1:20

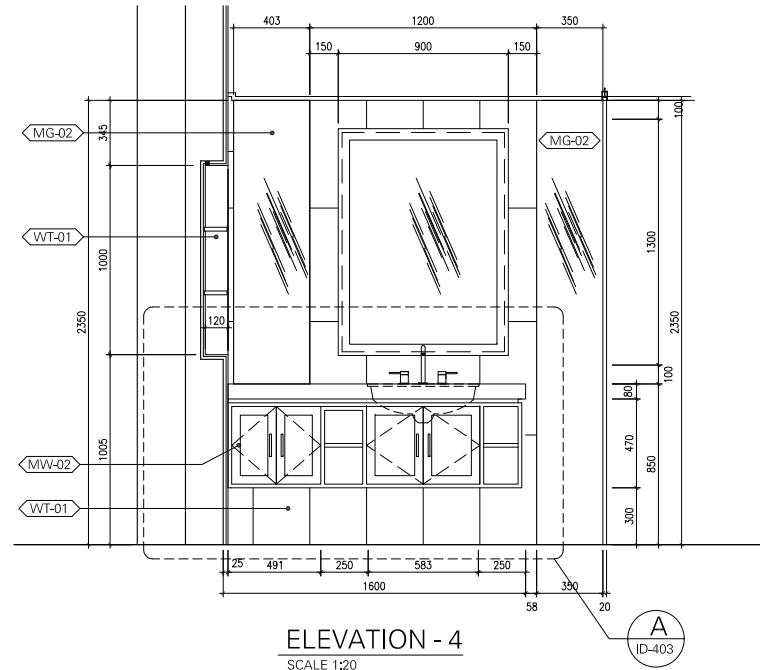

ELEVATION - 4
SCALE 1:20

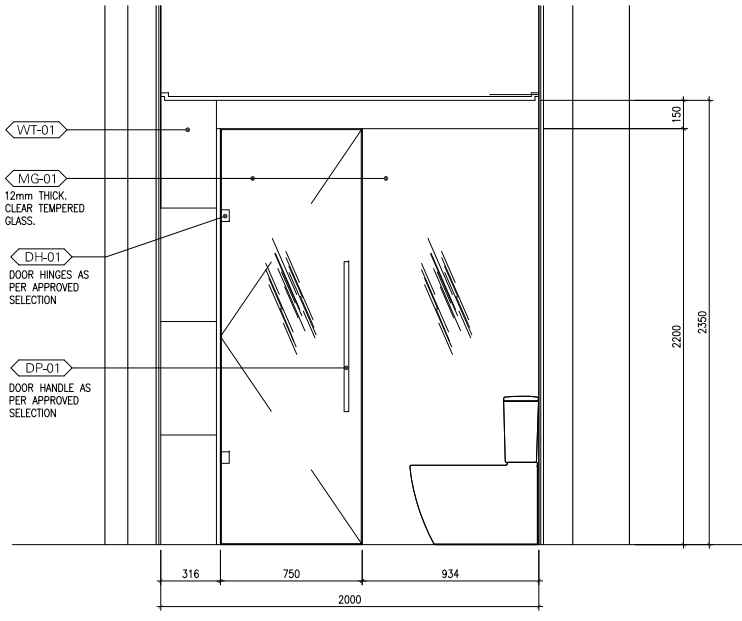

ELEVATION - 5
SCALE 1:20

GENERAL NOTES

1. This drawing shall be read in conjunction with all other relevant architectural, structural & electrical drawings including those of other consultants.
2. It is the responsibility of contractors & manufacturers to check all relevant site dimensions prior to the start of construction or manufacture.
3. All materials and components must be installed on site in accordance with manufacturer's instructions, shop drawings and standard details.
4. All dimensions are in millimeters unless noted otherwise.
5. Full working drawings, specifications and samples are to be provided by Contractor/Supplier for approval prior to manufacture.
6. Appropriate slope for the flooring to the drain to be provided by Contractor.

NOTES FOR MANUFACTURER:

- * Construction methods shown on drawings are suggested methods only.
- * All Fixing & Screws to be concealed. If not possible manufacturer to consult with designers before manufacture.
- * All site dimension to be confirmed by contractor prior to the manufacture of items.
- * All materials used in bathrooms to be water resistant, moisture, rust and mould treated such as marine ply, stainless steel, aluminum or equivalent.
- * All joints to be water sealed and water proof membrane to be provided as required.
- * All glass and mirrors to have polished smooth edges all round.
- * All Bathrooms, washrooms floors and steps to be in Hard non slip finish.


FINISHES

1. Full working drawings, specifications and samples are to be provided by Contractor/Supplier for approval prior to manufacture.
2. Please Refer to Finishing Schedule and Sanitary Schedule for full specifications:
KRR01-2-4-1-FIN
KRR01-2-4-1-WC

ACCESSORIES

1. All positions of sanitary accessories including towel rails, mirrors & artwork etc. to be confirmed on site and fixed after final approval.
2. Finishes will continue behind loose furniture fixtures. ie. mirrors and art works etc.











KEY PLAN

 


DRAWING TITLE			
MAIN VILLA - FIRST FLOOR BATH -2 (1-005) PLAN AND ELEVATIONS			
DRAWING NUMBER			REVISION
ID-302			
SCALE	FORMAT	ADDITIONAL NOTES	DESIGN DEVELOPMENT
1:20	A1		

**SIMA MALAK + ALSSAMOURE
DESIGN ASSOCIATES**
P.O. Box 15707 - Riyadh 11454 KSA
Tel. 01 441 4963 - Fax. 01 441 3867
simals@simals.com


©SIMA MALAK + ALSSAMOURE DESIGN ASSOCIATES (شركة) 2003
This document including all drawing and text is the property and copyright of SIMA MALAK + ALSSAMOURE DESIGN ASSOCIATES for use solely with respect to this Project and shall not be copied or reproduced by any means except by agreement in writing from SIMA MALAK + ALSSAMOURE DESIGN ASSOCIATES.

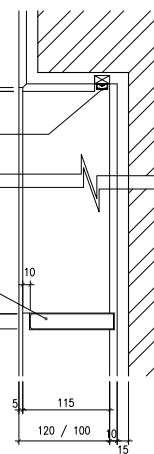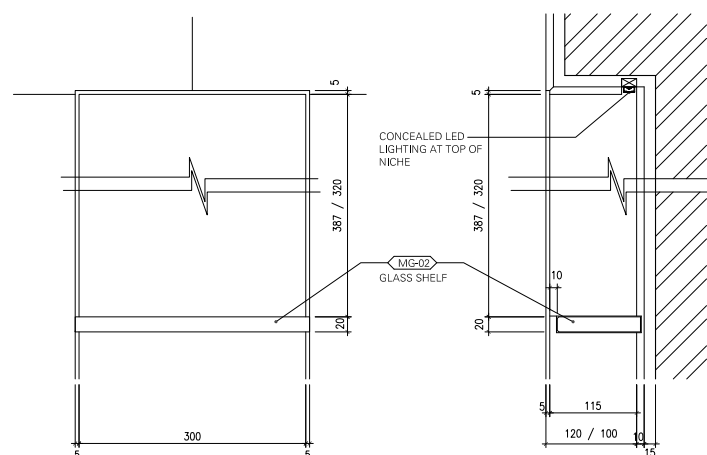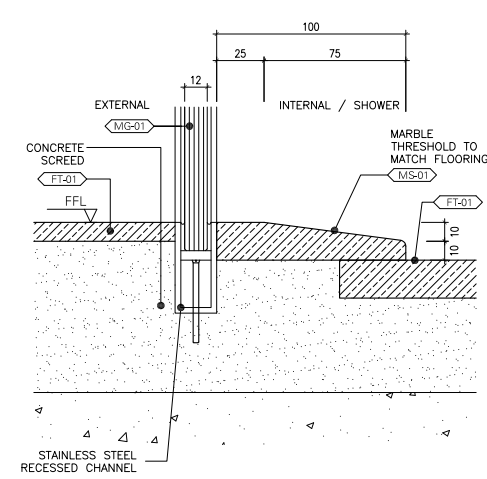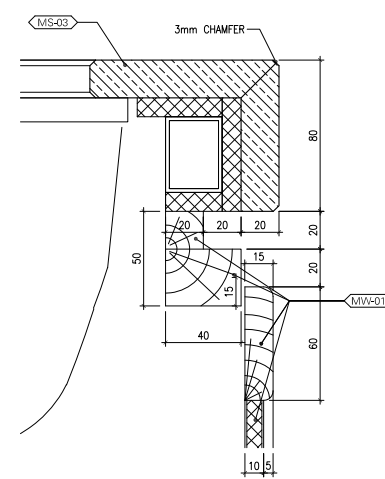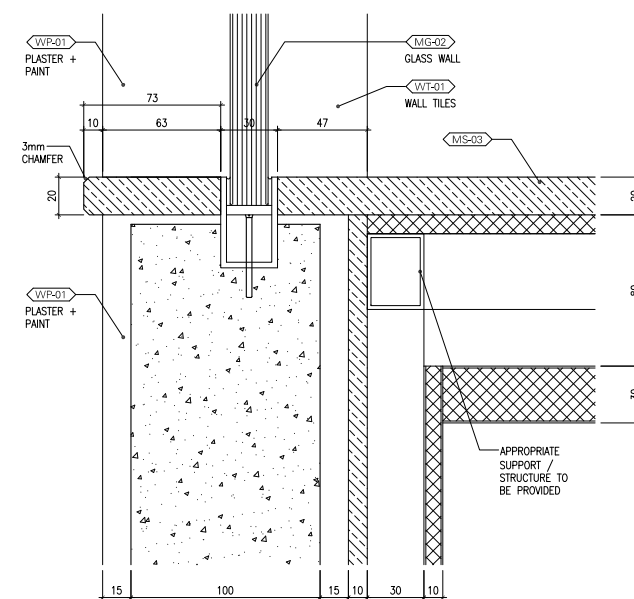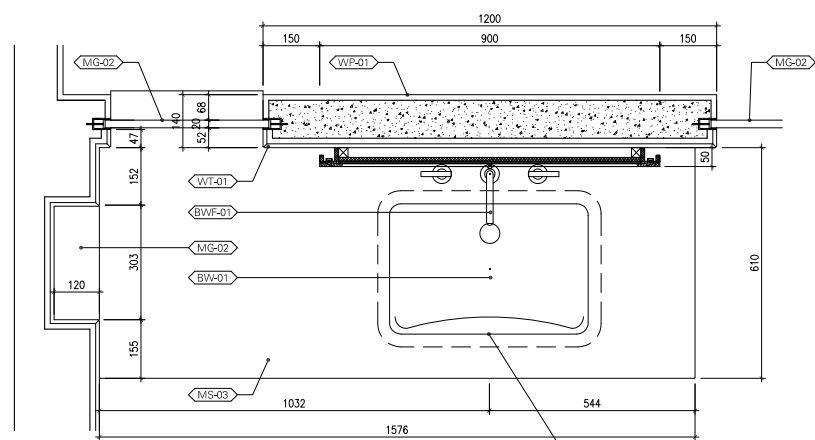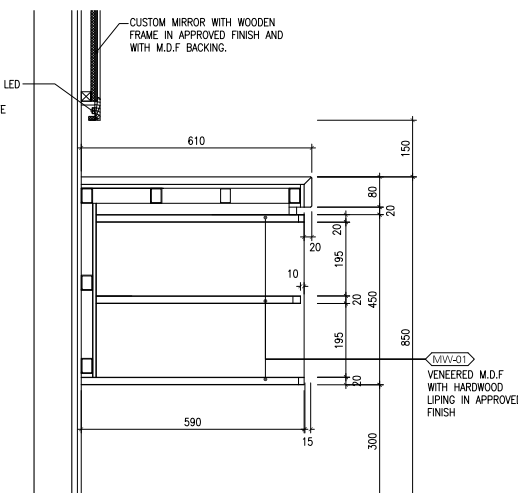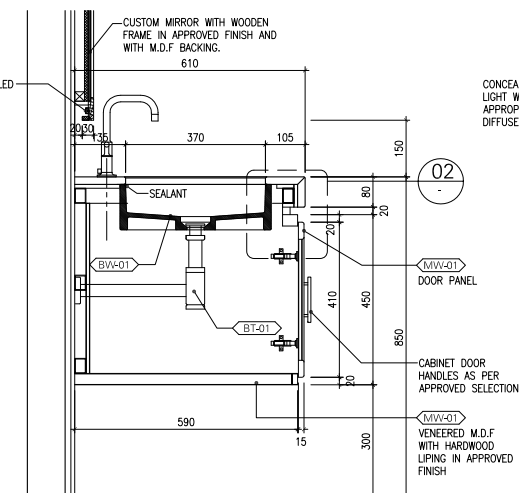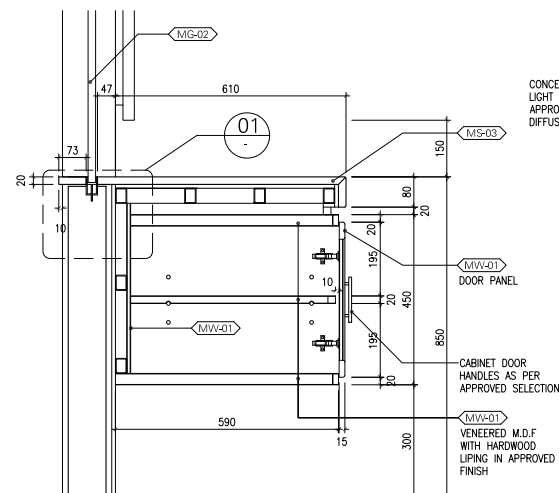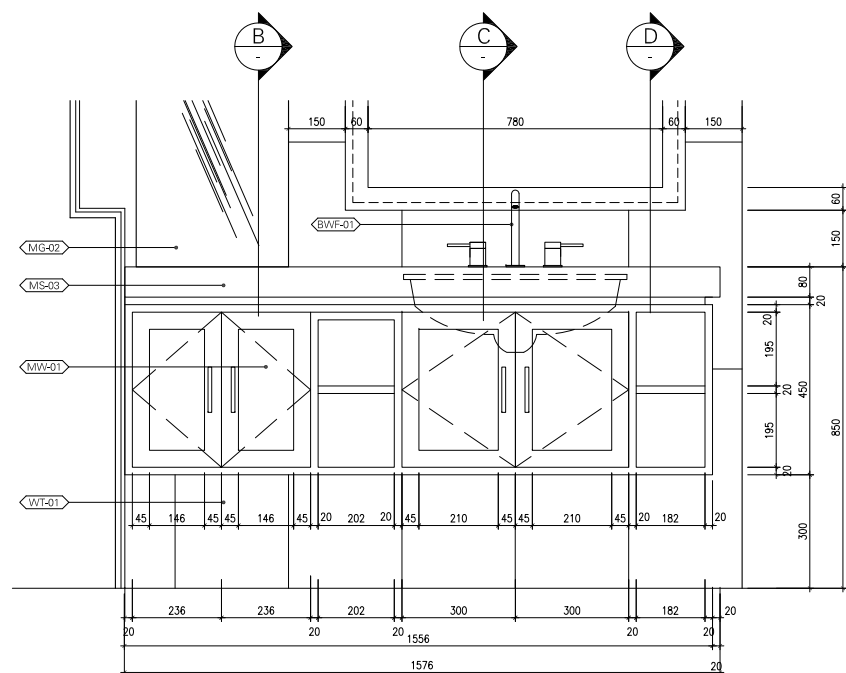


©SIMA MALAK + ALSSAMOURI DESIGN ASSOCIATES (السموري) 2007
This document including all drawing and text is the property and
copyright of SIMA MALAK + ALSSAMOURI DESIGN ASSOCIATES (السموري).
It shall not be copied, reproduced or used in any form or by any means
solely with respect to this Project and shall not be copied, reproduced
or used in any form or by any means except by agreement in writing from
SIMA MALAK + ALSSAMOURI DESIGN ASSOCIATES.

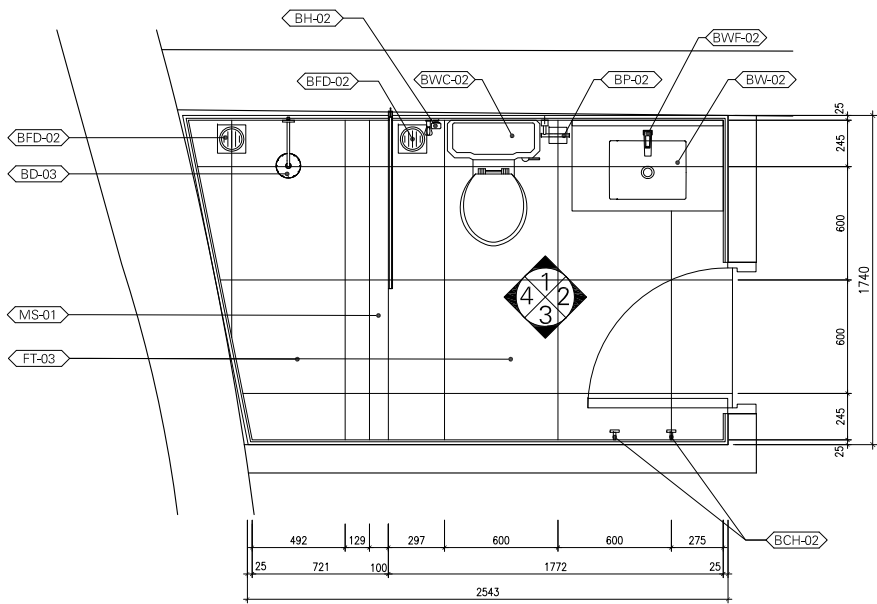


STAFF BATH-3 (1-008) PLAN
SCALE 1:20

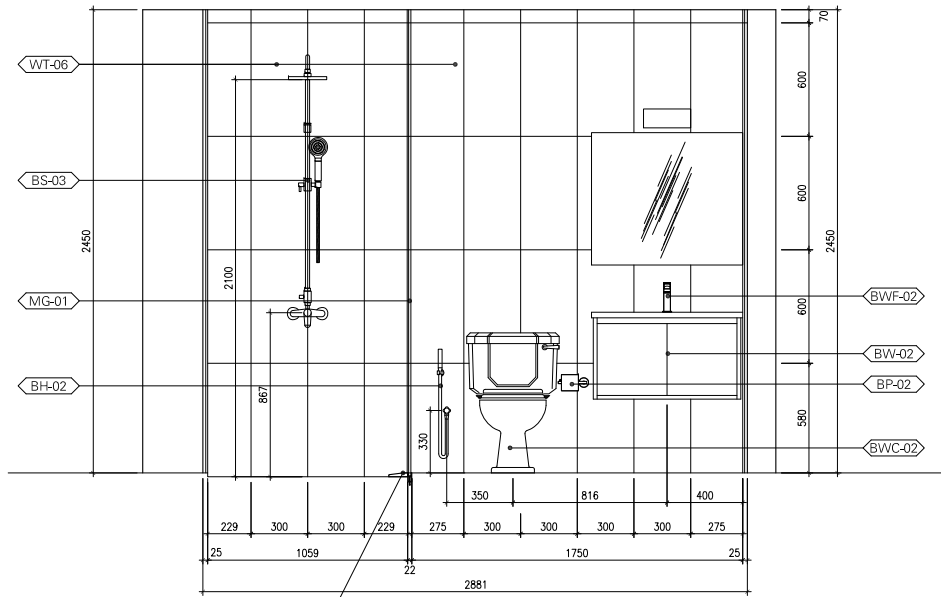


ELEVATION - 1
SCALE 1:20

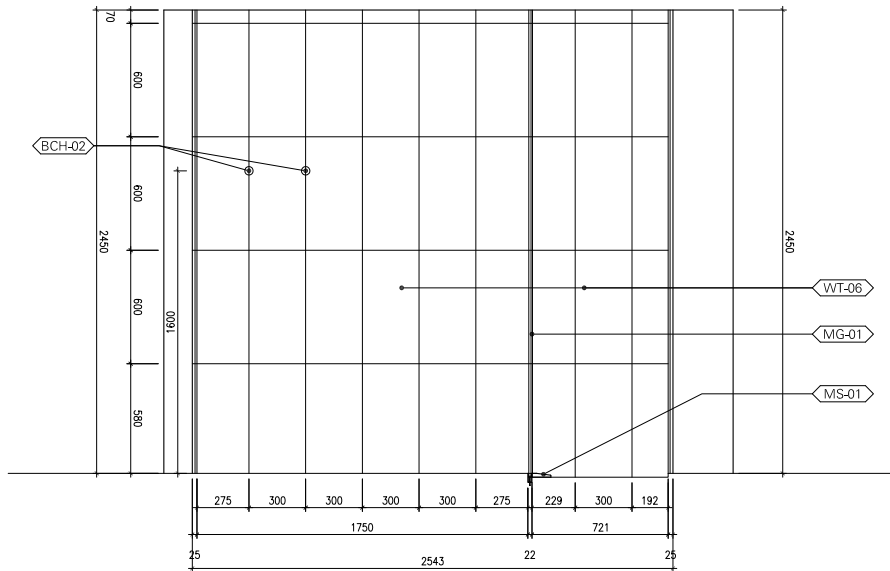

ELEVATION - 3
SCALE 1:20

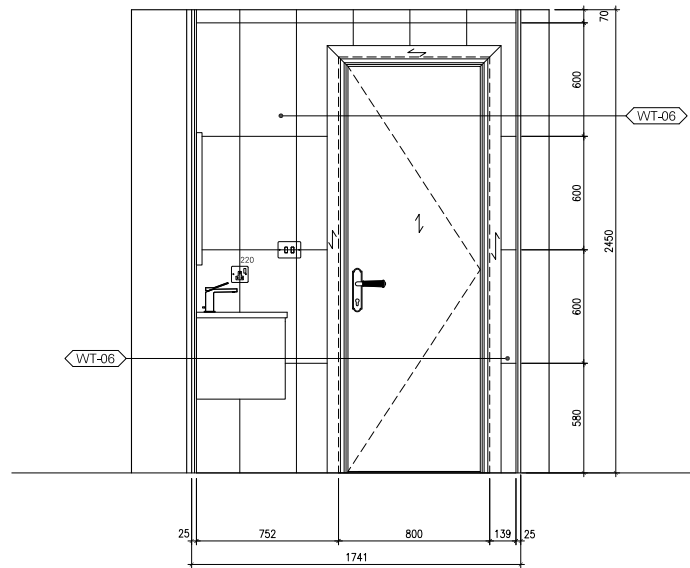

ELEVATION - 2
SCALE 1:20

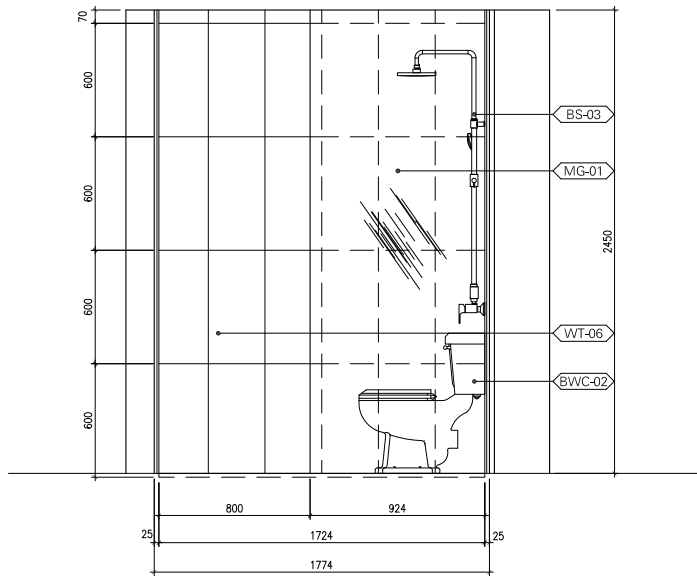

ELEVATION - 3
SCALE 1:20

GENERAL NOTES

1. This drawing shall be read in conjunction with all other relevant architectural, structural & electrical drawings including those of other consultants.
2. It is the responsibility of contractors & manufacturers to check all relevant site dimensions prior to the start of construction or manufacture.
3. All materials and components must be installed on site in accordance with manufacturer's instructions, shop drawings and standard details.
4. All dimensions are in millimeters unless noted otherwise.
5. Full working drawings, specifications and samples are to be provided by Contractor/Supplier for approval prior to manufacture.
6. Appropriate slope for the flooring to the drain to be provided by Contractor.

NOTES FOR MANUFACTURER:

- * Construction methods shown on drawings are suggested methods only.
- * All Fixing & Screws to be concealed. If not possible manufacturer to consult with designers before manufacture.
- * All site dimension to be confirmed by contractor prior to the manufacture of items.
- * All materials used in bathrooms to be water resistant, moisture, rust and mould treated such as marine ply, stainless steel, aluminum or equivalent.
- * All joints to be water sealed and water proof membrane to be provided as required.
- * All glass and mirrors to have polished smooth edges all round.
- * All Bathrooms, washrooms floors and steps to be in Hard non slip finish.

FINISHES

1. Full working drawings, specifications and samples are to be provided by Contractor/Supplier for approval prior to manufacture.
2. Please Refer to Finishing Schedule and Sanitary Schedule for full specifications:
KRR01-2-4-1-FIN
KRR01-2-4-1-WC

ACCESSORIES

1. All positions of sanitary accessories including towel rails, mirrors & artwork etc. to be confirmed on site and fixed after final approval.
2. Finishes will continue behind loose furniture fixtures. ie. mirrors and art works etc.

KEY PLAN

INITIAL ISSUE	MP	AM	SM	2025.02.11
REV.#	GENERAL NOTES	DRAWN BY	CHECKED BY	APPROVED BY

PROJECT TITLE	REFERENCE
---------------	-----------

KRR01-RIYADH	KRR01
	G

DRAWING TITLE

MAIN VILLA - FIRST FLOOR
STAFF BATH -3 (1-008)
PLAN AND ELEVATIONS

DRAWING NUMBER

ID-303

SCALE 1:20

FORMAT A1

ADDITIONAL NOTES

DESIGN DEVELOPMENT



SIMA MALAK + ALSSAMOURE DESIGN ASSOCIATES

P.O. Box 15707 - Riyadh 11454 KSA

Tel. 01 441 4963 - Fax. 01 441 3867

simal@simals.com

©SIMA MALAK + ALSSAMOURE DESIGN ASSOCIATES (شركة) 2003
This document including all drawing and text is the property and copyright of SIMA MALAK + ALSSAMOURE DESIGN ASSOCIATES for use solely with respect to this Project and shall not be copied or reproduced by any means except by agreement in writing from SIMA MALAK + ALSSAMOURE DESIGN ASSOCIATES.

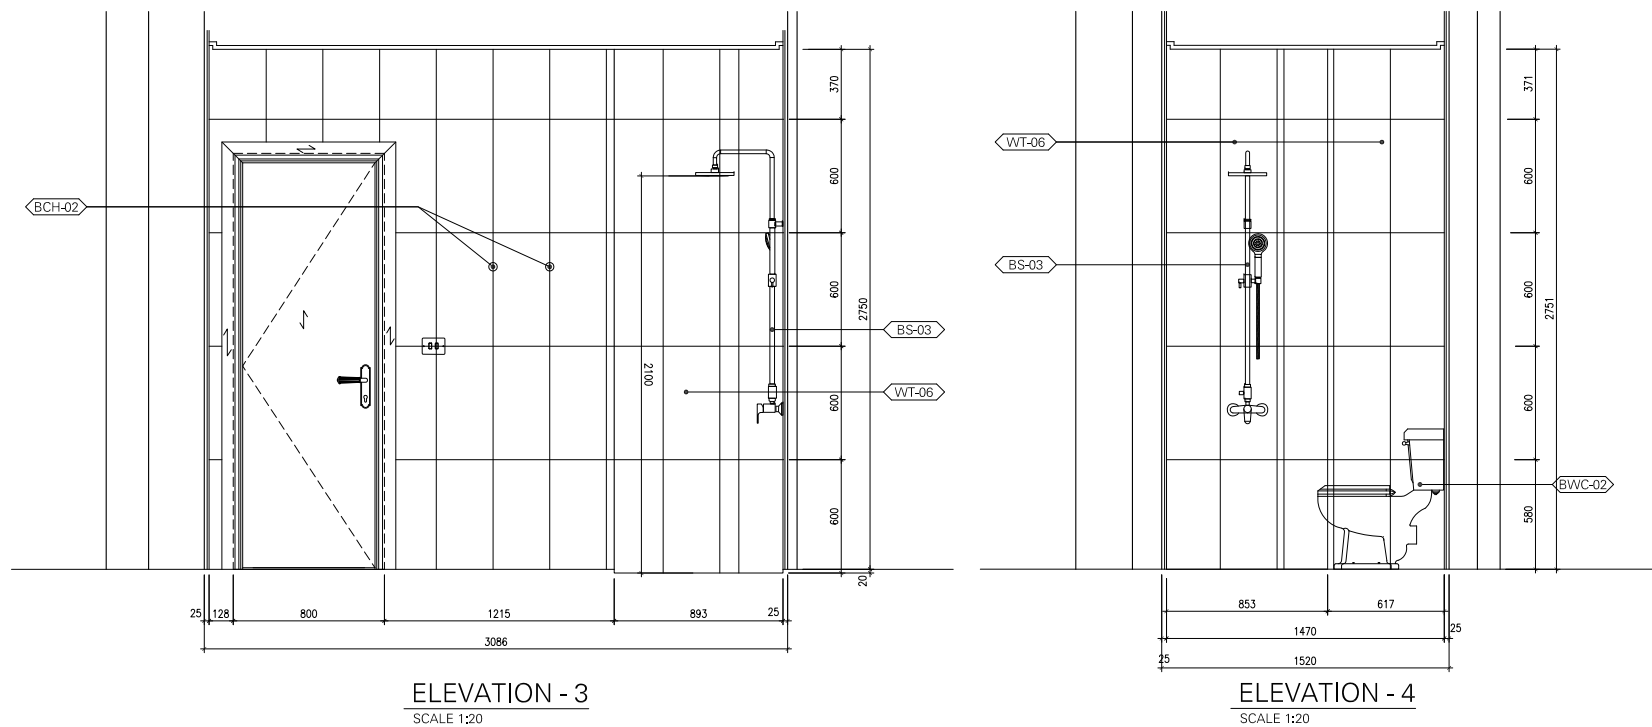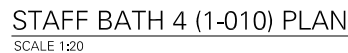

1. This drawing shall be read in conjunction with all other relevant architectural, structural & electrical drawings including those of other consultants.
2. It is the responsibility of contractors & manufacturers to check all relevant site dimensions prior to the start of construction or manufacture.
3. All materials and components must be installed on site in accordance with manufacturer's instructions, shop drawings and standard details.
4. All dimensions are in millimeters unless noted otherwise.
5. Full working drawings, specifications and samples are to be provided by Contractor/Supplier for approval prior to manufacture.
6. Appropriate slope for the flooring to the drain to be provided by Contractor.

- * Construction methods shown on drawings are suggested methods only.
- * All Fixing & Screws to be concealed. If not possible manufacturer to consult with designers before manufacture.
- * All site dimension to be confirmed by contractor prior to the manufacture of items.
- * All materials used in bathrooms to be water resistant, moisture, rust and mould treated such as marine ply, stainless steel, aluminum or equivalent.
- * All joints to be water sealed and water proof membrane to be applied as required.
- * All glass surfaces must have polished smooth edges all round.
- * All Bathrooms, washrooms floors and steps to be in Hard non slip finish.

1. Full working drawings, specifications and samples are to be provided by Contractor/Supplier for approval prior to manufacture.

2. Please Refer to Finishing Schedule and Sanitary Schedule for full specifications:

KRR01-2-4-1-FIN
KRR01-2-4-1-WC

1. All positions of sanitary accessories including towel rails, mirrors & artwork etc. to be confirmed on site and fixed after final approval.


2. Finishes will continue behind loose furniture fixtures. ie.mirrors and art works etc.

X	INITIAL ISSUE	AC	AM	SM	2025.02.11		
REV.#	GENERAL NOTES	DRAWN BY	CHECKED BY	APPROVED BY	DATE		
PROJECT TITLE						REFERENCE	
KRR01-RIYADH						KRR01 G	


DRAWING TITLE			
MAIN VILLA - FIRST FLOOR STAFF BATH - 4 (1-010) PLAN AND ELEVATIONS			
DRAWING NUMBER			REVISION
ID-304			
SCALE	FORMAT	ADDITIONAL NOTES	DESIGN DEVELOPMENT
1:20	A1		




©SIMA MALAK + ALSSAMOURÉ DESIGN ASSOCIATES (سـمـوـر) 2003
This document including all drawing and text is the property and
copyright of SIMA MALAK + ALSSAMOURÉ DESIGN ASSOCIATES for
use solely with respect to this Project and shall not be copied or
reproduced by any means except by agreement in writing from
SIMA MALAK + ALSSAMOURÉ DESIGN ASSOCIATES.

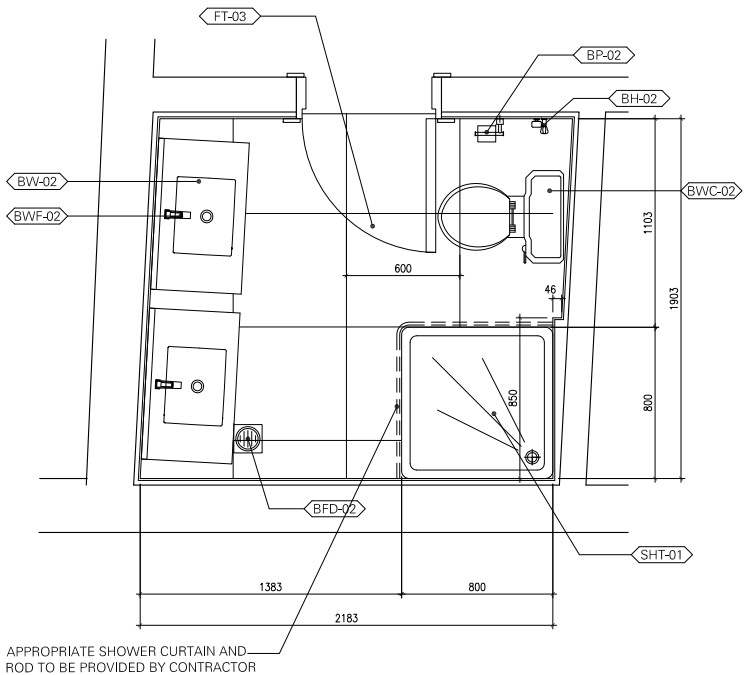


STAFF BATH-5 (1-015) PLAN
SCALE 1:20

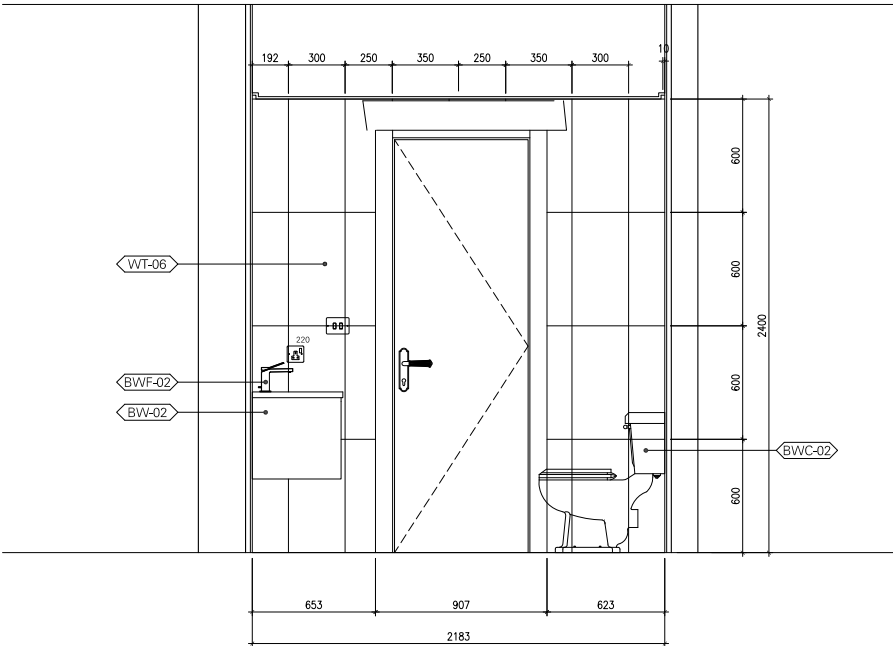


ELEVATION - 4
SCALE 1:20

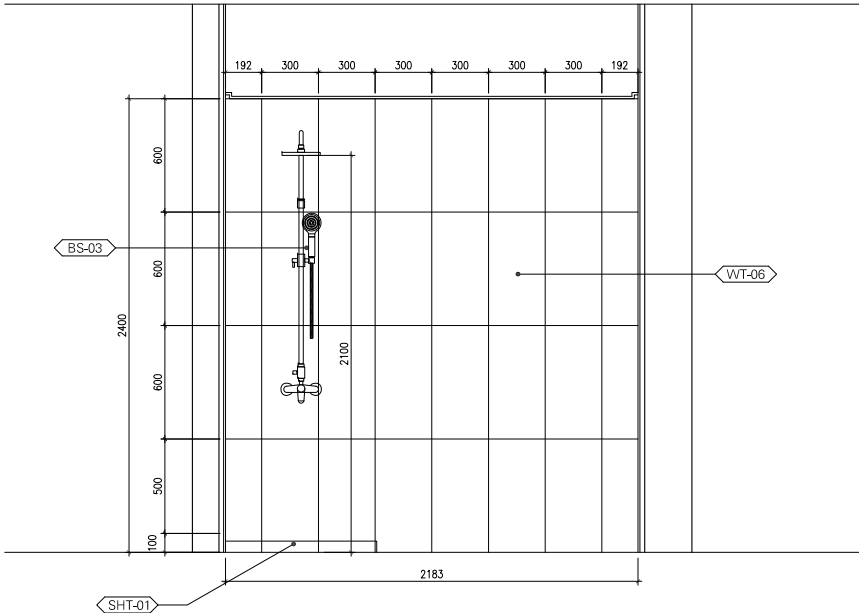

ELEVATION - 2
SCALE 1:20

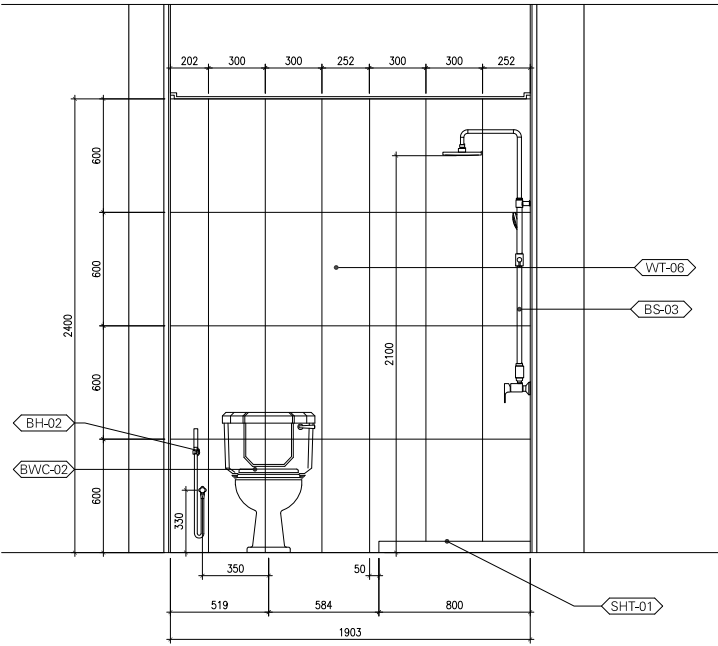

ELEVATION - 3
SCALE 1:20

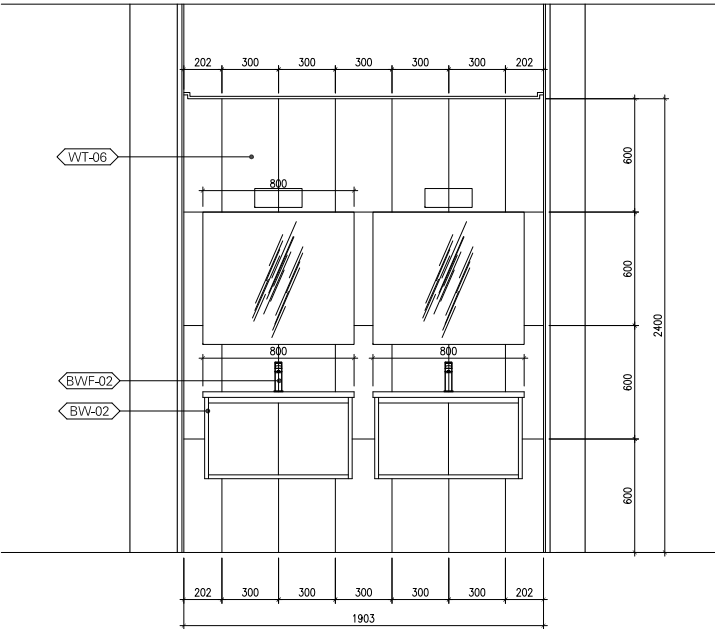

ELEVATION - 4
SCALE 1:20

GENERAL NOTES

1. This drawing shall be read in conjunction with all other relevant architectural, structural & electrical drawings including those of other consultants.
2. It is the responsibility of contractors & manufacturers to check all relevant site dimensions prior to the start of construction or manufacture.
3. All materials and components must be installed on site in accordance with manufacturer's instructions, shop drawings and standard details.
4. All dimensions are in millimeters unless noted otherwise.
5. Full working drawings, specifications and samples are to be provided by Contractor/Supplier for approval prior to manufacture.
6. Appropriate slope for the flooring to the drain to be provided by Contractor.

NOTES FOR MANUFACTURER:

- * Construction methods shown on drawings are suggested methods only.
- * All Fixing & Screws to be concealed. If not possible manufacturer to consult with designers before manufacture.
- * All site dimension to be confirmed by contractor prior to the manufacture of items.
- * All materials used in bathrooms to be water resistant, moisture, rust and mould treated such as marine ply, stainless steel, aluminum or equivalent.
- * All joints to be water sealed and water proof membrane to be provided as required.
- * All glass and mirrors to have polished smooth edges all round.
- * All Bathrooms, washrooms floors and steps to be in Hard non slip finish.

FINISHES

1. Full working drawings, specifications and samples are to be provided by Contractor/Supplier for approval prior to manufacture.
2. Please Refer to Finishing Schedule and Sanitary Schedule for full specifications:
KRR01-2-4-1-FIN
KRR01-2-4-1-WC

ACCESSORIES

1. All positions of sanitary accessories including towel rails, mirrors & artwork etc. to be confirmed on site and fixed after final approval.
2. Finishes will continue behind loose furniture fixtures. ie. mirrors and art works etc.


KEY PLAN

	INITIAL ISSUE	MP	AM	SM	2025.02.11
REV.#	GENERAL NOTES	DRAWN BY	CHECKED BY	APPROVED BY	DATE
PROJECT TITLE					REFERENCE
KRR01-RIYADH					KRR01
					G


DRAWING TITLE			
MAIN VILLA - FIRST FLOOR STAFF BATH-5 (1-015) PLAN AND ELEVATIONS			
DRAWING NUMBER			REVISION
ID-305			
SCALE	FORMAT	ADDITIONAL NOTES	DESIGN DEVELOPMENT
1:20	A1		

**SIMA MALAK + ALSSAMOURE
DESIGN ASSOCIATES**
P.O. Box 15707 - Riyadh 11454 KSA
Tel. 01 441 4963 - Fax. 01 441 3867
simals@simals.com


©SIMA MALAK + ALSSAMOURE DESIGN ASSOCIATES (شركة) 2003
This document including all drawing and text is the property and
copyright of SIMA MALAK + ALSSAMOURE DESIGN ASSOCIATES for
use solely with respect to this Project and shall not be copied or
reproduced by any means except by agreement in writing from
SIMA MALAK + ALSSAMOURE DESIGN ASSOCIATES.

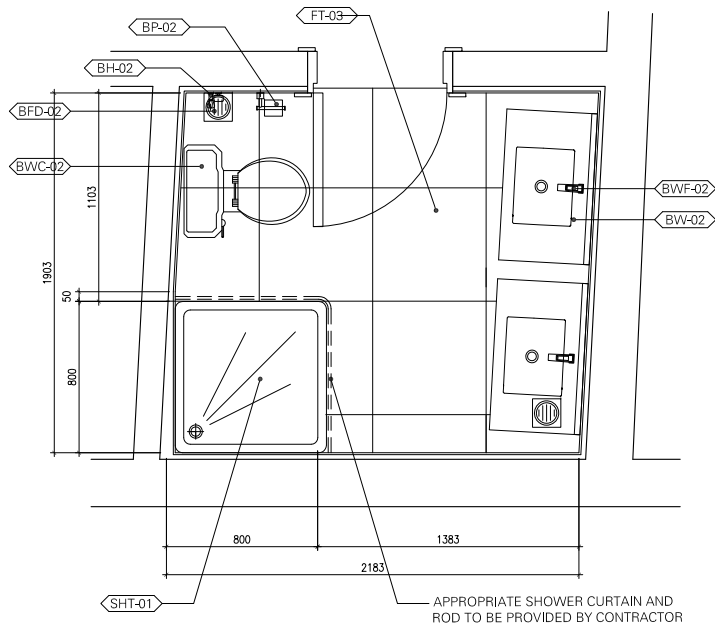


STAFF BATH-6 (1-016) PLAN
SCALE 1:20

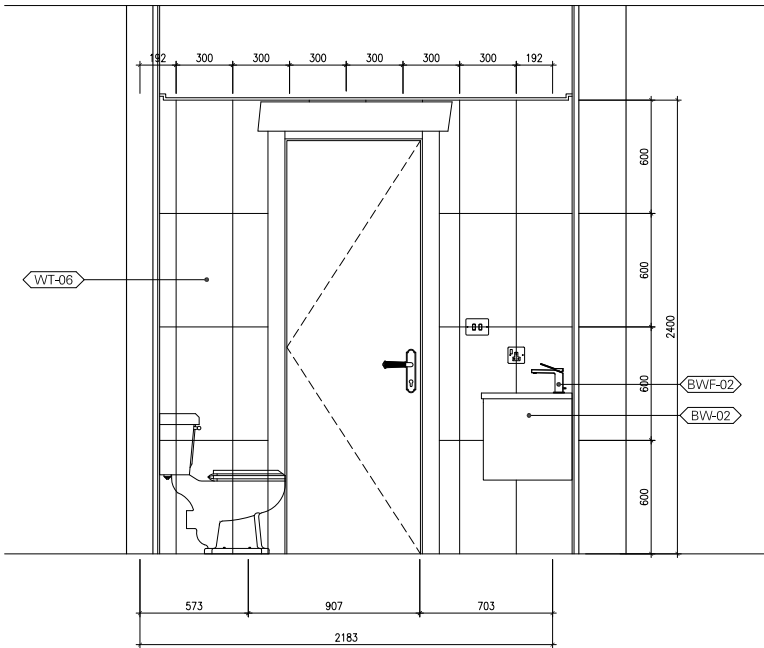


ELEVATION - 1
SCALE 1:20

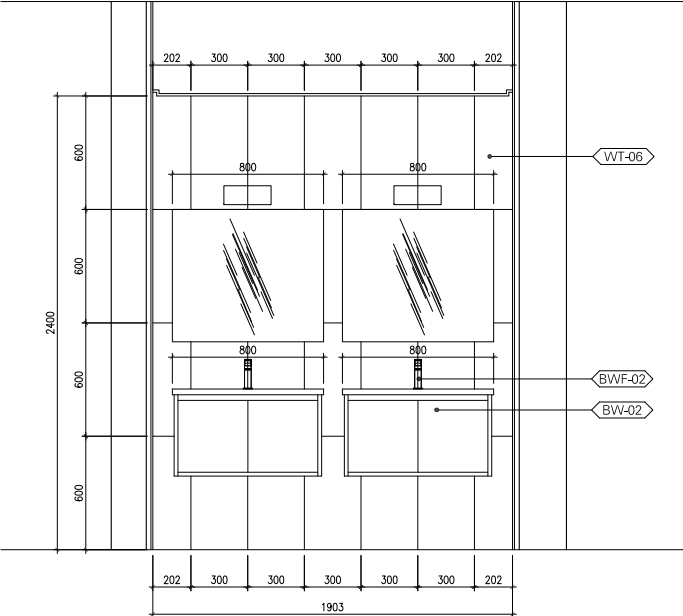

ELEVATION - 2
SCALE 1:20

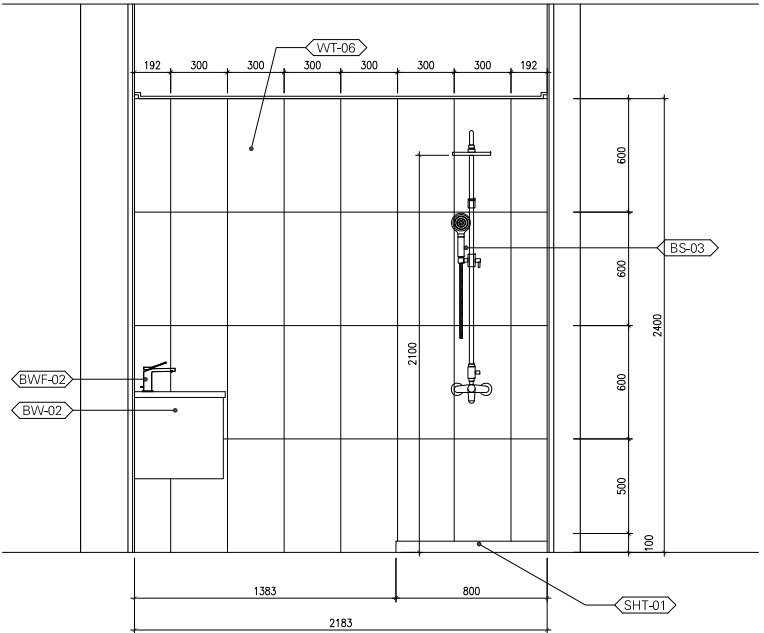

ELEVATION - 3
SCALE 1:20

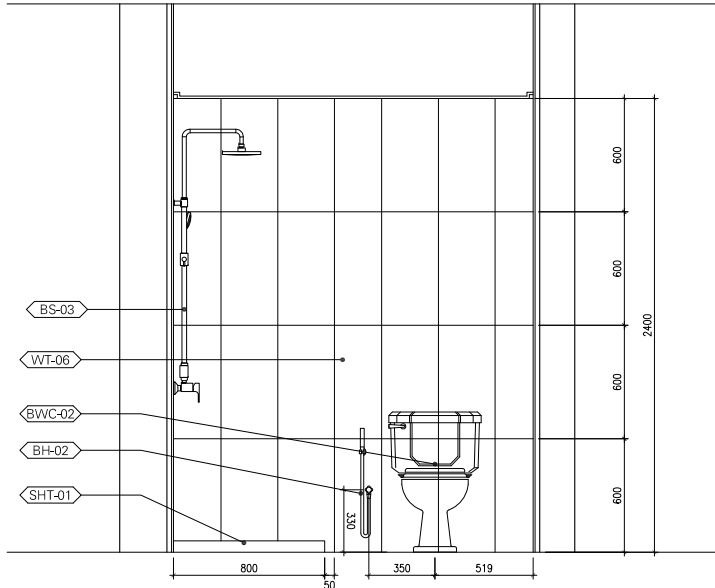

ELEVATION - 4
SCALE 1:20

GENERAL NOTES

1. This drawing shall be read in conjunction with all other relevant architectural, structural & electrical drawings including those of other consultants.
2. It is the responsibility of contractors & manufacturers to check all relevant site dimensions prior to the start of construction or manufacture.
3. All materials and components must be installed on site in accordance with manufacturer's instructions, shop drawings and standard details.
4. All dimensions are in millimeters unless noted otherwise.
5. Full working drawings, specifications and samples are to be provided by Contractor/Supplier for approval prior to manufacture.
6. Appropriate slope for the flooring to the drain to be provided by Contractor.

NOTES FOR MANUFACTURER:

- * Construction methods shown on drawings are suggested methods only.
- * All Fixing & Screws to be concealed. If not possible manufacturer to consult with designers before manufacture.
- * All site dimension to be confirmed by contractor prior to the manufacture of items.
- * All materials used in bathrooms to be water resistant, moisture, rust and mould treated such as marine ply, stainless steel, aluminum or equivalent.
- * All joints to be water sealed and water proof membrane to be provided as required.
- * All glass and mirrors to have polished smooth edges all round.
- * All Bathrooms, washrooms floors and steps to be in Honed non slip finish.

FINISHES

1. Full working drawings, specifications and samples are to be provided by Contractor/Supplier for approval prior to manufacture.
2. Please Refer to Finishing Schedule and Sanitary Schedule for full specifications:
KRR01-2-4-1-FIN
KRR01-2-4-1-WC

ACCESSORIES

1. All positions of sanitary accessories including towel rails, mirrors & artwork etc. to be confirmed on site and fixed after final approval.
2. Finishes will continue behind loose furniture fixtures. ie. mirrors and art works etc.

KEY PLAN

INITIAL ISSUE	AC	AM	SM	2025.02.11
REV.#	GENERAL NOTES	DRAWN BY	CHECKED BY	APPROVED BY

PROJECT TITLE	REFERENCE
KRR01-RIYADH	KRR01 G




DRAWING TITLE
MAIN VILLA - FIRST FLOOR STAFF BATH-6 (1-016) PLAN PLAN AND ELEVATIONS

DRAWING NUMBER	REVISION
ID-306	

SCALE	FORMAT	ADDITIONAL NOTES	DESIGN DEVELOPMENT
1:20	A1		

SIMA MALAK + ALSSAMOURE
DESIGN ASSOCIATES
P.O. Box 15707 - Riyadh 11454 KSA
Tel. 01 441 4963 - Fax. 01 441 3867
simals@simals.com

©SIMA MALAK + ALSSAMOURE DESIGN ASSOCIATES (شركة) 2003
This document including all drawing and text is the property and copyright of SIMA MALAK + ALSSAMOURE DESIGN ASSOCIATES for use solely with respect to this Project and shall not be copied or reproduced by any means except by agreement in writing from SIMA MALAK + ALSSAMOURE DESIGN ASSOCIATES.

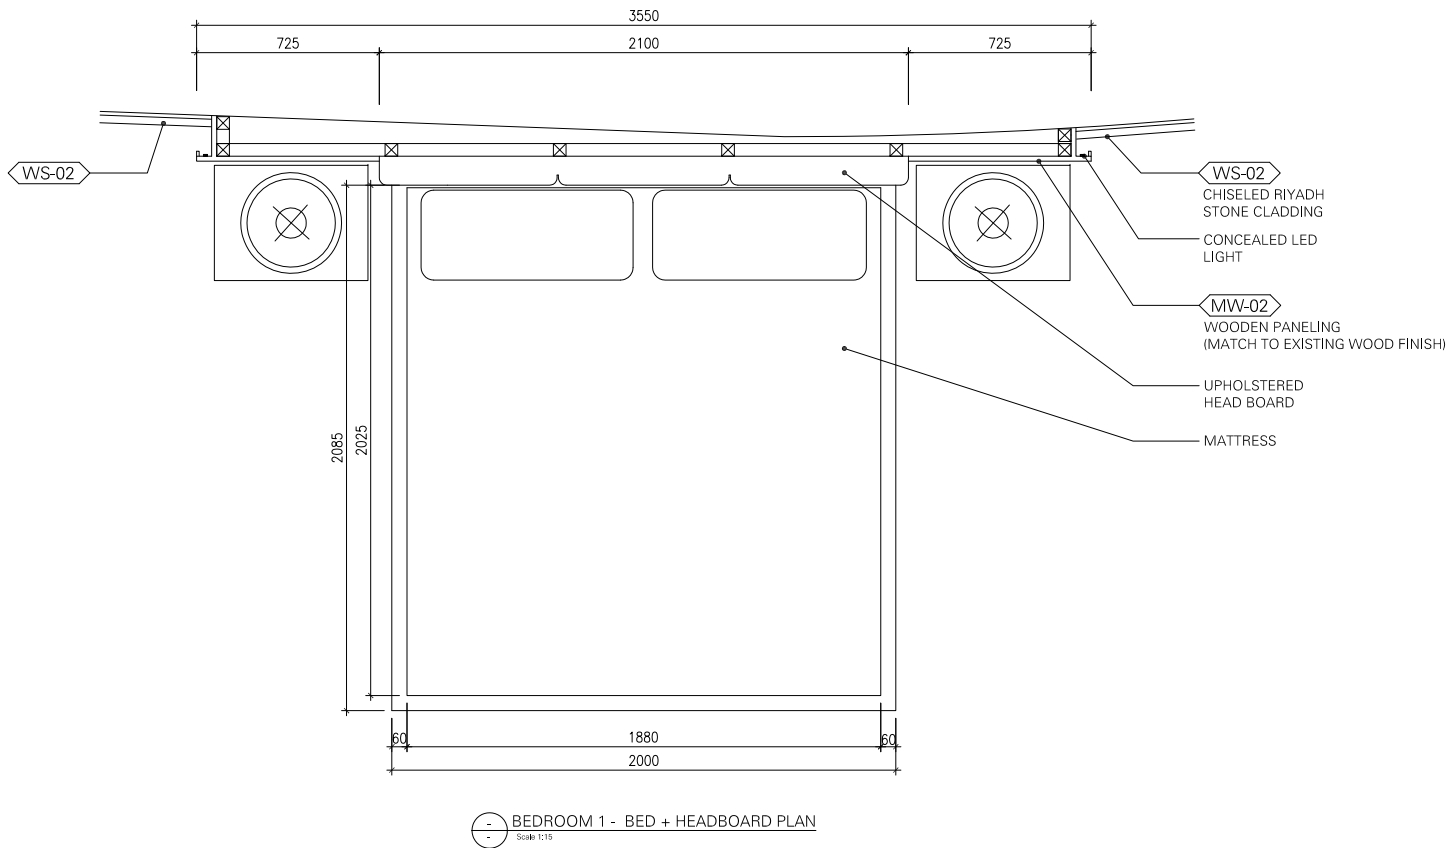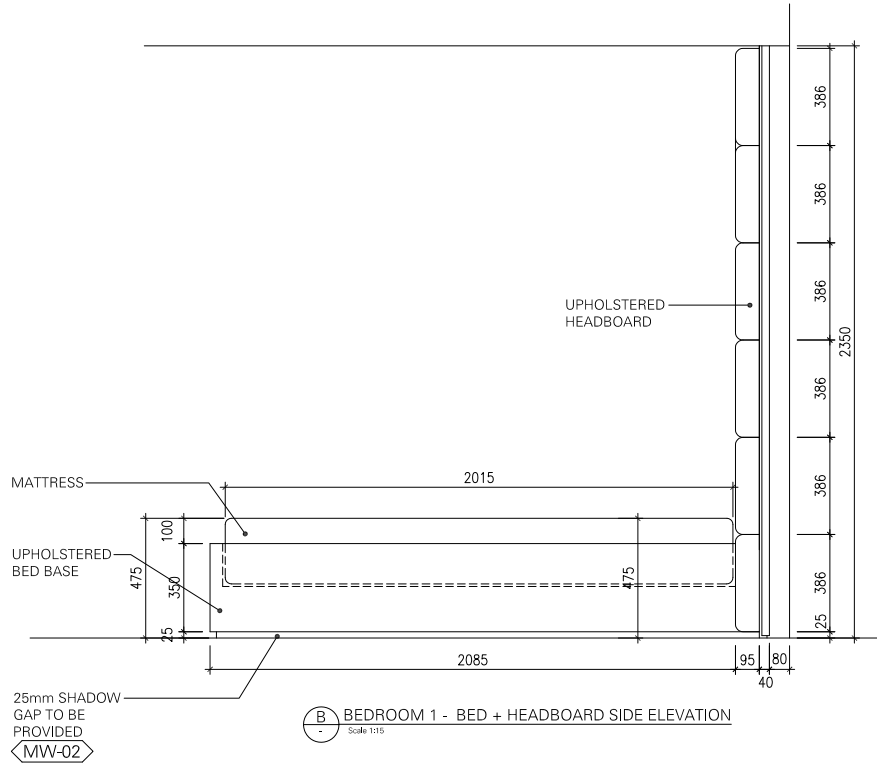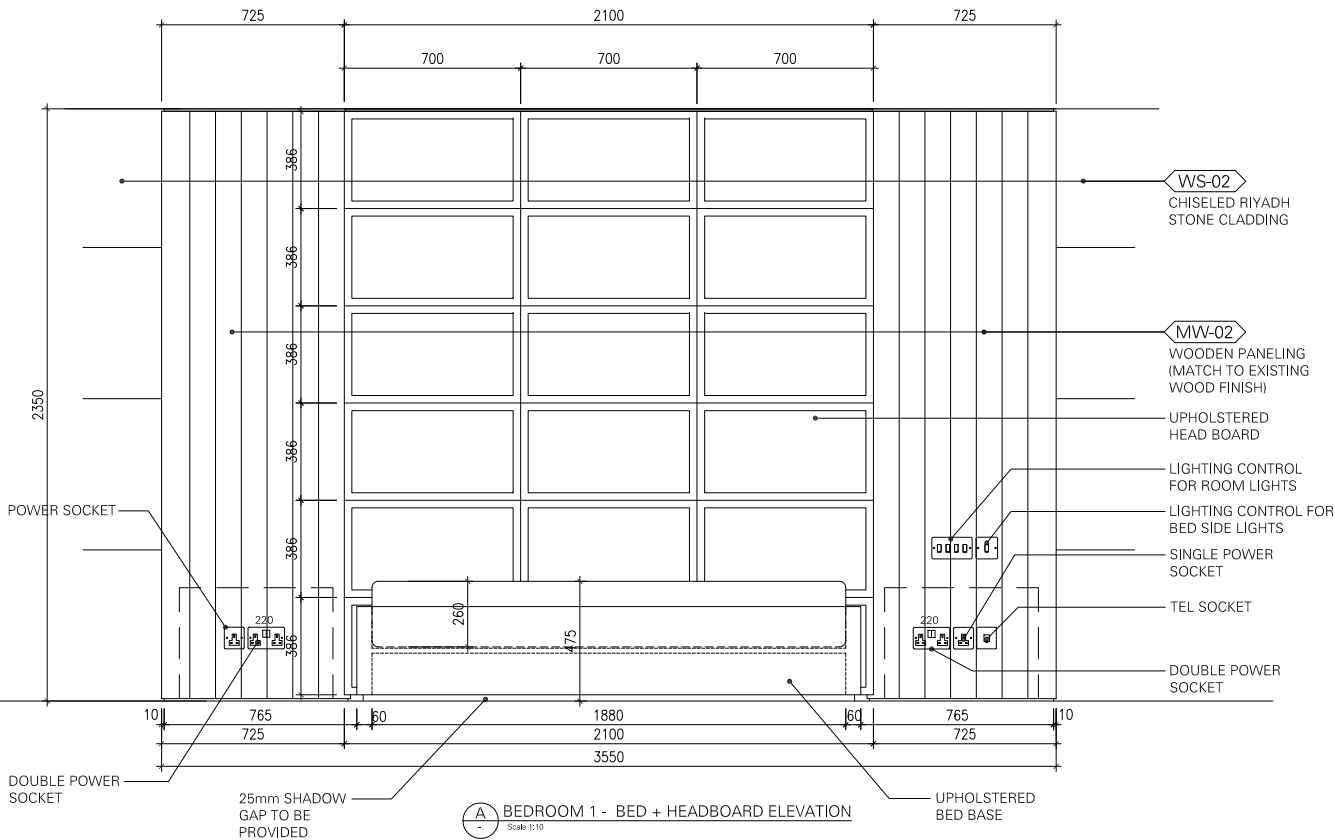

GENERAL NOTES

1. This drawing shall be read in conjunction with all other relevant architectural, structural & electrical drawings including those of other consultants.
2. It is the responsibility of contractors & manufacturers to check all relevant site dimensions prior to the start of construction or manufacture.
3. All materials and components must be installed on site in accordance with manufacturer's instructions, shop drawings and standard details.
4. All dimensions are in millimeters unless noted otherwise.
5. Full working drawings, specifications and samples are to be provided by Contractor/Supplier for approval prior to manufacture.

NOTES FOR MANUFACTURER:

- * Construction methods shown on drawings are suggested methods only.
- * All Fixing & Screws to be concealed. If not possible manufacturer to consult with designers before manufacture.
- * All site dimension to be confirmed by contractor prior to the manufacture of items.
- * All materials used in bathrooms to be water resistant, moisture, rust and mould treated such as marine ply, stainless steel, aluminum or equivalent.
- * All joints to be water sealed and water proof membrane to be provided as required.
- * All glass and mirrors to have polished smooth edges all round.

FINISHES

1. Full working drawings, specifications and samples are to be provided by Contractor/Supplier for approval prior to manufacture.
2. Please Refer to Finishing Schedule and Sanitary Schedule for full specifications:
KRR01-2-4-1-FIN
KRR01-2-4-1-WC

KEY PLAN

☒	INITIAL ISSUE	AC/MP	AM	SM	2025.02.11
REV.#	GENERAL NOTES	DRAWN BY	CHECKED BY	APPROVED BY	DATE

PROJECT TITLE	REFERENCE
---------------	-----------

KRR01-RIYADH	KRR01
	G

DRAWING TITLE

BEDROOM-1 (1-001)
BED + HEADBOARD
PLAN AND ELEVATIONS

DRAWING NUMBER REVISION




ID-401

SCALE	FORMAT	ADDITIONAL NOTES	DESIGN DEVELOPMENT
1:15	A1		



**SIMA MALAK + ALSSAMOURE
DESIGN ASSOCIATES**
P.O. Box 15707 - Riyadh 11454 KSA
Tel. 01 441 4963 - Fax. 01 441 3867
simals@simals.com

©SIMA MALAK + ALSSAMOURE DESIGN ASSOCIATES (شركة) 2003
This document including all drawing and text is the property and
copyright of SIMA MALAK + ALSSAMOURE DESIGN ASSOCIATES for
use solely with respect to this Project and shall not be copied or
reproduced by any means except by agreement in writing from
SIMA MALAK + ALSSAMOURE DESIGN ASSOCIATES.

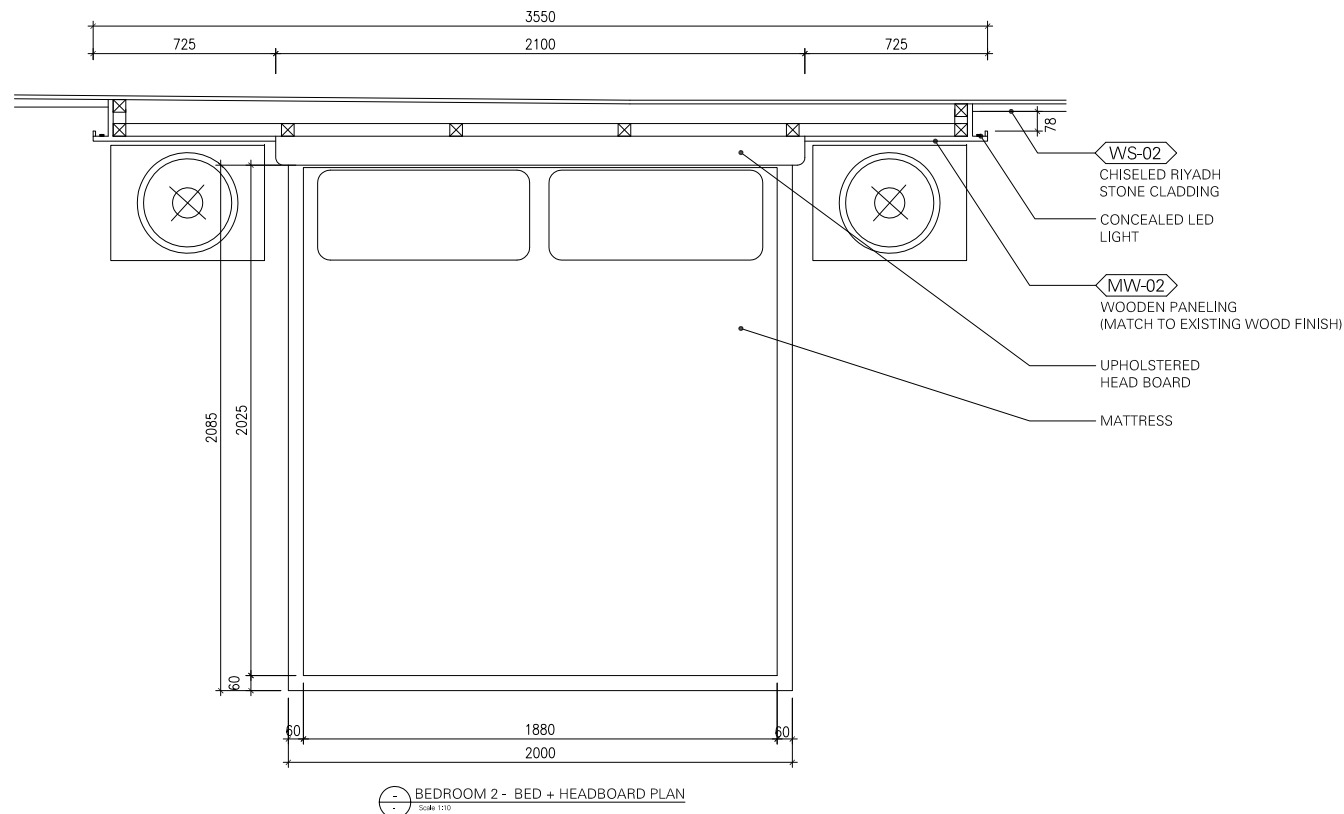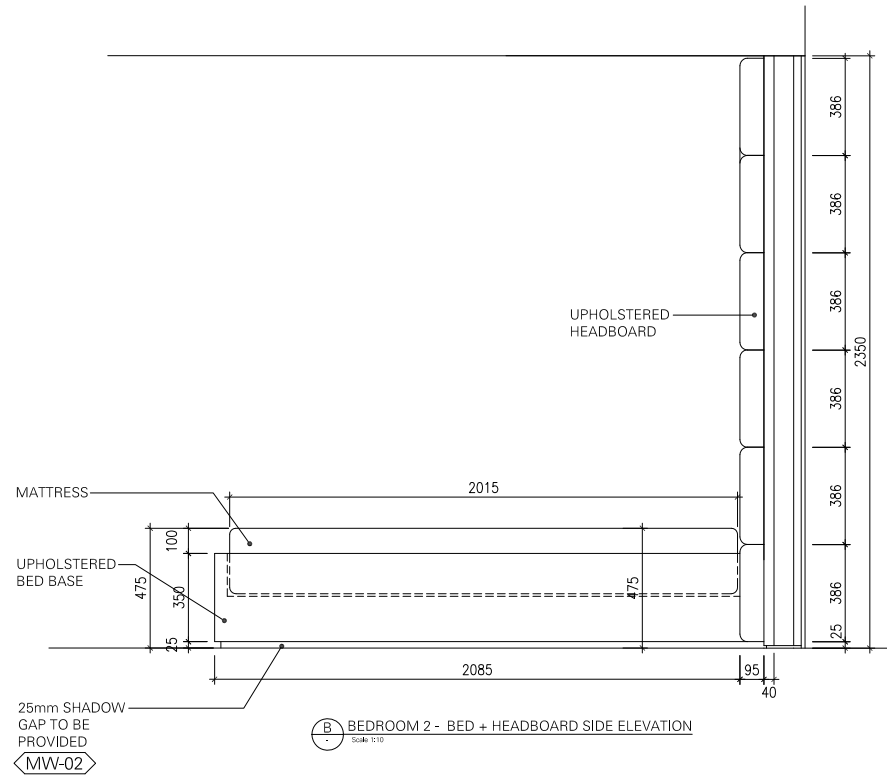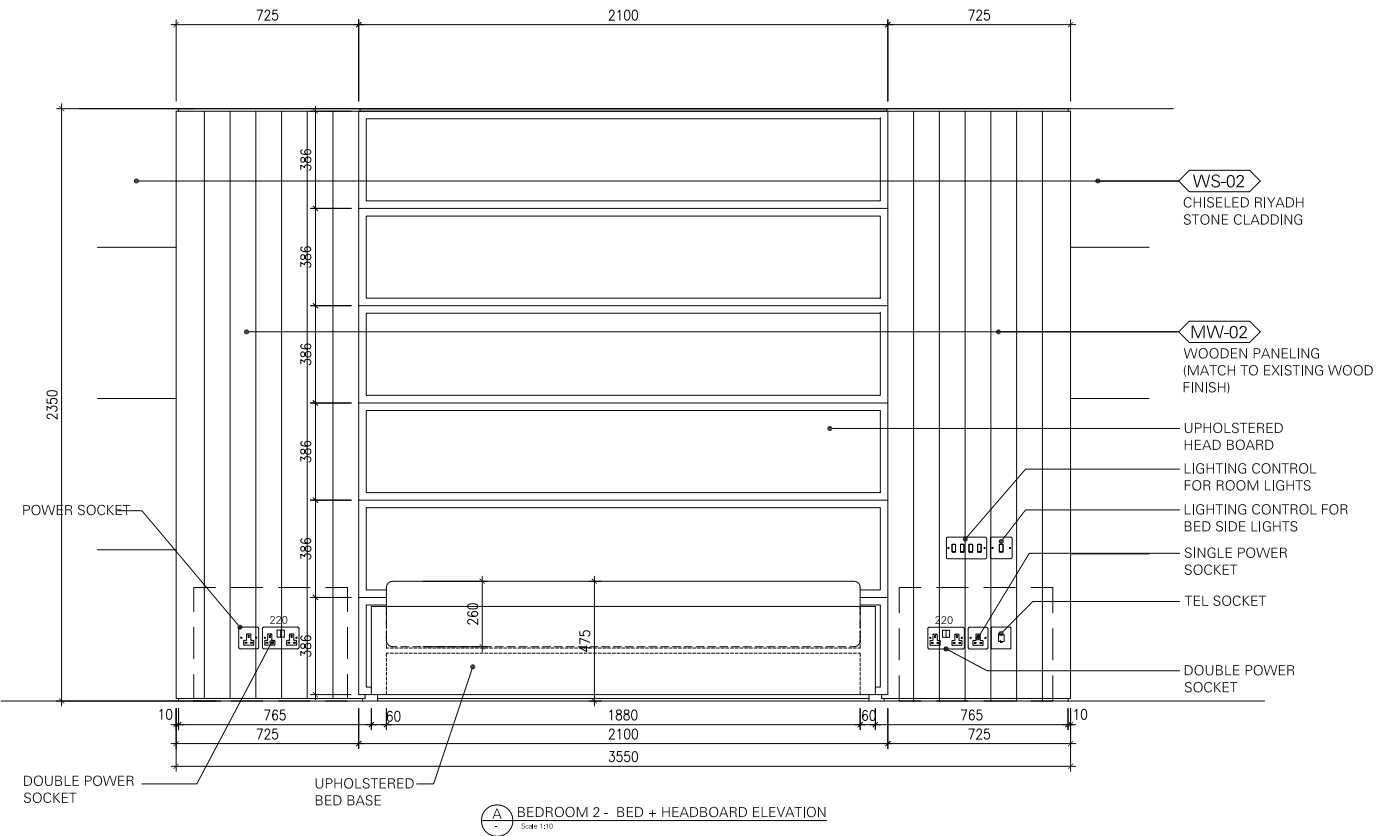

GENERAL NOTES

1. This drawing shall be read in conjunction with all other relevant architectural, structural & electrical drawings including those of other consultants.
2. It is the responsibility of contractors & manufacturers to check all relevant site dimensions prior to the start of construction or manufacture.
3. All materials and components must be installed on site in accordance with manufacturer's instructions, shop drawings and standard details.
4. All dimensions are in millimeters unless noted otherwise.
5. Full working drawings, specifications and samples are to be provided by Contractor/Supplier for approval prior to manufacture.

NOTES FOR MANUFACTURER:

- * Construction methods shown on drawings are suggested methods only.
- * All Fixing & Screws to be concealed. If not possible manufacturer to consult with designers before manufacture.
- * All site dimension to be confirmed by contractor prior to the manufacture of items.
- * All materials used in bathrooms to be water resistant, moisture, rust and mould treated such as marine ply, stainless steel, aluminum or equivalent.
- * All joints to be water sealed and water proof membrane to be provided as required.
- * All glass and mirrors to have polished smooth edges all round.

FINISHES

1. Full working drawings, specifications and samples are to be provided by Contractor/Supplier for approval prior to manufacture.
2. Please Refer to Finishing Schedule and Sanitary Schedule for full specifications:
KRR01-2-4-1-FIN
KRR01-2-4-1-WC

KEY PLAN

☒	INITIAL ISSUE	AC/MP	AM	SM	2025.02.11
-------------------------------------	---------------	-------	----	----	------------

REV.#	GENERAL NOTES	DRAWN BY	CHECKED BY	APPROVED BY	DATE
-------	---------------	----------	------------	-------------	------

PROJECT TITLE	REFERENCE
---------------	-----------

KRR01-RIYADH	KRR01 G
--------------	------------

DRAWING TITLE

BEDROOM-2 (1-004)
BED + HEADBOARD
PLAN AND ELEVATIONS

DRAWING NUMBER REVISION

ID-404


SCALE	FORMAT	ADDITIONAL NOTES	DESIGN DEVELOPMENT
1:15	A1		




**SIMA MALAK + ALSSAMOURE
DESIGN ASSOCIATES**

P.O. Box 15707 - Riyadh 11454 KSA
Tel. 01 441 4963 - Fax. 01 441 3867
simals@simals.com


©SIMA MALAK + ALSSAMOURE DESIGN ASSOCIATES (شركة) 2003
This document including all drawing and text is the property and
copyright of SIMA MALAK + ALSSAMOURE DESIGN ASSOCIATES for
use solely with respect to this Project and shall not be copied or
reproduced by any means except by agreement in writing from
SIMA MALAK + ALSSAMOURE DESIGN ASSOCIATES.

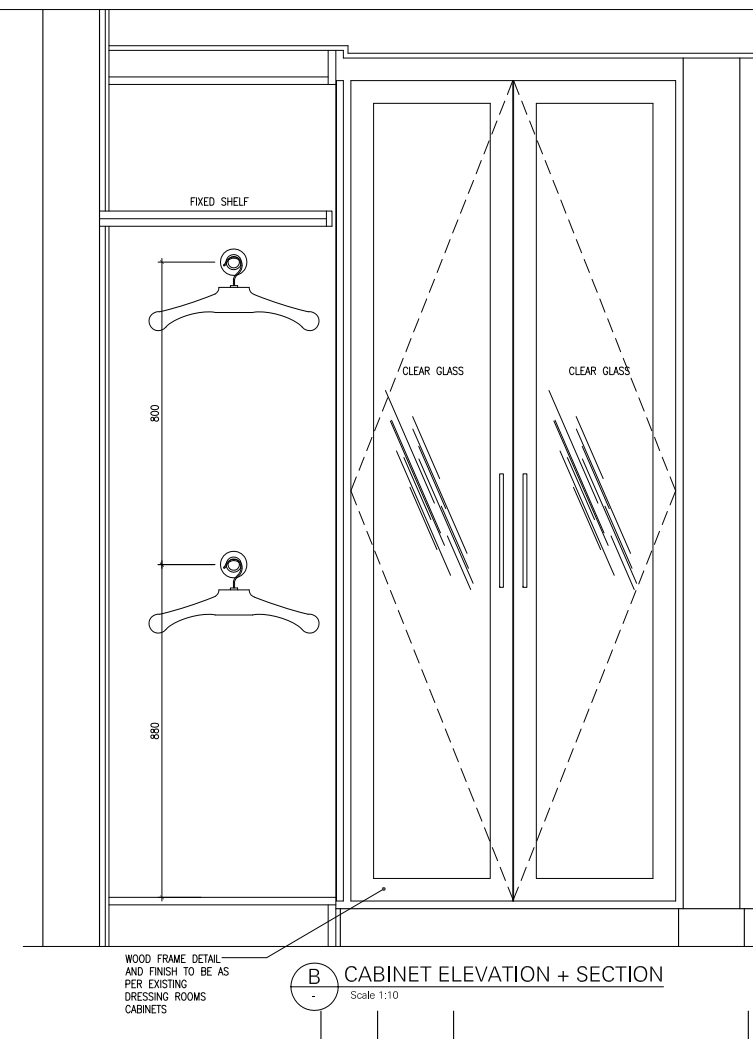

B CABINET ELEVATION + SECTION
- Scale 1:10

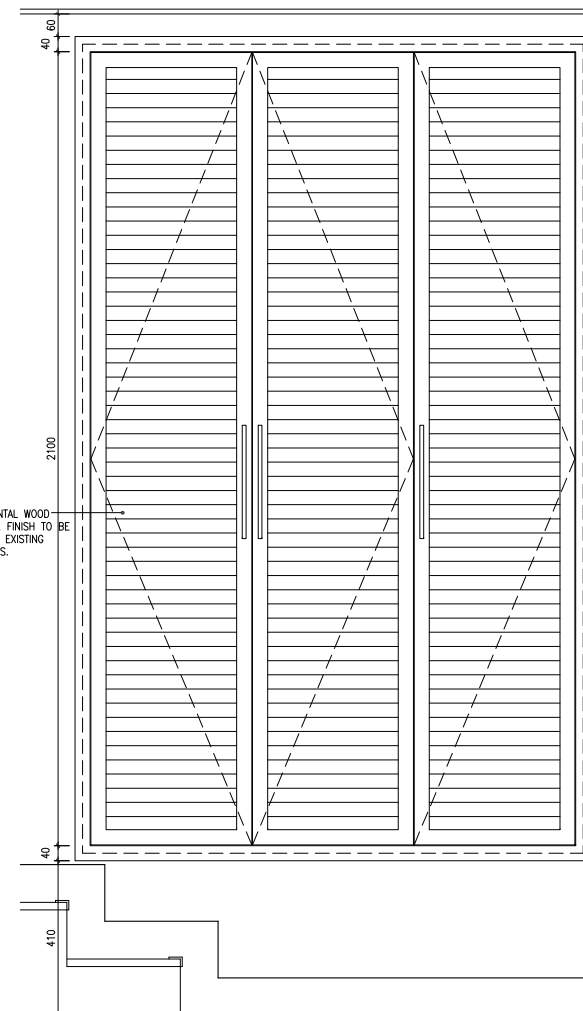

C CABINET ELEVATION
- Scale 1:10

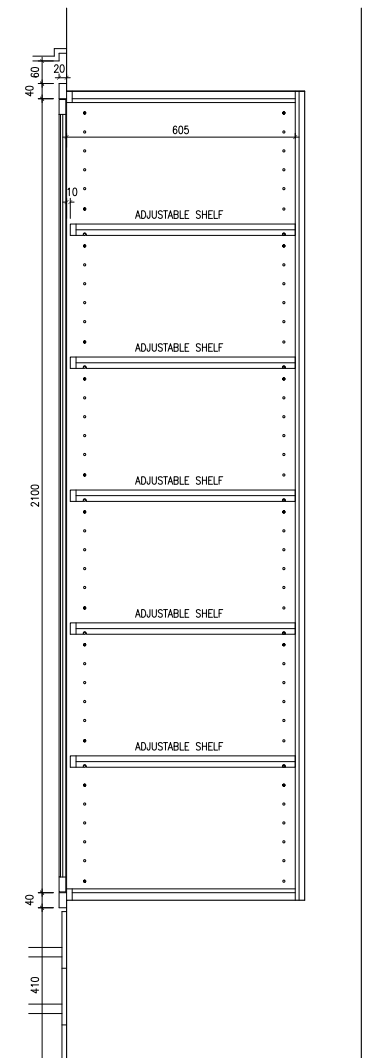

D CABINET SECTION
Scale 1:10

©SIMA MALAK + ALSSAMOUR DESIGN ASSOCIATES (سـمـا) 200
This document including all drawing and text is the property and
copyright of SIMA MALAK + ALSSAMOUR DESIGN ASSOCIATES (سـمـا).
It shall not be copied, reproduced or used in any form or by any
means, electronic or mechanical, including photocopying, recording,
or by any information storage and retrieval system, without the
written permission of SIMA MALAK + ALSSAMOUR DESIGN ASSOCIATES.