


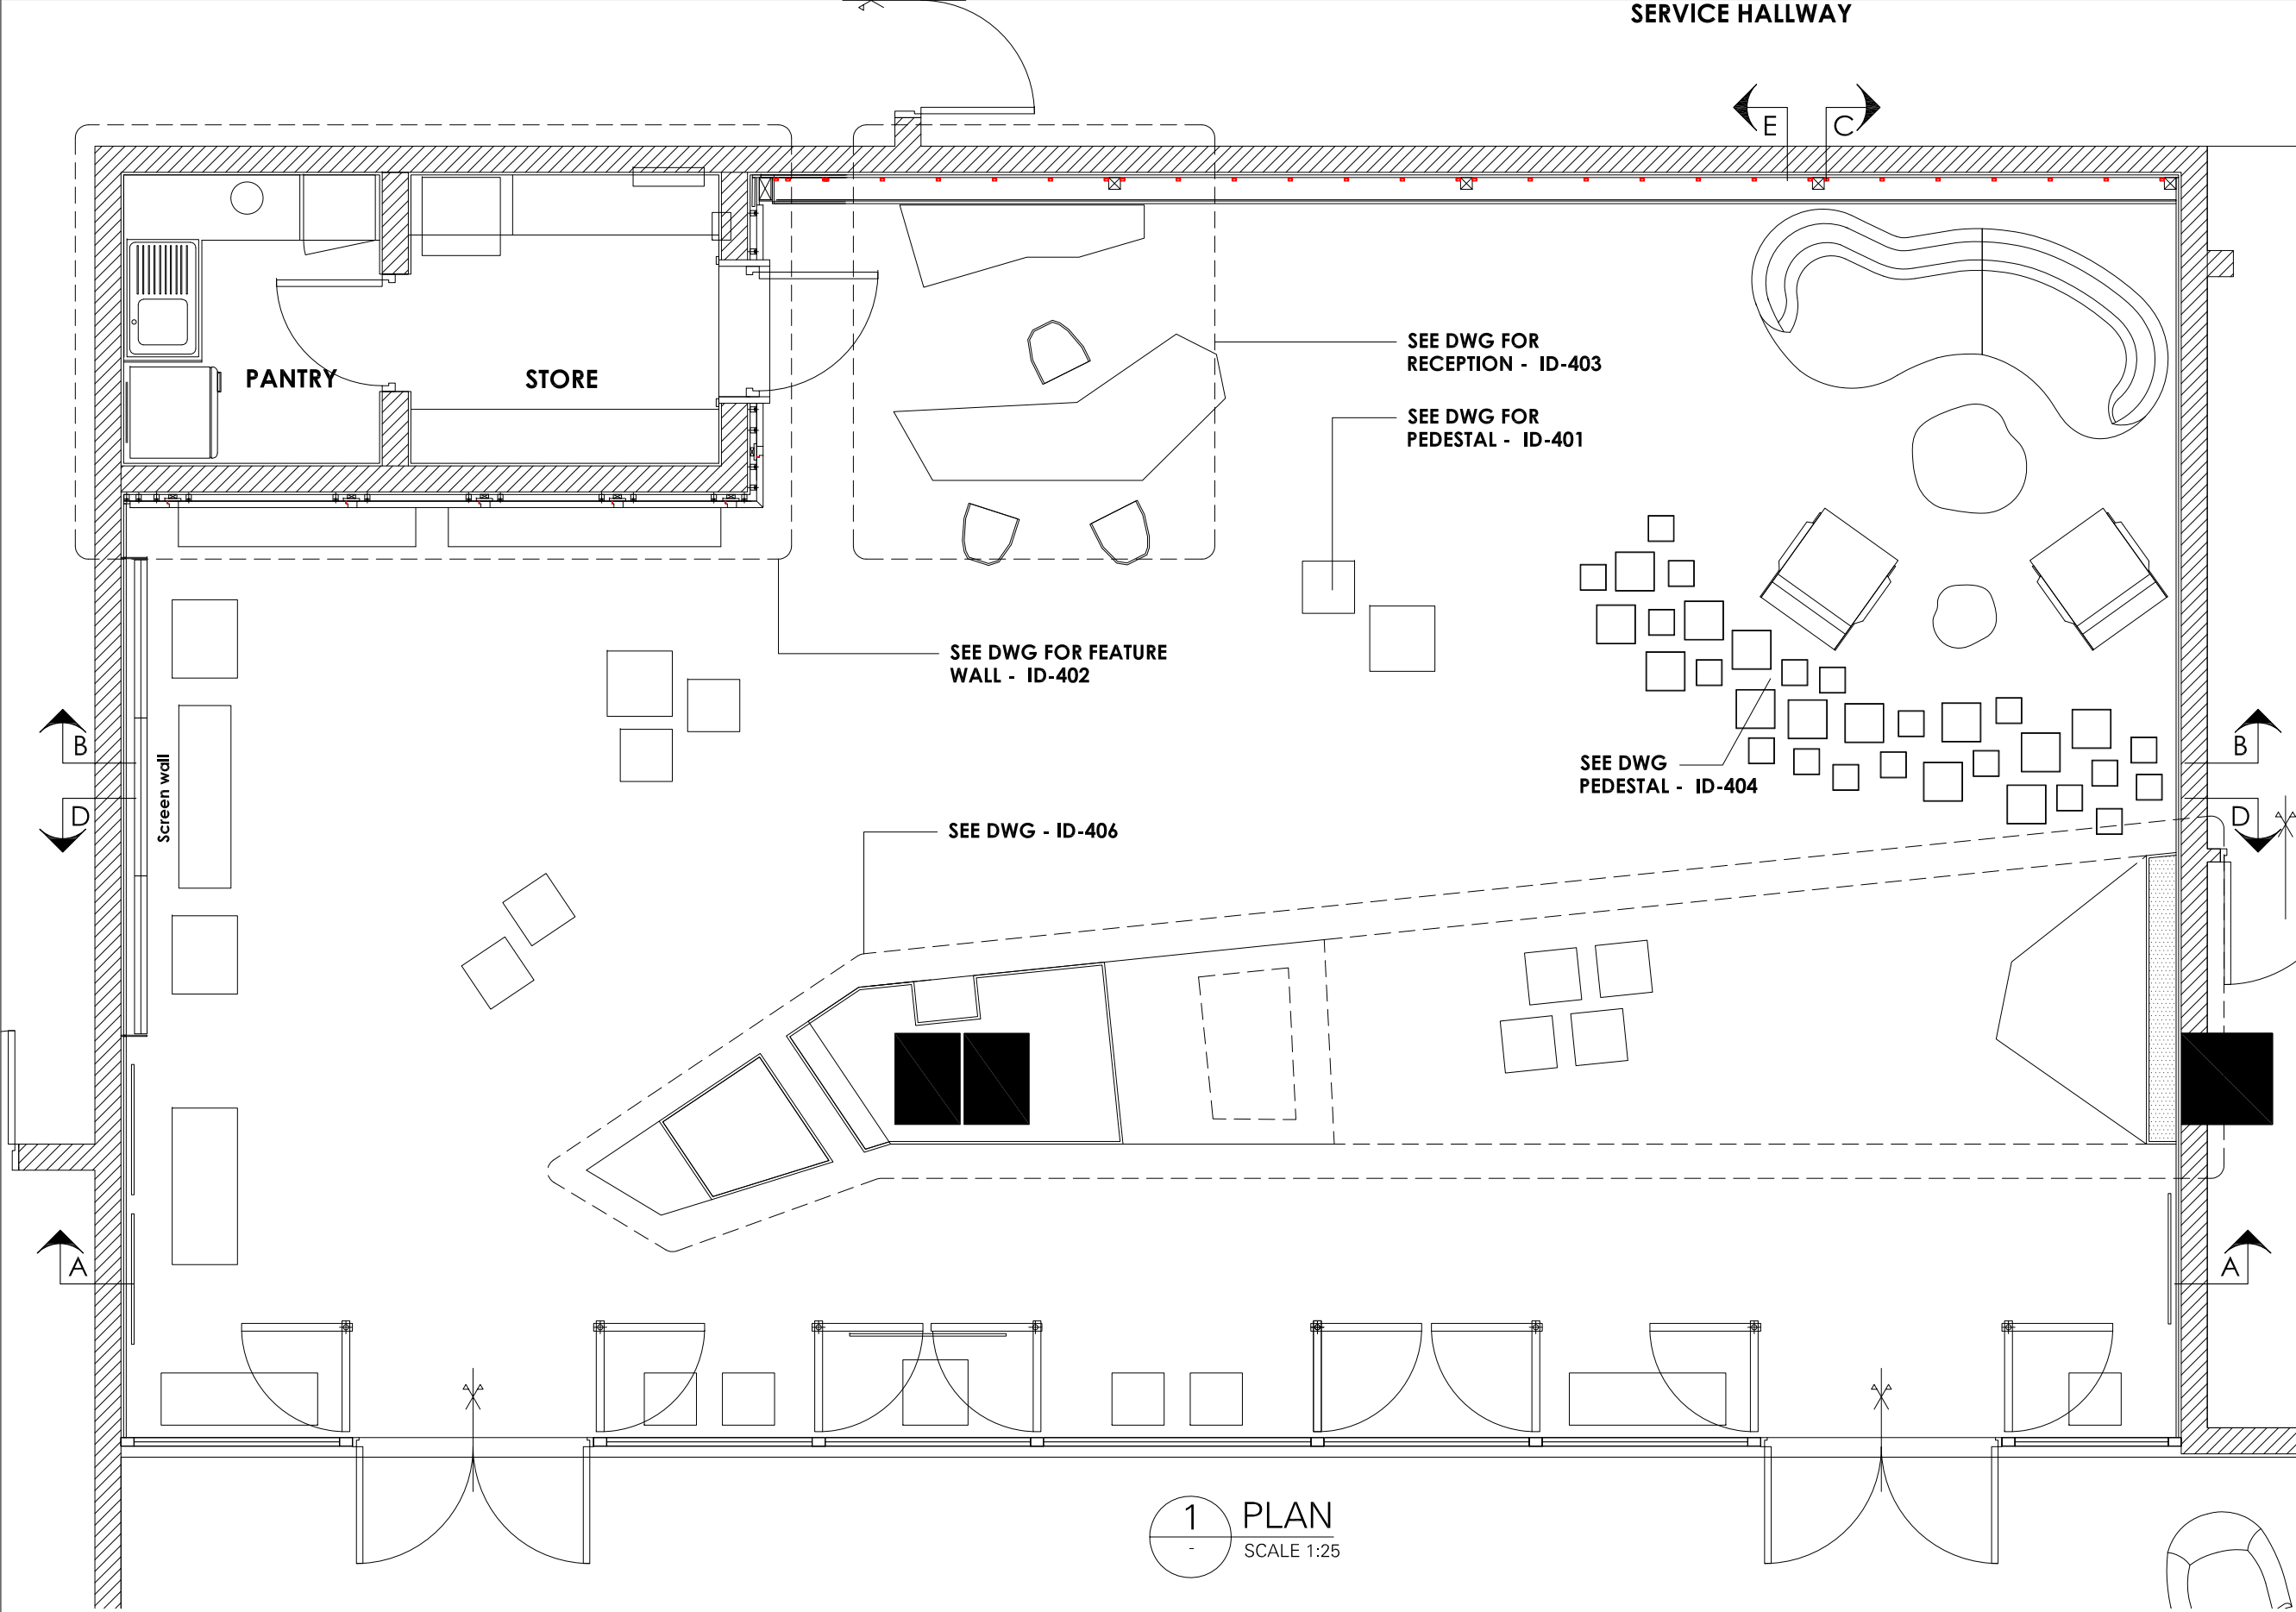

GENERAL NOTES

1. This drawing shall be read in conjunction with all other relevant architectural, structural & electrical drawings including those of other consultants.

2. It is the responsibility of contractors & manufacturers to check all relevant site dimensions prior to the start of construction or manufacture.

3. All materials and components must be installed on site in accordance with manufacturer's instructions, shop drawings and standard details.

4. All dimensions are in millimeters unless noted otherwise.

5. Full working drawings, specifications and samples are to be provided by Contractor/Supplier for approval prior to manufacture.

KEY PLAN

INITIAL ISSUE

MP

AM

SM

2022.11.09

REV.#

GENERAL NOTES

DRAWN BY

CHECKED BY

APPROVED BY

DATE

PROJECT TITLE

REFERENCE

RIC - RIYADH

RIC01
G

DRAWING TITLE

GENERAL LAYOUT

DRAWING NUMBER

REVISION

A-101

SCALE

FORMAT

ADDITIONAL

DESIGN DEVELOPMENT

1:25

A1

NOTES


SIMA MALAK + ALSSAMOURE
DESIGN ASSOCIATES

P.O. Box 15707 - Riyadh 11454 KSA
Tel. 01 441 4963 - Fax. 01 441 3867
simals@simals.com


©SIMA MALAK + ALSSAMOURE DESIGN ASSOCIATES (شركة) 2003
This document including all drawing and text is the property and copyright of SIMA MALAK + ALSSAMOURE DESIGN ASSOCIATES for use solely with respect to this Project and shall not be copied or reproduced by any means except by agreement in writing from SIMA MALAK + ALSSAMOURE DESIGN ASSOCIATES.



©SIMA MALAK + ALSSAMOURÉ DESIGN ASSOCIATES (مسا) 2003
This document including all drawing and text is the property and
copyright of SIMA MALAK + ALSSAMOURÉ DESIGN ASSOCIATES for
use solely with respect to this Project and shall not be copied or
reproduced by any means except by agreement in writing from
SIMA MALAK + ALSSAMOURÉ DESIGN ASSOCIATES.

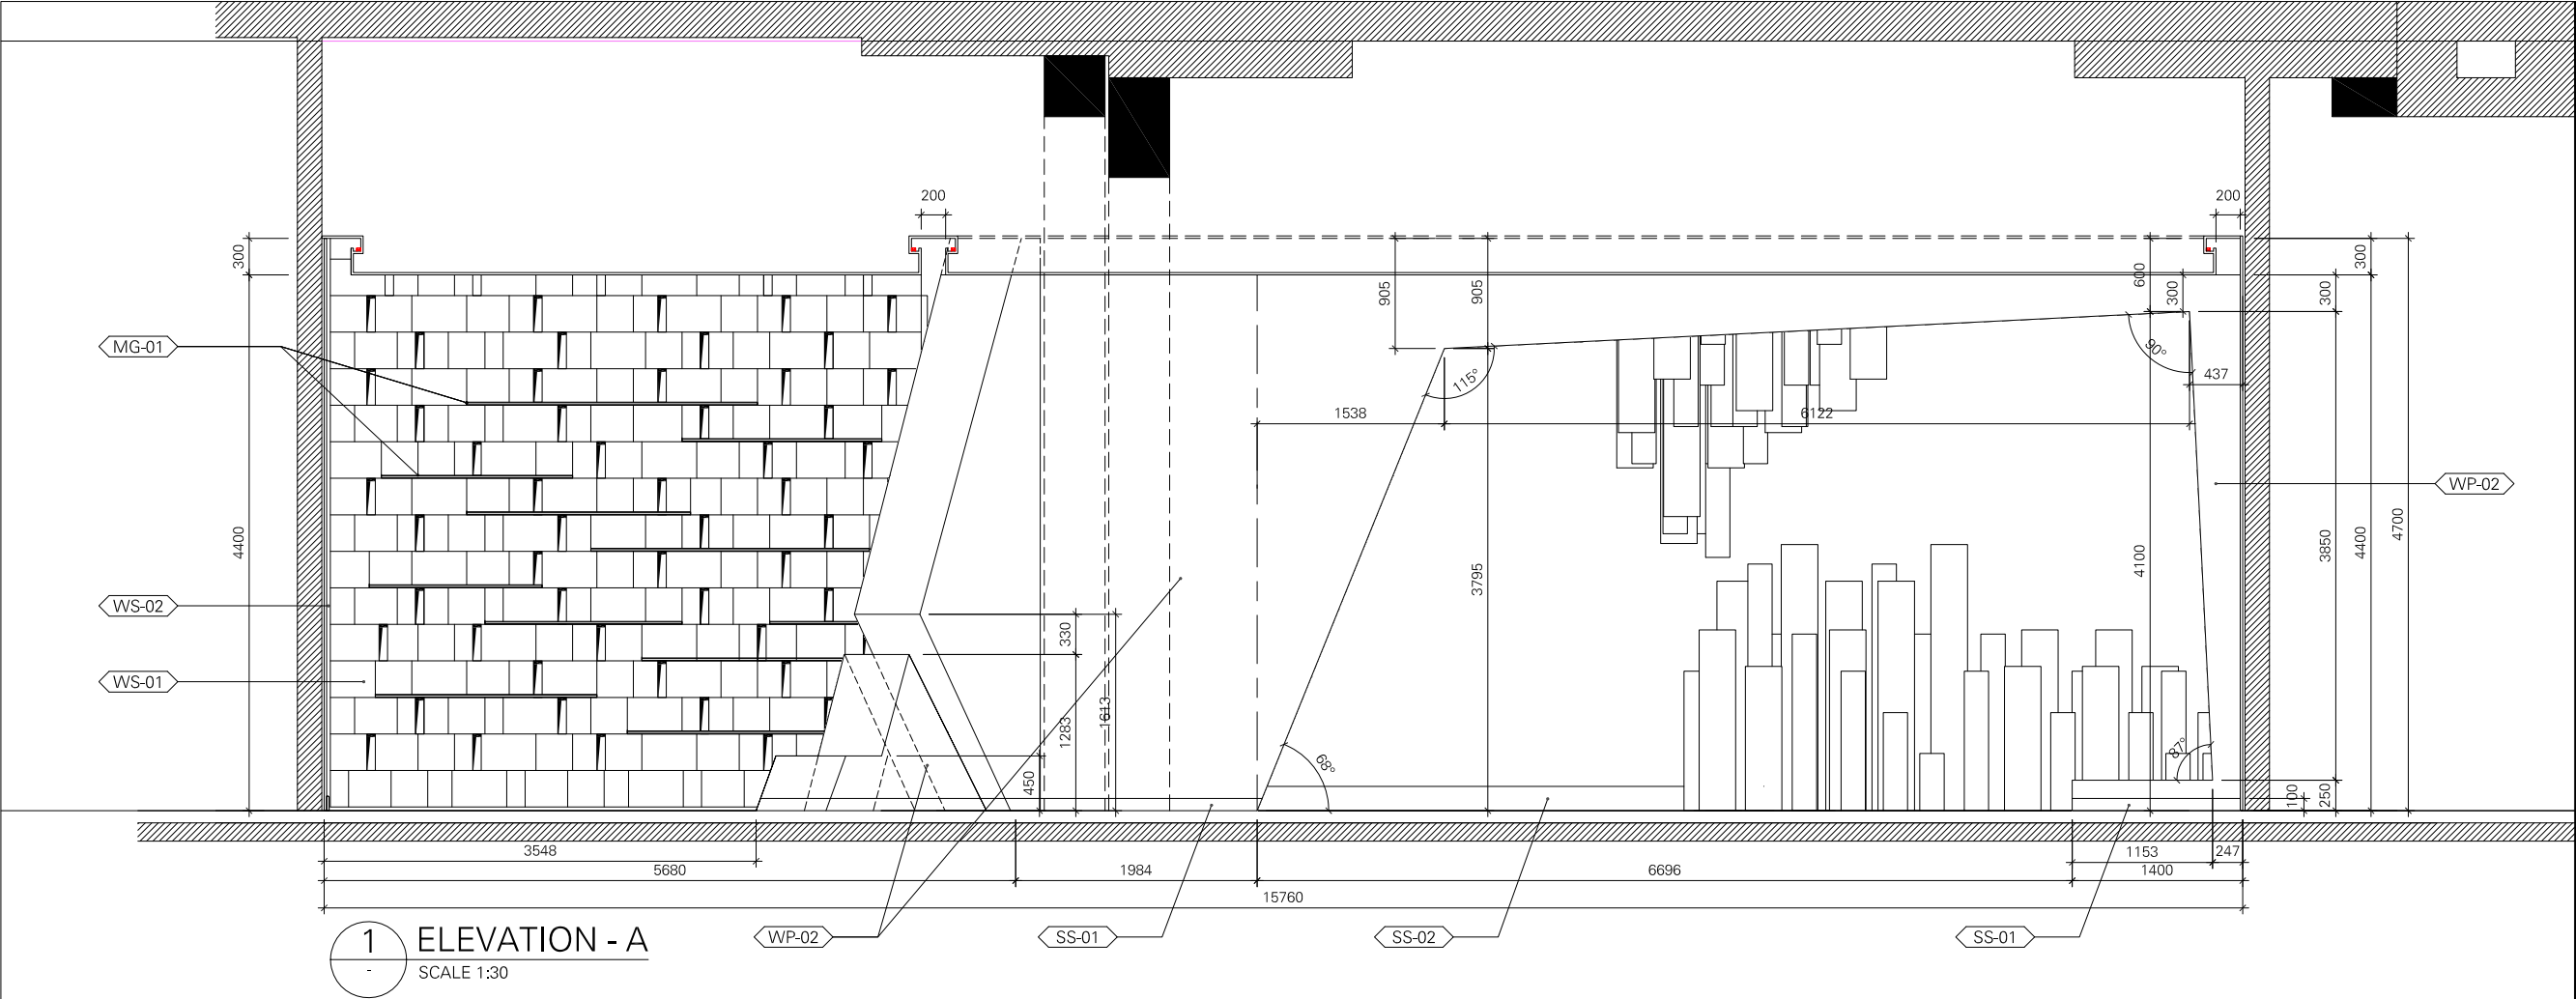

1 ELEVATION - A
SCALE 1:30

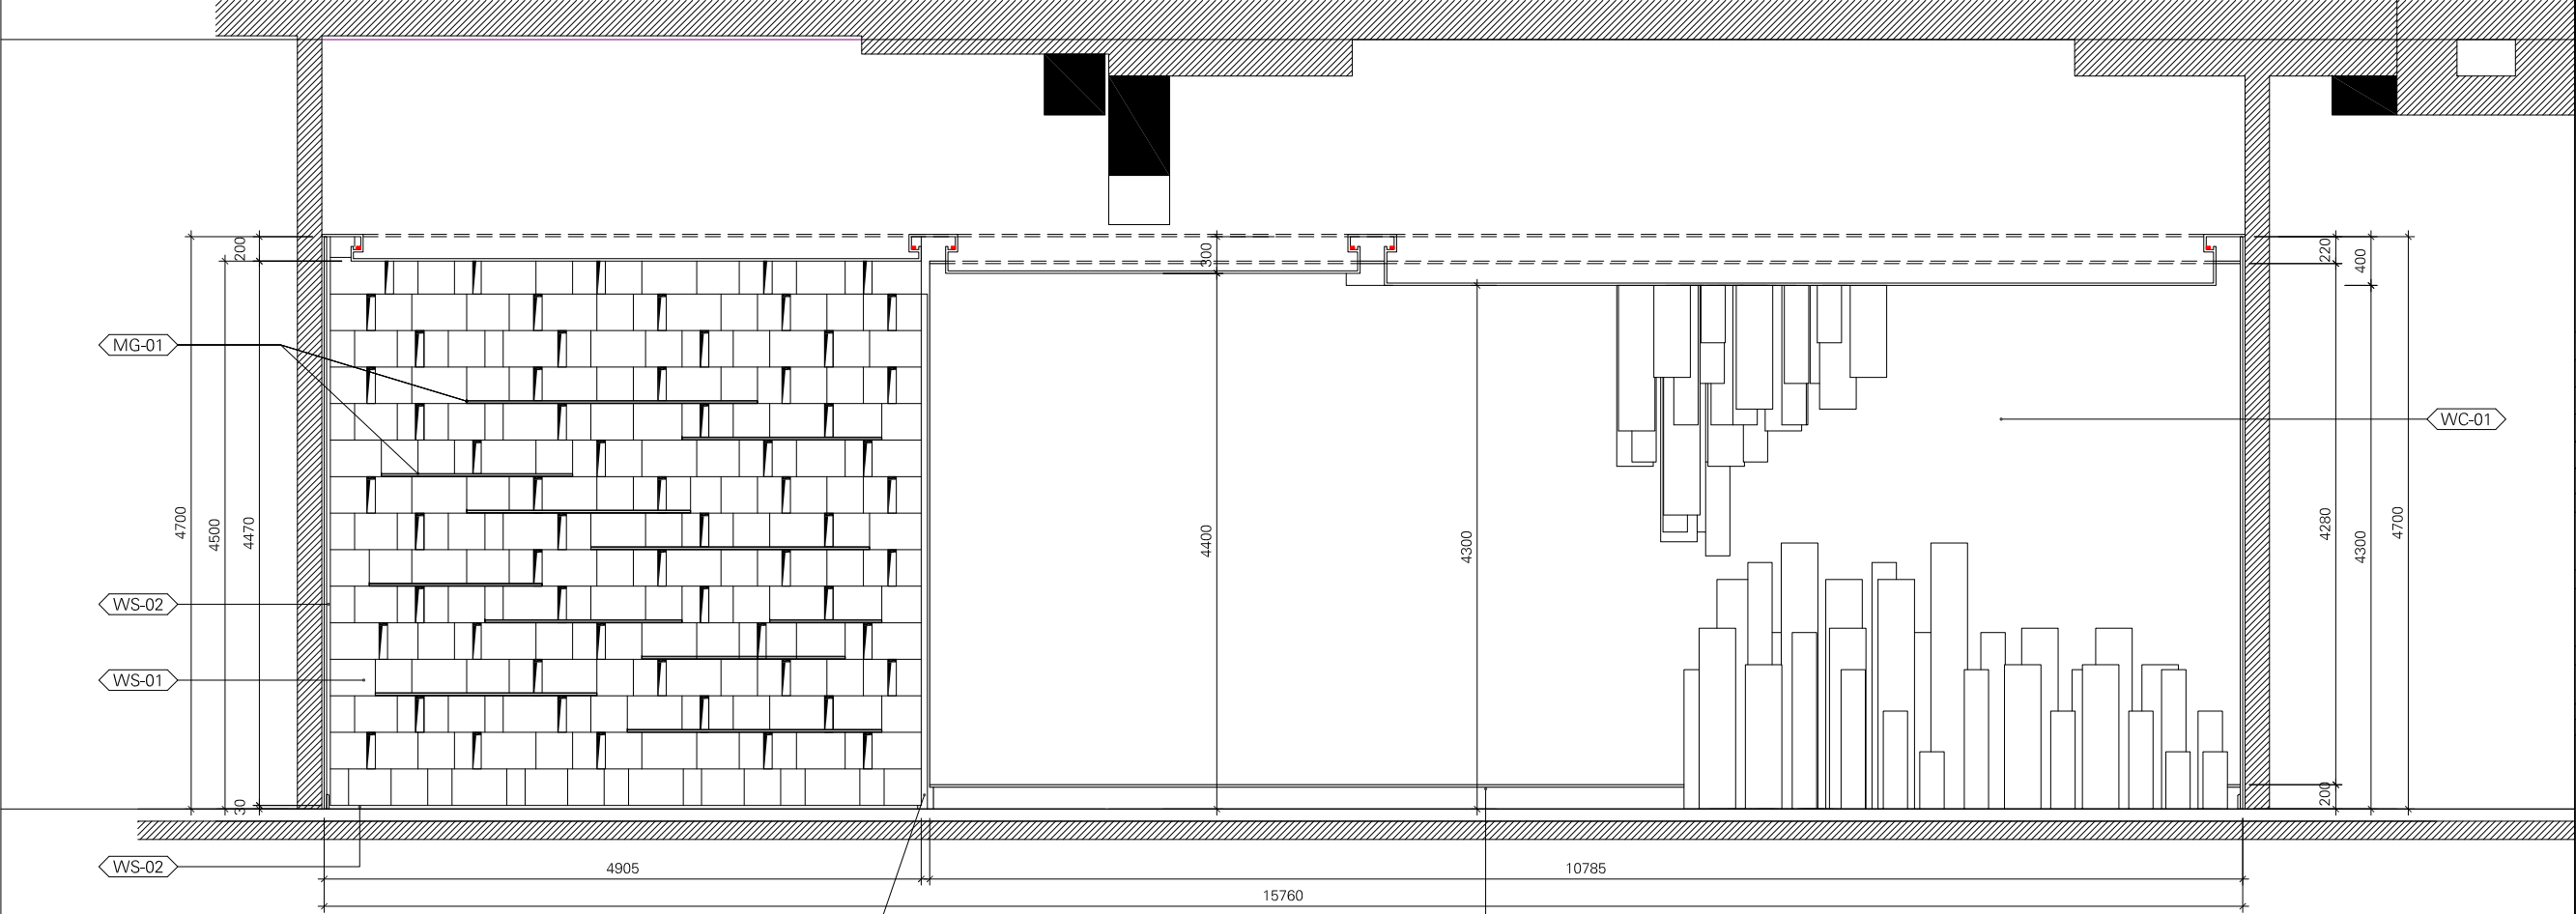

2 ELEVATION - B
SCALE 1:30

GENERAL NOTES

1. This drawing shall be read in conjunction with all other relevant architectural, structural & electrical drawings including those of other consultants.
2. It is the responsibility of contractors & manufacturers to check all relevant site dimensions prior to the start of construction or manufacture.
3. All materials and components must be installed on site in accordance with manufacturer's instructions, shop drawings and standard details.
4. All dimensions are in millimeters unless noted otherwise.
5. Full working drawings, specifications and samples are to be provided by Contractor/Supplier for approval prior to manufacture.

KEY PLAN

REV.#	GENERAL NOTES	DRAWN BY	CHECKED BY	APPROVED BY	DATE
A	GENERAL REV.	MP	AM	SM	2022.11.27
X	INITIAL ISSUE	AC	AM	SM	2022.11.14

PROJECT TITLE: RIC - RIYADH
REFERENCE: RIC01 G


DRAWING TITLE: ELEVATION-A AND ELEVATION-B

DRAWING NUMBER: A-103
REVISION: A


SCALE: 1:30
FORMAT: A1
ADDITIONAL NOTES: DESIGN DEVELOPMENT

SIMA MALAK + ALSSAMOURE DESIGN ASSOCIATES
P.O. Box 15707 - Riyadh 11454 KSA
Tel. 01 441 4963 - Fax. 01 441 3867
simals@simals.com

©SIMA MALAK + ALSSAMOURE DESIGN ASSOCIATES (شركة) 2003
This document including all drawing and text is the property and copyright of SIMA MALAK + ALSSAMOURE DESIGN ASSOCIATES for use solely with respect to this Project and shall not be copied or reproduced by any means except by agreement in writing from SIMA MALAK + ALSSAMOURE DESIGN ASSOCIATES.

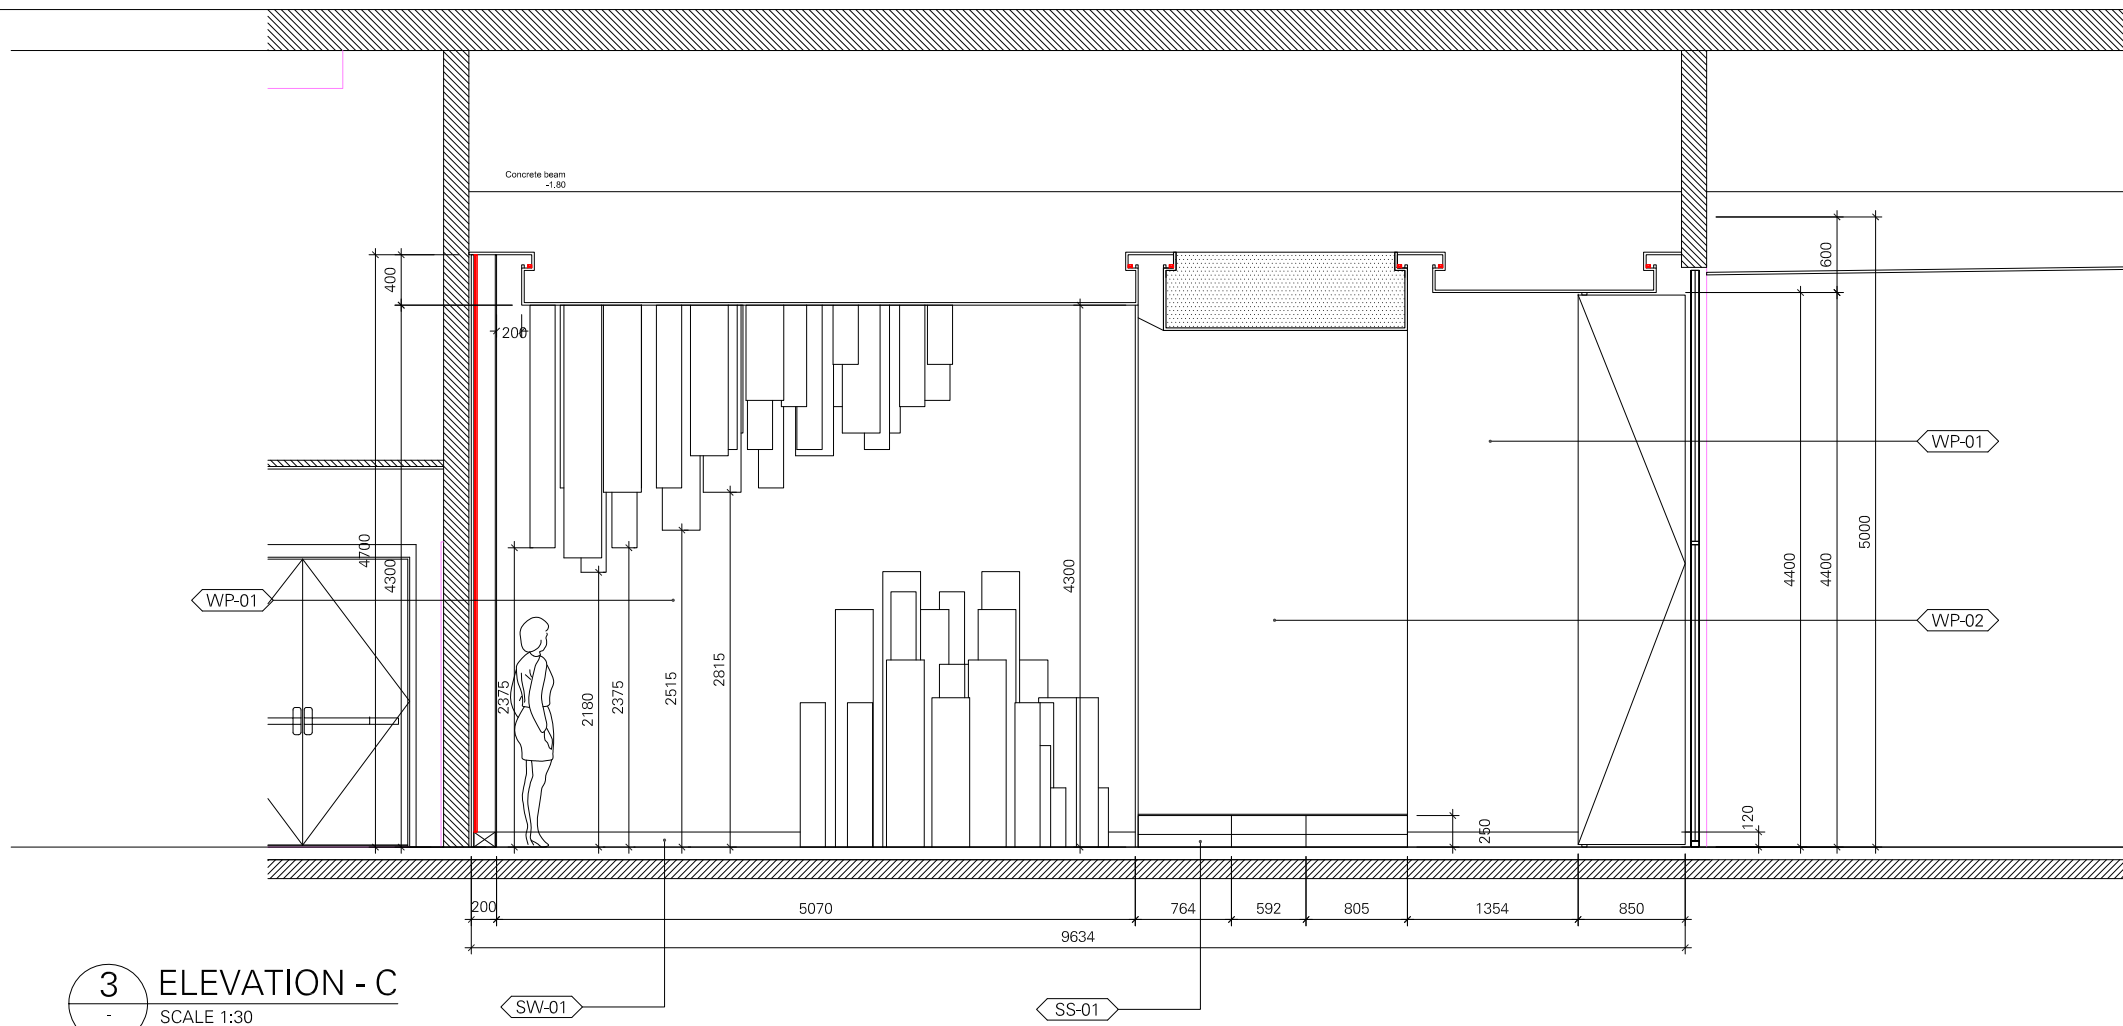

3 ELEVATION - C
SCALE 1:30

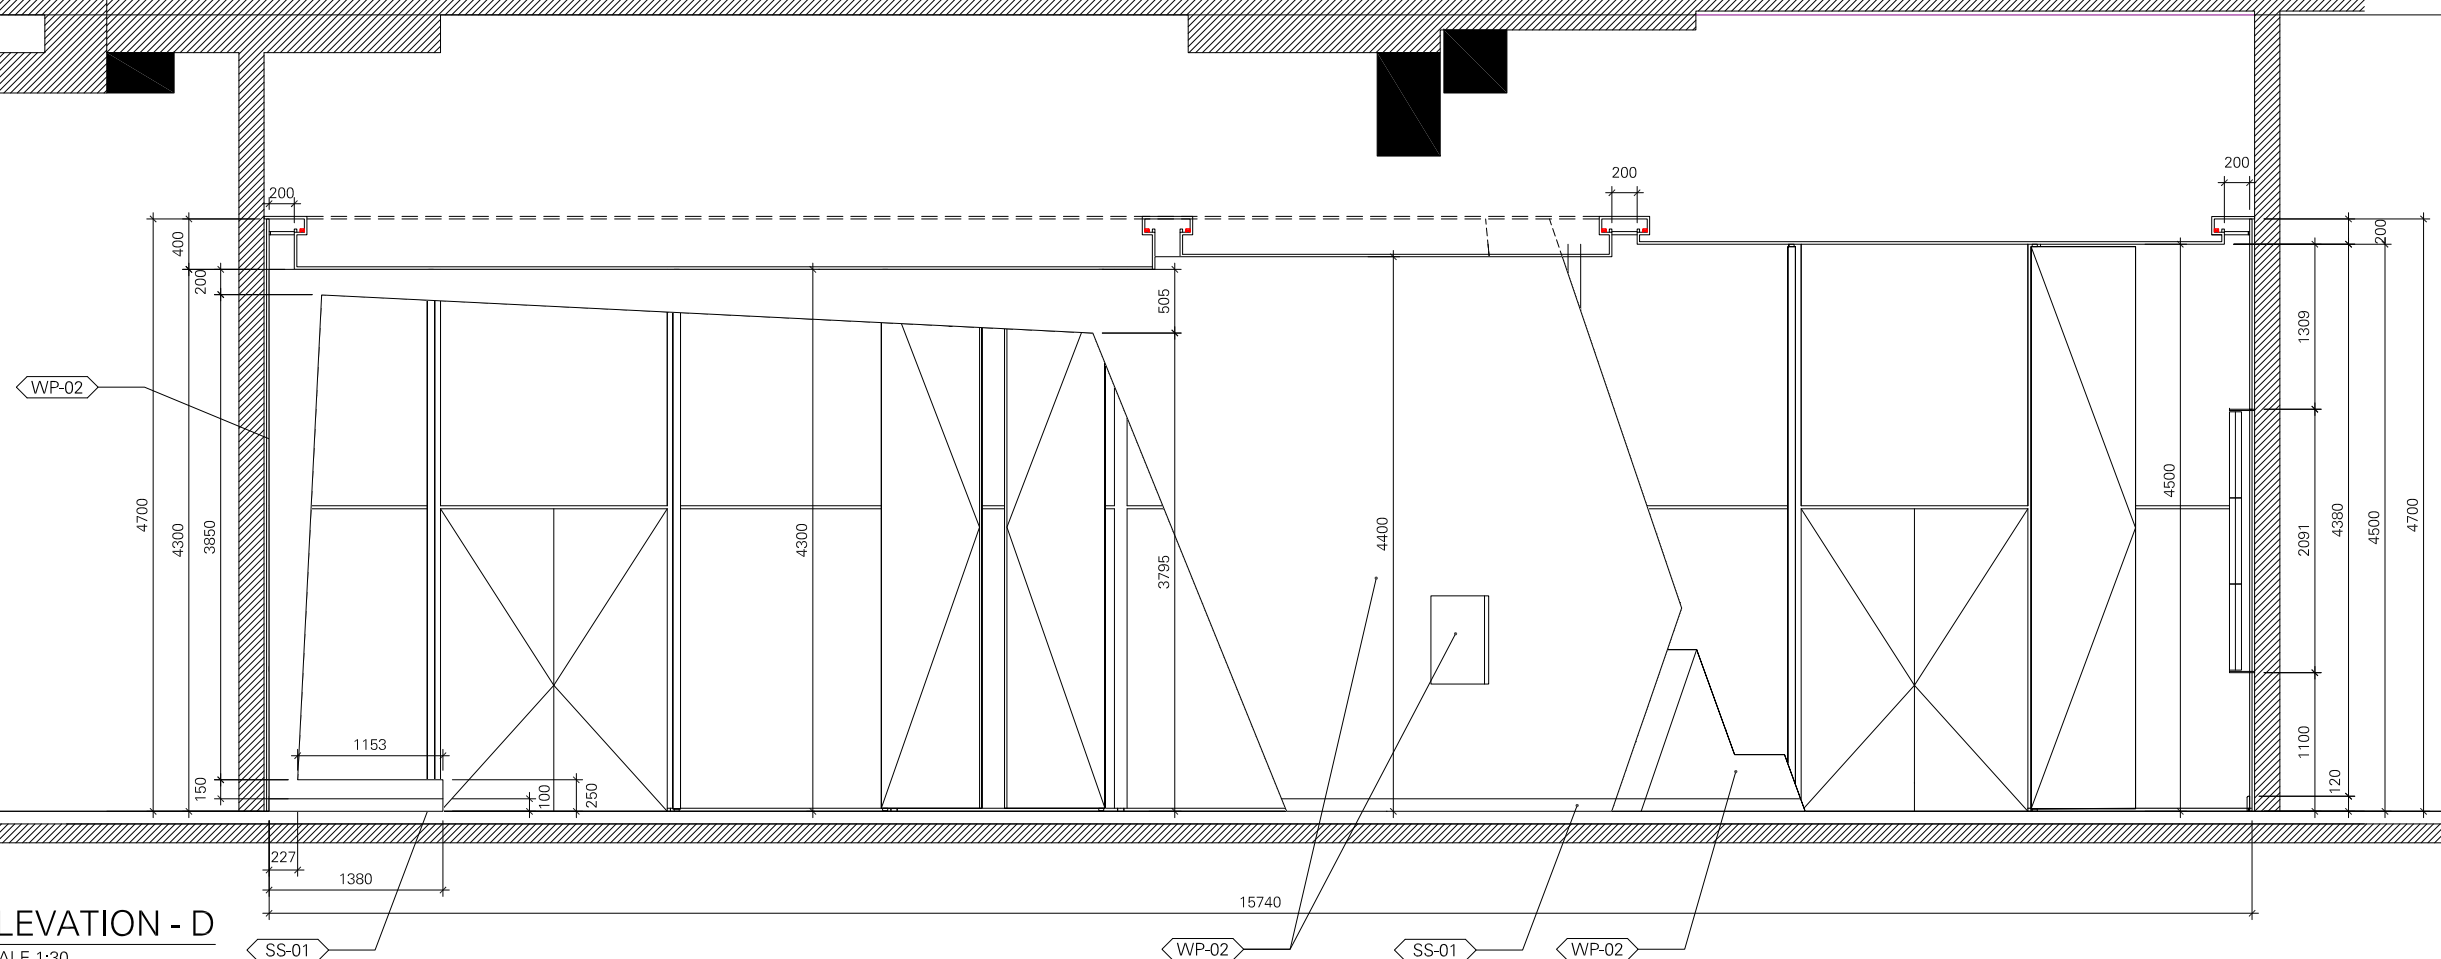

4 ELEVATION - D
SCALE 1:30

GENERAL NOTES

1. This drawing shall be read in conjunction with all other relevant architectural, structural & electrical drawings including those of other consultants.
2. It is the responsibility of contractors & manufacturers to check all relevant site dimensions prior to the start of construction or manufacture.
3. All materials and components must be installed on site in accordance with manufacturer's instructions, shop drawings and standard details.
4. All dimensions are in millimeters unless noted otherwise.
5. Full working drawings, specifications and samples are to be provided by Contractor/Supplier for approval prior to manufacture.

KEY PLAN

A	GENERAL REV.	MP	AM	SM	2022.11.27
X	INITIAL ISSUE	AC	AM	SM	2022.11.14
REV.#	GENERAL NOTES	DRAWN BY	CHECKED BY	APPROVED BY	DATE
PROJECT TITLE					REFERENCE
RIC - RIYADH					RIC01 G

DRAWING TITLE

ELEVATION-C AND ELEVATION-D

DRAWING NUMBER

A-104

REVISION

A

SCALE 1:30


FORMAT AT

ADDITIONAL NOTES

DESIGN DEVELOPMENT

SIMA MALAK + ALSSAMOURE
DESIGN ASSOCIATES
P.O. Box 15707 - Riyadh 11454 KSA
Tel. 01 441 4963 - Fax. 01 441 3867
simals@simals.com

©SIMA MALAK + ALSSAMOURE DESIGN ASSOCIATES (شركة) 2003
This document including all drawing and text is the property and
copyright of SIMA MALAK + ALSSAMOURE DESIGN ASSOCIATES for
use solely with respect to this Project and shall not be copied or
reproduced by any means except by agreement in writing from
SIMA MALAK + ALSSAMOURE DESIGN ASSOCIATES.

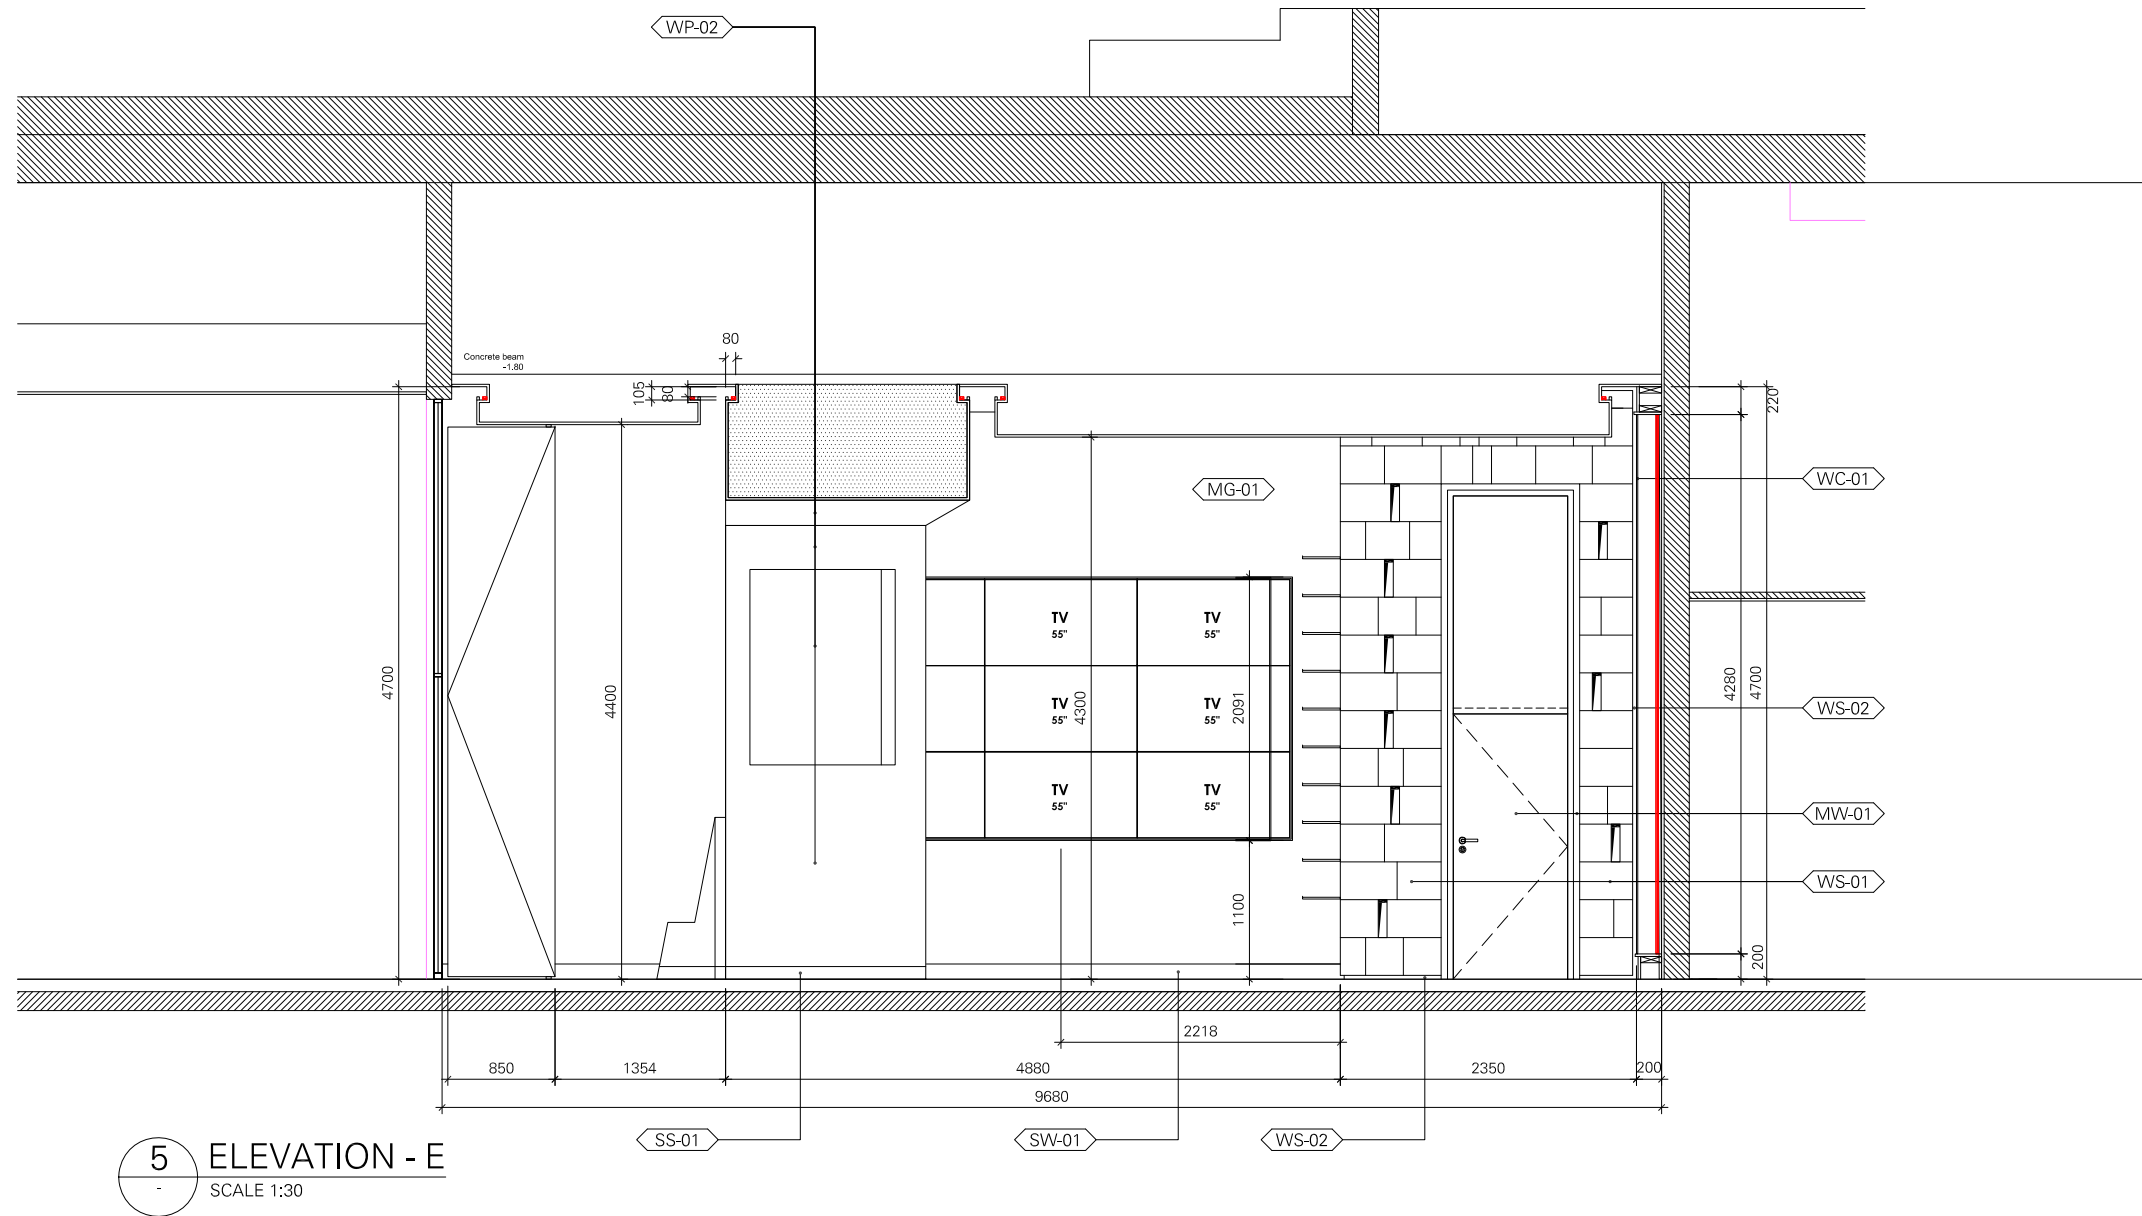

5 ELEVATION - E
SCALE 1:30

GENERAL NOTES


1. This drawing shall be read in conjunction with all other relevant architectural, structural & electrical drawings including those of other consultants.
2. It is the responsibility of contractors & manufacturers to check all relevant site dimensions prior to the start of construction or manufacture.
3. All materials and components must be installed on site in accordance with manufacturer's instructions, shop drawings and standard details.
4. All dimensions are in millimeters unless noted otherwise.
5. Full working drawings, specifications and samples are to be provided by Contractor/Supplier for approval prior to manufacture.

KEY PLAN

A	GENERAL REV.	MP	AM	SM	2022.11.27
X	INITIAL ISSUE	AC	AM	SM	2022.11.14
REV.#	GENERAL NOTES	DRAWN BY	CHECKED BY	APPROVED BY	DATE
PROJECT TITLE				REFERENCE	
RIC - RIYADH				RIC01 G	

DRAWING TITLE			
ELEVATION-E			
DRAWING NUMBER			REVISION
A-105			A
SCALE	FORMAT	ADDITIONAL NOTES	DESIGN DEVELOPMENT
1:30	A1		
SIMA MALAK + ALSSAMOURE DESIGN ASSOCIATES			
P.O. Box 15707 - Riyadh 11454 KSA Tel. 01 441 4963 - Fax. 01 441 3867 simals@simals.com			

©SIMA MALAK + ALSSAMOURE DESIGN ASSOCIATES (شركة) 2003
This document including all drawing and text is the property and copyright of SIMA MALAK + ALSSAMOURE DESIGN ASSOCIATES for use solely with respect to this Project and shall not be copied or reproduced by any means except by agreement in writing from SIMA MALAK + ALSSAMOURE DESIGN ASSOCIATES.

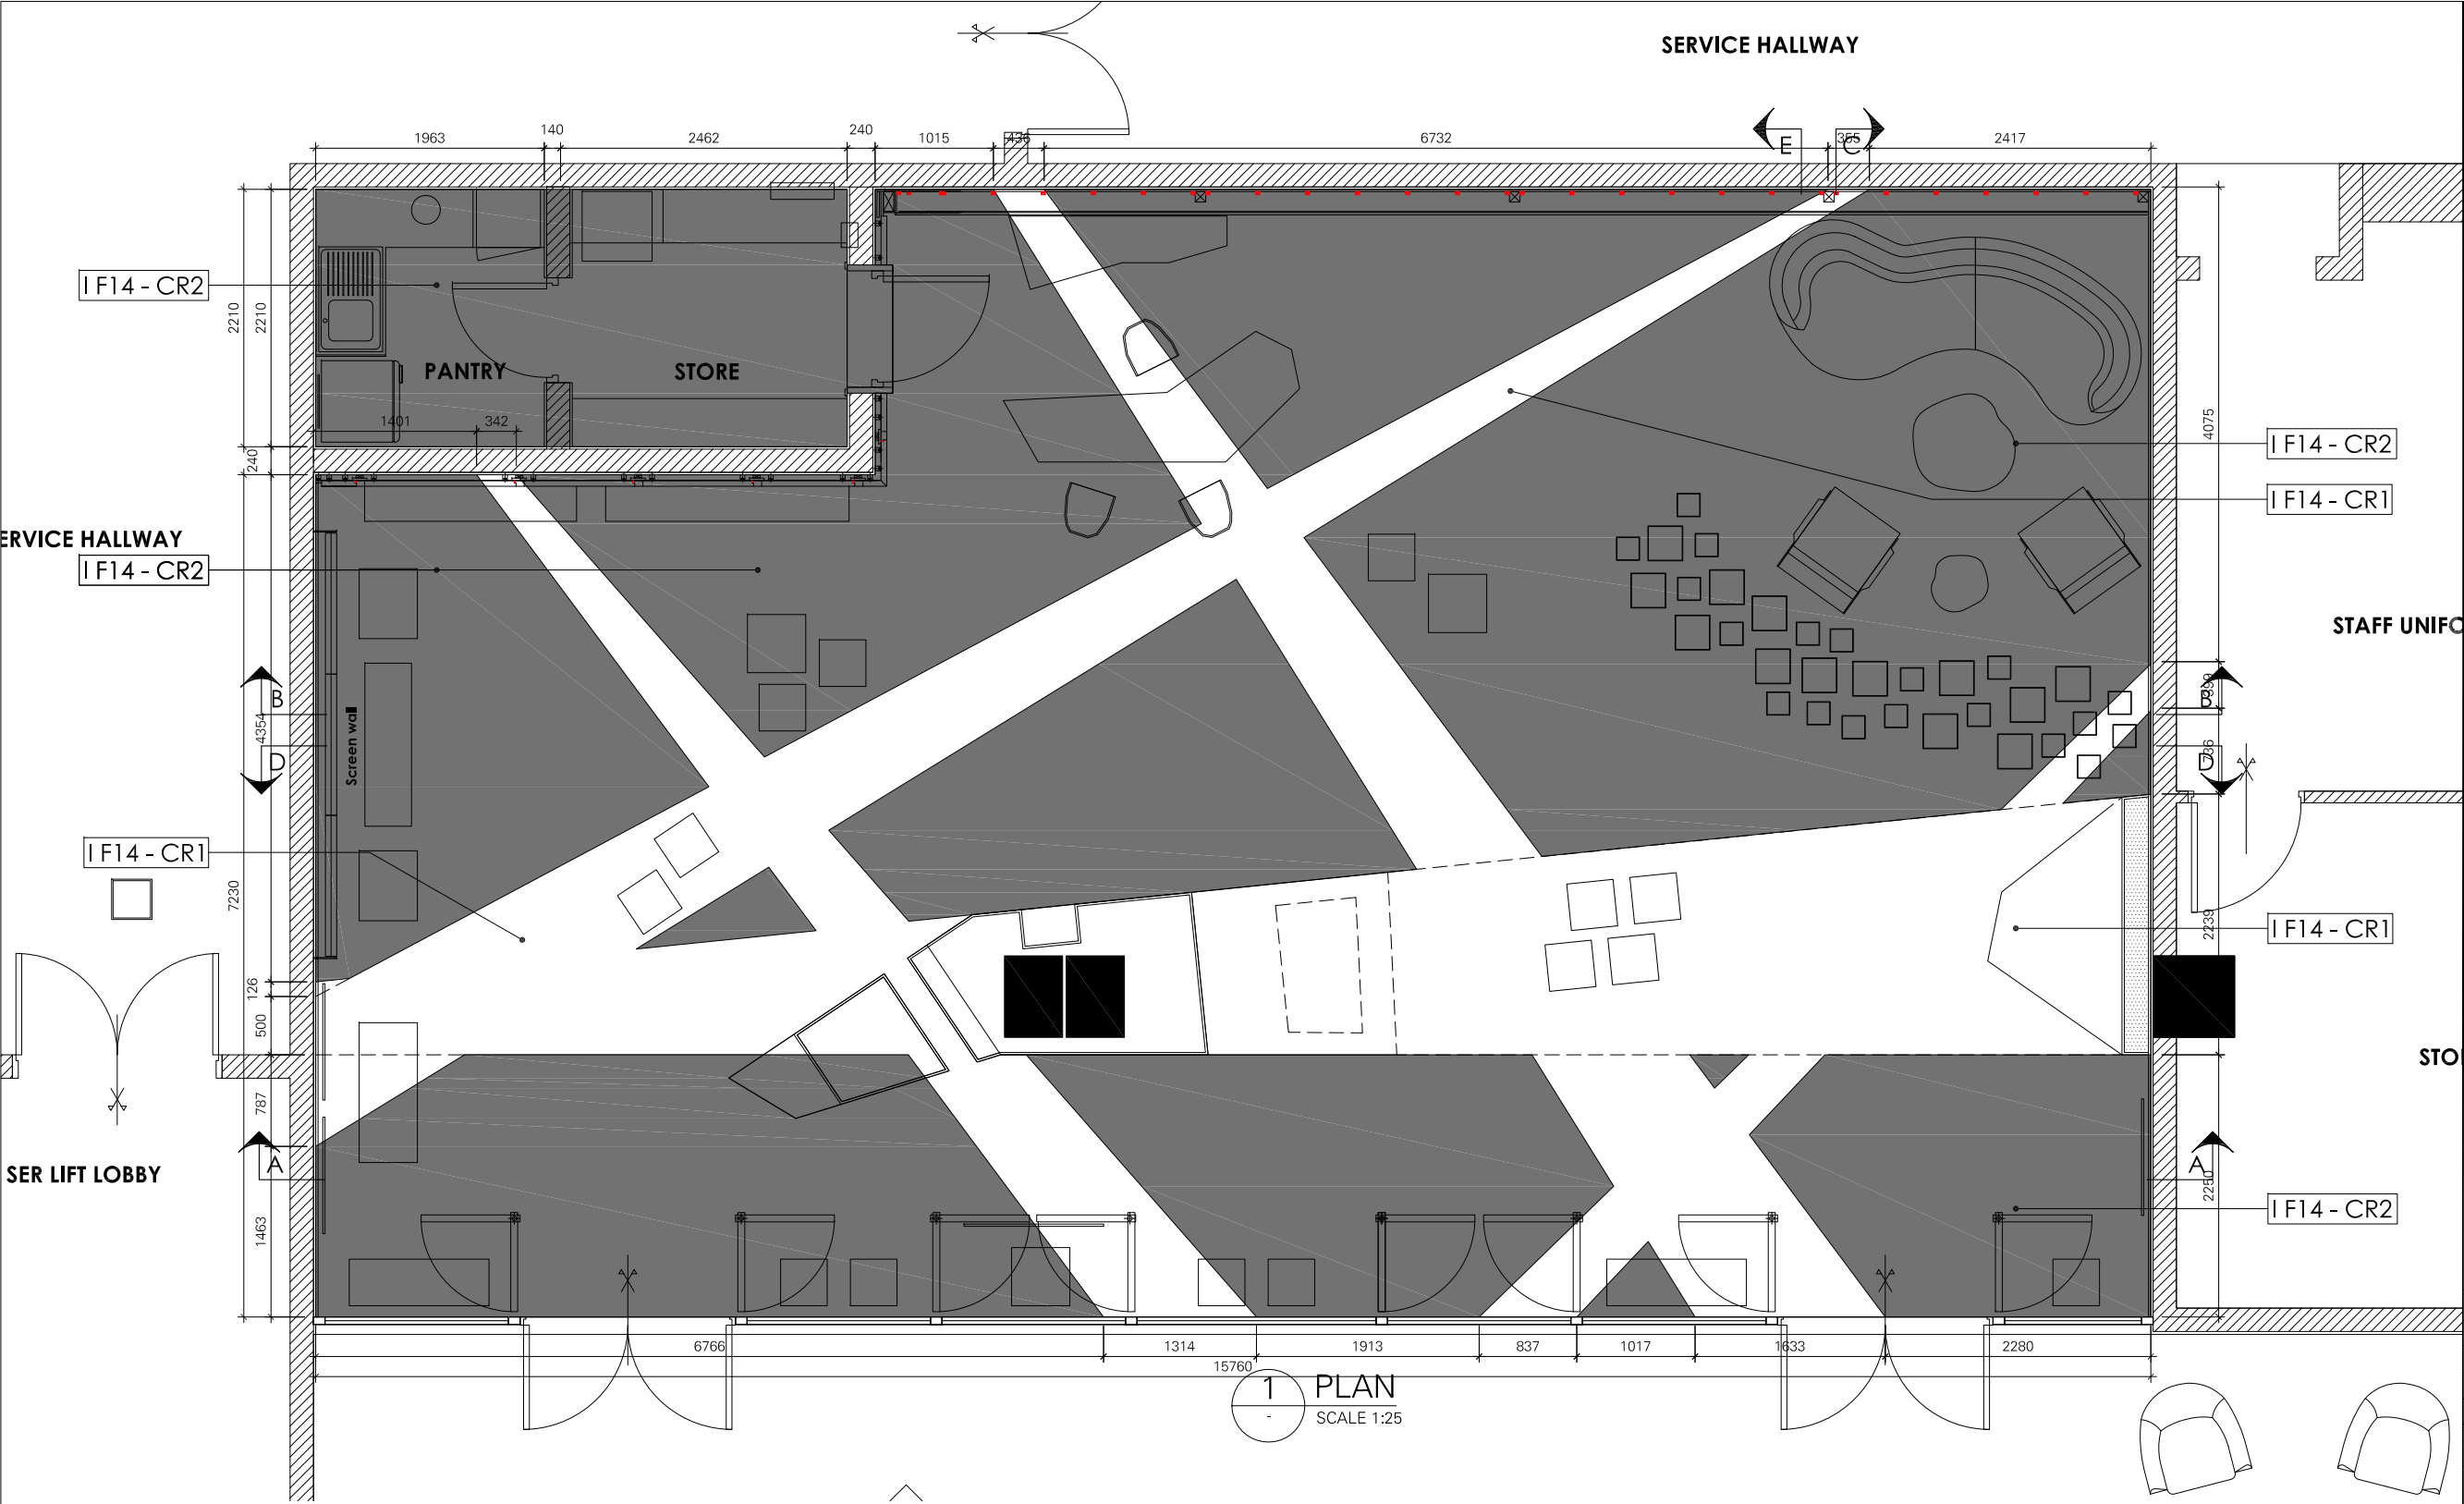

GENERAL NOTES

1. This drawing shall be read in conjunction with all other relevant architectural, structural & electrical drawings including those of other consultants.
2. It is the responsibility of contractors & manufacturers to check all relevant site dimensions prior to the start of construction or manufacture.
3. All materials and components must be installed on site in accordance with manufacturer's instructions, shop drawings and standard details.
4. All dimensions are in millimeters unless noted otherwise.
5. Full working drawings, specifications and samples are to be provided by Contractor/Supplier for approval prior to manufacture.

KEY PLAN

STO

A	FLOOR HATCH ADDED	CAD	AM	SM	2022.11.17
X	INITIAL ISSUE	AC	AM	SM	2022.11.10
REV.#	GENERAL NOTES	DRAWN BY	CHECKED BY	APPROVED BY	DATE
PROJECT TITLE					REFERENCE
RIC - RIYADH					RIC01
					G

DRAWING TITLE

FLOORING LAYOUT





DRAWING NUMBER				REVISION
ID-101				A
SCALE	FORMAT	ADDITIONAL NOTES	DESIGN DEVELOPMENT	
1:30	A1			

**SIMA MALAK + ALSSAMOURE
DESIGN ASSOCIATES**
P.O. Box 15707 - Riyadh 11454 KSA
Tel. 01 441 4963 - Fax. 01 441 3867
simals@simals.com

©SIMA MALAK + ALSSAMOURE DESIGN ASSOCIATES (شركة) 2003
This document including all drawing and text is the property and copyright of SIMA MALAK + ALSSAMOURE DESIGN ASSOCIATES for use solely with respect to this Project and shall not be copied or reproduced by any means except by agreement in writing from SIMA MALAK + ALSSAMOURE DESIGN ASSOCIATES.

NOTES

- I F14 - CR1 - TINTED CONCRETE. LIGHT GREY.
- I F14 - CR2 - TINTED CONCRETE. DARK GREY.
- SAMPLES TO BE PROVIDED FOR REVIEW / APPROVAL.
- PATTERN TO BE SET OUT ON SITE AND APPROVED BEFORE PROCEEDING WITH THE WORKS.

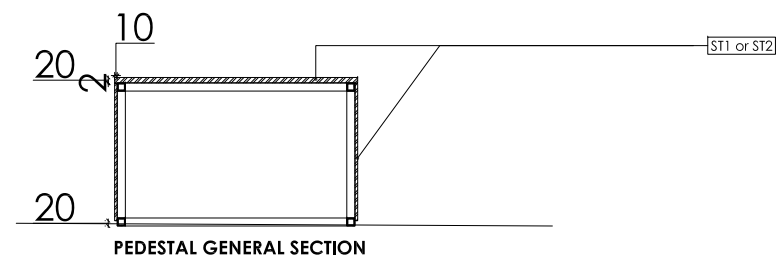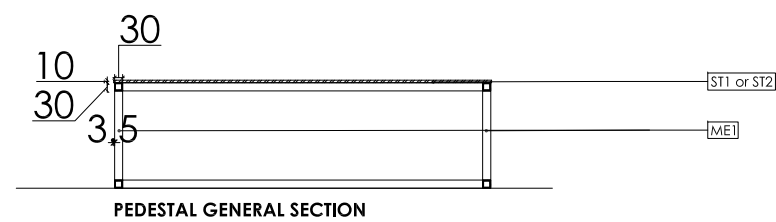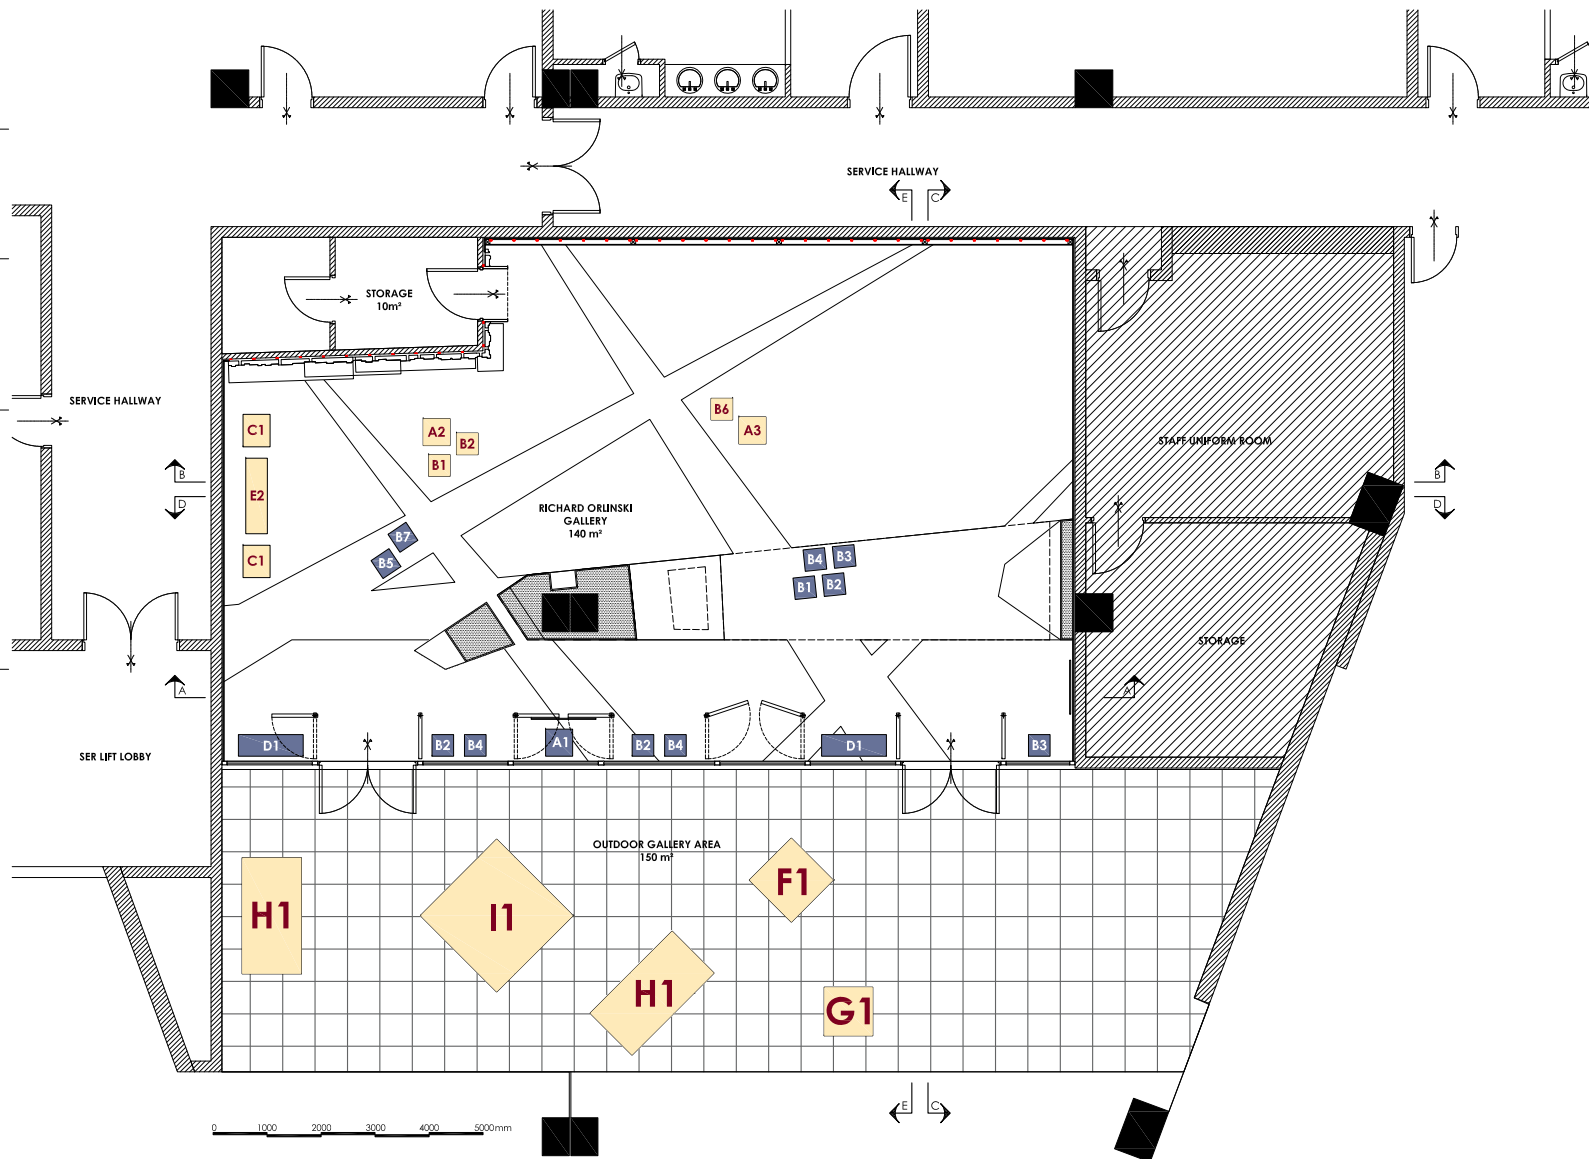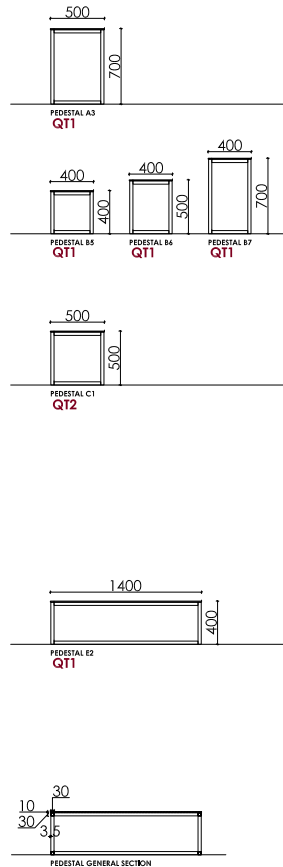

GENERAL NOTES

1. This drawing shall be read in conjunction with all other relevant architectural, structural & electrical drawings including those of other consultants.
2. It is the responsibility of contractors & manufacturers to check all relevant site dimensions prior to the start of construction or manufacture.
3. All materials and components must be installed on site in accordance with manufacturer's instructions , shop drawings and standard details.
4. All dimensions are in millimeters unless noted otherwise.
5. Full working drawings, specifications and samples are to be provided by Contractor/Supplier for approval prior to manufacture.

KEY PLAN

X	INITIAL ISSUE	CAD	AM	SM	2022.10.23	
REV.#	GENERAL NOTES	DRAWN BY	CHECKED BY	APPROVED BY	DATE	
PROJECT TITLE						REFERENCE
RIC - RIYADH						RIC01
						G






PEDESTALS DETAILS

DRAWING NUMBER			REVISION
ID-401			-
SCALE	FORMAT	ADDITIONAL NOTES	DESIGN DEVELOPMENT
1:50	A1		



SIMALAK + ALSSAMOURÉ
DESIGN ASSOCIATES
P.O. Box 15707 - Riyadh 11454 KSA
Tel. 01 441 4963 - Fax. 01 441 3867
simals@simals.com

©SIMA MALAK + ALSSAMOURÉ DESIGN ASSOCIATES (بـ) 2003
This document including all drawing and text is the property and
copyright of SIMA MALAK + ALSSAMOURÉ DESIGN ASSOCIATES for
use solely with respect to this Project and shall not be copied or
reproduced by any means except by agreement in writing from
SIMA MALAK + ALSSAMOURÉ DESIGN ASSOCIATES.

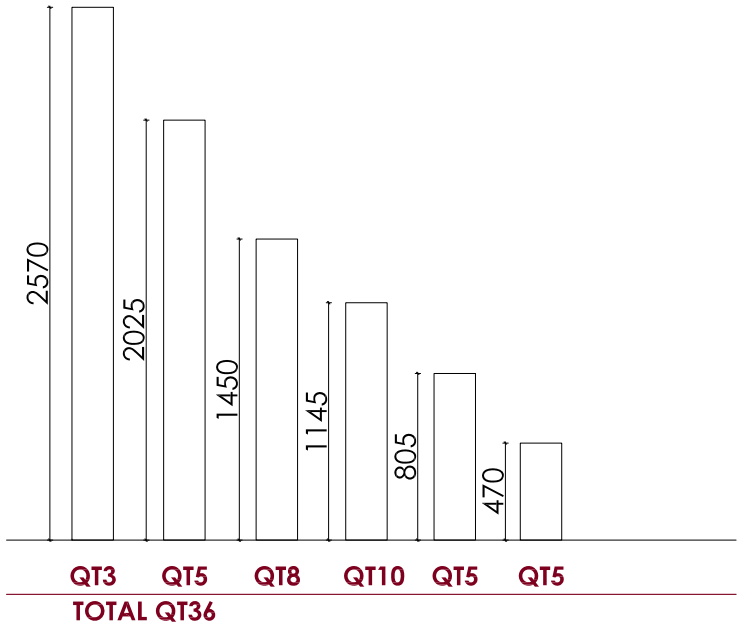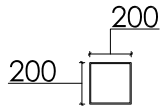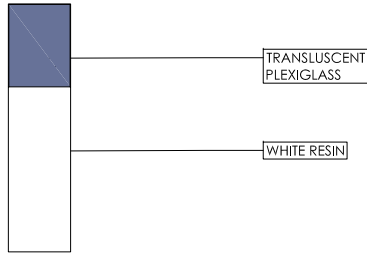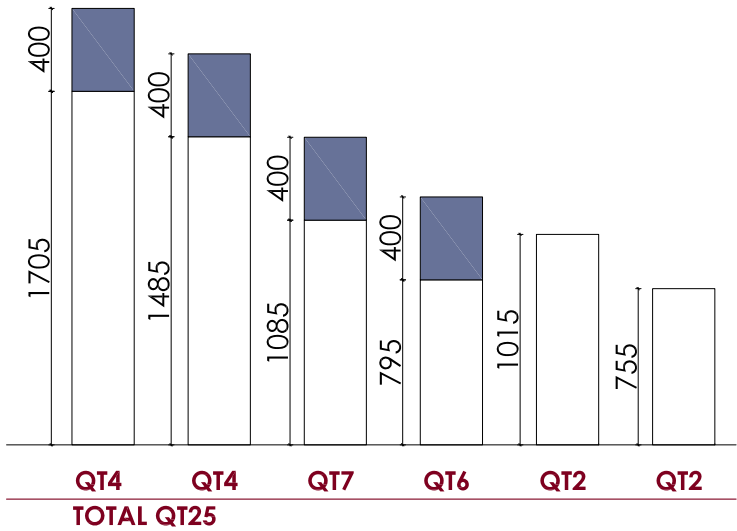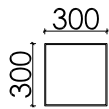

GENERAL NOTES

1. This drawing shall be read in conjunction with all other relevant architectural, structural & electrical drawings including those of other consultants.
2. It is the responsibility of contractors & manufacturers to check all relevant site dimensions prior to the start of construction or manufacture.
3. All materials and components must be installed on site in accordance with manufacturer's instructions, shop drawings and standard details.
4. All dimensions are in millimeters unless noted otherwise.
5. Full working drawings, specifications and samples are to be provided by Contractor/Supplier for approval prior to manufacture.

KEY PLAN

✗	INITIAL ISSUE	CAD	AM	SM	2022.10.23
REV.#	GENERAL NOTES	DRAWN BY	CHECKED BY	APPROVED BY	DATE

PROJECT TITLE	REFERENCE
---------------	-----------

RIC - RIYADH	RIC01
	G

DRAWING TITLE

RESIN PEDESTALS DETAIL

DRAWING NUMBER	REVISION
----------------	----------

ID-402	-
--------	---

SCALE	FORMAT	ADDITIONAL	DESIGN DEVELOPMENT
1:50	A1	NOTES	


**SIMA MALAK + ALSSAMOURE
DESIGN ASSOCIATES**

P.O. Box 15707 - Riyadh 11454 KSA
Tel. 01 441 4963 - Fax. 01 441 3867
simals@simals.com


©SIMA MALAK + ALSSAMOURE DESIGN ASSOCIATES (شركة) 2003
This document including all drawing and text is the property and
copyright of SIMA MALAK + ALSSAMOURE DESIGN ASSOCIATES for
use solely with respect to this Project and shall not be copied or
reproduced by any means except by agreement in writing from
SIMA MALAK + ALSSAMOURE DESIGN ASSOCIATES.




©SIMA MALAK + ALSSAMOURÉ DESIGN ASSOCIATES (سيدا) 2003
This document including all drawing and text is the property and
copyright of SIMA MALAK + ALSSAMOURÉ DESIGN ASSOCIATES for
use solely with respect to this Project and shall not be copied or
reproduced by any means except by agreement in writing from
SIMA MALAK + ALSSAMOURÉ DESIGN ASSOCIATES.

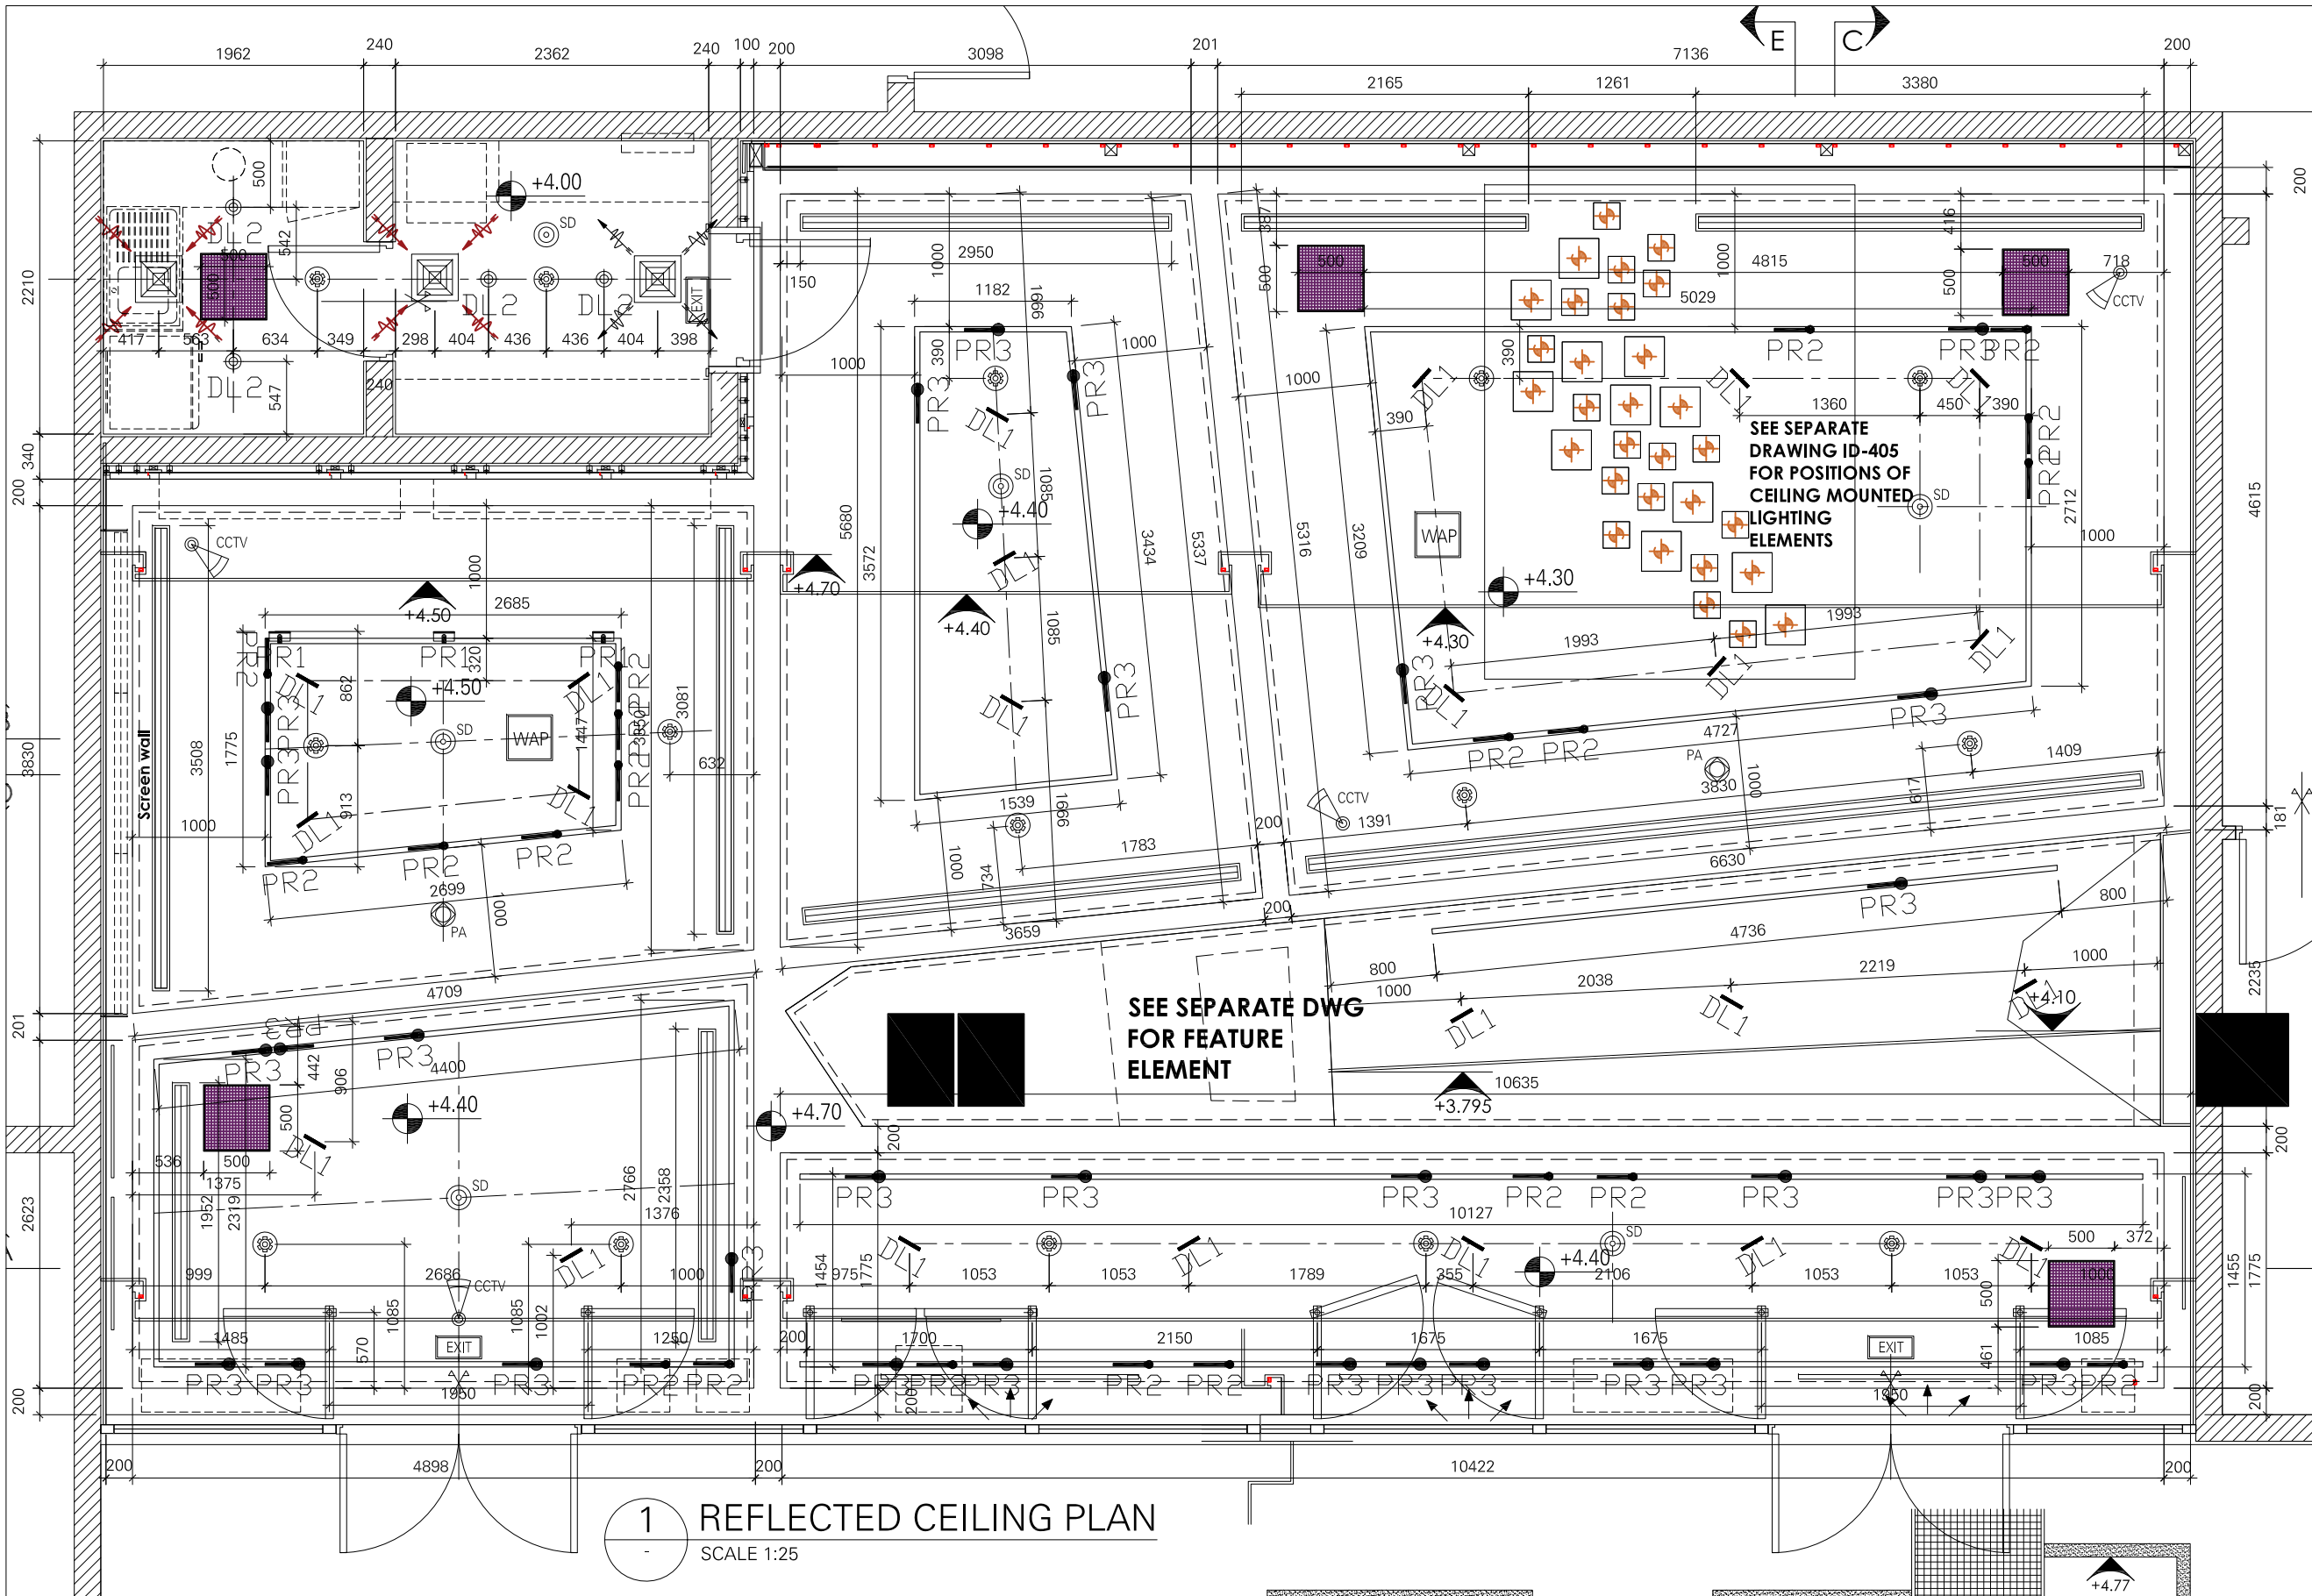

1 REFLECTED CEILING PLAN
SCALE 1:25

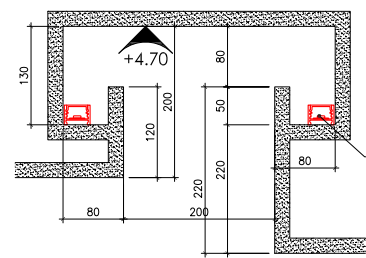

2 TYPICAL CLG DETAIL
SCALE 1:5

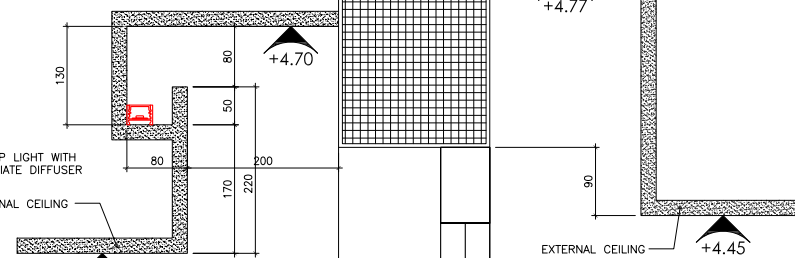

3 CLG DETAIL @ FACADE
SCALE 1:5

- GENERAL NOTES**
1. This drawing shall be read in conjunction with all other relevant architectural, structural & electrical drawings including those of other consultants.
 2. It is the responsibility of contractors & manufacturers to check all relevant site dimensions prior to the start of construction or manufacture.
 3. All materials and components must be installed on site in accordance with manufacturer's instructions, shop drawings and standard details.
 4. All dimensions are in millimeters unless noted otherwise.
 5. Full working drawings, specifications and samples are to be provided by Contractor/Supplier for approval prior to manufacture.
- LEGEND:**
- ACCESS PANEL
 - SD SMOKE DICTATOR
 - PA PA SPEAKER
 - WAP WI-FI ACCESS POINT
 - CCTV CCTV CAMERA
 - SPRINKLER
 - EXIT EXIT SIGN
- LOCATIONS OF ALL DEVICES TO BE VERIFIED BY APPROPRIATE ENGINEER / CONSULTANT
- SEE LIGHTING LAYOUT / SCHEDULE FOR LIGHTING FIXTURES AND DETAILS

KEY PLAN

B	CLG. HT. REV.	AC	AM	SM	2022.11.24
A	GENERAL REV.	AC	AM	SM	2022.11.14
X	INITIAL ISSUE	MP	AM	SM	2022.10.23
REV.#	GENERAL NOTES	DRAWN BY	CHECKED BY	APPROVED BY	DATE
PROJECT TITLE					REFERENCE
RIC - RIYADH					RIC01 G

DRAWING TITLE
REFLECTED CEILING LAYOUT

DRAWING NUMBER
ID-201

REVISION
A

SCALE
1:25, 5

FORMAT
A1

ADDITIONAL NOTES

DESIGN DEVELOPMENT

**SIMA MALAK + ALSSAMOURE
DESIGN ASSOCIATES**








P.O. Box 15707 - Riyadh 11454 KSA
Tel. 01 441 4963 - Fax. 01 441 3867
simals@simals.com

©SIMA MALAK + ALSSAMOURE DESIGN ASSOCIATES () 2003
This document including all drawing and text is the property and copyright of SIMA MALAK + ALSSAMOURE DESIGN ASSOCIATES for use solely with respect to this Project and shall not be copied or reproduced by any means except by agreement in writing from SIMA MALAK + ALSSAMOURE DESIGN ASSOCIATES.




5. Please Refer to Finishing Schedule and Sanitary Schedule for full specifications:
RIC01.1.3.FIN

©SIMA MALAK + ALSSAMOURE DESIGN ASSOCIATES (سما) 2001
This document including all drawing and text is the property and
copyright of SIMA MALAK + ALSSAMOURE DESIGN ASSOCIATES to
use solely with respect to this Project and shall not be copied or
reproduced by any means except by agreement in writing from
SIMA MALAK + ALSSAMOURE DESIGN ASSOCIATES.

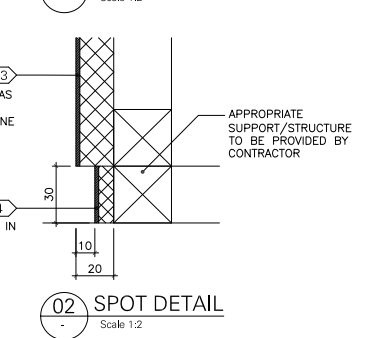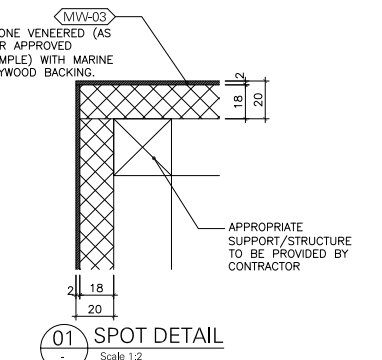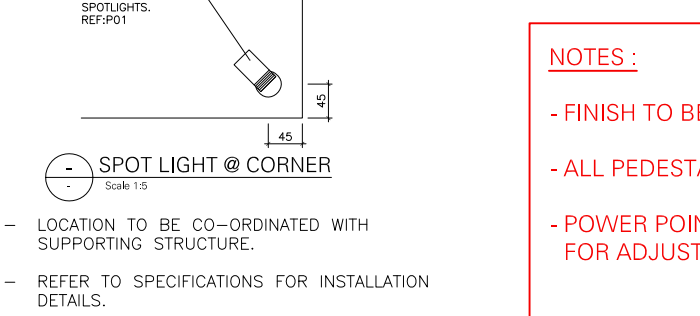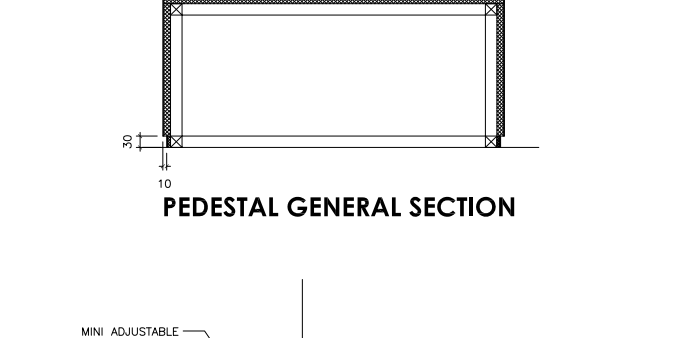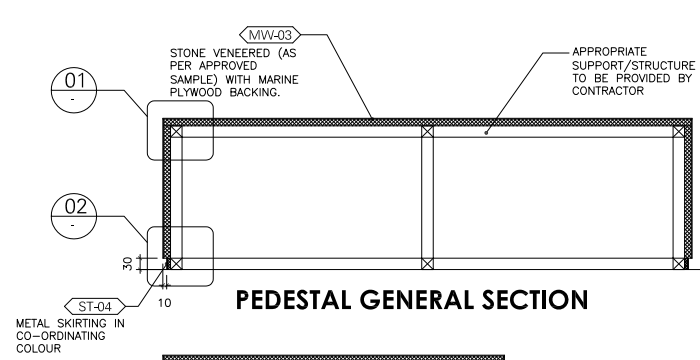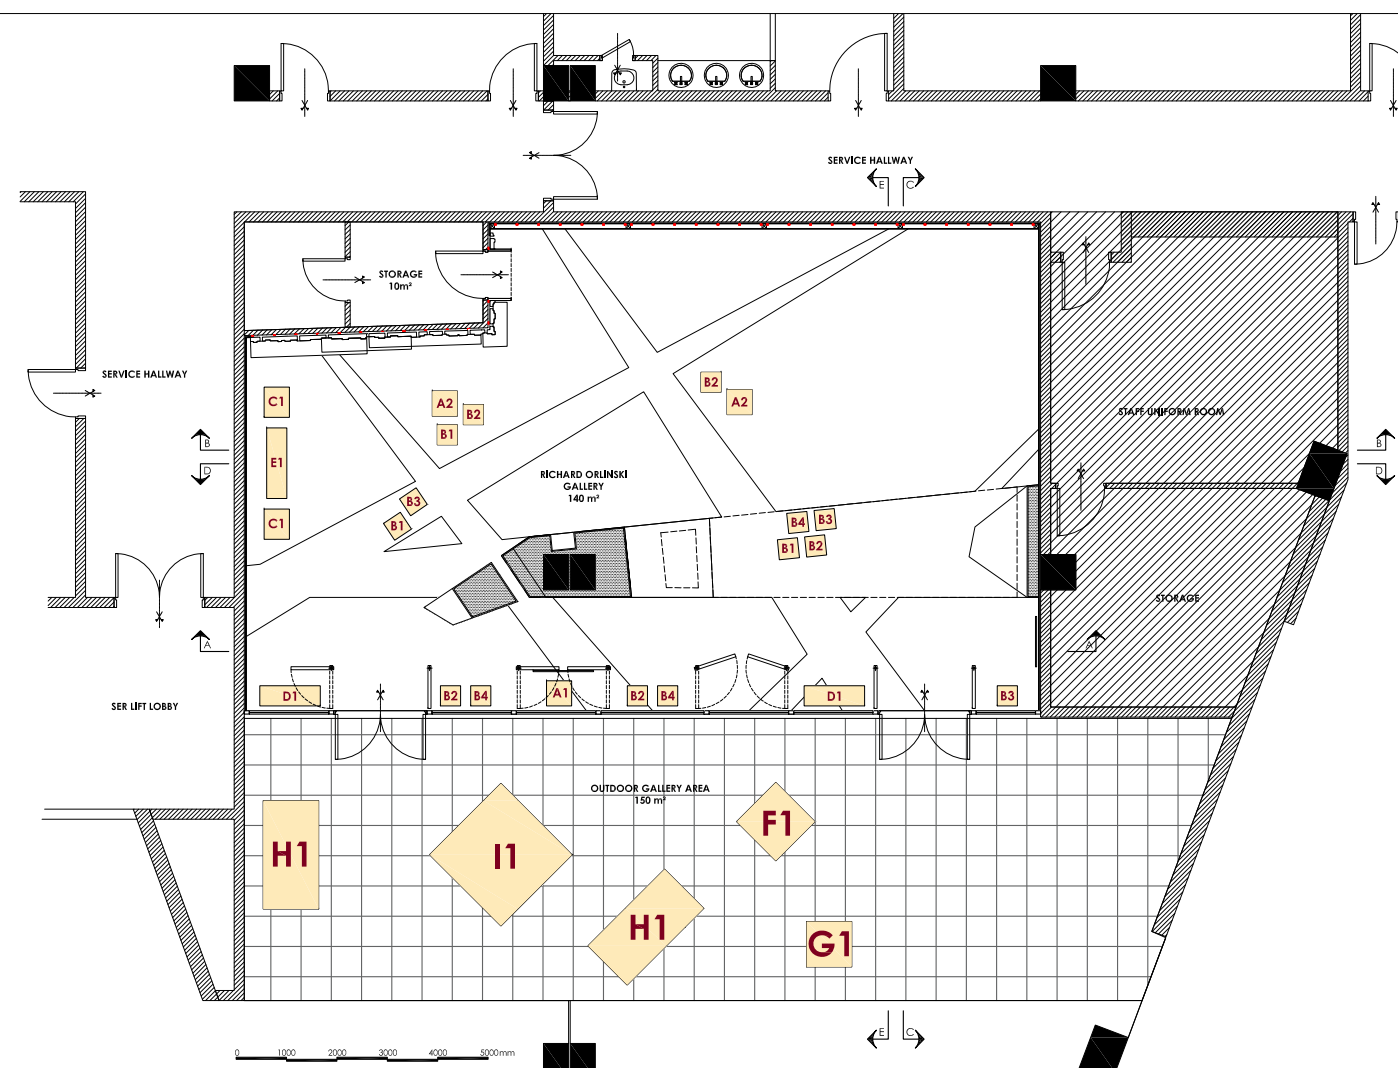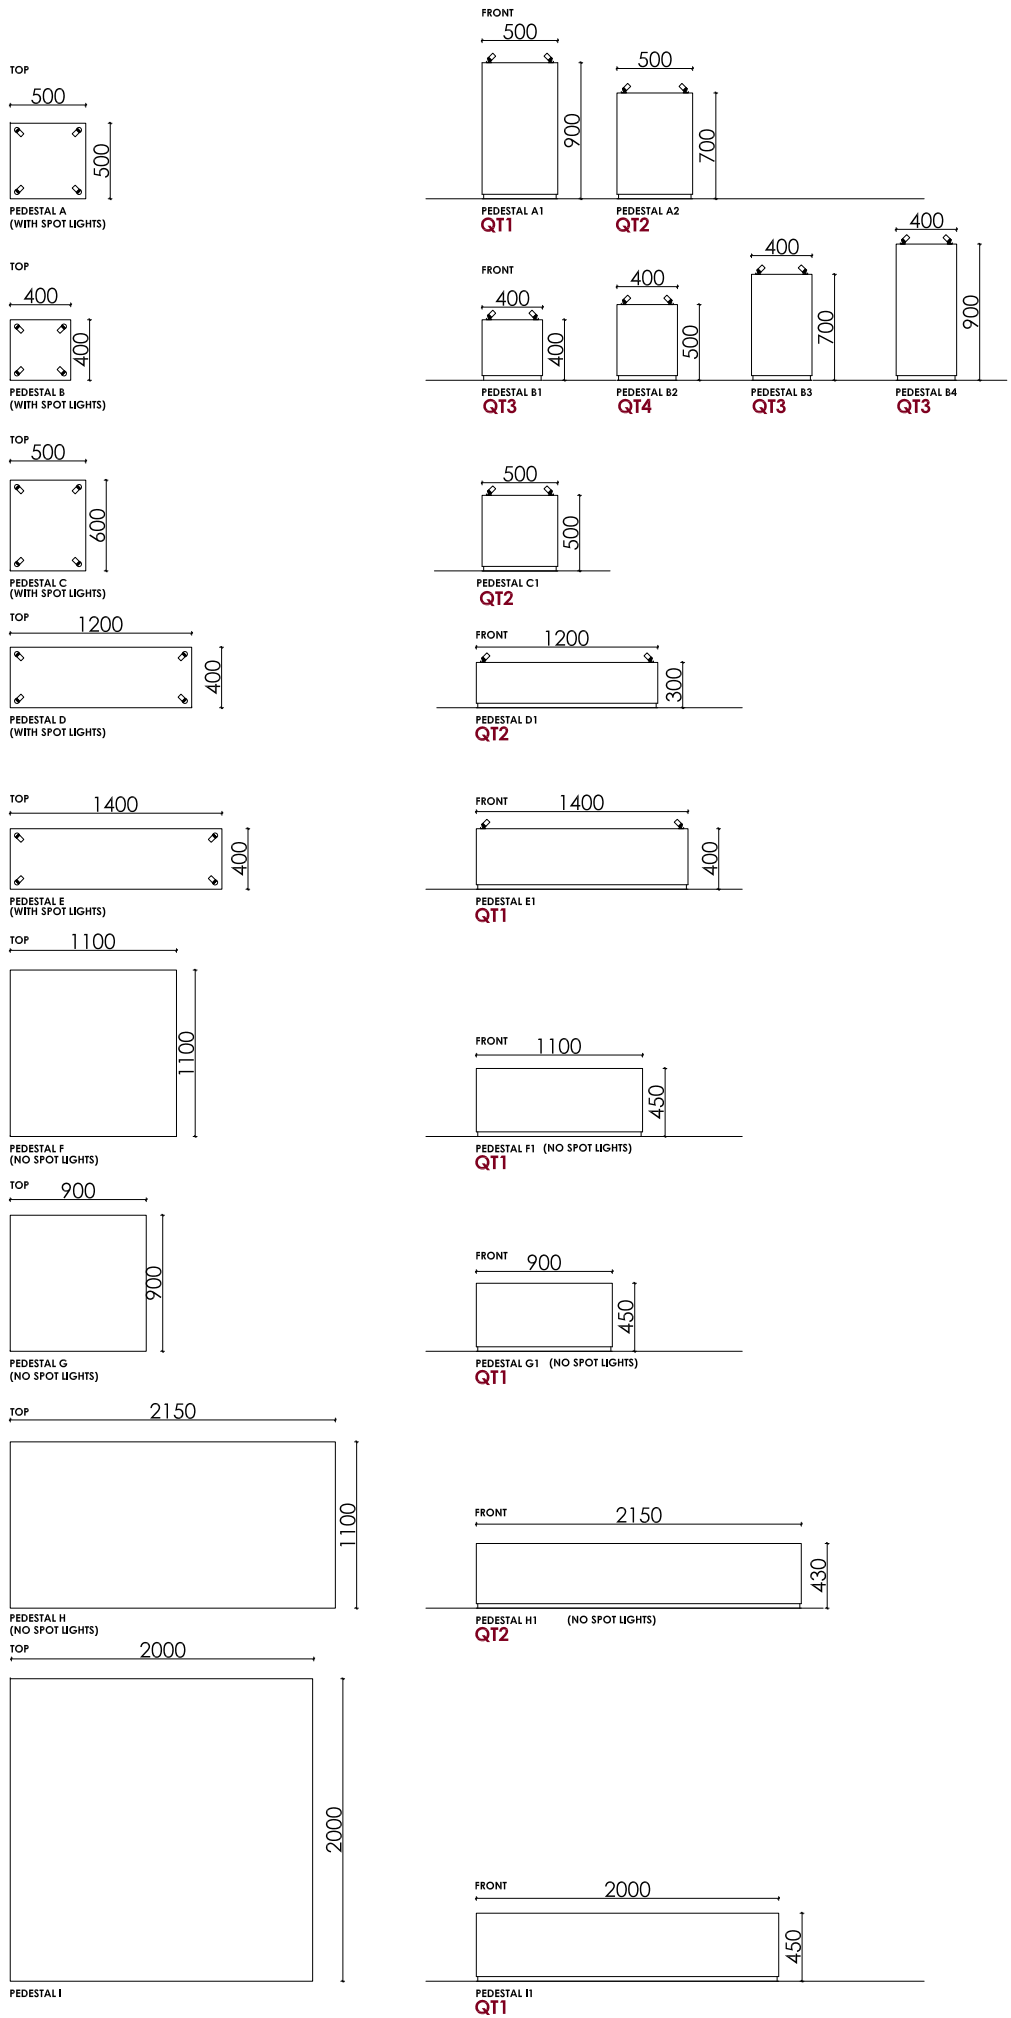

- GENERAL NOTES**
1. This drawing shall be read in conjunction with all other relevant architectural, structural & electrical drawings including those of other consultants.
 2. It is the responsibility of contractors & manufacturers to check all relevant site dimensions prior to the start of construction or manufacture.
 3. All materials and components must be installed on site in accordance with manufacturer's instructions, shop drawings and standard details.
 4. All dimensions are in millimeters unless noted otherwise.
 5. Full working drawings, specifications and samples are to be provided by Contractor/Supplier for approval prior to manufacture.

KEY PLAN

 

REV.#	GENERAL REV.	MP	AM	SM	DATE
1	INITIAL ISSUE	CAD	AM	SM	2022.10.23
2	GENERAL NOTES	DRAWN BY	CHECKED BY	APPROVED BY	DATE
PROJECT TITLE					REFERENCE
RIC - RIYADH					RIC01
DRAWING TITLE					G

PEDESTALS DETAILS

DRAWING NUMBER: ID-401

REVISION: A

SCALE: 1:50

FORMAT: A1

ADDITIONAL NOTES:

DESIGN DEVELOPMENT

SIMA MALAK + ALSSAMOURE DESIGN ASSOCIATES


P.O. Box 15707 - Riyadh 11454 KSA

Tel. 01 441 4963 - Fax. 01 441 3867


simal@simals.com

©SIMA MALAK + ALSSAMOURE DESIGN ASSOCIATES (شركة) 2003
This document including all drawing and text is the property and copyright of SIMA MALAK + ALSSAMOURE DESIGN ASSOCIATES for use solely with respect to this Project and shall not be copied or reproduced by any means except by agreement in writing from SIMA MALAK + ALSSAMOURE DESIGN ASSOCIATES.


- NOTES :**
- FINISH TO BE AS PER APPROVED SAMPLES.
 - ALL PEDESTALS TO BE IN ONE FINISH.
 - POWER POINT TO BE PROVIDED IN THE MIDDLE OF EACH PEDESTAL FOR ADJUSTABLE SPOTLIGHTS AT CORNERS.

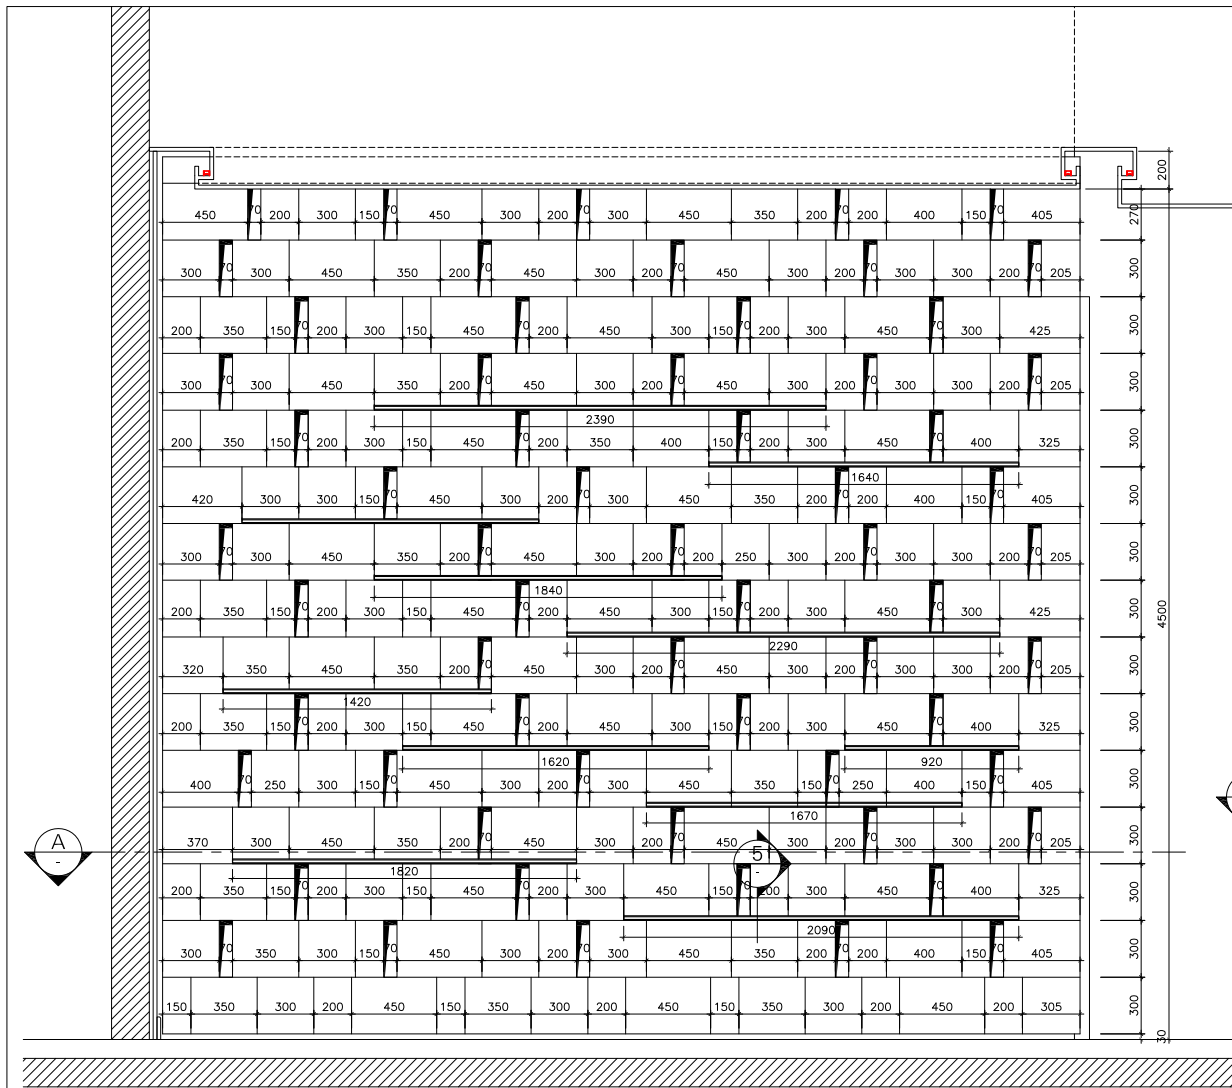


2 ELEVATION - B
SCALE 1:20

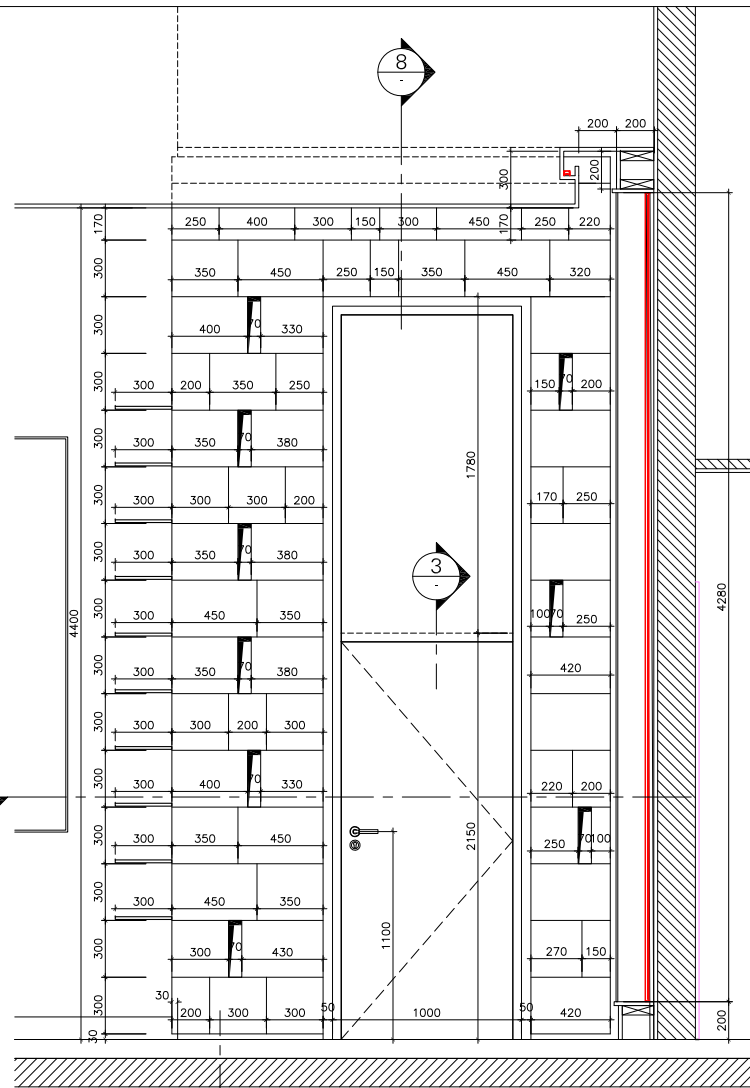


3 ELEVATION - C
SCALE 1:20

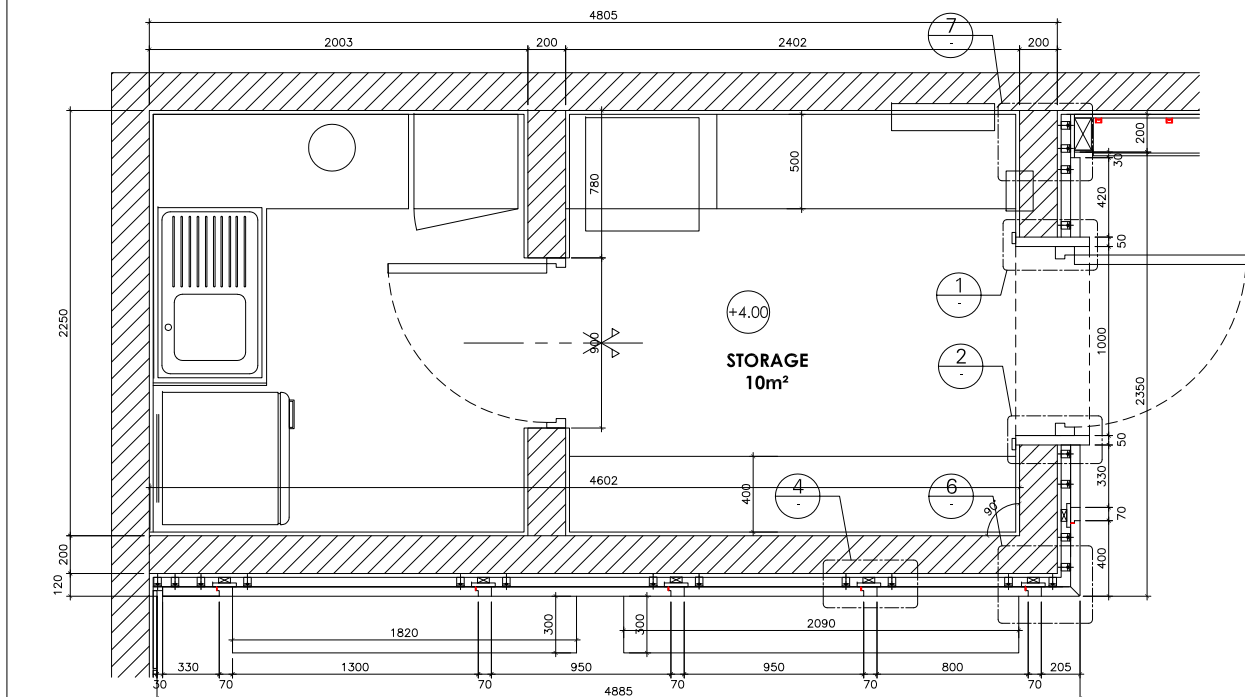


A PLAN
SCALE 1:20

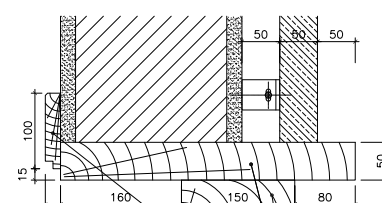


1 DETAIL
SCALE 1:5

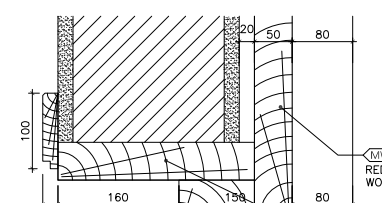


3 DETAIL
SCALE 1:5

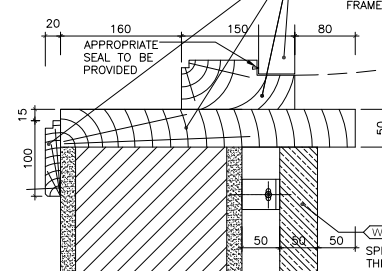


2 DETAIL
SCALE 1:5

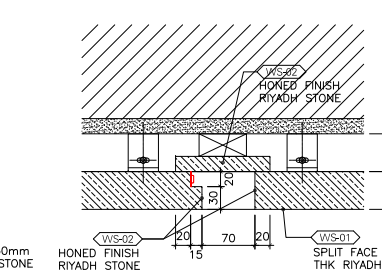


4 DETAIL
SCALE 1:5

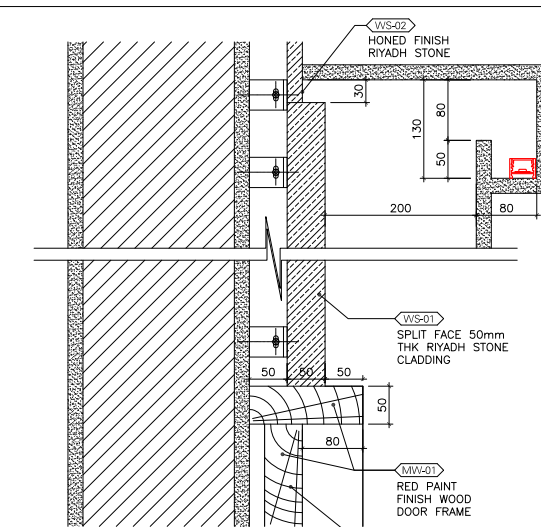


9 DETAIL
SCALE 1:5

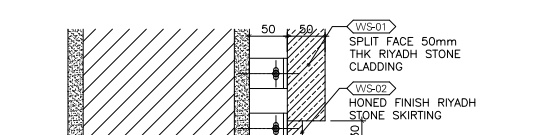


8 DETAIL
SCALE 1:5

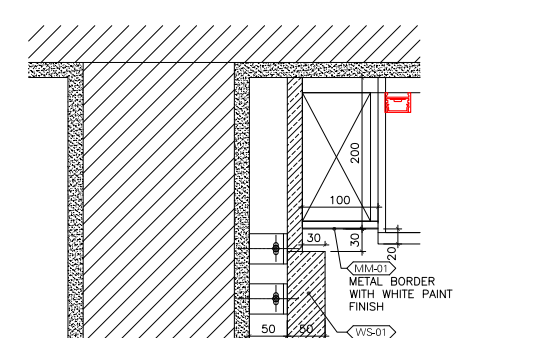

7 DETAIL
SCALE 1:5

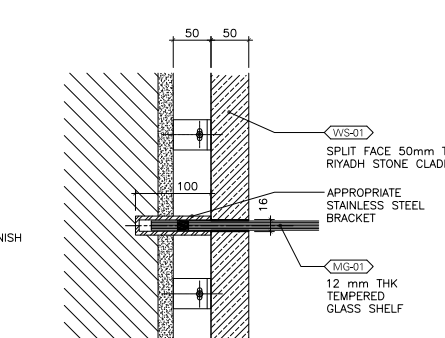

5 DETAIL
SCALE 1:5

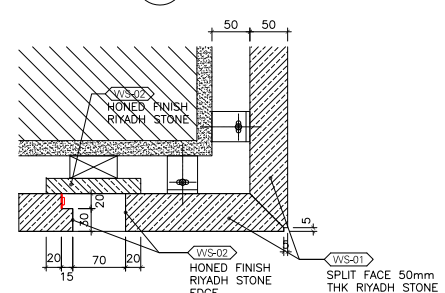

6 DETAIL
SCALE 1:5

GENERAL NOTES

1. This drawing shall be read in conjunction with all other relevant architectural, structural & electrical drawings including those of other consultants.
2. It is the responsibility of contractors & manufacturers to check all relevant site dimensions prior to the start of construction or manufacture.
3. All materials and components must be installed on site in accordance with manufacturer's instructions, shop drawings and standard details.
4. All dimensions are in millimeters unless noted otherwise.
5. Full working drawings, specifications and samples are to be provided by Contractor/Supplier for approval prior to manufacture.

NOTES FOR MANUFACTURER:

- * Construction methods shown on drawings are suggested methods only.
- * Construction methods must be discussed between designer and manufacturer prior to fabrication.
- * All details must be adhered to any deviation must be discussed with the designer prior to manufacture.
- * Structure to be specified by manufacturer considering practicalities and the aesthetics of the design.
- * All dimensions are shown using standard thickness, please allow veneer thickness when considering fitted elements.






KEY PLAN

B	GEN. REV.	AC	AM	SM	2022.11.27
A	GEN. REV.	AC	AM	SM	2022.11.08
X	INITIAL ISSUE	MP	AM	SM	2022.11.01
REV.#	GENERAL NOTES	DRAWN BY	CHECKED BY	APPROVED BY	DATE
PROJECT TITLE					REFERENCE
RIC-RIYADH					RIC01 G

DRAWING TITLE		PROPOSED FEATURE WALL DETAILS	
DRAWING NUMBER		REVISION	
ID-402		B	
SCALE	FORMAT	ADDITIONAL NOTES	DESIGN DEVELOPMENT
1:20, 5	A1		

**SIMA MALAK + ALSSAMOURÉ
DESIGN ASSOCIATES**
P.O. Box 15707 - Riyadh 11454 KSA
Tel. 01 441 4963 - Fax. 01 441 3867
simas@simas.com

©SIMA MALAK + ALSSAMOURÉ DESIGN ASSOCIATES () 2003
This document including all drawing and text is the property and
copyright of SIMA MALAK + ALSSAMOURÉ DESIGN ASSOCIATES for
use solely with respect to this Project and shall not be copied or
reproduced by any means except by agreement in writing from
SIMA MALAK + ALSSAMOURÉ DESIGN ASSOCIATES.

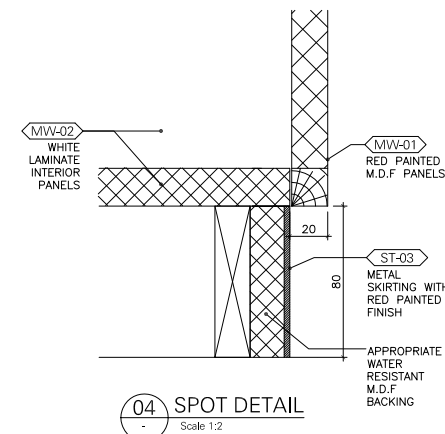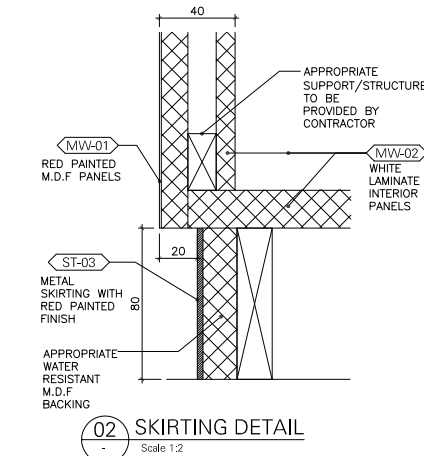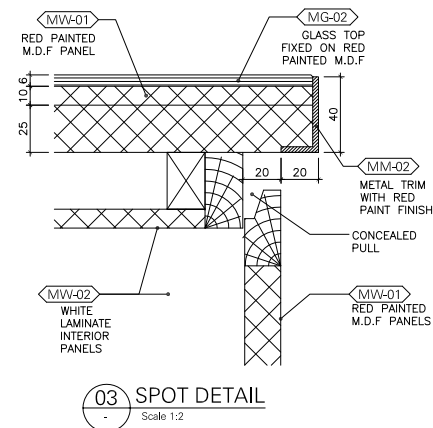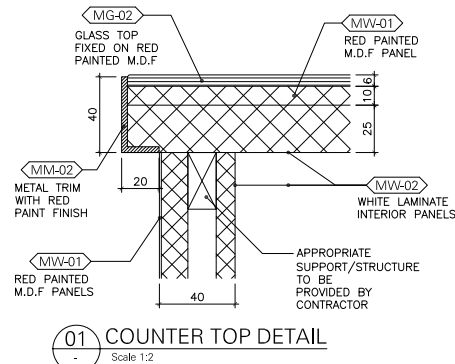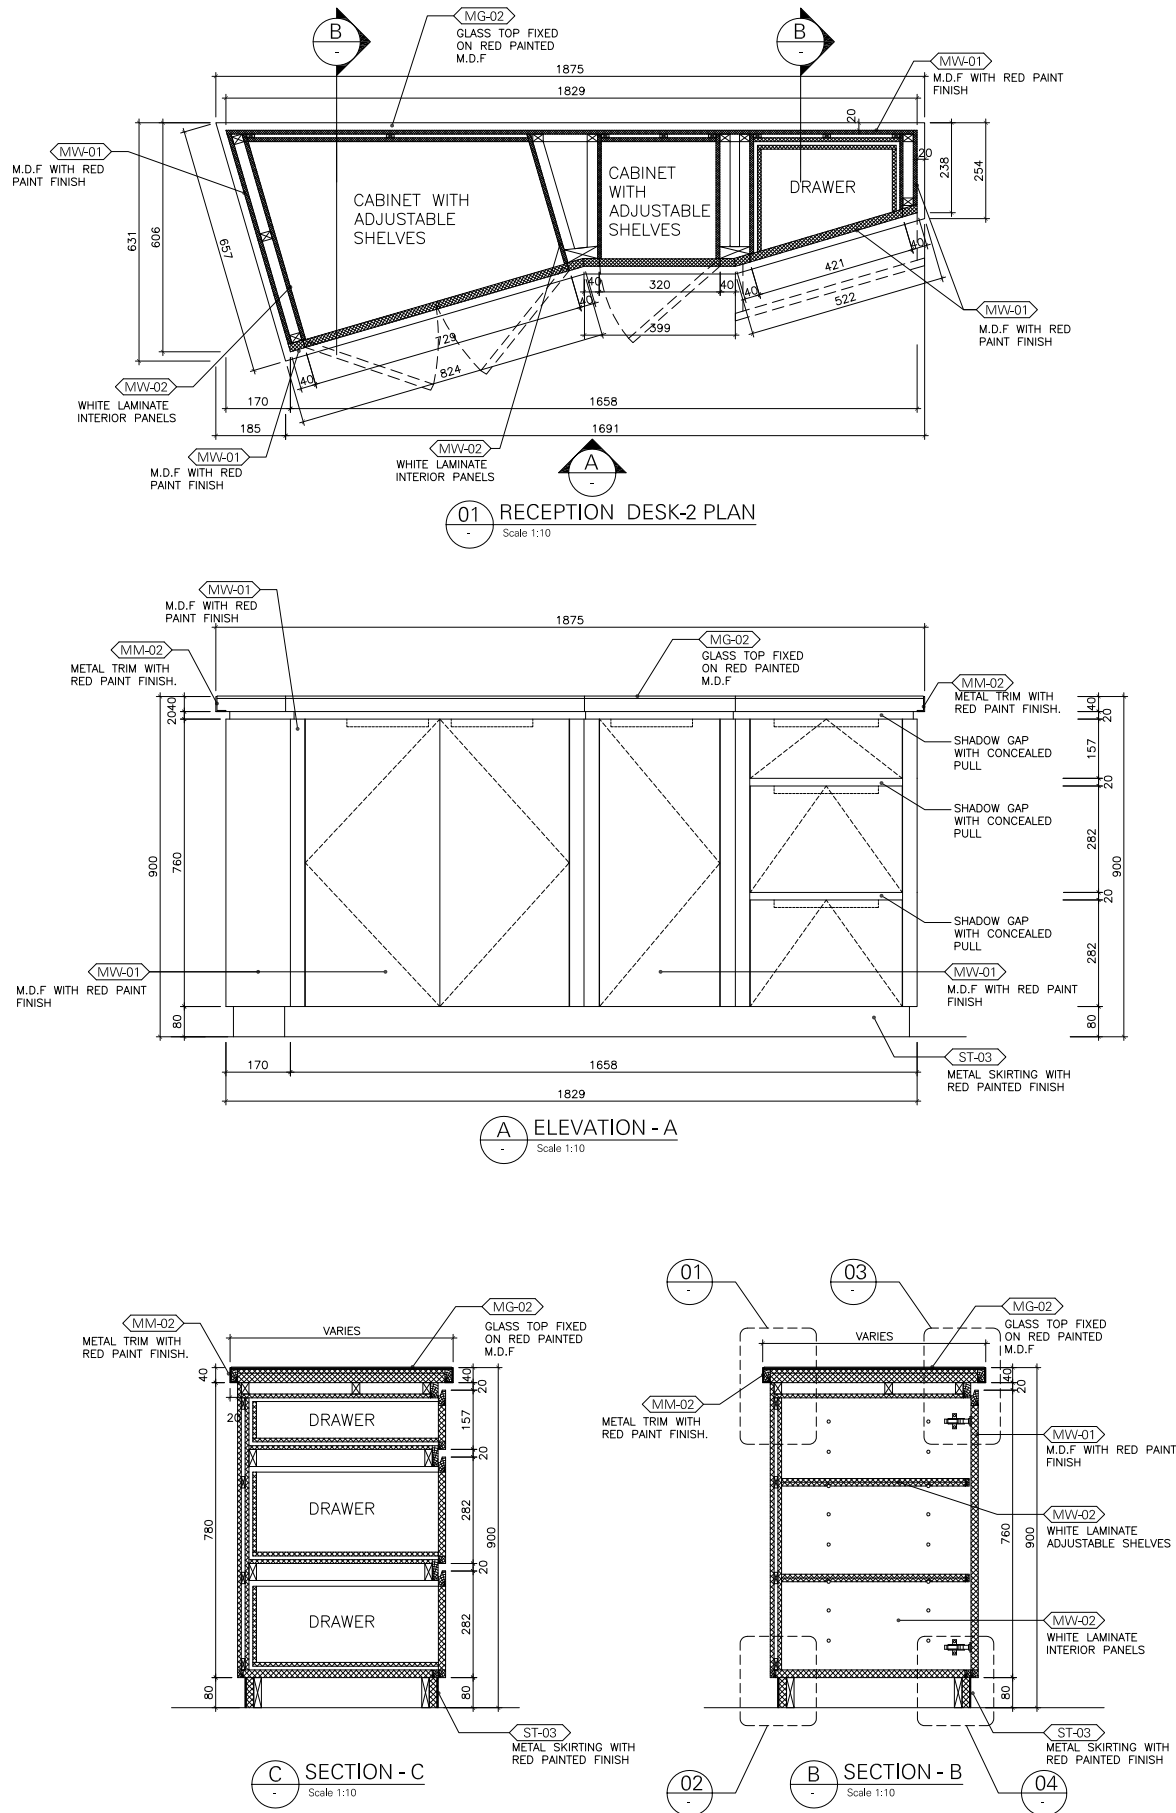

GENERAL NOTES

1. This drawing shall be read in conjunction with all other relevant architectural, structural & electrical drawings including those of other consultants.
2. It is the responsibility of contractors & manufacturers to check all relevant site dimensions prior to the start of construction or manufacture.
3. All materials and components must be installed on site in accordance with manufacturer's instructions, shop drawings and standard details.
4. All dimensions are in millimeters unless noted otherwise.
5. Full working drawings, specifications and samples are to be provided by Contractor/Supplier for approval prior to manufacture.

KEY PLAN

A	GENERAL REV.	MP	AM	SM	2022.11.08
X	INITIAL ISSUE	CAD	AM	SM	2022.10.23
REV.#	GENERAL NOTES	DRAWN BY	CHECKED BY	APPROVED BY	DATE
PROJECT TITLE					REFERENCE
RIC - RIYADH					RIC01 G


DRAWING TITLE

RECEPTION CONSOLE DETAILS


DRAWING NUMBER		REVISION	
ID-403-2		A	
SCALE	FORMAT	ADDITIONAL NOTES	DESIGN DEVELOPMENT
1:50	A1		

**SIMA MALAK + ALSSAMOURE
DESIGN ASSOCIATES**
P.O. Box 15707 - Riyadh 11454 KSA
Tel. 01 441 4963 - Fax. 01 441 3867
simals@simals.com


©SIMA MALAK + ALSSAMOURE DESIGN ASSOCIATES (شركة) 2003
This document including all drawing and text is the property and
copyright of SIMA MALAK + ALSSAMOURE DESIGN ASSOCIATES for
use solely with respect to this Project and shall not be copied or
reproduced by any means except by agreement in writing from
SIMA MALAK + ALSSAMOURE DESIGN ASSOCIATES.

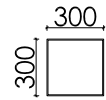


PLAN

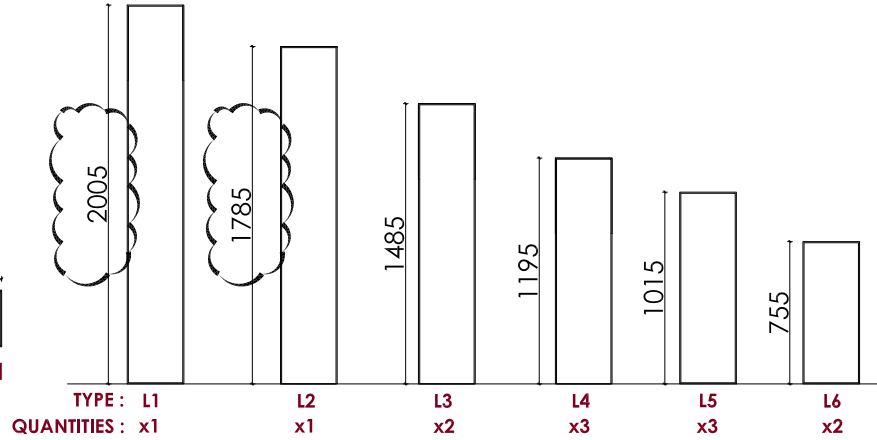



01 CEILING MOUNTED - LARGE ELEMENTS WITHOUT DISPLAY CASE - ELEVATIONS
Scale 1:20

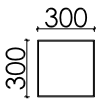


PLAN

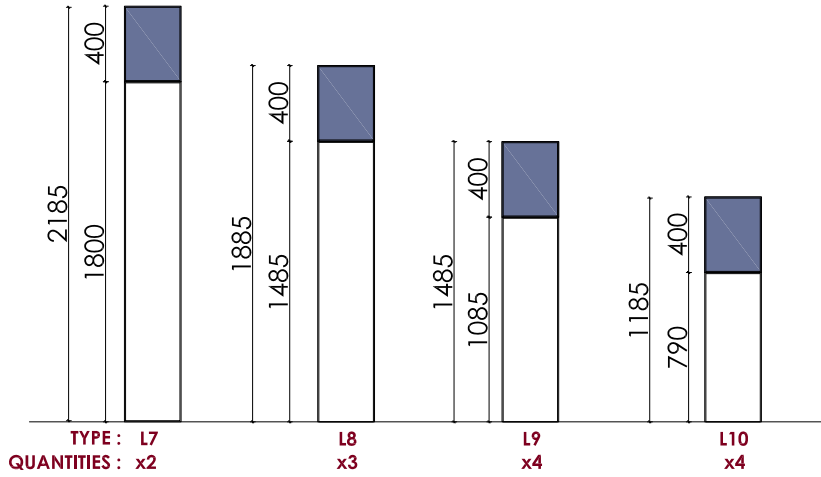


01 FLOOR STANDING - LARGE ELEMENTS WITH DISPLAY CASE - ELEVATIONS
Scale 1:20

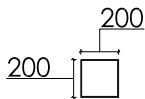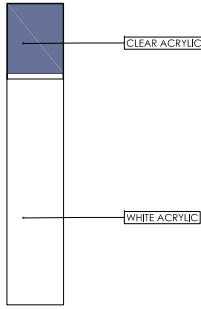


PLAN

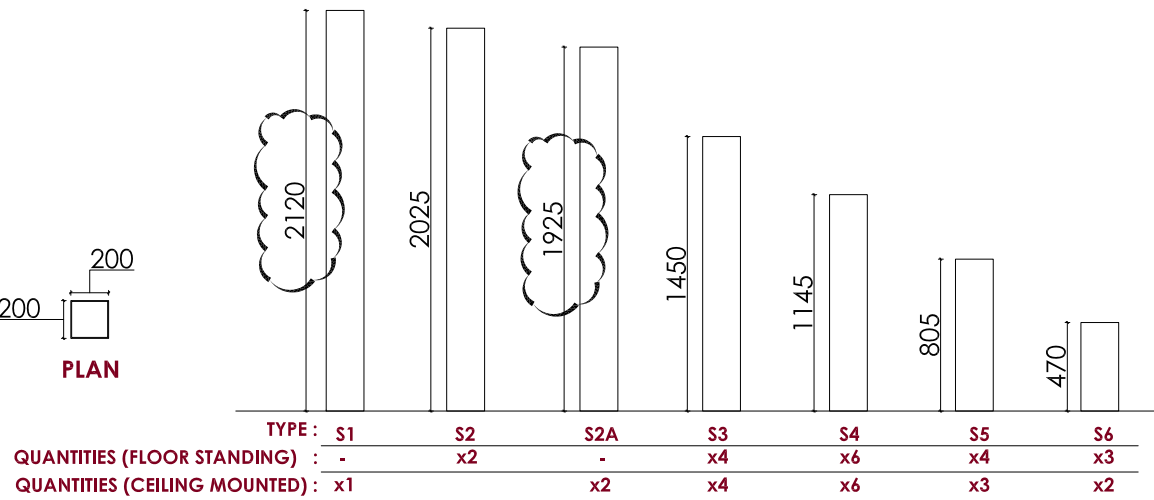


02 FLOOR STANDING + CEILING MOUNTED - SMALL ELEMENT ELEVATIONS
Scale 1:20

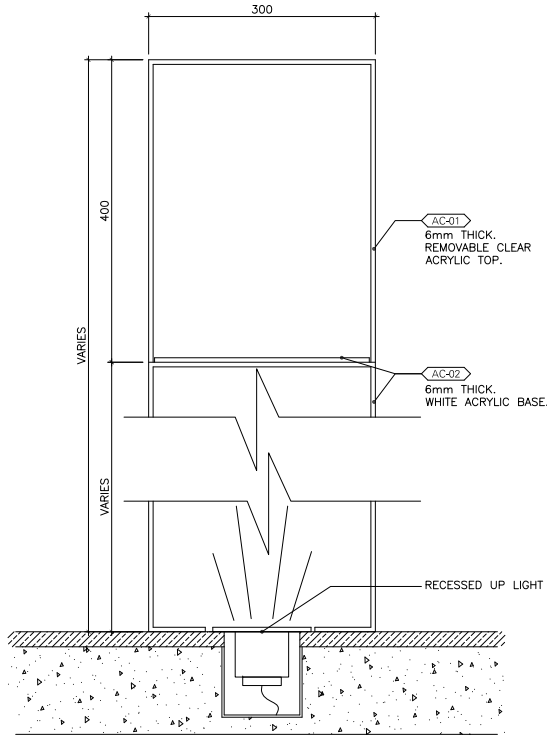


01 TYPICAL FLOOR STANDING PEDESTAL WITH DISPLAY CASE
Scale 1:5

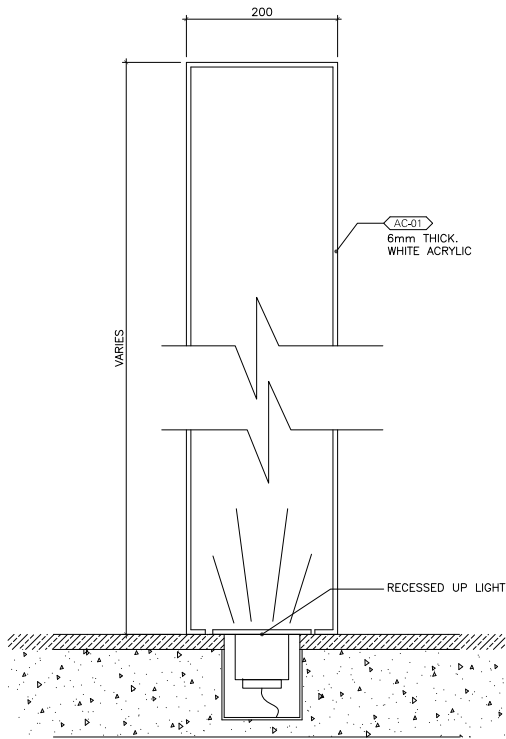

03 TYPICAL FLOOR STANDING PEDESTAL WITHOUT DISPLAY CASE
Scale 1:5

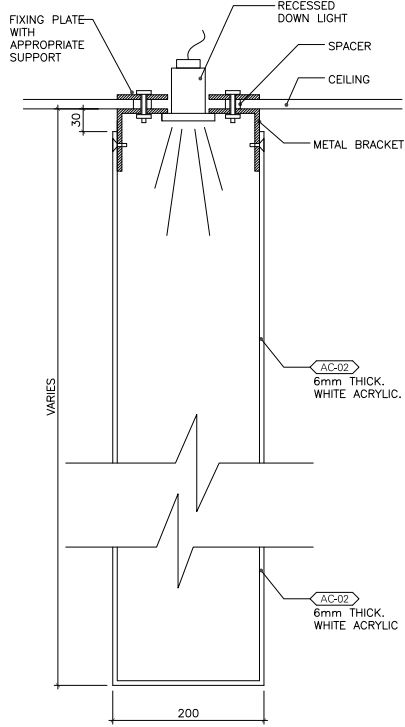

02 TYPICAL SMALL CEILING MOUNTED ELEMENTS
Scale 1:5

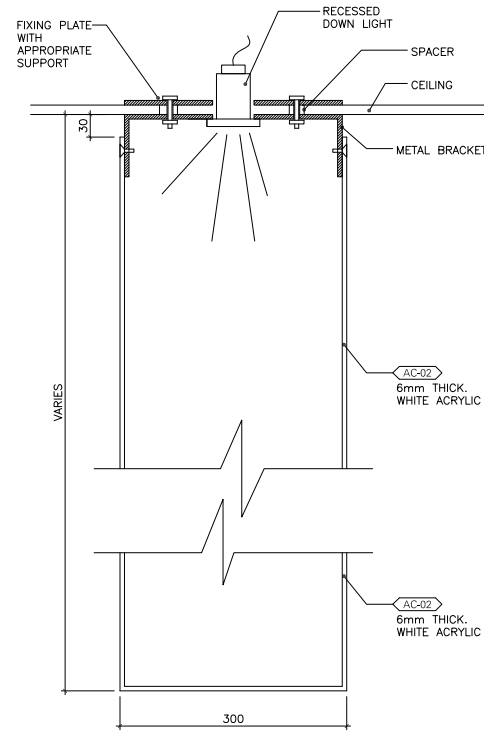

04 TYPICAL LARGE CEILING MOUNTED ELEMENTS
Scale 1:5

NOTES :

- FINISH AND CONSTRUCTION OF ACRYLIC ELEMENT AS PER APPROVED SAMPLES.

GENERAL NOTES

1. This drawing shall be read in conjunction with all other relevant architectural, structural & electrical drawings including those of other consultants.
2. It is the responsibility of contractors & manufacturers to check all relevant site dimensions prior to the start of construction or manufacture.
3. All materials and components must be installed on site in accordance with manufacturer's instructions, shop drawings and standard details.
4. All dimensions are in millimeters unless noted otherwise.
5. Full working drawings, specifications and samples are to be provided by Contractor/Supplier for approval prior to manufacture.

KEY PLAN

B	REV. WITH CLOUD	MP	AM	SM	2022.11.27
A	GENERAL REV.	MP	AM	SM	2022.11.14
X	INITIAL ISSUE	CAD	AM	SM	2022.10.23
REV.#	GENERAL NOTES	DRAWN BY	CHECKED BY	APPROVED BY	DATE
PROJECT TITLE					REFERENCE
RIC - RIYADH					RIC01 G

DRAWING TITLE

DISPLAY PEDESTAL / ELEMENT DETAILS

DRAWING NUMBER

ID-404

B

SCALE 1:20

FORMAT A1

ADDITIONAL NOTES

DESIGN DEVELOPMENT

SIMA MALAK + ALSSAMOURE
DESIGN ASSOCIATES
P.O. Box 15707 - Riyadh 11454 KSA
Tel. 01 441 4963 - Fax. 01 441 3867
simals@simals.com


©SIMA MALAK + ALSSAMOURE DESIGN ASSOCIATES (شركة) 2003
This document including all drawing and text is the property and copyright of SIMA MALAK + ALSSAMOURE DESIGN ASSOCIATES for use solely with respect to this Project and shall not be copied or reproduced by any means except by agreement in writing from SIMA MALAK + ALSSAMOURE DESIGN ASSOCIATES.



1. This drawing shall be read in conjunction with all other relevant architectural, structural & electrical drawings including those of other consultants.
2. It is the responsibility of contractors & manufacturers to check all relevant site dimensions prior to the start of construction or manufacture.
3. All materials and components must be installed on site in accordance with manufacturer's instructions, shop drawings and standard details.
4. All dimensions are in millimeters unless noted otherwise.
5. Full working drawings, specifications and samples are to be provided by Contractor/Supplier for approval prior to manufacture.

* UP-LIGHTS REF. SQ1 TO BE PROVIDED AT THE CENTER OF EACH PEDESTAL.

X	INITIAL ISSUE		MP		AM		SM		2022.11.14
REV.#	GENERAL NOTES	DRAWN BY	CHECKED BY	APPROVED BY					DATE
PROJECT TITLE								REFERENCE	
RIC - RIYADH								RICO1 G	
DRAWING TITLE									
FLOOR STANDING DISPLAY PEDESTAL KEY PLAN									
DRAWING NUMBER							REVISION		
ID-405-1							-		
SCALE		FORMAT		ADDITIONAL NOTES		DESIGN DEVELOPMENT			
1:10		A1							
									
SIMA MALAK + ALSSAMOURE DESIGN ASSOCIATES									
P.O. Box 15707 - Riyadh 11454 KSA Tel. 01 441 4963 - Fax. 01 441 3867 simals@simals.com									
©SIMA MALAK + ALSSAMOURE DESIGN ASSOCIATES (شركة) 2003 This document including all drawing and text is the property and copyright of SIMA MALAK + ALSSAMOURE DESIGN ASSOCIATES for use solely with respect to this Project and shall not be copied or reproduced by any means except by agreement in writing from SIMA MALAK + ALSSAMOURE DESIGN ASSOCIATES.									

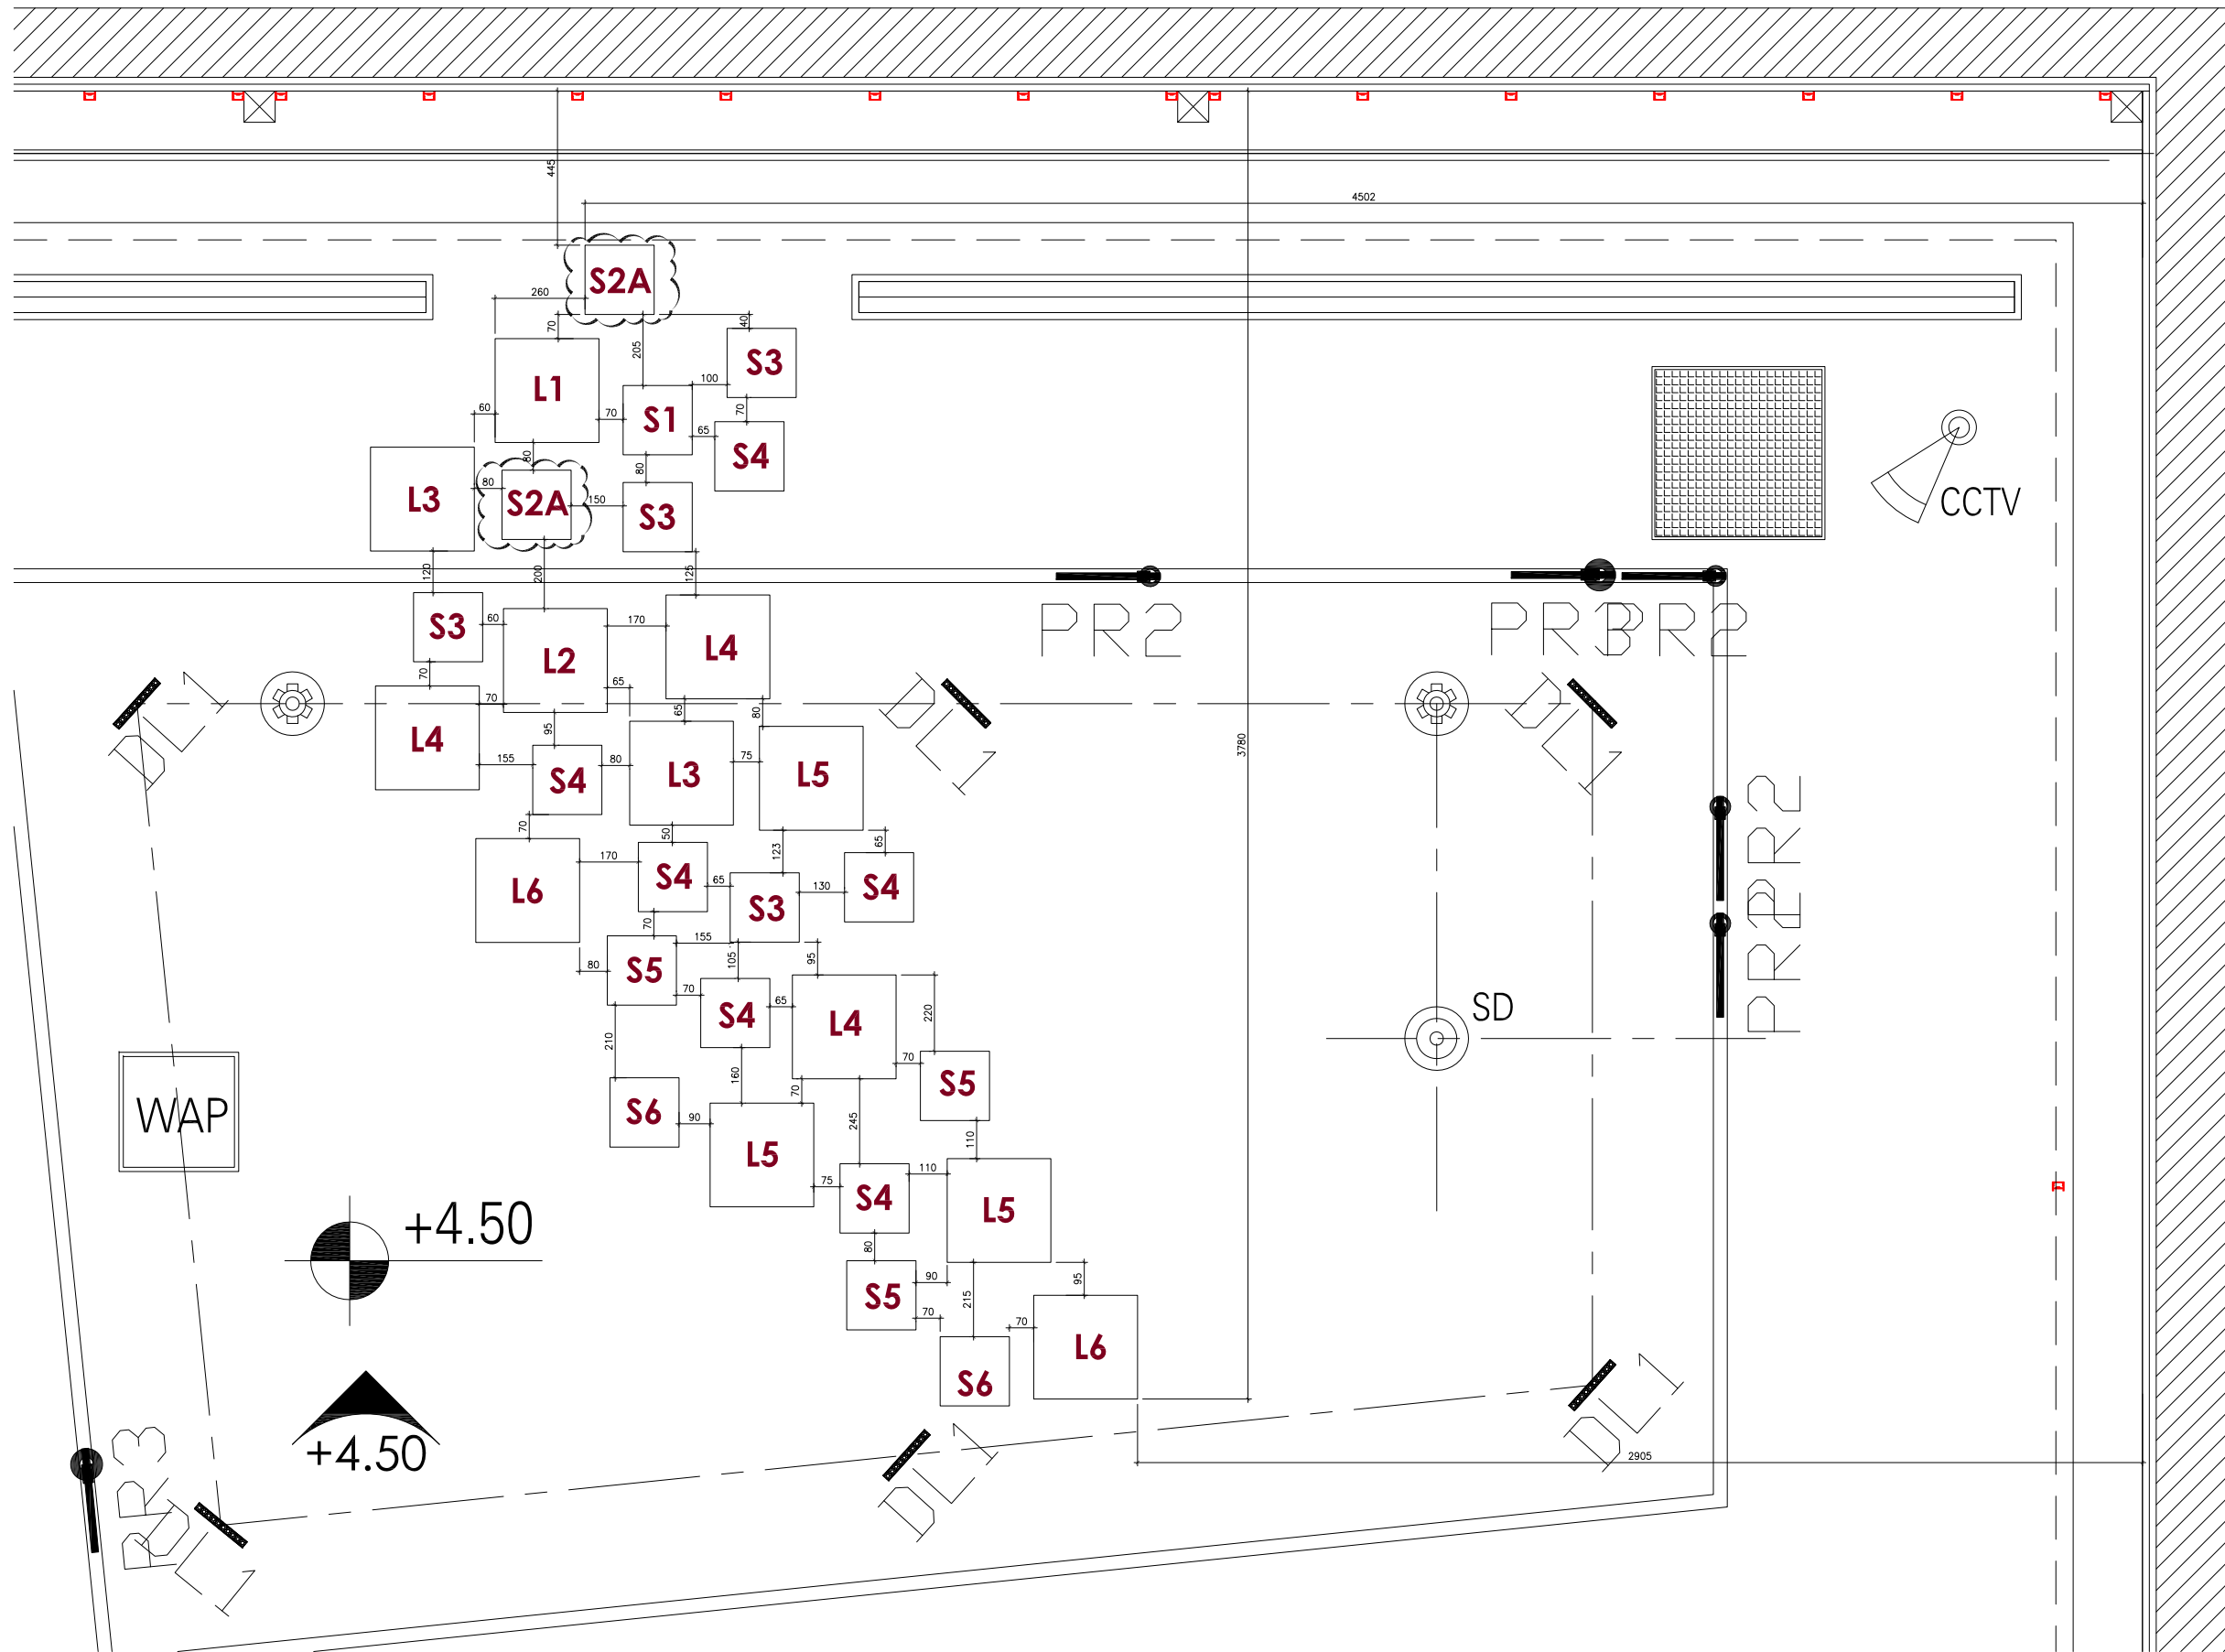


- GENERAL NOTES**
1. This drawing shall be read in conjunction with all other relevant architectural, structural & electrical drawings including those of other consultants.
 2. It is the responsibility of contractors & manufacturers to check all relevant site dimensions prior to the start of construction or manufacture.
 3. All materials and components must be installed on site in accordance with manufacturer's instructions, shop drawings and standard details.
 4. All dimensions are in millimeters unless noted otherwise.
 5. Full working drawings, specifications and samples are to be provided by Contractor/Supplier for approval prior to manufacture.

NOTES :

* DOWN LIGHTS REF. SQ1 TO BE PROVIDED AT THE CENTER OF EACH ELEMENT.

KEY PLAN

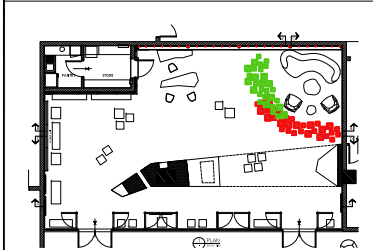

A	REV. WITH CLOUD	MP	AM	SM	2022.11.27
X	INITIAL ISSUE	MP	AM	SM	2022.11.14
REV.#	GENERAL NOTES	DRAWN BY	CHECKED BY	APPROVED BY	DATE
PROJECT TITLE					REFERENCE
RIC - RIYADH					RIC01
DRAWING TITLE					G



DRAWING NUMBER		REVISION	
ID-405-2		A	
SCALE	FORMAT	ADDITIONAL NOTES	DESIGN DEVELOPMENT
1:10	A1		


**SIMA MALAK + ALSSAMOURE
DESIGN ASSOCIATES**

P.O. Box 15707 - Riyadh 11454 KSA
Tel. 01 441 4963 - Fax. 01 441 3867
simals@simals.com


©SIMA MALAK + ALSSAMOURE DESIGN ASSOCIATES (شركة) 2003
This document including all drawing and text is the property and copyright of SIMA MALAK + ALSSAMOURE DESIGN ASSOCIATES for use solely with respect to this Project and shall not be copied or reproduced by any means except by agreement in writing from SIMA MALAK + ALSSAMOURE DESIGN ASSOCIATES.

02 CEILING MOUNTED - LIGHTING ELEMENTS KEY PLAN
Scale 1:10

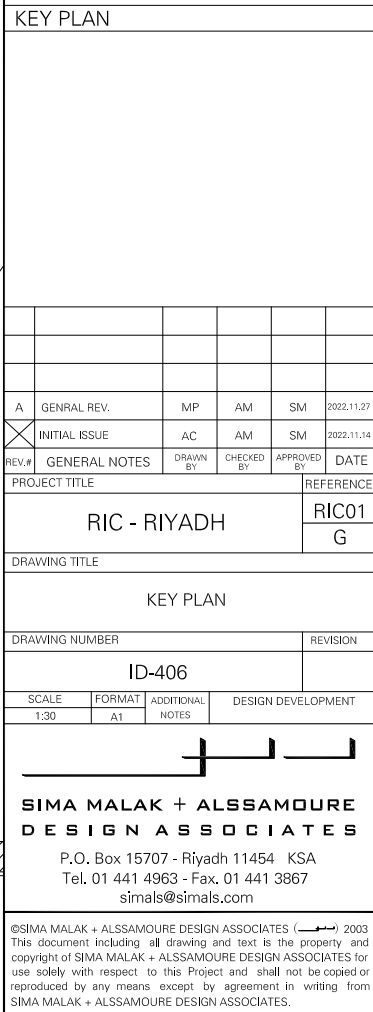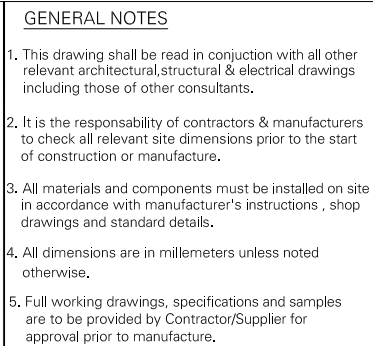


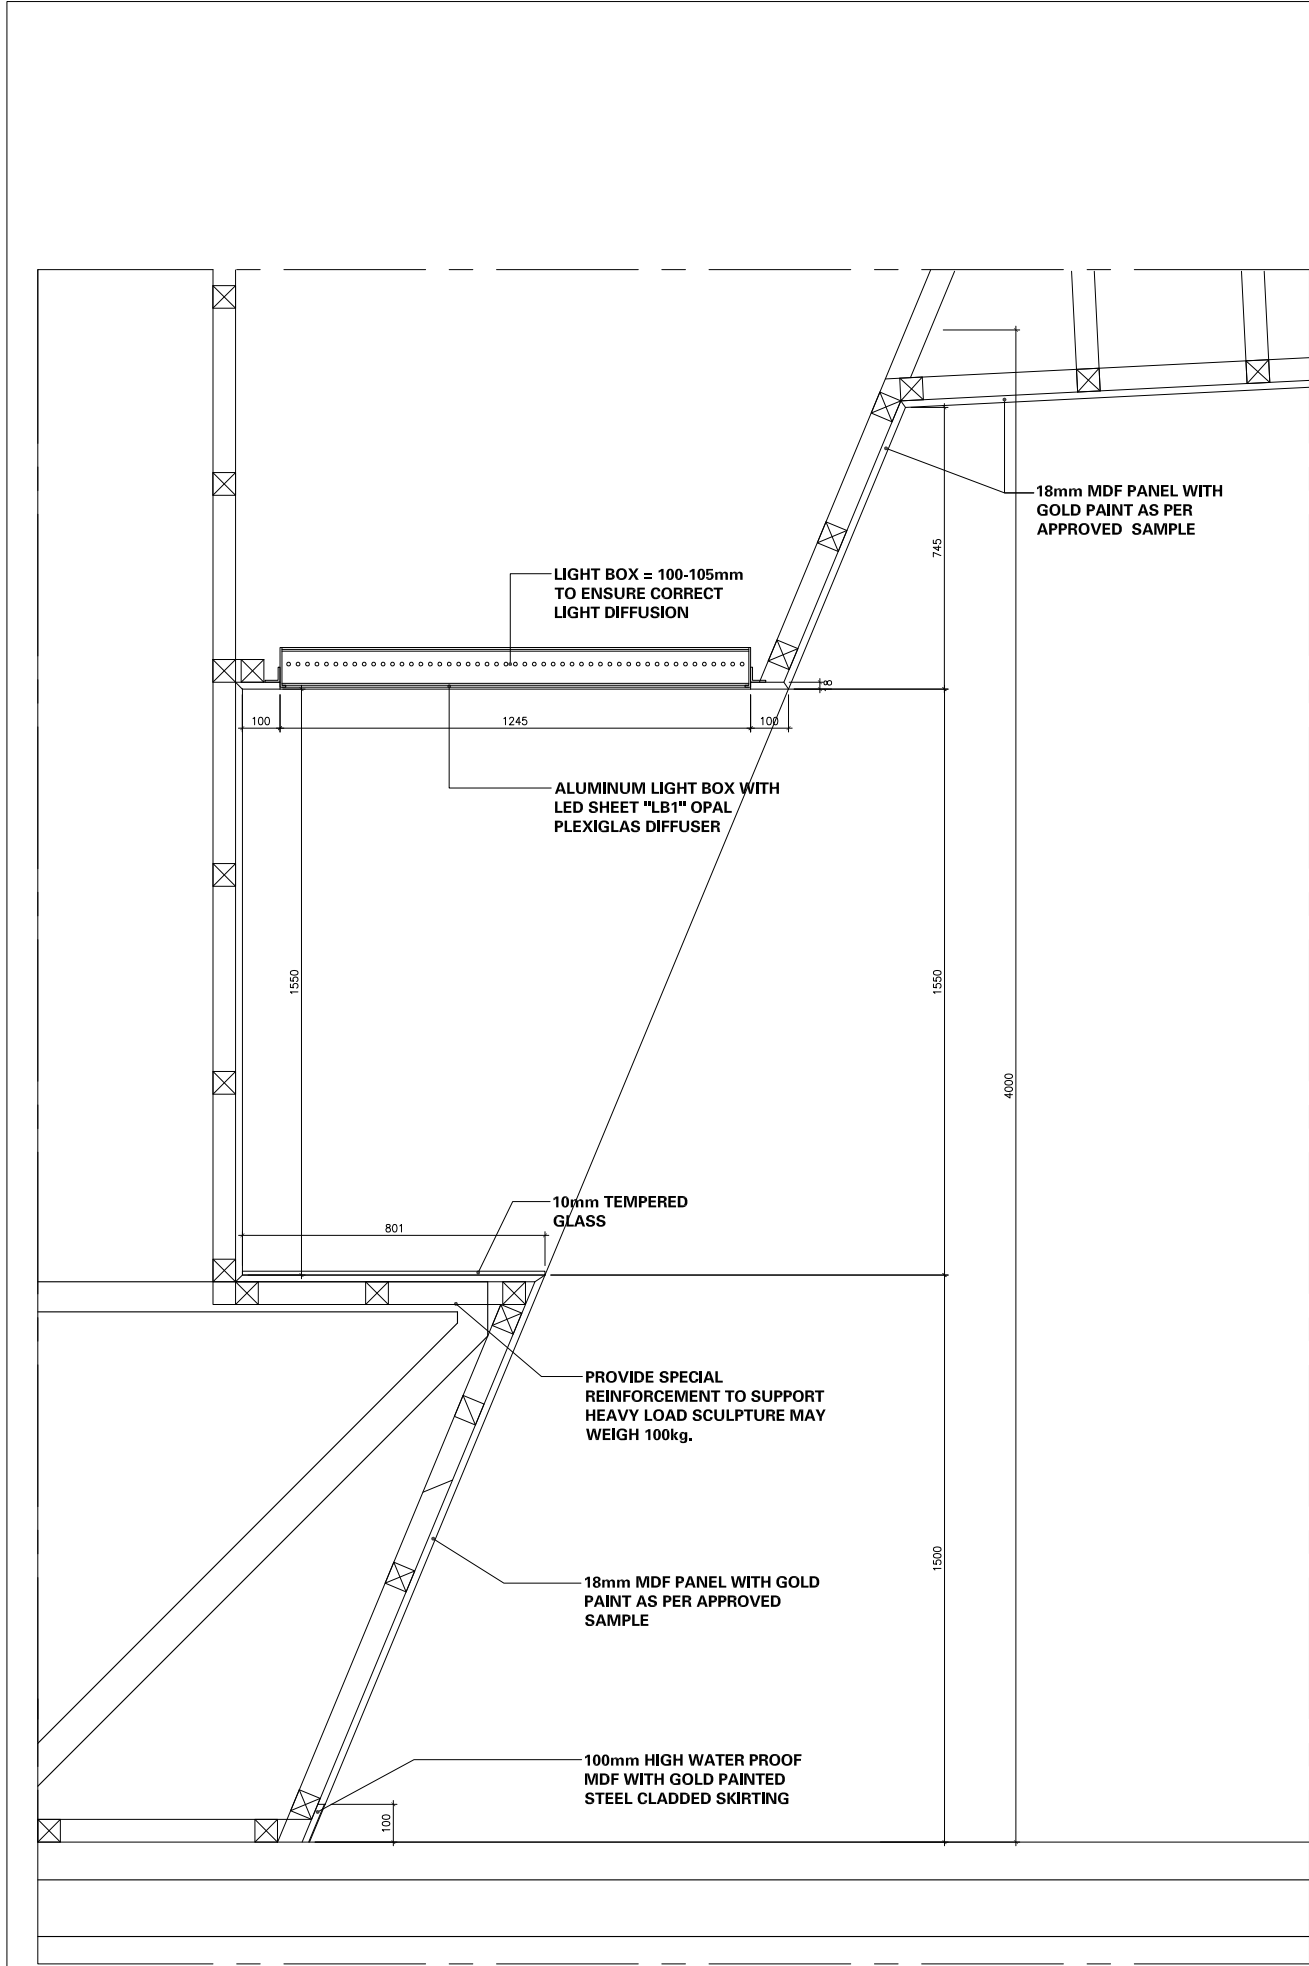

2 SECTION - A
SCALE 1:10

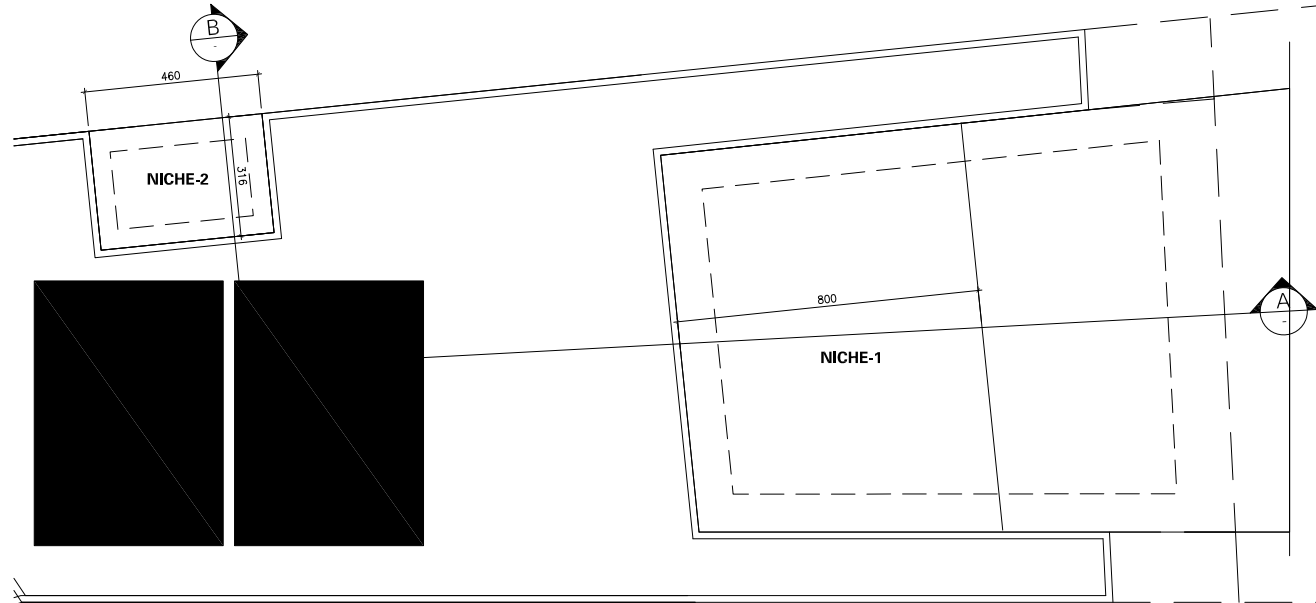

1 KEY PLAN
SCALE 1:10

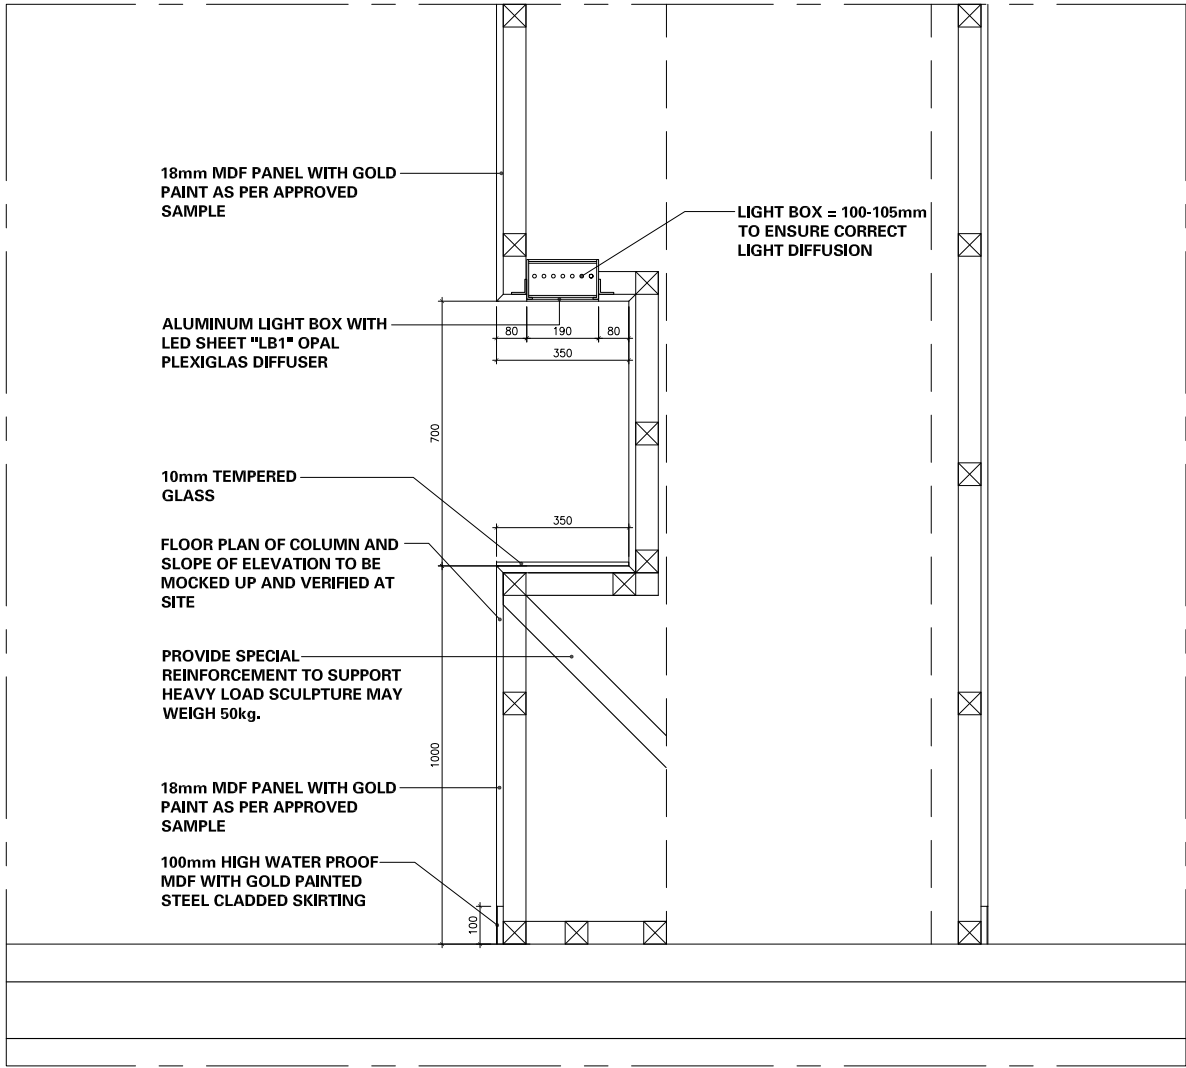

3 SECTION - B
SCALE 1:10

GENERAL NOTES

1. This drawing shall be read in conjunction with all other relevant architectural, structural & electrical drawings including those of other consultants.
2. It is the responsibility of contractors & manufacturers to check all relevant site dimensions prior to the start of construction or manufacture.
3. All materials and components must be installed on site in accordance with manufacturer's instructions, shop drawings and standard details.
4. All dimensions are in millimeters unless noted otherwise.
5. Full working drawings, specifications and samples are to be provided by Contractor/Supplier for approval prior to manufacture.


KEY PLAN


A	GENRAL REV.	MP	AM	SM	2022.11.27
X	INITIAL ISSUE	AC	AM	SM	2022.11.14
REV.#	GENERAL NOTES	DRAWN BY	CHECKED BY	APPROVED BY	DATE
PROJECT TITLE				REFERENCE	
RIC - RIYADH				RIC01 G	

DRAWING TITLE			
NICHE-1 & 2 DEATAILS			
DRAWING NUMBER			REVISION
ID-407			
SCALE	FORMAT	ADDITIONAL NOTES	DESIGN DEVELOPMENT
1:10	A1		

SIMA MALAK + ALSSAMOURE
DESIGN ASSOCIATES
P.O. Box 15707 - Riyadh 11454 KSA
Tel. 01 441 4963 - Fax. 01 441 3867
simals@simals.com

©SIMA MALAK + ALSSAMOURE DESIGN ASSOCIATES (شركة) 2003
This document including all drawing and text is the property and
copyright of SIMA MALAK + ALSSAMOURE DESIGN ASSOCIATES for
use solely with respect to this Project and shall not be copied or
reproduced by any means except by agreement in writing from
SIMA MALAK + ALSSAMOURE DESIGN ASSOCIATES.

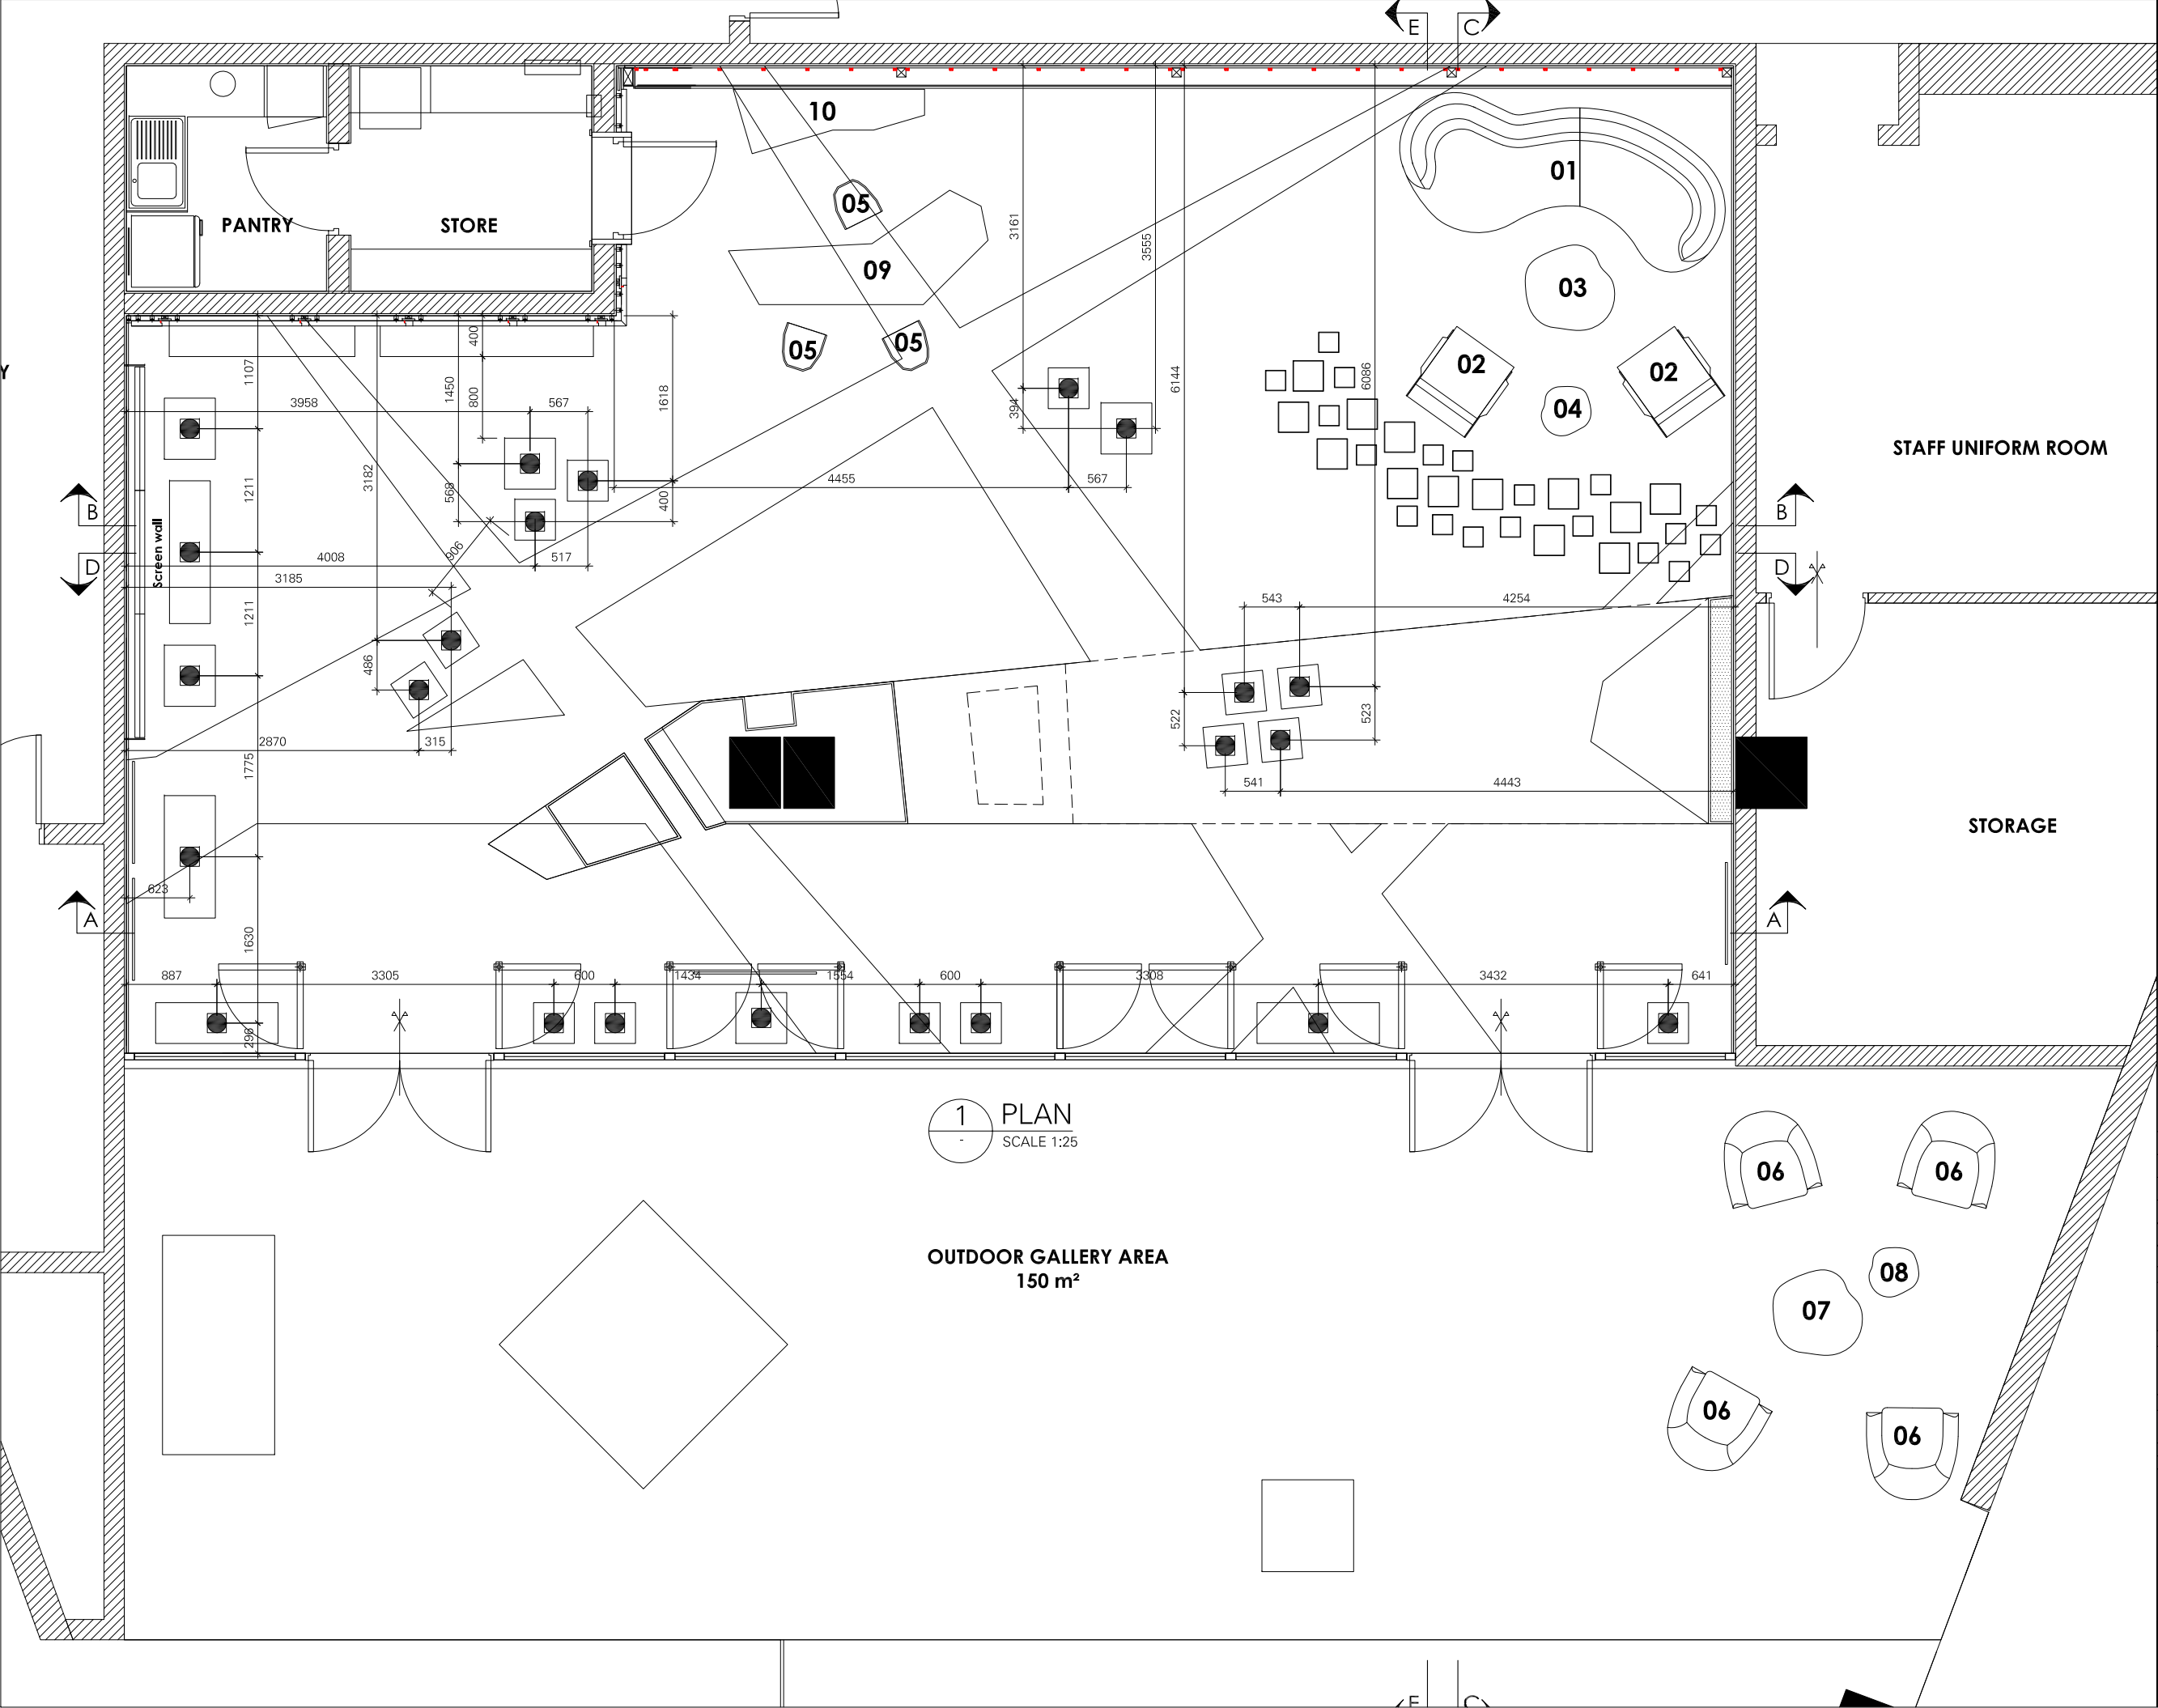

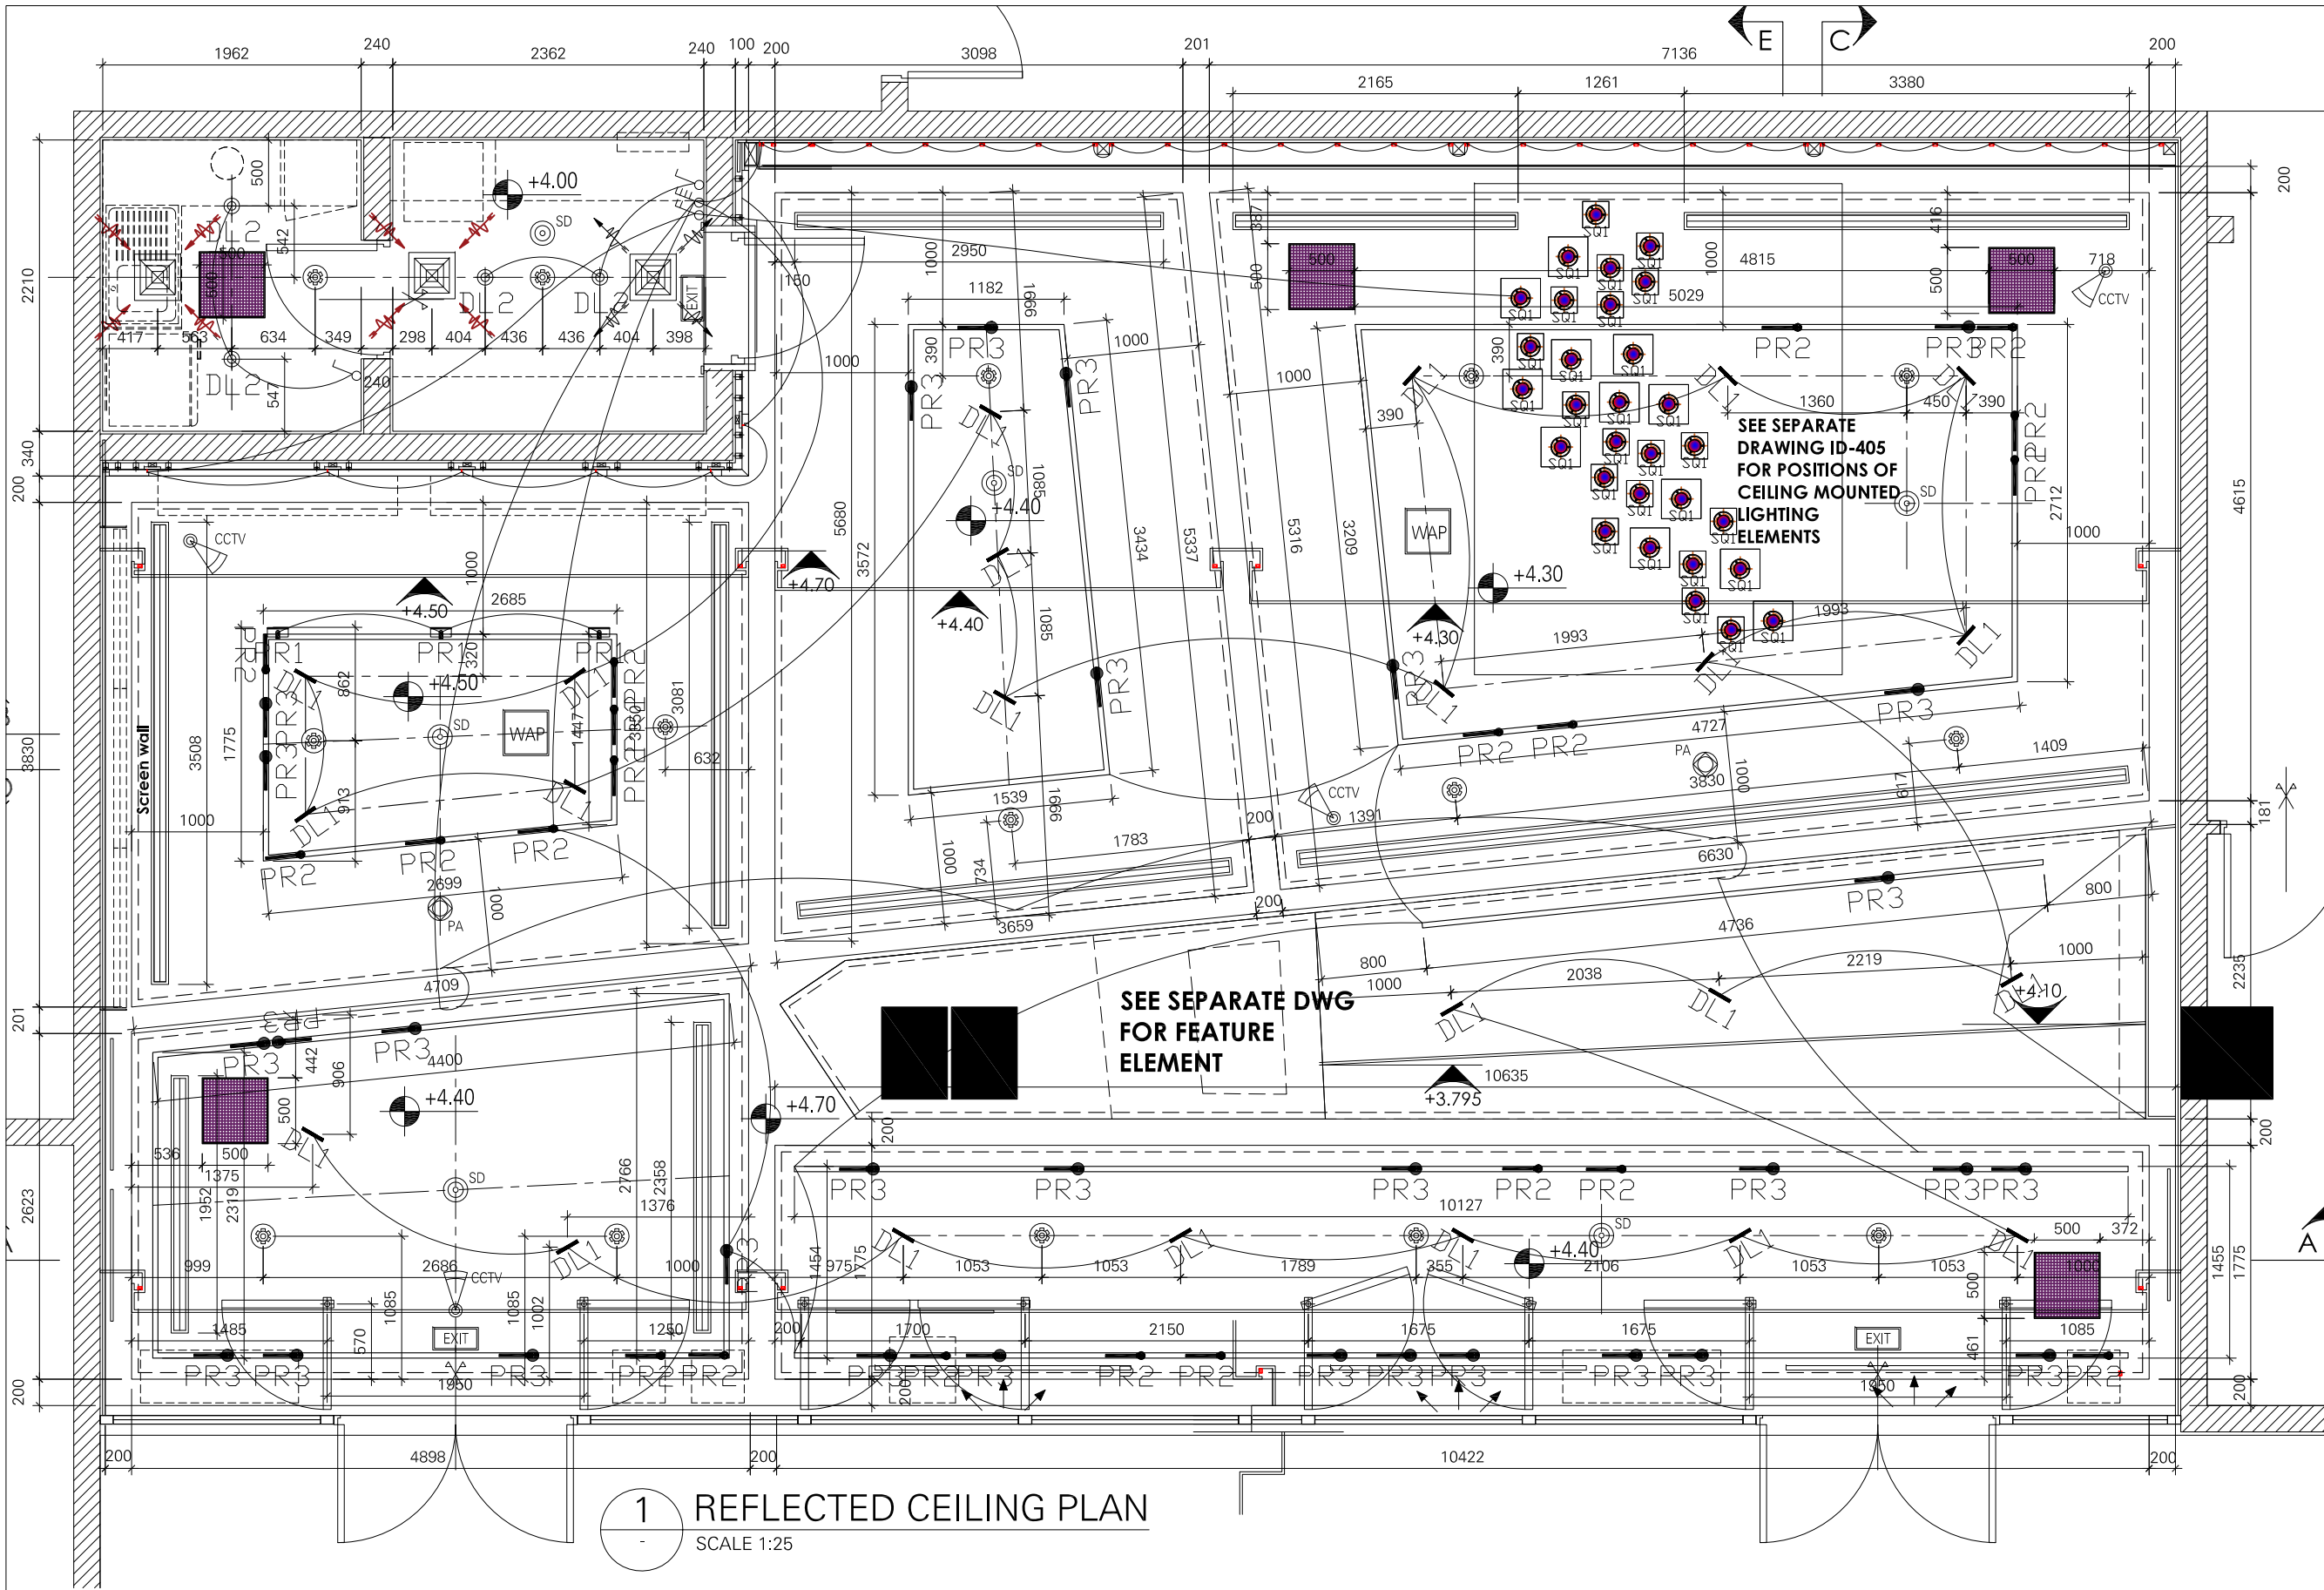


1 REFLECTED CEILING PLAN
SCALE 1:25

GENERAL NOTES


1. This drawing shall be read in conjunction with all other relevant architectural, structural & electrical drawings including those of other consultants.
2. It is the responsibility of contractors & manufacturers to check all relevant site dimensions prior to the start of construction or manufacture.
3. All materials and components must be installed on site in accordance with manufacturer's instructions, shop drawings and standard details.
4. All dimensions are in millimeters unless noted otherwise.
5. Full working drawings, specifications and samples are to be provided by Contractor/Supplier for approval prior to manufacture.

- LEGEND:
- 1 Gang Switch
 - 2 Gang Switch
 - 4 Gang Switch

TYPICAL LAYOUT OF SWITCHES

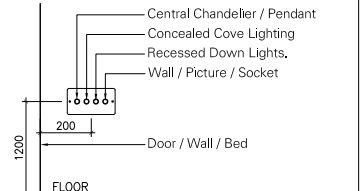

TYPICAL LAYOUT OF MULTIPLE FACE PLATE / SWITCHES

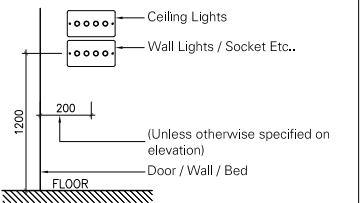


KEY PLAN

INITIAL ISSUE					AC	AM	SM	2022.11.16
REV.#	GENERAL NOTES	DRAWN BY	CHECKED BY	APPROVED BY	DATE			
PROJECT TITLE								REFERENCE
RIC - RIYADH								RIC01 G
DRAWING TITLE								
LIGHTING LAYOUT (PART-1)								
DRAWING NUMBER								REVISION
E-201								
SCALE	FORMAT	ADDITIONAL NOTES	DESIGN DEVELOPMENT					
1:25	A1							

SIMA MALAK + ALSSAMOURE
DESIGN ASSOCIATES

P.O. Box 15707 - Riyadh 11454 KSA
Tel. 01 441 4963 - Fax. 01 441 3867
simals@simals.com

©SIMA MALAK + ALSSAMOURE DESIGN ASSOCIATES () 2003
This document including all drawing and text is the property and copyright of SIMA MALAK + ALSSAMOURE DESIGN ASSOCIATES for use solely with respect to this Project and shall not be copied or reproduced by any means except by agreement in writing from SIMA MALAK + ALSSAMOURE DESIGN ASSOCIATES.

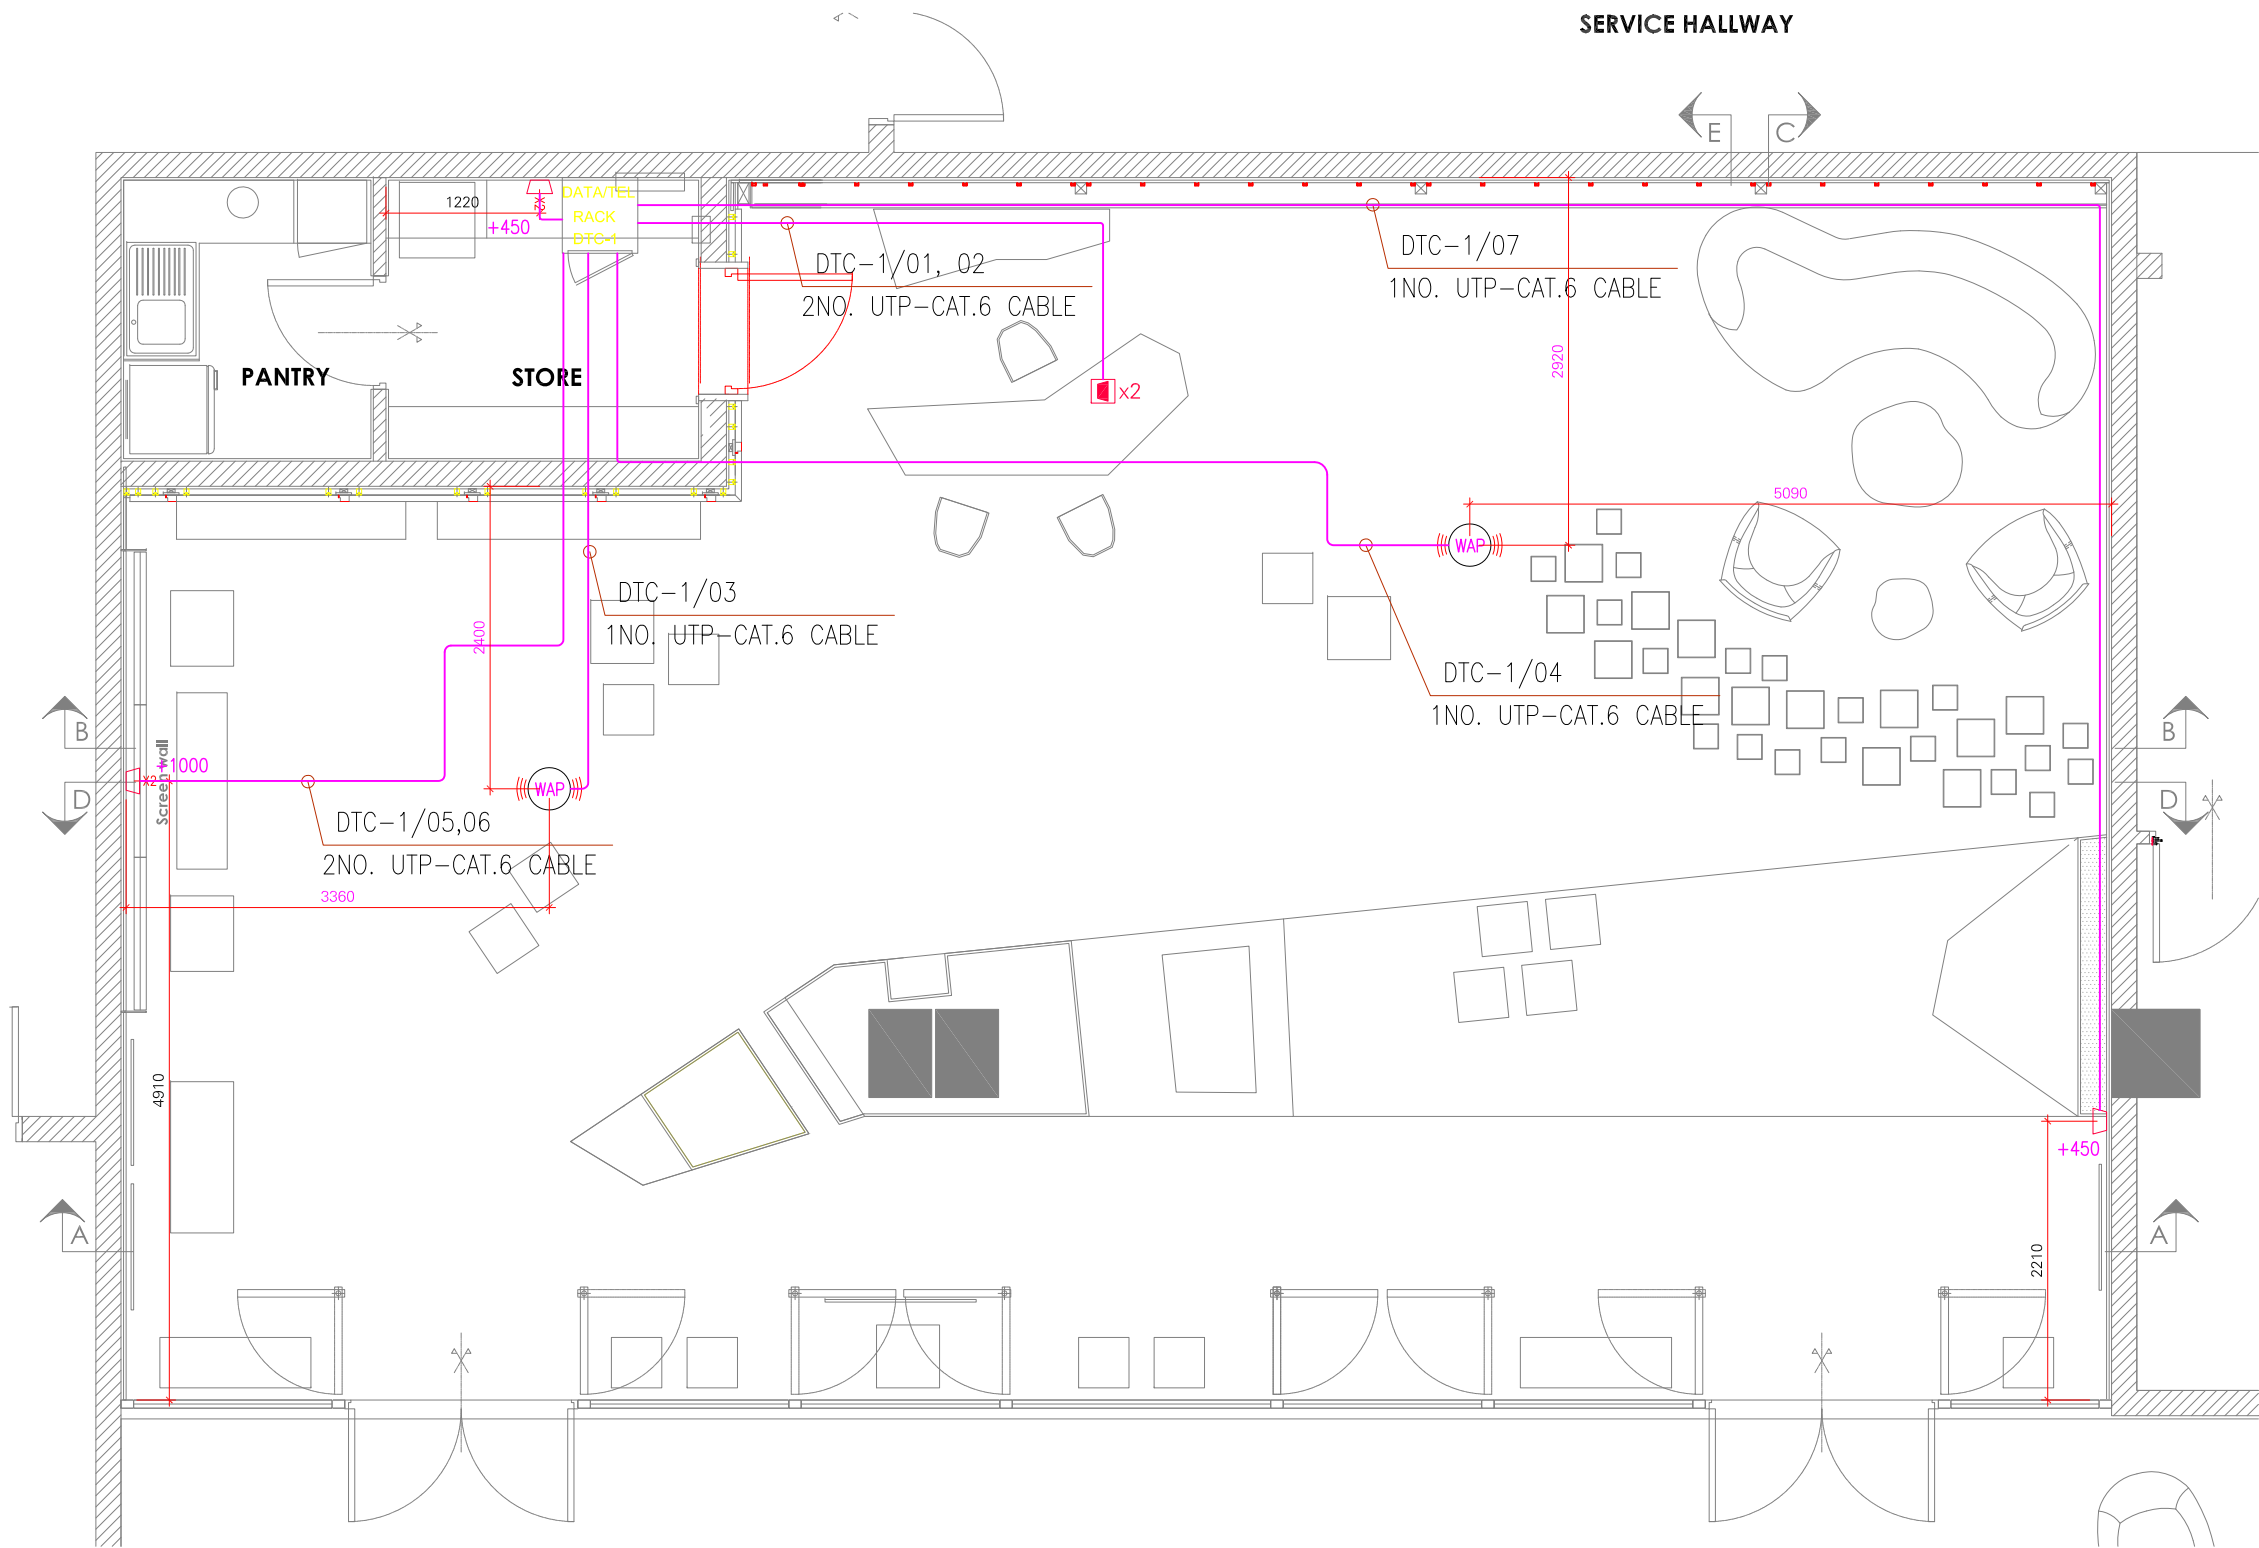

GENERAL NOTES

1. This drawing shall be read in conjunction with all other relevant architectural, structural & electrical drawings including those of other consultants.
2. It is the responsibility of contractors & manufacturers to check all relevant site dimensions prior to the start of construction or manufacture.
3. All materials and components must be installed on site in accordance with manufacturer's instructions, shop drawings and standard details.
4. All dimensions are in millimeters unless noted otherwise.
5. Full working drawings, specifications and samples are to be provided by Contractor/Supplier for approval prior to manufacture.

LEGEND:

SYMBOL	DISCRIPTION
	Wall socket power single
	Wall socket power double
	Wall socket power above counter - single
	Wall socket power above counter - double
	Wall socket DATA
	Floor Box (x2 Power)
	Floor Box (x2 Data)
	CEILING MOUNTED WI FI ACCESS POINT
	WALL MOUNTED DOUBLE DATA
	DATA RACK

KEY PLAN

☒	INITIAL ISSUE	CAD	AM	SM	2022.11.16
REV.#	GENERAL NOTES	DRAWN BY	CHECKED BY	APPROVED BY	DATE

PROJECT TITLE	REFERENCE
---------------	-----------

RIC - RIYADH	RIC01
	G

DRAWING TITLE

DATA SYSTEM LAYOUT

DRAWING NUMBER	REVISION
----------------	----------

EL-102	-
--------	---

SCALE	FORMAT	ADDITIONAL NOTES	DESIGN DEVELOPMENT
-------	--------	------------------	--------------------


1:30	A1		
------	----	--	--



**SIMA MALAK + ALSSAMOURE
DESIGN ASSOCIATES**

P.O. Box 15707 - Riyadh 11454 KSA
Tel. 01 441 4963 - Fax. 01 441 3867
simals@simals.com

©SIMA MALAK + ALSSAMOURE DESIGN ASSOCIATES (شركة) 2003
This document including all drawing and text is the property and
copyright of SIMA MALAK + ALSSAMOURE DESIGN ASSOCIATES for
use solely with respect to this Project and shall not be copied or
reproduced by any means except by agreement in writing from
SIMA MALAK + ALSSAMOURE DESIGN ASSOCIATES.

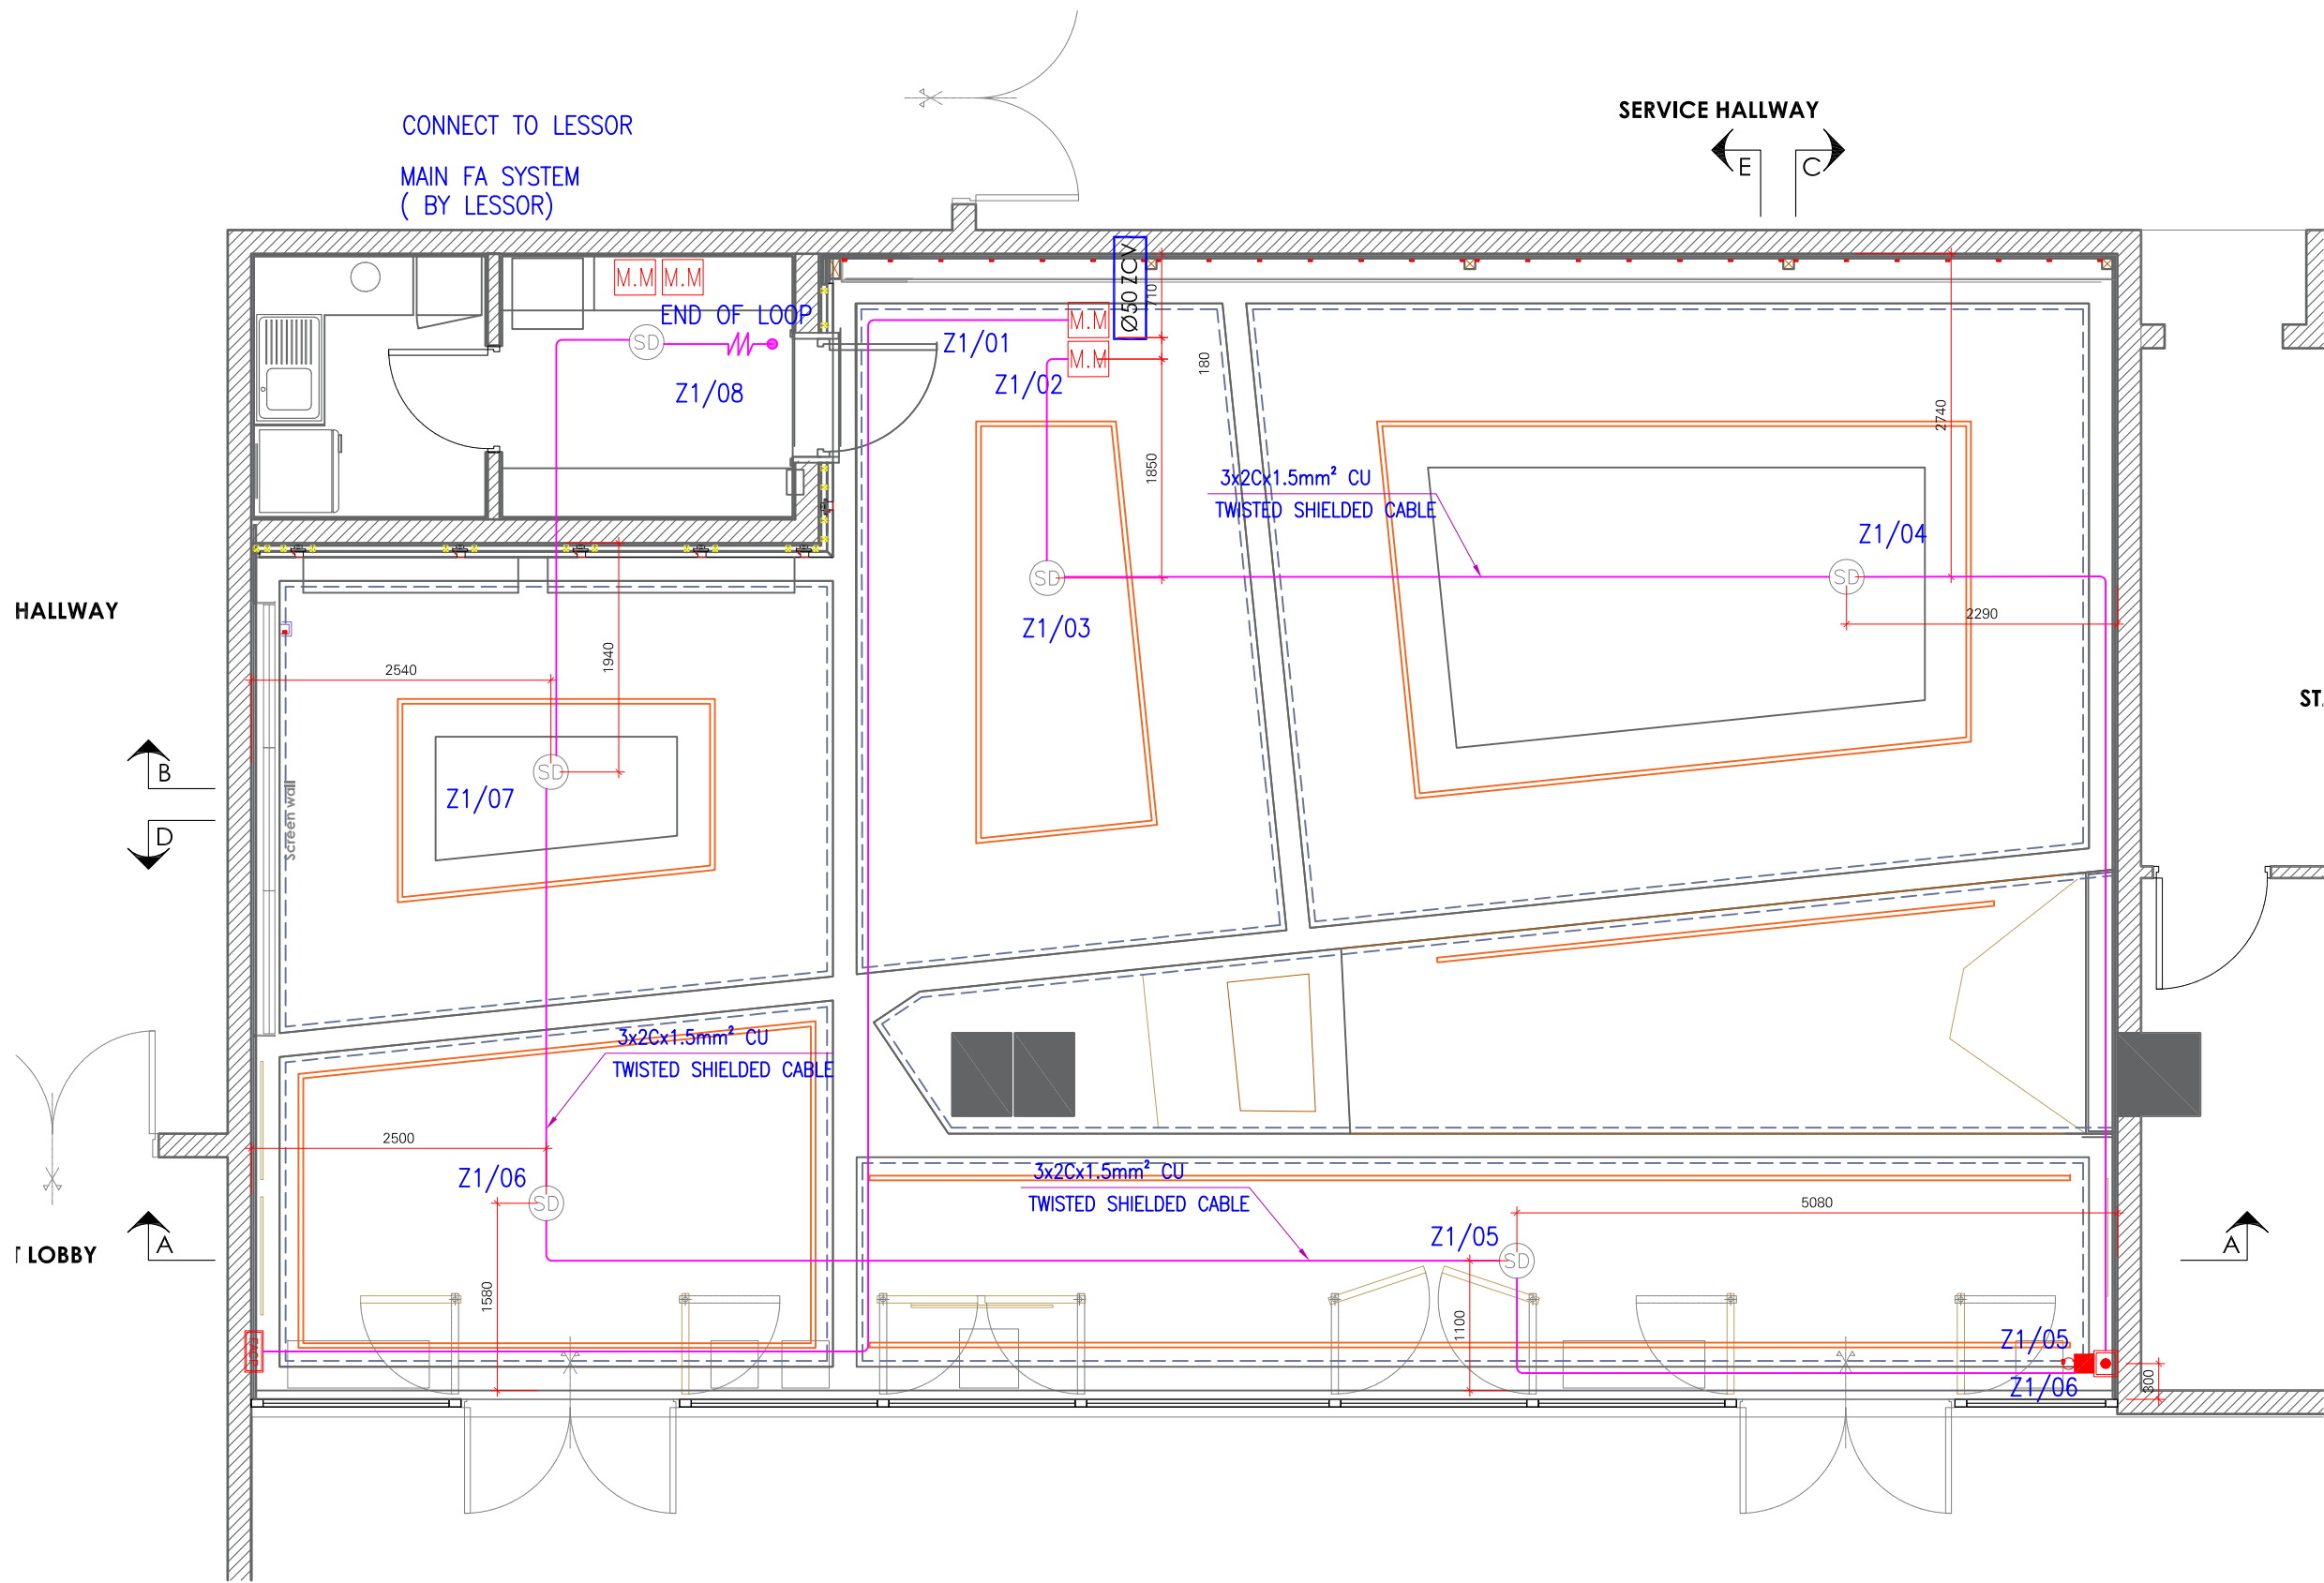

- GENERAL NOTES**
1. This drawing shall be read in conjunction with all other relevant architectural, structural & electrical drawings including those of other consultants.
 2. It is the responsibility of contractors & manufacturers to check all relevant site dimensions prior to the start of construction or manufacture.
 3. All materials and components must be installed on site in accordance with manufacturer's instructions, shop drawings and standard details.
 4. All dimensions are in millimeters unless noted otherwise.
 5. Full working drawings, specifications and samples are to be provided by Contractor/Supplier for approval prior to manufacture.

LEGEND:


SYMBOL	DISCRIPTION
	CONVENTIONAL FIRE ALARM CONTROL PANEL
	SMOKE DETECTOR
	MONITOR MODULE (CEILING MOUNTED)
	END OF ZONE RESISTANCE
	FIRE ALARM CABLE 2X1.5MM2

KEY PLAN

A	GEN. REV.	CAD	AM	SM	2022.11.17
X	INITIAL ISSUE	CAD	AM	SM	2022.11.16
REV.#	GENERAL NOTES	DRAWN BY	CHECKED BY	APPROVED BY	DATE
PROJECT TITLE					REFERENCE
RIC - RIYADH					RIC01 G

DRAWING TITLE			
FIRE ALARM SYSTEM LAYOUT			
DRAWING NUMBER			REVISION
EL-103			A
SCALE	FORMAT	ADDITIONAL NOTES	DESIGN DEVELOPMENT
1:30	A1		
			
SIMA MALAK + ALSSAMOURE			
DESIGN ASSOCIATES			
P.O. Box 15707 - Riyadh 11454 KSA			
Tel. 01 441 4963 - Fax. 01 441 3867			
simals@simals.com			

©SIMA MALAK + ALSSAMOURE DESIGN ASSOCIATES (شركة) 2003
This document including all drawing and text is the property and copyright of SIMA MALAK + ALSSAMOURE DESIGN ASSOCIATES for use solely with respect to this Project and shall not be copied or reproduced by any means except by agreement in writing from SIMA MALAK + ALSSAMOURE DESIGN ASSOCIATES.

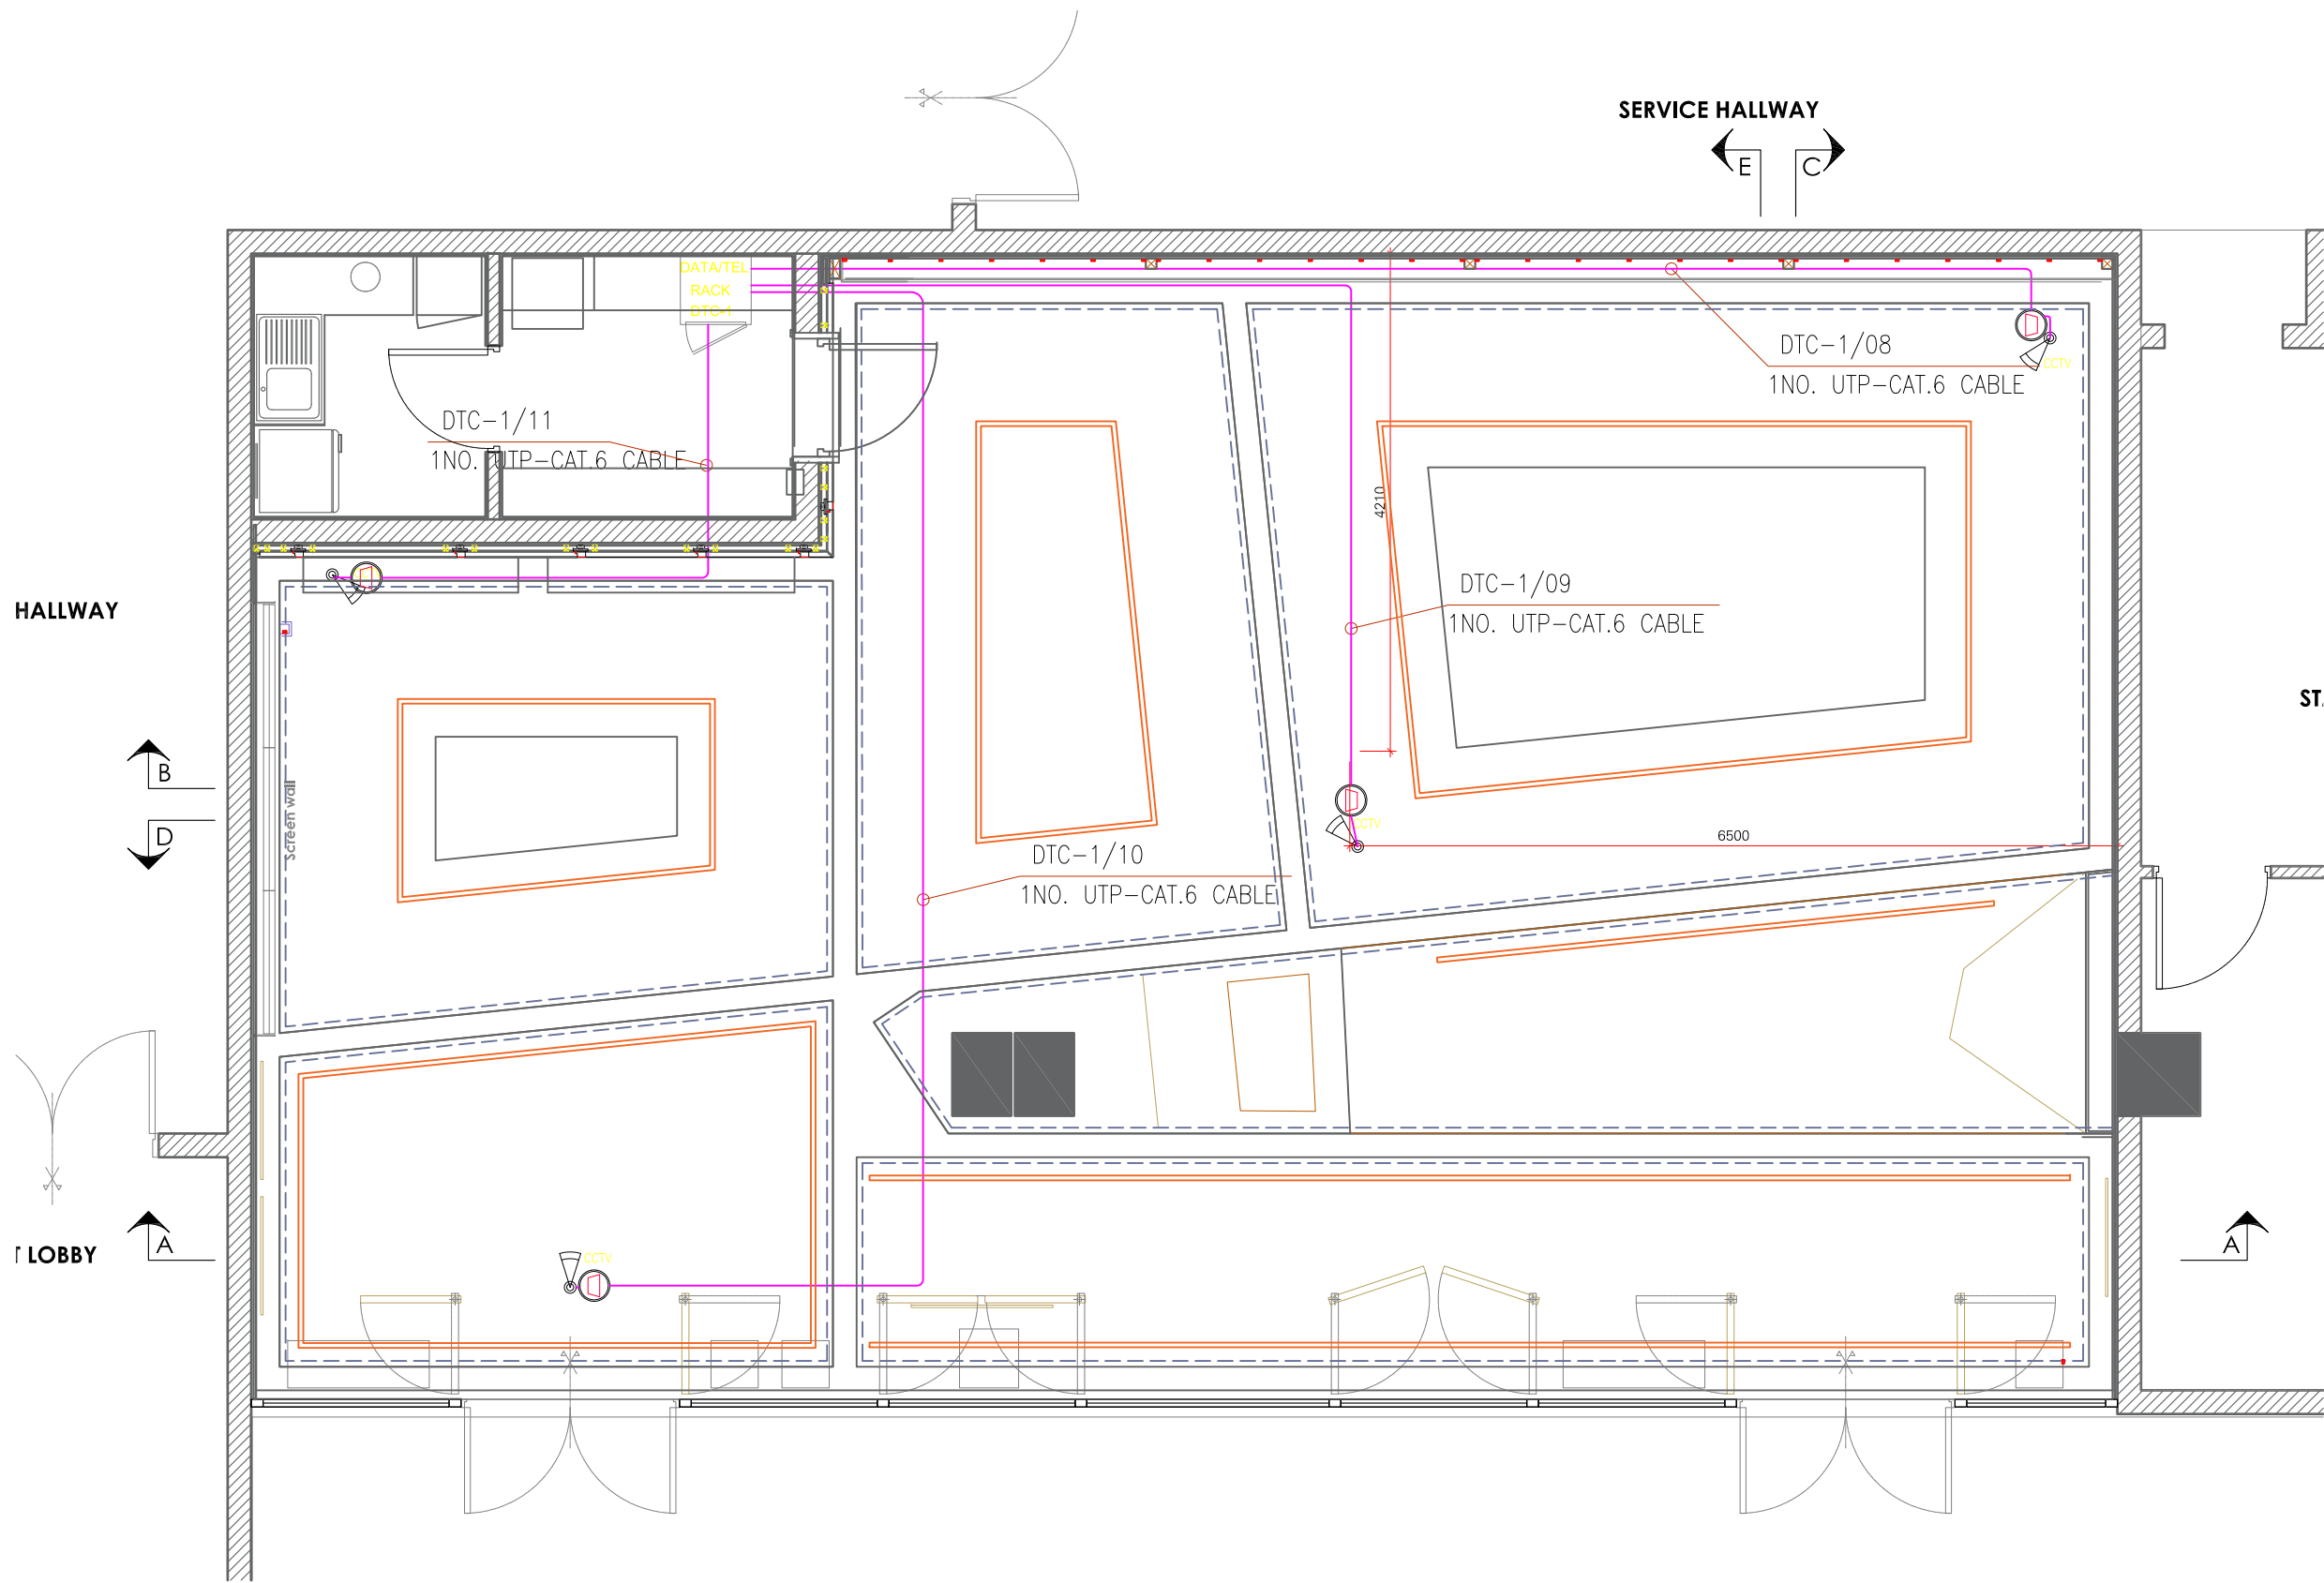

- GENERAL NOTES**
1. This drawing shall be read in conjunction with all other relevant architectural, structural & electrical drawings including those of other consultants.
 2. It is the responsibility of contractors & manufacturers to check all relevant site dimensions prior to the start of construction or manufacture.
 3. All materials and components must be installed on site in accordance with manufacturer's instructions, shop drawings and standard details.
 4. All dimensions are in millimeters unless noted otherwise.
 5. Full working drawings, specifications and samples are to be provided by Contractor/Supplier for approval prior to manufacture.

LEGEND:

SYMBOL	DISCRIPTION
	DATA RACK
	CEILING MOUNTED DATA OUTLET FOR CCTV
	CEILING MOUNTED IP CCTV CAMERA
	CAT.6 CABLE


KEY PLAN

A	GEN REV.	CAD	AM	SM	2022.11.17
X	INITIAL ISSUE	CAD	AM	SM	2022.11.16
REV.#	GENERAL NOTES	DRAWN BY	CHECKED BY	APPROVED BY	DATE
PROJECT TITLE					REFERENCE
RIC - RIYADH					RIC01 G

DRAWING TITLE			
IP CCTV SYSTEM LAYOUT			
DRAWING NUMBER			REVISION
EL-104			A
SCALE	FORMAT	ADDITIONAL NOTES	DESIGN DEVELOPMENT
1:30	A1		

**SIMA MALAK + ALSSAMOURE
DESIGN ASSOCIATES**
P.O. Box 15707 - Riyadh 11454 KSA
Tel. 01 441 4963 - Fax. 01 441 3867
simals@simals.com

©SIMA MALAK + ALSSAMOURE DESIGN ASSOCIATES (شركة) 2003
This document including all drawing and text is the property and
copyright of SIMA MALAK + ALSSAMOURE DESIGN ASSOCIATES for
use solely with respect to this Project and shall not be copied or
reproduced by any means except by agreement in writing from
SIMA MALAK + ALSSAMOURE DESIGN ASSOCIATES.

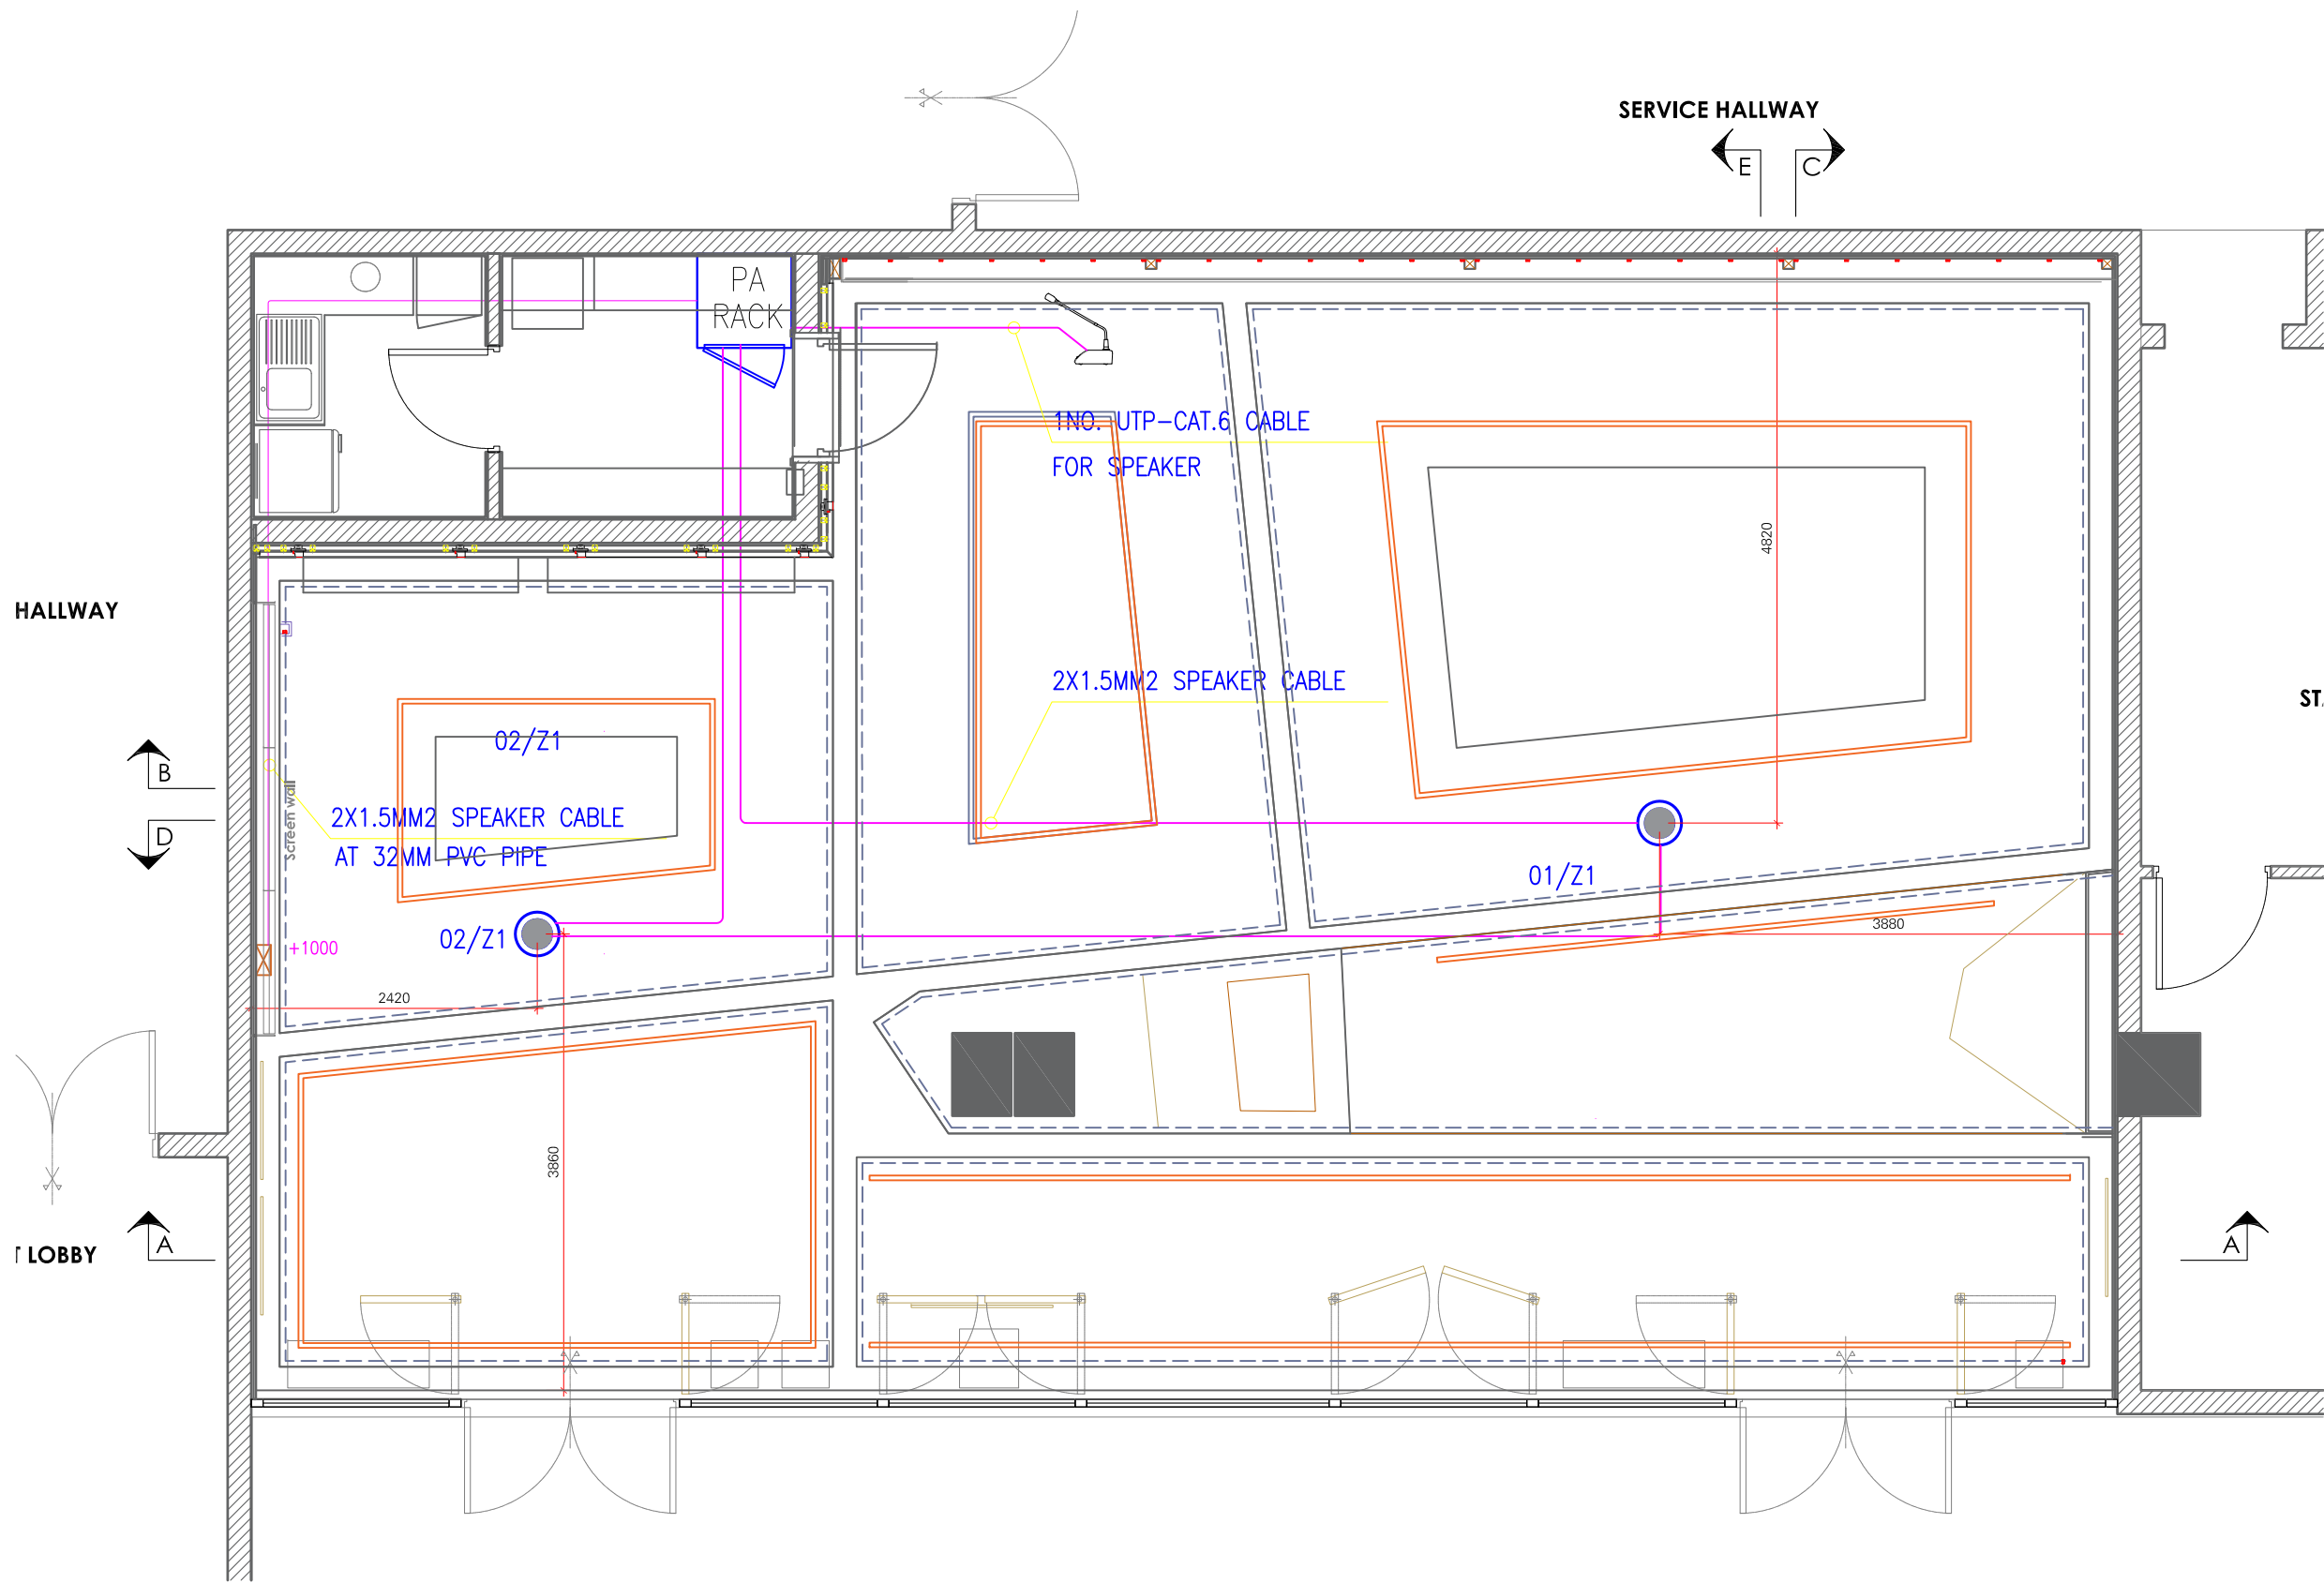

- GENERAL NOTES**
1. This drawing shall be read in conjunction with all other relevant architectural, structural & electrical drawings including those of other consultants.
 2. It is the responsibility of contractors & manufacturers to check all relevant site dimensions prior to the start of construction or manufacture.
 3. All materials and components must be installed on site in accordance with manufacturer's instructions, shop drawings and standard details.
 4. All dimensions are in millimeters unless noted otherwise.
 5. Full working drawings, specifications and samples are to be provided by Contractor/Supplier for approval prior to manufacture.

LEGEND:

SYMBOL	DISCRIPTION
	PUBLIC ADRESS RACK
	CEILING MOUNTED 6W SPEAKER
	2X1.5MM2 PUBLIC ADDRESS CABLE
	PULL BOX
	PUBLIC ADDRESS MICROPHONE


KEY PLAN

A	GEN. REV.	CAD	AM	SM	2022.11.17
X	INITIAL ISSUE	CAD	AM	SM	2022.11.16
REV.#	GENERAL NOTES	DRAWN BY	CHECKED BY	APPROVED BY	DATE
PROJECT TITLE					REFERENCE
RIC - RIYADH					RIC01 G

DRAWING TITLE			
PA SYSTEM LAYOUT			
DRAWING NUMBER			REVISION
EL-105			A
SCALE	FORMAT	ADDITIONAL NOTES	DESIGN DEVELOPMENT
1:30	A1		

**SIMA MALAK + ALSSAMOURE
DESIGN ASSOCIATES**
P.O. Box 15707 - Riyadh 11454 KSA
Tel. 01 441 4963 - Fax. 01 441 3867
simals@simals.com

©SIMA MALAK + ALSSAMOURE DESIGN ASSOCIATES (شركة) 2003
This document including all drawing and text is the property and copyright of SIMA MALAK + ALSSAMOURE DESIGN ASSOCIATES for use solely with respect to this Project and shall not be copied or reproduced by any means except by agreement in writing from SIMA MALAK + ALSSAMOURE DESIGN ASSOCIATES.

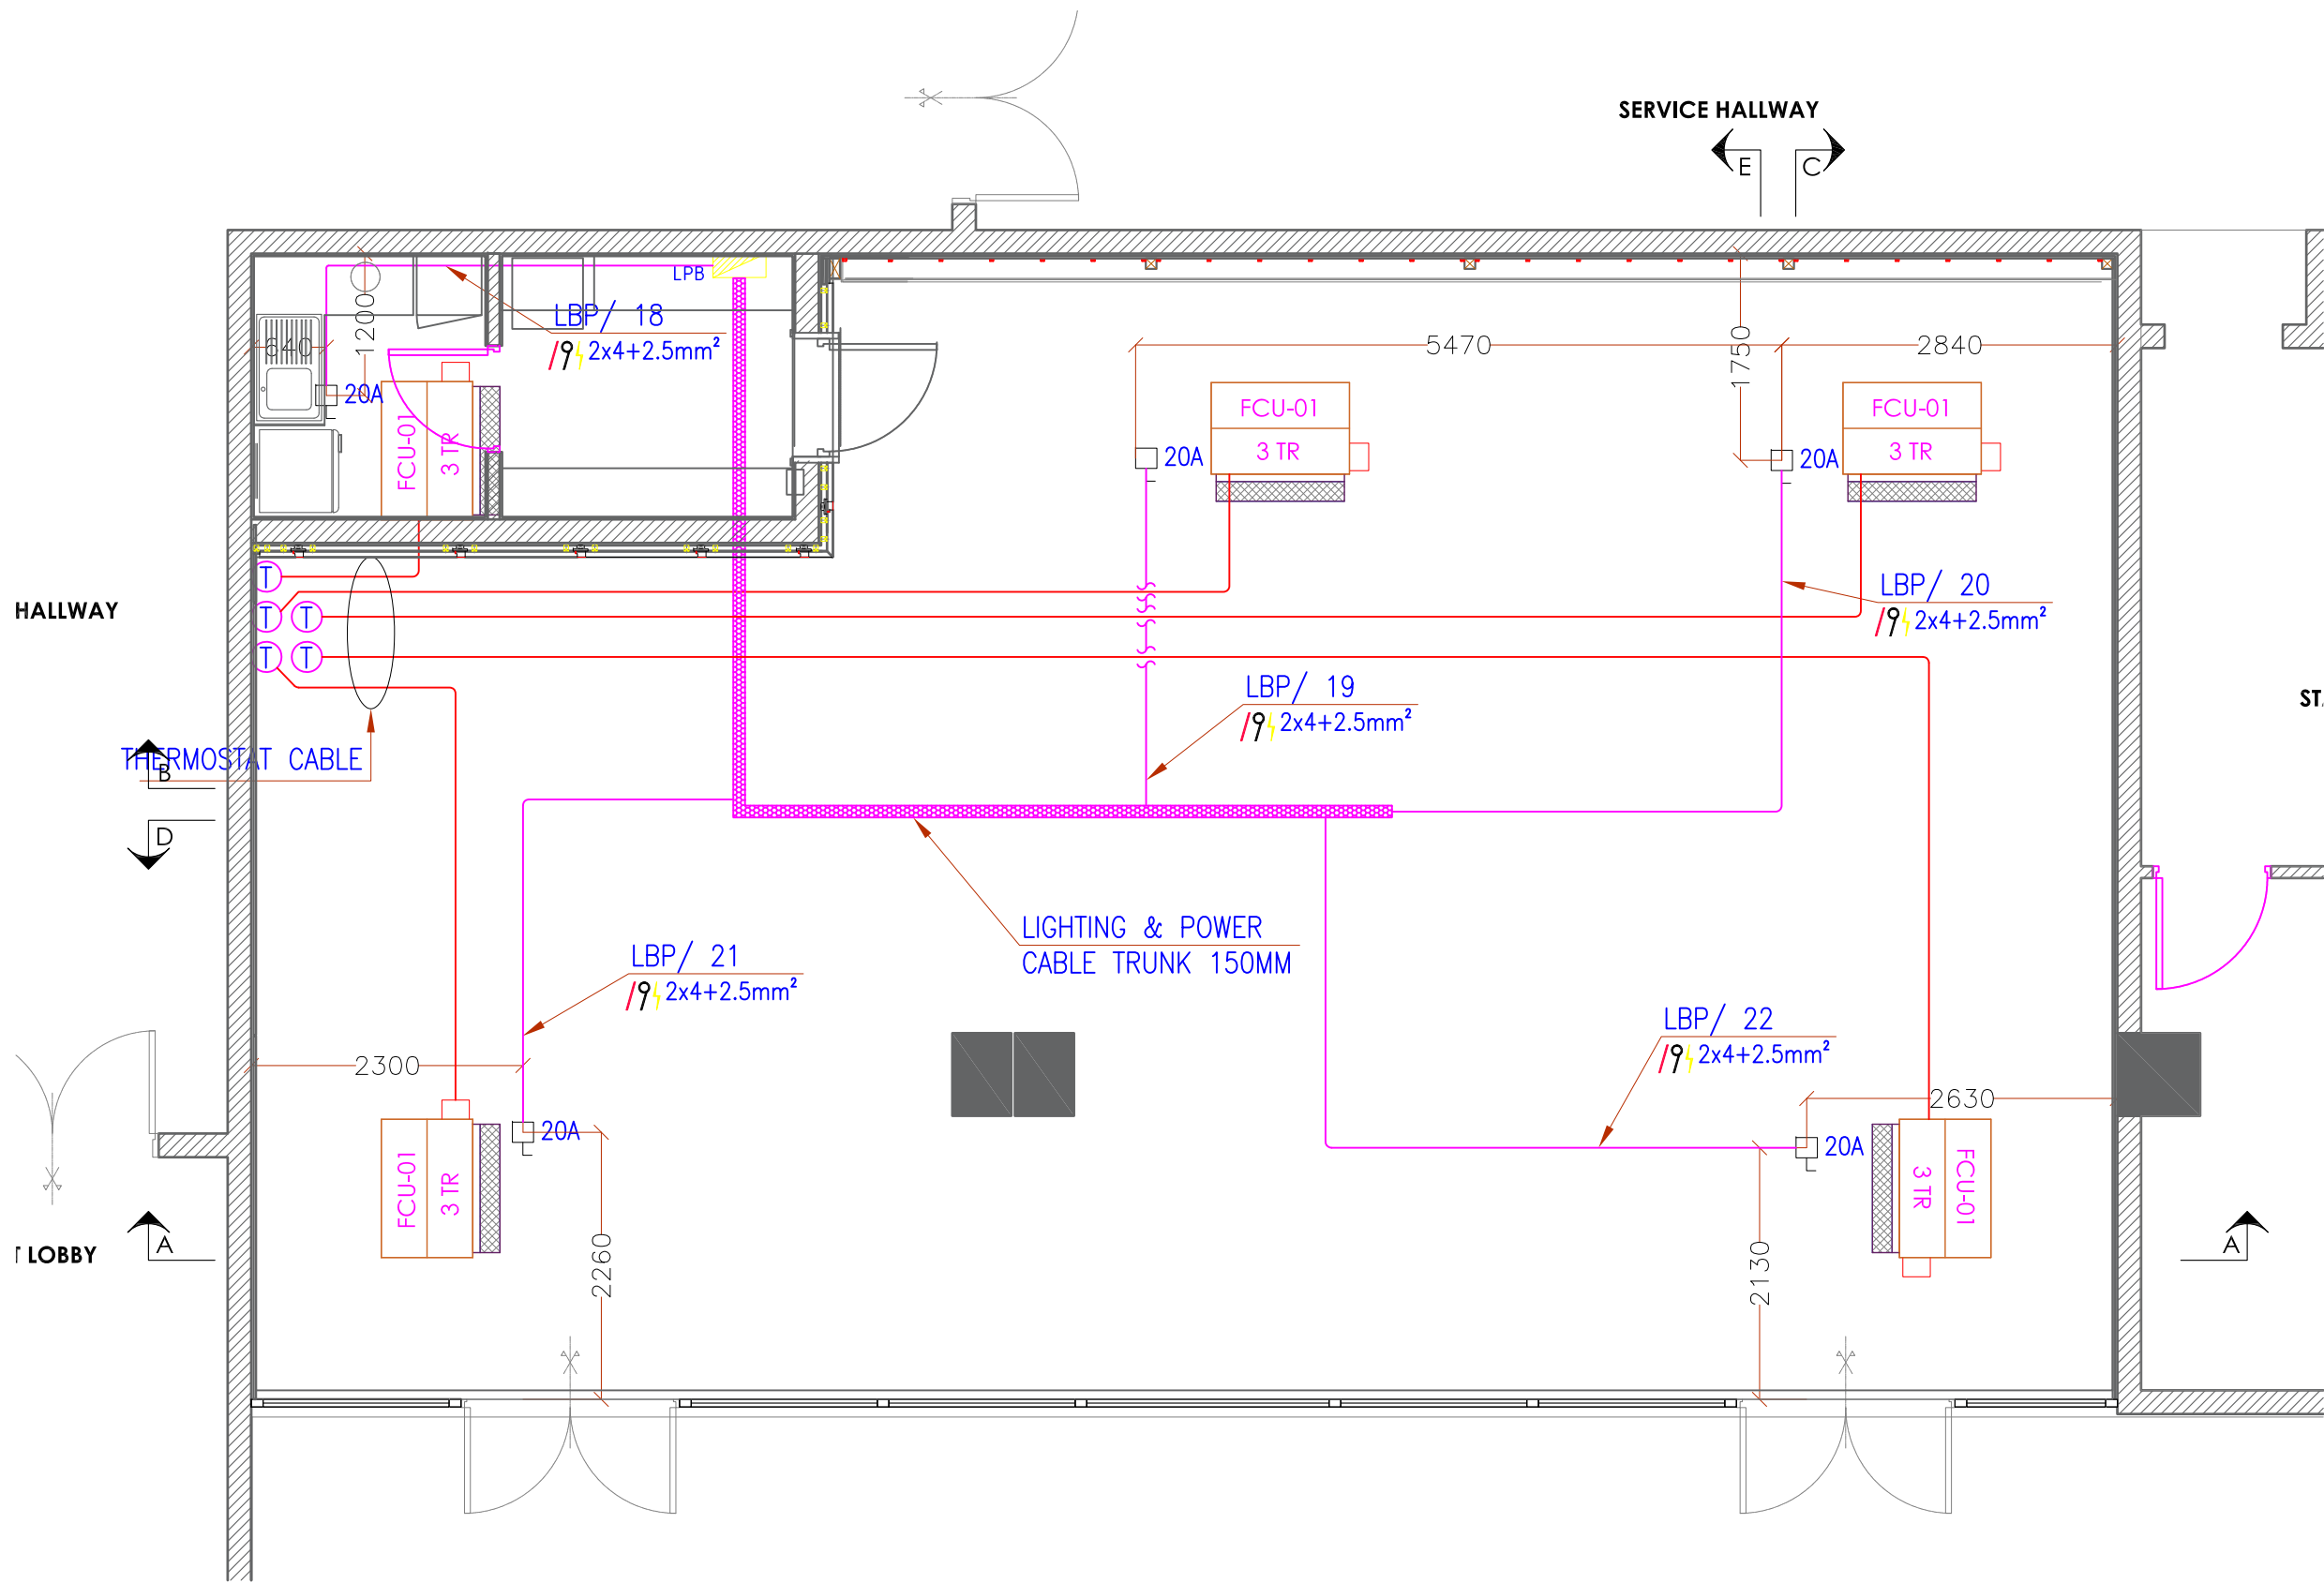

GENERAL NOTES

1. This drawing shall be read in conjunction with all other relevant architectural, structural & electrical drawings including those of other consultants.
2. It is the responsibility of contractors & manufacturers to check all relevant site dimensions prior to the start of construction or manufacture.
3. All materials and components must be installed on site in accordance with manufacturer's instructions, shop drawings and standard details.
4. All dimensions are in millimeters unless noted otherwise.
5. Full working drawings, specifications and samples are to be provided by Contractor/Supplier for approval prior to manufacture.

LEGEND:

SYMBOL	DISCRIPTION
	PUBLIC ADDRESS RACK
	CEILING MOUNTED 6W SPEAKER
	2X1.5MM² PUBLIC ADDRESS CABLE
	PULL BOX
	PUBLIC ADDRESS MICROPHONE

KEY PLAN

A	GEN. REV.	CAD	AM	SM	2022.11.17
X	INITIAL ISSUE	CAD	AM	SM	2022.11.16
REV.#	GENERAL NOTES	DRAWN BY	CHECKED BY	APPROVED BY	DATE

PROJECT TITLE	REFERENCE
RIC - RIYADH	RIC01 G


DRAWING TITLE
HVAC POWER SYSTEM PLAN

DRAWING NUMBER	REVISION
EL-106	A

SCALE	FORMAT	ADDITIONAL NOTES	DESIGN DEVELOPMENT
1:30	A1		

SIMA MALAK + ALSSAMOURE
DESIGN ASSOCIATES
P.O. Box 15707 - Riyadh 11454 KSA
Tel. 01 441 4963 - Fax. 01 441 3867
simals@simals.com

©SIMA MALAK + ALSSAMOURE DESIGN ASSOCIATES (شركة) 2003
This document including all drawing and text is the property and copyright of SIMA MALAK + ALSSAMOURE DESIGN ASSOCIATES for use solely with respect to this Project and shall not be copied or reproduced by any means except by agreement in writing from SIMA MALAK + ALSSAMOURE DESIGN ASSOCIATES.

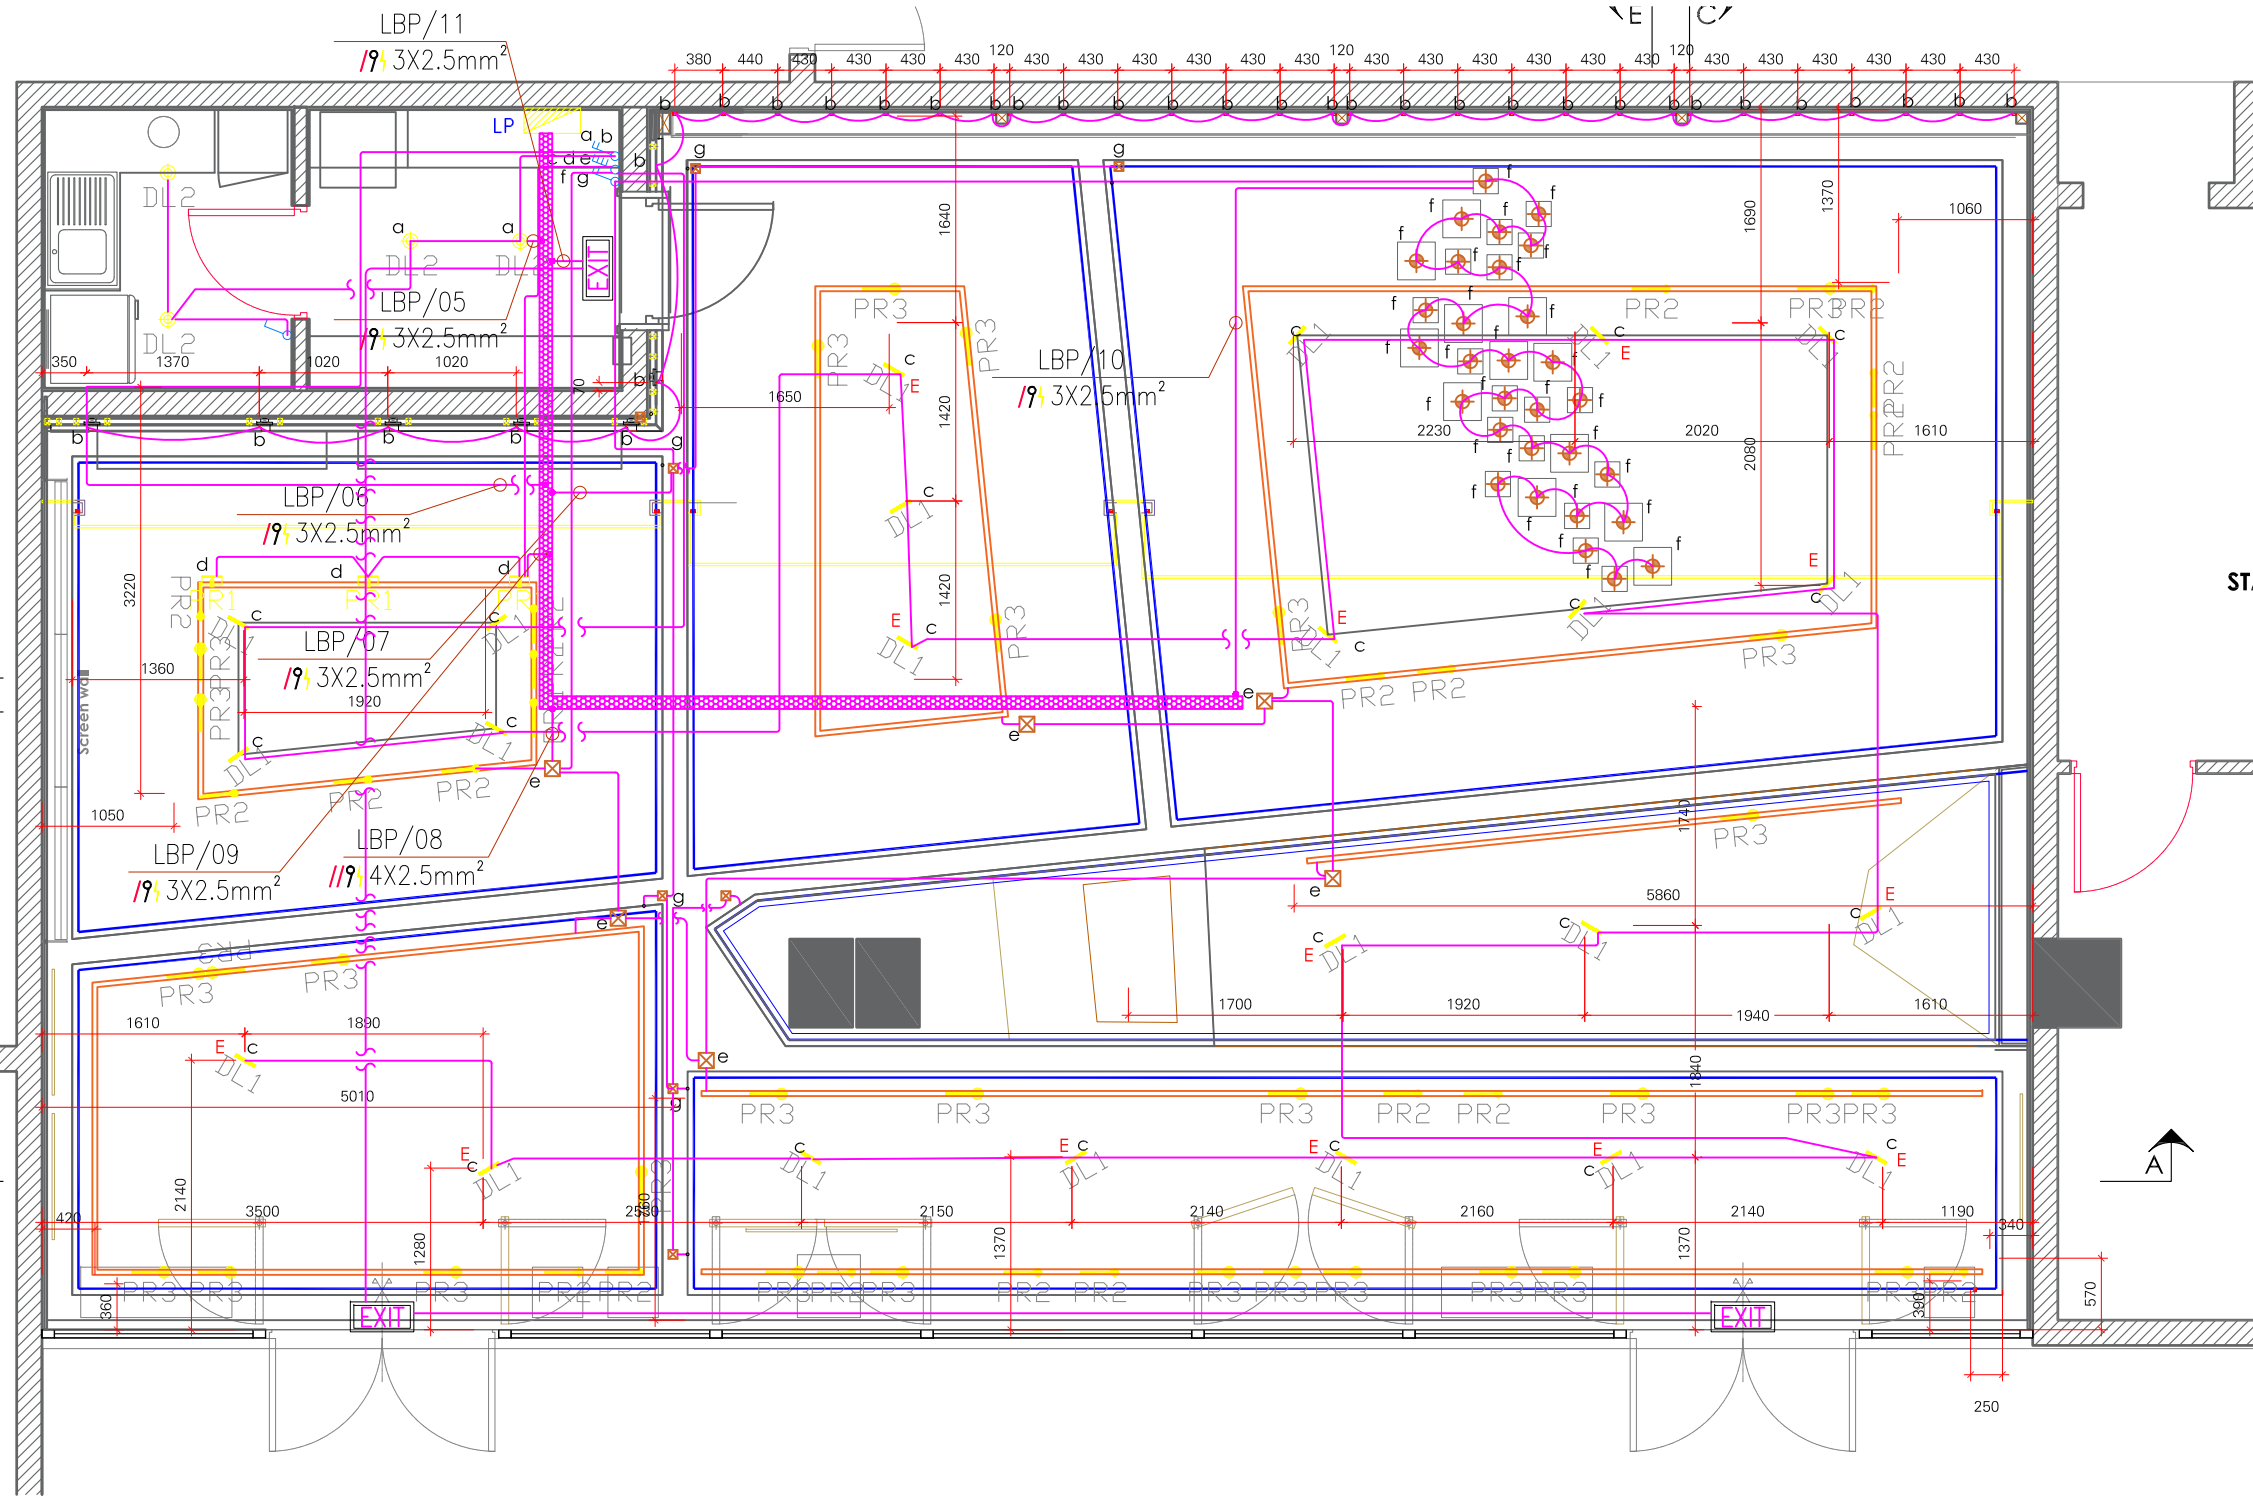

LEGEND

DL1		Small Rectangular Recessed LED downlight
DL1E		Emergency Recessed LED downlight
DL2		Recessed LED downlight with frame - wide beam
PR1		Rectangular adjustable projector on Track
PR2		Small circular adjustable projector on Track
PR3		Circular adjustable projector on Track
		Linear recessed power track with flange

PD1		Mini adjustable Spotlight
LR1		LEDs ribbon - average intensity
LR2		Flexible LEDs ribbon - low intensity
LB1		White Flexible LED sheet
LB2		RGBW Flexible LED sheet
SQ1		Circular recessed RGB LED projector (uplight and downlight mounting)
		Fire Exit Sign

GENERAL NOTES

1. This drawing shall be read in conjunction with all other relevant architectural, structural & electrical drawings including those of other consultants.
2. It is the responsibility of contractors & manufacturers to check all relevant site dimensions prior to the start of construction or manufacture.
3. All materials and components must be installed on site in accordance with manufacturer's instructions, shop drawings and standard details.
4. All dimensions are in millimeters unless noted otherwise.
5. Full working drawings, specifications and samples are to be provided by Contractor/Supplier for approval prior to manufacture.

KEY PLAN

A	GENERAL REV.	CAD	AM	SM	2022.12.19
X	INITIAL ISSUE	CAD	AM	SM	2022.11.16
REV.#	GENERAL NOTES	DRAWN BY	CHECKED BY	APPROVED BY	DATE
PROJECT TITLE					REFERENCE
RIC - RIYADH					RIC01 G

DRAWING TITLE

HIGH LEVEL LIGHTING SYSTEM LAYOUT

DRAWING NUMBER

EL-107

REVISION

A

SCALE

1:30

FORMAT

AT

ADDITIONAL NOTES

DESIGN DEVELOPMENT


SIMA MALAK + ALSSAMOURE DESIGN ASSOCIATES

P.O. Box 15707 - Riyadh 11454 KSA

Tel. 01 441 4963 - Fax. 01 441 3867

simals@simals.com

©SIMA MALAK + ALSSAMOURE DESIGN ASSOCIATES (شركة) 2003
This document including all drawing and text is the property and
copyright of SIMA MALAK + ALSSAMOURE DESIGN ASSOCIATES for
use solely with respect to this Project and shall not be copied or
reproduced by any means except by agreement in writing from
SIMA MALAK + ALSSAMOURE DESIGN ASSOCIATES.

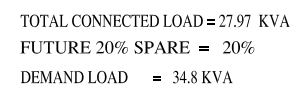

4C X 16mm2 + 10mm2G CU/XLPE/PVC
L= 15 m

DISCONNECT SWITCH RATED AS PER LESSEE PROVISION

1. This drawing shall be read in conjunction with all other relevant architectural, structural & electrical drawings including those of other consultants.
2. It is the responsibility of contractors & manufacturers to check all relevant site dimensions prior to the start of construction or manufacture.
3. All materials and components must be installed on site in accordance with manufacturer's instructions, shop drawings and standard details.
4. All dimensions are in millimeters unless noted otherwise.
5. Full working drawings, specifications and samples are to be provided by Contractor/Supplier for approval prior to manufacture.

REV.#	GENERAL NOTES	DRAWN BY	CHECKED BY	APPROVED BY	DATE
-------	---------------	----------	------------	-------------	------

PROJECT TITLE	REFERENCE
---------------	-----------

RIC - RIYADH	RIC01
	G

DRAWING TITLE

PANEL SINGLE LINE DIAGRAM (SLD)

DRAWING NUMBER	REVISION
----------------	----------

EL-111	-
--------	---

SCALE	FORMAT	ADDITIONAL NOTES	DESIGN DEVELOPMENT
1:30	A1		



SIMA MALAK + ALSSAMOURE
DESIGN ASSOCIATES

P.O. Box 15707 - Riyadh 11454 KSA
Tel. 01 441 4963 - Fax. 01 441 3867
simals@simals.com

©SIMA MALAK + ALSSAMOURI DESIGN ASSOCIATES (السمورى) 2003.
This document including all drawing and text is the property and
copyright of SIMA MALAK + ALSSAMOURI DESIGN ASSOCIATES for
use solely with respect to this Project and shall not be copied or
reproduced by any means except by agreement in writing from
SIMA MALAK + ALSSAMOURI DESIGN ASSOCIATES.

PANEL NAME:			LPB					MOUNTING:			SURFACE MOUNTED					FEEDER ENTRY:			TOP					
LOCATION:								ROOM			CORRIDOR					FEEDER FROM:			EXISTING DISCONNECT SW.					
VOLTAGE:			400 , 230V, 3PH					NO. OF WAYS:			24					CONSIDERED P.F.			0.8					
WIRE SIZE mm²	CKT. NO.	LOAD DESC.	CONN. LOAD (VA)	CONNECTED LOAD/ PHASE			CKT. BREAKER		D.F	D.L (VA)	PHASE			D.L (VA)	D.F	CKT. BREAKER		CONNECTED LOAD/ PHASE			CONN. LOAD (VA)	LOAD DESC.	CKT. NO.	WIRE SIZE mm²
				R	Y	B	NO. OF	TRIP			R	Y	B			TRIP	NO. OF	R	Y	B				
				VA	VA	VA	POLES	AMP.								AMP.	POLES	VA	VA	VA				
2X4+2.5	1	SOCKETS	1,440	1,440			1	30	0.8	1152	•			720	0.8	20	1	900			900	SOCKETS	2	2X4+2.5
2X4+2.5	3	FLOOR BOX	360		360		1	30	0.8	288		•		1872	0.8	20	1		2,340		2,340	SOCKETS	4	2X4+2.5
3X2.5	5	LIGHTING	75			75	1	20	1.0	75			•	2000	1.0	30	1			2,000	2,000	LIGHTING	6	3X2.5
3X2.5	7	LIGHTING	655	655			1	30	1.0	655	•			662	1.0	20	1	662			662	LIGHTING	8	3X2.5
3X2.5	9	LIGHTING	449		449		1	20	1.0	449		•		750	1.0	20	1		750		750	LIGHTING	10	3X2.5
3X2.5	11	LIGHTING	30			30	1	20	1.0	30			•	750	1.0	20	1			750	750	LIGHTING	12	3X2.5
3X2.5	13	LIGHTING	1,200	1,200			1	20	1.0	1200	•			200	1.0	20	1	200			200	LIGHTING	14	3X2.5
3X2.5	15	LIGHTING	300		300		1	20	1.0	300		•		1058	1.0	30	1		1,058		1,058	FCU	16	2X4+2.5
2X4+2.5	17	FCU	1,058			1,058	1	30	10.0	10580			•	1058	1.0	30	1			1,058	1,058	FCU	18	
2X4+2.5	19	FCU	1,058	1,058			1	30	1.0	1058	•			846	0.8	30	1	1,058			1,058	FCU	20	2X4+2.5
	21	SPARE	0				1	20	1.0	0		•		846	0.8	30	1		1,058		1,058	FCU	22	2X4+2.5
	23	SPARE	0				1	30	1.0	0			•		0.8	30	1				0	SPARE	24	
			6,625	4,353	1,109	1,163				15,787				10,763				2,820	5,206	3,808	11,834			

TOTAL CONNECTED LOAD/ PHASE

TOTAL DEMAND LOAD

DEMAND LOAD CURRENT

MAIN BREAKER SIZE

7,173 6,315 4,971

26,550 VA
45.99 A
60 A.T/

100 A.F

TOTAL LOAD AFTER FUTURE 20 % SPARE=		31.86 KVA	
FEEDING CABLE		4X16+10 MM2 CU/XLPE/PVC	
I s.c		18 KA	

GENERAL NOTES

1. This drawing shall be read in conjunction with all other relevant architectural,structural & electrical drawings including those of other consultants.
2. It is the responsibility of contractors & manufacturers to check all relevant site dimensions prior to the start of construction or manufacture.
3. All materials and components must be installed on site in accordance with manufacturer's instructions , shop drawings and standard details.
4. All dimensions are in millimeters unless noted otherwise.
5. Full working drawings, specifications and samples are to be provided by Contractor/Supplier for approval prior to manufacture.

KEY PLAN

✗	INITIAL ISSUE	CAD	AM	SM	2022.11.16
---	---------------	-----	----	----	------------

REV.#	GENERAL NOTES	DRAWN BY	CHECKED BY	APPROVED BY	DATE
-------	---------------	----------	------------	-------------	------

PROJECT TITLE				REFERENCE
---------------	--	--	--	-----------

RIC - RIYADH				RIC01 G
--------------	--	--	--	------------

DRAWING TITLE				
---------------	--	--	--	--

LOAD CALCULATION SCHEDULE				
---------------------------	--	--	--	--

DRAWING NUMBER				REVISION
----------------	--	--	--	----------

EL-112				-
--------	--	--	--	---

SCALE	FORMAT	ADDITIONAL	DESIGN DEVELOPMENT	
-------	--------	------------	--------------------	--

1:30	A1	NOTES		
------	----	-------	--	--



**SIMA MALAK + ALSSAMOURE
DESIGN ASSOCIATES**
P.O. Box 15707 - Riyadh 11454 KSA
Tel. 01 441 4963 - Fax. 01 441 3867
simals@simals.com

©SIMA MALAK + ALSSAMOURE DESIGN ASSOCIATES (شركة) 2003
This document including all drawing and text is the property and
copyright of SIMA MALAK + ALSSAMOURE DESIGN ASSOCIATES for
use solely with respect to this Project and shall not be copied or
reproduced by any means except by agreement in writing from
SIMA MALAK + ALSSAMOURE DESIGN ASSOCIATES.