

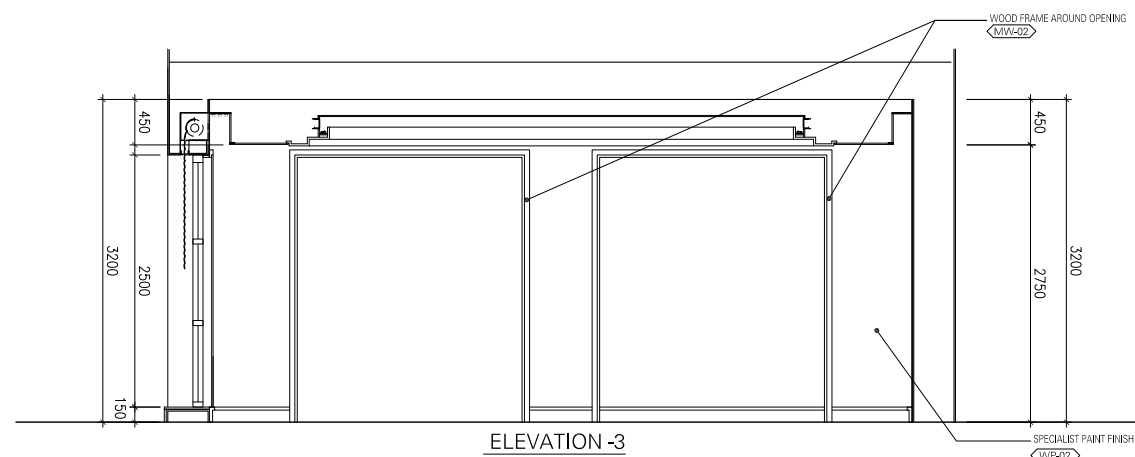
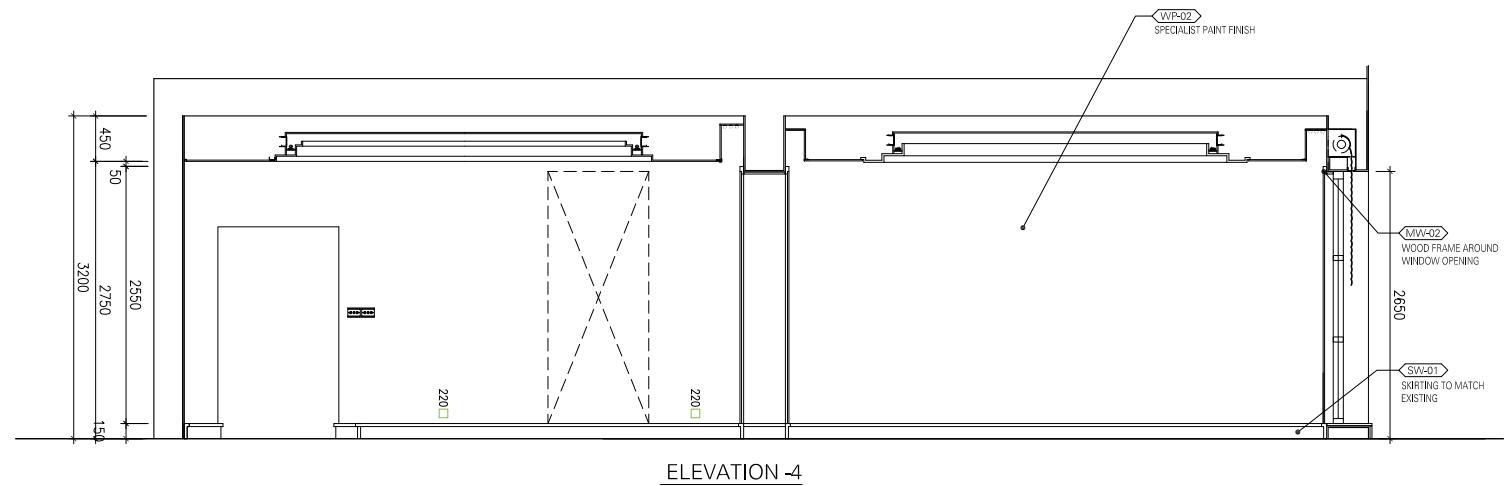


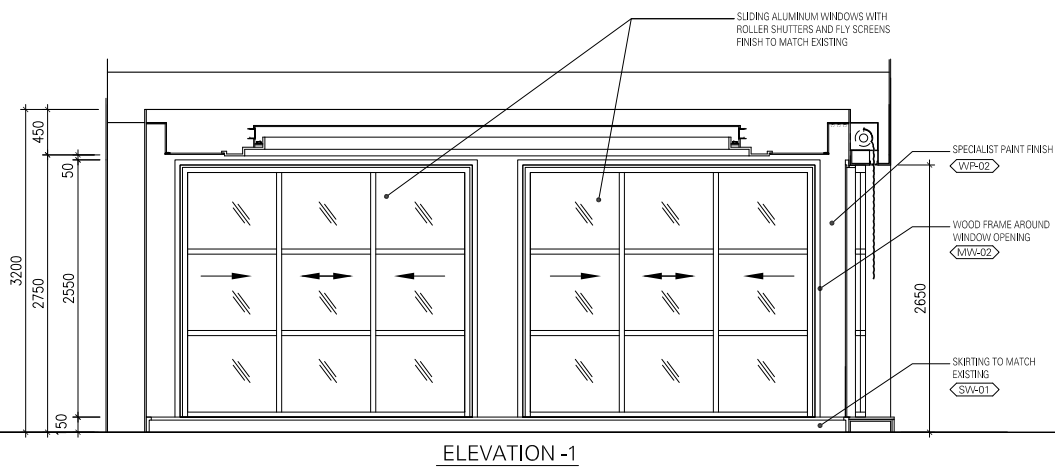

©SIMA MALAK + ALSSAMOURE DESIGN ASSOCIATES (سما) 2003
This document including all drawing and text is the property and
copyright of SIMA MALAK + ALSSAMOURE DESIGN ASSOCIATES for
use solely with respect to this Project and shall not be copied or
reproduced by any means except by agreement in writing from
SIMA MALAK + ALSSAMOURE DESIGN ASSOCIATES.

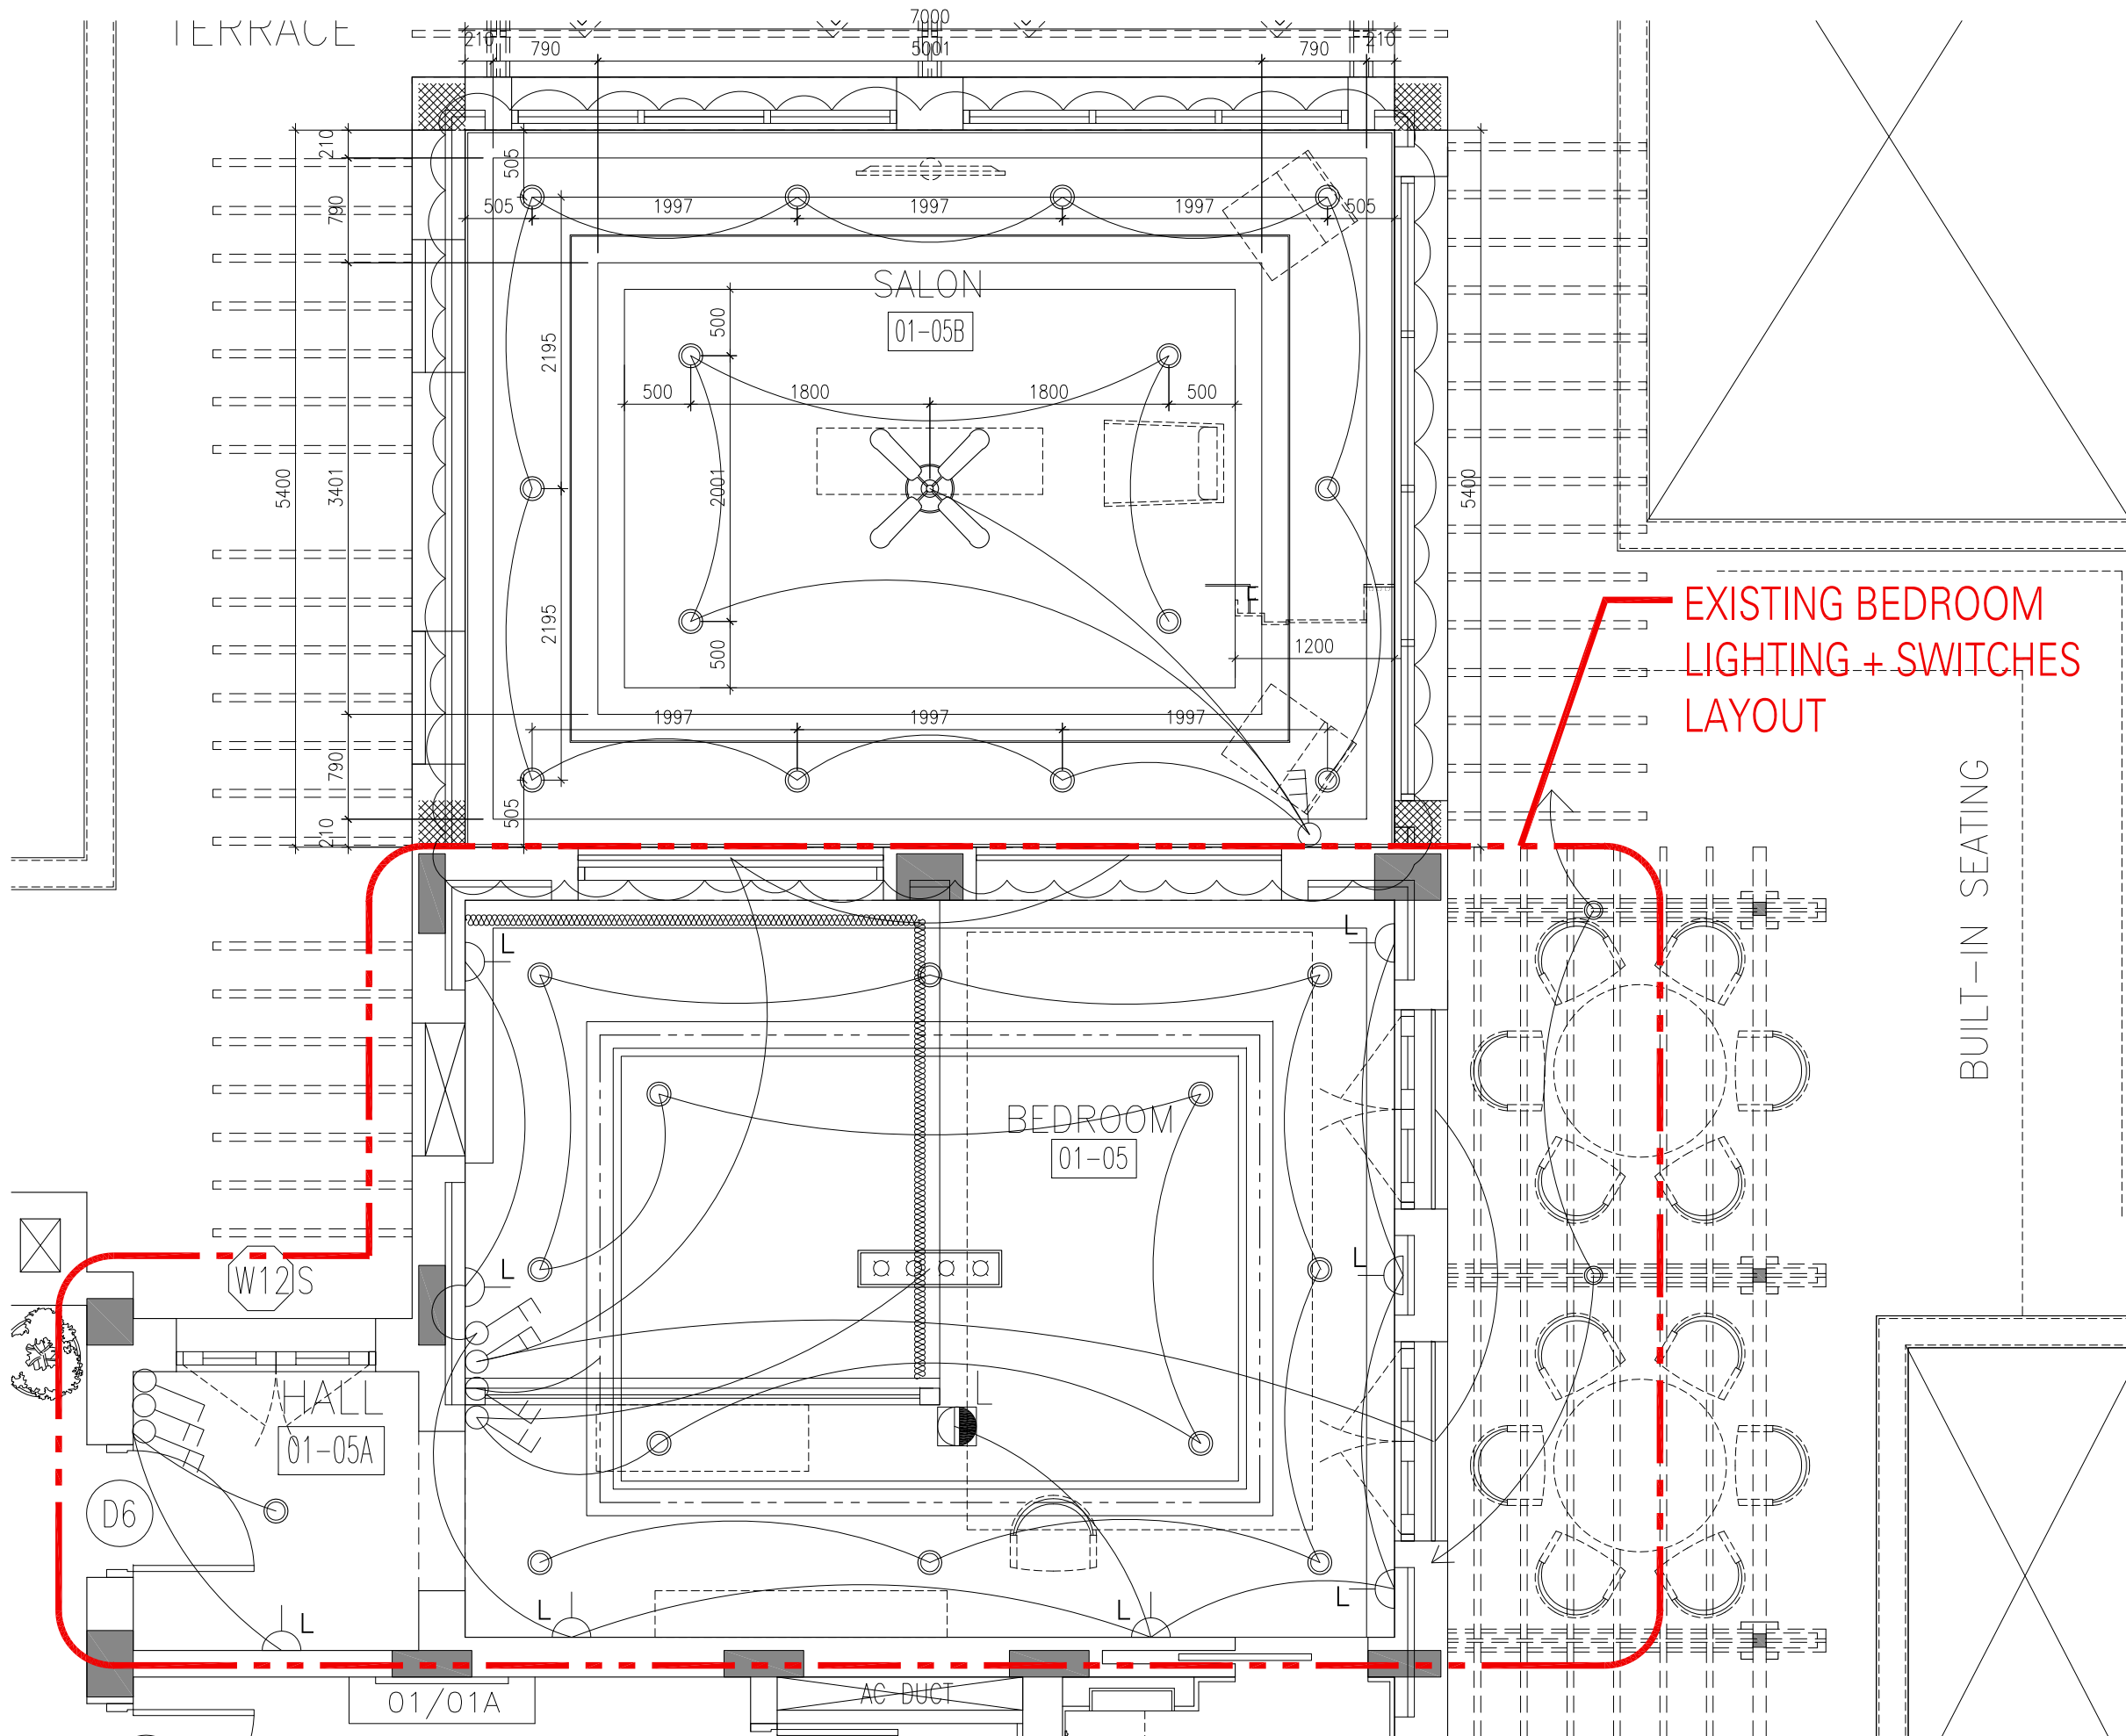

BEDROOM + SALON LIGHTING LAYOUT

SCALE 1:50


GENERAL NOTES

1. This drawing shall be read in conjunction with all other relevant architectural, structural & electrical drawings including those of other consultants.
2. It is the responsibility of contractors & manufacturers to check all relevant site dimensions prior to the start of construction or manufacture.
3. All materials and components must be installed on site in accordance with manufacturer's instructions, shop drawings and standard details.
4. All dimensions are in millimeters unless noted otherwise.
5. Full working drawings, specifications and samples are to be provided by Contractor/Supplier for approval prior to manufacture.

LEGEND :

- ✱ Chandelier
- Recessed Downlight
- 3 Gang Switch

TYPICAL LAYOUT OF SWITCHES

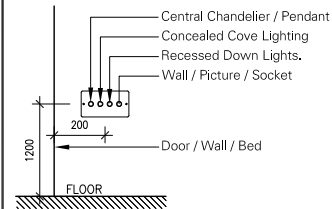

KEY PLAN


REV.#	GENERAL NOTES	DRAWN BY	CHECKED BY	APPROVED BY	DATE
B	CLG+LTG REV.	AC	AM	SM	2025.04.29
A	GENEAL REV.	MP	AM	SM	2024.07.03
X	INITIAL ISSUE	AC	AM	SM	2024.05.09

PROJECT TITLE	REFERENCE
SAF-RIYADH	SAF01 G


DRAWING TITLE			
FIRST FLOOR - EXTENSION BEDROOM + SALON CEILING + LIGHTING LAYOUT			
DRAWING NUMBER			REVISION
SK-130			B
SCALE	FORMAT	ADDITIONAL NOTES	DESIGN DEVELOPMENT
1:50	A1		

SIMA MALAK + ALSSAMOURE
DESIGN ASSOCIATES
P.O. Box 15707 - Riyadh 11454 KSA
Tel. 01 441 4963 - Fax. 01 441 3867
simals@simals.com


©SIMA MALAK + ALSSAMOURE DESIGN ASSOCIATES (شركة) 2003
This document including all drawing and text is the property and copyright of SIMA MALAK + ALSSAMOURE DESIGN ASSOCIATES for use solely with respect to this Project and shall not be copied or reproduced by any means except by agreement in writing from SIMA MALAK + ALSSAMOURE DESIGN ASSOCIATES.

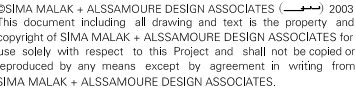


SCALE 1:50

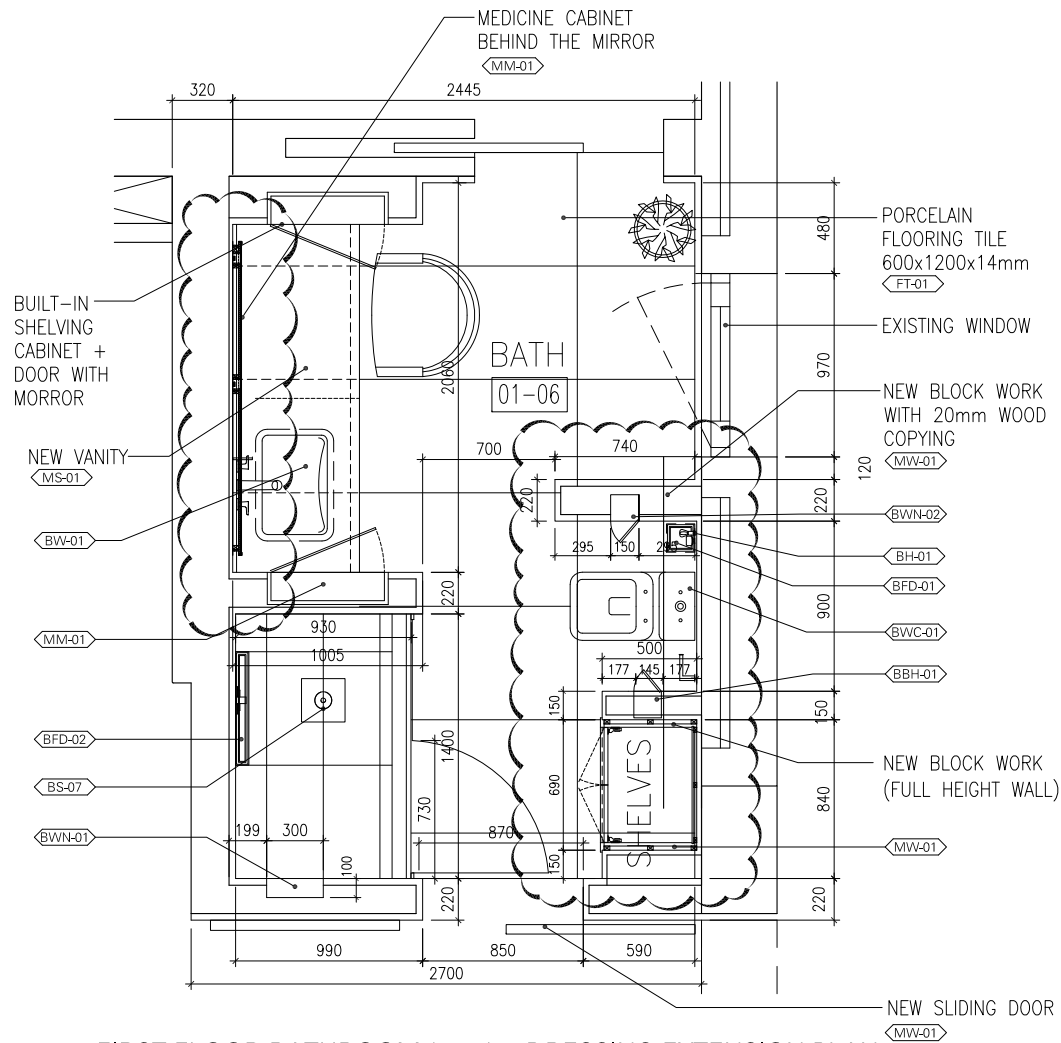


FIRST FLOOR BATHROOM (1-06) + DRESSING EXTENSION PLAN
SCALE 1:25

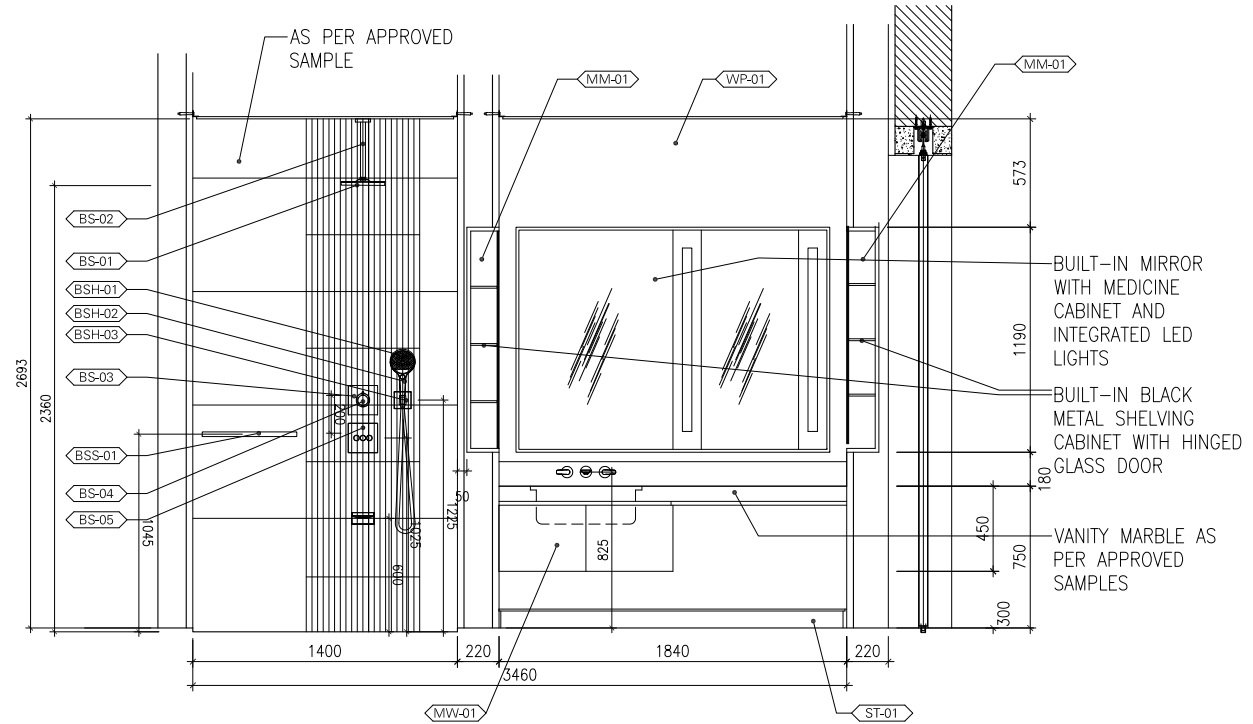


ELEVATION - 01
SCALE 1:25

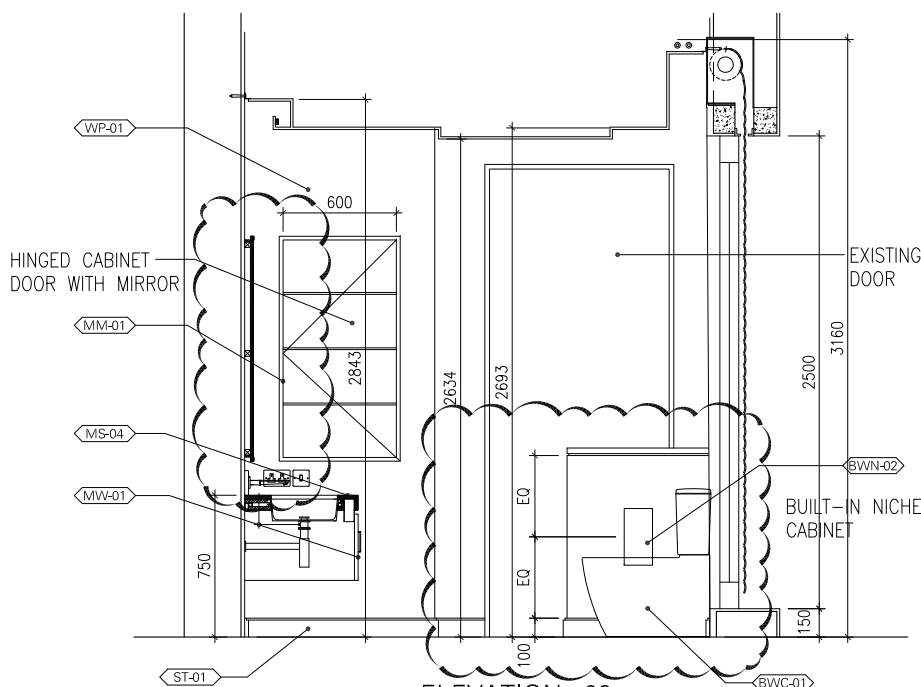

ELEVATION - 02
SCALE 1:25

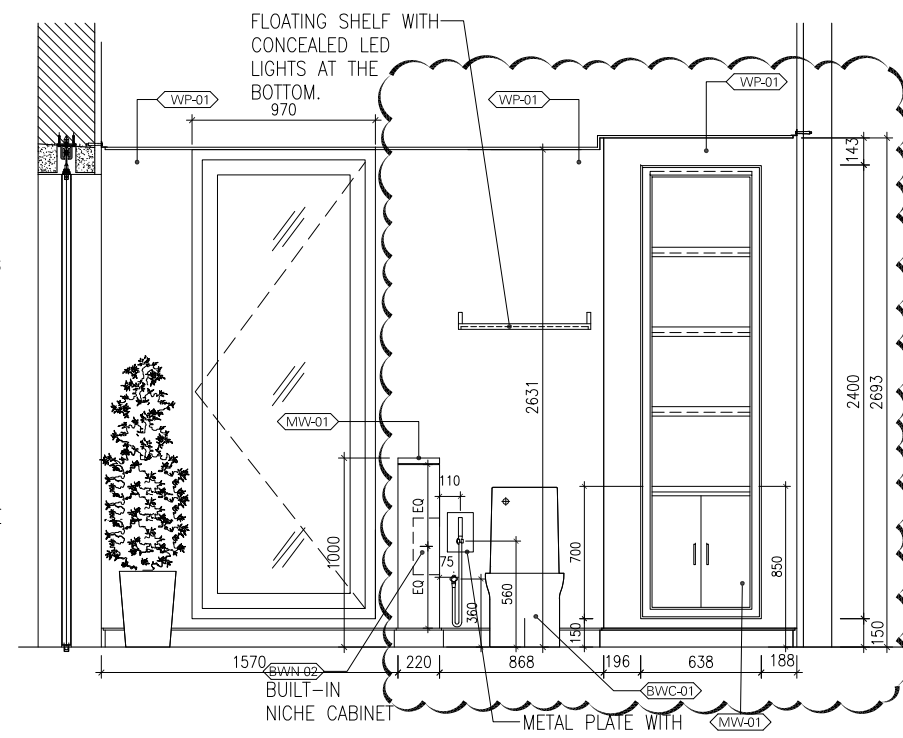

ELEVATION - 03
SCALE 1:25

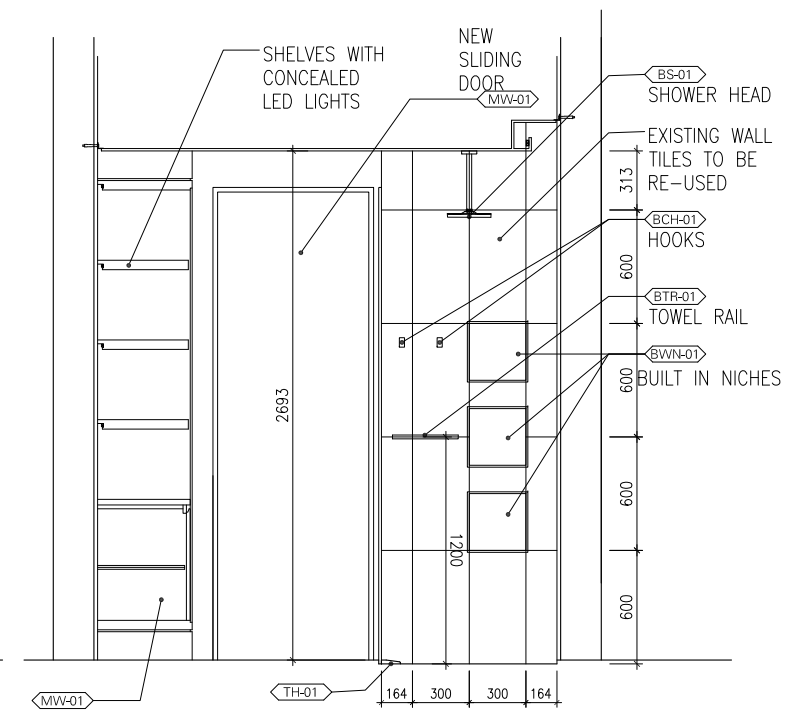

ELEVATION - 04
SCALE 1:25

GENERAL NOTES

1. This drawing shall be read in conjunction with all other relevant architectural, structural & electrical drawings including those of other consultants.
2. It is the responsibility of contractors & manufacturers to check all relevant site dimensions prior to the start of construction or manufacture.
3. All materials and components must be installed on site in accordance with manufacturer's instructions, shop drawings and standard details.
4. All dimensions are in millimeters unless noted otherwise.
5. Full working drawings, specifications and samples are to be provided by Contractor/Supplier for approval prior to manufacture.

KEY PLAN


E	REV. WITH CLOUD	AC	AM	AM	2024.12.12
D	VANITY+MIRROR REV.	AC	AM	AM	2024.12.11
C	REV. SANITARY FLUX.	MP	AM	SM	2024.11.04
B	GENERAL REV.	MP	AM	SM	2024.10.13
A	GENERAL REV.	MP	AM	SM	2024.07.02
X	INITIAL ISSUE	AC/MP	AM	AM	2024.06.07
REV.#	GENERAL NOTES	DRAWN BY	CHECKED BY	APPROVED BY	DATE

PROJECT TITLE	REFERENCE
SAF-RIYADH	SAF01 G

DRAWING TITLE	REVISION
FIRST FLOOR BATHROOM (01-06) PROPOSED PLAN + ELEVATIONS	D
DRAWING NUMBER	SK-106
SCALE	FORMAT
1:50	A1
ADDITIONAL NOTES	DESIGN DEVELOPMENT


SIMA MALAK + ALSSAMOUR
DESIGN ASSOCIATES
P.O. Box 15707 - Riyadh 11454 KSA
Tel. 01 441 4963 - Fax. 01 441 3867
simas@simas.com

©SIMA MALAK + ALSSAMOUR DESIGN ASSOCIATES () 2003
This document including all drawing and text is the property and copyright of SIMA MALAK + ALSSAMOUR DESIGN ASSOCIATES for use solely with respect to this Project and shall not be copied or reproduced by any means except by agreement in writing from SIMA MALAK + ALSSAMOUR DESIGN ASSOCIATES.

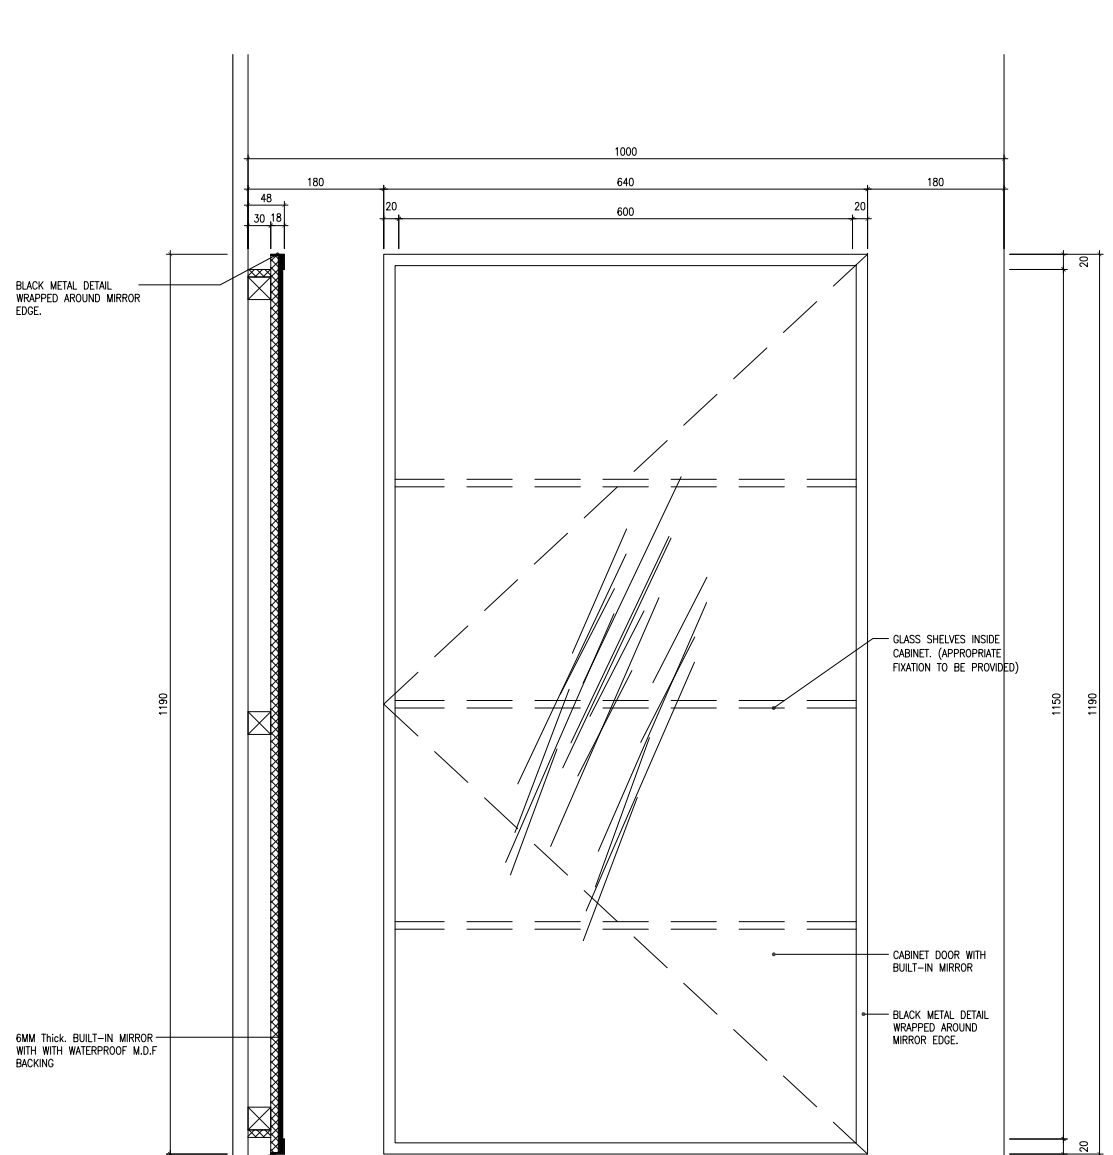


VANITY ELEVATION

SCALE 1:10

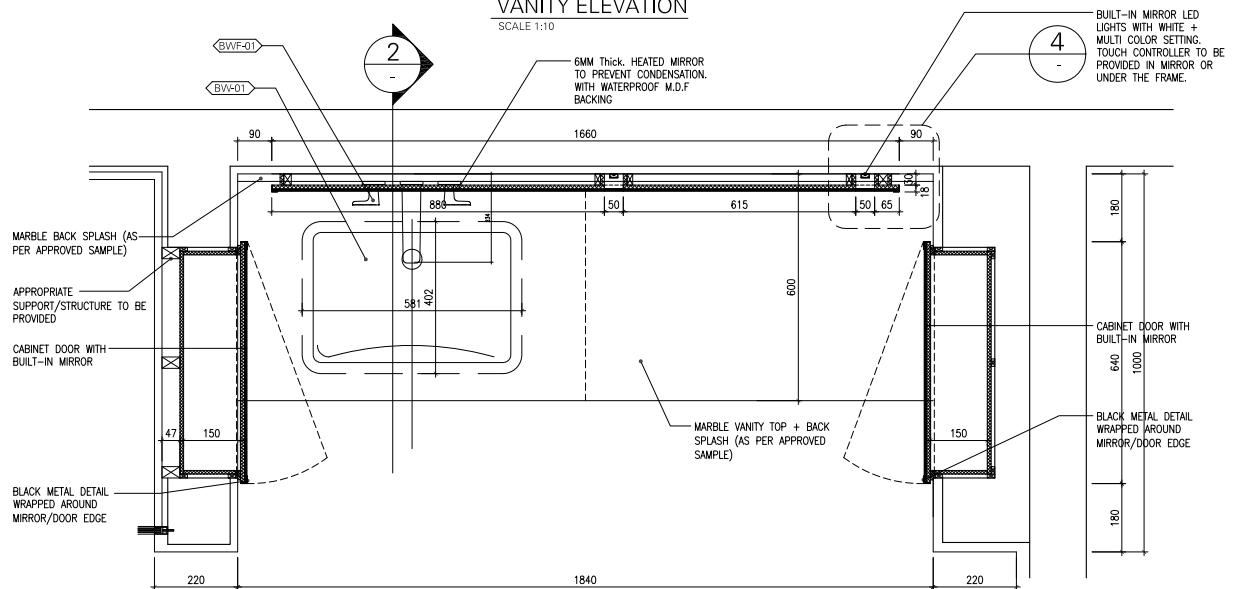

01 VANITY PLAN

Scale 1:10

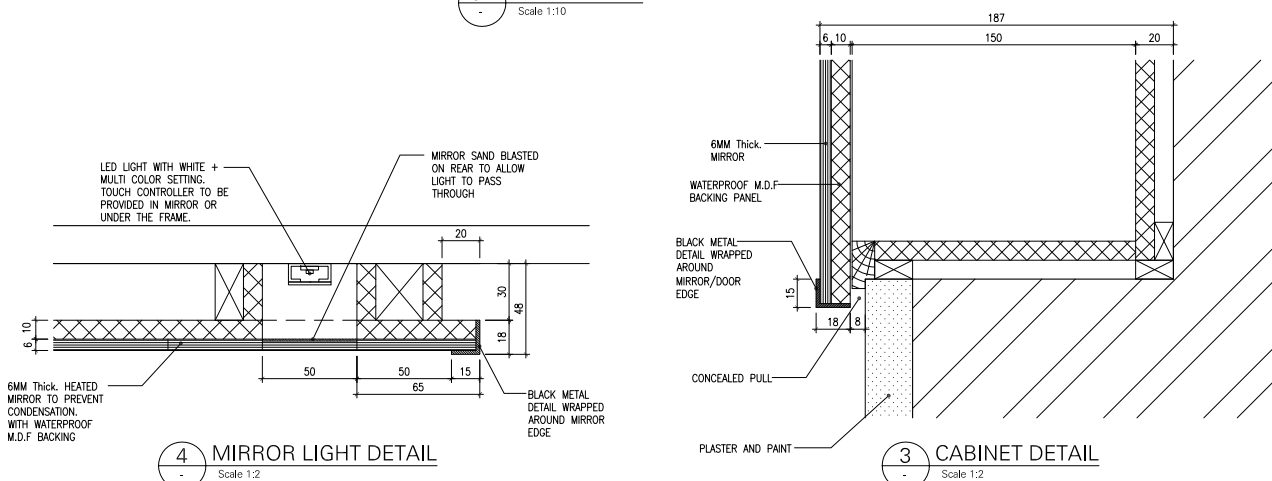


4 MIRROR LIGHT DETAIL

Scale 1:2

02 VANITY SECTION

Scale 1:5

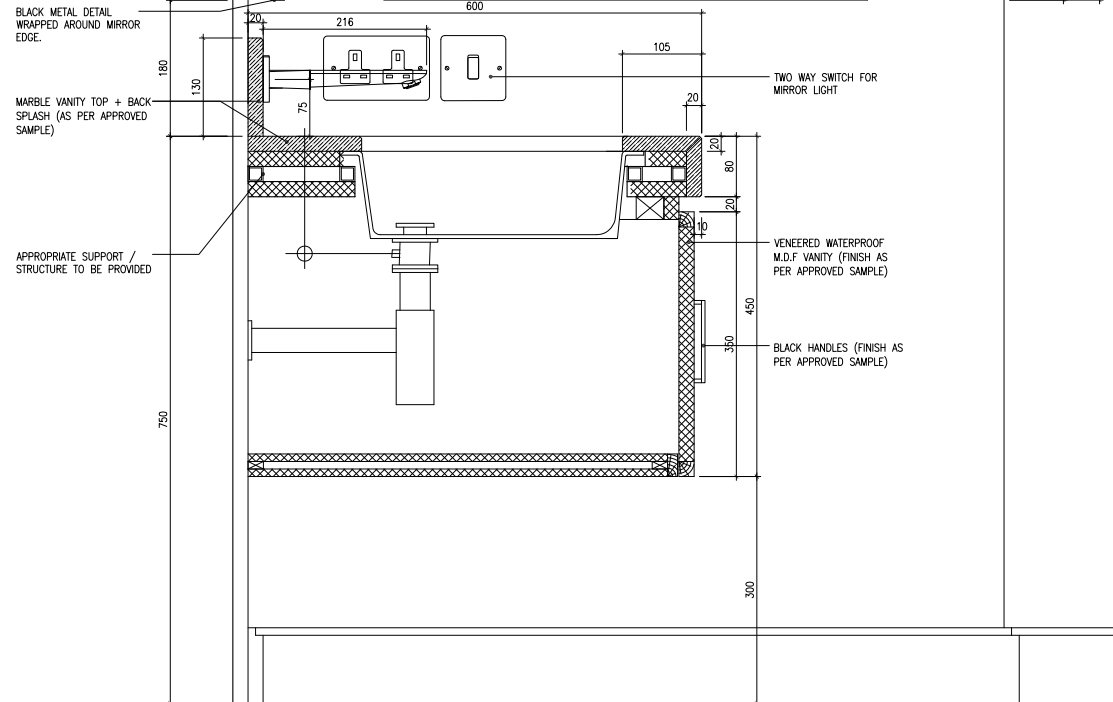

02 VANITY SECTION

Scale 1:5

GENERAL NOTES

1. This drawing shall be read in conjunction with all other relevant architectural, structural & electrical drawings including those of other consultants.
2. It is the responsibility of contractors & manufacturers to check all relevant site dimensions prior to the start of construction or manufacture.
3. All materials and components must be installed on site in accordance with manufacturer's instructions , shop drawings and standard details.
4. All dimensions are in millimeters unless noted otherwise.
5. Full working drawings, specifications and samples are to be provided by Contractor/Supplier for approval prior to manufacture.

KEY PLAN

A	VANITY+MIRROR REV.	AC	AM	AM	2024.12.11		
X	INITIAL ISSUE	AC/M/P	AM	AM	2024.10.01		
REV.#	GENERAL NOTES	DRAWN BY	CHECKED BY	APPROVED BY	DATE		
PROJECT TITLE						REFERENCE	
SAF-RIYADH						SAF01	
						G	

DRAWING TITLE	
---------------	--

FIRST FLOOR
BATHROOM (01-06)
VANITY + CABINET DETAILS

DRAWING NUMBER	REVISION
----------------	----------

SK-106-2	S
----------	---


SCALE	FORMAT	ADDITIONAL NOTES	DESIGN DEVELOPMENT
1:50	A1		






SIMA MALAK + ALSSAMOUR
DESIGN ASSOCIATES

P.O. Box 15707 - Riyadh 11454 KSA
Tel. 01 441 4963 - Fax. 01 441 3867
simals@simals.com

©SIMA MALAK + ALSSAMOURI DESIGN ASSOCIATES (مسلم) 2003
This document including all drawing and text is the property and
copyright of SIMA MALAK + ALSSAMOURI DESIGN ASSOCIATES for
use solely with respect to this Project and shall not be copied or
reproduced by any means except by agreement in writing from
SIMA MALAK + ALSSAMOURI DESIGN ASSOCIATES.

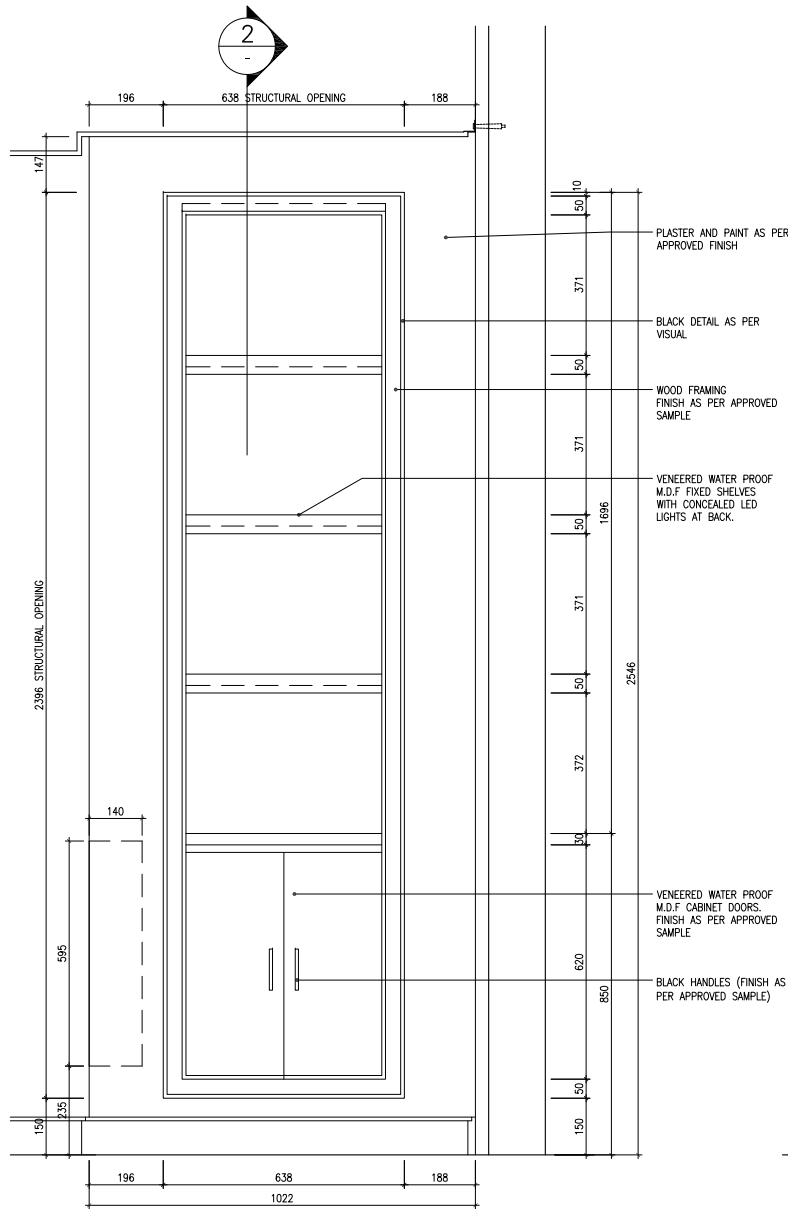

SHELVING + STORAGE UNIT ELEVATION
SCALE 1:10

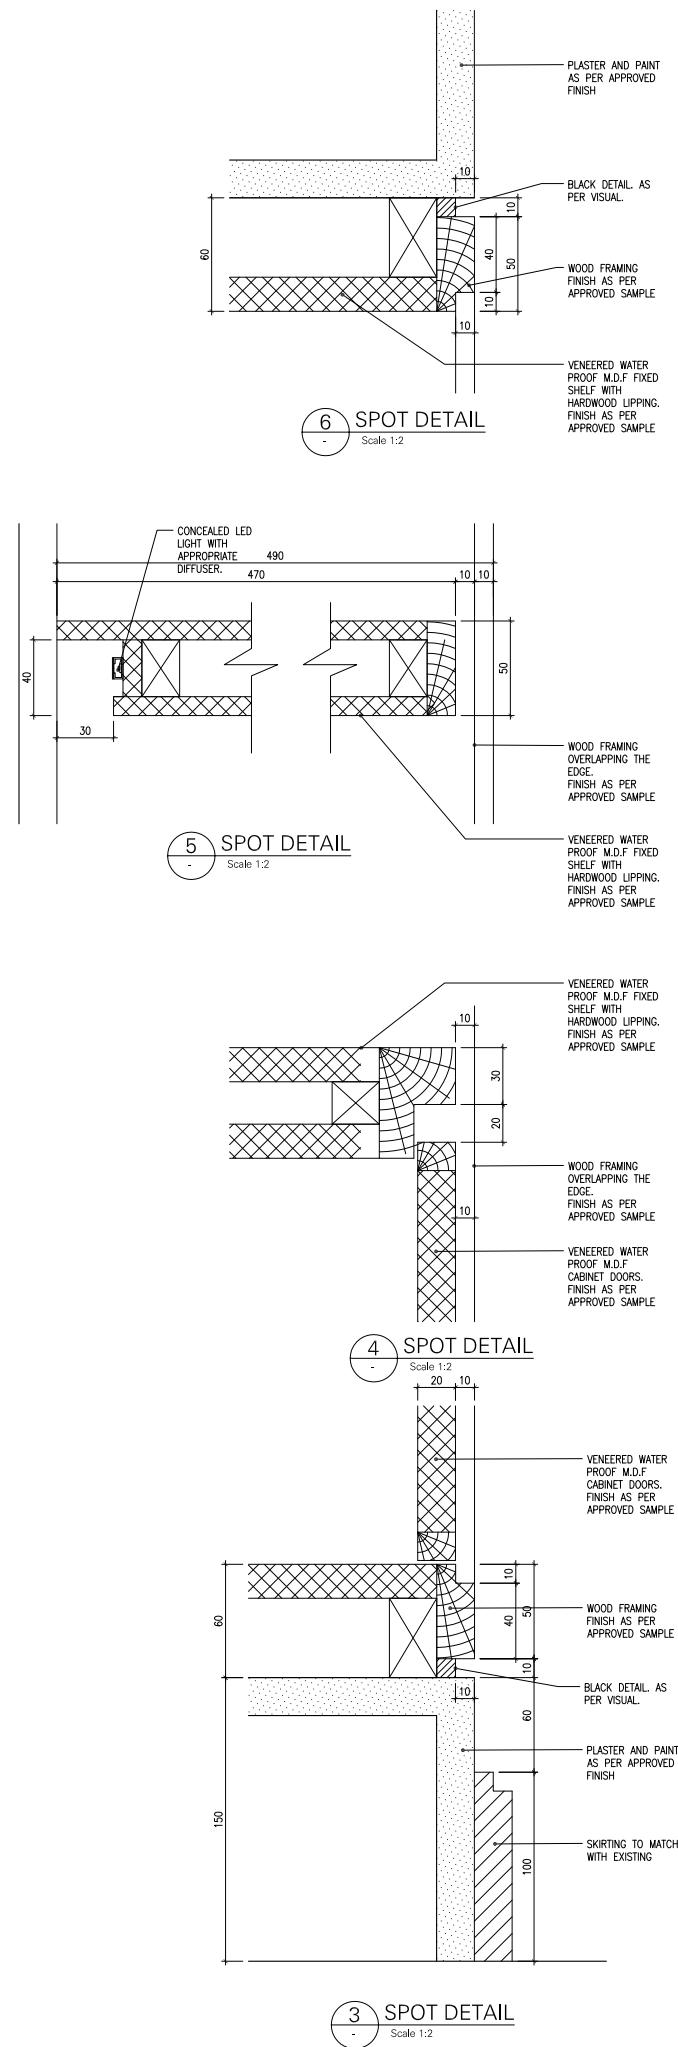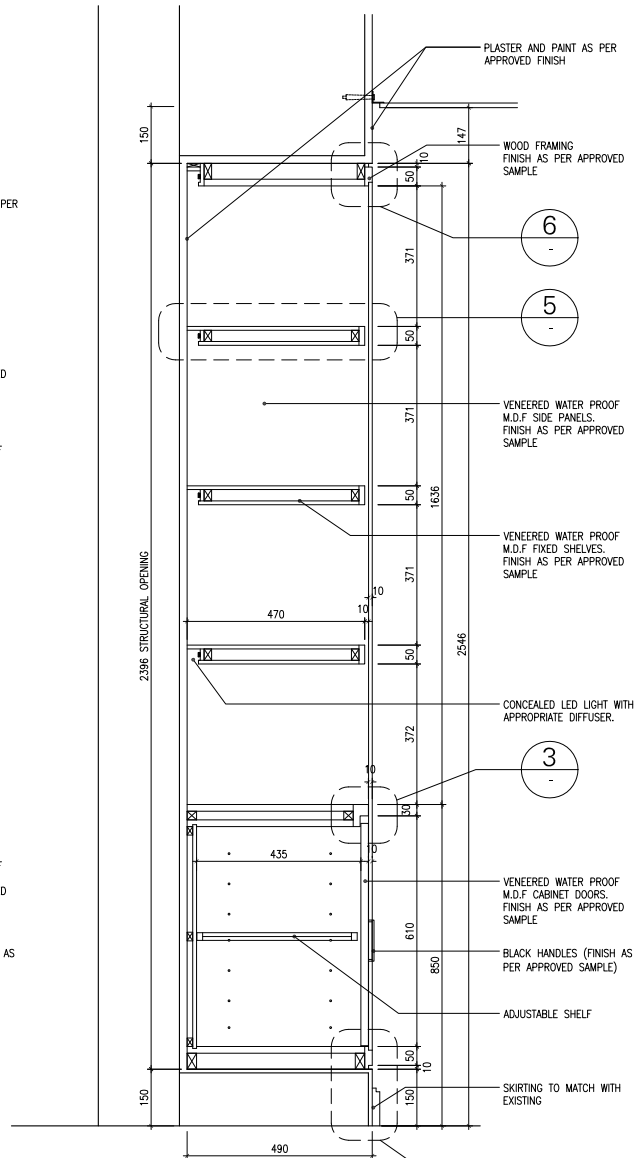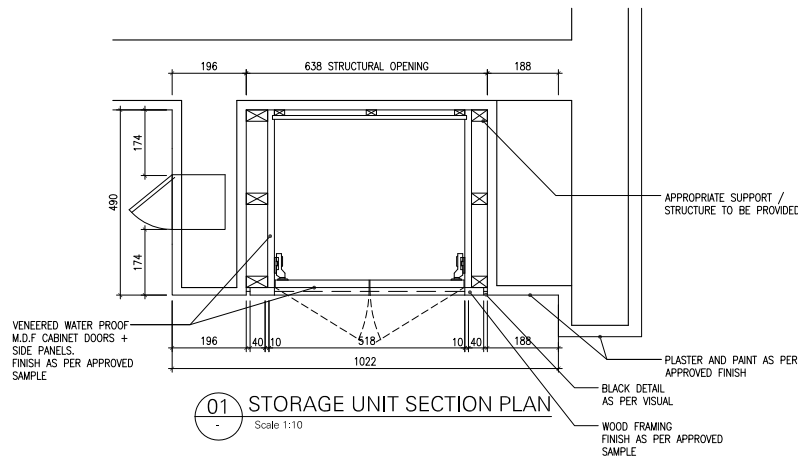

GENERAL NOTES

1. This drawing shall be read in conjunction with all other relevant architectural, structural & electrical drawings including those of other consultants.
2. It is the responsibility of contractors & manufacturers to check all relevant site dimensions prior to the start of construction or manufacture.
3. All materials and components must be installed on site in accordance with manufacturer's instructions, shop drawings and standard details.
4. All dimensions are in millimeters unless noted otherwise.
5. Full working drawings, specifications and samples are to be provided by Contractor/Supplier for approval prior to manufacture.

KEY PLAN


B	GENERAL REV.	MP	AM	SM	2025.06.24
A	REV. WITH CLOUD	AC	AM	AM	2024.12.12
X	INITIAL ISSUE	AC/MP	AM	AM	2024.10.01
REV.#	GENERAL NOTES	DRAWN BY	CHECKED BY	APPROVED BY	DATE
PROJECT TITLE				REFERENCE	
SAF-RIYADH				SAF01 G	

DRAWING TITLE		REVISION	
FIRST FLOOR BATHROOM (01-06) SHELVING + STORAGE UNIT DETAILS		A	
DRAWING NUMBER		SK-106-3	
SCALE	FORMAT	ADDITIONAL NOTES	DESIGN DEVELOPMENT
1:50	A1		


**SIMA MALAK + ALSSAMOURE
DESIGN ASSOCIATES**

P.O. Box 15707 - Riyadh 11454 KSA
Tel. 01 441 4963 - Fax. 01 441 3867
simals@simals.com



©SIMA MALAK + ALSSAMOURE DESIGN ASSOCIATES () 2003
This document including all drawing and text is the property and
copyright of SIMA MALAK + ALSSAMOURE DESIGN ASSOCIATES for
use solely with respect to this Project and shall not be copied or
reproduced by any means except by agreement in writing from
SIMA MALAK + ALSSAMOURE DESIGN ASSOCIATES.

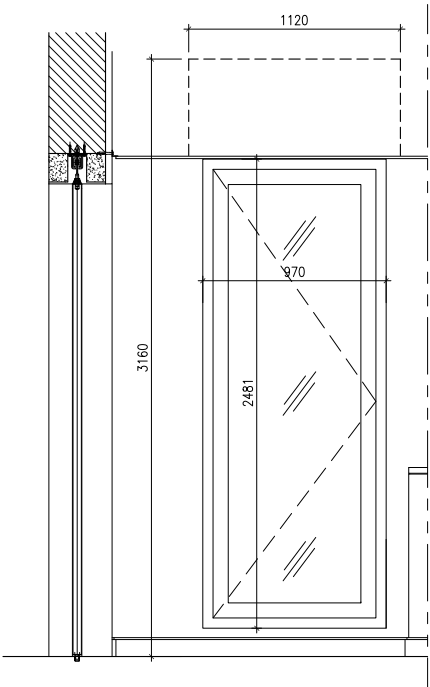

BATHROOM WINDOW ELEVATION

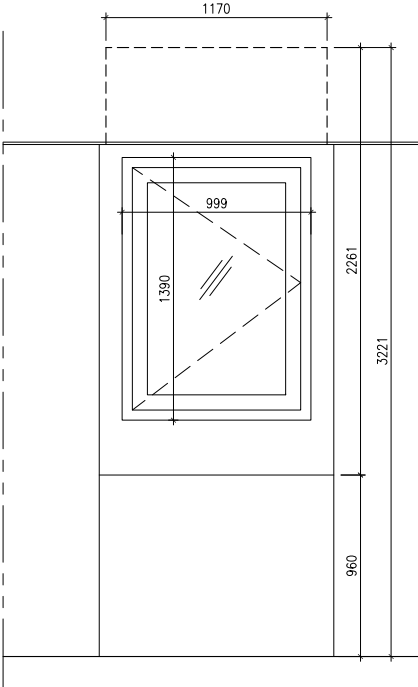

DRESSING WINDOW ELEVATION

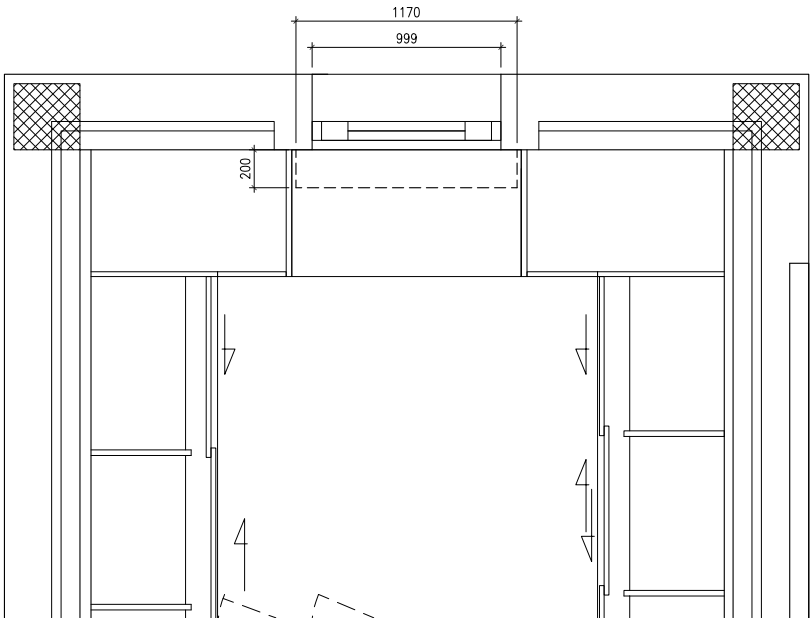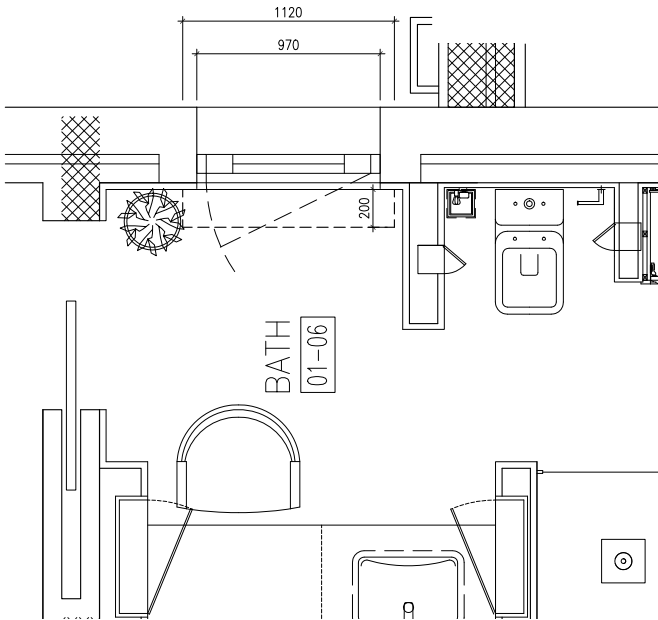

GENERAL NOTES

1. This drawing shall be read in conjunction with all other relevant architectural, structural & electrical drawings including those of other consultants.
2. It is the responsibility of contractors & manufacturers to check all relevant site dimensions prior to the start of construction or manufacture.
3. All materials and components must be installed on site in accordance with manufacturer's instructions, shop drawings and standard details.
4. All dimensions are in millimeters unless noted otherwise.
5. Full working drawings, specifications and samples are to be provided by Contractor/Supplier for approval prior to manufacture.

KEY PLAN

REV.#	GENERAL NOTES	DRAWN BY	CHECKED BY	APPROVED BY	DATE

PROJECT TITLE	REFERENCE
SAF-RIYADH	SAF01 G


DRAWING TITLE	REVISION
FIRST FLOOR BATHROOM (01-06) + DRESS (01-07A) WINDOWS PLAN AND ELEVATIONS	-

DRAWING NUMBER	REVISION
SK-140	-

SCALE	FORMAT	ADDITIONAL NOTES	DESIGN DEVELOPMENT
1:20	A1		


SIMA MALAK + ALSSAMOURE
DESIGN ASSOCIATES

P.O. Box 15707 - Riyadh 11454 KSA
Tel. 01 441 4963 - Fax. 01 441 3867
simals@simals.com

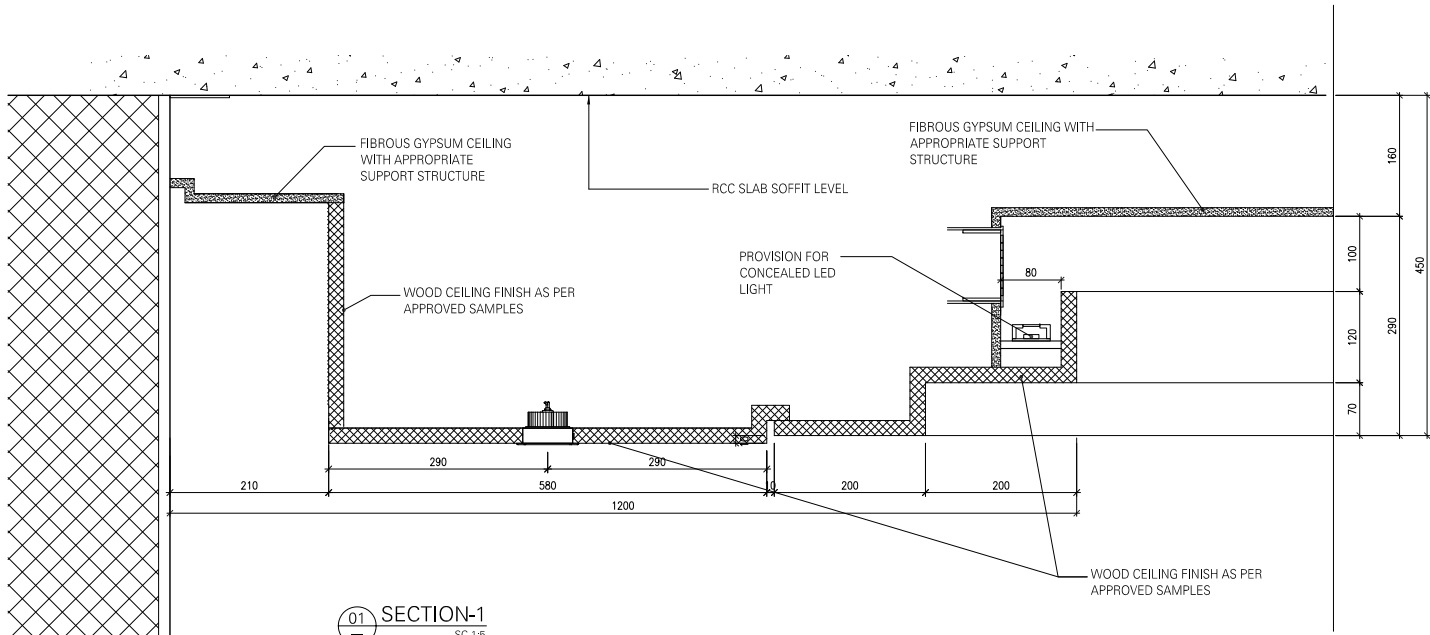

01 SECTION-1
SC.1:5

TYPICAL CEILING SECTION AT SALON (01-05B)

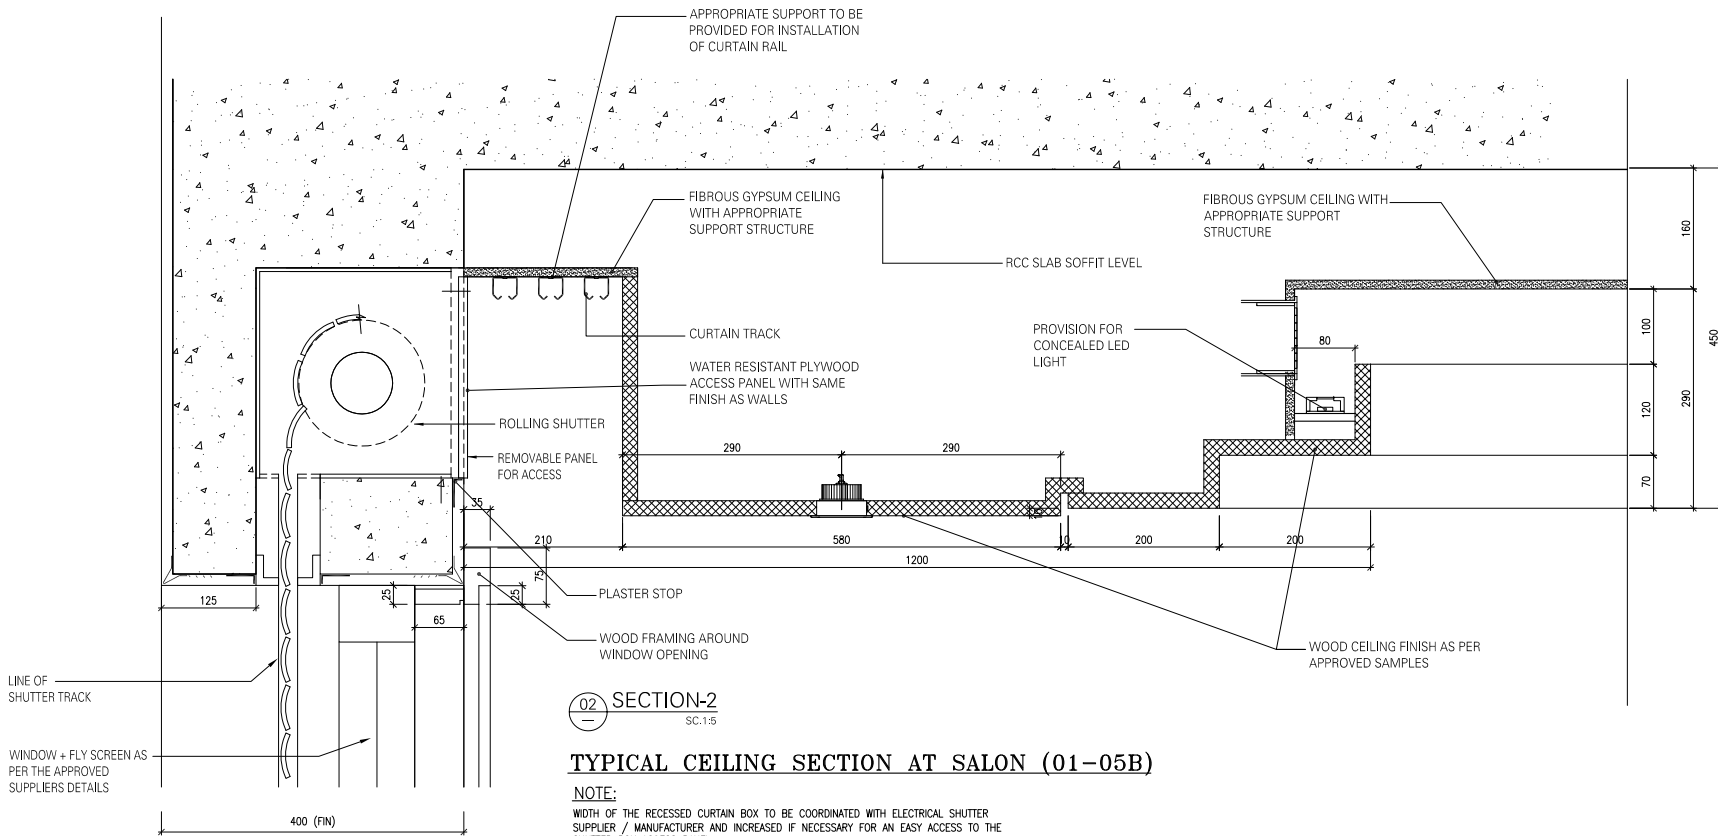

02 SECTION-2
SC.1:5

TYPICAL CEILING SECTION AT SALON (01-05B)

NOTE:
WIDTH OF THE RECESSED CURTAIN BOX TO BE COORDINATED WITH ELECTRICAL SHUTTER SUPPLIER / MANUFACTURER AND INCREASED IF NECESSARY FOR AN EASY ACCESS TO THE SHUTTER BOX ACCESS PANEL.
FINAL COORDINATED SECTION AND DETAILS TO BE SUBMITTED BY CONTRACTOR FOR REVIEW / APPROVAL.

GENERAL NOTES

1. This drawing shall be read in conjunction with all other relevant architectural, structural & electrical drawings including those of other consultants.
2. It is the responsibility of contractors & manufacturers to check all relevant site dimensions prior to the start of construction or manufacture.
3. All materials and components must be installed on site in accordance with manufacturer's instructions, shop drawings and standard details.
4. All dimensions are in millimeters unless noted otherwise.
5. Full working drawings, specifications and samples are to be provided by Contractor/Supplier for approval prior to manufacture.

KEY PLAN

A	DETS REV.	AC	AM	SM	2025.04.29
X	INITIAL ISSUE	AC	AM	AM	2024.05.09

REV.#	GENERAL NOTES	DRAWN BY	CHECKED BY	APPROVED BY	DATE

PROJECT TITLE	REFERENCE
SAF-RIYADH	SAF01 G

DRAWING TITLE

FIRST FLOOR
SALON (01-05B)
CEILING DETAILS

DRAWING NUMBER

SK-141

REVISION

A

SCALE

1:5

FORMAT

A1

ADDITIONAL

NOTES

DESIGN DEVELOPMENT

SIMA MALAK + ALSSAMOURE

DESIGN ASSOCIATES

P.O. Box 15707 - Riyadh 11454 KSA

Tel. 01 441 4963 - Fax. 01 441 3867

simals@simals.com

©SIMA MALAK + ALSSAMOURE DESIGN ASSOCIATES (شركة) 2003


This document including all drawing and text is the property and

copyright of SIMA MALAK + ALSSAMOURE DESIGN ASSOCIATES for

use solely with respect to this Project and shall not be copied or

reproduced by any means except by agreement in writing from

SIMA MALAK + ALSSAMOURE DESIGN ASSOCIATES.

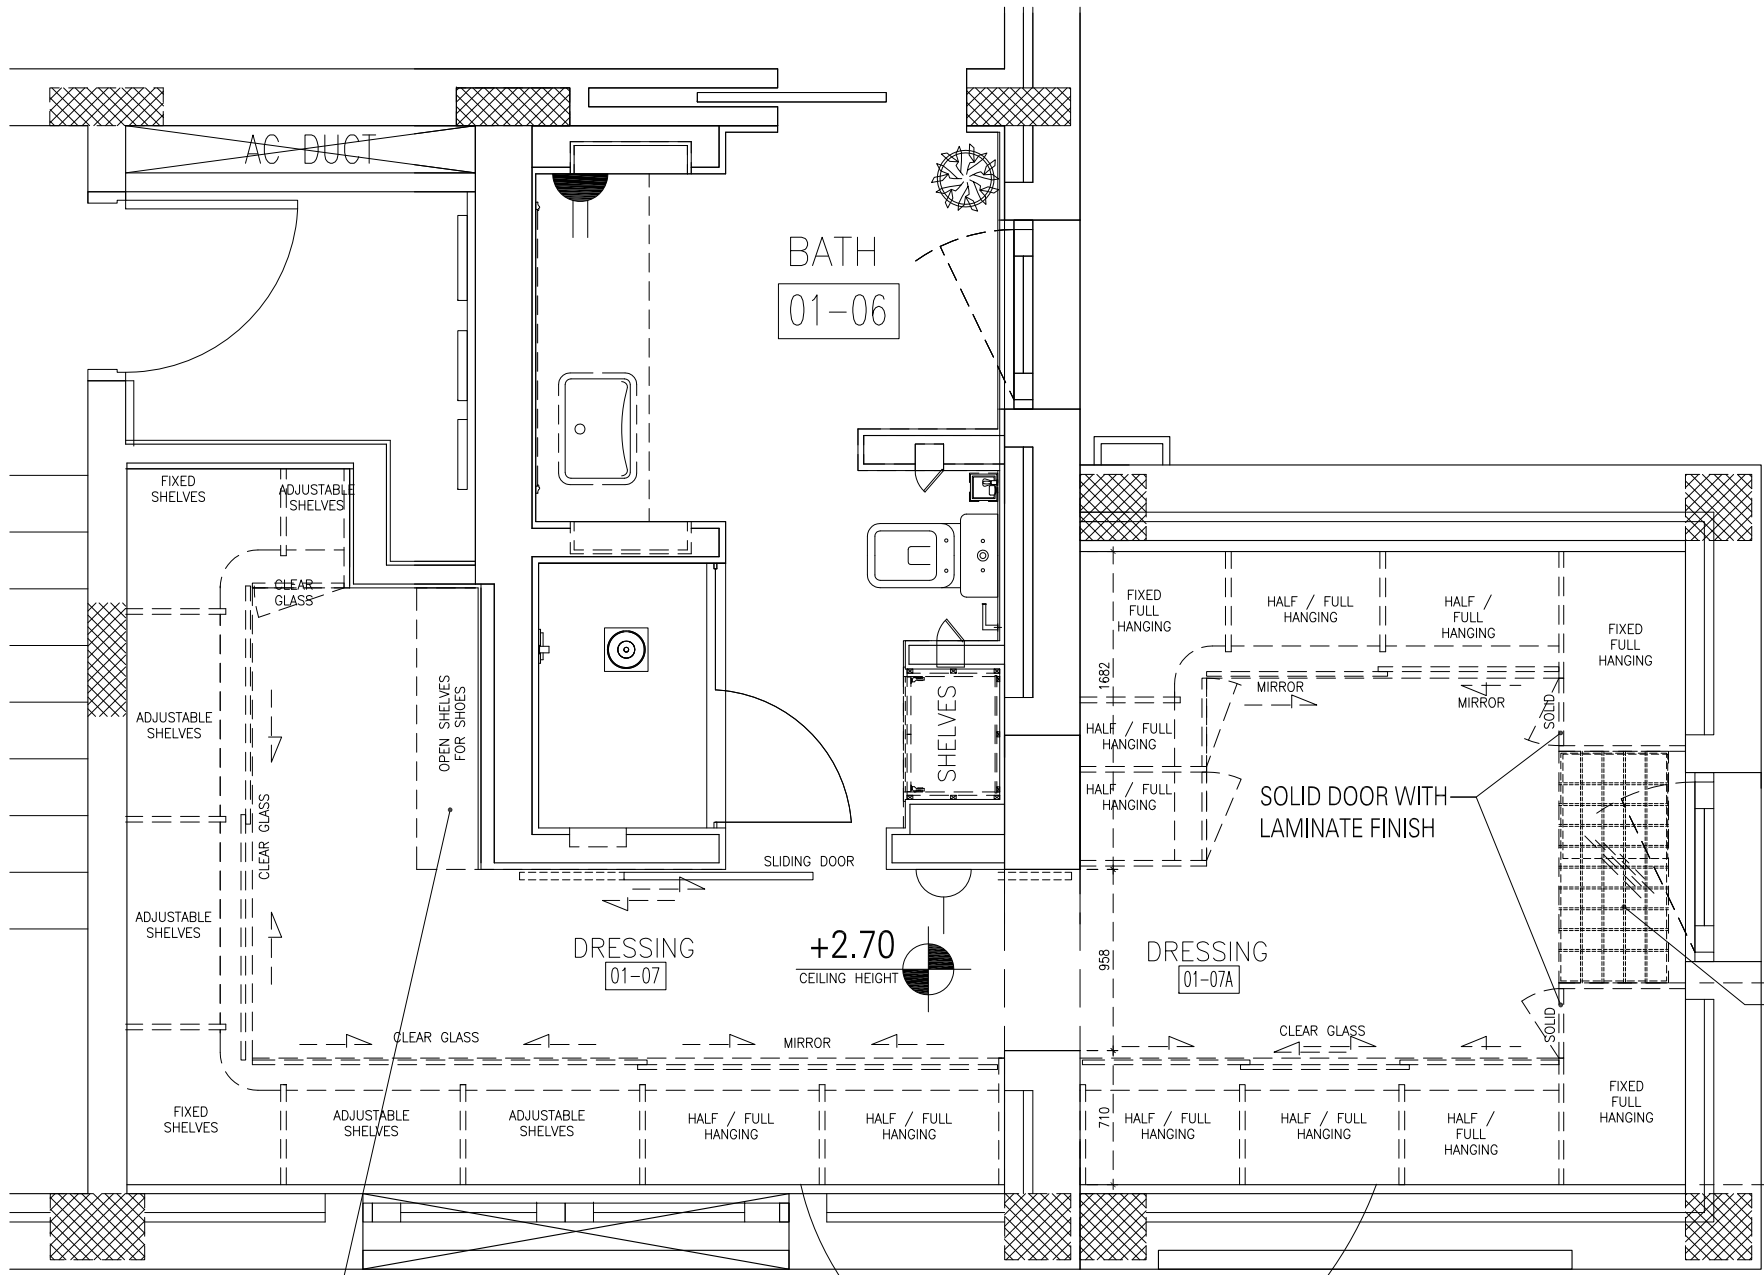

REQUIREMENTS TO BE
VERIFIED AT SITE AFTER
CABINETS HAVE BEEN
INSTALLED

POWER TO BE
PROVIDED FOR
AUTOMATED
CONCEALED LIGHTING

CABINETS WITH DRAWERS
ABOVE AND GLASS TOP. TOP
DRAWER TO HAVE DIVIDERS
THAT CAN BE RECONFIGURED
AS REQUIRED FOR BELTS Etc...
PUSH TO RELEASE OR
CONCEALED PULL.

POWER + COMMUNICATION LAYOUT

SCALE 1:20

GENERAL NOTES

1. This drawing shall be read in conjunction with all other relevant architectural, structural & electrical drawings including those of other consultants.
2. It is the responsibility of contractors & manufacturers to check all relevant site dimensions prior to the start of construction or manufacture.
3. All materials and components must be installed on site in accordance with manufacturer's instructions, shop drawings and standard details.
4. All dimensions are in millimeters unless noted otherwise.
5. Full working drawings, specifications and samples are to be provided by Contractor/Supplier for approval prior to manufacture.


LEGEND :

- Wall socket power single
- Wall socket power double
- Above counter Wall socket power double
- Wall socket telephone

NOTE:

-All External sockets to be waterproof. Contractor to submit samples for Review/Approval.
-Appropriate provisions to be provided for security system, It system etc... Requirements and specifications to be provided by specialist consultants.

TYPICAL SOCKET POSITIONS :

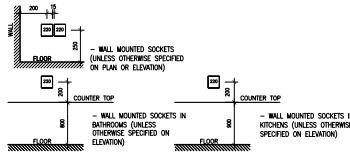


KEY PLAN

A	PLAN REV.	AC	AM	SM	2025.04.22
X	INITIAL ISSUE	AC	AM	AM	2024.08.22
REV.#	GENERAL NOTES	DRAWN BY	CHECKED BY	APPROVED BY	DATE
PROJECT TITLE					REFERENCE
SAF-RIYADH					SAF01 G

DRAWING TITLE	
FIRST FLOOR DRESSING + BATH POWER + COMMUNICATION LAYOUT	
DRAWING NUMBER	REVISION
SK-131	A
SCALE	FORMAT
1:25	A1
ADDITIONAL NOTES	DESIGN DEVELOPMENT

**SIMA MALAK + ALSSAMOURE
DESIGN ASSOCIATES**
P.O. Box 15707 - Riyadh 11454 KSA
Tel. 01 441 4963 - Fax. 01 441 3867
simals@simals.com

©SIMA MALAK + ALSSAMOURE DESIGN ASSOCIATES (شركة) 2003
This document including all drawing and text is the property and copyright of SIMA MALAK + ALSSAMOURE DESIGN ASSOCIATES for use solely with respect to this Project and shall not be copied or reproduced by any means except by agreement in writing from SIMA MALAK + ALSSAMOURE DESIGN ASSOCIATES.

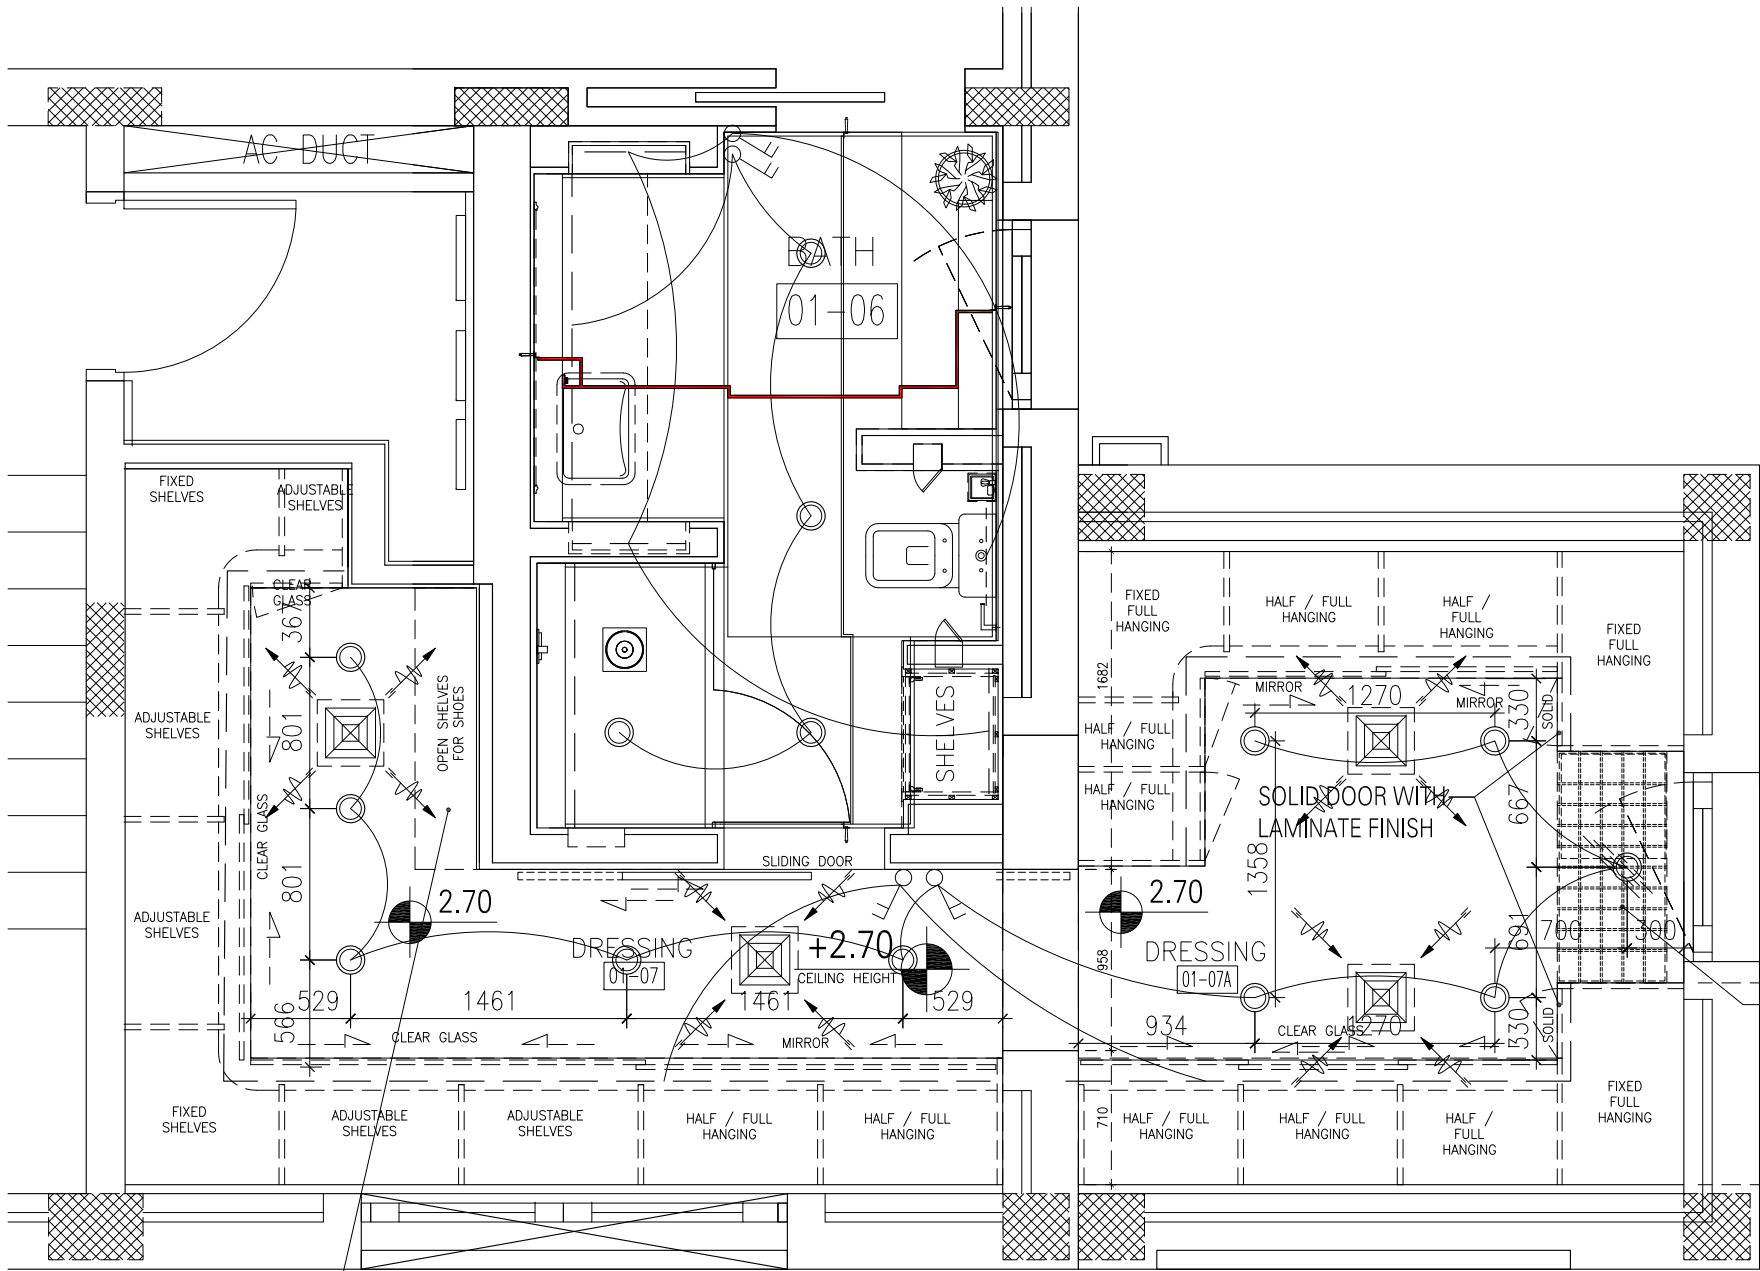

LIGHTING LAYOUT

SCALE 1:20


GENERAL NOTES

1. This drawing shall be read in conjunction with all other relevant architectural, structural & electrical drawings including those of other consultants.
2. It is the responsibility of contractors & manufacturers to check all relevant site dimensions prior to the start of construction or manufacture.
3. All materials and components must be installed on site in accordance with manufacturer's instructions, shop drawings and standard details.
4. All dimensions are in millimeters unless noted otherwise.
5. Full working drawings, specifications and samples are to be provided by Contractor/Supplier for approval prior to manufacture.

LEGEND :

- Chandelier
- Recessed Downlight
- 3 Gang Switch

TYPICAL LAYOUT OF SWITCHES

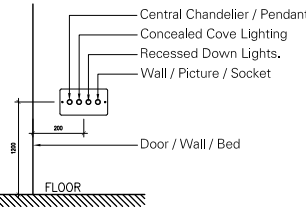

KEY PLAN

B	GEN. REV.	AC	AM	SM	2025.04.22
A	GENERAL REV.	MP	AM	SM	2024.07.03
X	INITIAL ISSUE	AC	AM	AM	2024.08.22
REV.#	GENERAL NOTES	DRAWN BY	CHECKED BY	APPROVED BY	DATE

PROJECT TITLE REFERENCE

SAF-RIYADH SAF01
G


DRAWING TITLE

FIRST FLOOR DRESSING + BATH
LIGHTING LAYOUT

DRAWING NUMBER REVISION

SK-132 B


SCALE	FORMAT	ADDITIONAL	DESIGN DEVELOPMENT
1:25	A1	NOTES	

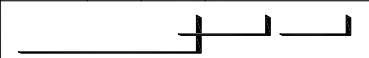


**SIMA MALAK + ALSSAMOURE
DESIGN ASSOCIATES**
P.O. Box 15707 - Riyadh 11454 KSA
Tel. 01 441 4963 - Fax. 01 441 3867
simals@simals.com

©SIMA MALAK + ALSSAMOURE DESIGN ASSOCIATES (شركة) 2003
This document including all drawing and text is the property and
copyright of SIMA MALAK + ALSSAMOURE DESIGN ASSOCIATES for
use solely with respect to this Project and shall not be copied or
reproduced by any means except by agreement in writing from
SIMA MALAK + ALSSAMOURE DESIGN ASSOCIATES.

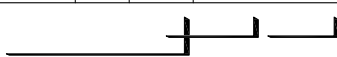

KEY PLAN					
G	REV. WITH CLOUD	AC	AM	SM	2025.05.06
F	REV. AS PER SITE	AC	AM	SM	2025.03.20
E	GENERAL REV.	AC	AM	SM	2024.10.09
D	GENERAL REV.	MP	AM	SM	2024.10.13
C	GENERAL REV.	MP	AM	SM	2024.06.20
B	GENERAL REV.	MP	AM	SM	2024.06.13
A	GENERAL REV.	MP	AM	SM	2024.06.11
X	INITIAL ISSUE	AC	AM	SM	2024.05.21
REV.#	GENERAL NOTES	DRAWN BY	CHECKED BY	APPROVED BY	DATE
PROJECT TITLE					REFERENCE
SAF-RIYADH					SAF01
					G
DRAWING TITLE					
FIRST FLOOR DRESSING (01-07) LAYOUT - OP 01					
DRAWING NUMBER					REVISION
SK-121					G
SCALE	FORMAT	ADDITIONAL NOTES	DESIGN DEVELOPMENT		
1:20	A1				
 SIMA MALAK + ALSSSAMOURE DESIGN ASSOCIATES P.O. Box 15707 - Riyadh 11454 KSA Tel. 01 441 4963 - Fax. 01 441 3867 simals@simals.com					
©SIMA MALAK + ALSSSAMOURE DESIGN ASSOCIATES (شركة) 2003 This document including all drawing and text is the property and copyright of SIMA MALAK + ALSSSAMOURE DESIGN ASSOCIATES for use solely with respect to this Project and shall not be copied or reproduced by any means except by permission in writing from SIMA MALAK + ALSSSAMOURE DESIGN ASSOCIATES.					

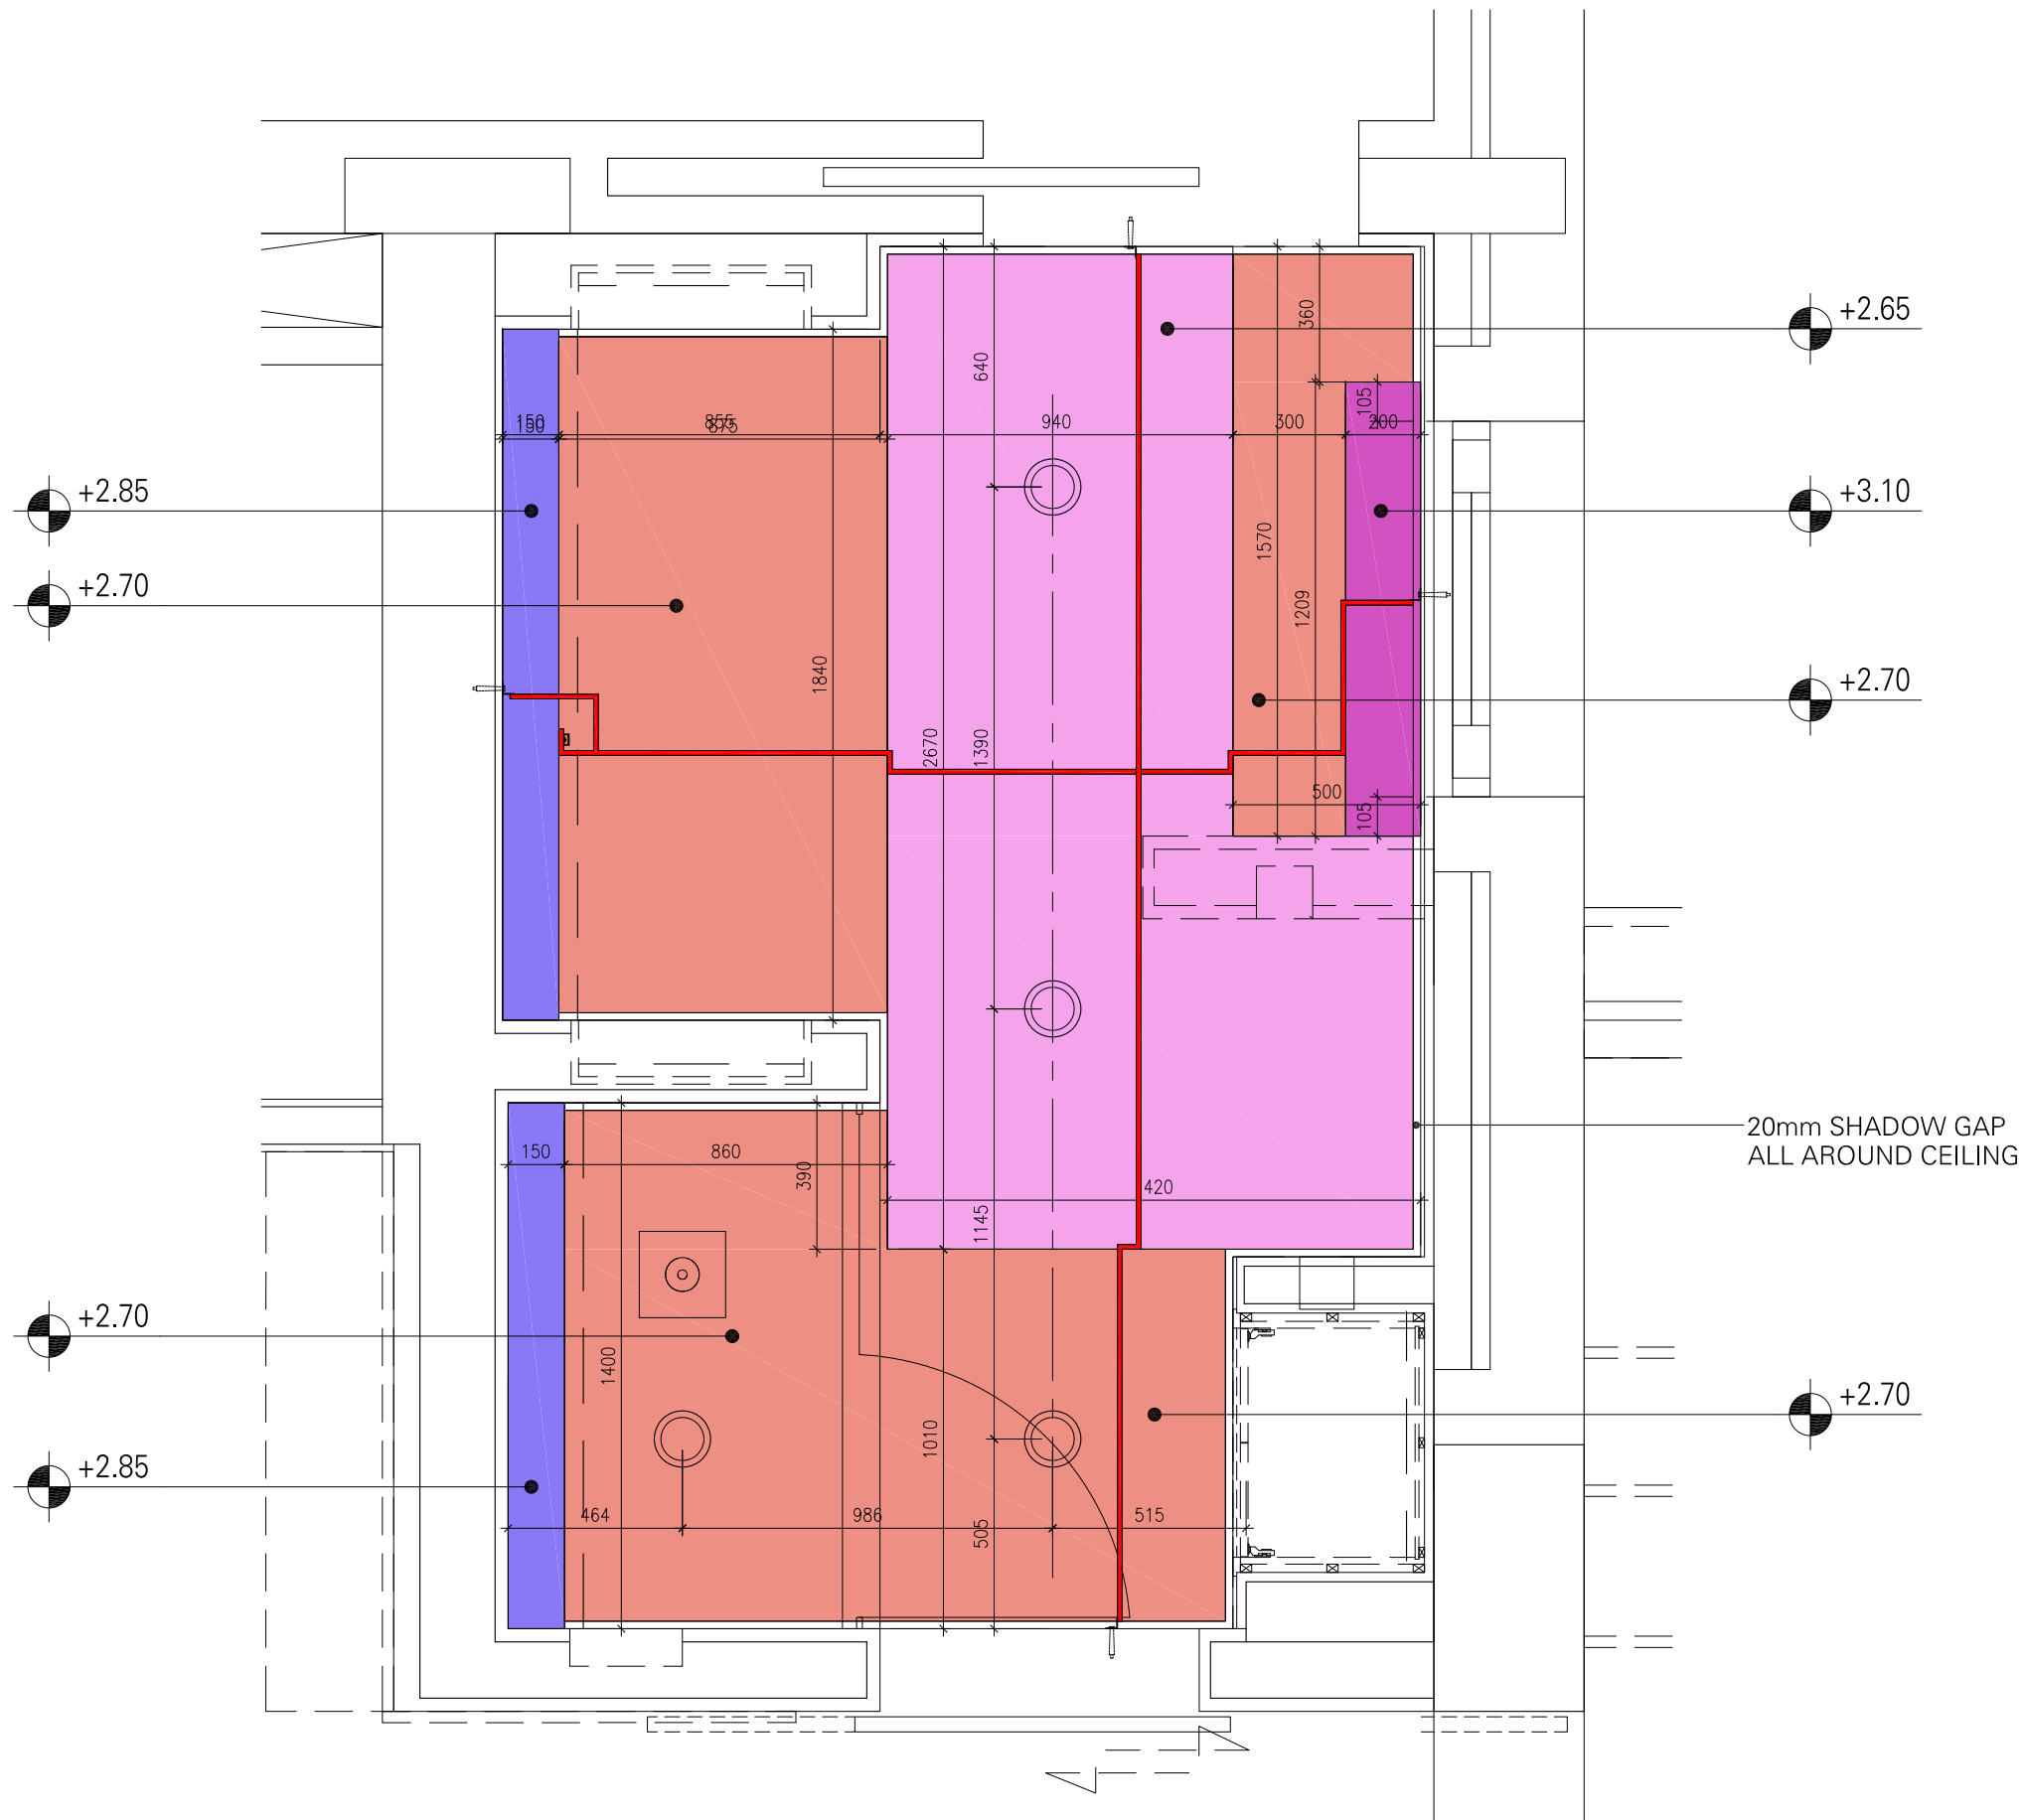

BATH (01-06) CEILING LAYOUT

SCALE 1:10

GENERAL NOTES

1. This drawing shall be read in conjunction with all other relevant architectural, structural & electrical drawings including those of other consultants.
2. It is the responsibility of contractors & manufacturers to check all relevant site dimensions prior to the start of construction or manufacture.
3. All materials and components must be installed on site in accordance with manufacturer's instructions, shop drawings and standard details.
4. All dimensions are in millimeters unless noted otherwise.
5. Full working drawings, specifications and samples are to be provided by Contractor/Supplier for approval prior to manufacture.

LEGEND :

- ✱ Chandelier
- Recessed Downlight

KEY PLAN

✱	INITIAL ISSUE	AC	AM	AM	2025.04.08
REV.#	GENERAL NOTES	DRAWN BY	CHECKED BY	APPROVED BY	DATE

PROJECT TITLE	REFERENCE
---------------	-----------

SAF-RIYADH	SAF01 G
------------	------------

DRAWING TITLE

FIRST FLOOR BATH (01-06) CEILING LAYOUT
--

DRAWING NUMBER	REVISION
----------------	----------

SK-140	
--------	--


SCALE	FORMAT	ADDITIONAL	DESIGN DEVELOPMENT
1:10	A1	NOTES	



**SIMA MALAK + ALSSAMOURE
DESIGN ASSOCIATES**
P.O. Box 15707 - Riyadh 11454 KSA
Tel. 01 441 4963 - Fax. 01 441 3867
simals@simals.com


©SIMA MALAK + ALSSAMOURE DESIGN ASSOCIATES (شركة) 2003
This document including all drawing and text is the property and
copyright of SIMA MALAK + ALSSAMOURE DESIGN ASSOCIATES for
use solely with respect to this Project and shall not be copied or
reproduced by any means except by agreement in writing from
SIMA MALAK + ALSSAMOURE DESIGN ASSOCIATES.

©SIMA MALAK + ALSSAMOURÉ DESIGN ASSOCIATES (المصمم) 2003
This document including all drawing and text is the property and
copyright of SIMA MALAK + ALSSAMOURÉ DESIGN ASSOCIATES for
use solely with respect to this Project and shall not be copied or
reproduced by any means except by agreement in writing from
SIMA MALAK + ALSSAMOURÉ DESIGN ASSOCIATES.

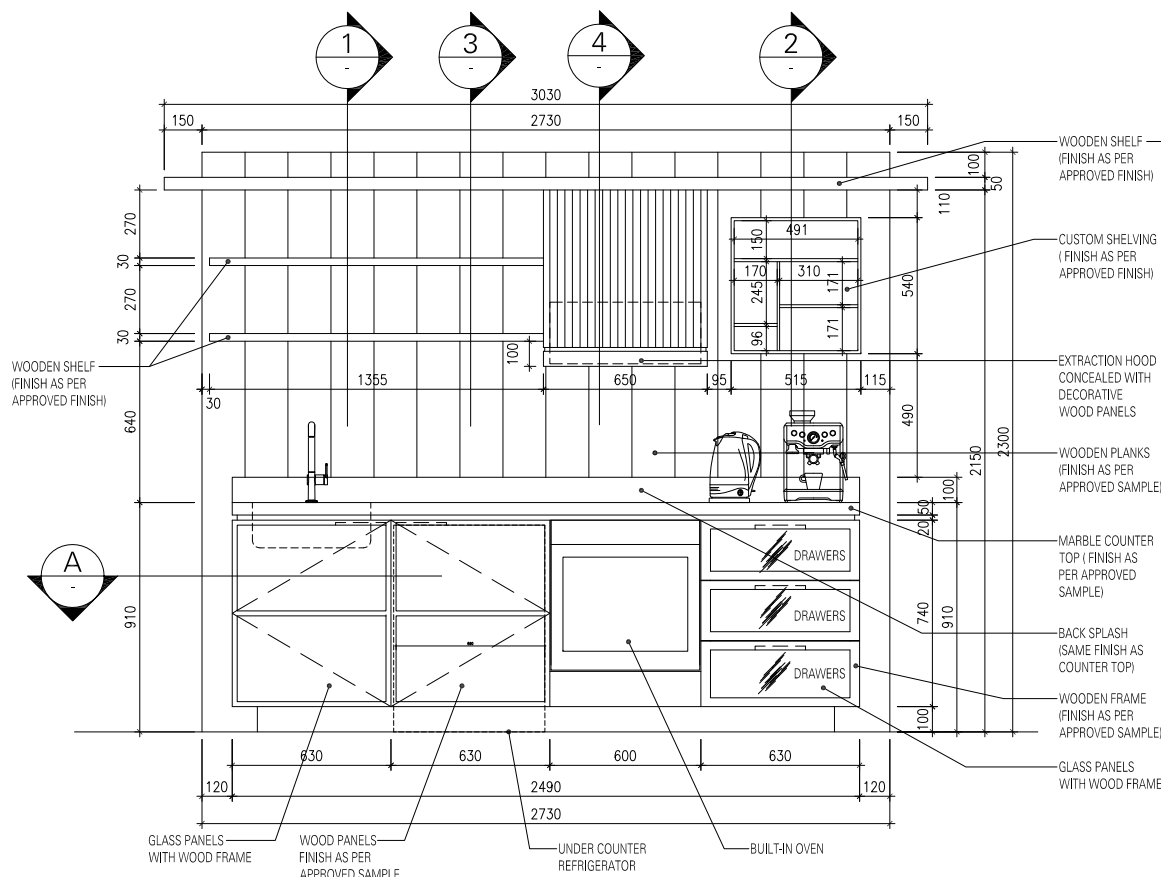


KITCHENETTE ELEVATION


SCALE 1:20

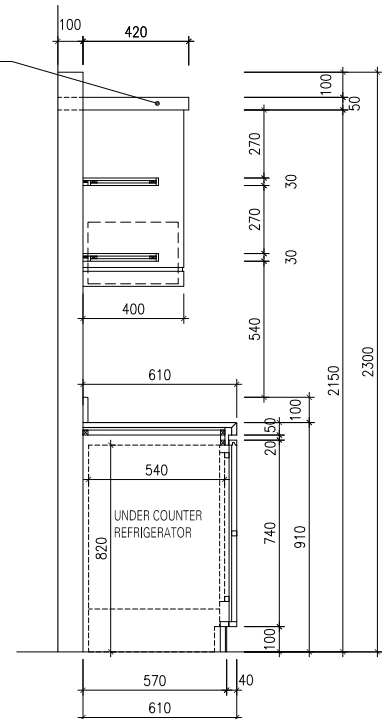


SECTION-1

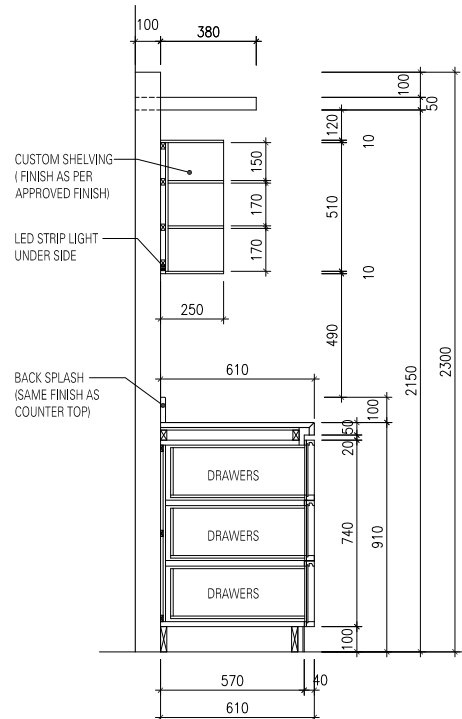

SECTION-2

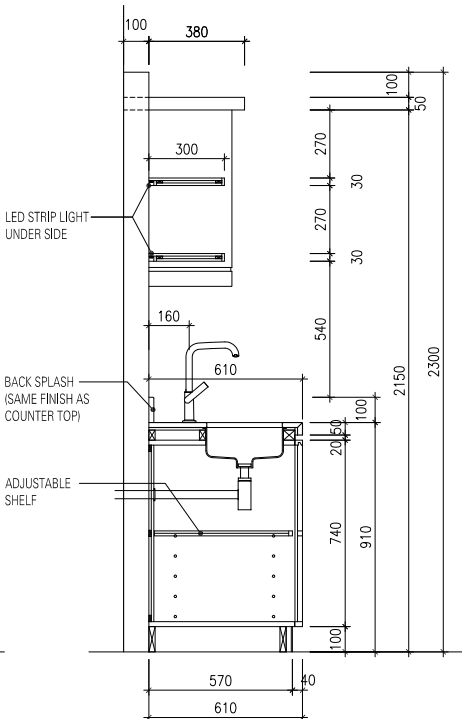


SECTION-3

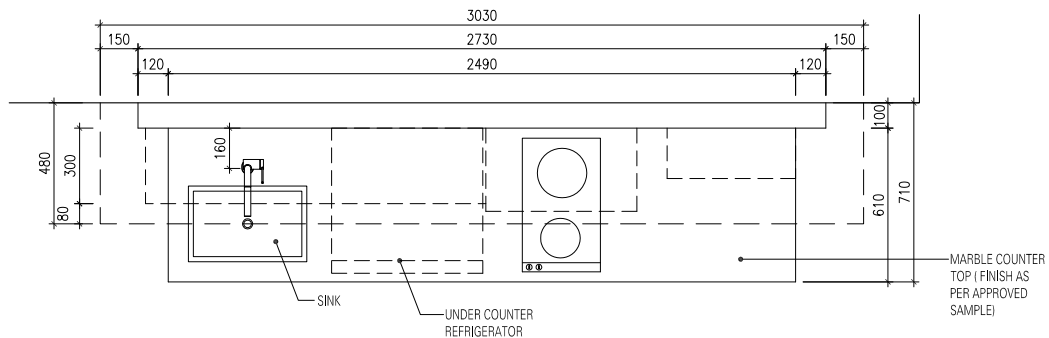


KITCHENETTE PLAN

SCALE 1:20

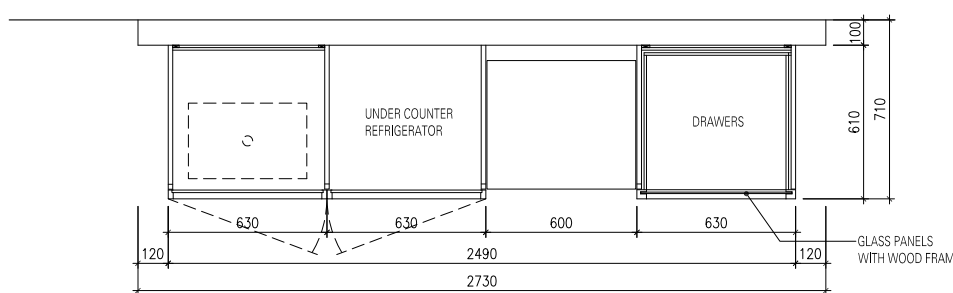

PLAN SECTION - A

SCALE 1:20

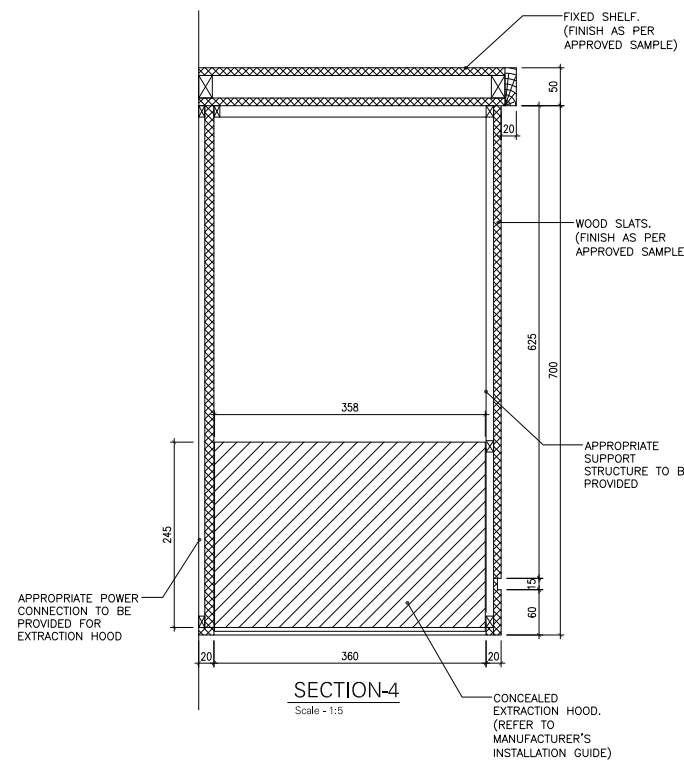

SECTION-4

Scale : 1:5

GENERAL NOTES

1. This drawing shall be read in conjunction with all other relevant architectural, structural & electrical drawings including those of other consultants.
2. It is the responsibility of contractors & manufacturers to check all relevant site dimensions prior to the start of construction or manufacture.
3. All materials and components must be installed on site in accordance with manufacturer's instructions, shop drawings and standard details.
4. All dimensions are in millimeters unless noted otherwise.
5. Full working drawings, specifications and samples are to be provided by Contractor/Supplier for approval prior to manufacture.

KEY PLAN

B	GENERAL REV.	MP	AM	SM	2025.08.21
A	GENERAL REV.	MP	AM	SM	2025.02.07
X	INITIAL ISSUE	AC	AM	AM	2025.01.05
REV.#	GENERAL NOTES	DRAWN BY	CHECKED BY	APPROVED BY	DATE
PROJECT TITLE					REFERENCE

SAF-RIYADH					SAF01
					G

DRAWING TITLE					
FIRST FLOOR KITCHENETTE (01-01) PLAN, ELEVATION, SECTIONS					

DRAWING NUMBER					REVISION
SK-120					B

SCALE	FORMAT	ADDITIONAL	DESIGN DEVELOPMENT		
1:20	A1	NOTES			

SIMA MALAK + ALSSAMOURE
DESIGN ASSOCIATES
P.O. Box 15707 - Riyadh 11454 KSA
Tel. 01 441 4963 - Fax. 01 441 3867
simals@simals.com

©SIMA MALAK + ALSSAMOURE DESIGN ASSOCIATES (شركة) 2003
This document including all drawing and text is the property and
copyright of SIMA MALAK + ALSSAMOURE DESIGN ASSOCIATES for
use solely with respect to this Project and shall not be copied or
reproduced by any means except by agreement in writing from
SIMA MALAK + ALSSAMOURE DESIGN ASSOCIATES.